




V4
ESC 1:30

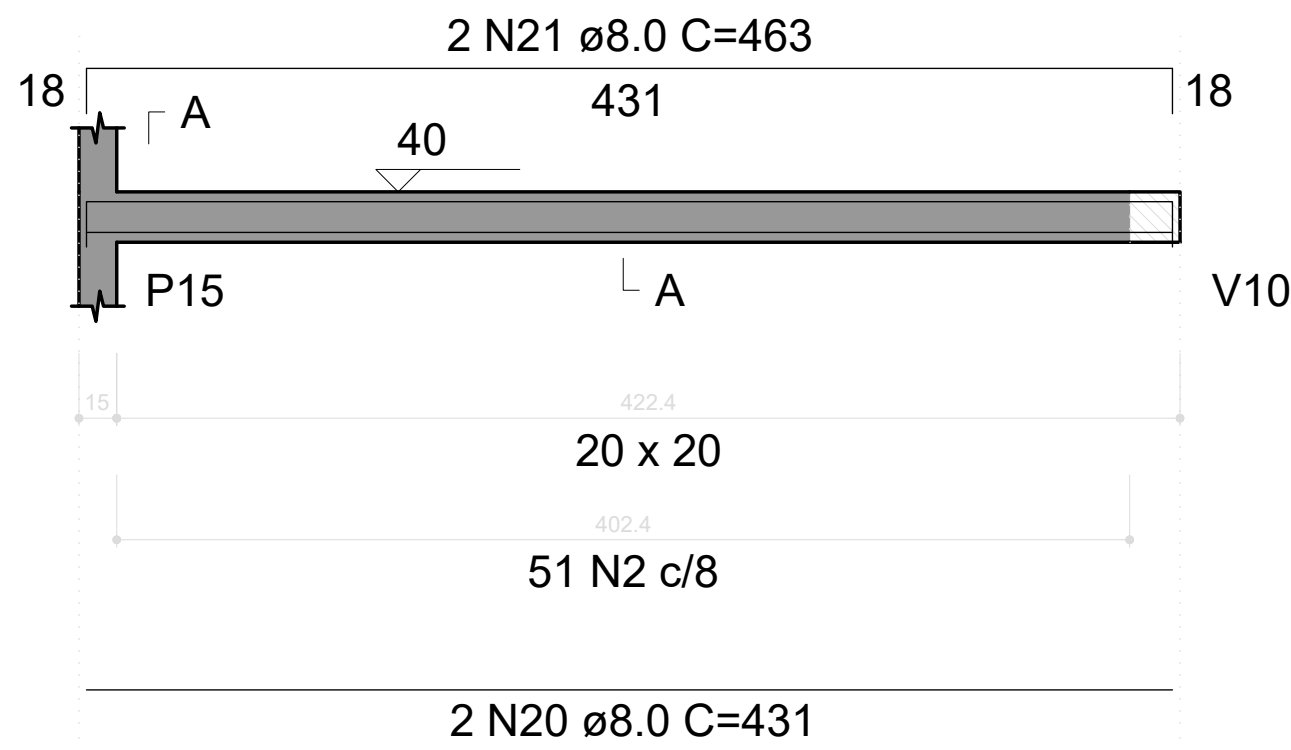


SEÇÃO A-A
ESC 1:25

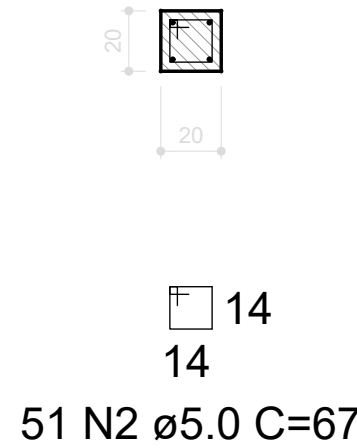


V5
ESC 1:30

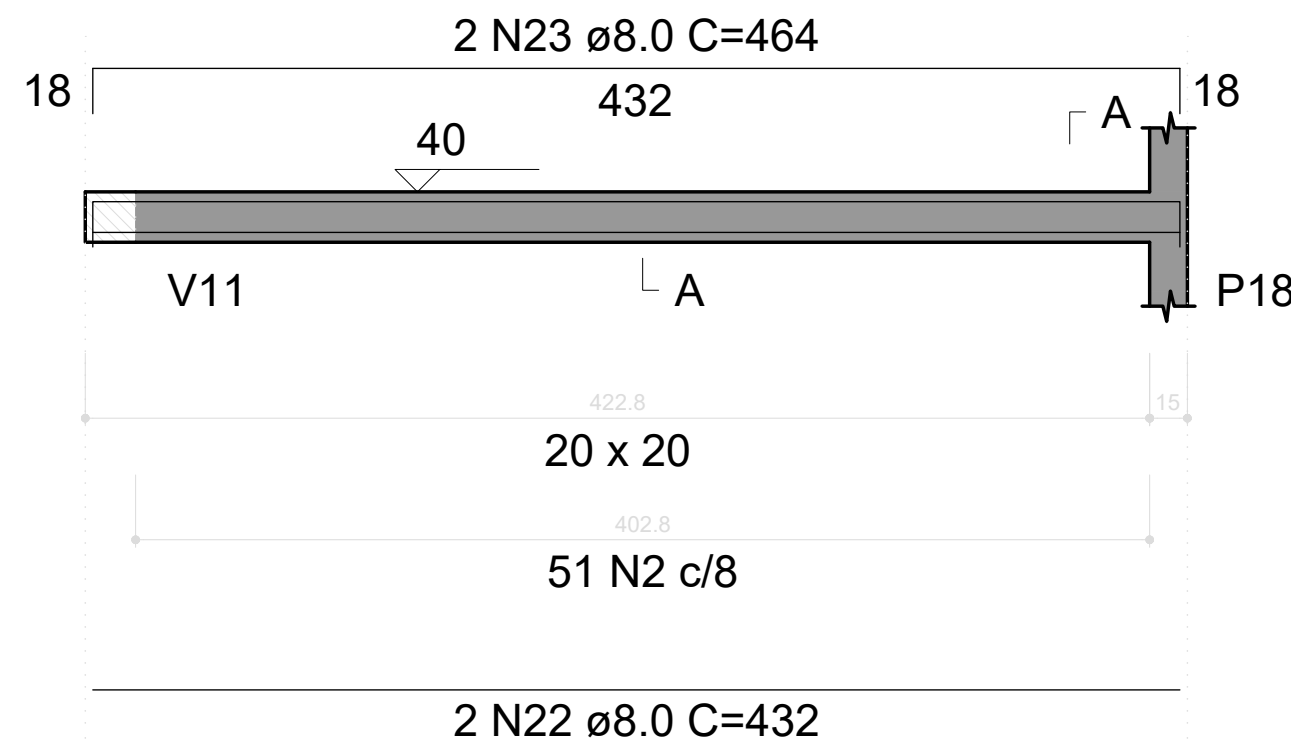


SEÇÃO A-A
ESC 1:25

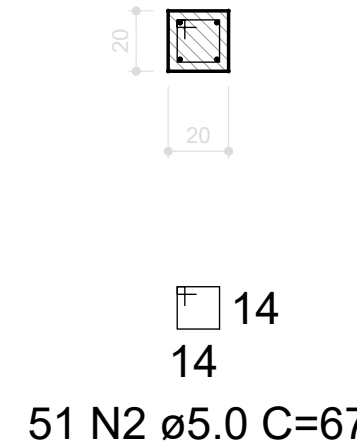

V14
ESC 1:30

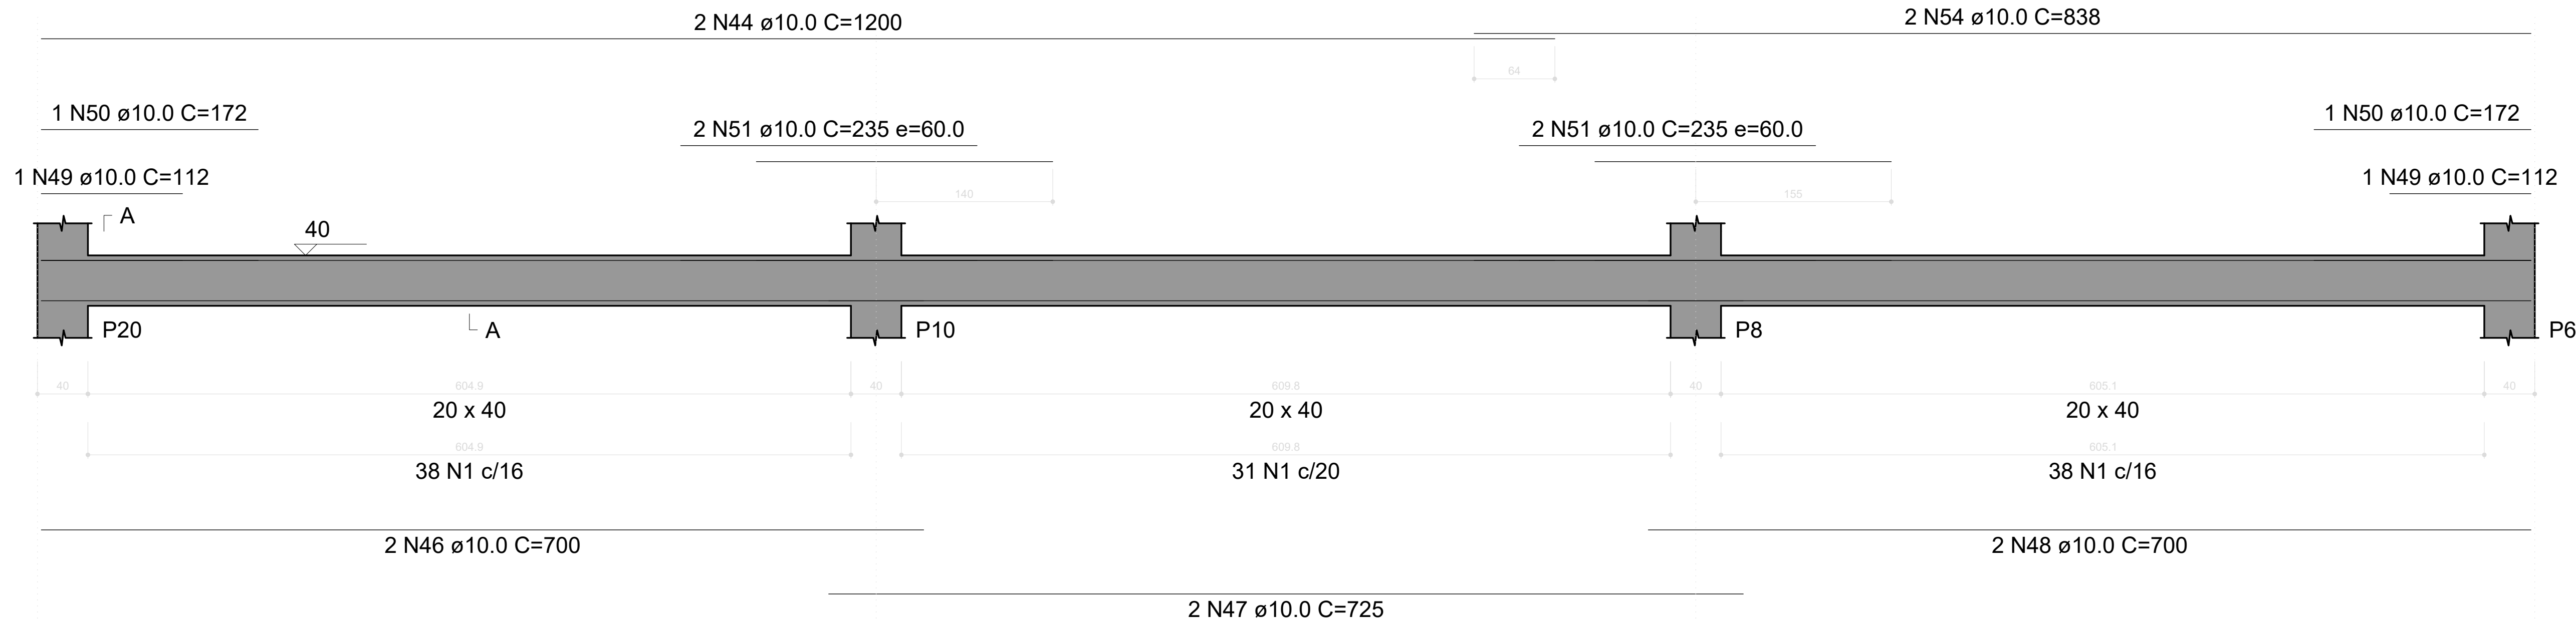

SEÇÃO A-A
ESC 1:25

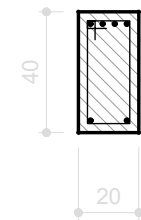

107 N1 ø5.0 C=107

RELAÇÃO DO AÇO					
AÇO	N	DIAM (mm)	QUANT	C.UNIT (cm)	C.TOTAL (cm)
CA60	1	5.0	477	107	51039
	2	5.0	295	67	19765
CA50	3	5.0	6	57	342
	4	8.0	2	604	1208
	5	8.0	2	618	1236
	6	8.0	1	660	660
	7	8.0	1	395	395
	8	8.0	2	1195	2390
	9	8.0	1	305	305
	10	8.0	1	201	201
	11	8.0	2	1048	2096
	12	8.0	1	805	805
	13	8.0	2	617	1234
	14	8.0	2	99	198
	15	8.0	1	747	747
	16	8.0	1	748	748
	17	8.0	2	1198	2396
	18	8.0	2	1200	2400
	19	8.0	2	434	868
	20	8.0	2	431	862
	21	8.0	2	463	926
	22	8.0	2	432	864
	23	8.0	2	464	928
	24	8.0	2	264	528
	25	8.0	2	278	556
	26	8.0	2	72	144
	27	8.0	4	84	336
	28	8.0	4	159	636
	29	8.0	2	182	364
	30	8.0	1	85	85
	31	8.0	2	312	624
	32	8.0	1	117	117
	33	8.0	1	160	160
	34	8.0	2	331	662
	35	8.0	2	304	608
	36	8.0	2	331	662
	37	8.0	2	166	332
	38	8.0	2	82	164
	39	10.0	2	1084	2168
	40	10.0	2	178	356
	41	10.0	2	1025	2050
	42	10.0	2	590	1180
	43	10.0	2	1198	2396
	44	10.0	6	1200	7200
	45	10.0	2	496	992
	46	10.0	4	700	2800
	47	10.0	4	725	2900
	48	10.0	4	700	2800
	49	10.0	4	112	448
	50	10.0	4	172	688
	51	10.0	8	235	1880
	52	10.0	2	839	1678
	53	10.0	1	109	109
	54	10.0	2	838	1676

RESUMO DO AÇO			
AÇO	DIAM (mm)	C.TOTAL (m)	PESO + 10% (kg)
CA50	8.0	274.4	119.1
CA60	10.0	313.2	212.4
CA60	5.0	711.5	120.6
PESO TOTAL (kg)			
CA50	331.5		
CA60	120.6		

Volume de concreto (C-25) = 8.66 m³
Área de forma = 111.16 m²

PROPRIETÁRIO: PREFEITURA MUNICIPAL DE COREMAS - PB
LINCOLN CARTAXO DE LIRA JUNIOR:06897861405
PROJETO: LINCOLN CARTAXO DE LIRA JÚNIOR CREA 160.814.689-8

CONSTRUÇÃO:

14/26

FOLHA: 14/26
PROJETO: CONSTRUÇÃO DE GINÁSIO POLIESPORTIVO - ESTRUTURAL
CONVENIENTE: PREFEITURA MUNICIPAL DE COREMAS - PB
CONVENIADO: MUNICÍPIO DE COREMAS - PB
LOCALIDADE: COREMAS - PB

DESENHO	DATA	RESPONSÁVEL	RUBRICA	DADOS
CÓPIA	AGO/2025	LINCOLN CARTAXO		
VISTO				

ESCALAS	DESENHOS	CONVÊNIO
Indicada	- VIGAS PAV. BALDRAMES (NÍVEL 40)	GOVERNO DO ESTADO
		ARQUIVO

Aprovações: