


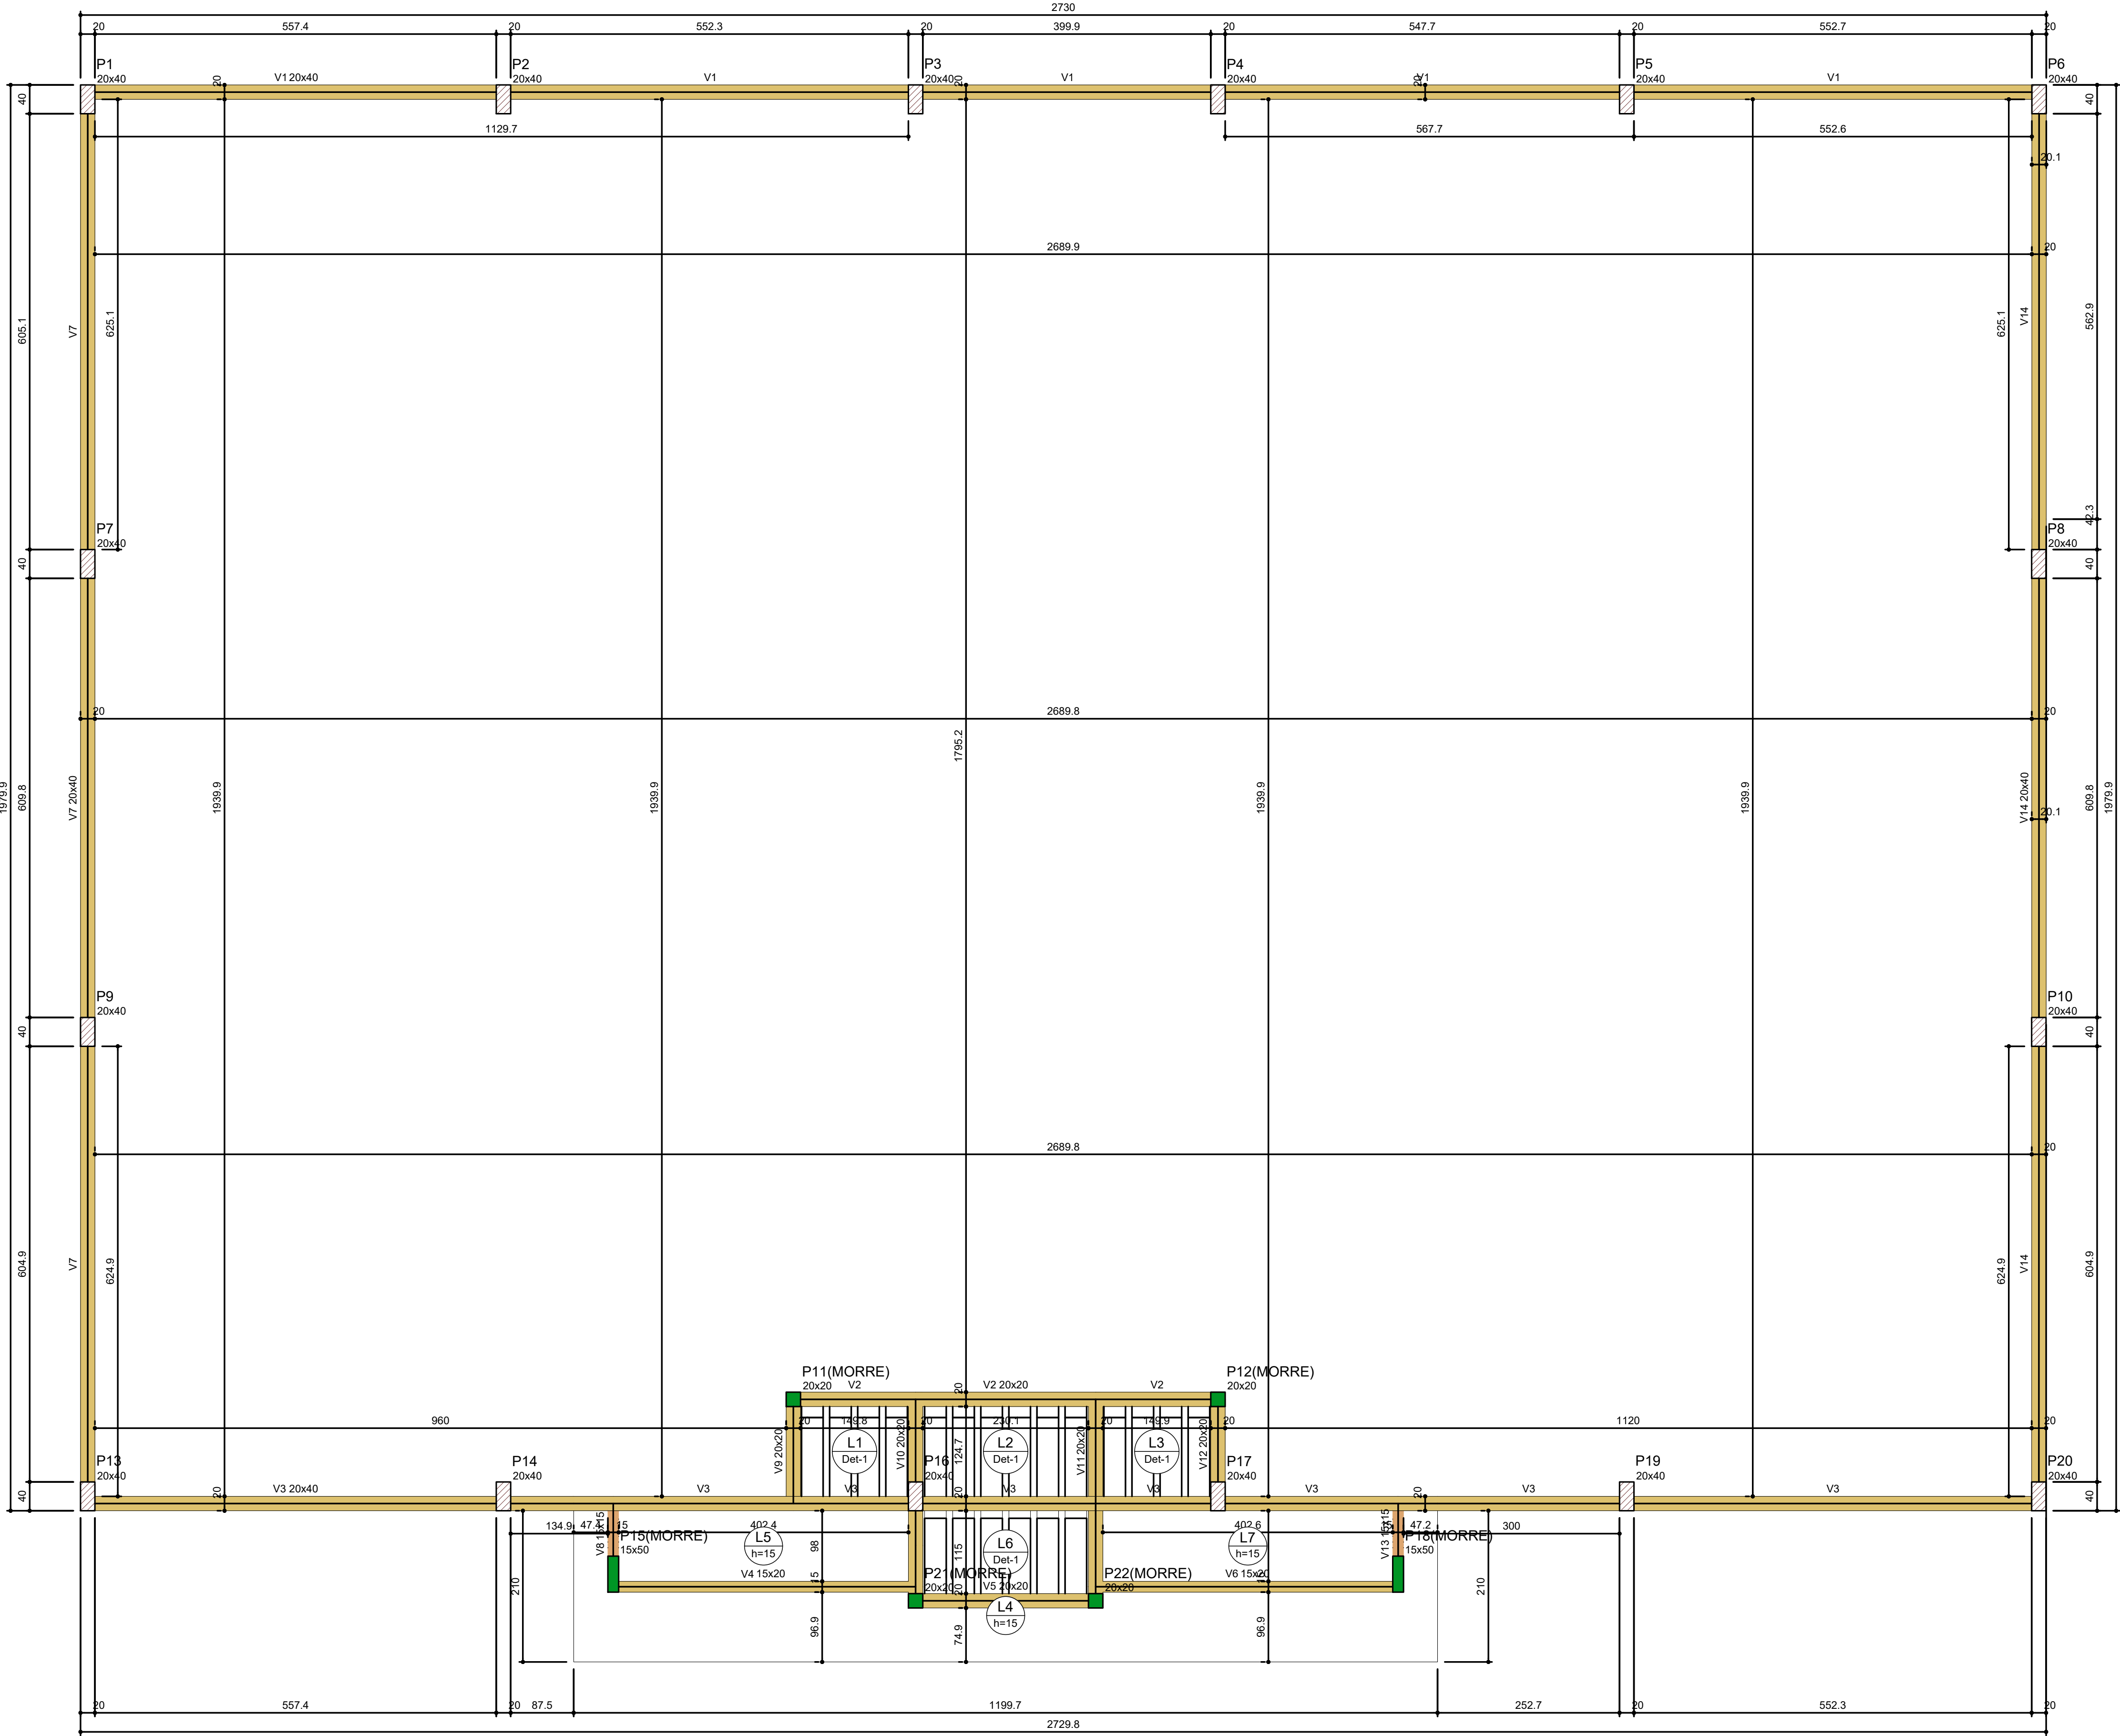

Forma do pavimento Laje (Nível 305)
escala 1:50

Vigas			
Nome	Seção (cm)	Elevação (cm)	Nível (cm)
V1	20x40	0	305
V2	20x20	0	305
V3	20x40	0	305
V4	15x20	0	305
V5	20x20	0	305
V6	15x20	0	305
V7	20x40	0	305
V8	15x15	0	305
V9	20x20	0	305
V10	20x20	0	305
V11	20x20	0	305
V12	20x20	0	305
V13	15x15	0	305
V14	20x40	0	305

Lajes						
Nome	Tipo	Dados			Sobrecarga (kgf/m²)	
		Altura (cm)	Elevação (cm)	Nível (cm)	Adicional	Acidental
L1	Trelçada 1D	15	0	305	50	50
L2	Trelçada 1D	15	0	305	50	50
L3	Trelçada 1D	15	0	305	50	50
L4	Maciça	15	0	305	50	50
L5	Maciça	15	0	305	50	50
L6	Trelçada 1D	15	0	305	50	50
L7	Maciça	15	0	305	50	50


Área de lajes			
Tipo	Altura (cm)	Bloco de Enchimento	Área (m²)
Maciça	15	-	20.00
Trelçada 1D	15	B8/30/125	9.25

Características dos materiais	
fck (kgf/cm²)	Ecs (kgf/cm²)
250	241500

Pilares			
Nome	Seção (cm)	Elevação (cm)	Nível (cm)
P1	20x40	0	305
P2	20x40	0	305
P3	20x40	0	305
P4	20x40	0	305
P5	20x40	0	305
P6	20x40	0	305
P7	20x40	0	305
P8	20x40	0	305
P9	20x40	0	305
P10	20x40	0	305
P11	20x20	0	305
P12	20x20	0	305
P13	20x40	0	305
P14	20x40	0	305
P15	15x50	0	305
P16	20x40	0	305
P17	20x40	0	305
P18	15x50	0	305
P19	20x40	0	305
P20	20x40	0	305
P21	20x20	0	305
P22	20x20	0	305

Legenda dos pilares	
	Pilar que morre
	Pilar que passa

Legenda das vigas e paredes	
	Viga
	Viga chata ou invertida

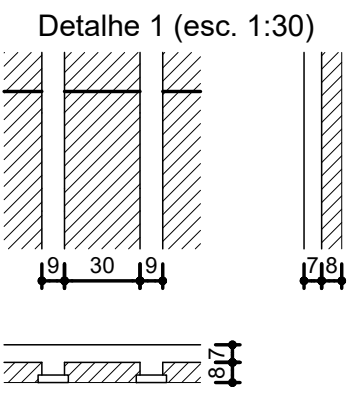

Blocos de enchimento					
Detalhe	Tipo	Nome	Dimensões (cm)		
			hb	bx	by
1	EPS Unidirecional	B8/30/125	8	30	125
					34

PROPRIETÁRIO: PREFEITURA MUNICIPAL DE COREMAS - PB

PROJETO: LINCOLN CARTAXO DE LIRA JÚNIOR CREA 160.814.889-8

CONSTRUÇÃO:

FOLHA 15/26
PROJETO: CONSTRUÇÃO DE GINÁSIO POLIESPORTIVO - ESTRUTURAL
CONVENIENTE: PREFEITURA MUNICIPAL DE COREMAS - PB
CONVENIADO: MUNICÍPIO DE COREMAS - PB
LOCALIDADE: COREMAS - PB

DESENHO	DATA	RESPONSÁVEL	RUBRICA	DADOS
CÓPIA	AGO/2025	LINCOLN CARTAXO		
VISTO				
ESCALAS	DESENHOS			CONVÊNIO
Indicada	- FORMA DO PAVIMENTO LAJE (NÍVEL 305)			GOVERNO DO ESTADO
				ARQUIVO

Aprovações: