




V3
ESC 1:30

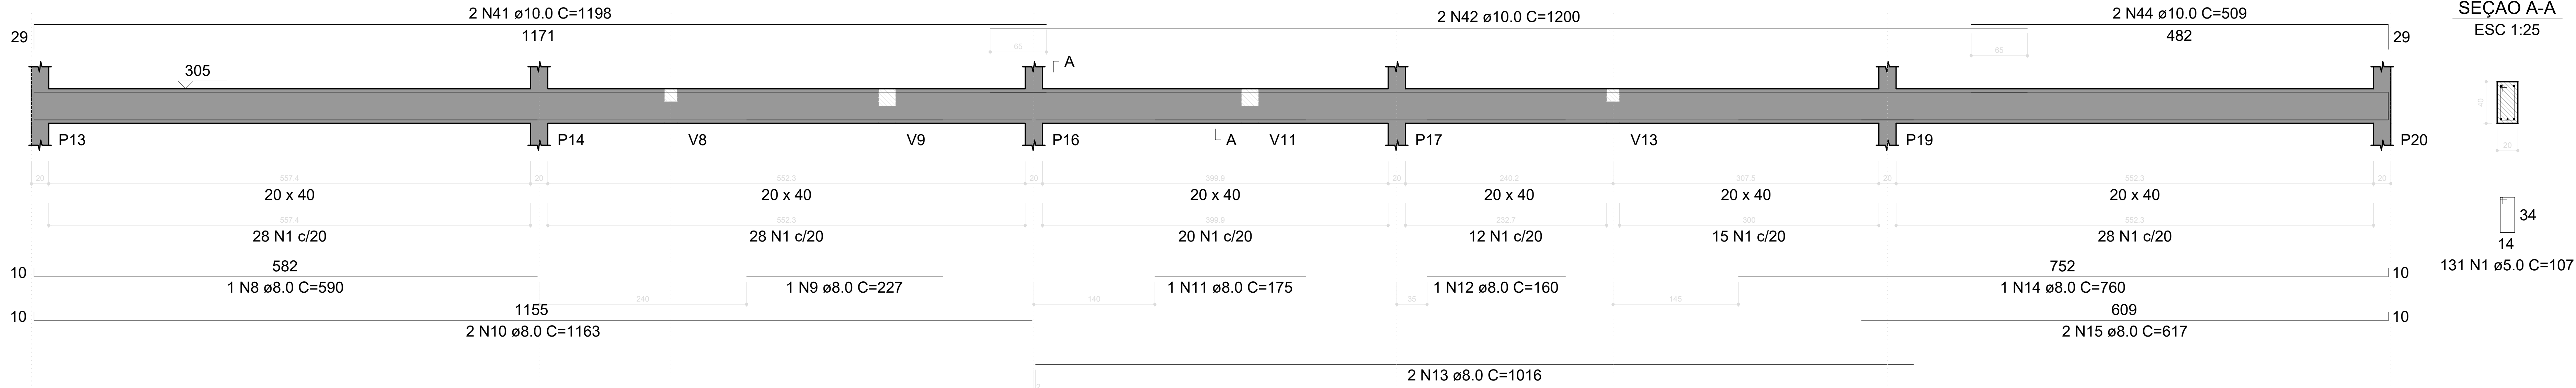

V2
ESC 1:30

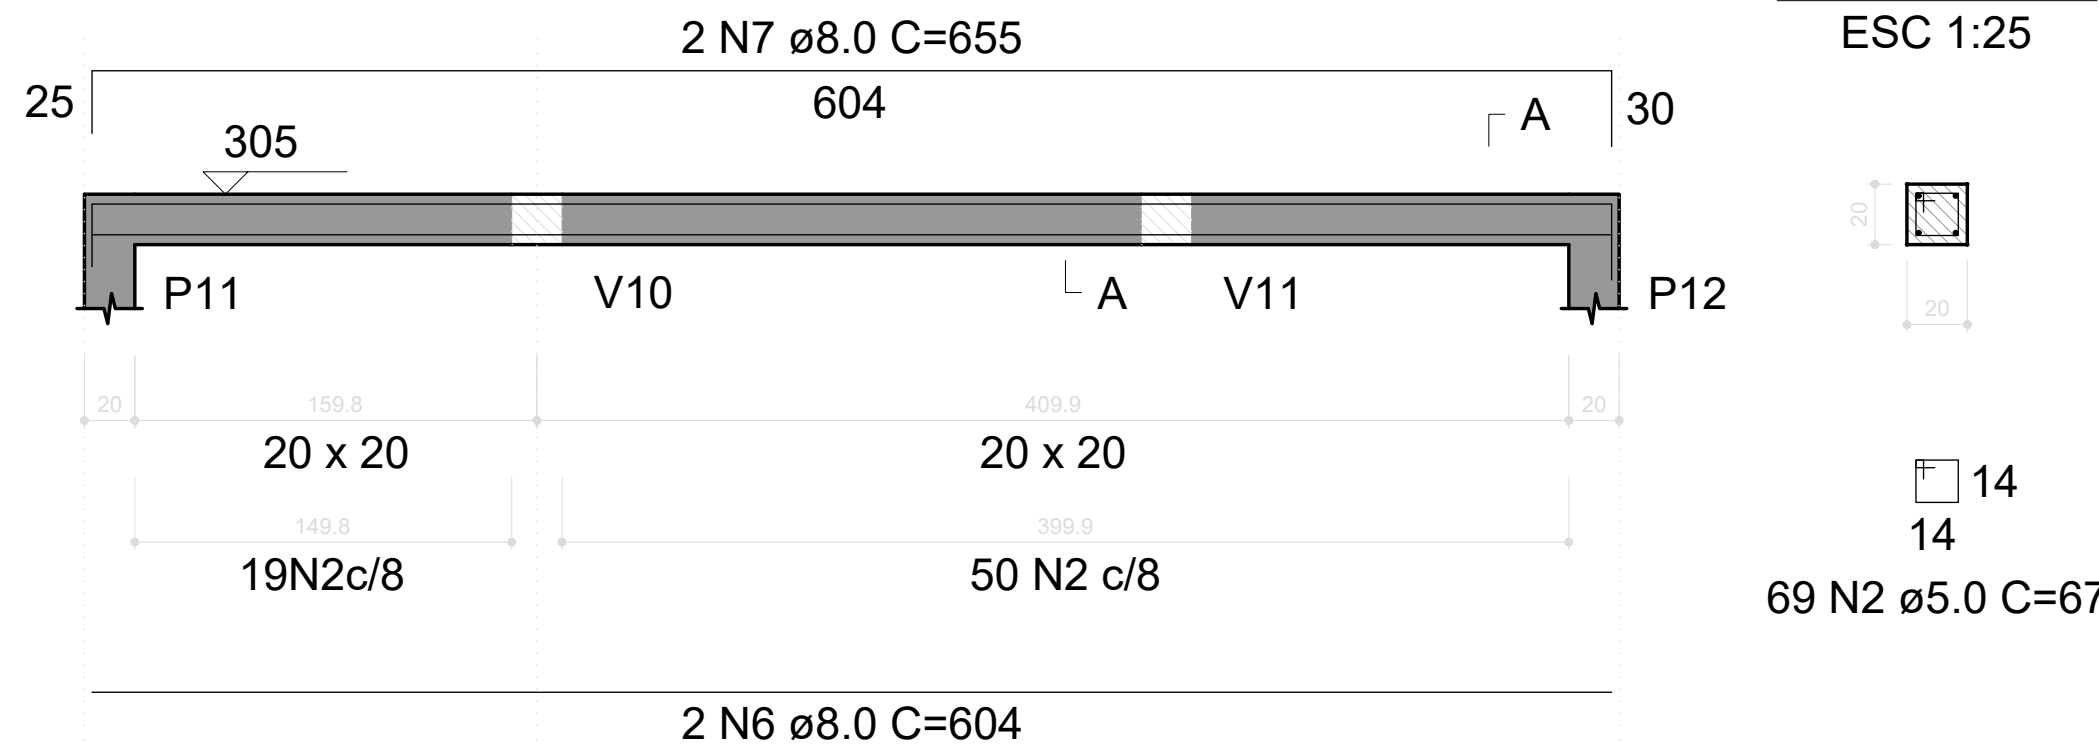


V8
ESC 1:30

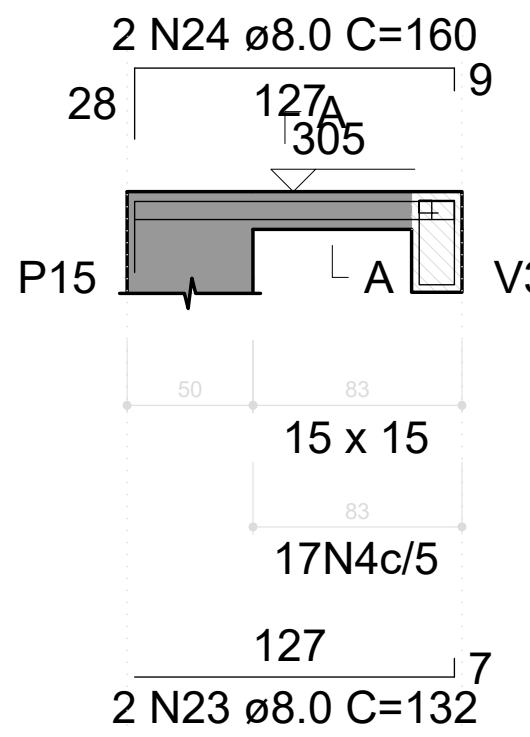


SEÇÃO A-A
ESC 1:25

SUSPENSÃO V3
ESC 1:25

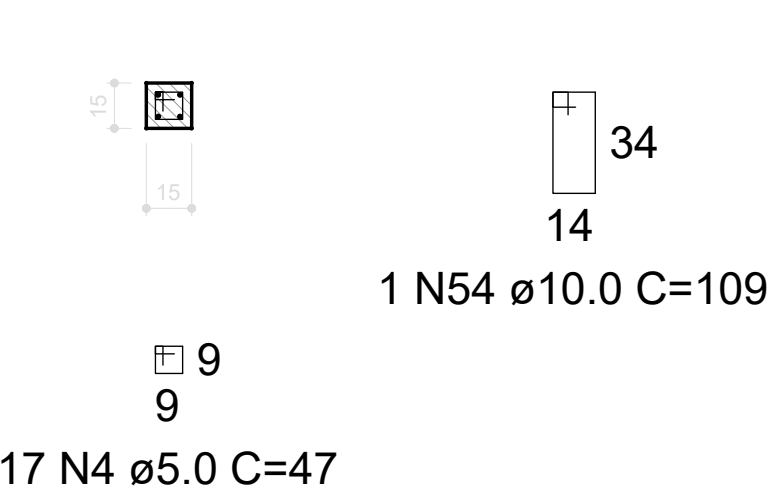


V10
ESC 1:30

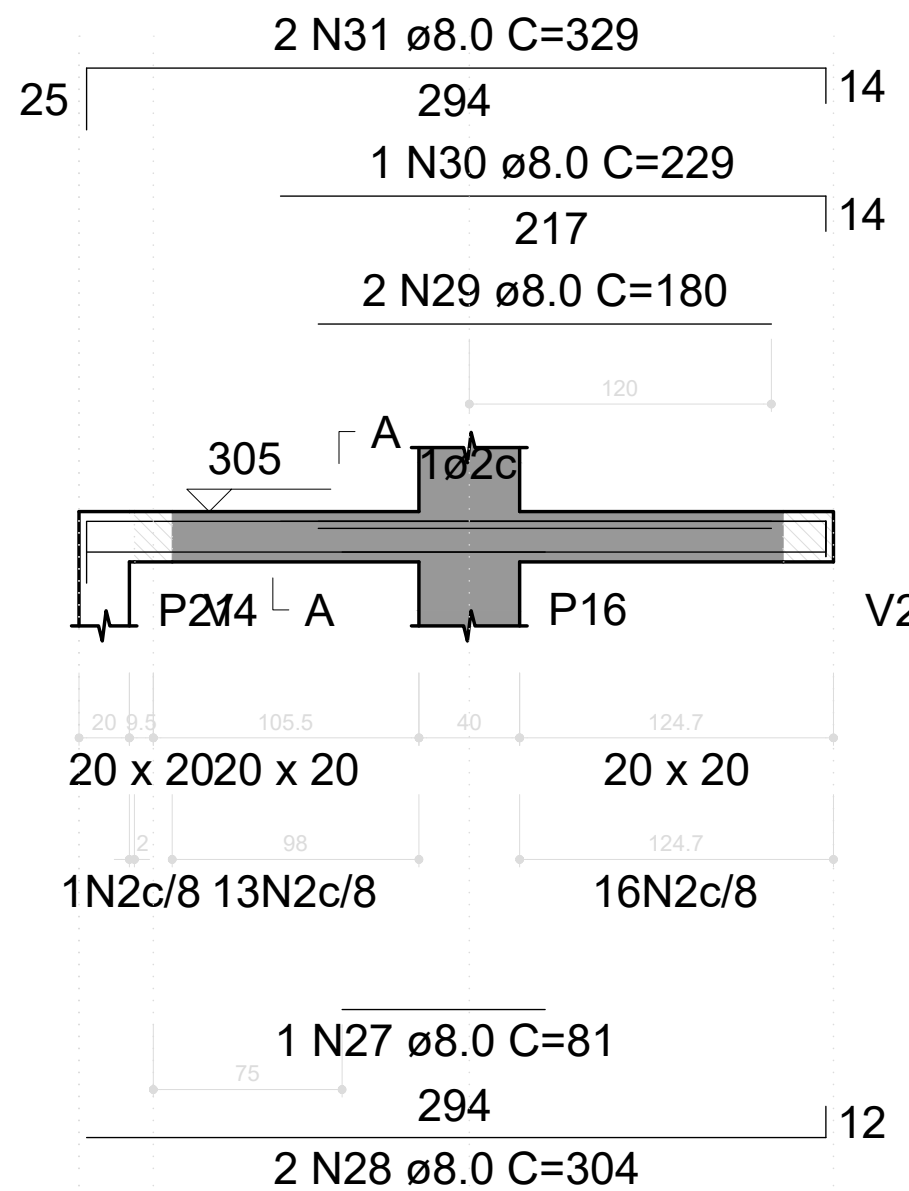


SEÇÃO A-A
ESC 1:25

V11
ESC 1:30

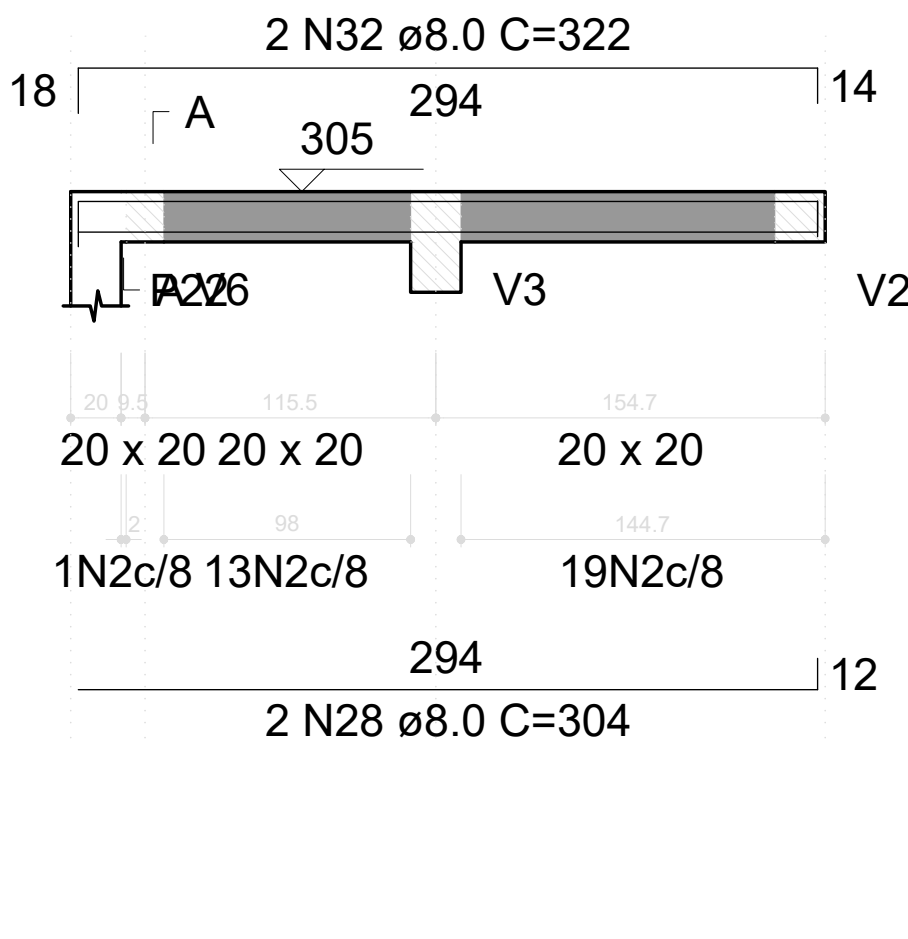


SEÇÃO A-A
ESC 1:25

V12
ESC 1:30

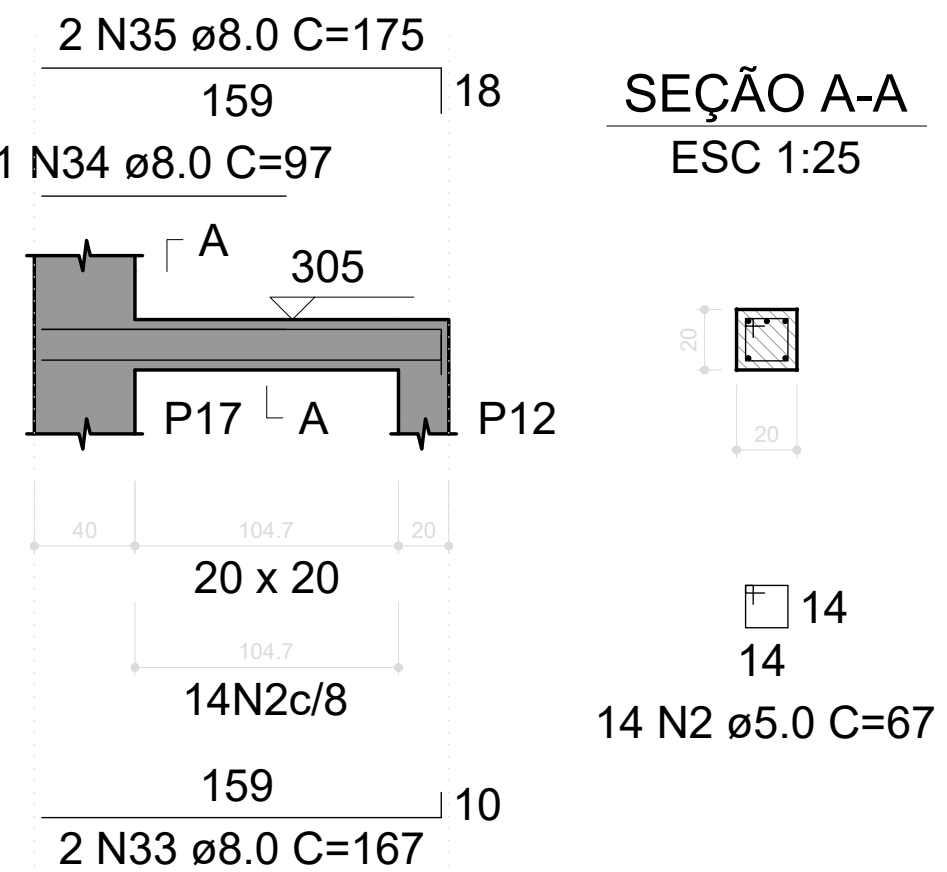

SEÇÃO A-A
ESC 1:25

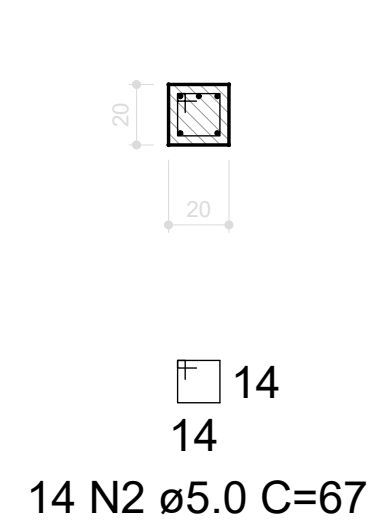

*OBS.: OS QUADROS RESUMO REFERENTES A ESTA PRANCHA CONSTAM NA PRANCHA 18/26

PROPRIETÁRIO: PREFEITURA MUNICIPAL DE COREMAS - PB

PROJETO: LINCOLN CARTAXO DE LIRA JÚNIOR CREA 160.814.689-8

CONSTRUÇÃO:

FOLHA	PROJETO:	CONSTRUÇÃO DE GINÁSIO POLIESPORTIVO - ESTRUTURAL		
17/26	CONVENIENTE:	PREFEITURA MUNICIPAL DE COREMAS - PB		
	CONVENIADO:	MUNICÍPIO DE COREMAS - PB		
	LOCALIDADE:	COREMAS - PB		
DESENHO	DATA	RESPONSÁVEL	RUBRICA	DADOS
CÓPIA	AGO/2025	LINCOLN CARTAXO		
VISTO				
ESCALAS	DESENHOS			CONVÊNIO
Indicada	- VIGAS DO PAVIMENTO LAJE (NÍVEL 305)			GOVERNO DO ESTADO
				ARQUIVO

Aprovações: