

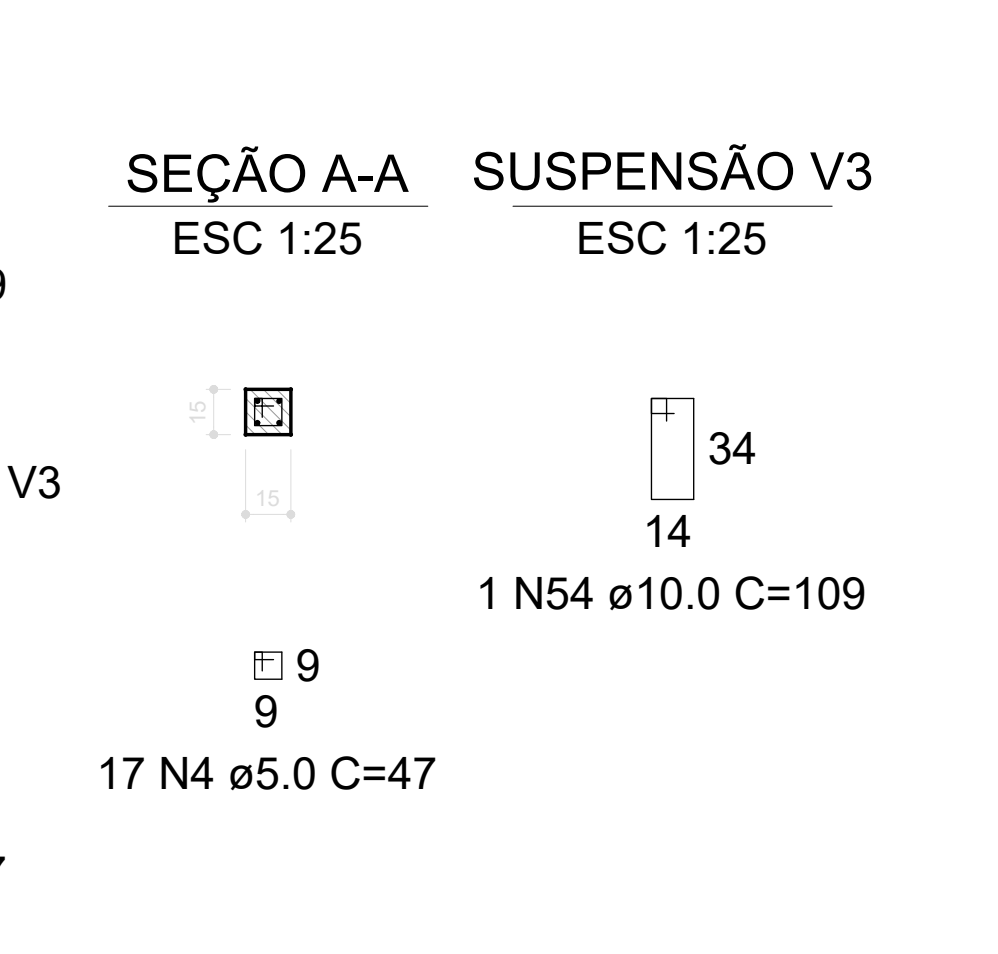
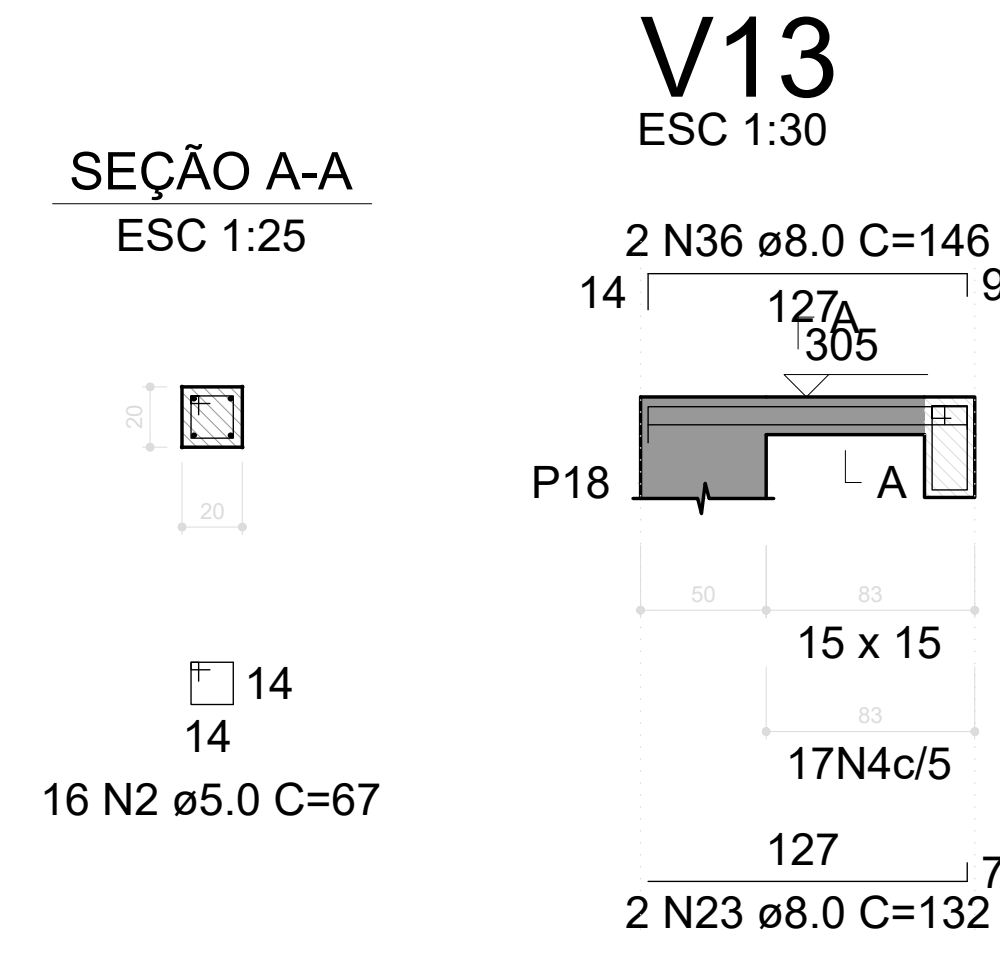
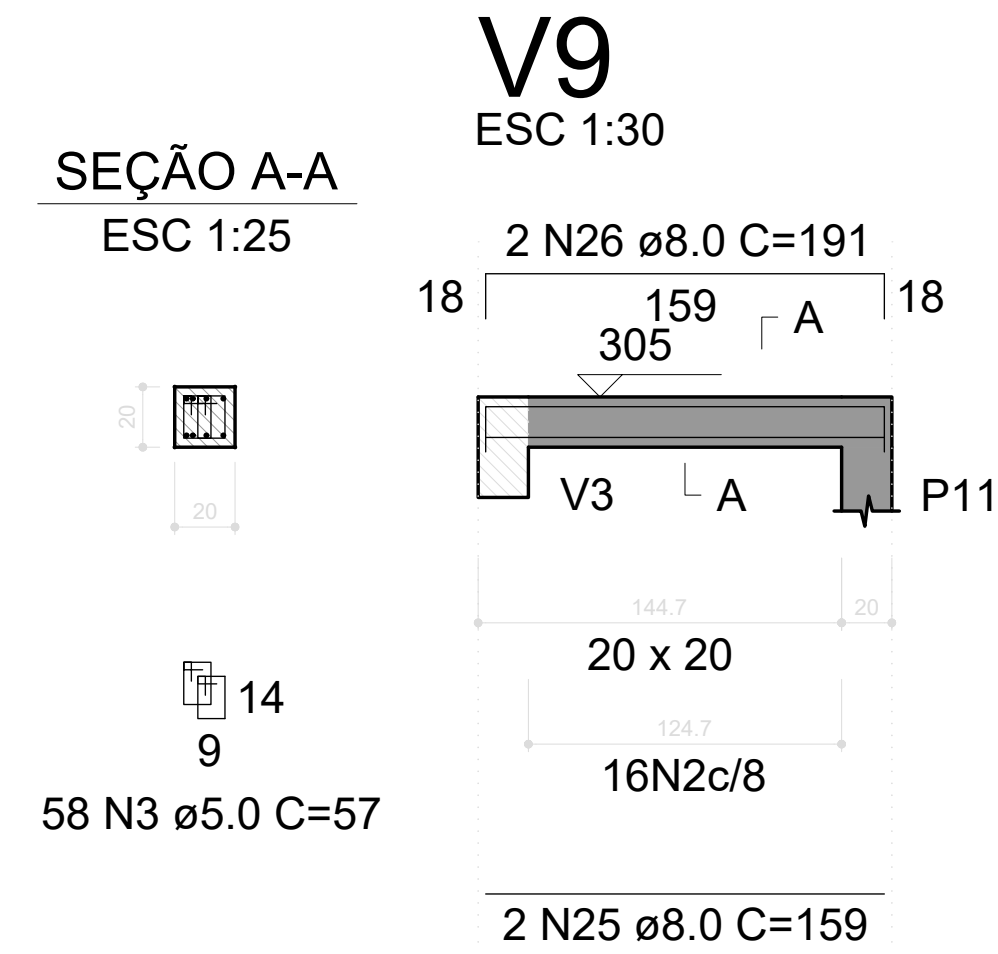
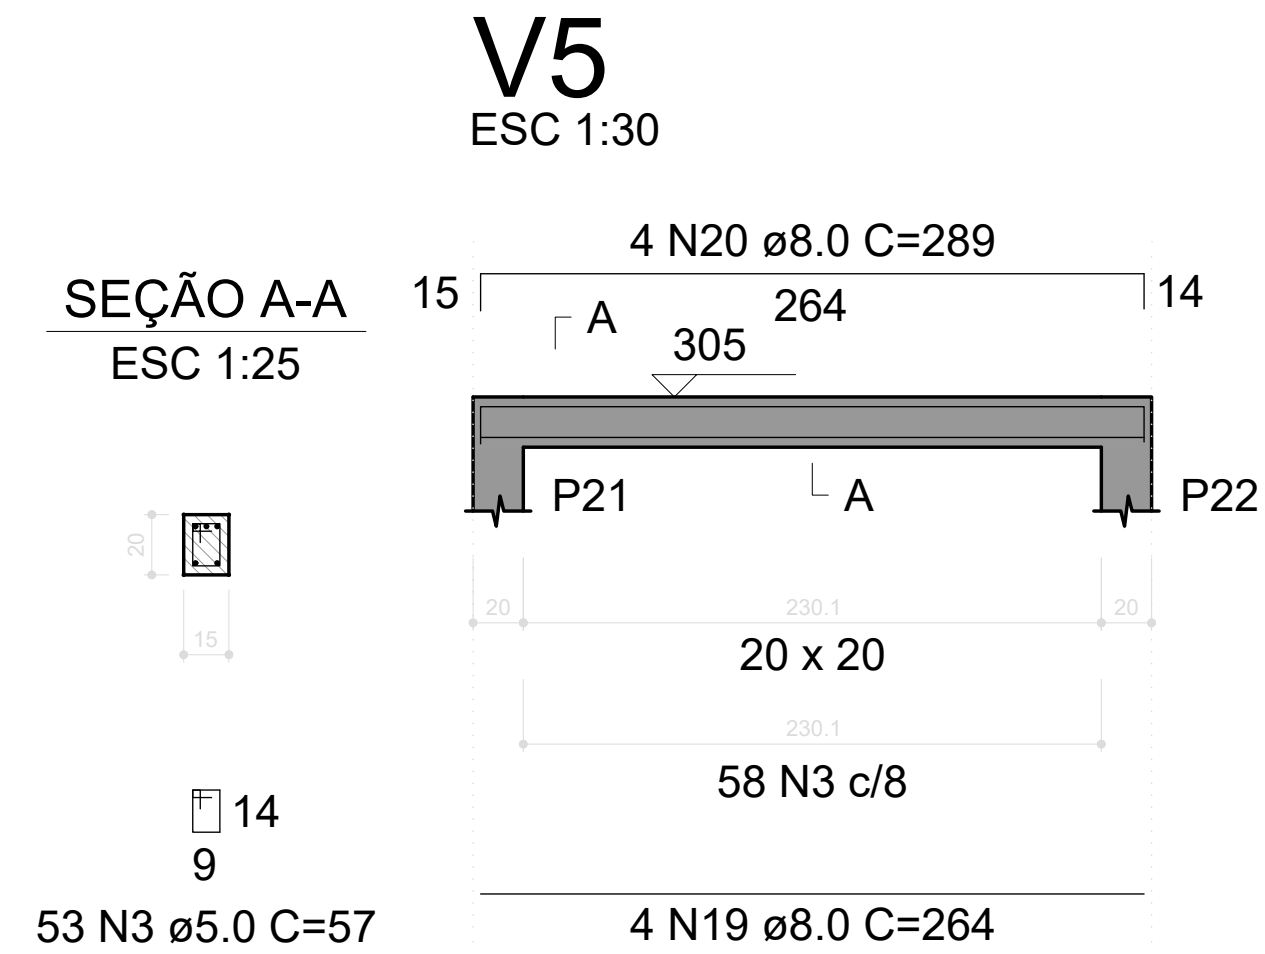
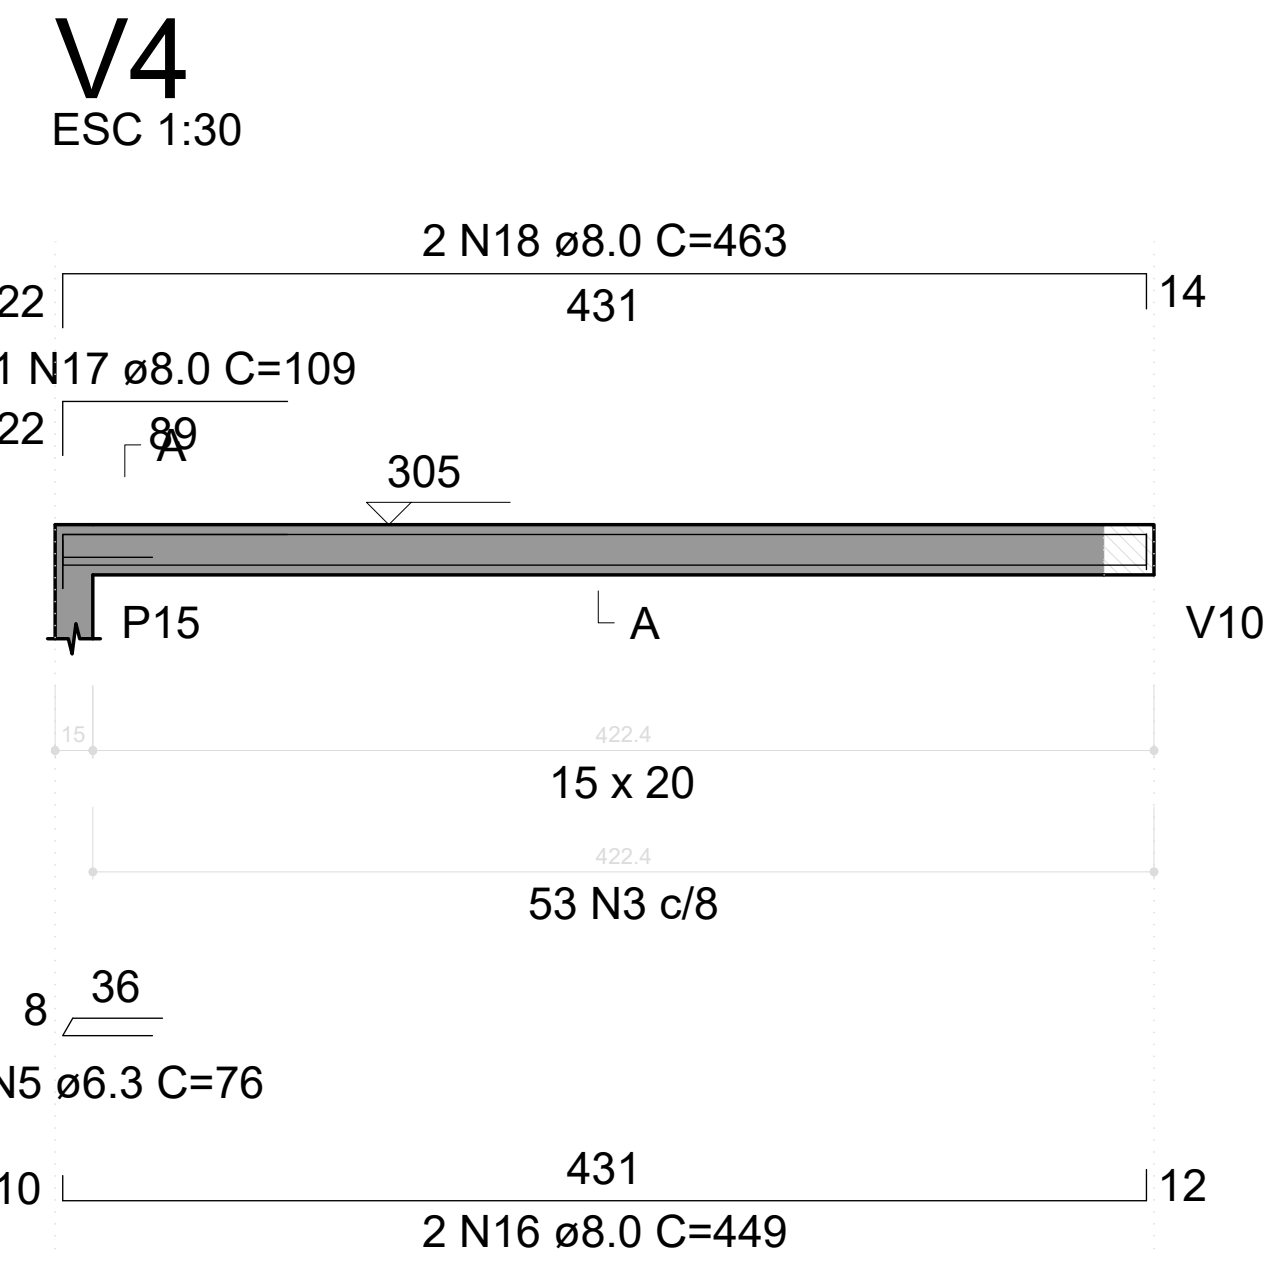
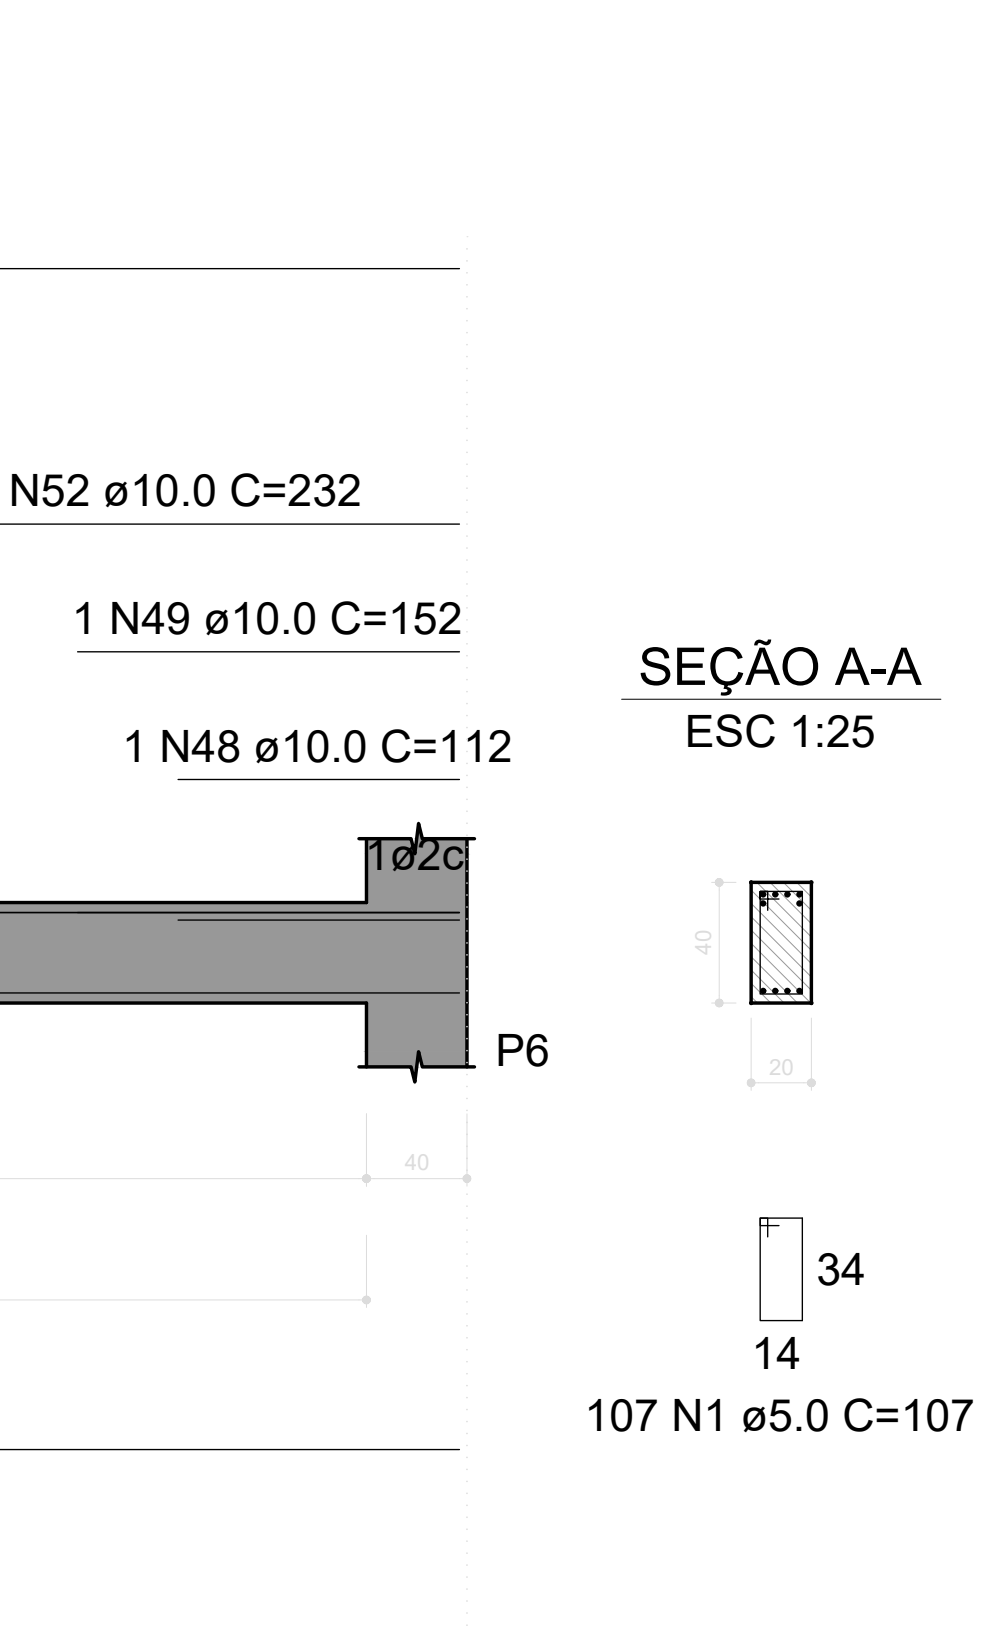
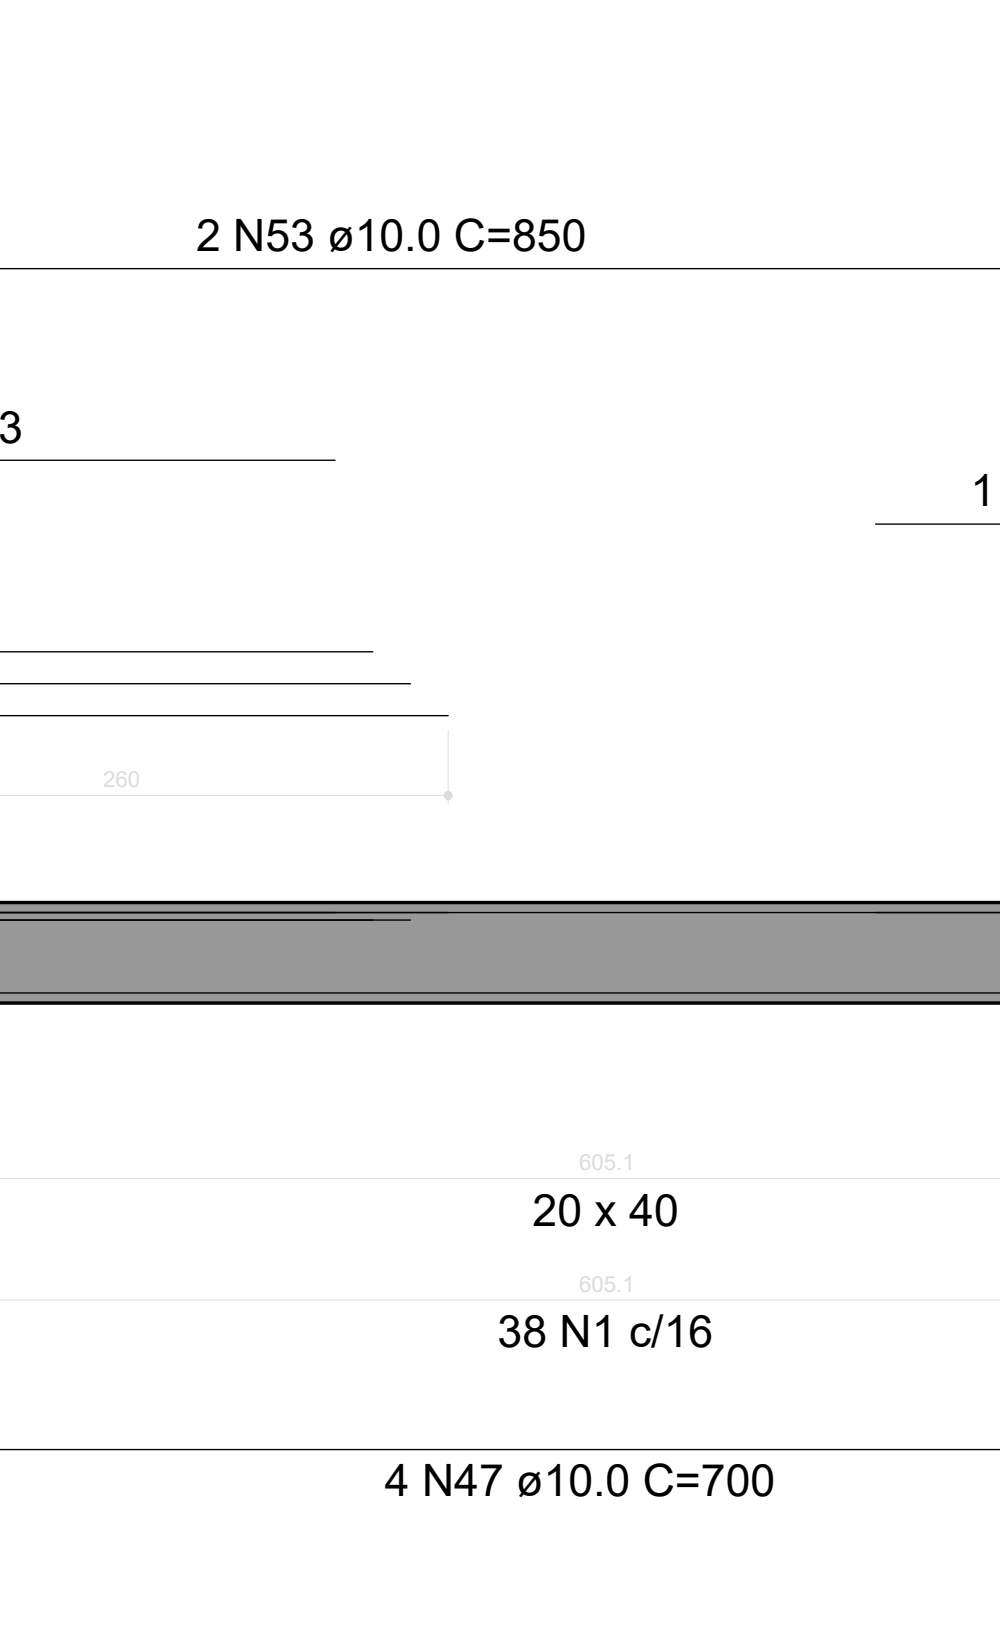
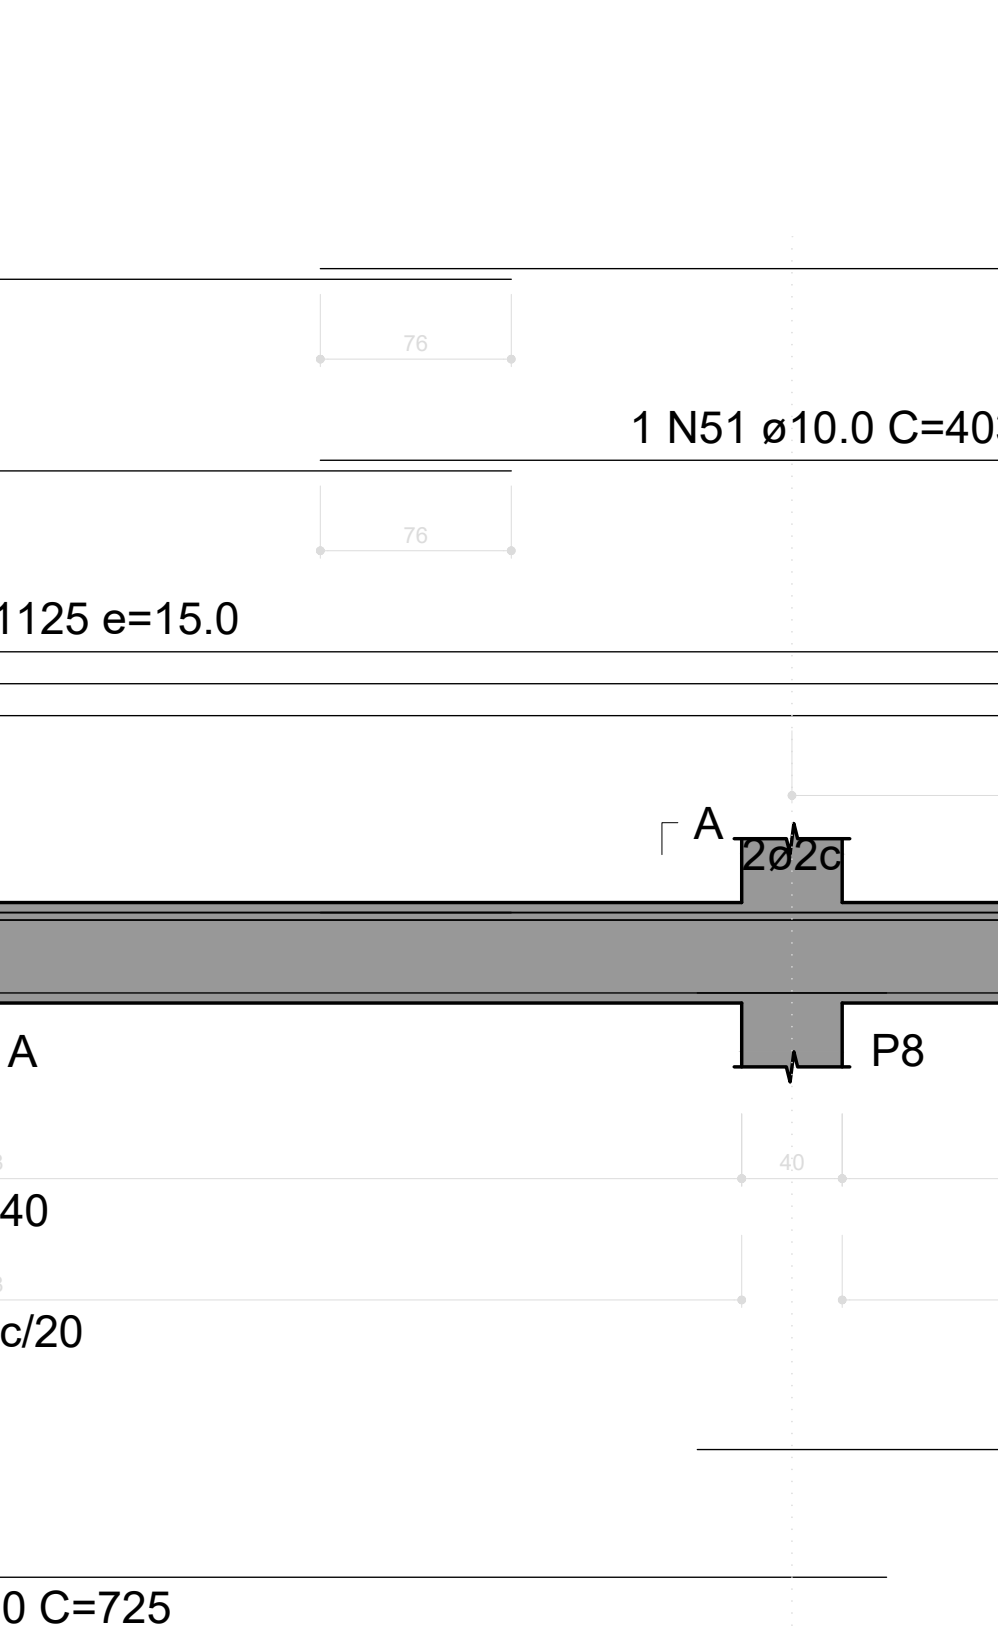


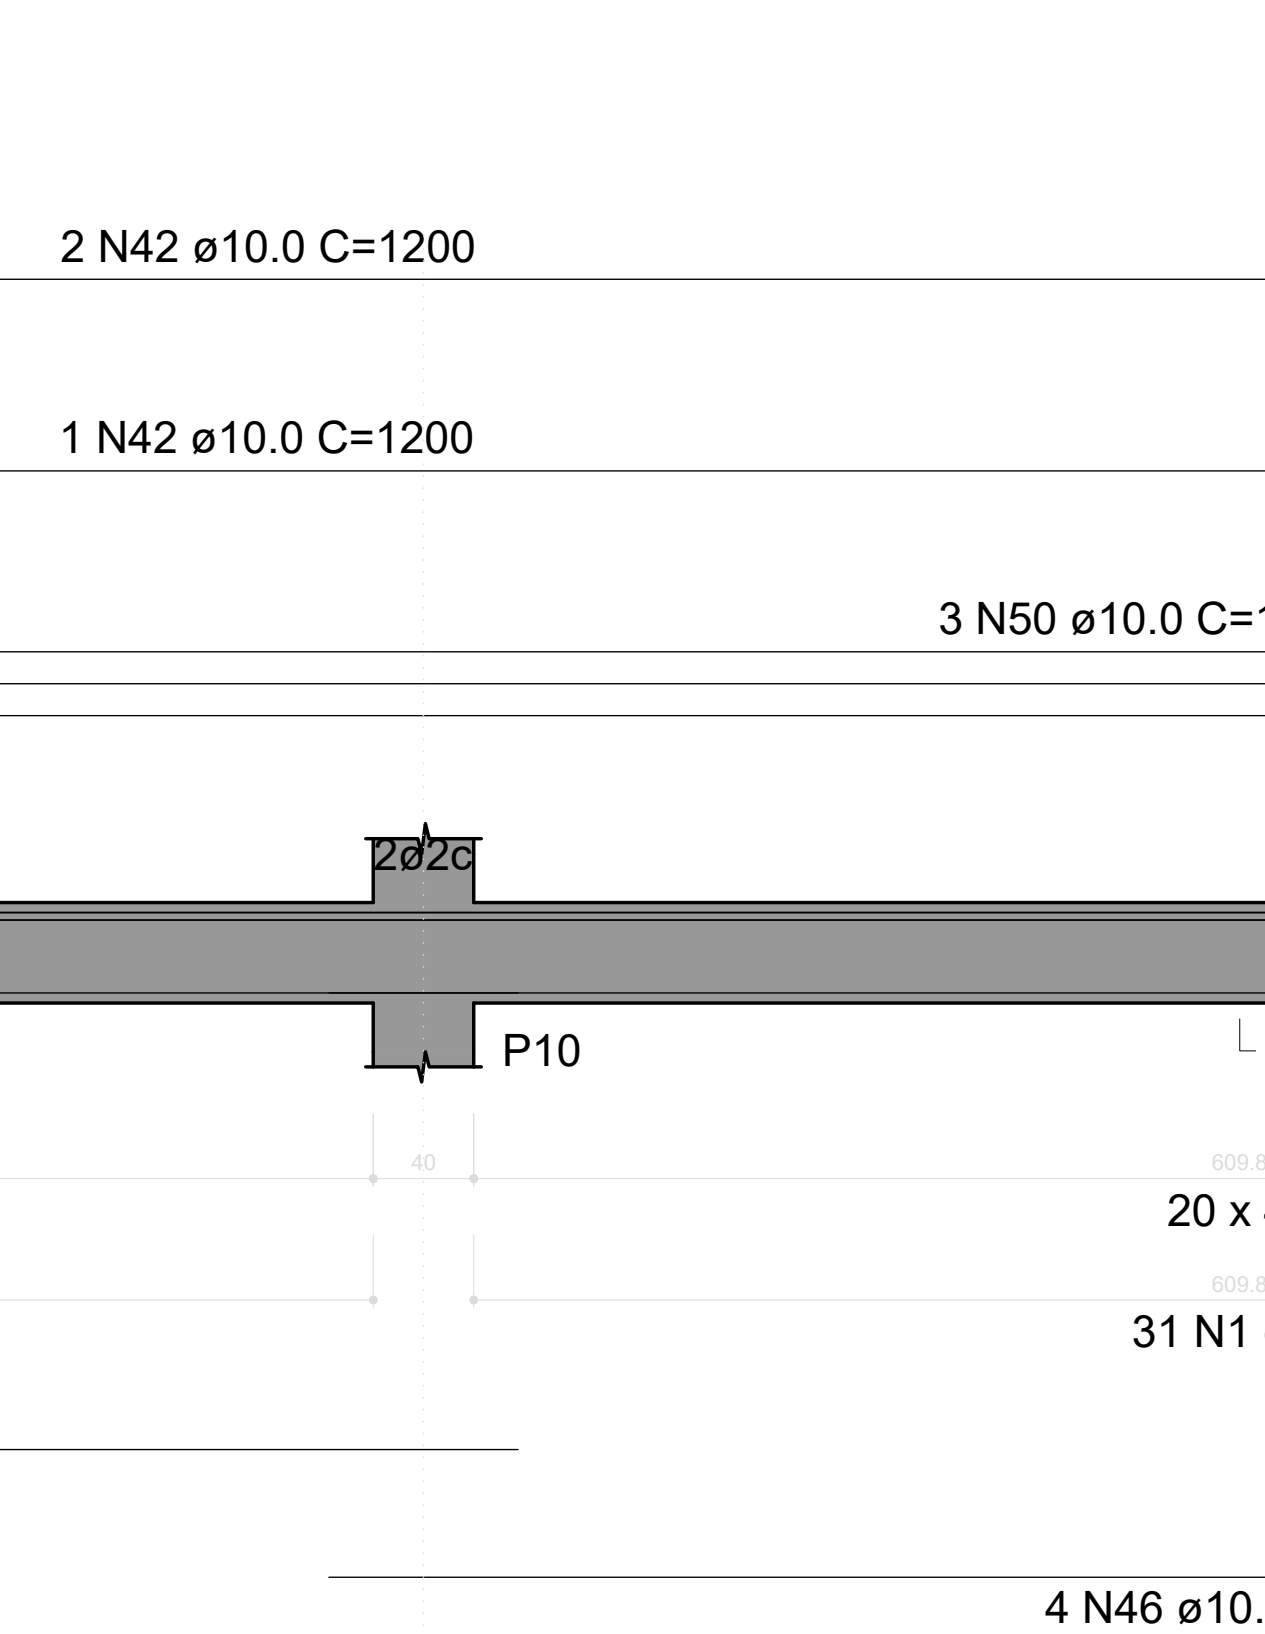

RELAÇÃO DO AÇO

AÇO	N	DIAM (mm)	QUANT	C.UNIT (cm)	C.TOTAL (cm)
V1	1	5.0	477	107	51039
V4	2	5.0	162	67	10854
V7	3	5.0	164	57	9348
V10	4	5.0	34	47	1598
V13	5	6.3	2	76	152
	6	8.0	2	604	1208
	7	8.0	2	655	1310
	8	8.0	1	590	590
	9	8.0	1	227	227
	10	8.0	2	1163	2326
	11	8.0	1	175	175
	12	8.0	1	160	160
	13	8.0	2	1016	2032
	14	8.0	1	760	760
	15	8.0	2	617	1234
	16	8.0	2	449	898
	17	8.0	1	109	109
	18	8.0	2	463	926
	19	8.0	4	264	1056
	20	8.0	4	289	1156
	21	8.0	2	450	900
	22	8.0	2	472	944
	23	8.0	4	132	528
	24	8.0	2	160	320
	25	8.0	2	159	318
	26	8.0	2	191	382
	27	8.0	1	81	81
	28	8.0	4	304	1216
	29	8.0	2	180	360
	30	8.0	1	229	229
	31	8.0	2	329	658
	32	8.0	2	322	644
	33	8.0	2	167	334
	34	8.0	1	97	97
	35	8.0	2	175	350
	36	8.0	2	146	292
	37	10.0	2	1084	2168
	38	10.0	2	178	356
	39	10.0	2	1025	2050
	40	10.0	2	590	1180
	41	10.0	4	1198	4792
	42	10.0	10	1200	12000
	43	10.0	2	496	992
	44	10.0	2	509	1018
	45	10.0	8	700	5600
	46	10.0	8	725	5800
	47	10.0	8	700	5600
	48	10.0	4	112	448
	49	10.0	4	152	608
	50	10.0	6	1125	6750
	51	10.0	2	403	806
	52	10.0	2	232	464
	53	10.0	4	850	3400
	54	10.0	2	109	218

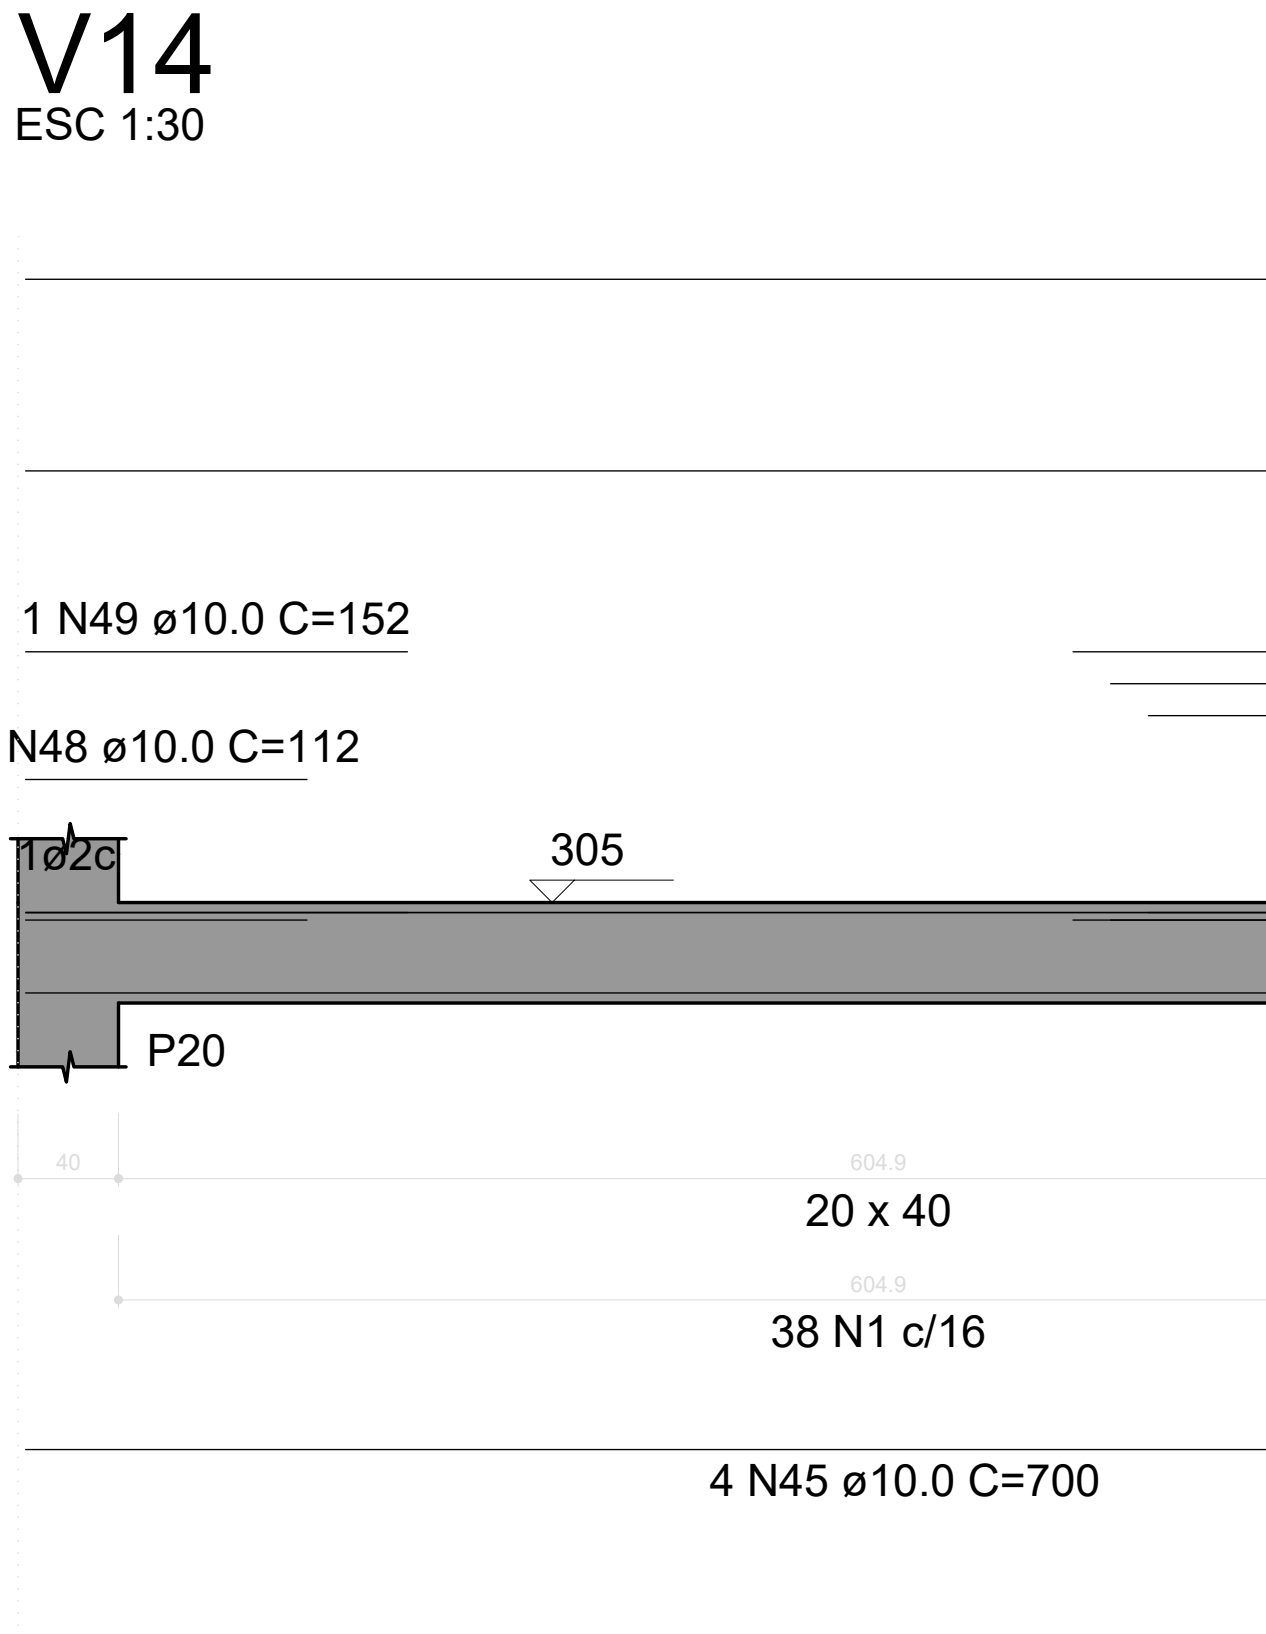

RESUMO DO AÇO

AÇO	DIAM (mm)	C.TOTAL (m)	PESO + 10% (kg)
CA50	6.3	1.5	0.4
	8.0	218.2	94.7
	10.0	542.5	367.9
CA60	5.0	728.4	123.5
PESO TOTAL (kg)			
CA50	463		
CA60	123.5		

Volume de concreto (C-25) = 8.58 m³
Área de forma = 111.05 m²

PROPRIETÁRIO: PREFEITURA MUNICIPAL DE COREMAS - PB

PROJETO: LINCOLN CARTAXO DE LIRA JÚNIOR CREA 160.814.689-8

CONSTRUÇÃO:

FOLHA: 18/26
PROJETO: CONSTRUÇÃO DE GINÁSIO POLIESPORTIVO - ESTRUTURAL
CONVENIENTE: PREFEITURA MUNICIPAL DE COREMAS - PB
CONVENIADO: MUNICÍPIO DE COREMAS - PB
LOCALIDADE: COREMAS - PB

DATA	RESPONSÁVEL	RUBRICA	DADOS
AGO/2025	LINCOLN CARTAXO		

DESENHO	DESENHOS	CONVÊNIO
CÓPIA		
VISTO		
ESCALAS	Indicada	GOVERNO DO ESTADO
		ARQUIVO

Aprovações: