

LAJE - L3

SEÇÃO
ESC 1:20

20

40

VISTA H


34

295

VISTA B


14

2 N1 ø5.0 C=107



47

10
4 N11 ø12.5 C=57



2 N1 ø5

*OBS.: OS QUADROS RESUMO REFERENTES A
ESTA PRANCHA CONSTAM NA PRANCHA 21/26

PROPRIETÁRIO: PREFEITURA MUNICIPAL DE COREMAS - PB

PROJETO: LINCOLN CARTAXO DE LIRA JÚNIOR CREA 160.814.689-8

CONSTRUÇÃO:

19/26

FOLHA

PROJETO:

CONSTRUÇÃO DE GINÁSIO POLIESPORTIVO - ESTRUTURAL

CONVENIENTE:

PREFEITURA MUNICIPAL DE COREMAS - PB

CONVENIADO:

MUNICÍPIO DE COREMAS - PB

LOCALIDADE:

COREMAS - PB

	DATA	RESPONSÁVEL	RUBRICA	DADOS
DESENHO	AGO/2025	LINCOLN CARTAXO		
CÓPIA				
VISTO				
ESCALAS	DESENHOS			CONVÊNIO
Indicada	- ARMADURAS DOS PILARES PAV. LAJE (NÍVEL 305)			GOVERNO DO ESTADO
				ARQUIVO

Aprovações: