



P11=P12=P21=P22

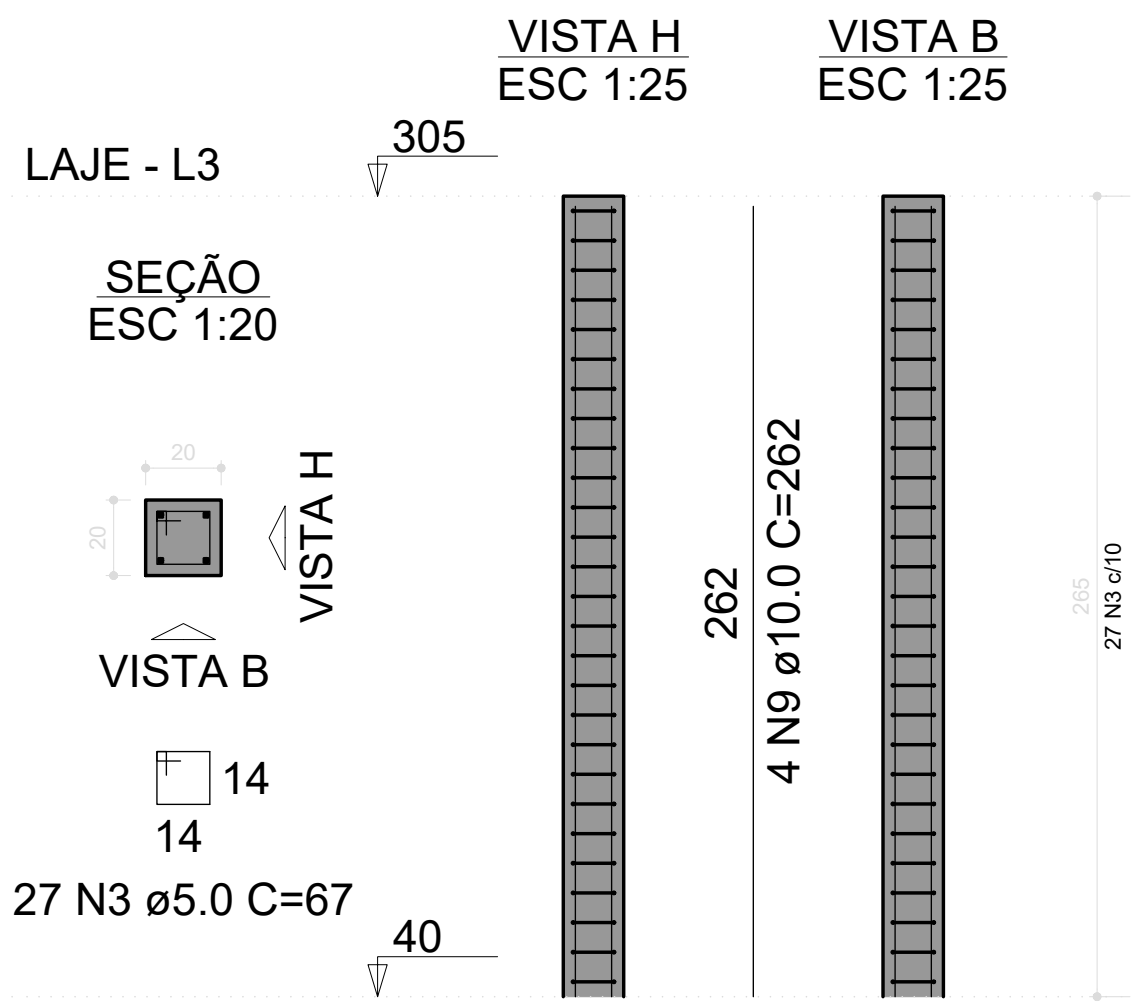

P15=P18

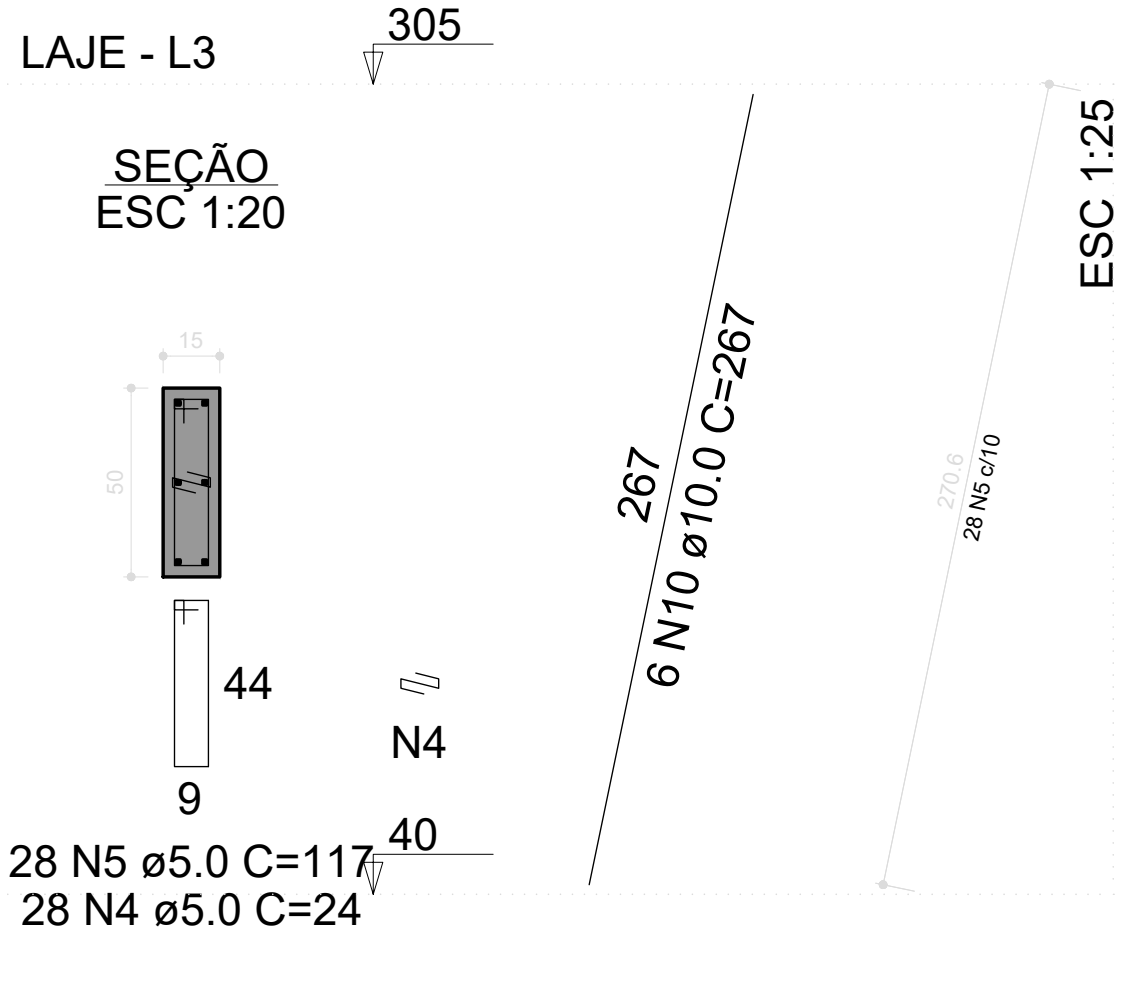


RELAÇÃO DO AÇO					
AÇO	N	DIAM (mm)	QUANT	C.UNIT (cm)	C.TOTAL (cm)
CA60	1	5.0	305	107	32635
	2	5.0	573	29	16617
	3	5.0	108	67	7236
	4	5.0	56	24	1344
CA50	5	5.0	56	117	6552
	6	10.0	18	48	864
	7	10.0	30	303	9090
	8	10.0	6	75	450
	9	10.0	96	262	25152
	10	10.0	12	267	3204
	11	12.5	4	57	228
	12	12.5	12	312	3744
	13	16.0	40	121	4840


RESUMO DO AÇO			
AÇO	DIAM (mm)	C.TOTAL (m)	PESO + 10% (kg)
CA50	10.0	387.6	262.9
	12.5	39.7	42.1
	16.0	48.4	84
CA60	5.0	643.8	109.2
PESO TOTAL (kg)			
CA50	389		
CA60	109.2		

Volume de concreto (C-25) = 3.41 m³
Área de forma = 54.16 m²


P5=P14=P16=P17=P19

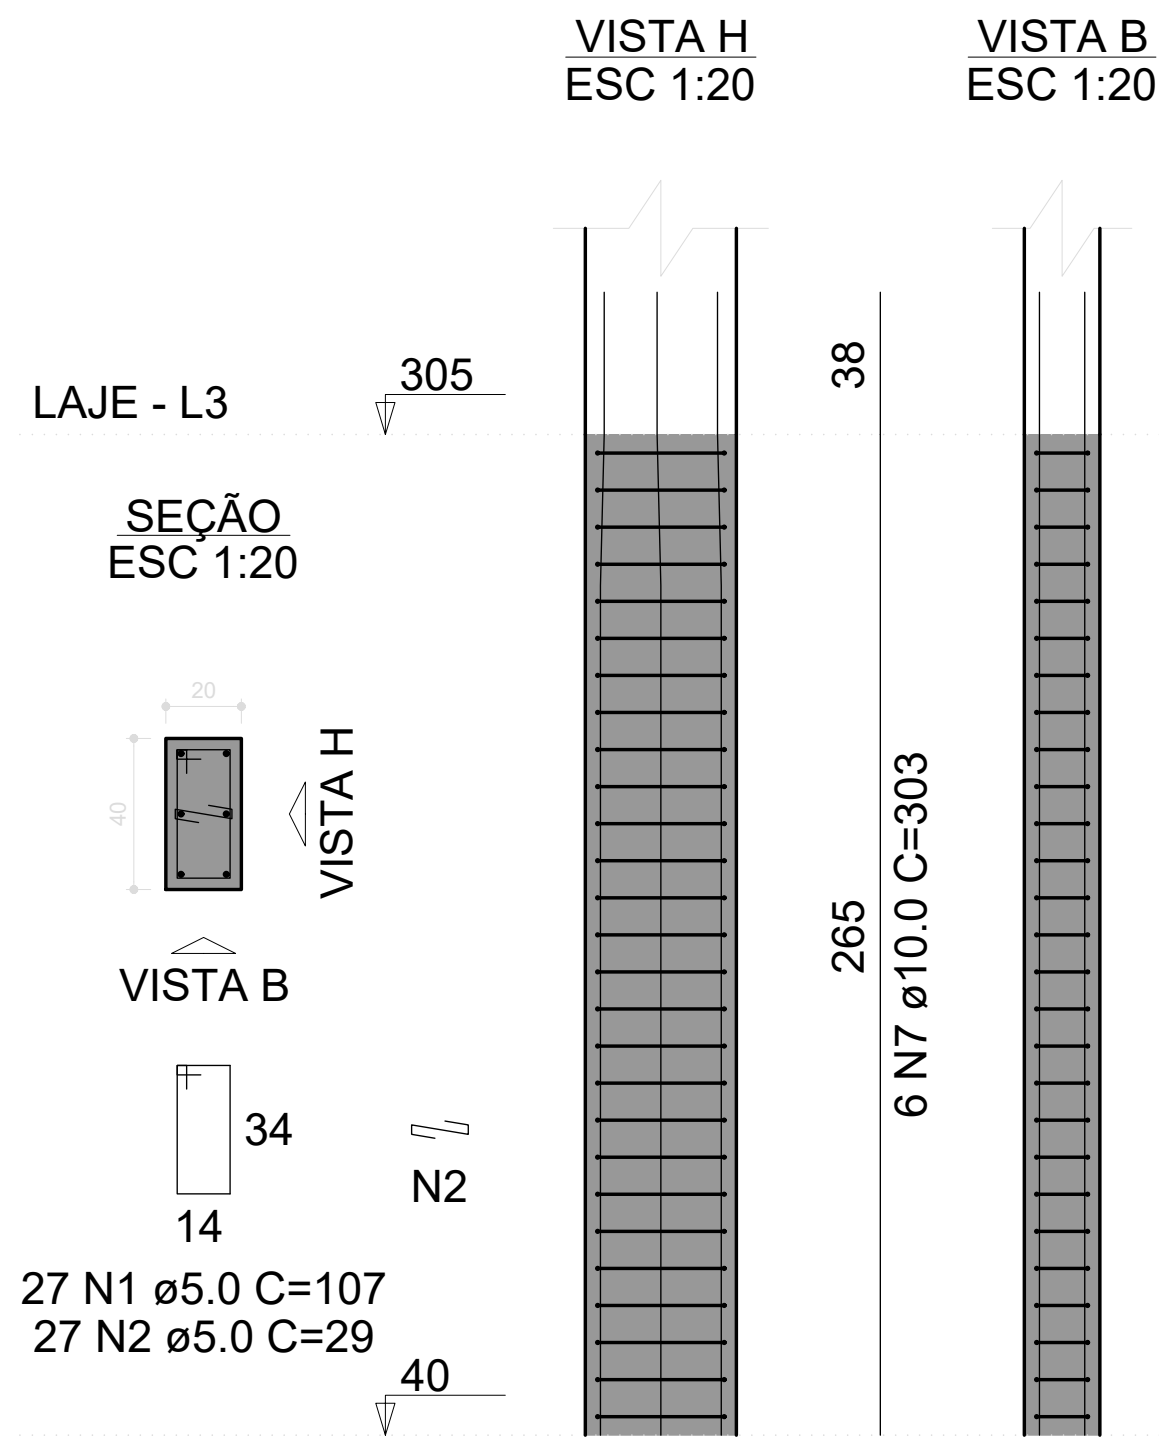

P6=P13=P20

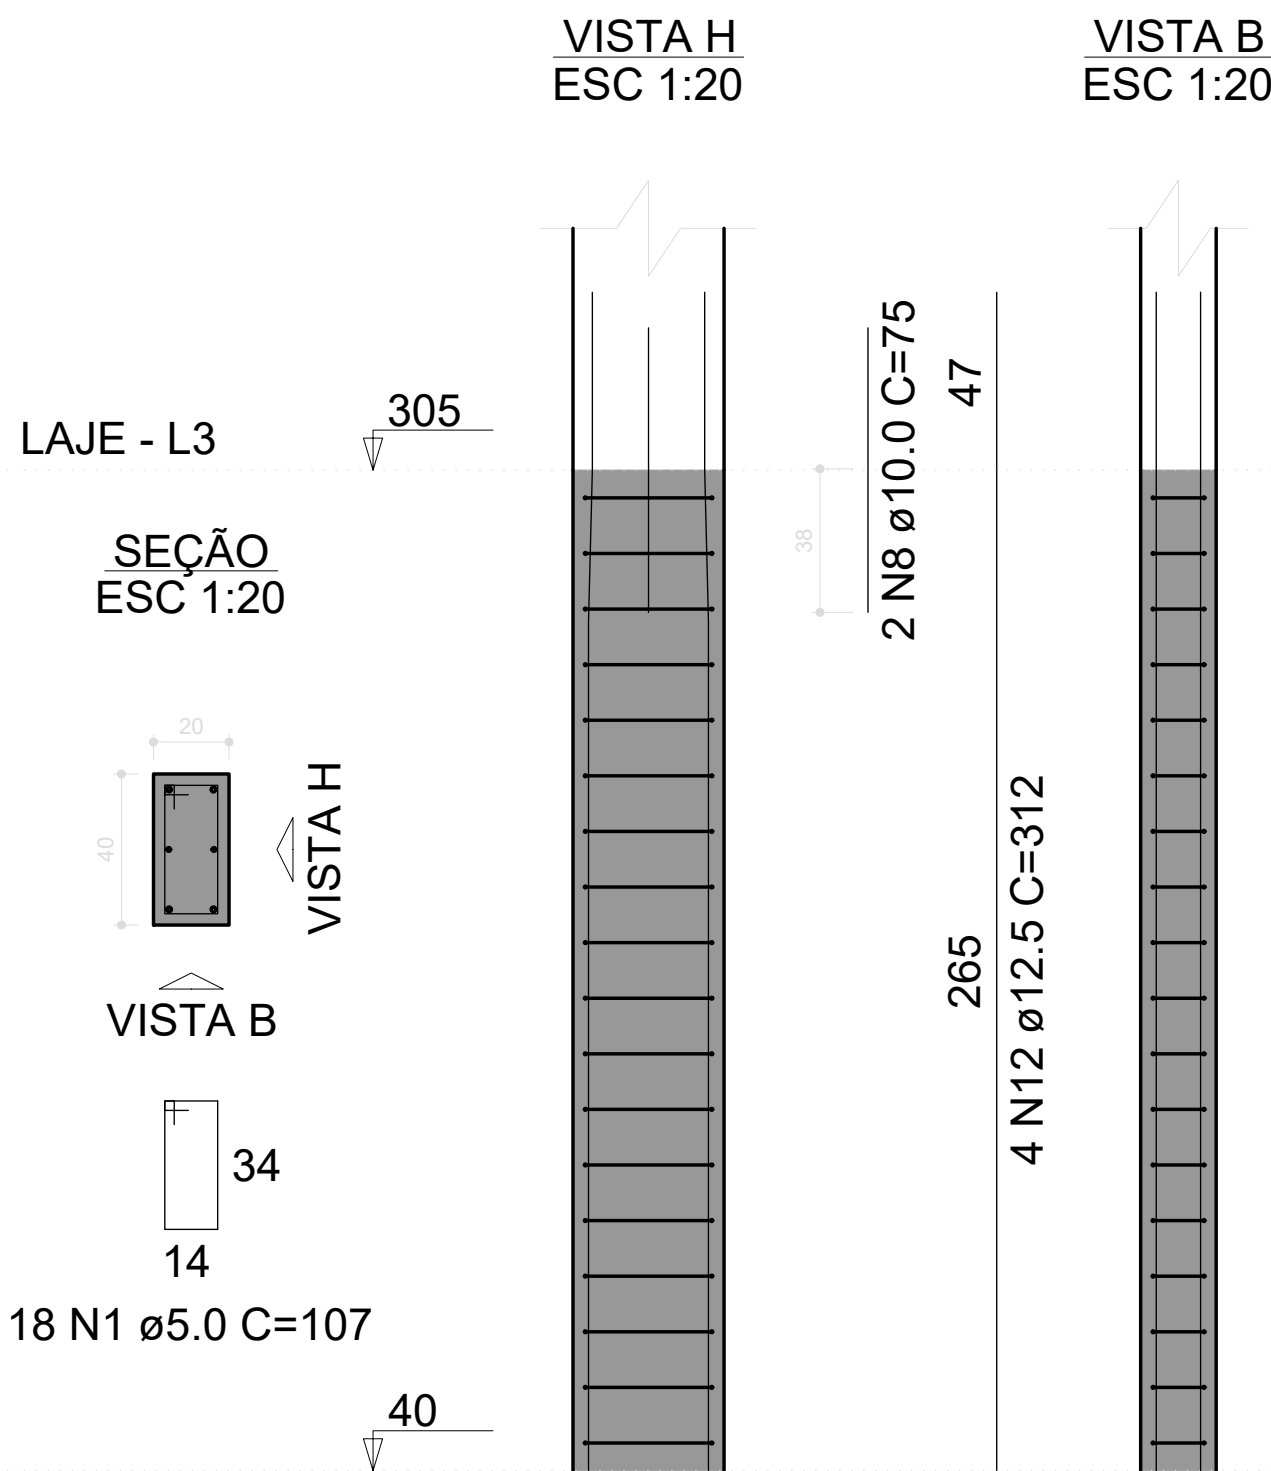

P7=P8=P9=P10

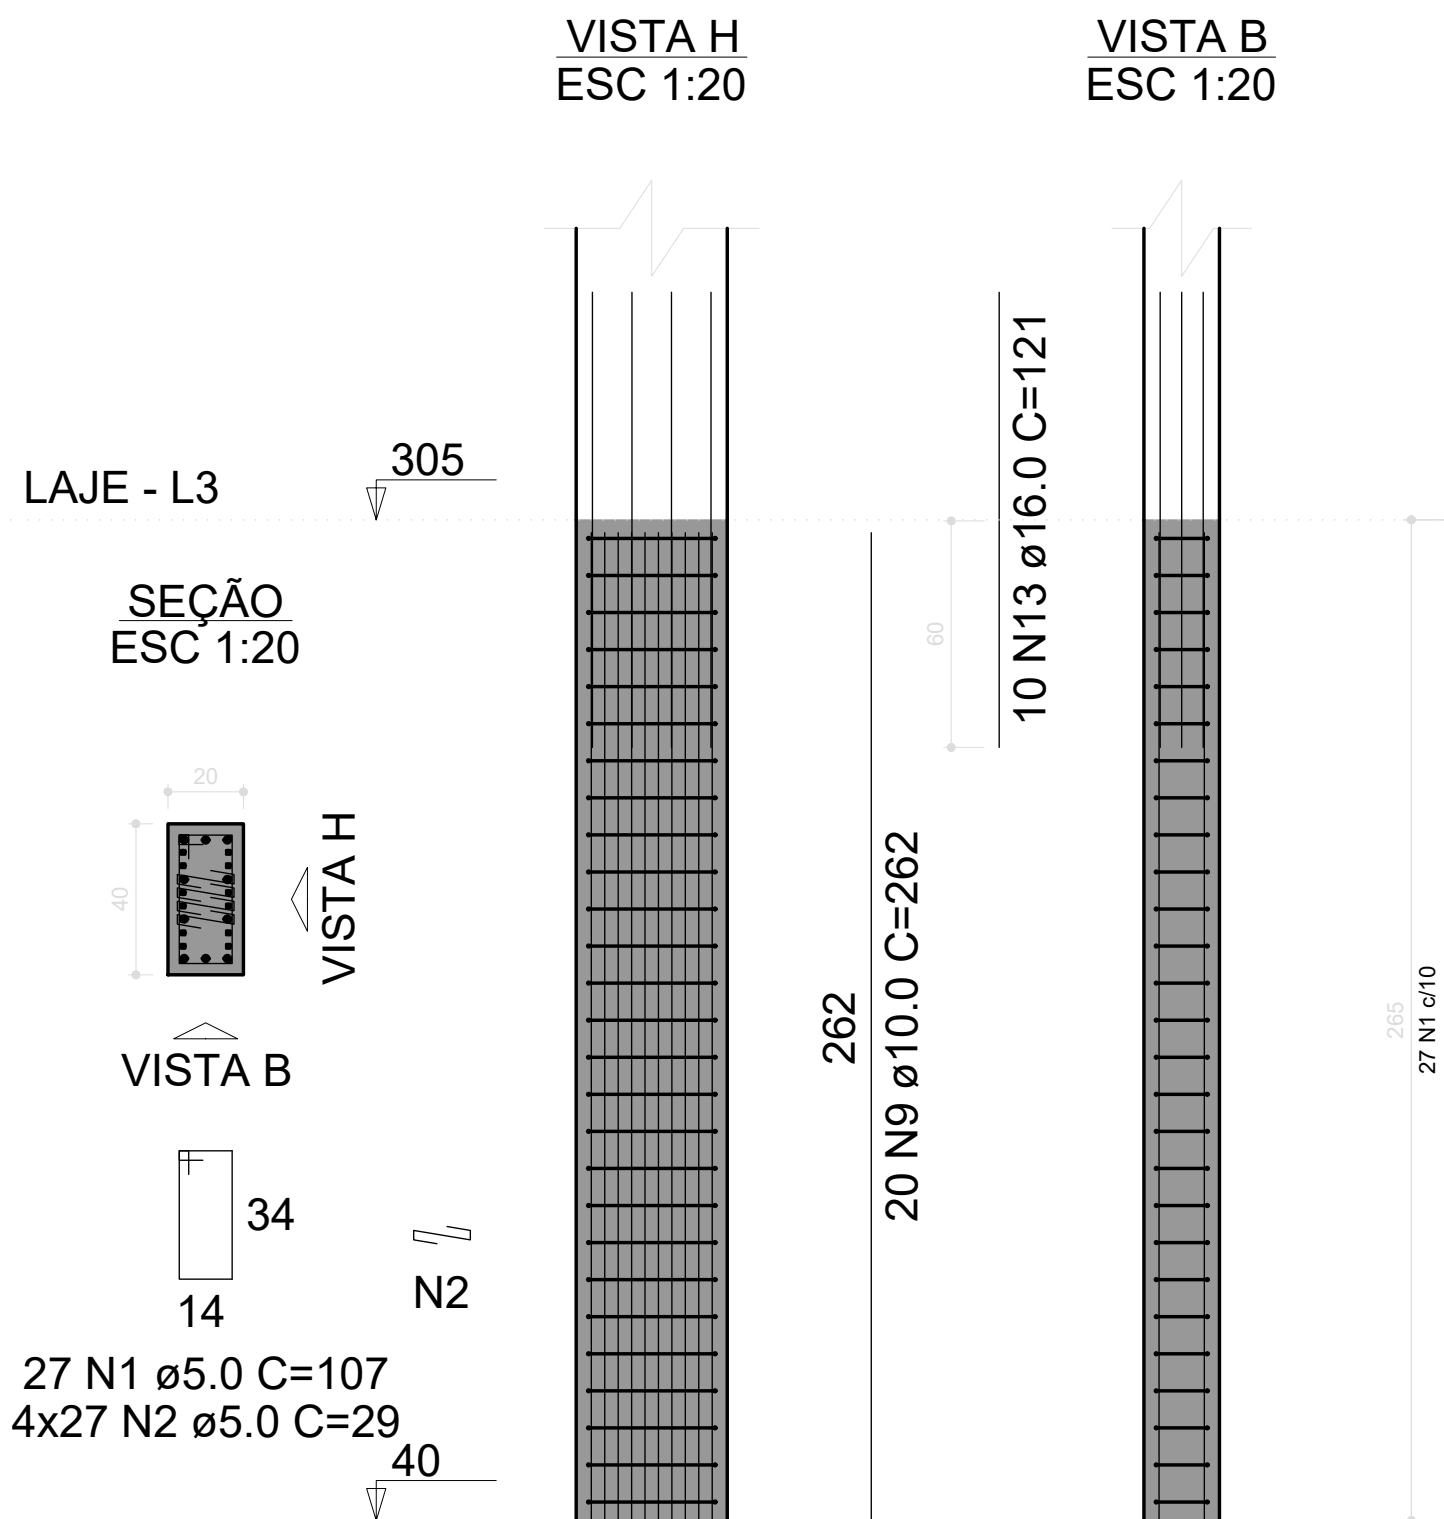

PROPRIETÁRIO: PREFEITURA MUNICIPAL DE COREMAS - PB

LINCOLN CARTAXO DE LIRA JUNIOR:06897861405

Assinado de forma digital por LINCOLN CARTAXO DE LIRA JUNIOR:06897861405
Dados: 2025.08.08 12:26:28 -03'00'

PROJETO: LINCOLN CARTAXO DE LIRA JÚNIOR CREA 160.814.689-8

CONSTRUÇÃO:

FOLHA 21/26

PROJETO: CONSTRUÇÃO DE GINÁSIO POLIESPORTIVO - ESTRUTURAL

CONVENIENTE: PREFEITURA MUNICIPAL DE COREMAS - PB

CONVENIADO: MUNICÍPIO DE COREMAS - PB

LOCALIDADE: COREMAS - PB

DESENHO	DATA	RESPONSÁVEL	RUBRICA	DADOS
CÓPIA	AGO/2025	LINCOLN CARTAXO		
VISTO				

ESCALAS	DESENHOS	CONVÊNIO
Indicada	- ARMADURAS DOS PILARES PAV. LAJE (NÍVEL 305)	GOVERNO DO ESTADO
		ARQUIVO

Aprovações:

LCL PROJETOS

Av. Gov. Flávio Ribeiro Coutinho, 500, sl. 601
Jardim Oceania, 58037-005 - João Pessoa (PB)
Tel +55 (83) 99924.4447
e-mail: contato@lclprojetos.com