


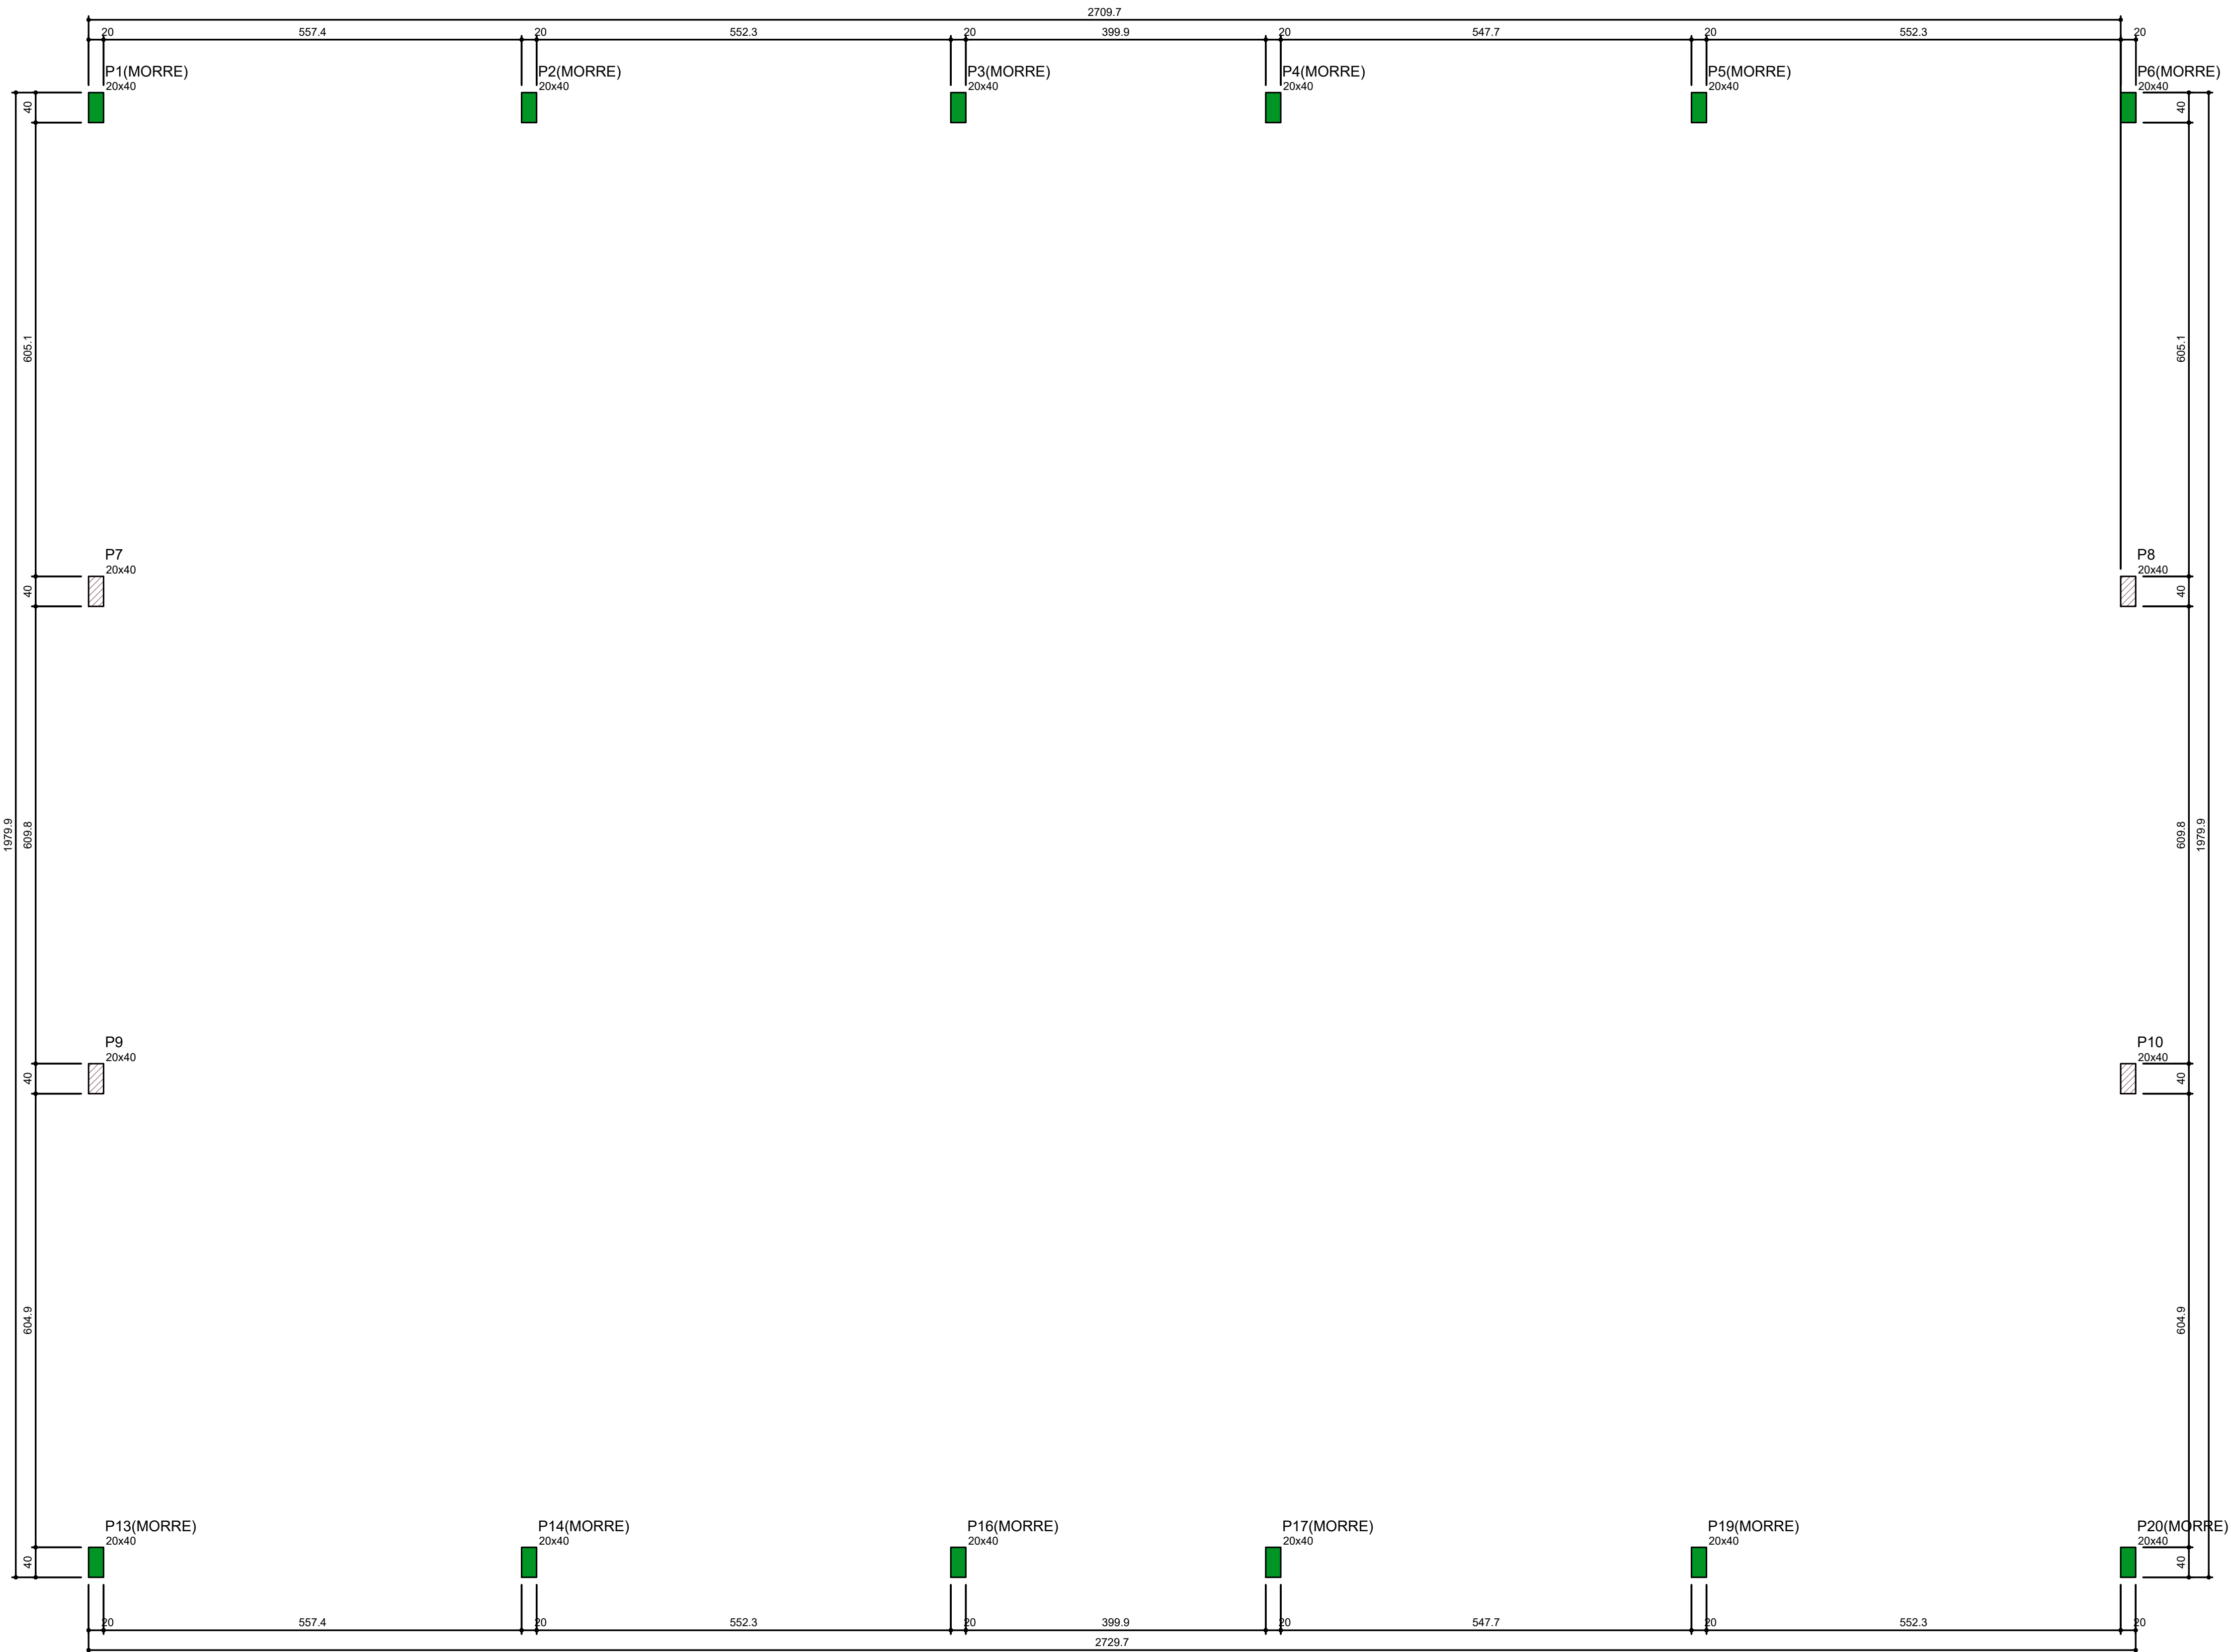

Características dos materiais	
fck (kgf/cm²)	Ecs (kgf/cm³)
250	241500

Pilares			
Nome	Seção (cm)	Elevação (cm)	Nível (cm)
P1	20x40	0	330
P2	20x40	0	330
P3	20x40	0	330
P4	20x40	0	330
P5	20x40	0	330
P6	20x40	0	330
P7	20x40	0	330
P8	20x40	0	330
P9	20x40	0	330
P10	20x40	0	330
P13	20x40	0	330
P14	20x40	0	330
P16	20x40	0	330
P17	20x40	0	330
P19	20x40	0	330
P20	20x40	0	330

Legenda dos pilares	
	Pilar que morre
	Pilar que passa

Forma do pavimento Térreo (Nível 330)
escala 1:50

PROPRIETÁRIO: PREFEITURA MUNICIPAL DE COREMAS - PB

PROJETO: LINCOLN CARTAXO DE LIRA JÚNIOR CREA 160.814.689-8

CONSTRUÇÃO:

FOLHA 23/26
PROJETO: CONSTRUÇÃO DE GINÁSIO POLIESPORTIVO - ESTRUTURAL
CONVENIENTE: PREFEITURA MUNICIPAL DE COREMAS - PB
CONVENIADO: MUNICÍPIO DE COREMAS - PB
LOCALIDADE: COREMAS - PB

DESENHO	DATA	RESPONSÁVEL	RUBRICA	DADOS
CÓPIA	AGO/2025	LINCOLN CARTAXO		
VISTO				
ESCALAS	DESENHOS			CONVÊNIO
Indicada	- FORMA DO PAVIMENTO TÉRREO (NÍVEL 330)			GOVERNO DO ESTADO
				ARQUIVO

Aprovações: