



P1=P2=P3=P4

TÉRREO - L4

SEÇÃO
ESC 1:20

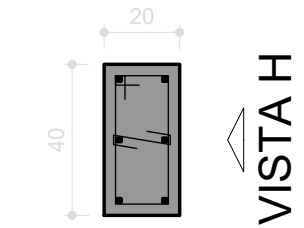


VISTA B

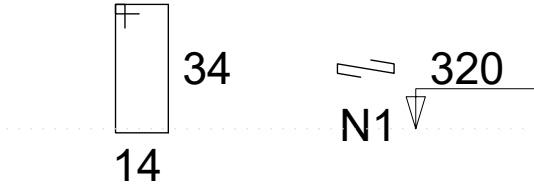

2 N2 ø5.0 C=107
2 N1 ø5.0 C=29

VISTA H
ESC 1:1

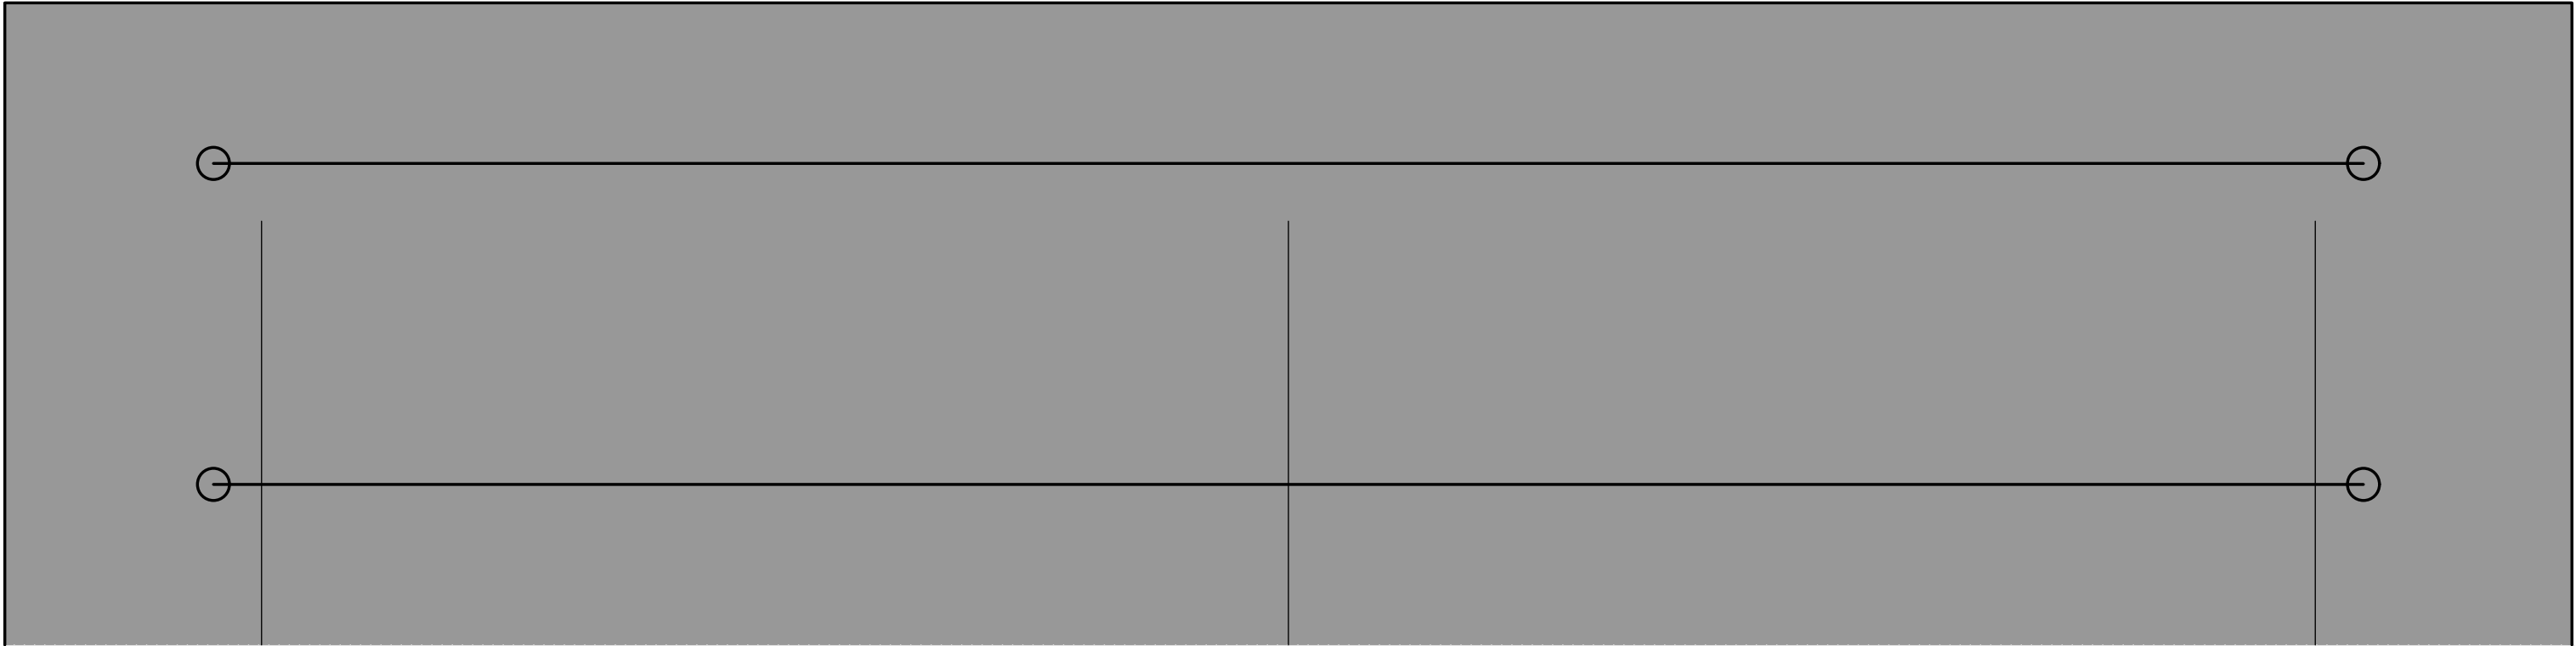

7
6 N4 ø10.0 C=7

VISTA B
ESC 1:1




10
2 N2 ø5


P5=P6=P13=P14=P16=P17=P19=P20

TÉRREO - L4

SEÇÃO
ESC 1:20

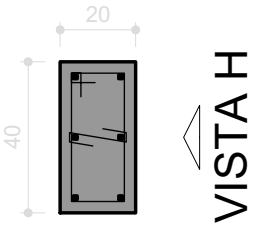


VISTA B

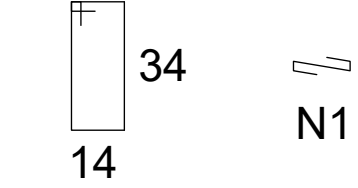


3 N2 ø5.0 C=107
3 N1 ø5.0 C=29

VISTA H
ESC 1:2

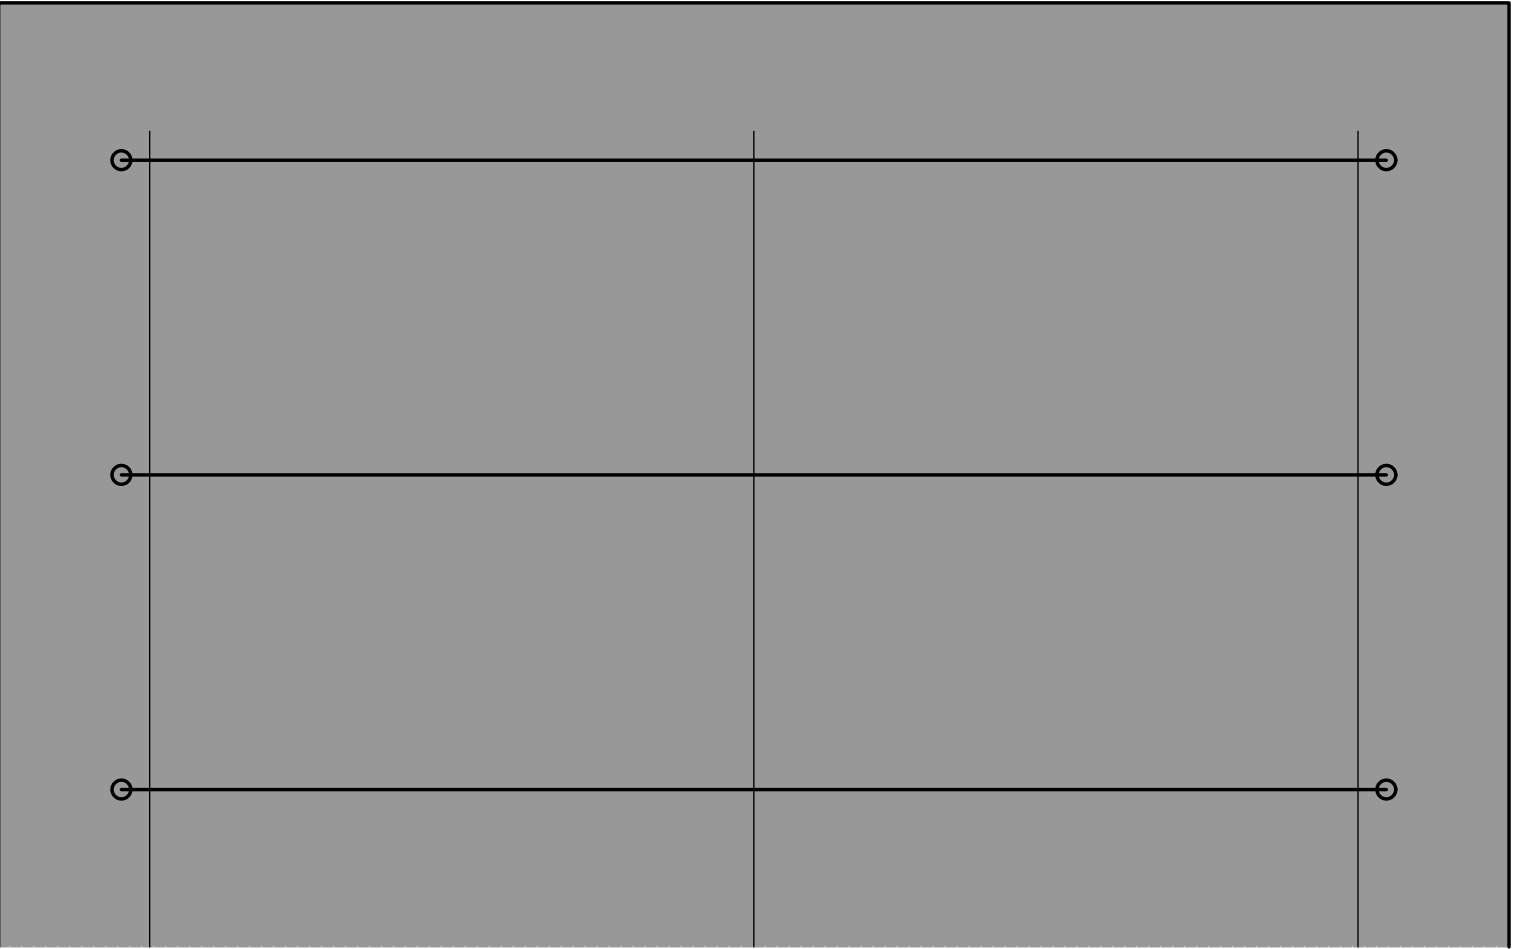

22
6 N5 ø10.0 C=22

VISTA B
ESC 1:2

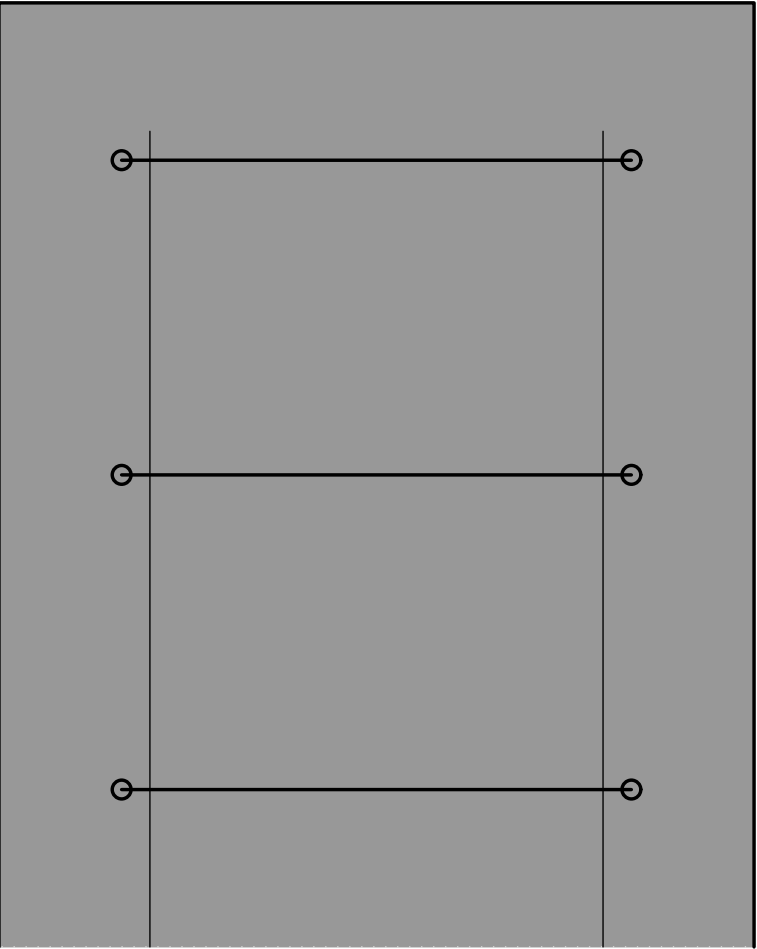

25
3 N2 ø10

*OBS.: OS QUADROS RESUMO REFERENTES A
ESTA PRANCHA CONSTAM NA PRANCHA 25/26

PROPRIETÁRIO: PREFEITURA MUNICIPAL DE COREMAS - PB

PROJETO: LINCOLN CARTAXO DE LIRA JÚNIOR CREA 160.814.689-8

CONSTRUÇÃO:

FOLHA 24/26	PROJETO: CONSTRUÇÃO DE GINÁSIO POLIESPORTIVO - ESTRUTURAL			
	CONVENIENTE: PREFEITURA MUNICIPAL DE COREMAS - PB			
	CONVENIADO: MUNICÍPIO DE COREMAS - PB			
	LOCALIDADE: COREMAS - PB			
DESENHO	DATA	RESPONSÁVEL	RUBRICA	DADOS
CÓPIA	AGO/2025	LINCOLN CARTAXO		
VISTO				
ESCALAS	DESENHOS			CONVÊNIO
	Indicada			GOVERNO DO ESTADO
				ARQUIVO

Aprovações:

 **LCL PROJETOS**

Av. Gov. Flávio Ribeiro Coutinho, 500, sl. 601
Jardim Oceania, 58037-005 - João Pessoa (PB)
Tel. +55 (83) 99924.4447
e-mail: contato@lclprojetos.com