



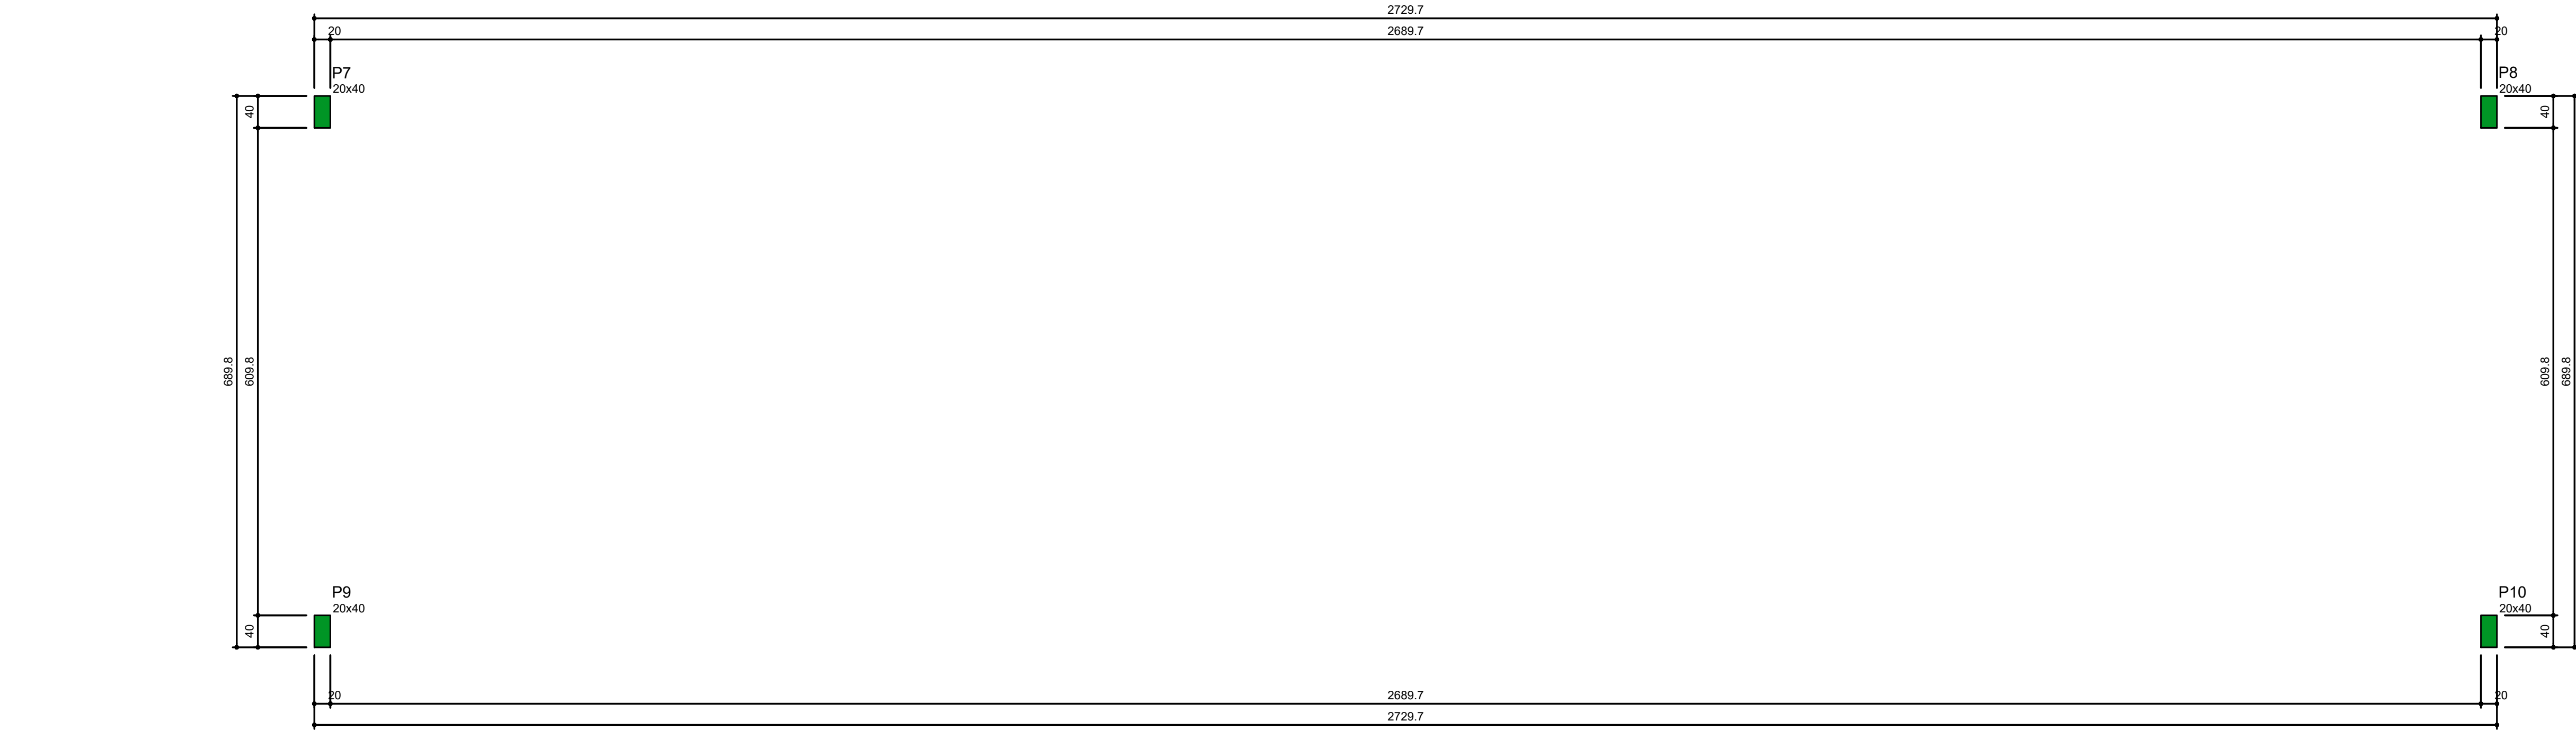

Forma do pavimento Pilares testada (Nível 830)
escala 1:50

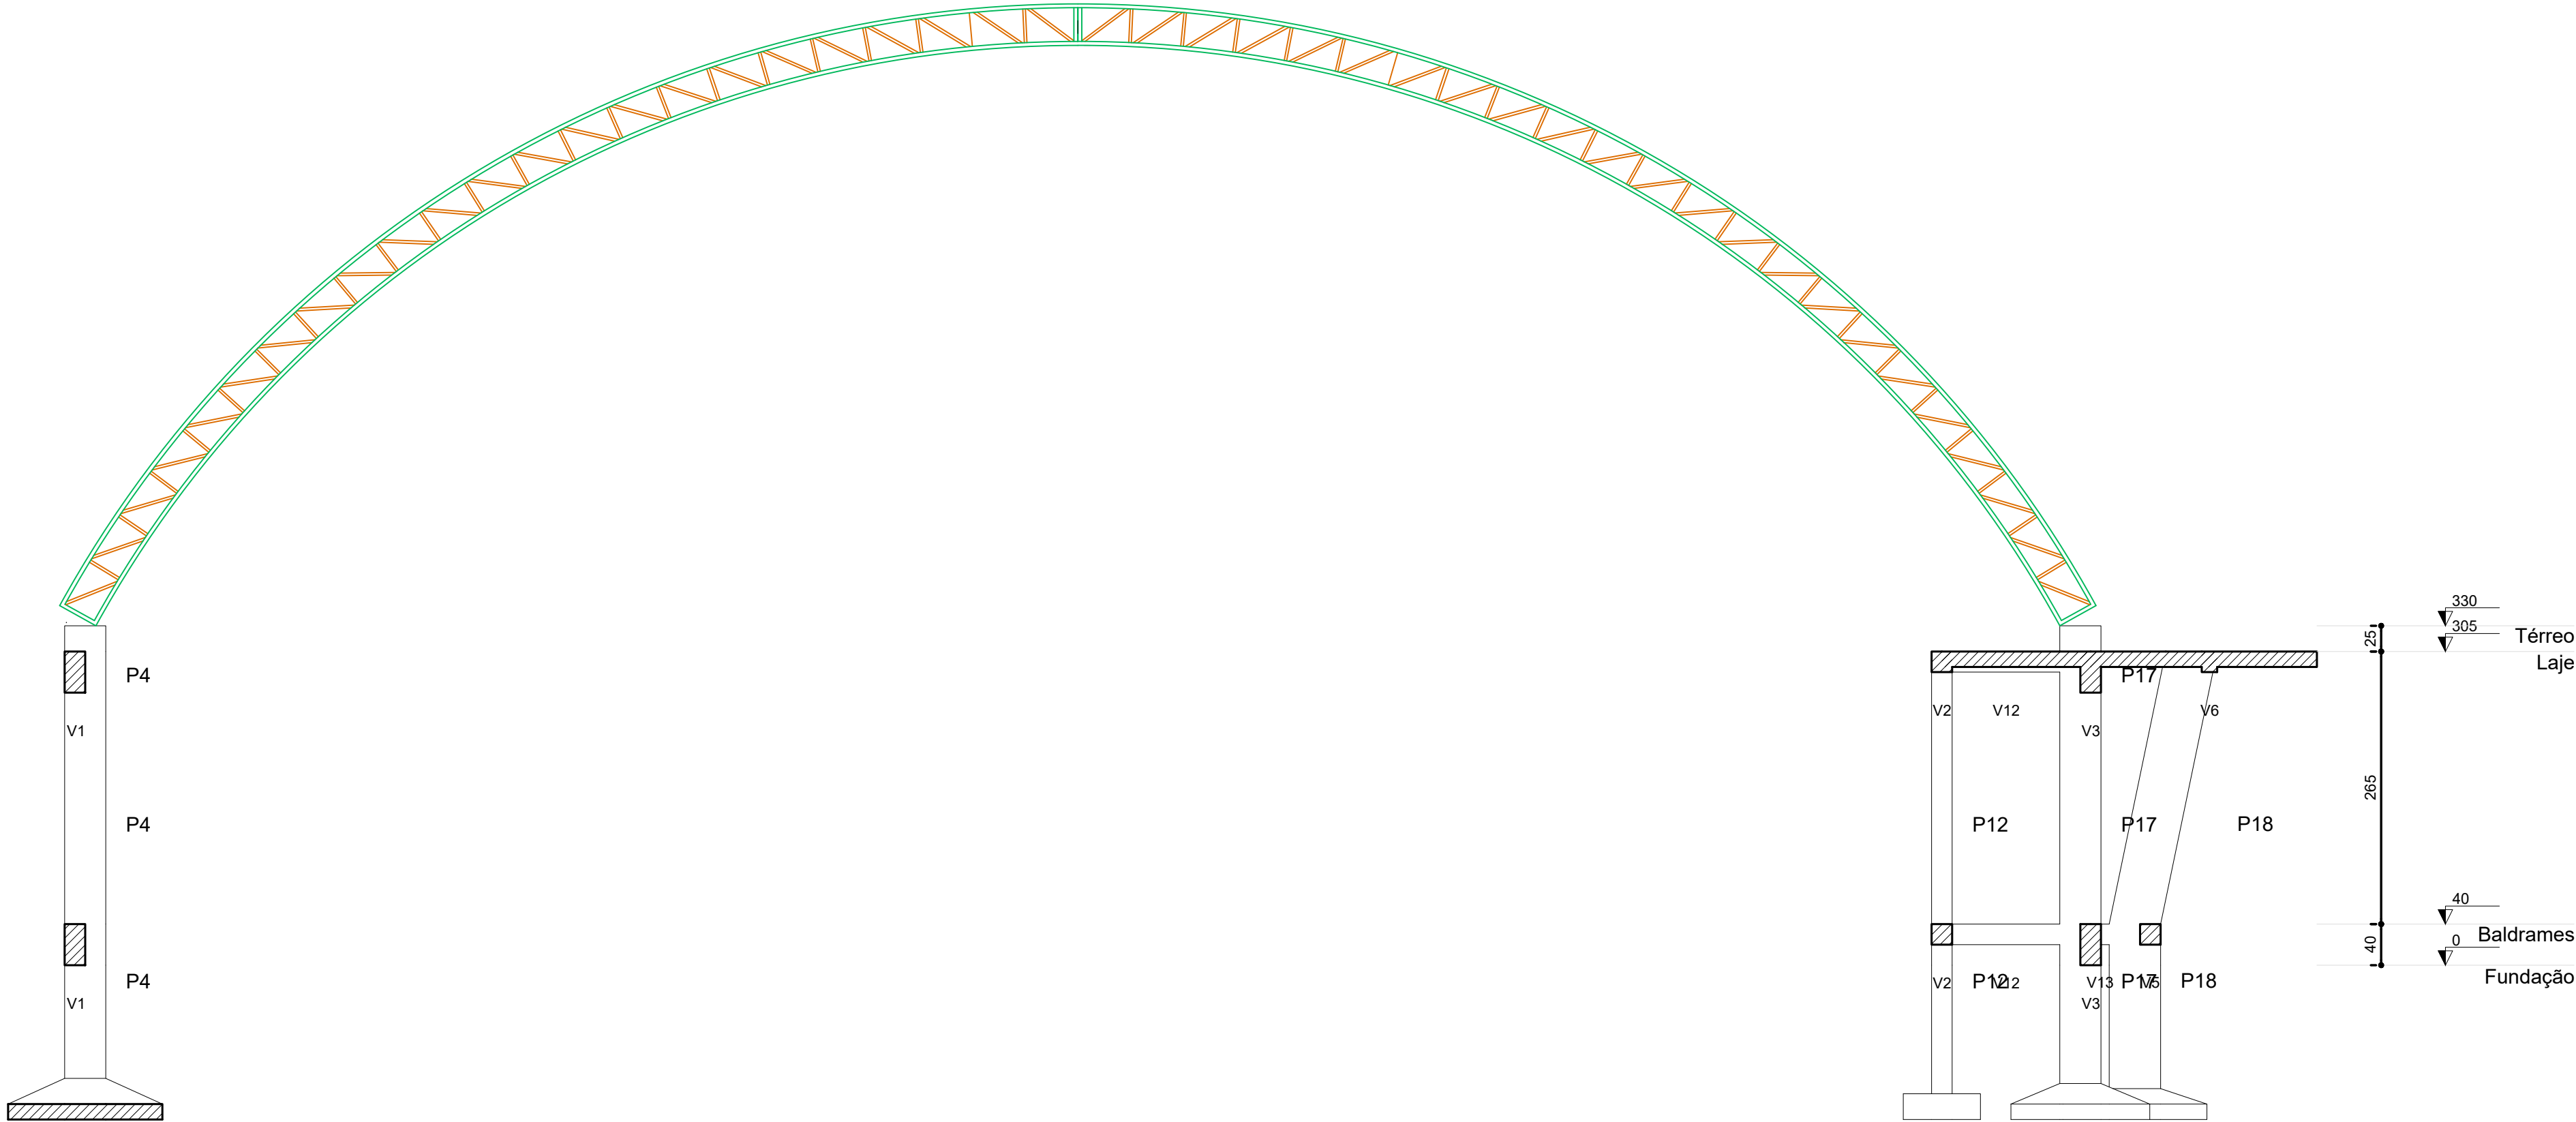


Corte A-A
escala 1:50


P7=P8=P9=P10

PILARES TESTADA - L5

SEÇÃO
ESC 1:20

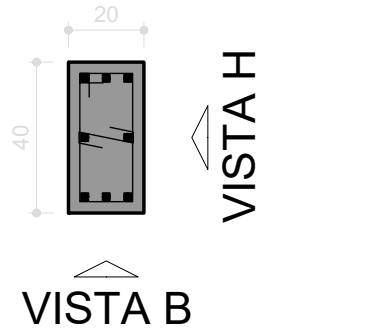

29 N2 ø5.0 C=107
29 N1 ø5.0 C=29

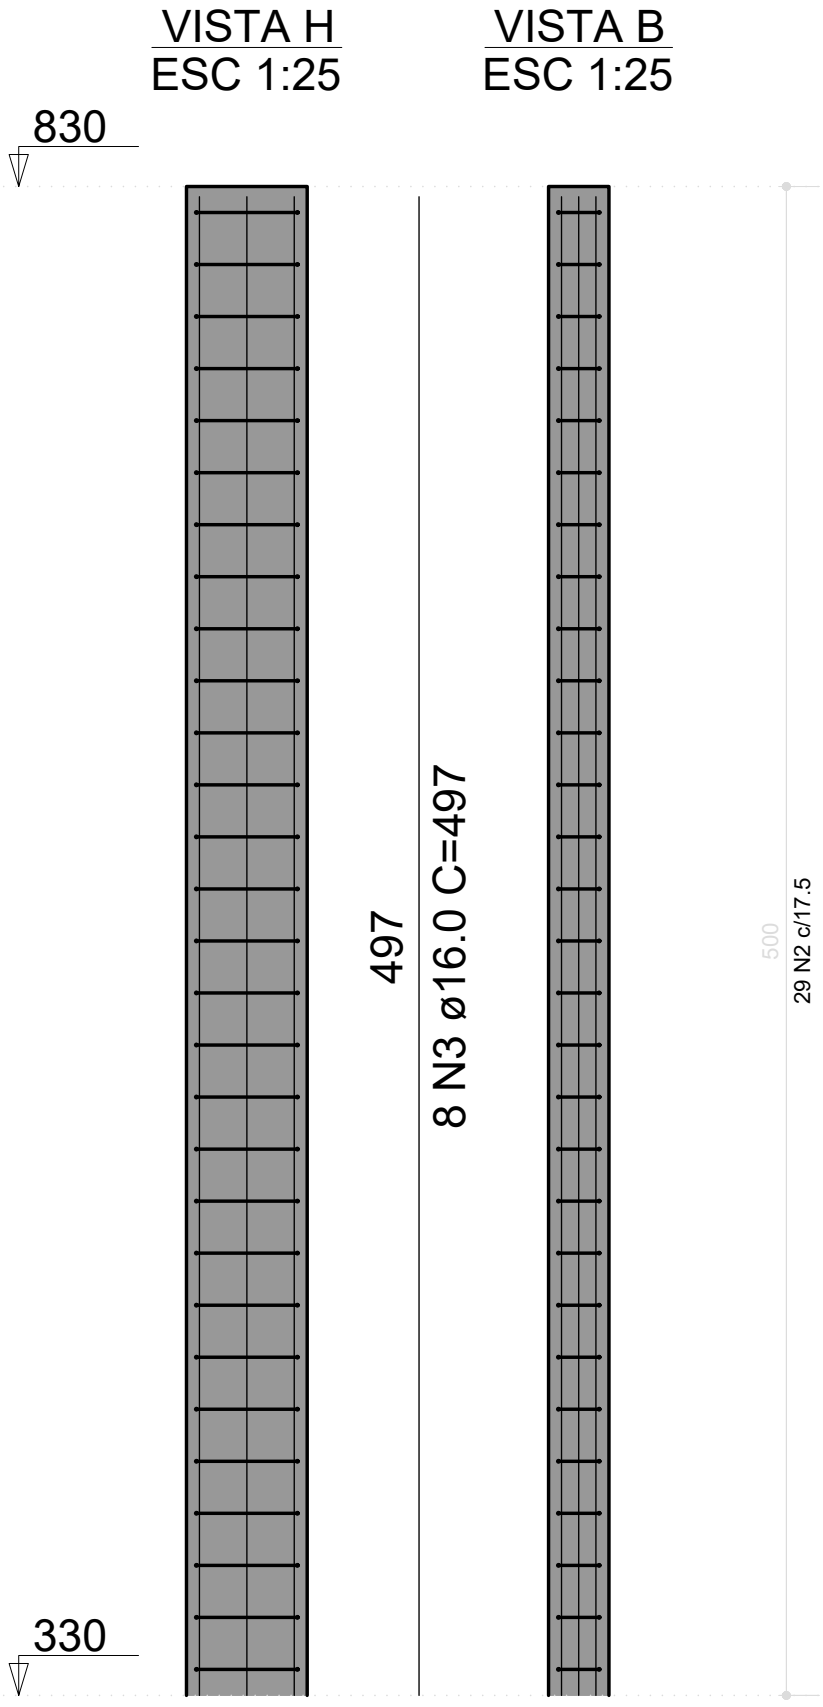

RELAÇÃO DO AÇO

4xP7

AÇO	N	DIAM (mm)	QUANT	C.UNIT (cm)	C.TOTAL (cm)
CA60	1	5.0	116	29	3364
CA50	2	5.0	116	107	12412
	3	16.0	32	497	15904

RESUMO DO AÇO

AÇO	DIAM (mm)	C.TOTAL (m)	PESO + 10% (kg)
CA50	16.0	159	276.1
CA60	5.0	157.8	26.7
PESO TOTAL (kg)			
CA50	276.1		
CA60	26.7		

Volume de concreto (C-25) = 1.60 m³
Área de forma = 24.00 m²

PROPRIETÁRIO: PREFEITURA MUNICIPAL DE COREMAS - PB

LINCOLN CARTAXO DE LIRA JUNIOR:06897861405

Assinado de forma digital por LINCOLN CARTAXO DE LIRA JUNIOR:06897861405
Dados: 2025.08.08 12:26:15 -03'00'

PROJETO: LINCOLN CARTAXO DE LIRA JÚNIOR CREA 160.814.689-8

CONSTRUÇÃO:

FOLHA 26/26

PROJETO: CONSTRUÇÃO DE GINÁSIO POLIESPORTIVO - ESTRUTURAL

CONVENIENTE: PREFEITURA MUNICIPAL DE COREMAS - PB

CONVENIADO: MUNICÍPIO DE COREMAS - PB

LOCALIDADE: COREMAS - PB

DESENHO	DATA	RESPONSÁVEL	RUBRICA	DADOS
COPIA	AGO/2025	LINCOLN CARTAXO		
VISTO				
ESCALAS	DESENHOS			CONVÊNIO
	- FORMA DO PAV. PILARES TESTADA (NÍVEL 830) - ARMADURAS PILARES PAV. PILARES TESTADAS (NÍVEL 830) - CORTE AA			GOVERNO DO ESTADO
				ARQUIVO

Aprovações: