


Detalhe 01

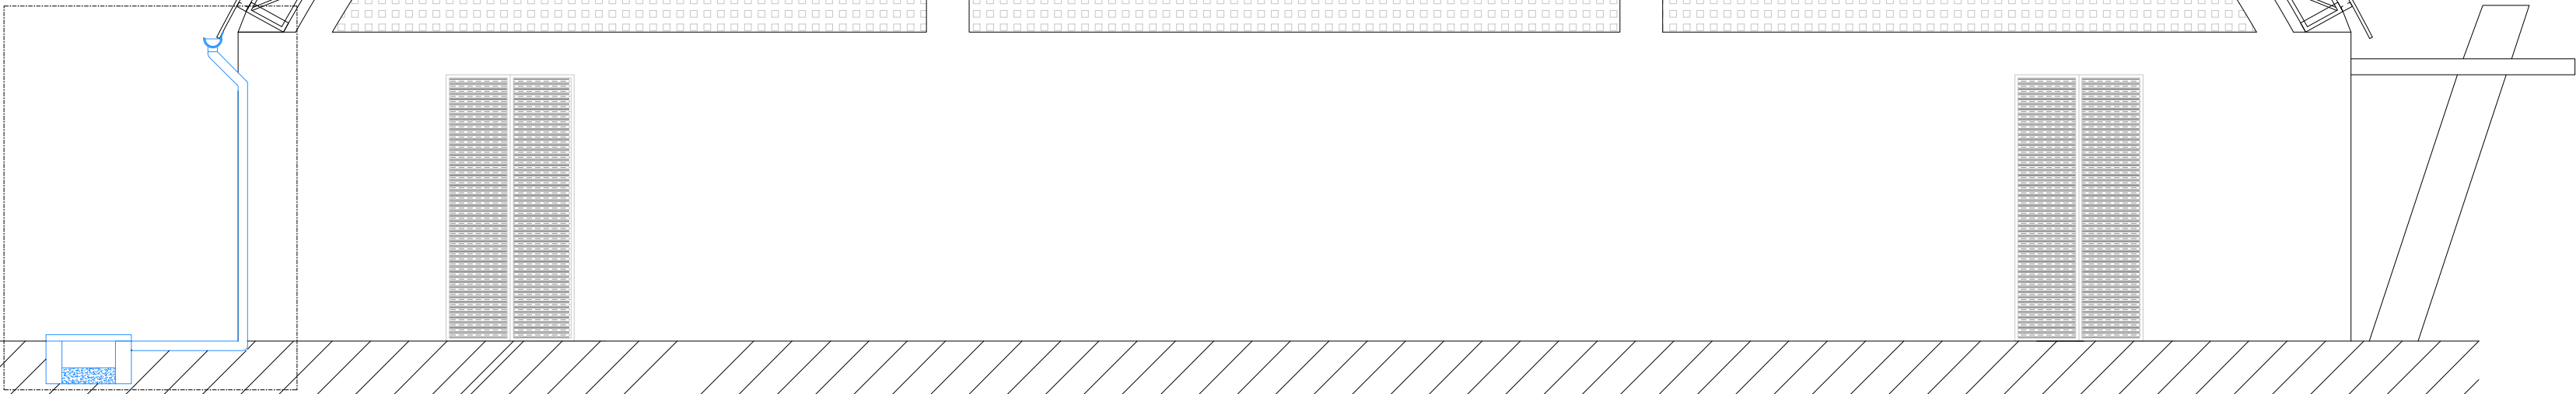

FACHADA

Escala _____ SEM

Suporte de calha em PVC

Calha semicircular de PVC Ø 125 mm


Joelho 45° Ø 100 mm

Joelho 45° Ø 100 mm

Condutor vertical PVC Ø100 mm


Joelho 90° Ø 100 mm

Caixa pluvial com fundo de brita

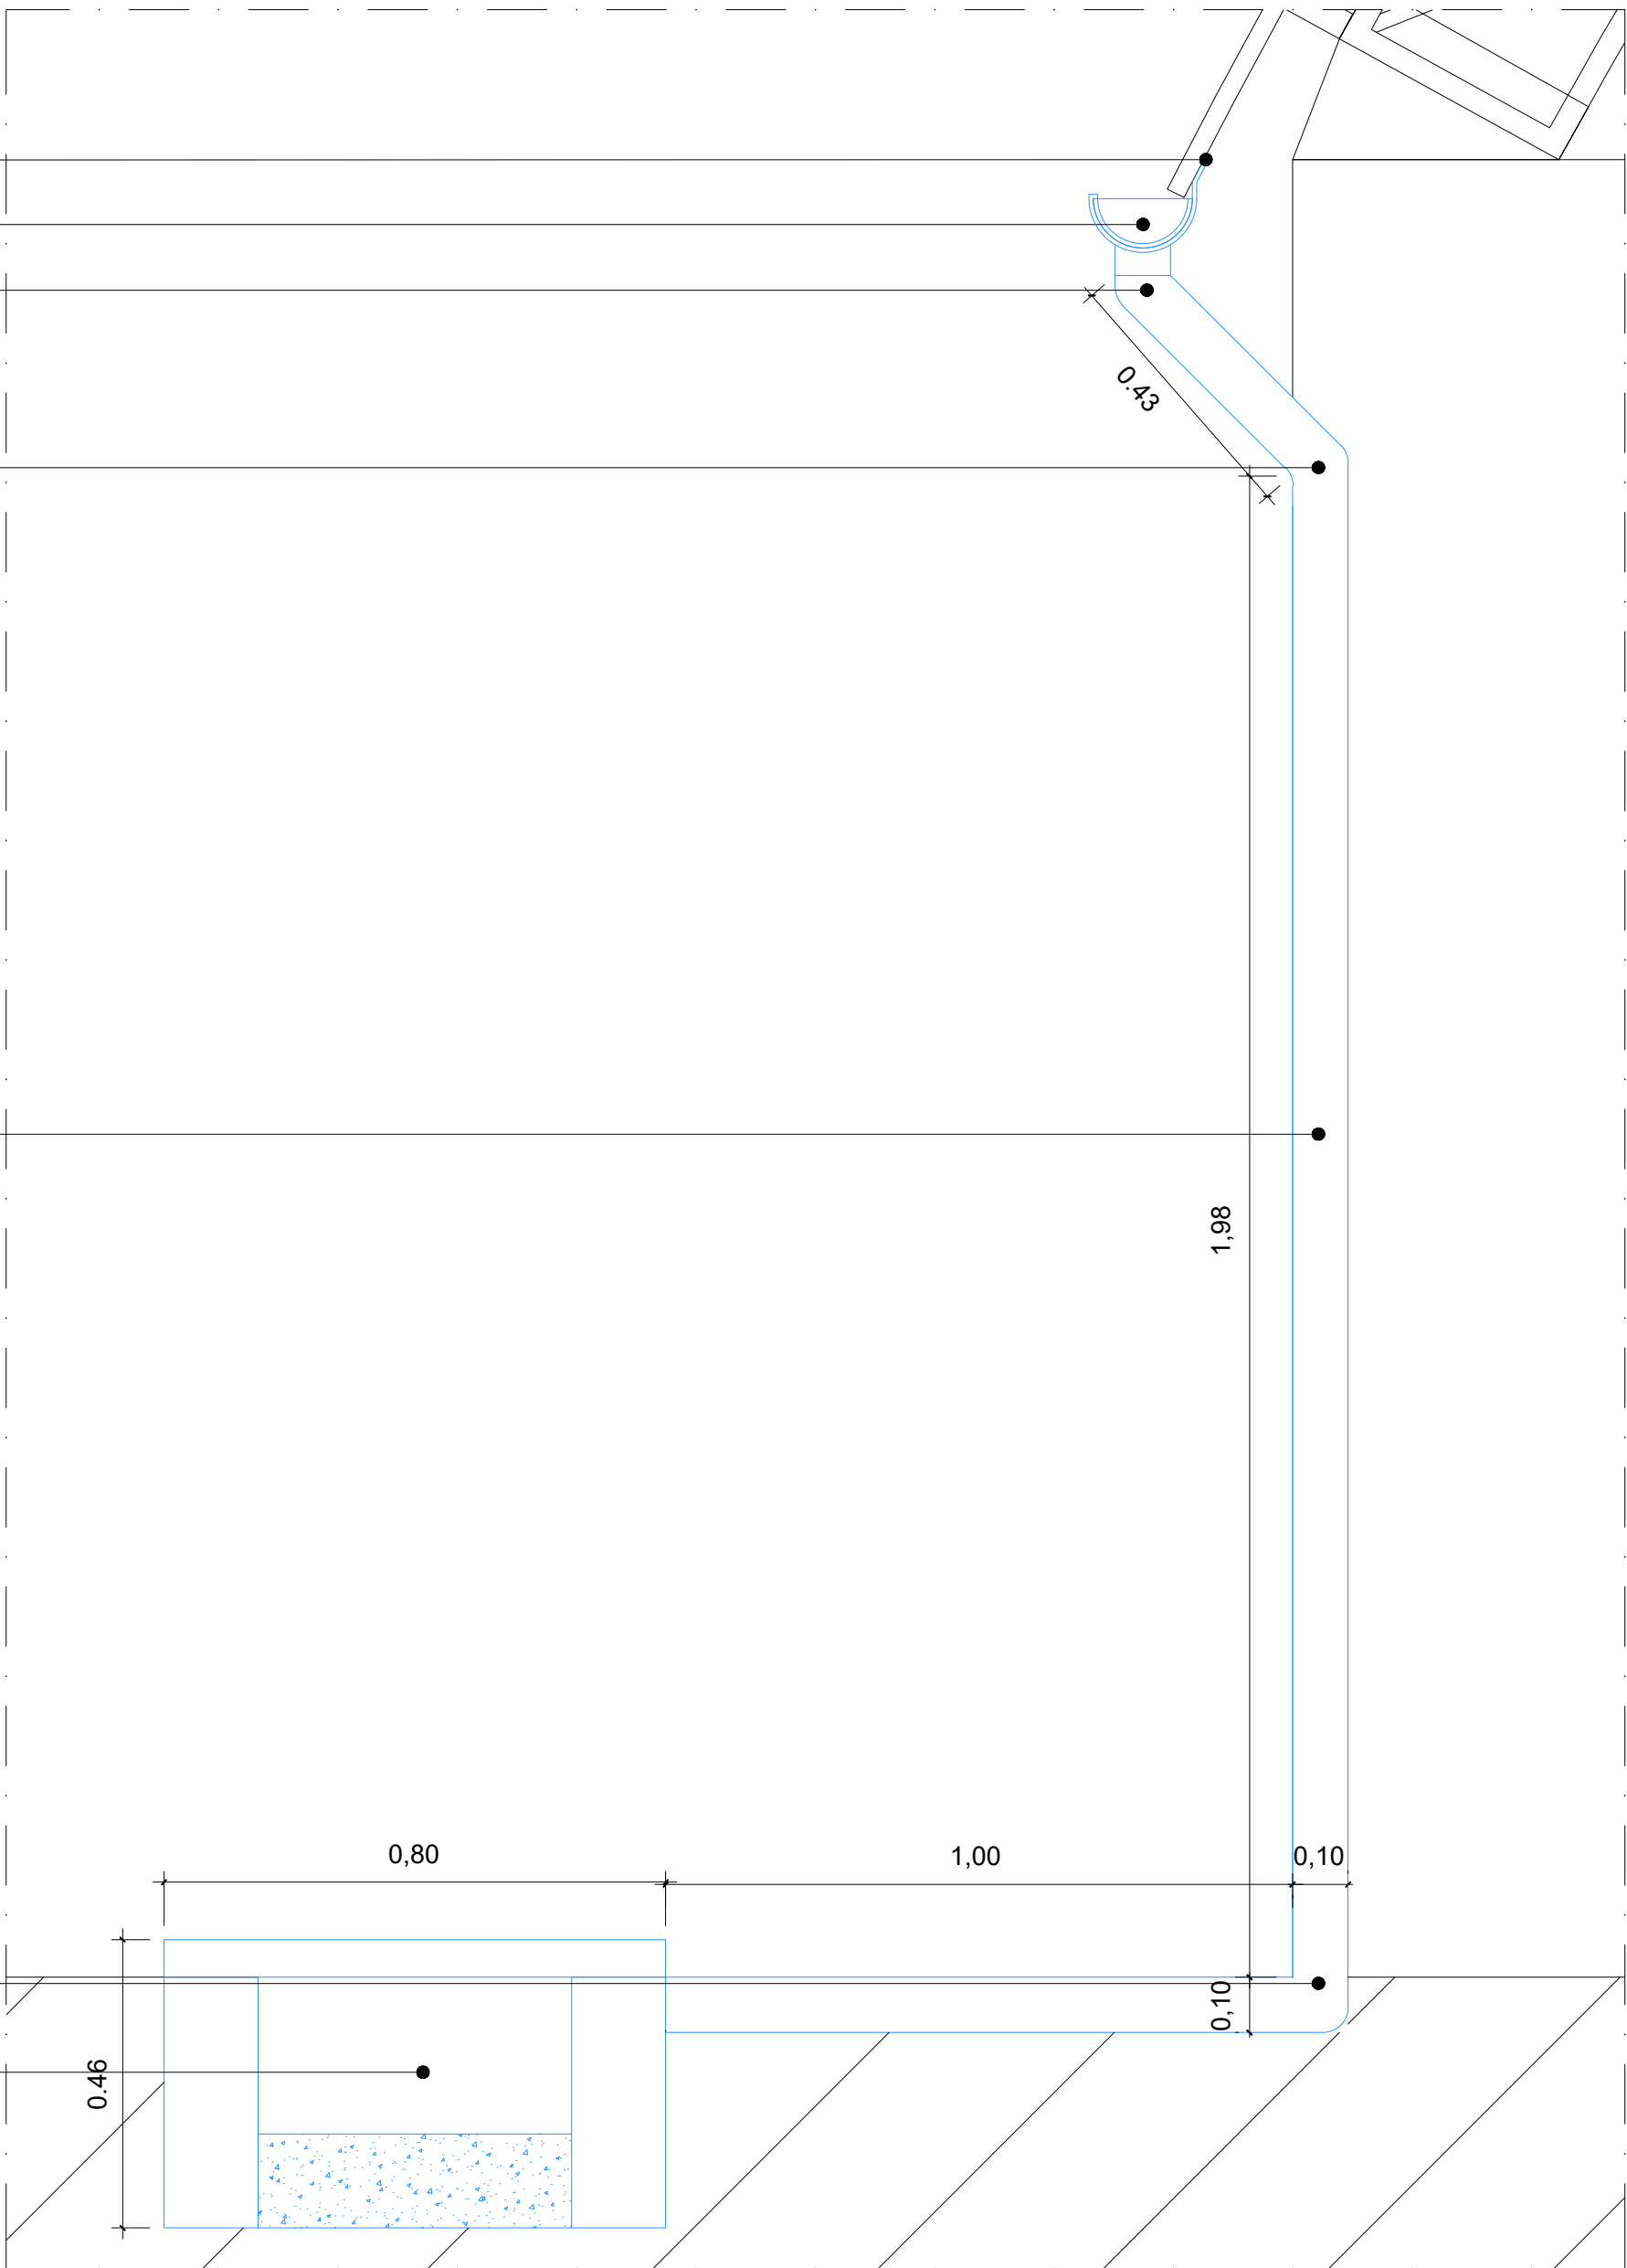


Detalhe 01

Escala _____ SEM

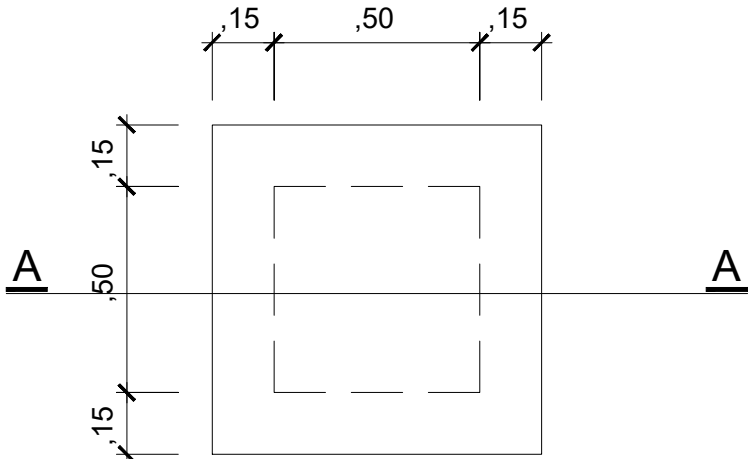

PLANTA BAIXA

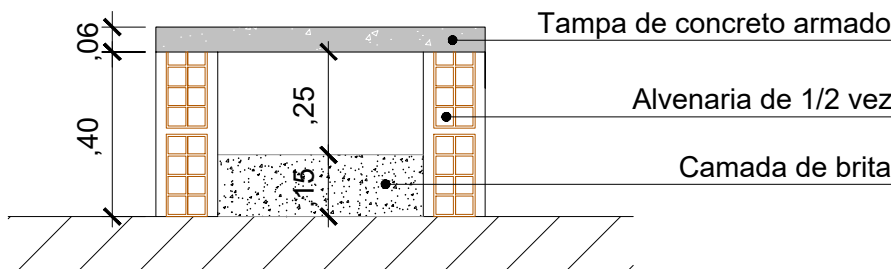

CORTE AA

Detalhe 02 - Caixa pluvial com fundo de brita

Escala _____ SEM

PROPRIETÁRIO: PREFEITURA MUNICIPAL DE COREMAS - PB

PROJETO: LINCOLN CARTAXO DE LIRA JÚNIOR CREA 160.814.689-8

FOLHA		PROJETO: CONSTRUÇÃO DE QUADRA POLIESPORTIVA		
02/02		CONVENIENTE: PREFEITURA MUNICIPAL DE COREMAS - PB		
		CONVENIADO: MUNICIPIO DE COREMAS - PB		
		LOCALIDADE: COREMAS - PB		
DESENHO	DATA	RESPONSÁVEL	RUBRICA	DADOS
CÓPIA	AGO/2025	LINCOLN CARTAXO		CREA 160.814.689-8
VISTO				
ESCALAS	DESENHOS			CONVÊNIO
	FACHADA			GOVERNO DO ESTADO
	DETALHE DA COLETA DE ÁGUAS PLUVIAIS			
INDICADO		ARQUIVO		

Aprovações:



LCL PROJETOS

Av. Gov. Flavio R. Coutinho, 500, sl. 601
Jd. Oceania, 58037-005 - Joao Pessoa (PB)
Tel +55 (83) 99924-4447
e-mail: lclprojetos@hotmail.com