



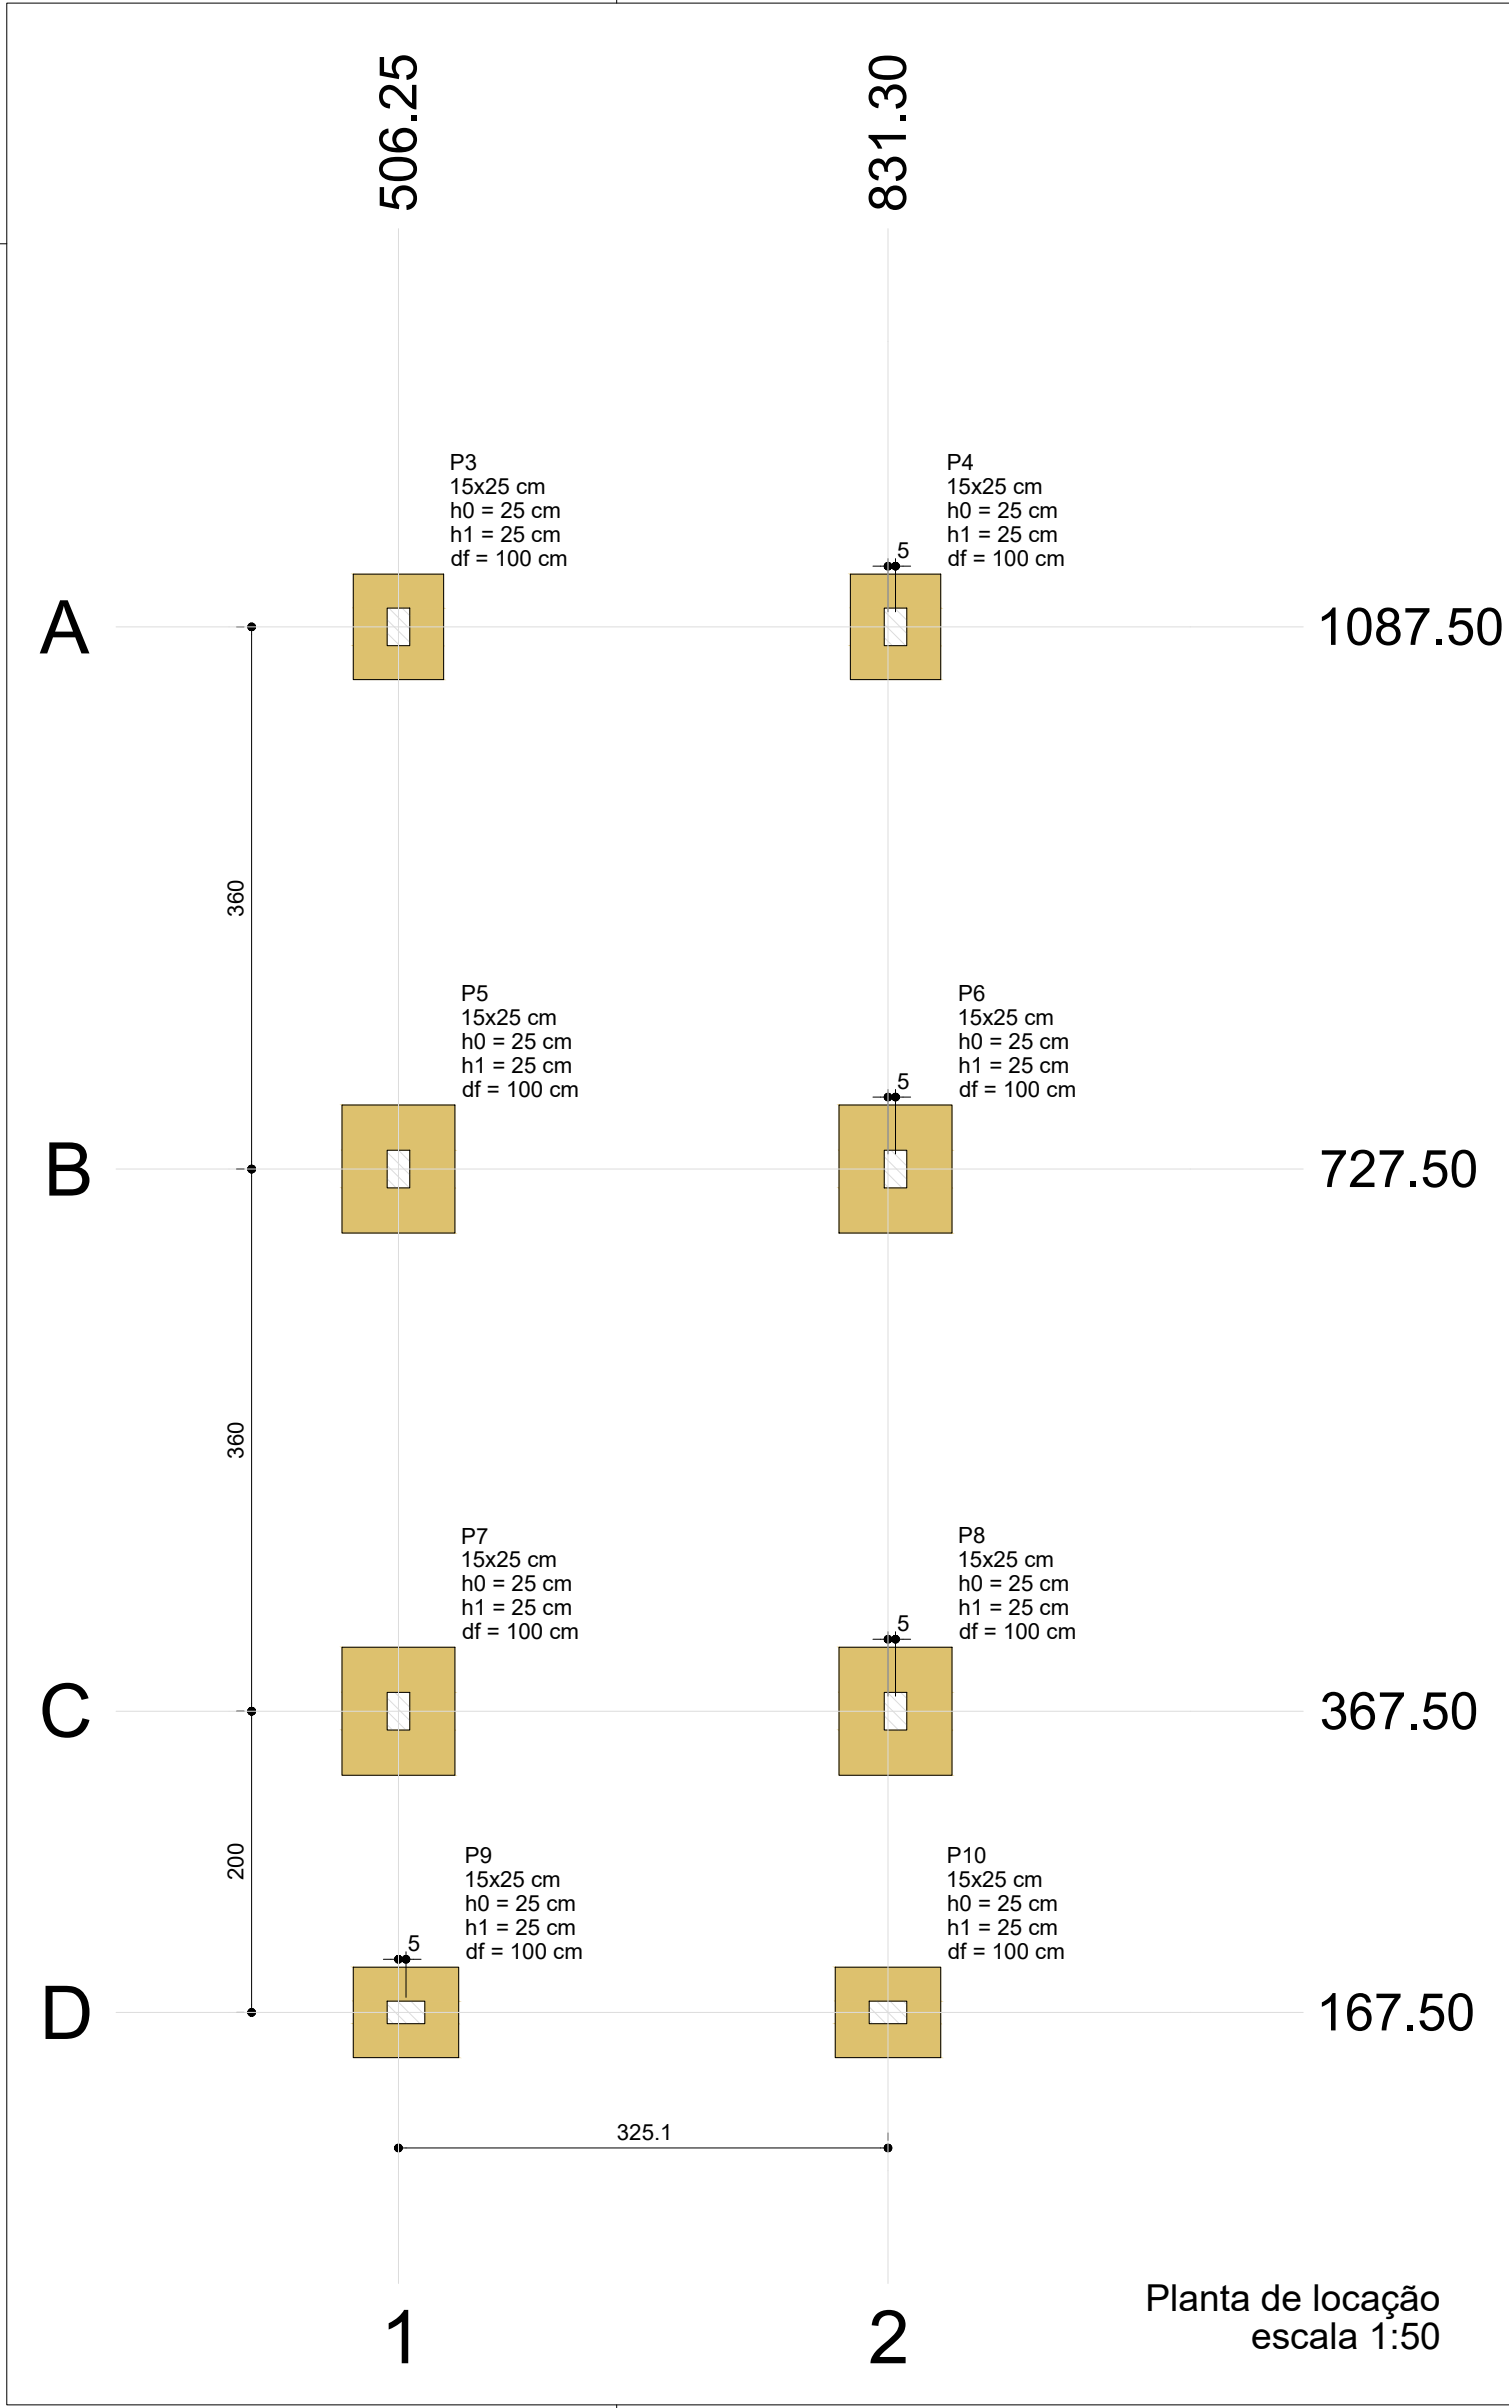

Pilar						Fundação				
Nome	Seção (cm)	X (cm)	Y (cm)	Carga Máx. (tf)	Carga Mín. (tf)	Lado B (cm)	Lado H (cm)	h0 / ha (cm)	h1 / hb (cm)	df (cm)
P3	15x25	506.25	1087.50	5.5	4.1	60	70	25	25	100
P4	15x25	836.30	1087.50	5.5	4.1	60	70	25	25	100
P5	15x25	506.25	727.50	8.7	7.2	75	85	25	25	100
P6	15x25	836.30	727.50	8.7	7.2	75	85	25	25	100
P7	15x25	506.25	367.50	9.5	8.0	75	85	25	25	100
P8	15x25	836.30	367.50	9.5	7.9	75	85	25	25	100
P9	15x25	511.25	167.50	5.9	4.4	60	70	25	25	100
P10	15x25	831.30	167.50	5.9	4.3	60	70	25	25	100

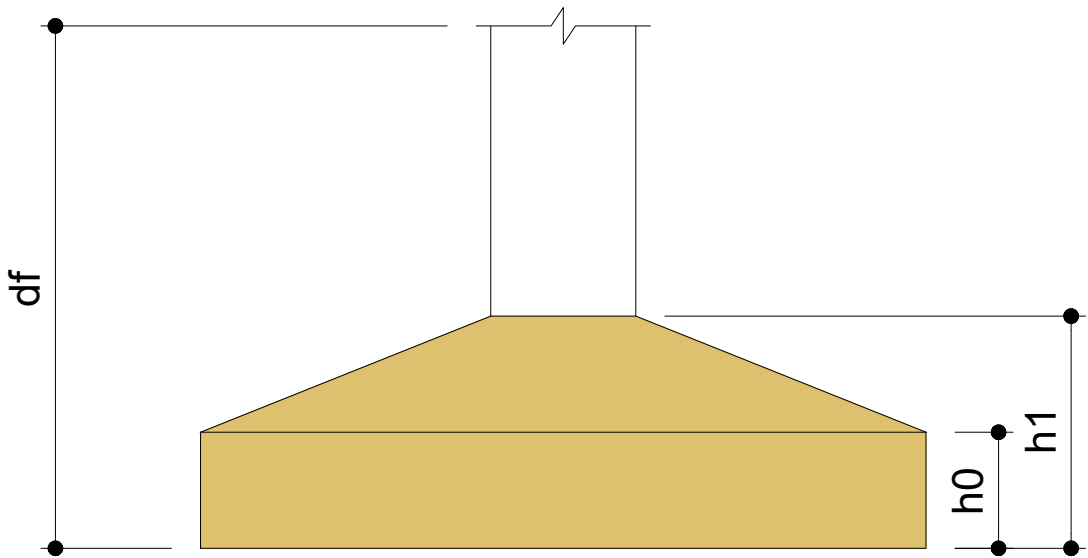


Locação no eixo X		Locação no eixo Y	
Coordenadas (cm)	Nome	Coordenadas (cm)	Nome
506.25	P3, P5, P7	1087.50	P3, P4
511.25	P9	727.50	P5, P6
831.30	P10	367.50	P7, P8
836.30	P4, P6, P8	167.50	P9, P10

Vigas			
Nome	Seção (cm)	Elevação (cm)	Nível (cm)
VB2	15x30	0	0
VB3	15x30	0	0
VB4	15x30	0	0
VB5	15x30	0	0
VB6	15x30	0	0
VB7	15x30	0	0
VB8	15x30	0	0
VB9	15x30	0	0
VB10	15x30	0	0

Pilares			
Nome	Seção (cm)	Elevação (cm)	Nível (cm)
P3	15x25	0	0
P4	15x25	0	0
P5	15x25	0	0
P6	15x25	0	0
P7	15x25	0	0
P8	15x25	0	0
P9	15x25	0	0
P10	15x25	0	0

Características dos materiais	
fck (kgf/cm²)	Ecs (kgf/cm²)
250	241500

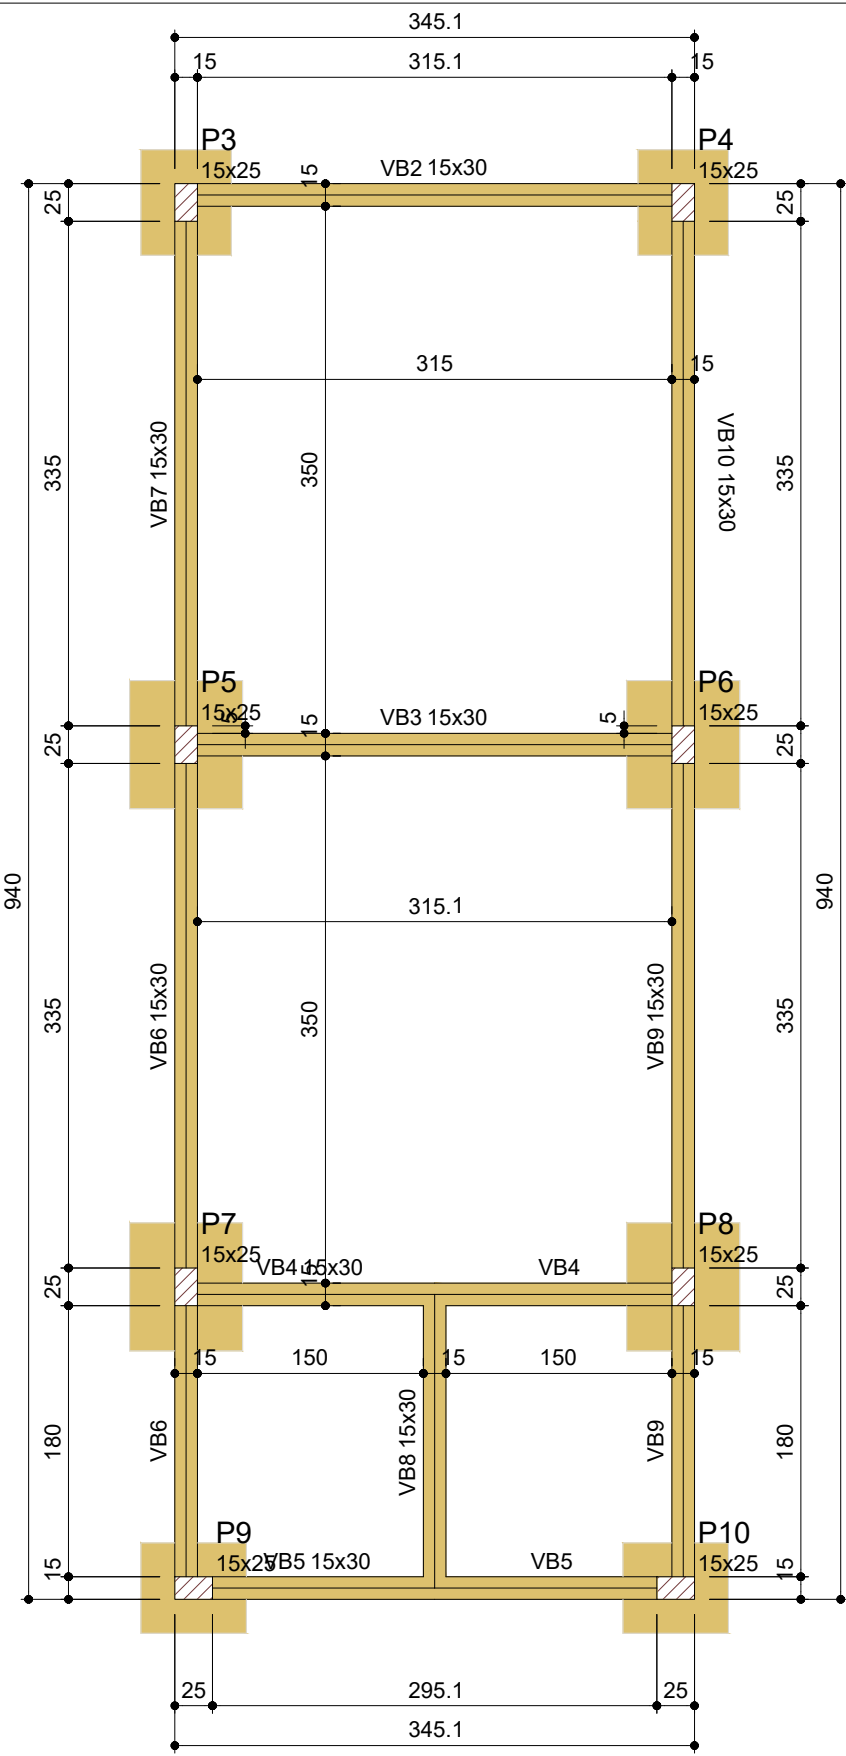

Legenda dos pilares	
	Pilar que passa
Legenda das vigas e paredes	
	Viga

PROPRIETÁRIO: PREFEITURA MUNICIPAL DE COREMAS - PB

LINCOLN CARTAXO DE LIRA JUNIOR:06897861405

PROJETO: LINCOLN CARTAXO DE LIRA JÚNIOR CREA 160.814.689-8

Assinado de forma digital por LINCOLN CARTAXO DE LIRA JUNIOR:06897861405

Dados: 2025.08.08 13:33:38 -03'00'

FOLHA

01/12

PROJETO: CONSTRUÇÃO DE GINÁSIO POLIESPORTIVO

CONVENIENTE: PREFEITURA MUNICIPAL DE COREMAS - PB

CONVENIADO: MUNICÍPIO DE COREMAS - PB

LOCALIDADE: COREMAS - PB

	DATA	RESPONSÁVEL	RUBRICA	DADOS
DESENHO	AGO/2025	LINCOLN CARTAXO		
CÓPIA				
VISTO				

ESCALAS

Indicada

DESENHOS

- Planta de Locação

- Forma do Pavimento Fundação (Nível 0)

CONVÊNIO

GOVERNO DO ESTADO

ARQUIVO


Aprovações:

Av. Gov. Flávio Ribeiro Coutinho, 500, sl. 601

Jardim Oceania, 58037-005 - João Pessoa (PB)

Tel +55 (83) 99924.4447

e-mail: contato@lclprojetos.com

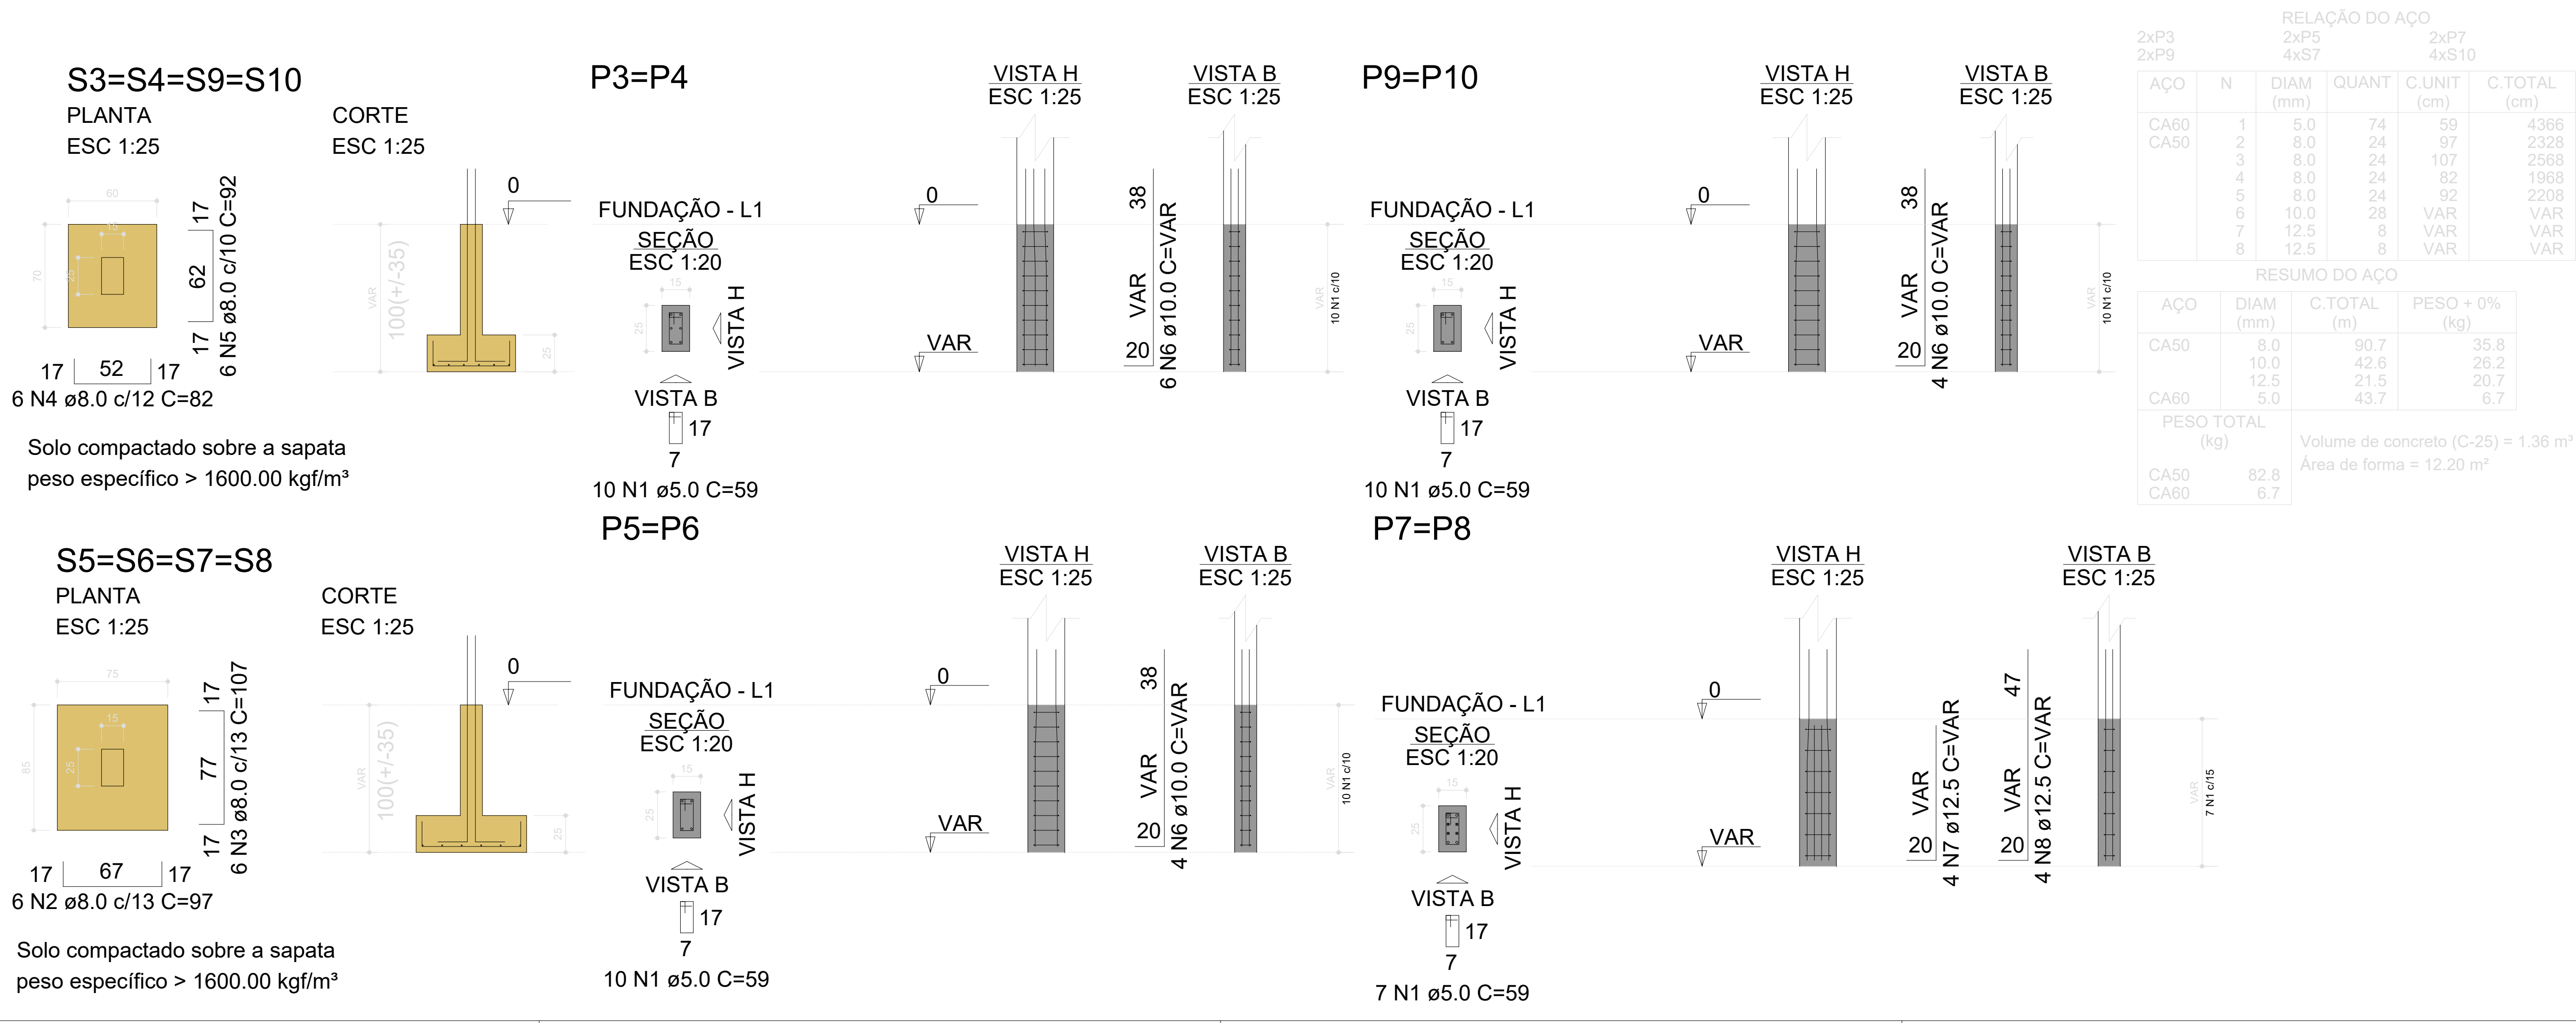

PROPRIETÁRIO: PREFEITURA MUNICIPAL DE COREMAS - PB

LINCOLN CARTAXO DE LIRA JÚNIOR:06897861405

Assinado de forma digital por LINCOLN CARTAXO DE LIRA JÚNIOR:06897861405

Dados: 2025.08.08 13:32:23 -03'00'

PROJETO: LINCOLN CARTAXO DE LIRA JÚNIOR CREA 160.814.689-8

CONSTRUÇÃO:

FOLHA

02/12

PROJETO: CONSTRUÇÃO DE GINÁSIO POLIESPORTIVO

CONVENIENTE: PREFEITURA MUNICIPAL DE COREMAS - PB

CONVENIADO: MUNICÍPIO DE COREMAS - PB

LOCALIDADE: COREMAS - PB

	DATA	RESPONSÁVEL	RUBRICA	DADOS
DESENHO	AGO/2025	LINCOLN CARTAXO		
CÓPIA				
VISTO				

ESCALAS

Indicada

DESENHOS

- Fundações

CONVÊNIO

GOVERNO DO ESTADO

ARQUIVO

Aprovações:

LCL PROJETOS


Av. Gov. Flávio Ribeiro Coutinho, 500, sl. 601

Jardim Oceania, 59037-005 - João Pessoa (PB)

Tel +55 (83) 99924.4447


e-mail: contato@lclprojetos.com

VB2
ESC 1:30

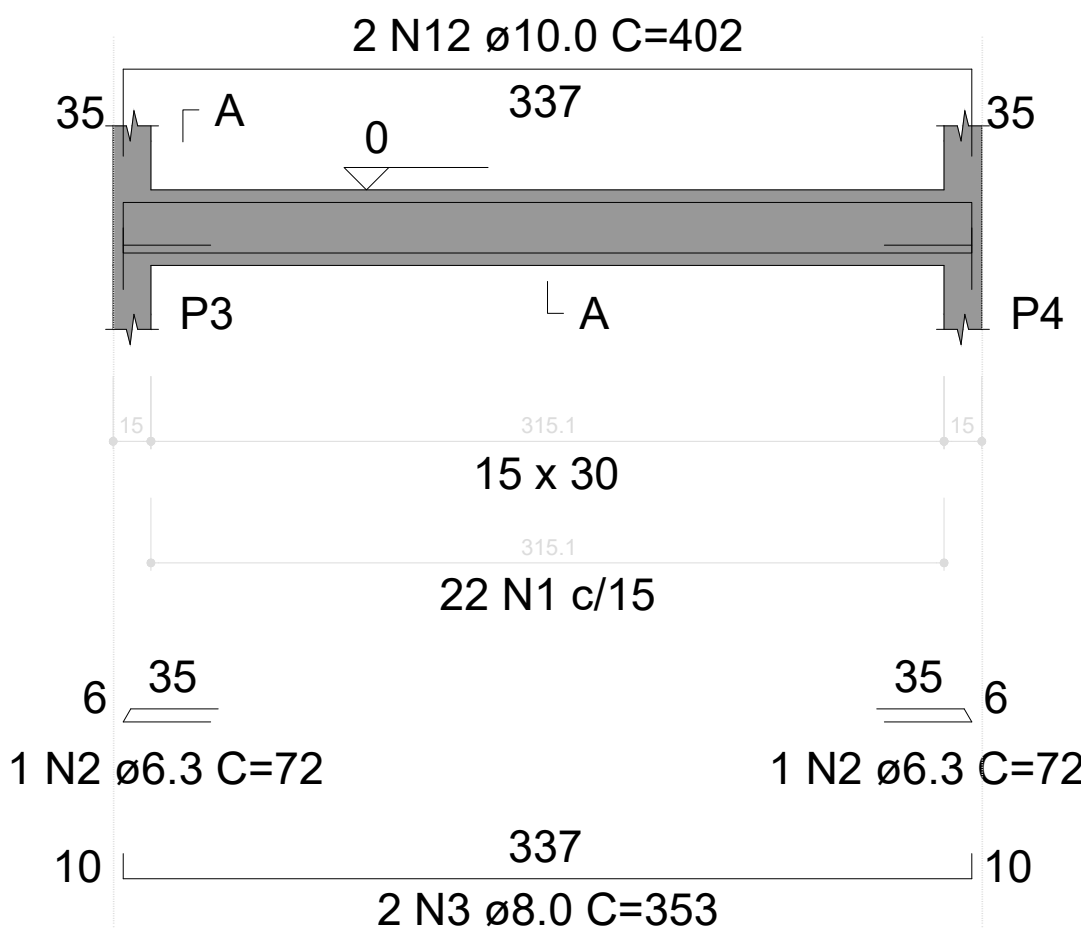


VB3
ESC 1:30

SEÇÃO A-A
ESC 1:25

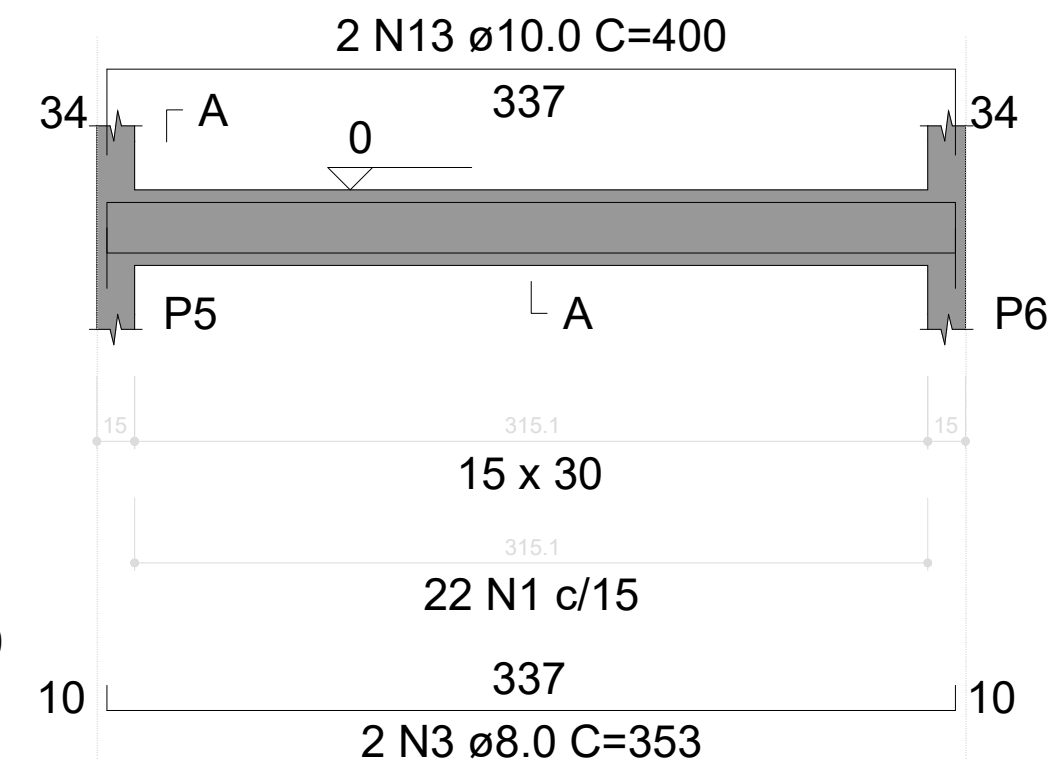


VB4
ESC 1:30


SEÇÃO A-A
ESC 1:25

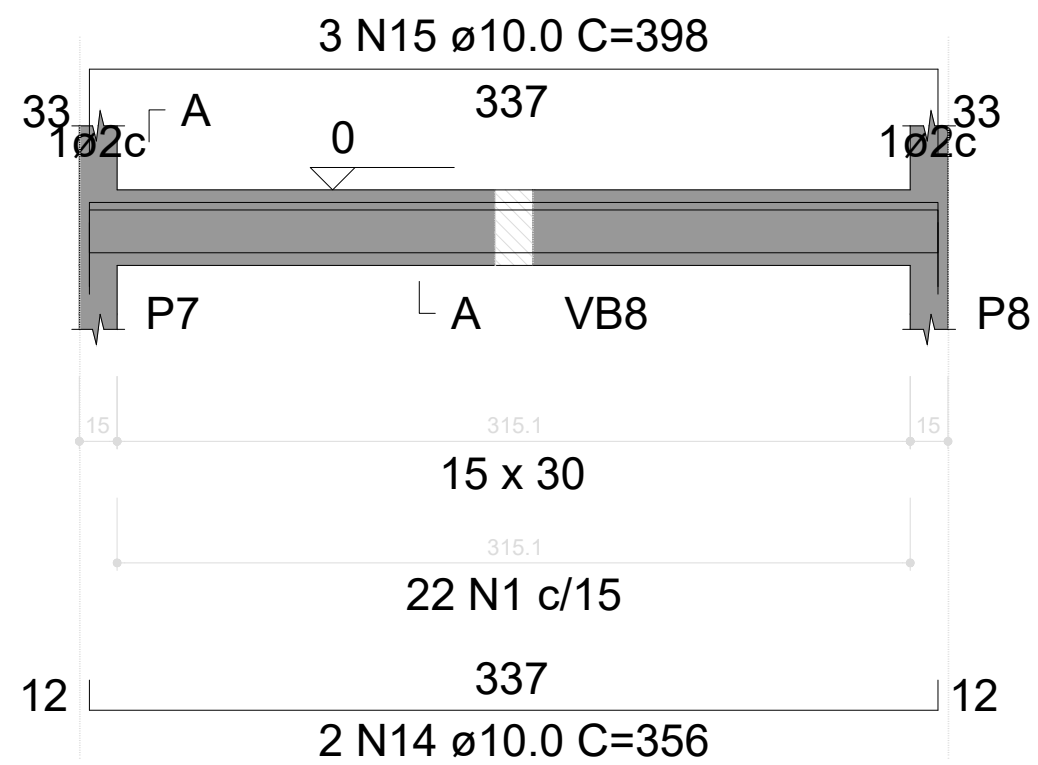


SEÇÃO A-A
ESC 1:25

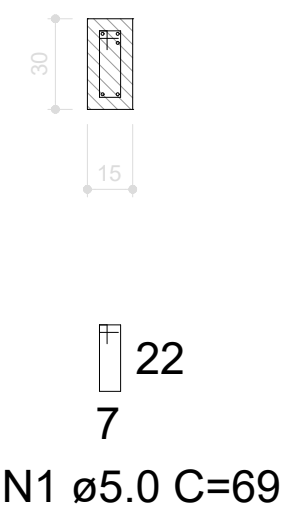


VB5
ESC 1:30

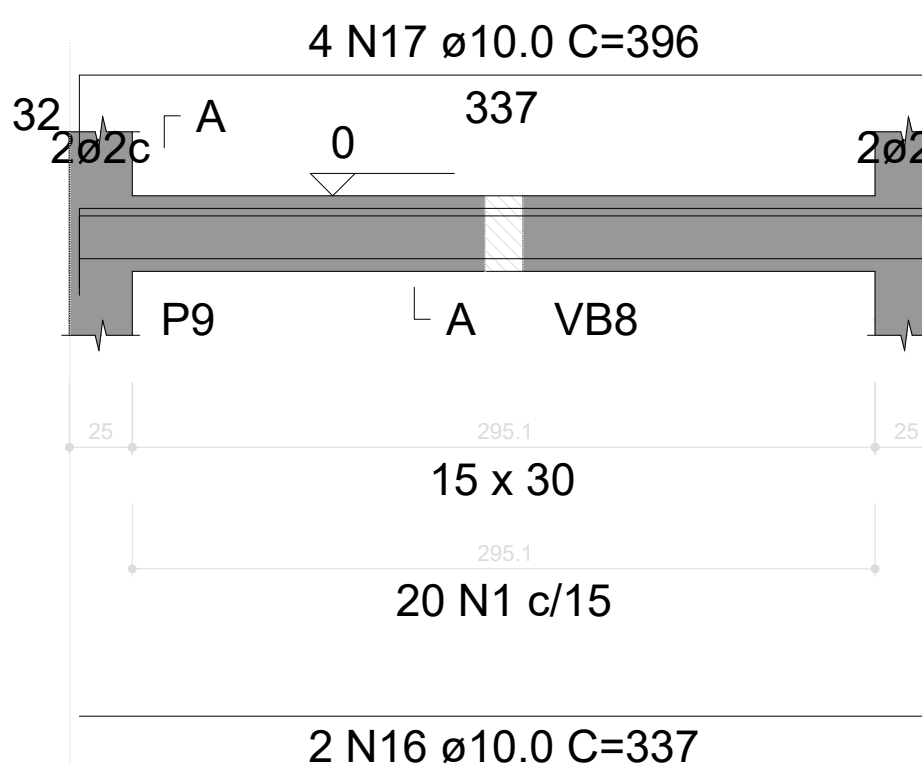


SEÇÃO A-A
ESC 1:25

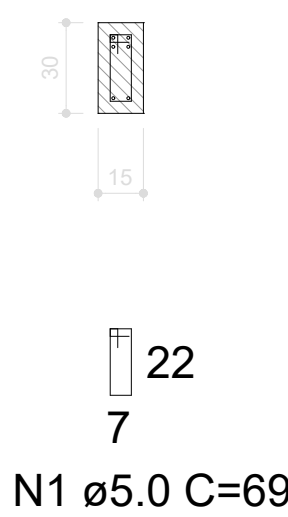


VB6
ESC 1:30

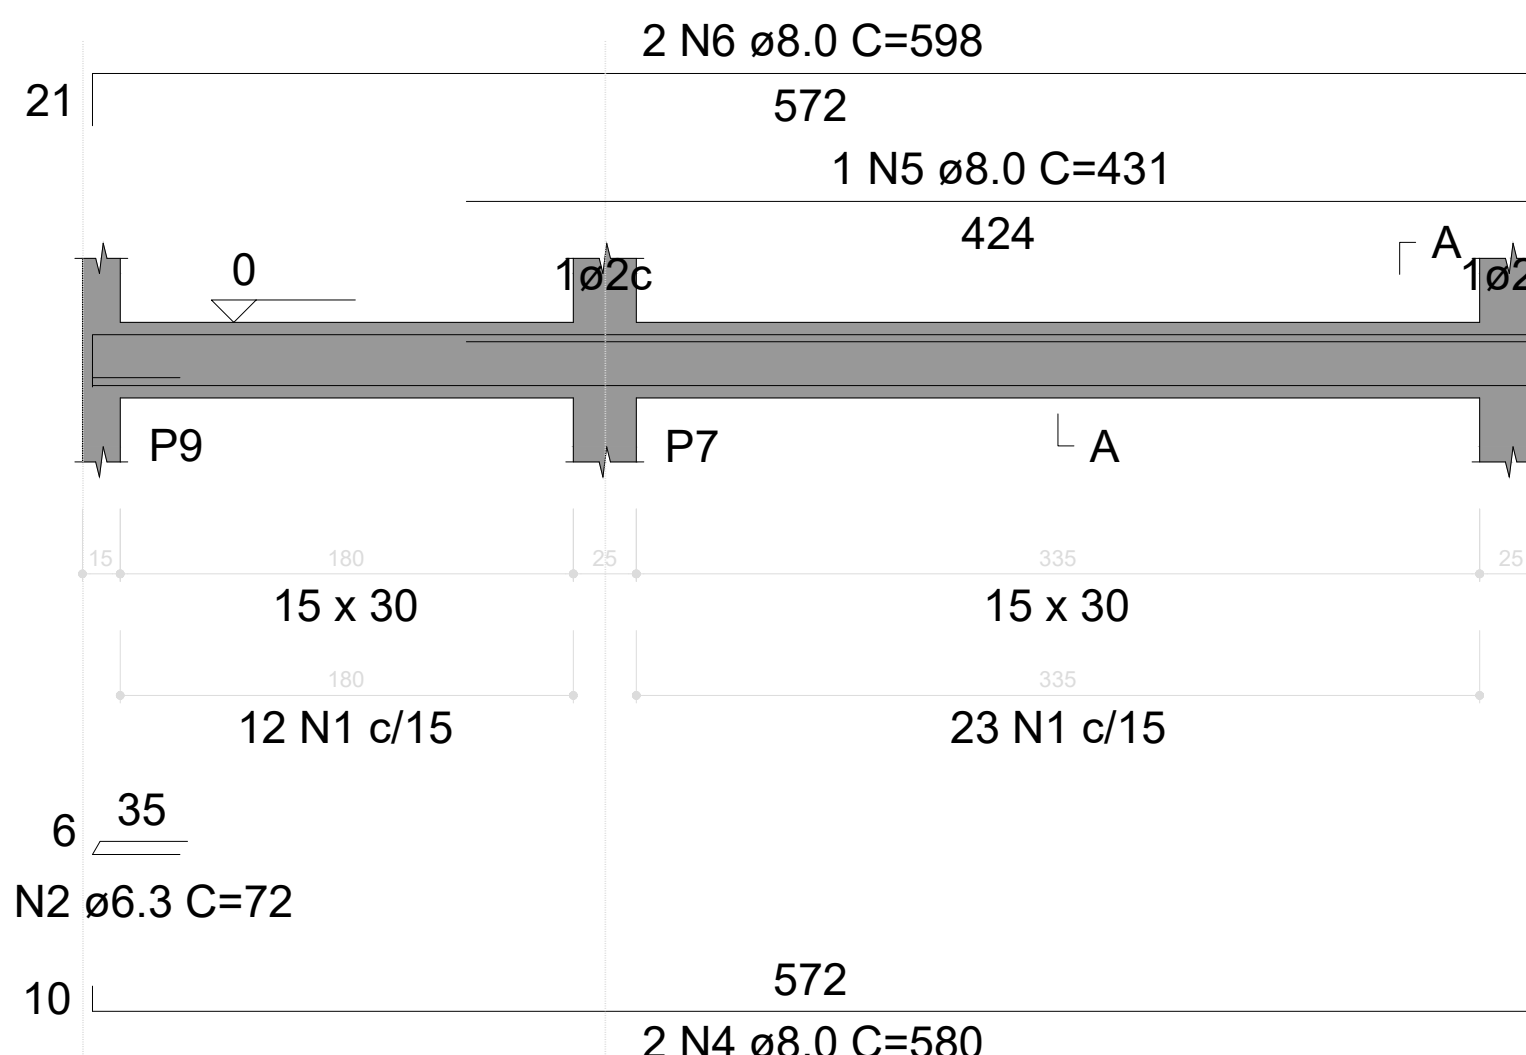


SEÇÃO A-A
ESC 1:25

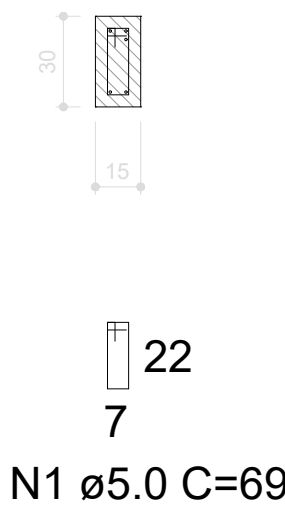


VB7
ESC 1:30

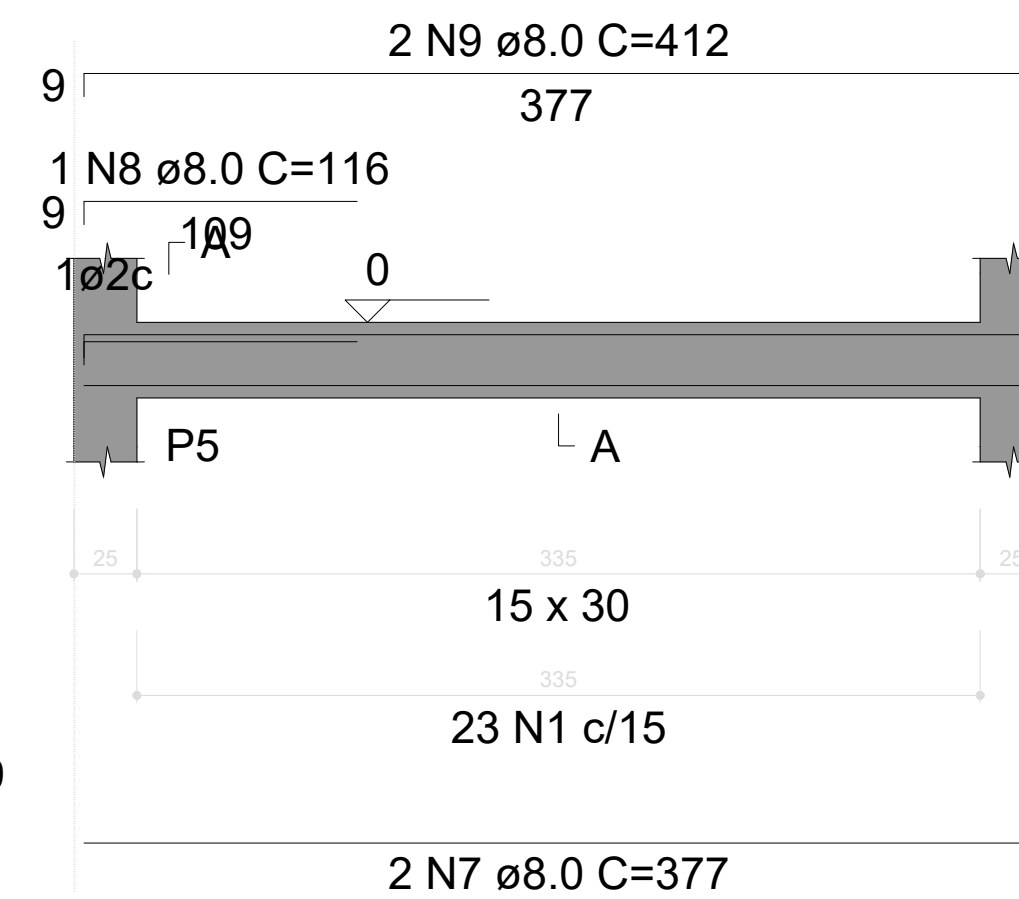


SEÇÃO A-A
ESC 1:25

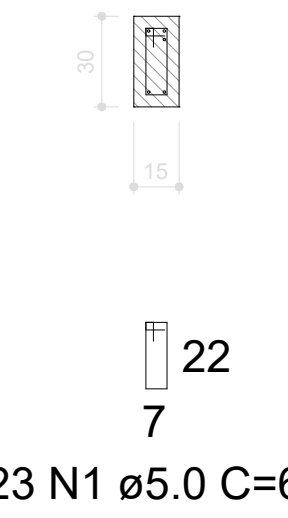


VB8
ESC 1:30

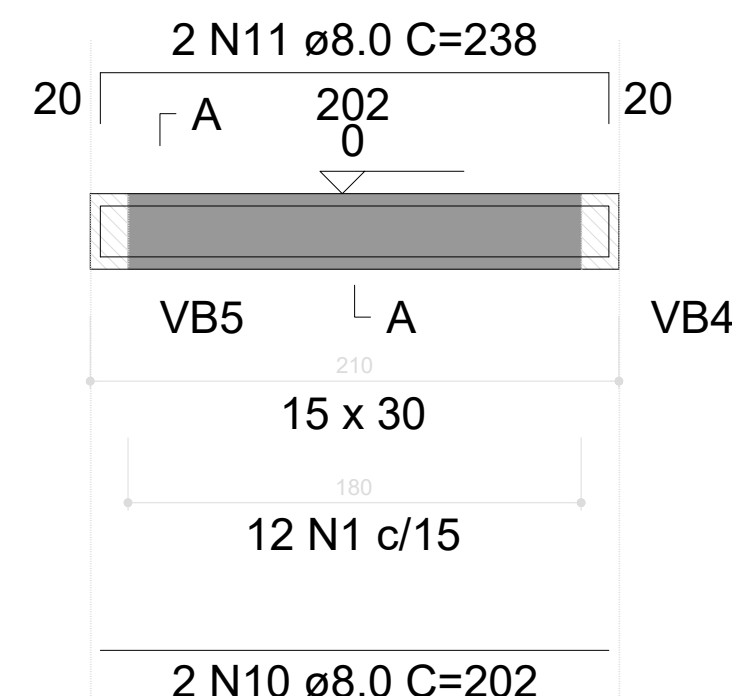


SEÇÃO A-A
ESC 1:25

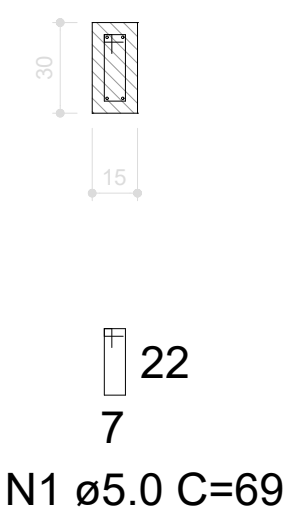


VB9
ESC 1:30

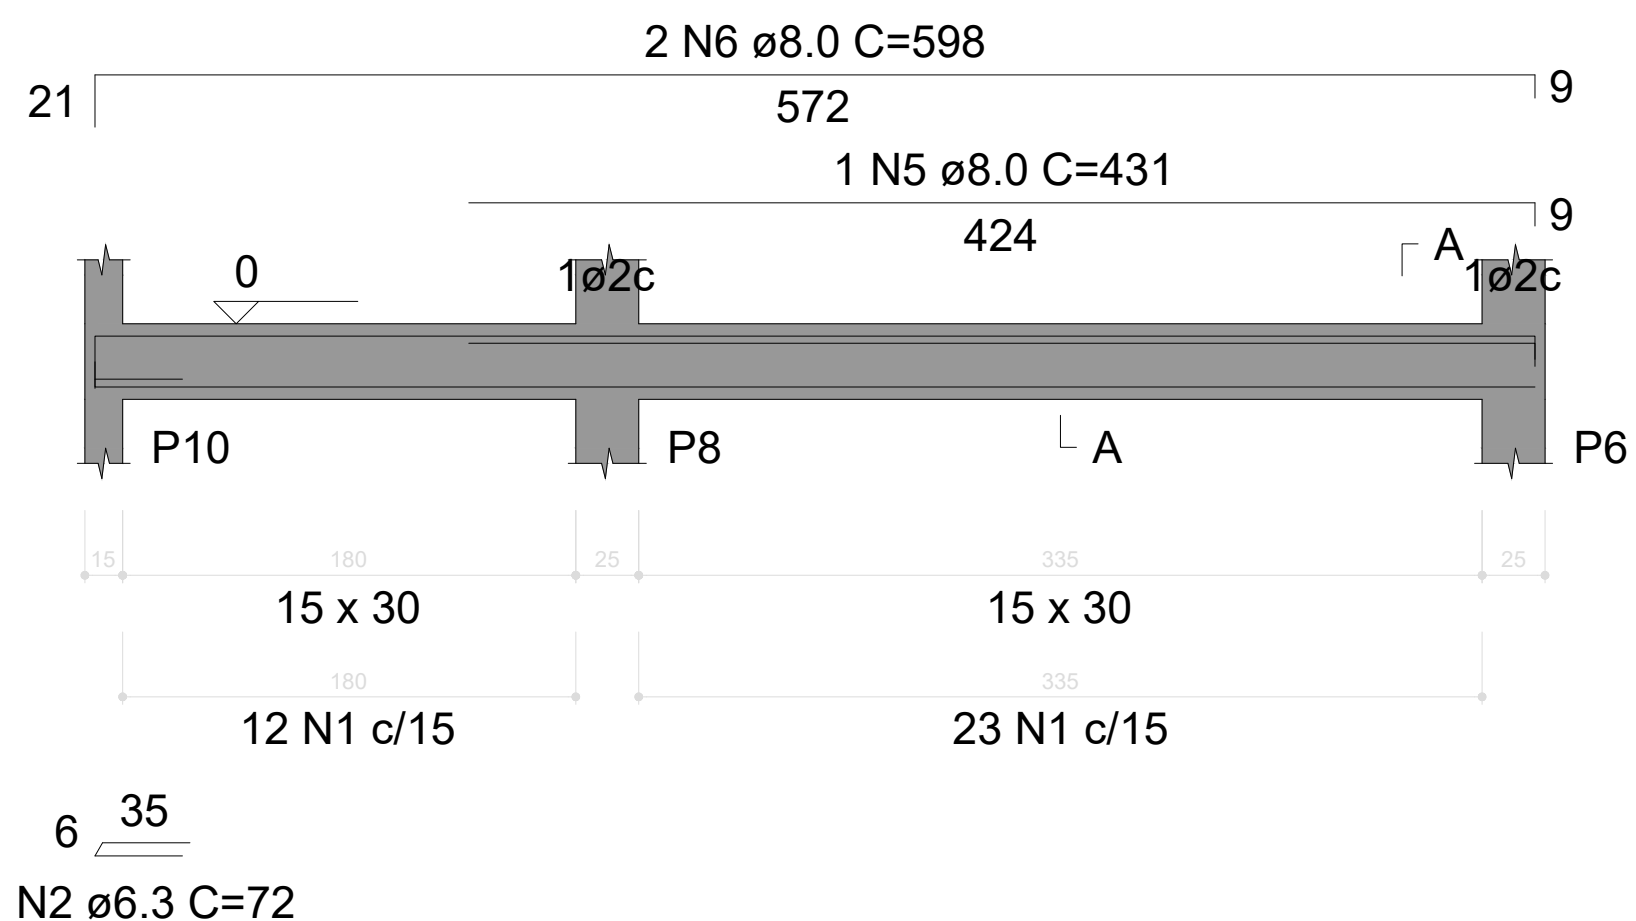


SEÇÃO A-A
ESC 1:25

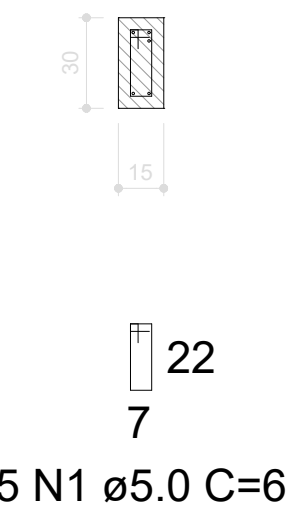

VB10
ESC 1:30

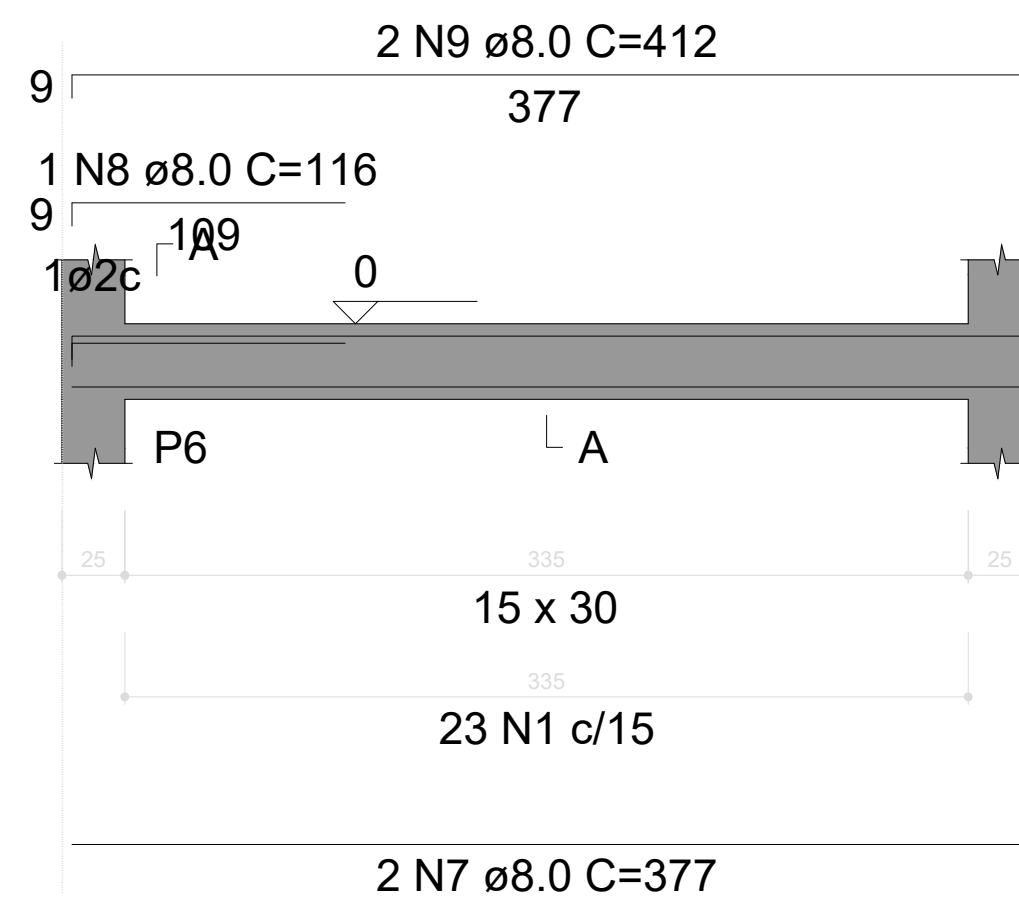

SEÇÃO A-A
ESC 1:25

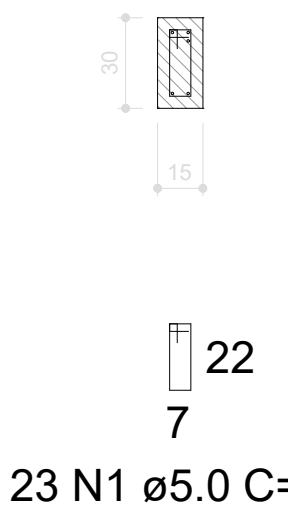

RELAÇÃO DO AÇO					
AÇO	N	DIAM (mm)	QUANT	VB2	VB3
				VB5	VB6
				VB8	VB9
				VB4	VB7
				VB10	C.TOTAL (cm)
CA60 CA50	1	5.0	214	69	14766
	2	6.3	4	72	288
	3	8.0	4	353	1412
	4	8.0	4	580	2320
	5	8.0	2	431	862
	6	8.0	4	598	2392
	7	8.0	4	377	1508
	8	8.0	2	116	232
	9	8.0	4	412	1648
	10	8.0	2	202	404
	11	8.0	2	238	476
	12	10.0	2	402	804
	13	10.0	2	400	800
	14	10.0	2	356	712
	15	10.0	3	398	1194
	16	10.0	2	337	674
	17	10.0	4	396	1584

RESUMO DO AÇO

AÇO	DIAM (mm)	C.TOTAL (m)	PESO + 0% (kg)
CA50	6.3	2.9	0.7
	8.0	112.5	44.4
	10.0	57.7	35.6
CA60	5.0	147.7	22.8
PESO TOTAL (kg)		Volume de concreto (C-25) = 1.58 m³	
CA50	80.7	Área de forma = 26.40 m²	
CA60	22.8		

PROPRIETÁRIO: PREFEITURA MUNICIPAL DE COREMAS - PB

LINCOLN CARTAXO DE LIRA JUNIOR:06897861405

PROJETO: LINCOLN CARTAXO DE LIRA JÚNIOR CREA 160.814.689-8


CONSTRUÇÃO:

FOLHA 03/12	PROJETO:	CONSTRUÇÃO DE GINÁSIO POLIESPORTIVO		
	CONVENIENTE:	PREFEITURA MUNICIPAL DE COREMAS - PB		
	CONVENIADO:	MUNICÍPIO DE COREMAS - PB		
	LOCALIDADE:	COREMAS - PB		
	DATA	RESPONSÁVEL	RUBRICA	DADOS
DESENHO	AGO/2025	LINCOLN CARTAXO		
CÓPIA				
VISTO				
ESCALAS	DESENHOS			CONVÊNIO
Indicada	- Vigas Baldrames			GOVERNO DO ESTADO
				ARQUIVO

Aprovações:



Av. Gov. Flávio Ribeiro Coutinho, 500, sl. 601
Jardim Oceania, 58037-005 - João Pessoa (PB)
Tel +55 (83) 99924.4447
e-mail: contato@lclprojetos.com

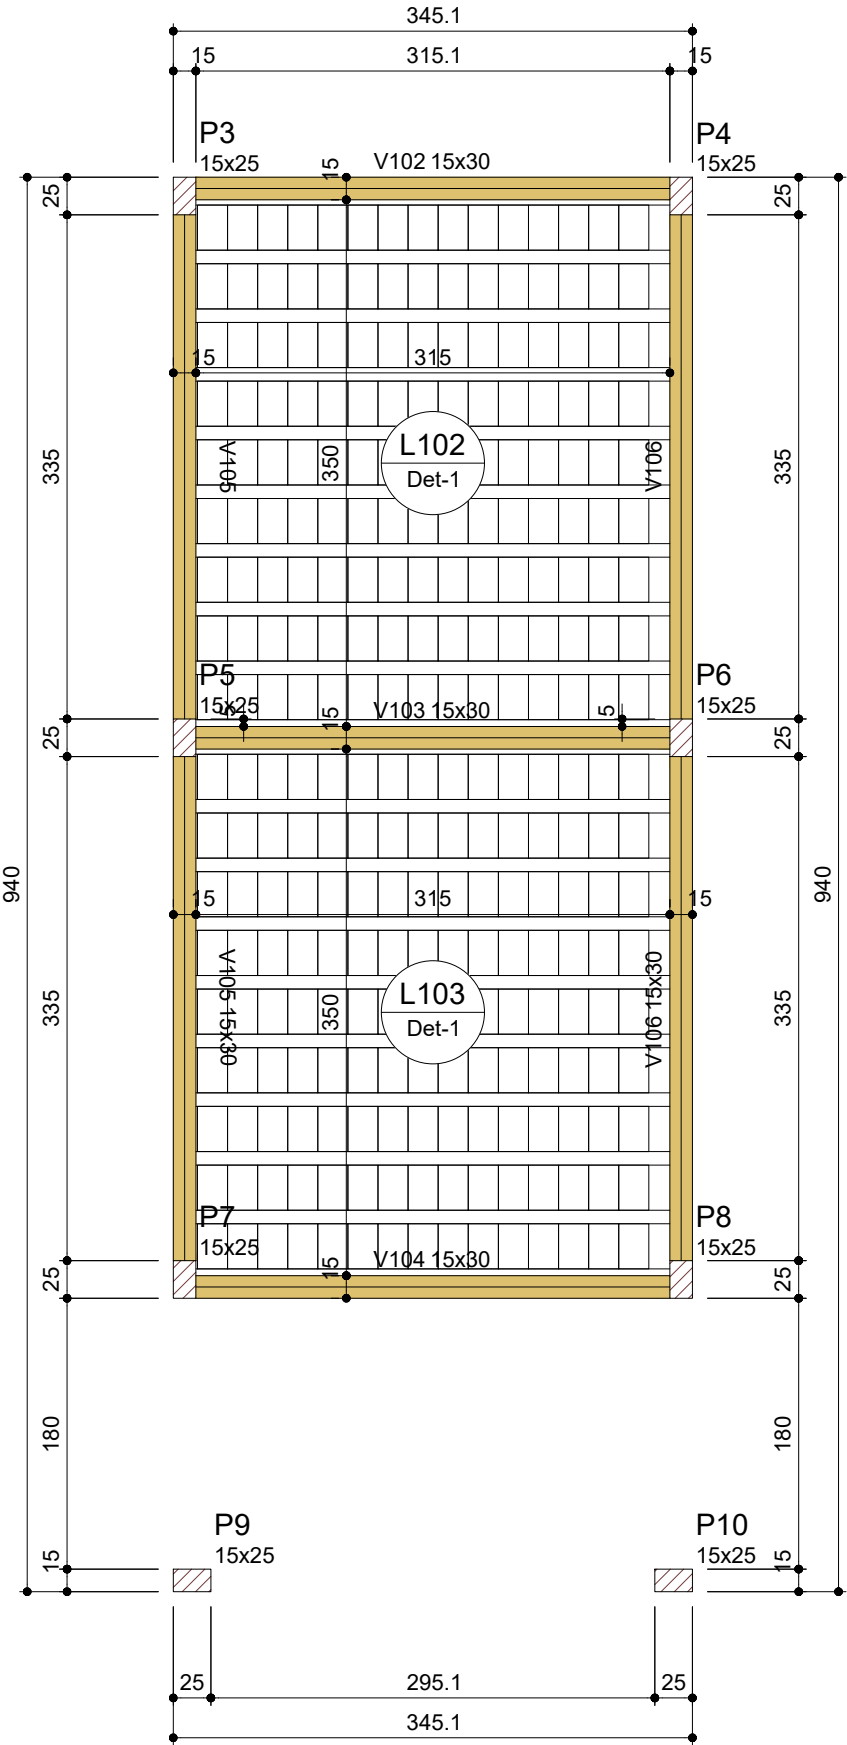

Forma do pavimento Térreo (Nível 290)
escala 1:50

Vigas			
Nome	Seção (cm)	Elevação (cm)	Nível (cm)
V102	15x30	0	290
V103	15x30	0	290
V104	15x30	0	290
V105	15x30	0	290
V106	15x30	0	290

Pilares			
Nome	Seção (cm)	Elevação (cm)	Nível (cm)
P3	15x25	0	290
P4	15x25	0	290
P5	15x25	0	290
P6	15x25	0	290
P7	15x25	0	290
P8	15x25	0	290
P9	15x25	0	290
P10	15x25	0	290

Legenda dos pilares	
	Pilar que passa

Legenda das vigas e paredes	
	Viga


Características dos materiais	
fck (kgf/cm²)	Ecs (kgf/cm²)
250	241500

Lajes								
Dados						Sobrecarga (kgf/m²)		
Nome	Tipo	Altura (cm)	Elevação (cm)	Nível (cm)	Peso próprio (kgf/m²)	Adicional	Acidental	Localizada
L102	Treliçada 1D	15	0	290	316	50	50	-
L103	Treliçada 1D	15	0	290	316	50	50	-

Área de lajes			
Tipo	Altura (cm)	Bloco de Enchimento	Área (m²)
Treliçada 1D	15	B10/30/20	22.05

Blocos de enchimento						
Detalhe	Tipo	Nome	Dimensões(cm)			Quantidade
			hb	bx	by	
1	Lajota cerâmica	B10/30/20	10	30	20	270

Detalhe 1 (esc. 1:30)

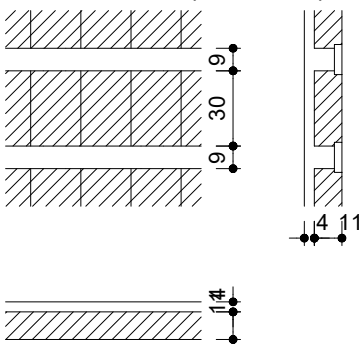

PROPRIETÁRIO: PREFEITURA MUNICIPAL DE COREMAS - PB

LINCOLN CARTAXO DE LIRA JUNIOR:06897861405

Assinado de forma digital por LINCOLN CARTAXO DE LIRA JUNIOR:06897861405
Dados: 2025.08.08 13:32:39 -03'00'

PROJETO: LINCOLN CARTAXO DE LIRA JÚNIOR CREA 160.814.689-8

CONSTRUÇÃO:

FOLHA

04/12

PROJETO: CONSTRUÇÃO DE GINÁSIO POLIESPORTIVO

CONVENIENTE: PREFEITURA MUNICIPAL DE COREMAS - PB

CONVENIADO: MUNICÍPIO DE COREMAS - PB

LOCALIDADE: COREMAS - PB

	DATA	RESPONSÁVEL	RUBRICA	DADOS
DESENHO	AGO/2025	LINCOLN CARTAXO		
CÓPIA				
VISTO				

ESCALAS	DESENHOS	CONVÊNIO
Indicada	- Forma do Pavimento Térreo (Nível 290)	GOVERNO DO ESTADO
		ARQUIVO


Aprovações:

LCL PROJETOS

Av. Gov. Flávio Ribeiro Coutinho, 500, sl. 601
Jardim Oceania, 58037-005 - João Pessoa (PB)
Tel +55 (83) 99924.4447
e-mail: contato@lclprojetos.com

V102


ESC 1:30

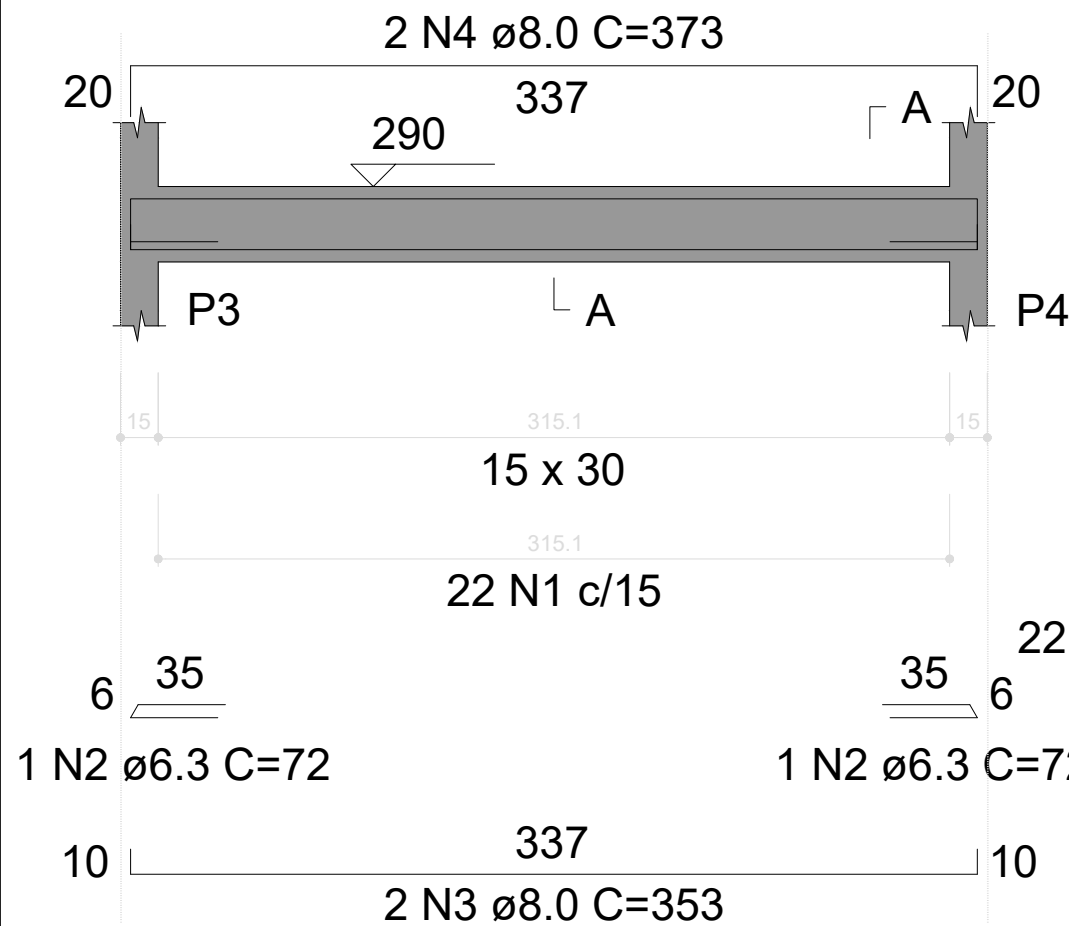

V103

ESC 1:30


SEÇÃO A-A
ESC 1:25

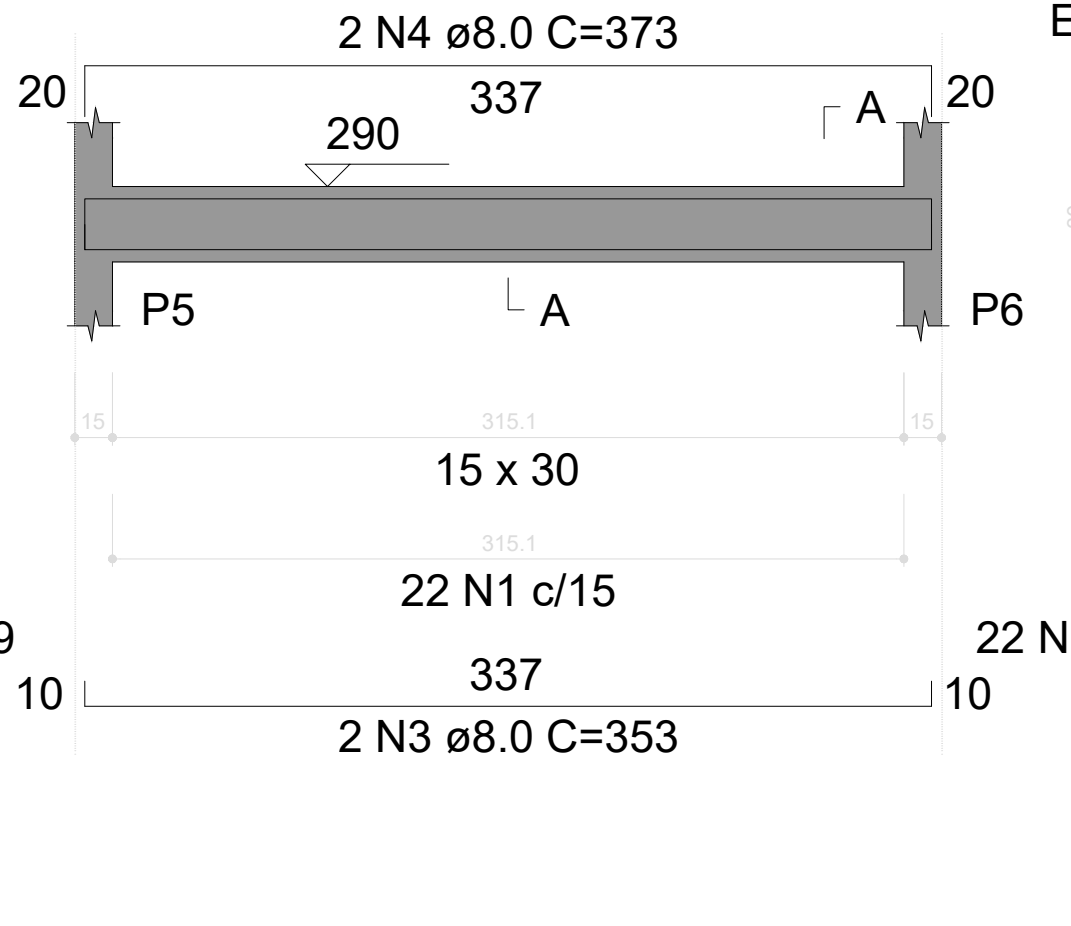


V104

ESC 1:30

SEÇÃO A-A
ESC 1:25

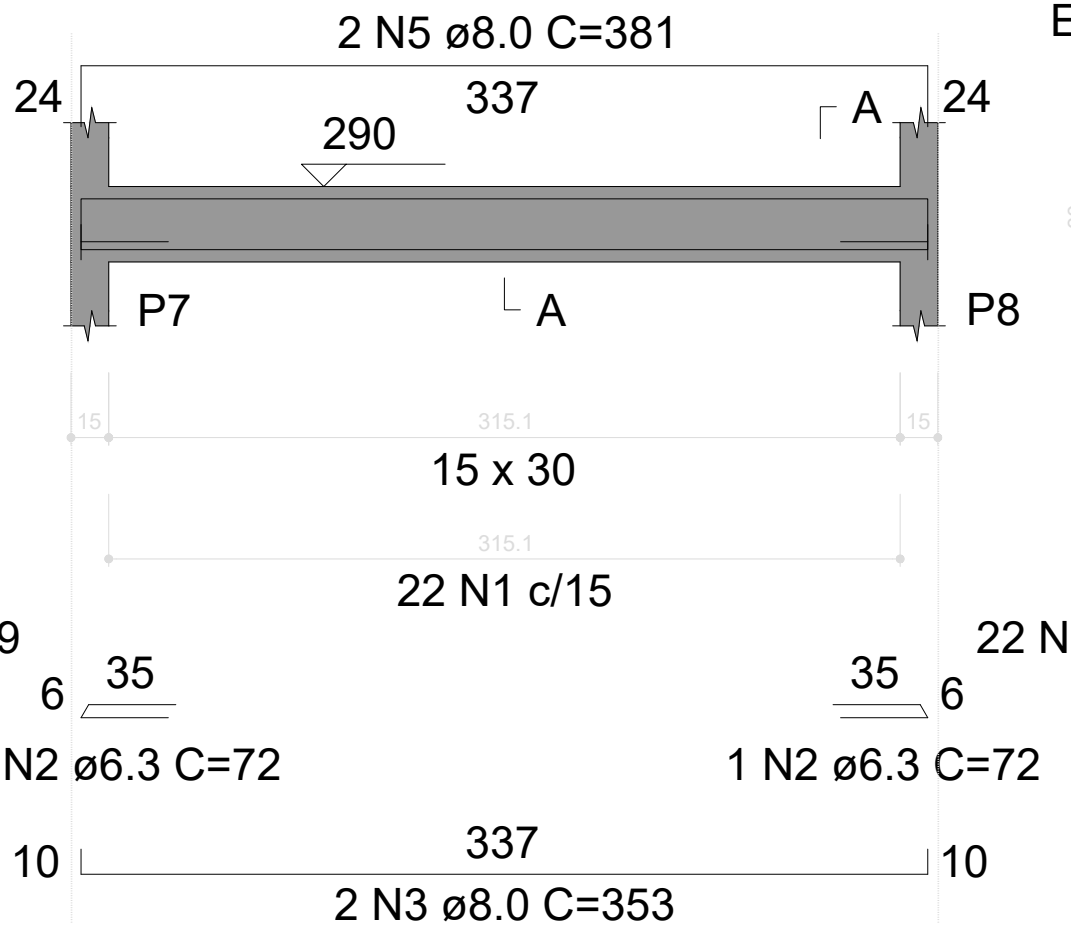

SEÇÃO A-A
ESC 1:25

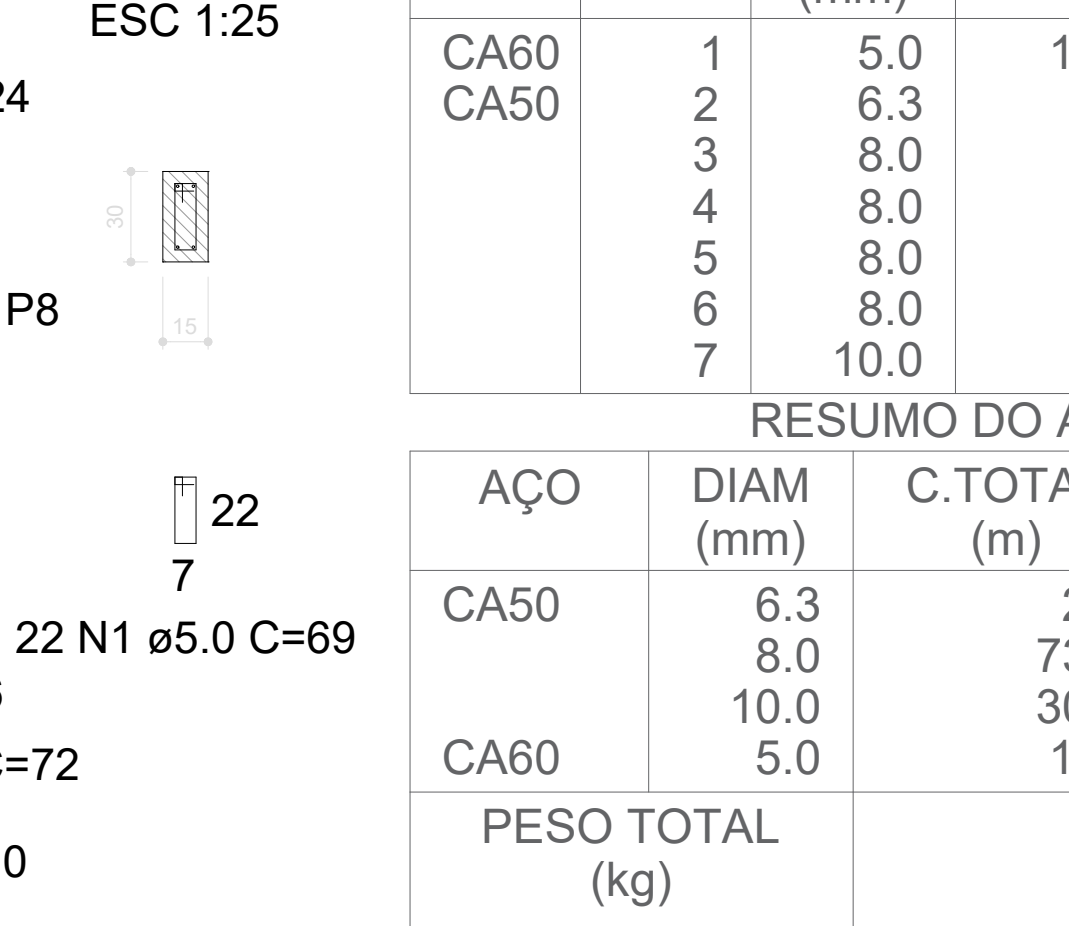

V102
V105

RELAÇÃO DO AÇO

AÇO	N	DIAM (mm)	QUANT	C.UNIT (cm)	C.TOTAL (cm)
CA60	1	5.0	158	69	10902
CA50	2	6.3	4	72	288
	3	8.0	6	353	2118
	4	8.0	4	373	1492
	5	8.0	2	381	762
	6	8.0	4	737	2948
	7	10.0	4	756	3024

RESUMO DO AÇO


AÇO	DIAM (mm)	C.TOTAL (m)	PESO + 0% (kg)
CA50	6.3	2.9	0.7
	8.0	73.2	28.9
	10.0	30.2	18.6
CA60	5.0	109	16.8

PESO TOTAL (kg)


CA50	48.2	Volume de concreto (C-25) = 1.14 m³ Área de forma = 18.94 m²
CA60	16.8	

V105

ESC 1:30

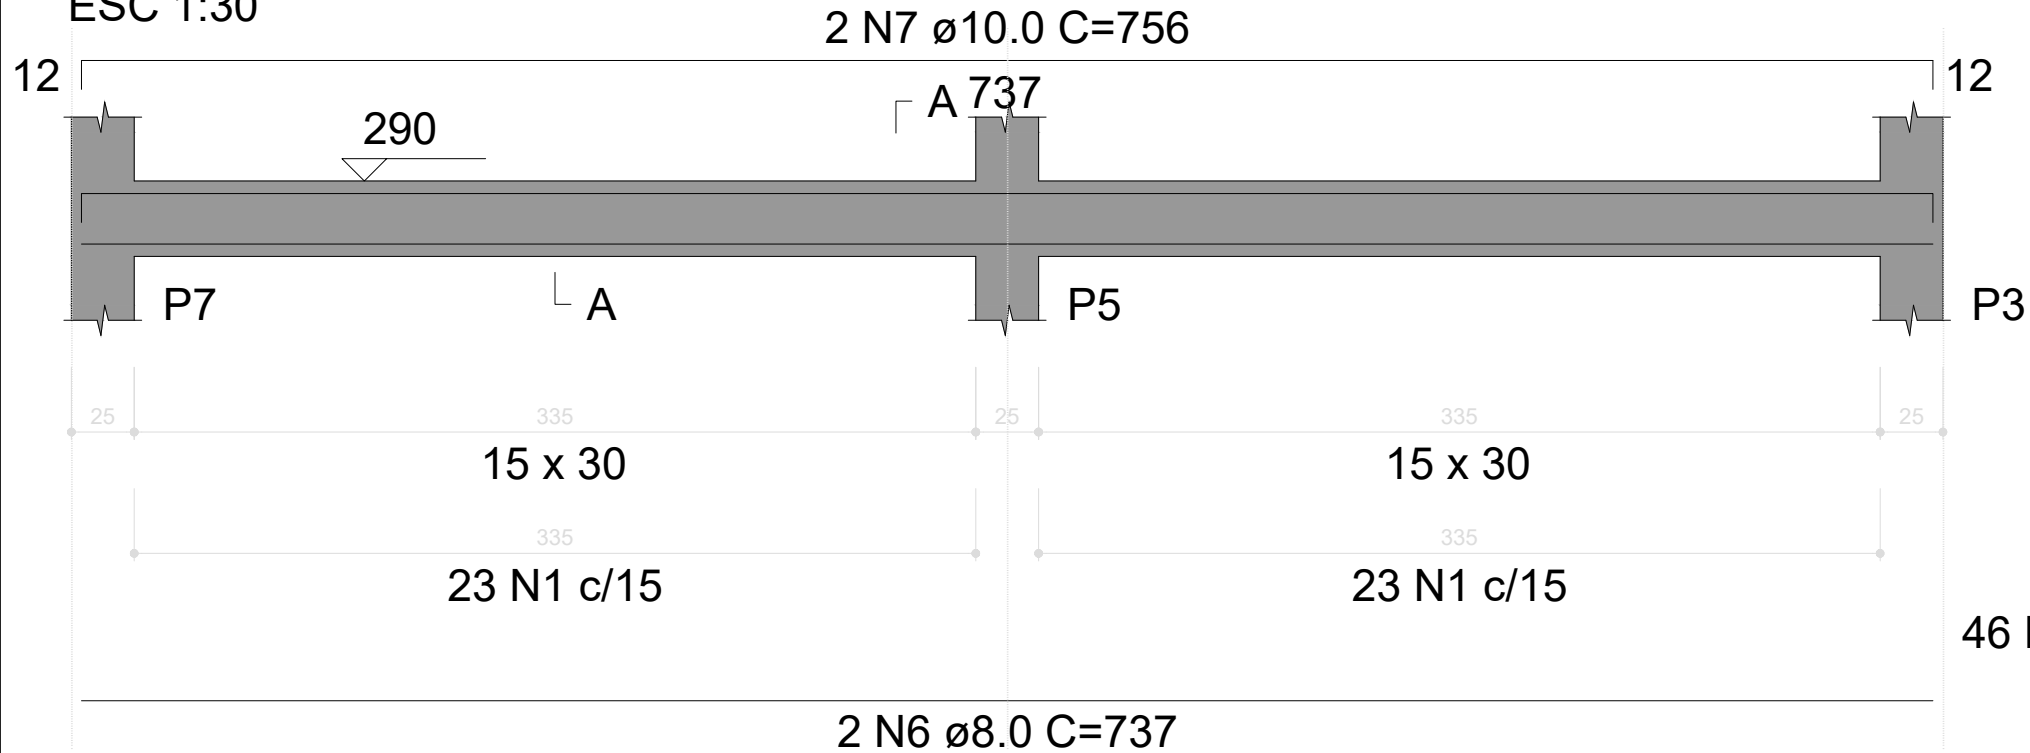


SEÇÃO A-A
ESC 1:25

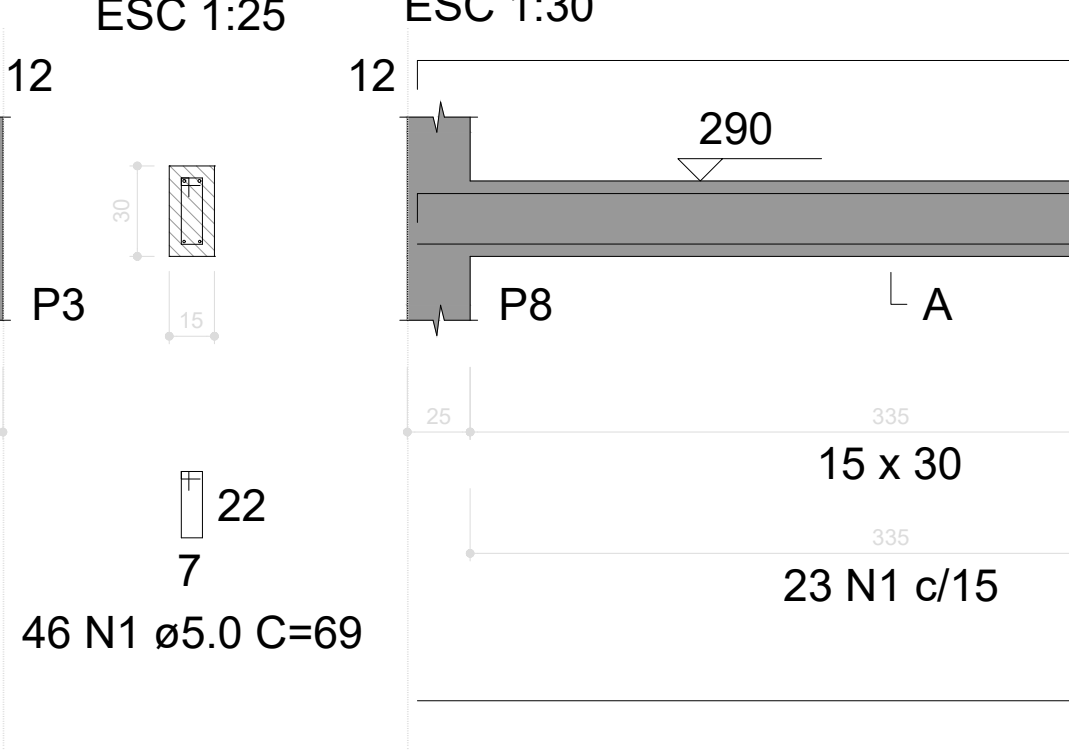


V106

ESC 1:30

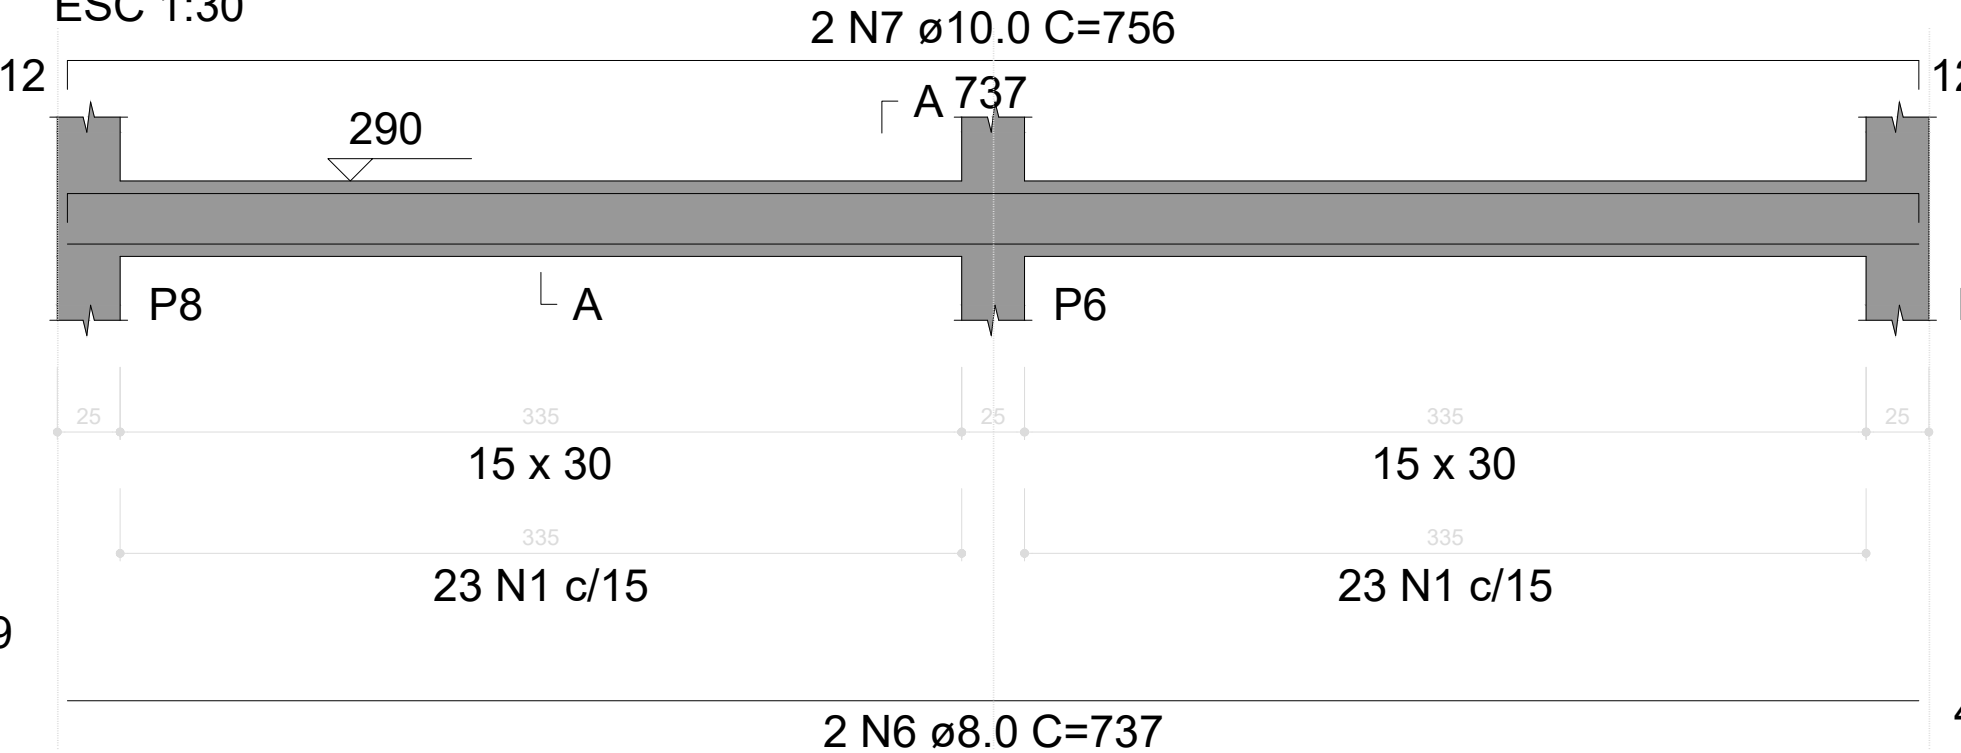

SEÇÃO A-A
ESC 1:25

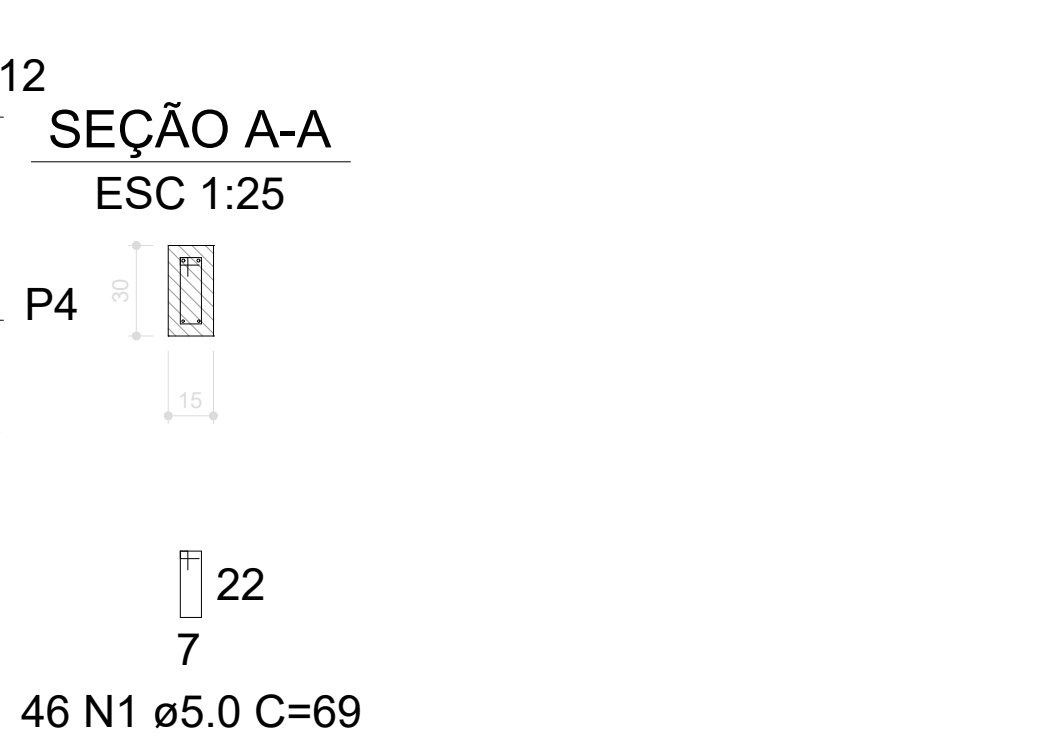

PROPRIETÁRIO: PREFEITURA MUNICIPAL DE COREMAS - PB
LINCOLN CARTAXO DE LIRA JUNIOR:06897861405
Assinado de forma digital por LINCOLN CARTAXO DE LIRA JUNIOR:06897861405
Dados: 2025.08.08 13:33:09 -03'00'

PROJETO: LINCOLN CARTAXO DE LIRA JÚNIOR CREA 160.814.689-8

CONSTRUÇÃO:

FOLHA

05/12

PROJETO: CONSTRUÇÃO DE GINÁSIO POLIESPORTIVO
CONVENIENTE: PREFEITURA MUNICIPAL DE COREMAS - PB
CONVENIADO: MUNICÍPIO DE COREMAS - PB
LOCALIDADE: COREMAS - PB

	DATA	RESPONSÁVEL	RUBRICA	DADOS
DESENHO	AGO/2025	LINCOLN CARTAXO		
CÓPIA				
VISTO				

ESCALAS	DESENHOS	CONVÊNIO
Indicada	- Vigas Térreo	GOVERNO DO ESTADO
		ARQUIVO

Aprovações:



Av. Gov. Flávio Ribeiro Coutinho, 500, sl. 601
Jardim Oceania, 58037-005 - João Pessoa (PB)
Tel +55 (83) 99924.4447
e-mail: contato@lclprojetos.com

P3=P4

VISTA H
ESC 1:25

VISTA B
ESC 1:25

P5=P6=P9=P10

VISTA H
ESC 1:25

VISTA B
ESC 1:25

P7=P8

VISTA H
ESC 1:25

VISTA B
ESC 1:25

2xP3

RELAÇÃO DO AÇO

AÇO	N	DIAM (mm)	QUANT	C.UNIT (cm)	C.TOTAL (cm)
CA60	1	5.0	214	59	12626
CA50	2	10.0	4	286	1144
	3	10.0	24	328	7872
	4	12.5	8	337	2696

RESUMO DO AÇO

AÇO	DIAM (mm)	C.TOTAL (m)	PESO + 0% (kg)
CA50	10.0	90.2	55.6
	12.5	27	26
CA60	5.0	126.3	19.5
PESO TOTAL (kg)			
CA50	81.6		
CA60	19.5		

Volume de concreto (C-25) = 0.87 m³

Área de forma = 18.56 m²

PROPRIETÁRIO: PREFEITURA MUNICIPAL DE COREMAS - PB
LINCOLN CARTAXO DE LIRA JUNIOR:06897861405
Assinado de forma digital por LINCOLN CARTAXO DE LIRA JUNIOR:06897861405
Dados: 2025.08.08 13:32:54 -03'00'

PROJETO: LINCOLN CARTAXO DE LIRA JÚNIOR CREA 160.814.689-8

CONSTRUÇÃO:

FOLHA
06/12


PROJETO: CONSTRUÇÃO DE GINÁSIO POLIESPORTIVO
CONVENENTE: PREFEITURA MUNICIPAL DE COREMAS - PB
CONVENIADO: MUNICÍPIO DE COREMAS - PB
LOCALIDADE: COREMAS - PB

	DATA	RESPONSÁVEL	RUBRICA	DADOS
DESENHO	AGO/2025	LINCOLN CARTAXO		
CÓPIA				
VISTO				
ESCALAS	DESENHOS			CONVÊNIO
Indicada	- Pilares Térreo			GOVERNO DO ESTADO
				ARQUIVO


Aprovações:



Av. Gov. Flávio Ribeiro Coutinho, 500, sl. 601
Jardim Oceania, 58037-005 - João Pessoa (PB)
Tel +55 (83) 99924.4447
e-mail: contato@lclprojetos.com

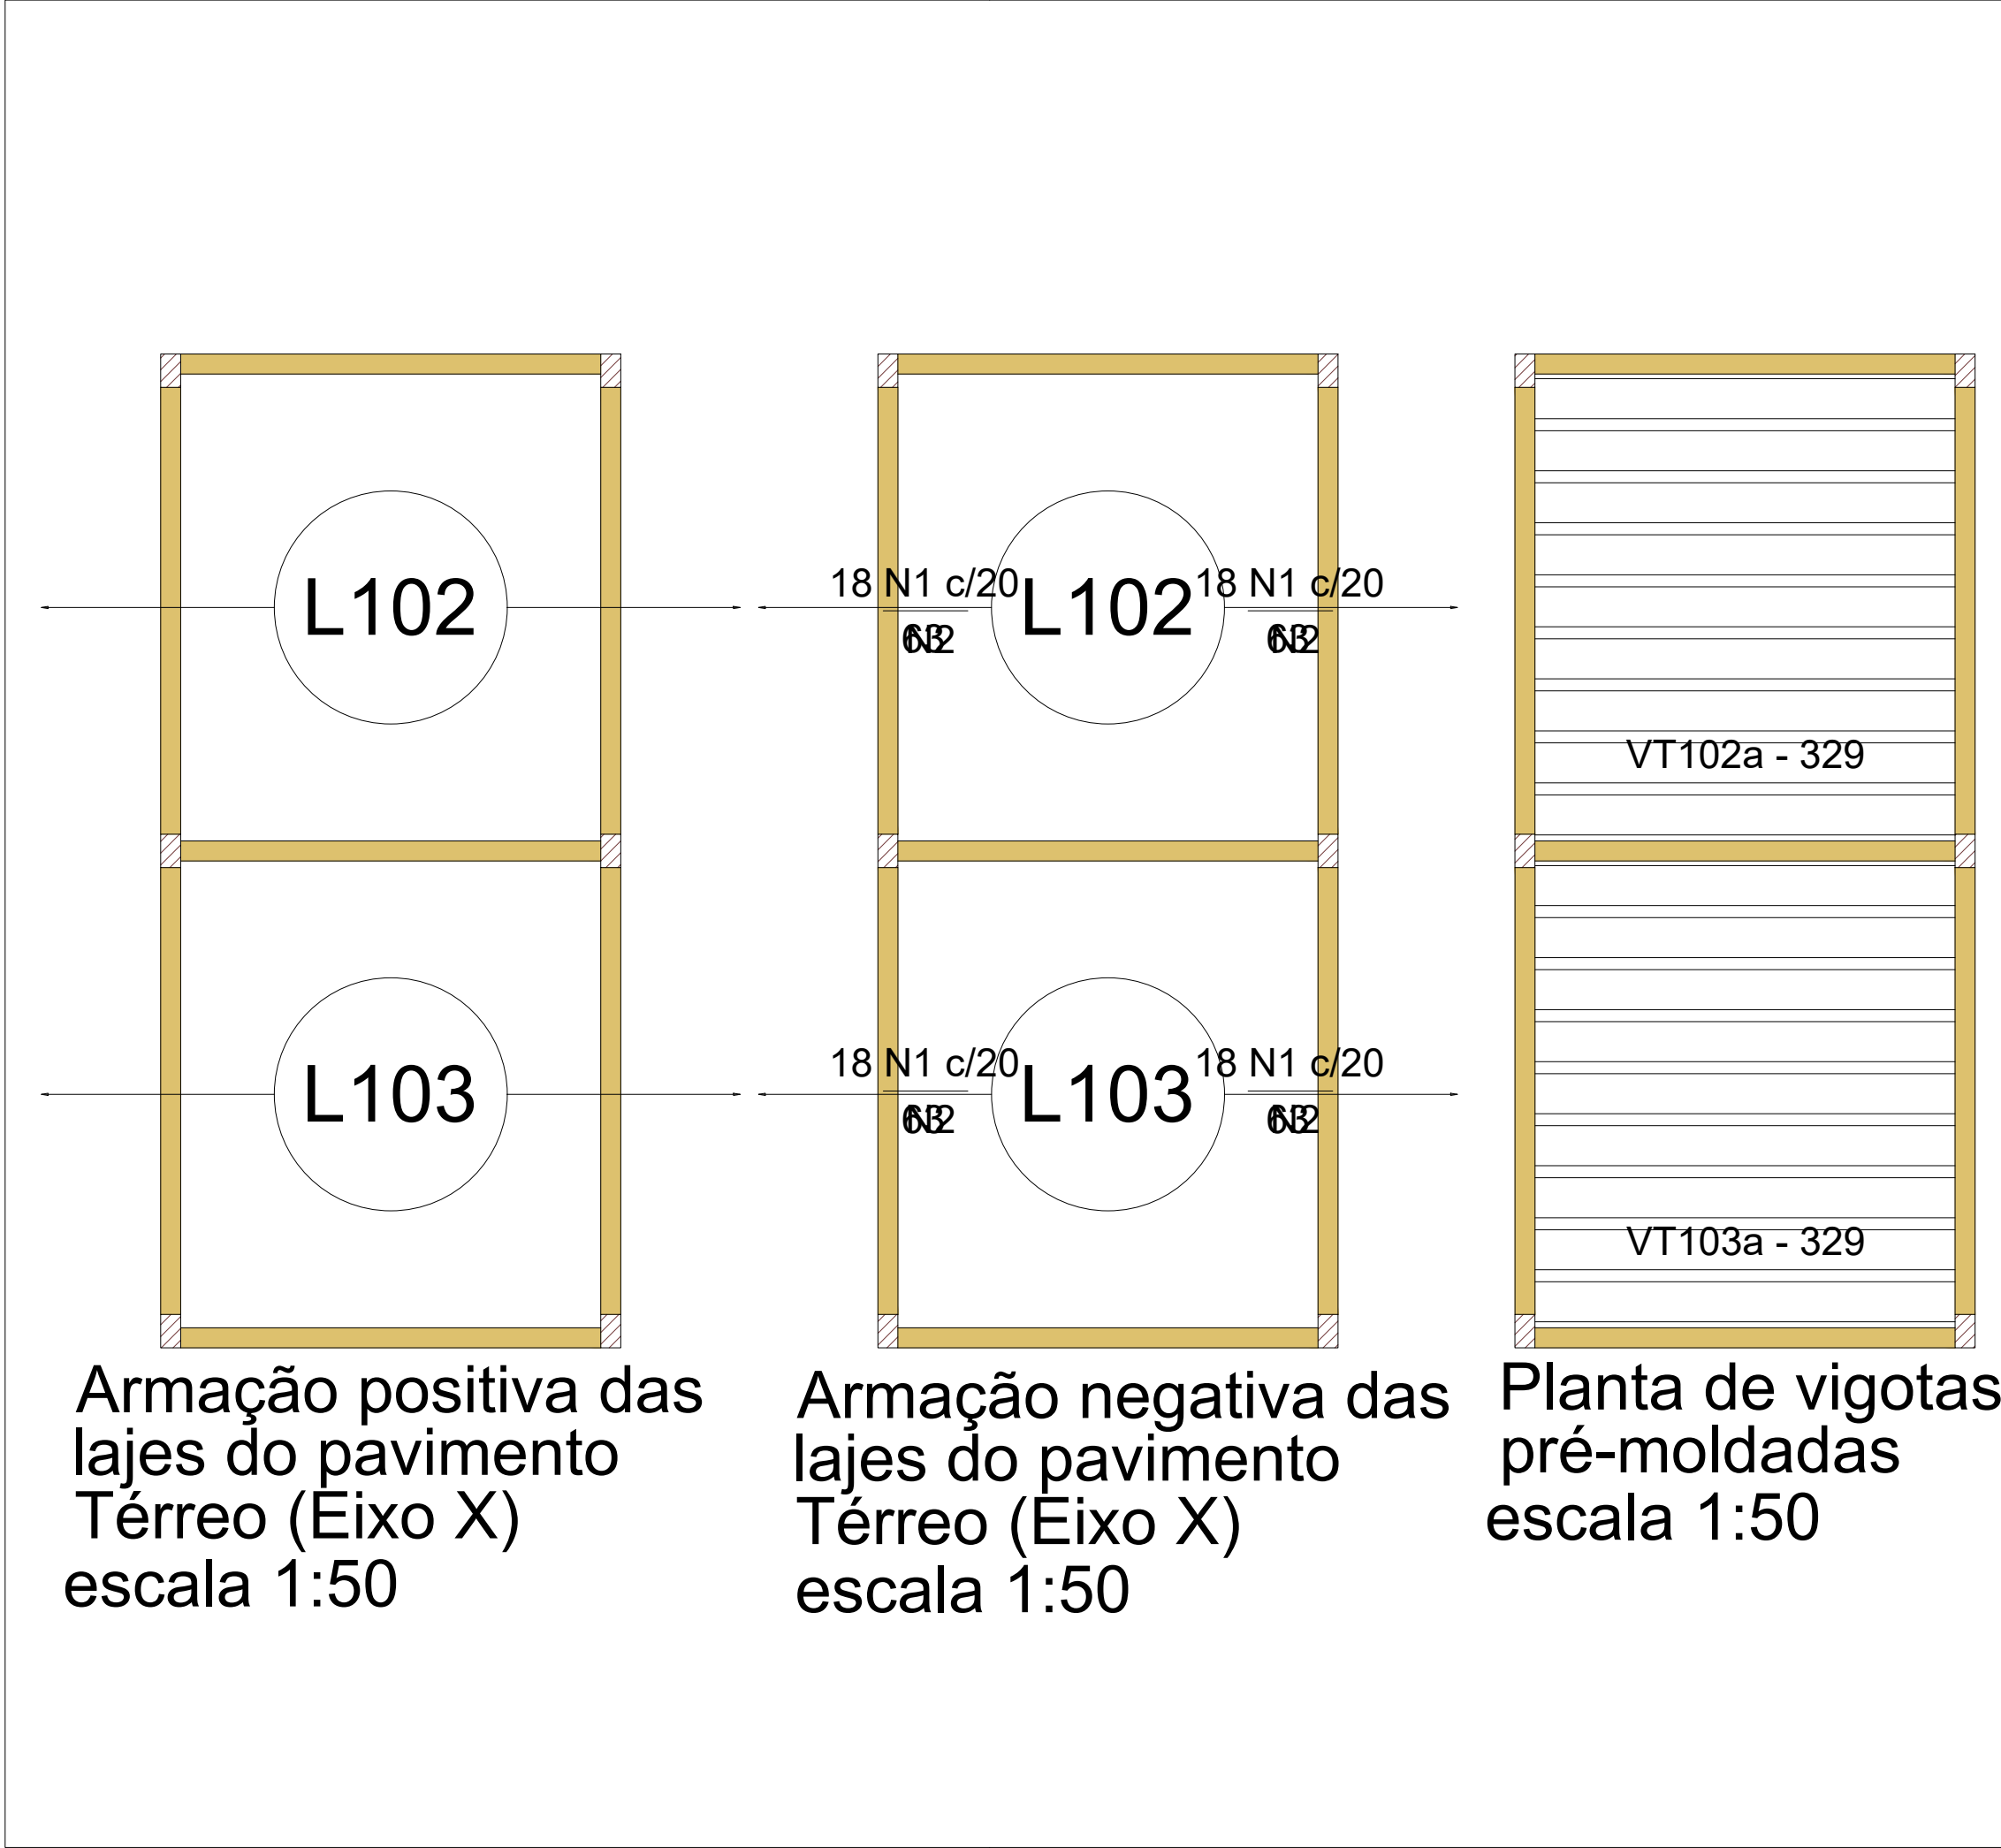

DETALHE DA ARMADURA DE SUPERIOR DE CONTINUIDADE DA LAJE E MONTAGEM DA ARMADURA DE DISTRIBUIÇÃO

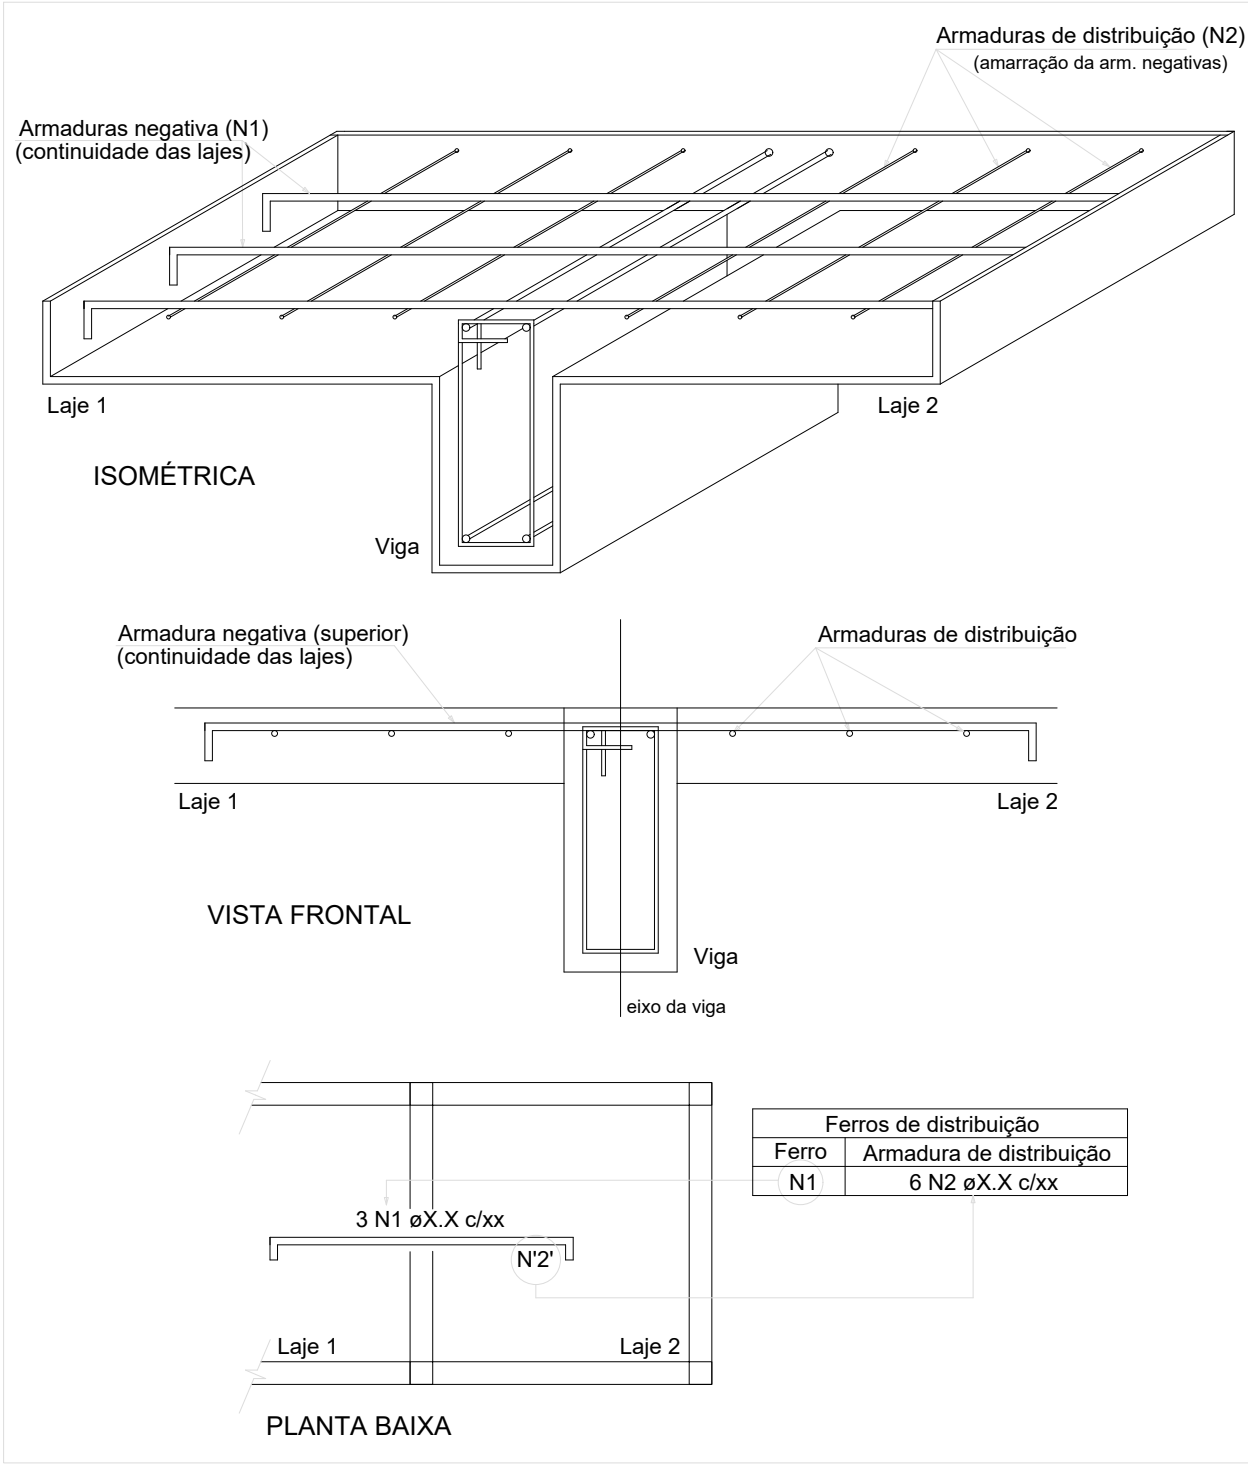

RELAÇÃO DO AÇO

Negativos X

AÇO	N	DIAM (mm)	QUANT	C.UNIT (cm)	C.TOTAL (cm)
CA60	1	5.0	72	63	4536
	2	5.0	16	353	5648

RESUMO DO AÇO

AÇO	DIAM (mm)	C.TOTAL (m)	PESO + 0% (kg)
CA60	5.0	101.8	15.7

PESO TOTAL (kg)	
CA60 15.7	Volume de concreto (C-25) = 1.24 m³ Área de forma = 0.00 m²

Armaduras de distribuição	
Armadura	Armadura de distribuição
N1	4 N2 ø5.0 c/20 C=353
N1	4 N2 ø5.0 c/20 C=353
N1	4 N2 ø5.0 c/20 C=353
N1	4 N2 ø5.0 c/20 C=353

PROPRIETÁRIO: PREFEITURA MUNICIPAL DE COREMAS - PB
LINCOLN CARTAXO DE LIRA JUNIOR:06897861405
Assinado de forma digital por LINCOLN CARTAXO DE LIRA JUNIOR:06897861405
Dados: 2025.08.08 13:29:38 -03'00'

PROJETO: LINCOLN CARTAXO DE LIRA JÚNIOR CREA 160.814.689-8

CONSTRUÇÃO:

FOLHA
07/12
PROJETO: CONSTRUÇÃO DE GINÁSIO POLIESPORTIVO
CONVENIENTE: PREFEITURA MUNICIPAL DE COREMAS - PB
CONVENIADO: MUNICÍPIO DE COREMAS - PB
LOCALIDADE: COREMAS - PB


	DATA	RESPONSÁVEL	RUBRICA	DADOS
DESENHO	AGO/2025	LINCOLN CARTAXO		
CÓPIA				
VISTO				

ESCALAS	DESENHOS	CONVÊNIO
Indicada	- Laje	GOVERNO DO ESTADO
		ARQUIVO

Aprovações:



Av. Gov. Flávio Ribeiro Coutinho, 500, sl. 601
Jardim Oceania, 58037-005 - João Pessoa (PB)
Tel +55 (83) 99924.4447
e-mail: contato@lclprojetos.com

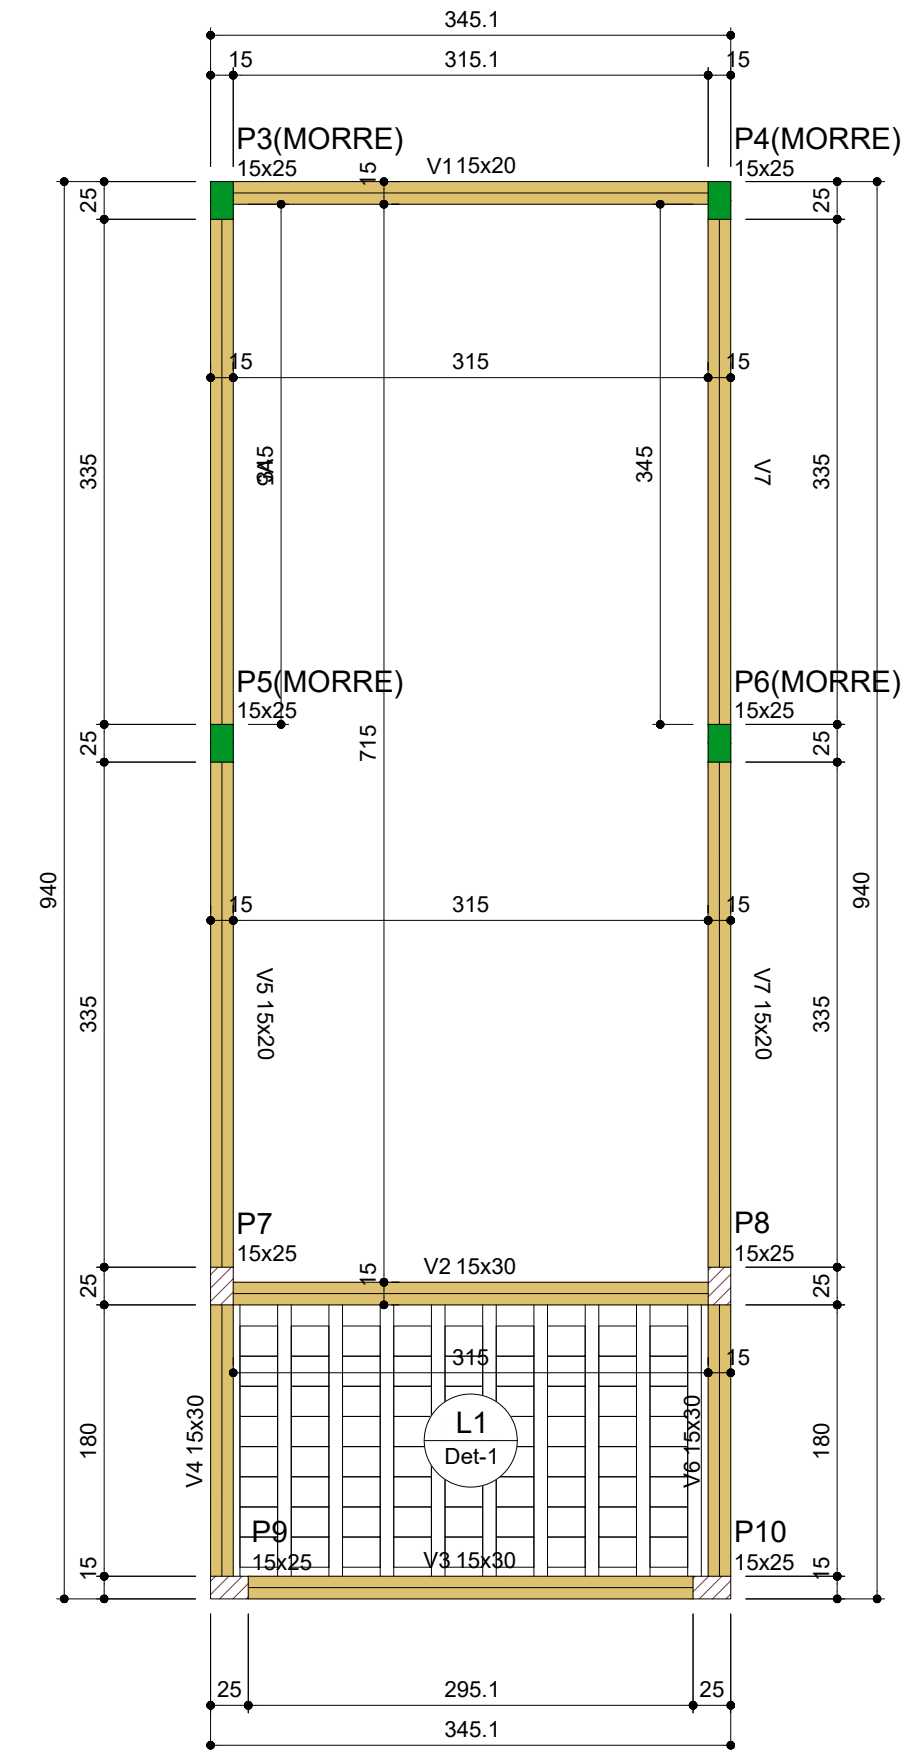

Forma do pavimento Fundo de Caixa d'água (Nível 390)
escala 1:50

Vigas			
Nome	Seção (cm)	Elevação (cm)	Nível (cm)
V1	15x20	0	390
V2	15x30	0	390
V3	15x30	0	390
V4	15x30	0	390
V5	15x20	0	390
V6	15x30	0	390
V7	15x20	0	390

Pilares			
Nome	Seção (cm)	Elevação (cm)	Nível (cm)
P3	15x25	0	390
P4	15x25	0	390
P5	15x25	0	390
P6	15x25	0	390
P7	15x25	0	390
P8	15x25	0	390
P9	15x25	0	390
P10	15x25	0	390


Legenda dos pilares	
	Pilar que morre
	Pilar que passa

Legenda das vigas e paredes	
	Viga

Lajes							
Dados					Sobrecarga (kgf/m²)		
Nome	Tipo	Altura (cm)	Elevação (cm)	Nível (cm)	Peso próprio (kgf/m²)	Adicional	Acidental
L1	Treliçada 1D	12	0	390	259	342	50

Área de lajes				Características dos materiais	
Tipo	Altura (cm)	Bloco de Enchimento	Área (m²)	fck (kgf/cm²)	Ecs (kgf/cm²)
Treliçada 1D	12	B8/25/20	5.67	250	241500

Blocos de enchimento					
Detalhe	Tipo	Nome	Dimensões(cm)		
			hb	bx	by
1	Lajota cerâmica	B8/25/20	8	25	20

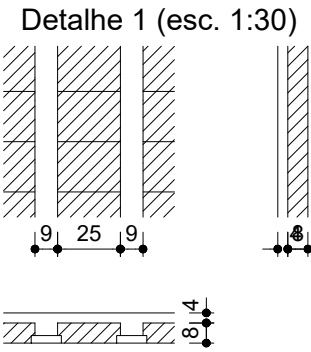

PROPRIETÁRIO: PREFEITURA MUNICIPAL DE COREMAS - PB
LINCOLN CARTAXO DE LIRA JUNIOR:06897861405
Assinado de forma digital por LINCOLN CARTAXO DE LIRA JUNIOR:06897861405
Dados: 2025.08.08 12:30:09 -03'00'

PROJETO: LINCOLN CARTAXO DE LIRA JÚNIOR CREA 160.814.689-8

CONSTRUÇÃO:


FOLHA 08/12
PROJETO: CONSTRUÇÃO DE GINÁSIO POLIESPORTIVO
CONVENIENTE: PREFEITURA MUNICIPAL DE COREMAS - PB
CONVENIADO: MUNICÍPIO DE COREMAS - PB
LOCALIDADE: COREMAS - PB

	DATA	RESPONSÁVEL	RUBRICA	DADOS
DESENHO	AGO/2025	LINCOLN CARTAXO		
CÓPIA				
VISTO				
ESCALAS	DESENHOS	CONVÊNIO		
Indicada	- Forma do Pavimento Fundo de Caixa d'água (Nível 390)	GOVERNO DO ESTADO		
		ARQUIVO		


Aprovações:




Av. Gov. Flávio Ribeiro Coutinho, 500, sl. 601
Jardim Oceania, 58037-005 - João Pessoa (PB)
Tel +55 (83) 99924.4447
e-mail: contato@lclprojetos.com

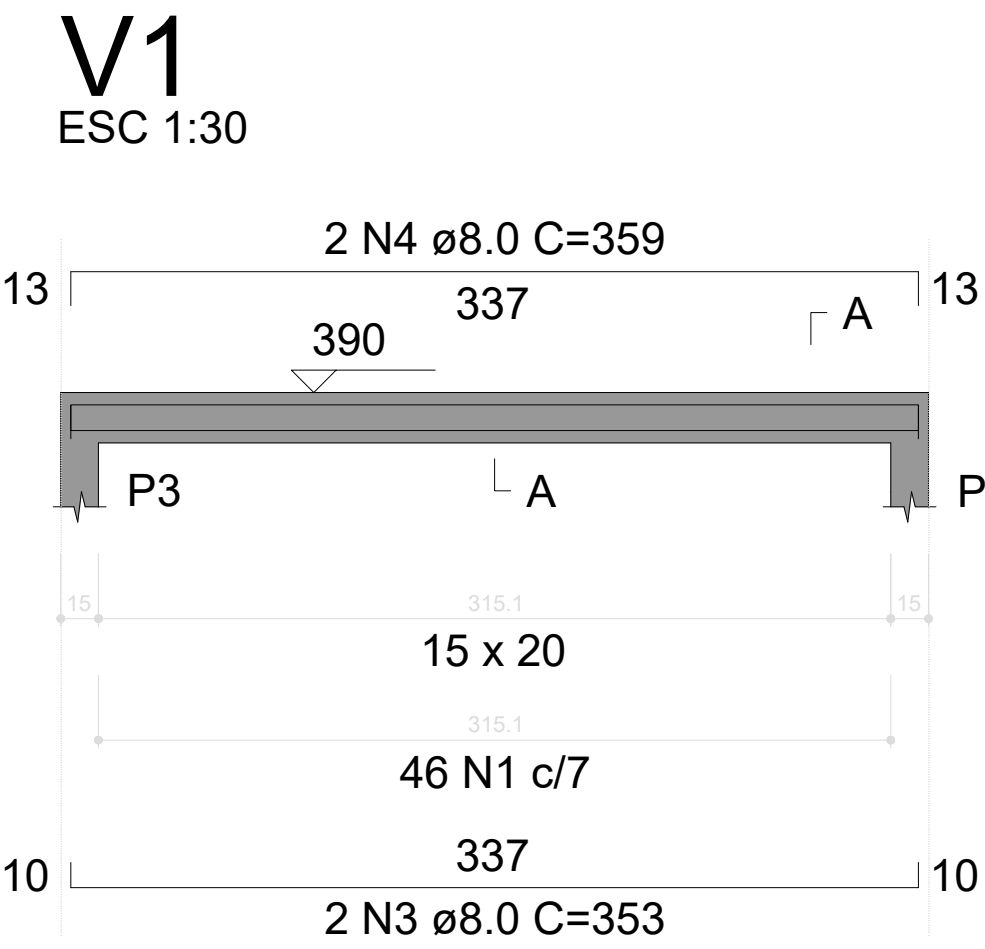


SEÇÃO A-A
ESC 1:25

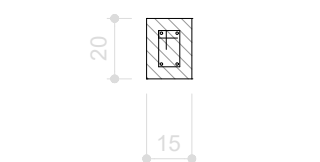


46 N1 ø5.0 C=49

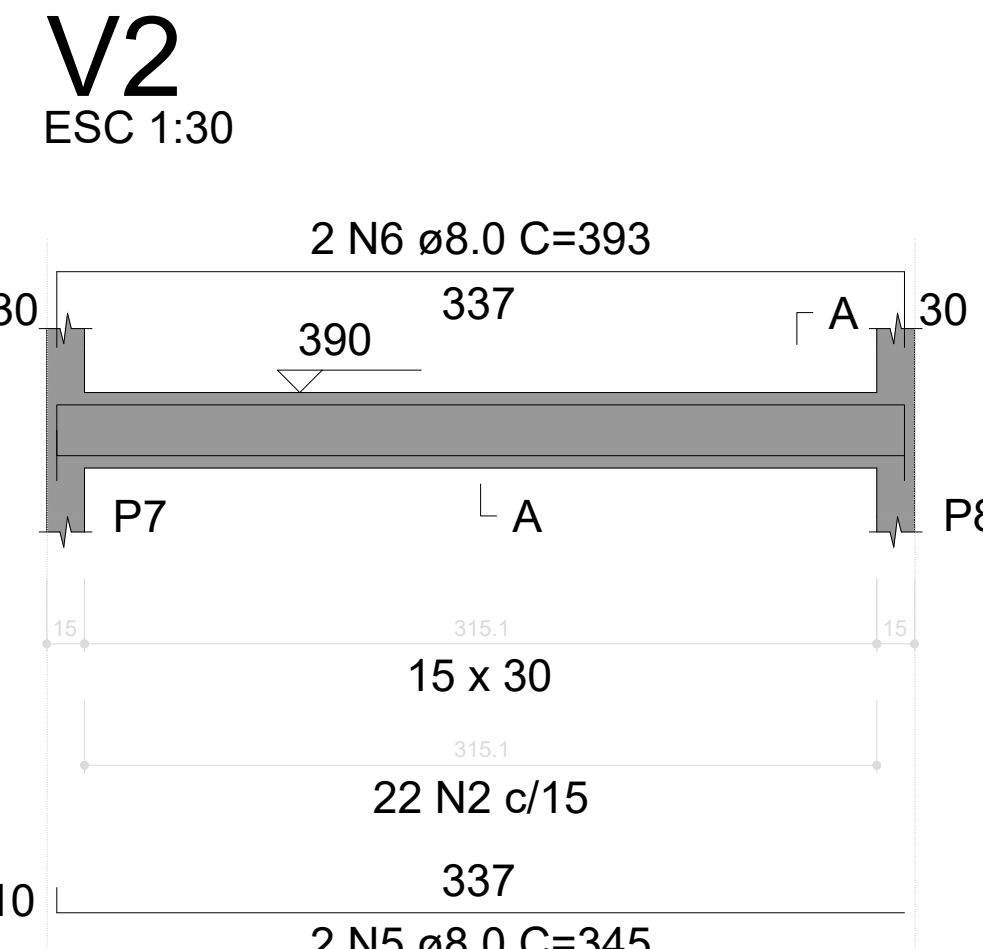


SEÇÃO A-A
ESC 1:25

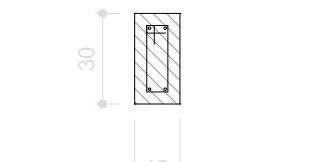


22 N2 ø5.0 C=69

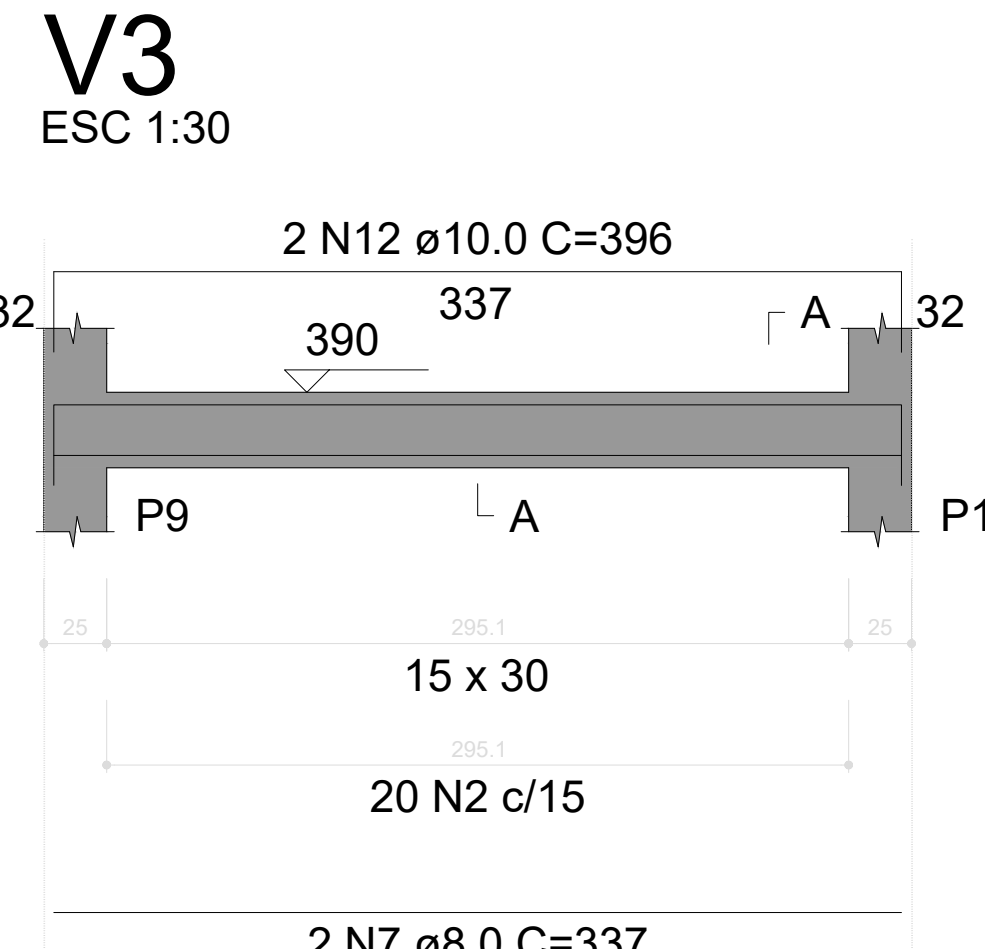

SEÇÃO A-A
ESC 1:25

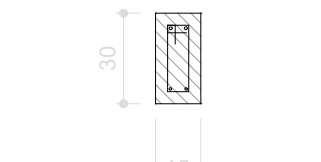


20 N2 ø5.0 C=69

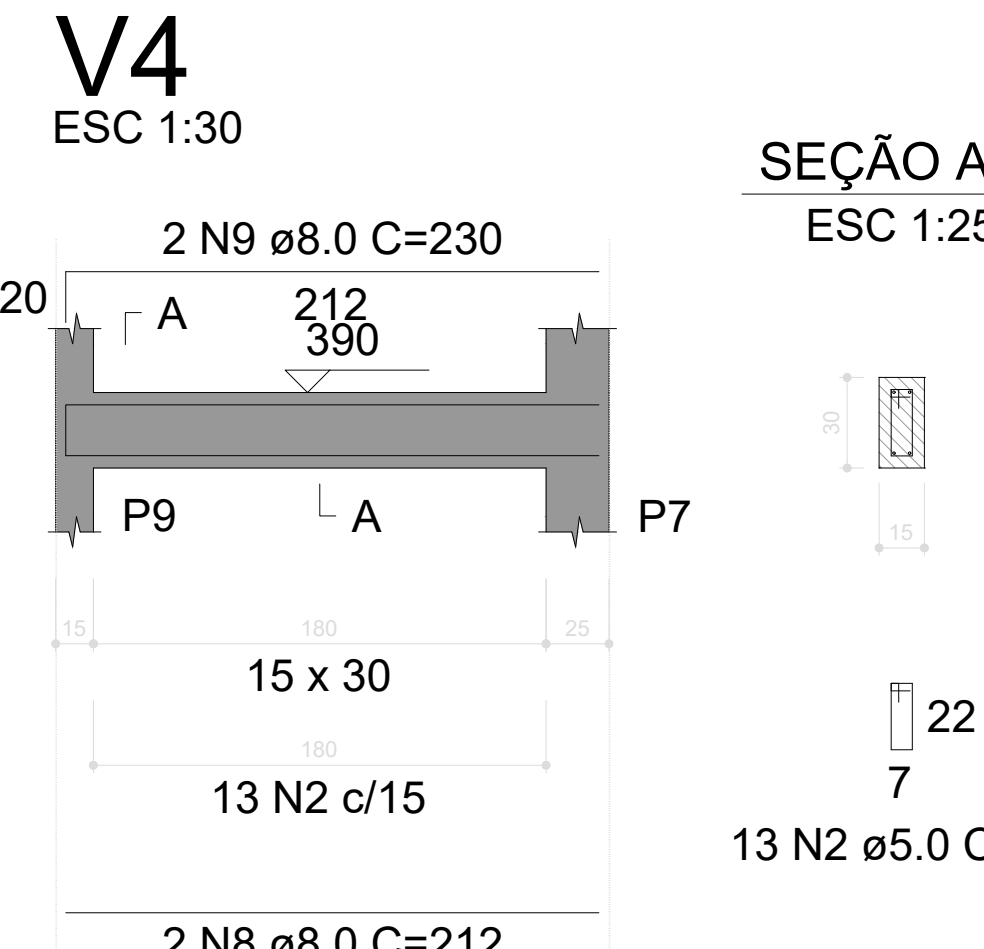


SEÇÃO A-A
ESC 1:25




13 N2 ø5.0 C=69

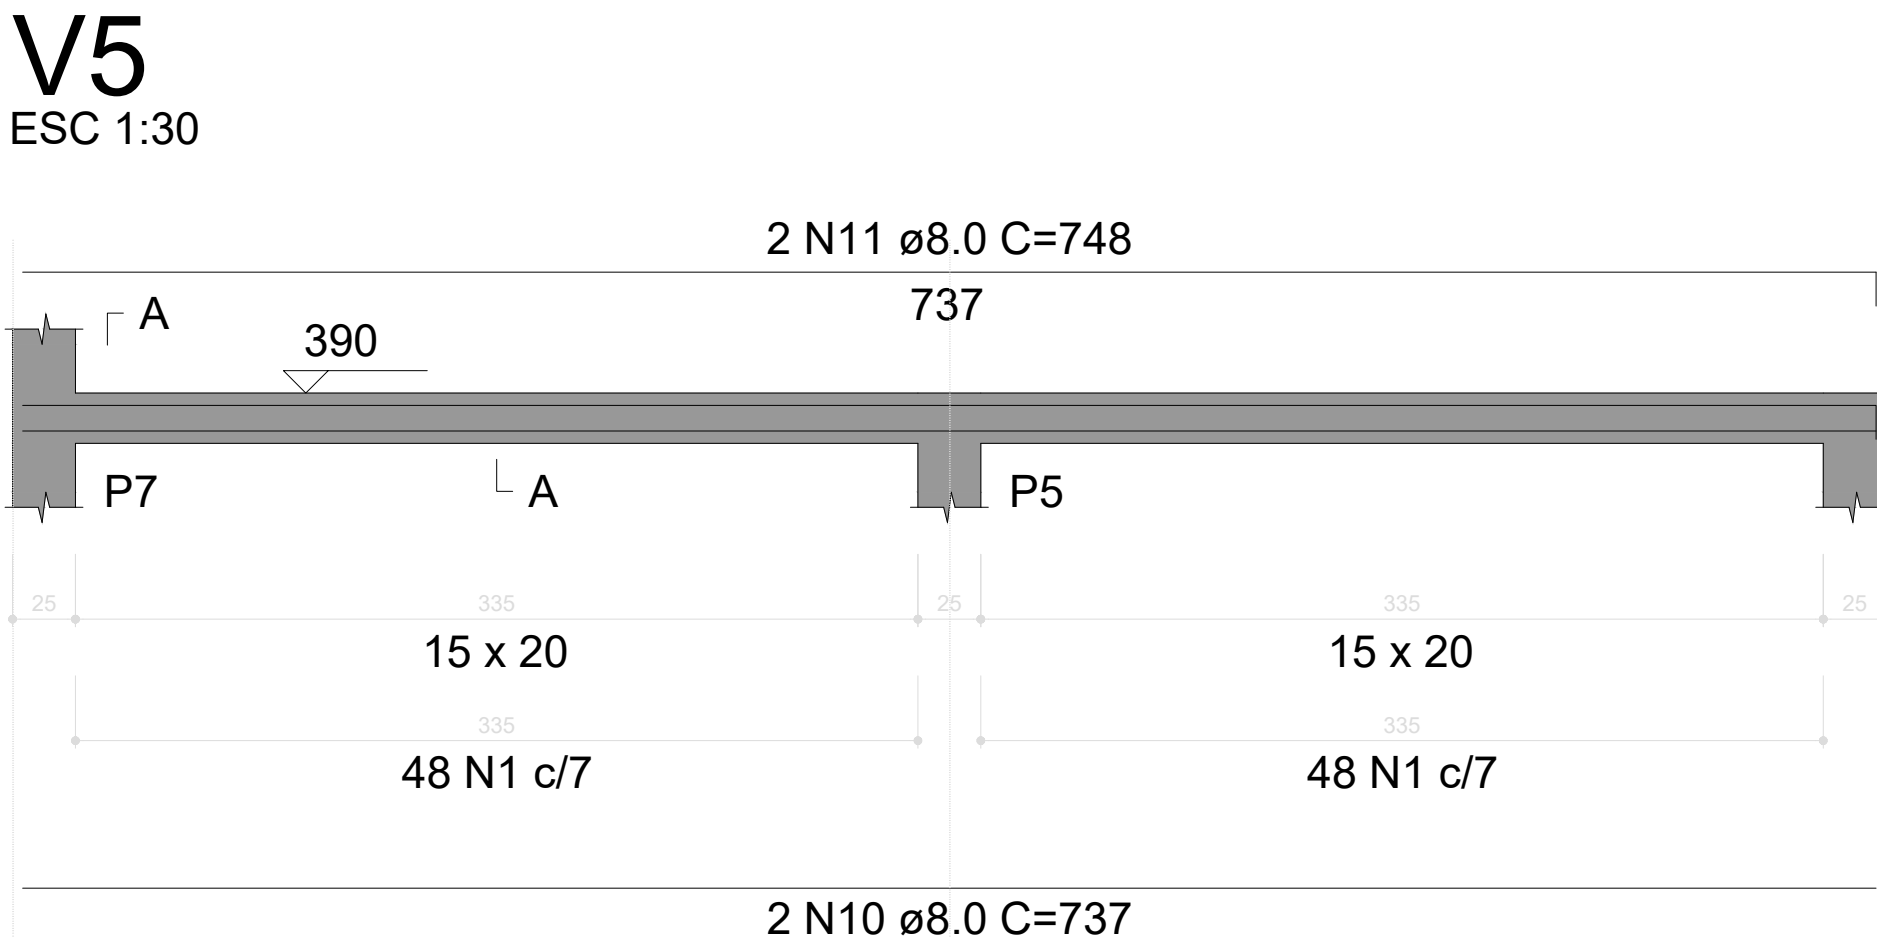


SEÇÃO A-A
ESC 1:25

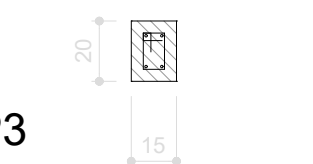


96 N1 ø5.0 C=49

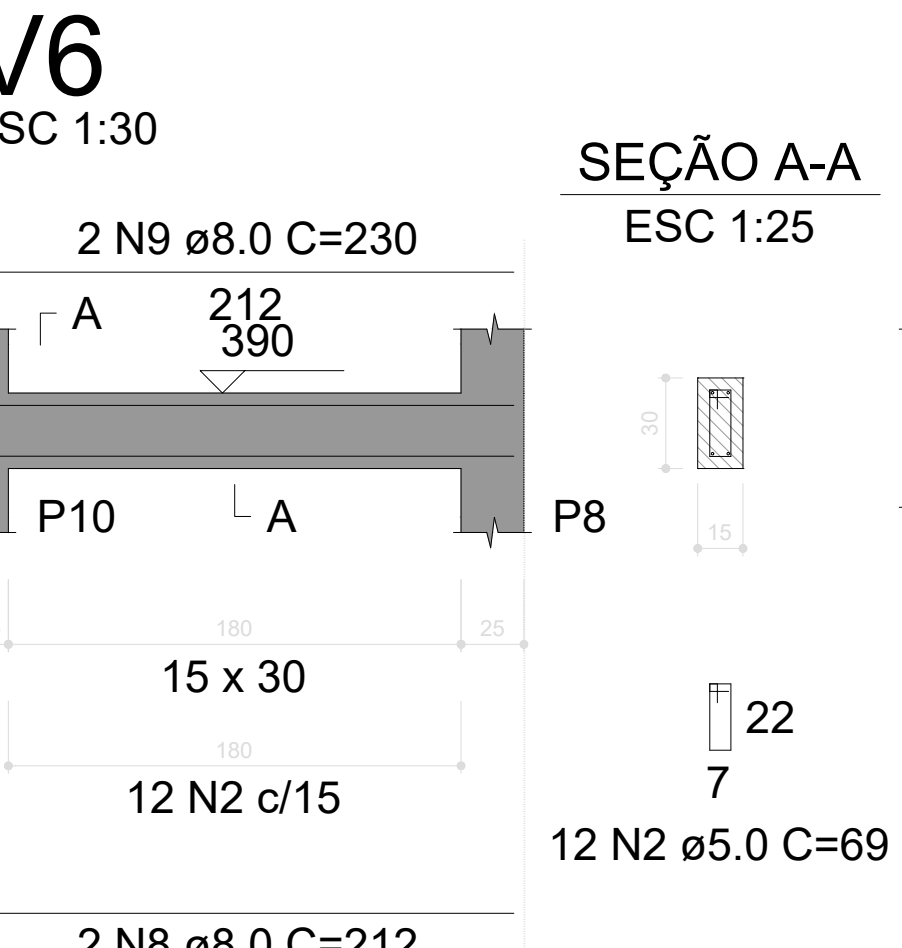

SEÇÃO A-A
ESC 1:25

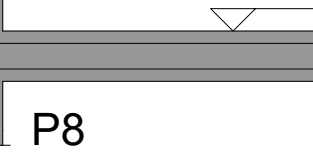

12 N2 ø5.0 C=69

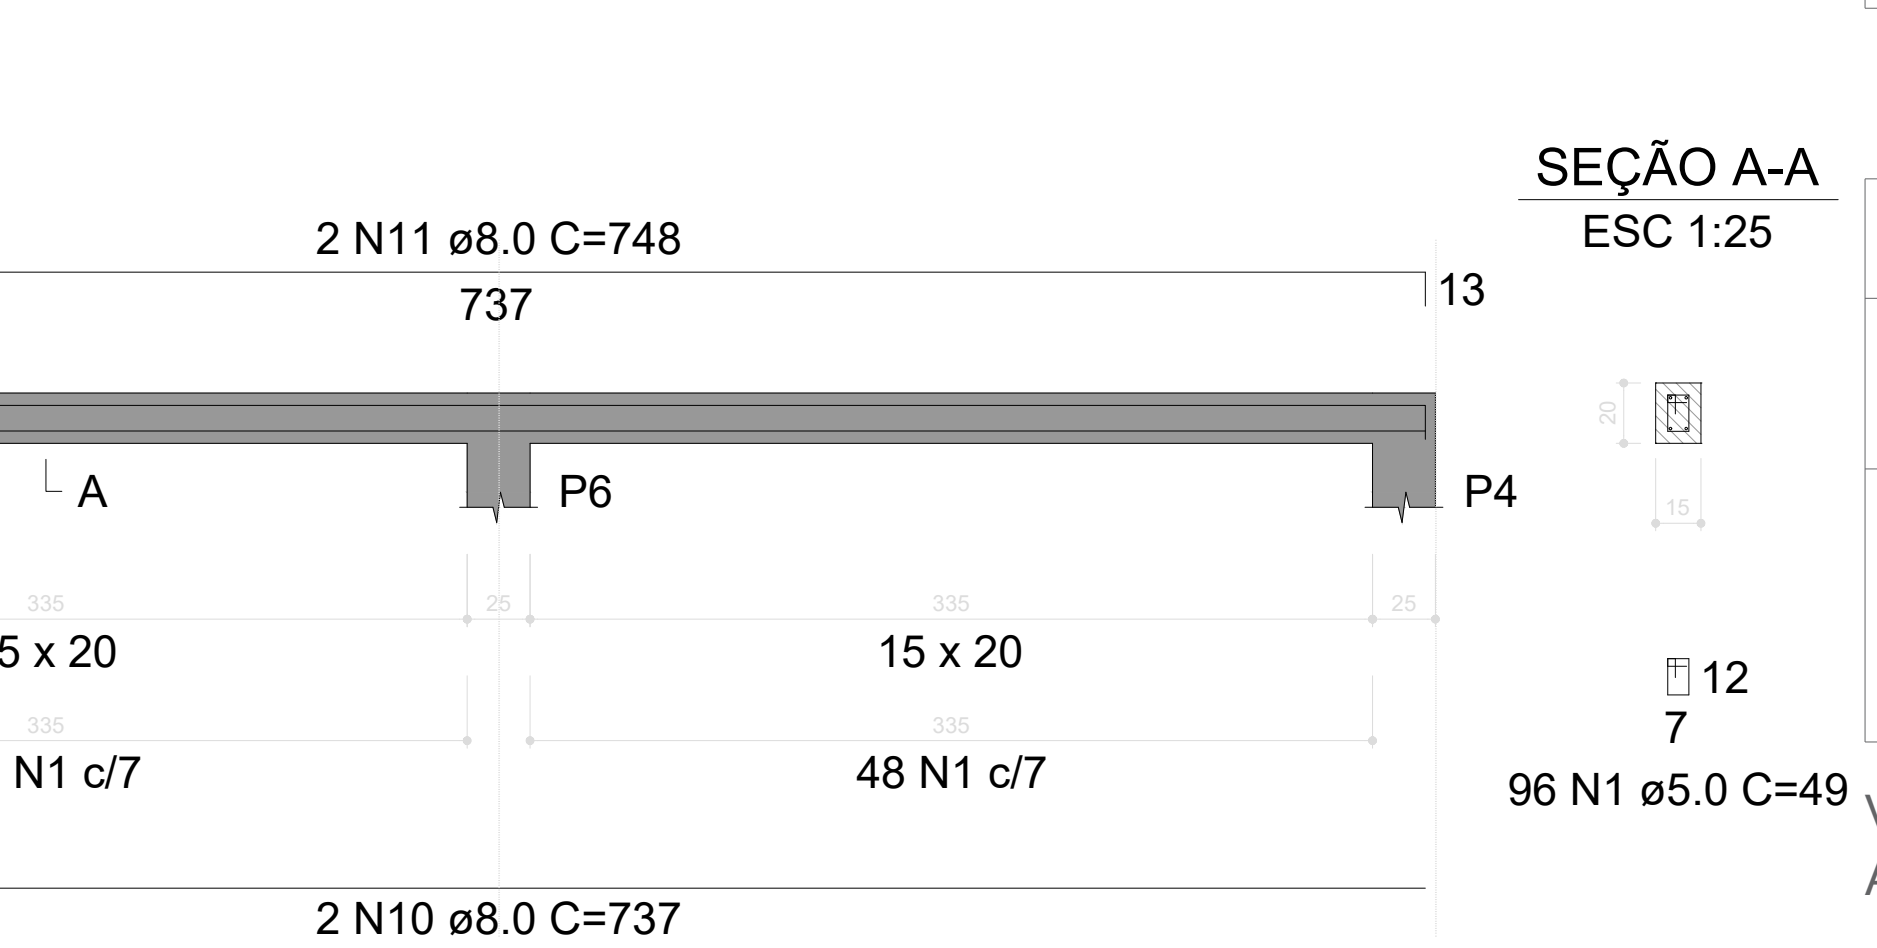

SEÇÃO A-A
ESC 1:25



96 N1 ø5.0 C=49

RELAÇÃO DO AÇO

AÇO	N	DIAM (mm)	QUANT	C.UNIT (cm)	C.TOTAL (cm)
CA60	1	5.0	238	49	11662
	2	5.0	67	69	4623
CA50	3	8.0	2	353	706
	4	8.0	2	359	718
	5	8.0	2	345	690
	6	8.0	2	393	786
	7	8.0	2	337	674
	8	8.0	4	212	848
	9	8.0	4	230	920
	10	8.0	4	737	2948
	11	8.0	4	748	2992
	12	10.0	2	396	792

RESUMO DO AÇO

AÇO	DIAM (mm)	C.TOTAL (m)	PESO + 0% (kg)
CA50	8.0	112.8	44.5
	10.0	7.9	4.9
CA60	5.0	162.8	25.1
PESO TOTAL (kg)			
CA50		49.4	
CA60		25.1	

Volume de concreto (C-25) = 1.06 m³

Área de forma = 18.57 m²

PROPRIETÁRIO: PREFEITURA MUNICIPAL DE COREMAS - PB
LINCOLN CARTAXO DE LIRA JUNIOR:06897861405
PROJETO: LINCOLN CARTAXO DE LIRA JÚNIOR CREA 160.814.689-8

Assinado de forma digital por LINCOLN CARTAXO DE LIRA JUNIOR:06897861405
Dados: 2025.08.08 12:30:41 -03'00'

CONSTRUÇÃO:

FOLHA **09/12**
PROJETO: CONSTRUÇÃO DE GINÁSIO POLIESPORTIVO
CONVENIENTE: PREFEITURA MUNICIPAL DE COREMAS - PB
CONVENIADO: MUNICÍPIO DE COREMAS - PB
LOCALIDADE: COREMAS - PB

DESENHO	DATA	RESPONSÁVEL	RUBRICA	DADOS
CÓPIA	AGO/2025	LINCOLN CARTAXO		
VISTO				


ESCALAS	DESENHOS	CONVÊNIO
Indicada	- Vigas Caixa D'água	GOVERNO DO ESTADO
		ARQUIVO

Aprovações:


P3=P4=P5=P6

FUNDO DE CAIXA D'ÁGUA - L3

SEÇÃO
ESC 1:20

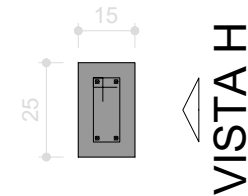

VISTA B

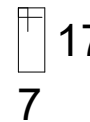

10 N1 ø5.0 C=59

VISTA H
ESC 1:10


VISTA B
ESC 1:10

96
4 N2 ø10.0 C=96


P7=P8=P9=P10

FUNDO DE CAIXA D'ÁGUA - L3

SEÇÃO
ESC 1:20

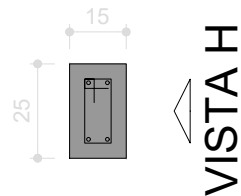

VISTA B

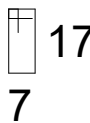

10 N1 ø5.0 C=59

VISTA H
ESC 1:10

VISTA B
ESC 1:10

38

100
4 N3 ø10.0 C=138

RELAÇÃO DO AÇO

4xP3

4xP7

AÇO	N	DIAM (mm)	QUANT	C.UNIT (cm)	C.TOTAL (cm)
CA60	1	5.0	80	59	4720
CA50	2	10.0	16	96	1536
	3	10.0	16	138	2208

RESUMO DO AÇO

AÇO	DIAM (mm)	C.TOTAL (m)	PESO + 0% (kg)
CA50	10.0	37.4	23.1
CA60	5.0	47.2	7.3

PESO TOTAL (kg)

CA50 23.1
CA60 7.3

Volume de concreto (C-25) = 0.30 m³
Área de forma = 6.40 m²

PROPRIETÁRIO: PREFEITURA MUNICIPAL DE COREMAS - PB

LINCOLN CARTAXO DE LIRA JUNIOR:06897861405

Assinado de forma digital por LINCOLN CARTAXO DE LIRA JUNIOR:06897861405
Dados: 2025.08.08 12:30:24 -03'00'

PROJETO: LINCOLN CARTAXO DE LIRA JÚNIOR CREA 160.814.689-8

CONSTRUÇÃO:

FOLHA

PROJETO: CONSTRUÇÃO DE GINÁSIO POLIESPORTIVO

CONVENIENTE: PREFEITURA MUNICIPAL DE COREMAS - PB

CONVENIADO: MUNICÍPIO DE COREMAS - PB

LOCALIDADE: COREMAS - PB

	DATA	RESPONSÁVEL	RUBRICA	DADOS
DESENHO	AGO/2025	LINCOLN CARTAXO		
CÓPIA				
VISTO				


ESCALAS	DESENHOS	CONVÊNIO
Indicada	- Pilares Caixa D'água	GOVERNO DO ESTADO
		ARQUIVO

Aprovações:




Av. Gov. Flávio Ribeiro Coutinho, 500, sl. 601
Jardim Oceania, 58037-005 - João Pessoa (PB)
Tel +55 (83) 99924.4447
e-mail: contato@lclprojetos.com


Armação positiva das lajes do pavimento Fundo de Caixa d'água (Eixo Y) escala 1:50

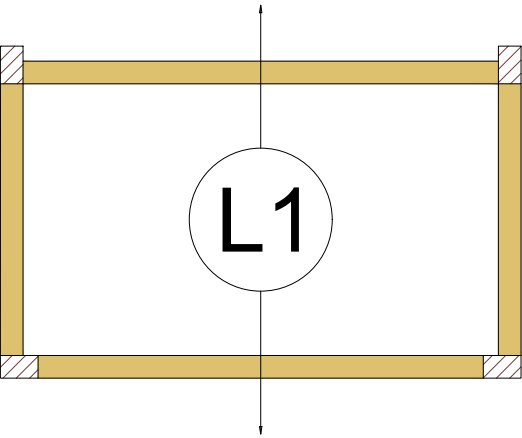


Armação negativa das lajes do pavimento Fundo de Caixa d'água (Eixo X) escala 1:50

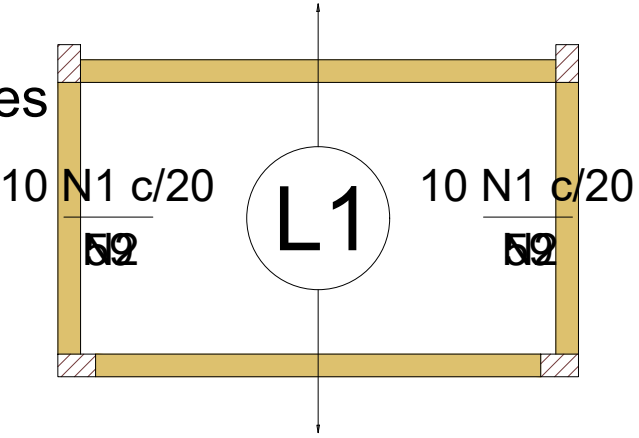

Armação negativa das lajes do pavimento Fundo de Caixa d'água (Eixo Y) escala 1:50

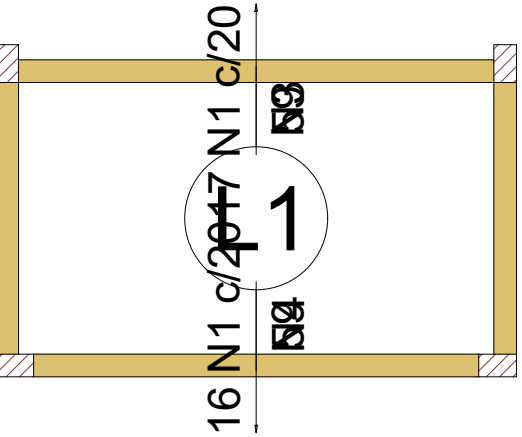




Planta de vigotas pré-moldadas escala 1:50

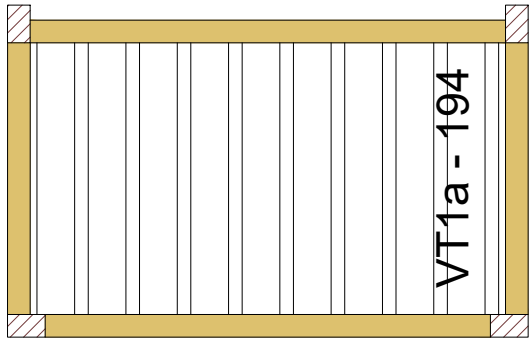

Armaduras de distribuição	
Armadura	Armadura de distribuição
N1	3 N2 ø5.0 c/20 C=197
N1	3 N2 ø5.0 c/20 C=197

Armaduras de distribuição	
Armadura	Armadura de distribuição
N1	3 N3 ø5.0 c/20 C=330
N1	3 N4 ø5.0 c/20 C=313

DETALHE DA ARMADURA DE SUPERIOR DE CONTINUIDADE DA LAJE E MONTAGEM DA ARMADURA DE DISTRIBUIÇÃO

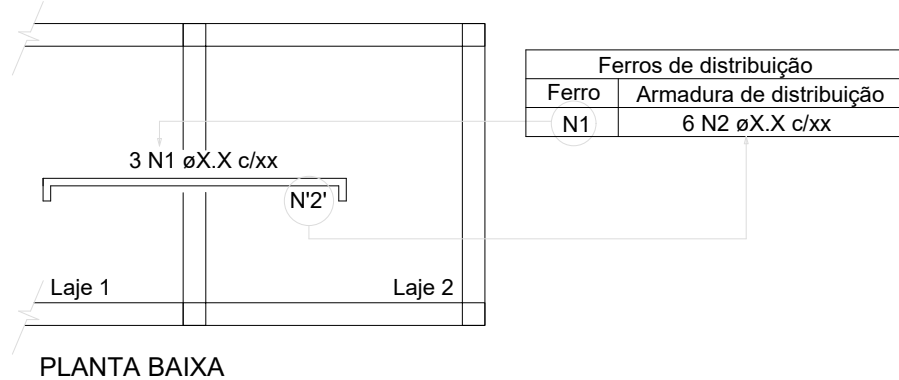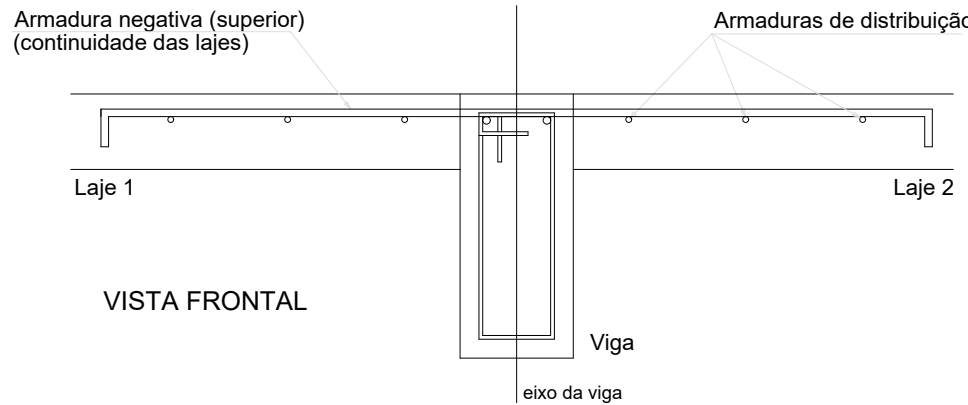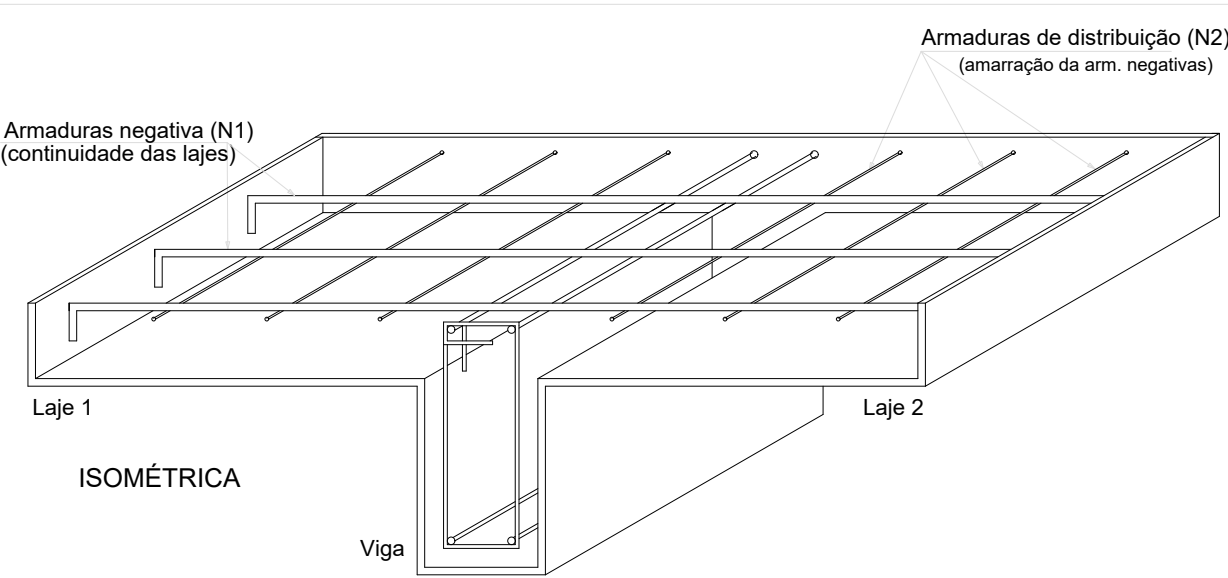

RELAÇÃO DO AÇO

Negativos X

Negativos Y

AÇO	N	DIAM (mm)	QUANT	C.UNIT (cm)	C.TOTAL (cm)
CA60	1	5.0	53	59	3127
	2	5.0	6	197	1182
	3	5.0	3	330	990
	4	5.0	3	313	939

RESUMO DO AÇO

AÇO	DIAM (mm)	C.TOTAL (m)	PESO + 0% (kg)
CA60	5.0	62.4	9.6
PESO TOTAL (kg)			
CA60	9.6		

Volume de concreto (C-25) = 0.30 m³

Área de forma = 0.00 m²

PROPRIETÁRIO: PREFEITURA MUNICIPAL DE COREMAS - PB

LINCOLN CARTAXO DE LIRA JUNIOR:06897861405

Assinado de forma digital por LINCOLN CARTAXO DE LIRA JUNIOR:06897861405
Dados: 2025.08.08 13:29:16 -03'00'

PROJETO: LINCOLN CARTAXO DE LIRA JÚNIOR CREA 160.814.689-8

CONSTRUÇÃO:


FOLHA 11/12
PROJETO: CONSTRUÇÃO DE GINÁSIO POLIESPORTIVO
CONVENIENTE: PREFEITURA MUNICIPAL DE COREMAS - PB
CONVENIADO: MUNICÍPIO DE COREMAS - PB
LOCALIDADE: COREMAS - PB

	DATA	RESPONSÁVEL	RUBRICA	DADOS
DESENHO	AGO/2025	LINCOLN CARTAXO		
CÓPIA				
VISTO				
ESCALAS	DESENHOS			CONVÊNIO
Indicada	- Laje Caixa D'água			GOVERNO DO ESTADO
				ARQUIVO

Aprovações:



Av. Gov. Flávio Ribeiro Coutinho, 500, sl. 601
Jardim Oceania, 58037-005 - João Pessoa (PB)
Tel +55 (83) 99924.4447
e-mail: contato@lclprojetos.com

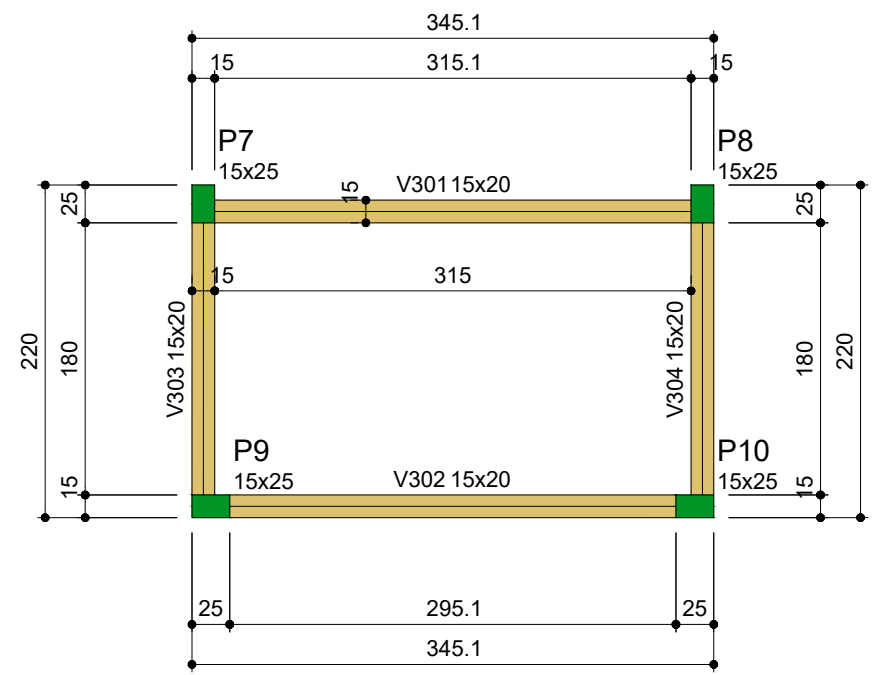

Forma do pavimento Platibanda
(Nível 455)
escala 1:50

Vigas			
Nome	Seção (cm)	Elevação (cm)	Nível (cm)
V301	15x20	0	455
V302	15x20	0	455
V303	15x20	0	455
V304	15x20	0	455

Características dos materiais	
fck (kgf/cm²)	Ecs (kgf/cm²)
250	241500


Legenda dos pilares	
	Pilar que morre

Pilares			
Nome	Seção (cm)	Elevação (cm)	Nível (cm)
P7	15x25	0	455
P8	15x25	0	455
P9	15x25	0	455
P10	15x25	0	455

Legenda das vigas e paredes	
	Viga

V301


ESC 1:30

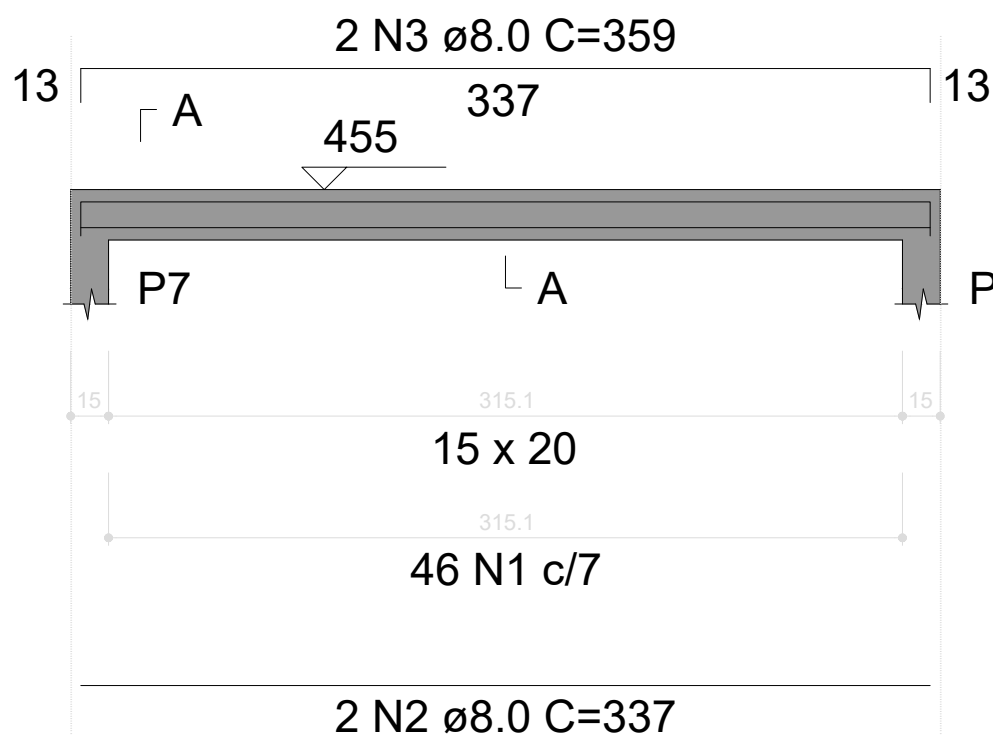

V302

ESC 1:30


SEÇÃO A-A
ESC 1:25

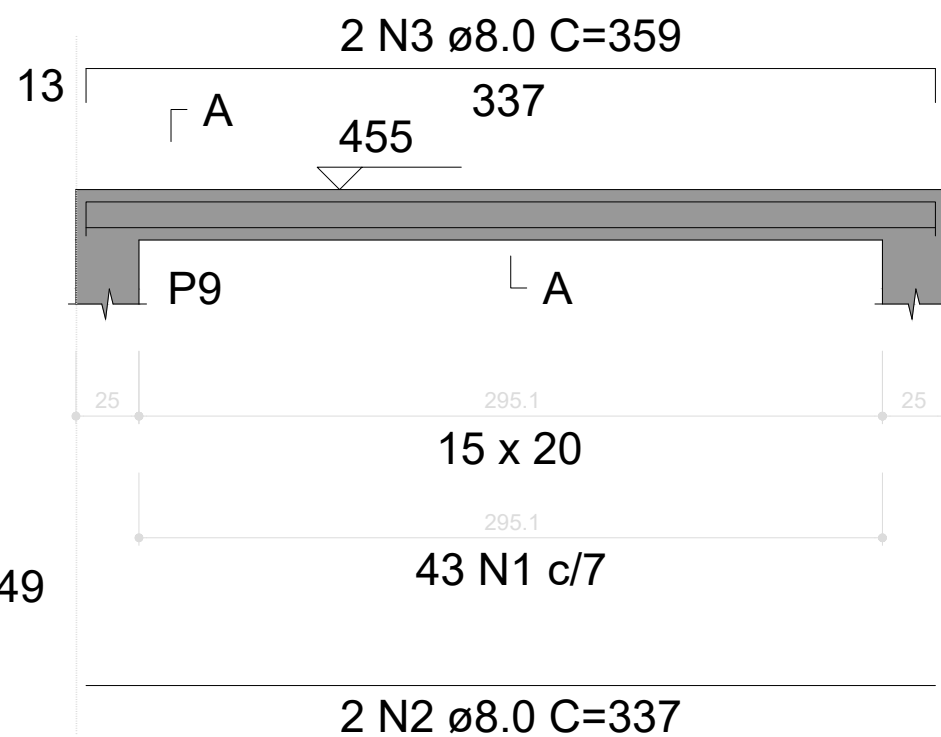

V303

ESC 1:30


SEÇÃO A-A
ESC 1:25

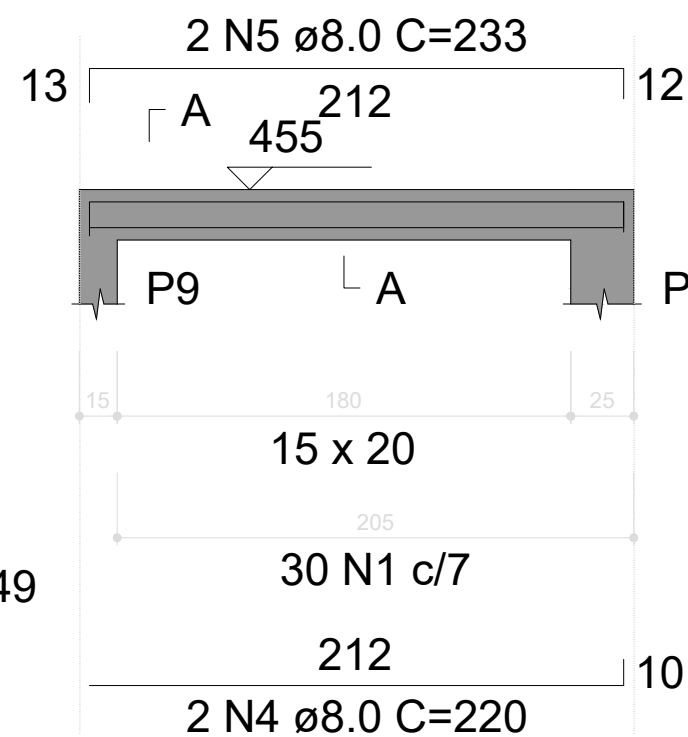

V304

ESC 1:30

SEÇÃO A-A
ESC 1:25

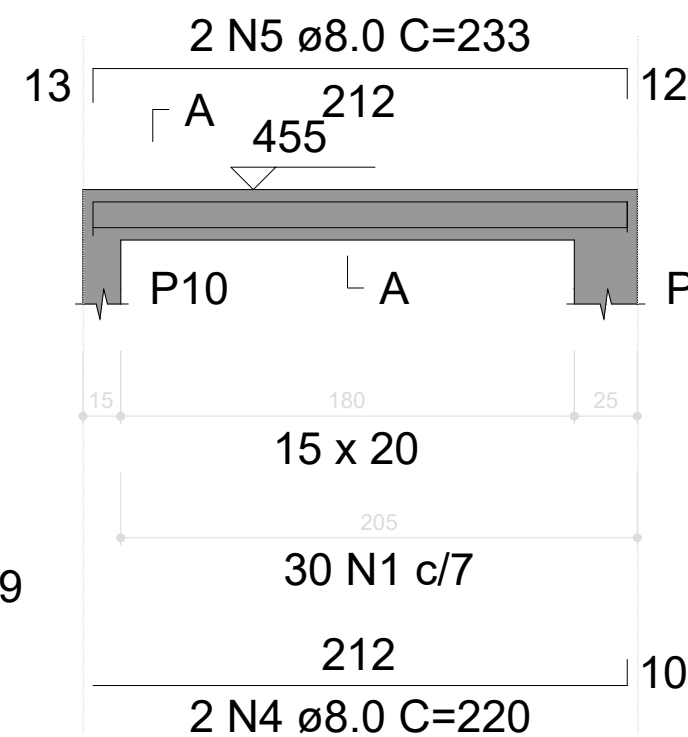

RELAÇÃO DO AÇO

V301
V304

V302

V303

AÇO	N	DIAM (mm)	QUANT	C.UNIT (cm)	C.TOTAL (cm)
CA60	1	5.0	149	49	7301
CA50	2	8.0	4	337	1348
	3	8.0	4	359	1436
	4	8.0	4	220	880
	5	8.0	4	233	932

RESUMO DO AÇO

AÇO	DIAM (mm)	C.TOTAL (m)	PESO + 0% (kg)
CA50	8.0	46	18.1
CA60	5.0	73	11.3
PESO TOTAL (kg)			
CA50	18.1		
CA60	11.3		

Volume de concreto (C-25) = 0.34 m³
Área de forma = 6.22 m²

P7=P8=P9=P10



RELAÇÃO DO AÇO

4xP7

AÇO	N	DIAM (mm)	QUANT	C.UNIT (cm)	C.TOTAL (cm)
CA60	1	5.0	28	59	1652
CA50	2	10.0	16	61	976

RESUMO DO AÇO

AÇO	DIAM (mm)	C.TOTAL (m)	PESO + 0% (kg)
CA50	10.0	9.8	6
CA60	5.0	16.5	2.5
PESO TOTAL (kg)			
CA50	6		
CA60	2.5		

Volume de concreto (C-25) = 0.10 m³
Área de forma = 2.08 m²

PROPRIETÁRIO: PREFEITURA MUNICIPAL DE COREMAS - PB
LINCOLN CARTAXO DE LIRA JUNIOR:06897861405
Assinado de forma digital por LINCOLN CARTAXO DE LIRA JUNIOR:06897861405
Dados: 2025.08.08 13:34:05 -03'00'

PROJETO: LINCOLN CARTAXO DE LIRA JÚNIOR CREA 160.814.689-8

CONSTRUÇÃO:

FOLHA	PROJETO:	CONVENIENTE:	CONVENIADO:	LOCALIDADE:
12/12	CONSTRUÇÃO DE GINÁSIO POLIESPORTIVO	PREFEITURA MUNICIPAL DE COREMAS - PB	MUNICÍPIO DE COREMAS - PB	COREMAS - PB
DESENHO	DATA	RESPONSÁVEL	RUBRICA	DADOS
CÓPIA	AGO/2025	LINCOLN CARTAXO		
VISTO				
ESCALAS	DESENHOS	CONVÊNIO	GOVERNO DO ESTADO	
Indicada	- Forma Tampa Caixa D'água - Vigas Tampa Caixa D'água - Pilares Tampa Caixa D'água		ARQUIVO	

Aprovações:

LCL PROJETOS

Av. Gov. Flávio Ribeiro Coutinho, 500, sl. 601
Jardim Oceania, 58037-005 - João Pessoa (PB)
Tel: +55 (83) 99924-4447
e-mail: contato@lclprojetos.com