



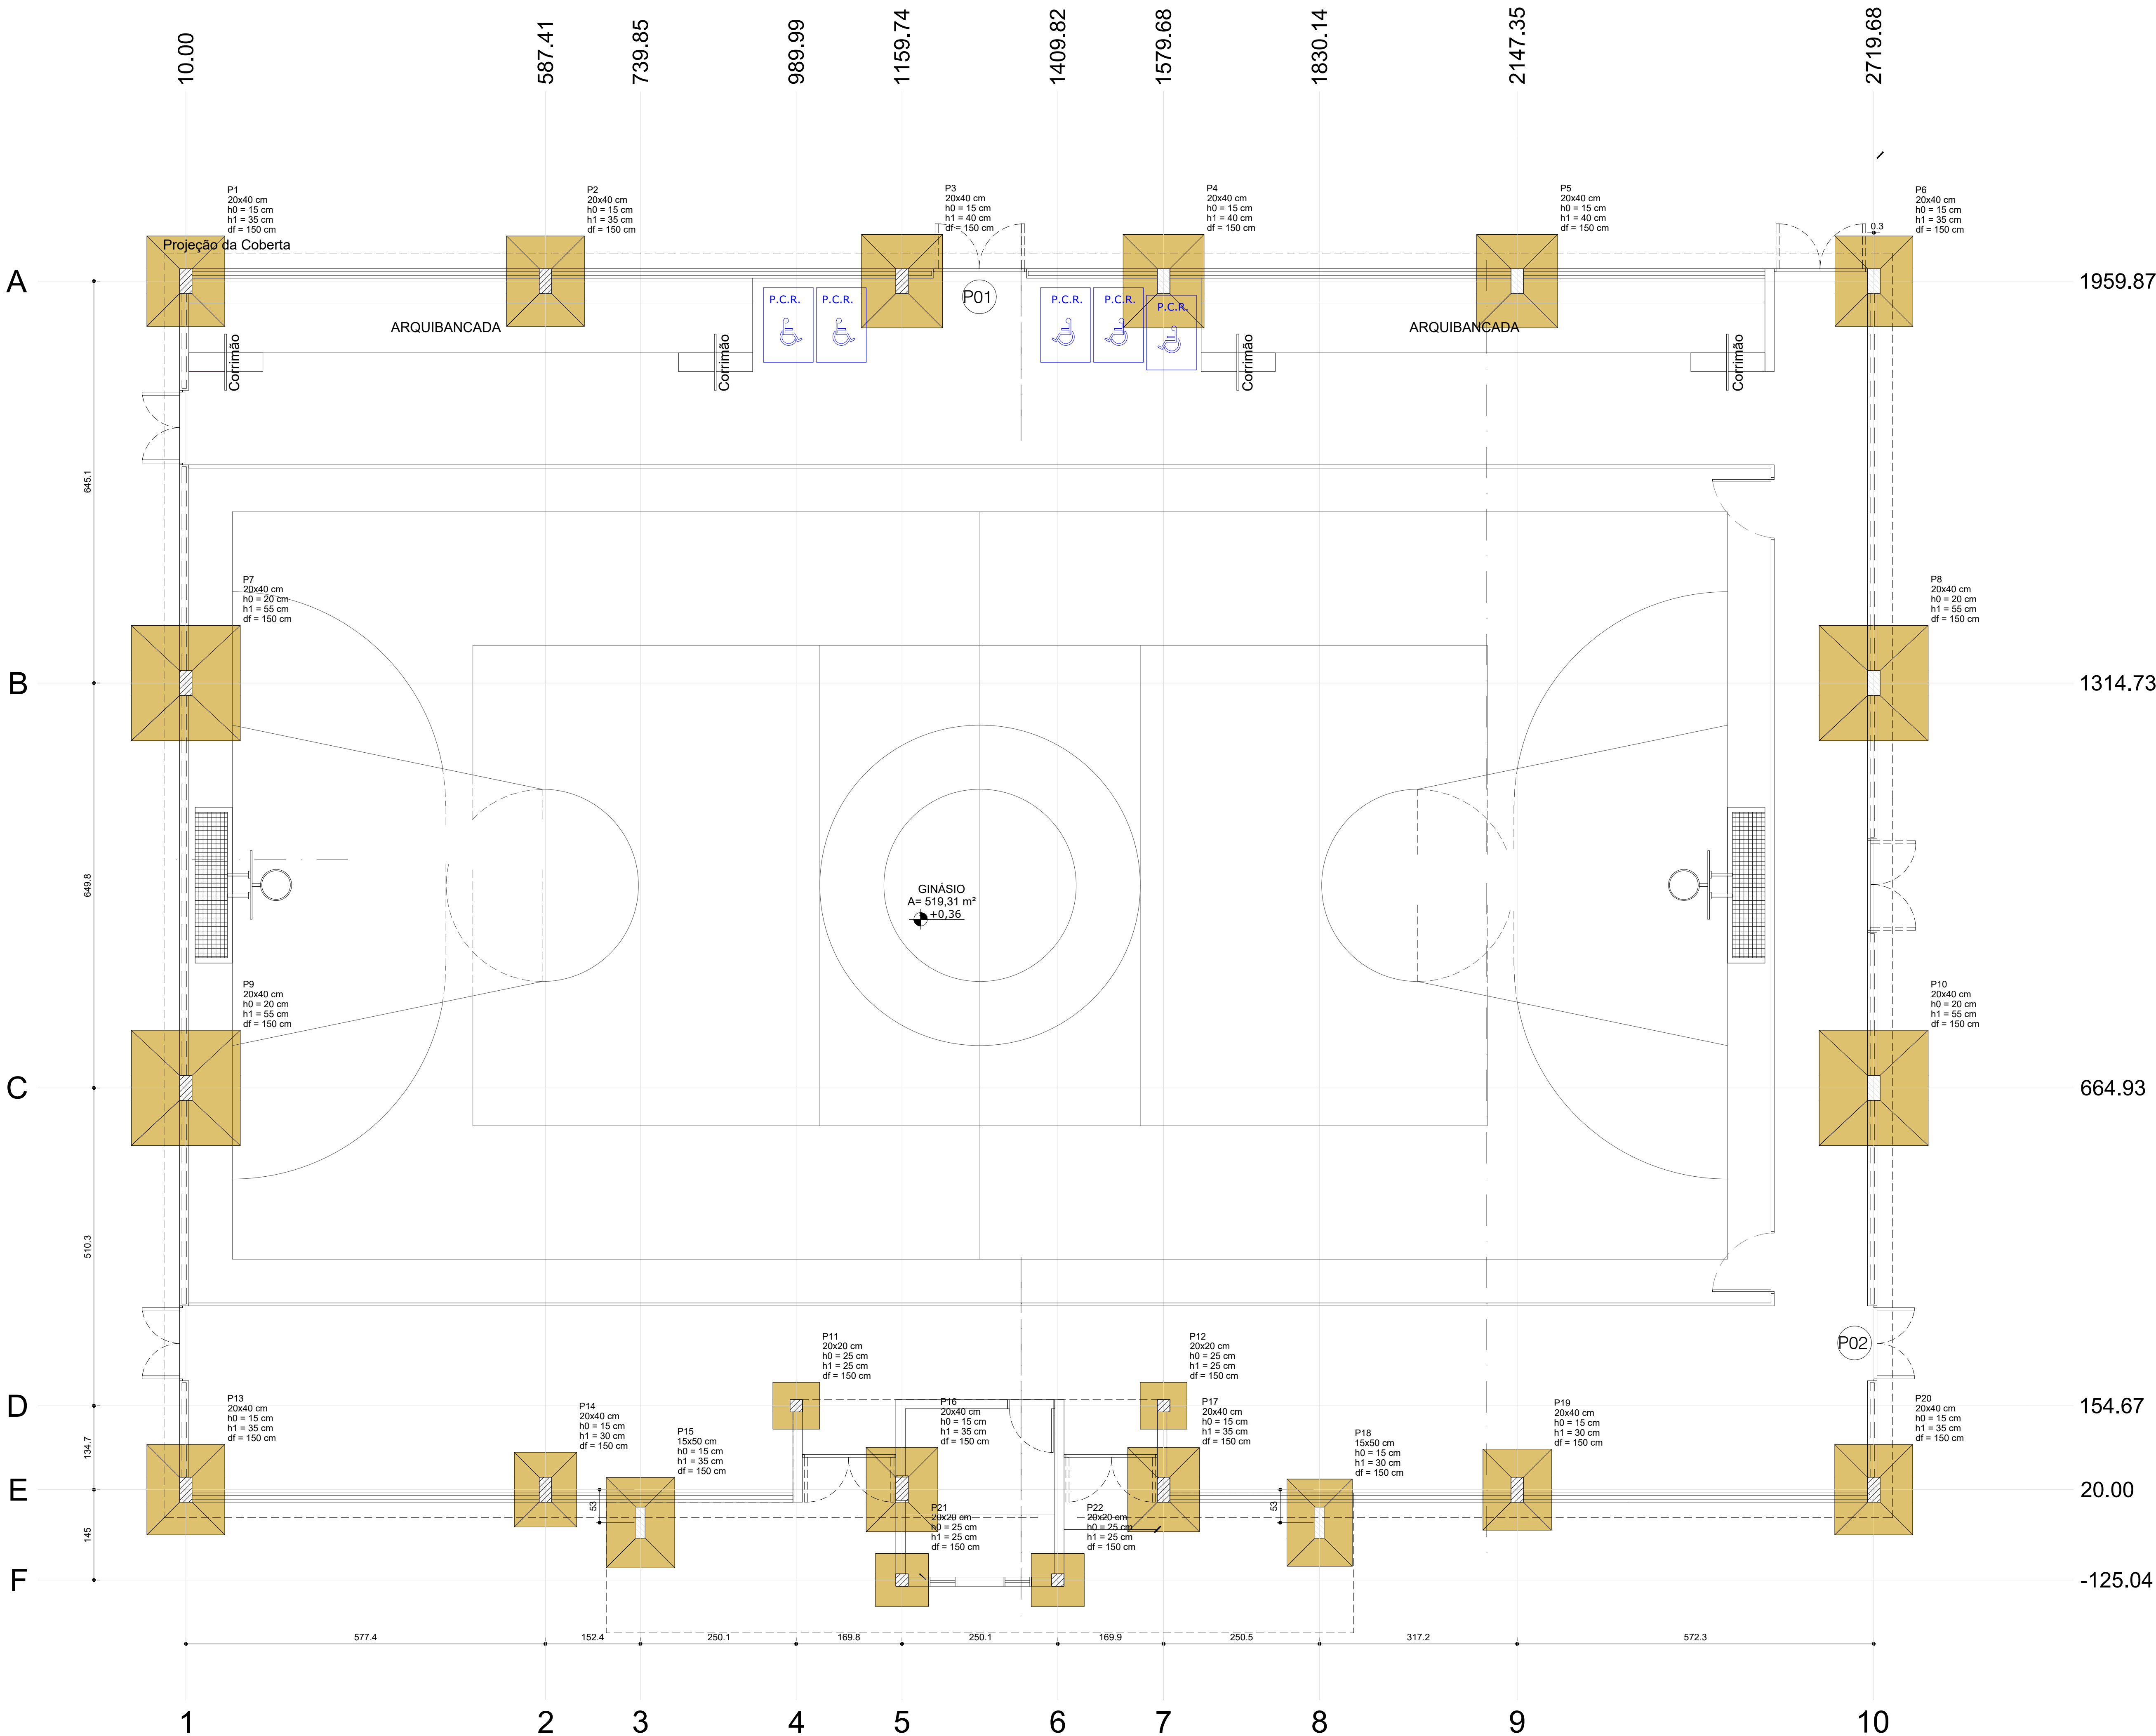

Planta de locação
escala 1:50

		Pilar		Carga Máx. (tf)	Carga Mín. (tf)	Fundação		h1 / hb (cm)	df (cm)
Nome	Seção (cm)	X (cm)	Y (cm)			Lado B (cm)	Lado H (cm)		
P1	20x40	10.00	1959.87	8.7	5.6	125	145	15	35
P2	20x40	587.41	1959.87	7.5	7.0	125	145	15	35
P3	20x40	1159.74	1959.87	7.1	6.5	130	150	15	40
P4	20x40	1579.68	1959.87	7.1	6.5	130	150	15	40
P5	20x40	2147.35	1959.87	7.5	7.0	130	150	15	40
P6	20x40	2720.00	1959.87	8.7	5.6	125	145	15	35
P7	20x40	10.00	1314.73	4.7	4.1	175	185	20	55
P8	20x40	2719.68	1314.73	4.7	4.1	175	185	20	55
P9	20x40	10.00	664.93	4.7	4.1	175	185	20	55
P10	20x40	2719.68	664.93	4.7	4.1	175	185	20	55
P11	20x20	989.99	154.67	1.8	0.6	75	75	25	25
P12	20x20	1579.68	154.67	2.0	0.2	75	75	25	25
P13	20x40	10.00	20.00	8.8	5.6	125	145	15	35
P14	20x40	587.41	20.00	7.0	5.5	100	120	15	30
P15	15x50	739.85	-33.04	6.0	3.9	110	145	15	35
P16	20x40	1159.74	20.00	11.1	8.4	115	135	15	35
P17	20x40	1579.68	20.00	8.9	8.1	115	135	15	35
P18	15x50	1830.14	-33.04	5.2	3.8	105	140	15	30
P19	20x40	2147.35	20.00	7.0	6.3	110	130	15	30
P20	20x40	2719.68	20.00	8.8	5.6	125	145	15	35
P21	20x20	1159.74	-125.04	5.1	2.1	85	85	25	25
P22	20x20	1409.82	-125.04	3.8	2.5	85	85	25	25

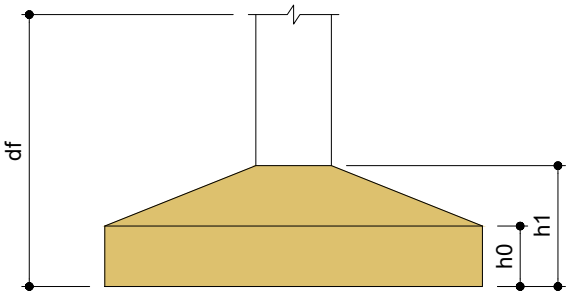

Localização no eixo X		Localização no eixo Y	
Coordenadas (cm)	Nome	Coordenadas (cm)	Nome
10.00	P1, P7, P9, P13	1959.87	P1, P2, P3, P4, P5, P6
587.41	P2, P14	1314.73	P7, P8
739.85	P15	664.93	P9, P10
989.99	P11	154.67	P11, P12
1159.74	P3, P16, P21	20.00	P13, P14, P16, P17, P19, P20
1409.82	P22	-33.04	P15, P18
1579.68	P4, P12, P17	-125.04	P21, P22
1830.14	P18		
2147.35	P6, P19		
2719.68	P8, P10, P20		
2720.00	P6		

- B - CARACTERÍSTICAS DAS SAPATAS:
1. DADOS PARA O DIMENSIONAMENTO ESTRUTURAL DAS SAPATAS:
- FUNDAÇÕES NA COTA DE -1,5 METROS
 - VIGAS BALDRAMES NÍVEL +40 CM
 - TENSÃO ADMISSÍVEL DO SOLO 1,5 KGf/cm²

PROPRIETÁRIO: PREFEITURA MUNICIPAL DE COREMAS - PB

LINCOLN CARTAXO DE LIRA Assinado de forma digital por LINCOLN CARTAXO DE LIRA JUNIOR:06897861405
Dados: 2025.08.08 12:17:24 -03'00'

PROJETO: LINCOLN CARTAXO DE LIRA JÚNIOR CREA 160.814.689-8

CONSTRUÇÃO:

FOLHA 01/26

PROJETO: CONSTRUÇÃO DE GINÁSIO POLIESPORTIVO - ESTRUTURAL


CONVENIENTE: PREFEITURA MUNICIPAL DE COREMAS - PB

CONVENIADO: MUNICÍPIO DE COREMAS - PB

LOCALIDADE: COREMAS - PB

DATA	RESPONSÁVEL	RUBRICA	DADOS
AGO/2025	LINCOLN CARTAXO		
DESENHO			
CÓPIA			
VISTO			
ESCALAS	DESENHOS		CONVÊNIO
Indicada	- Planta de Locação		GOVERNO DO ESTADO
			ARQUIVO

Aprovações:

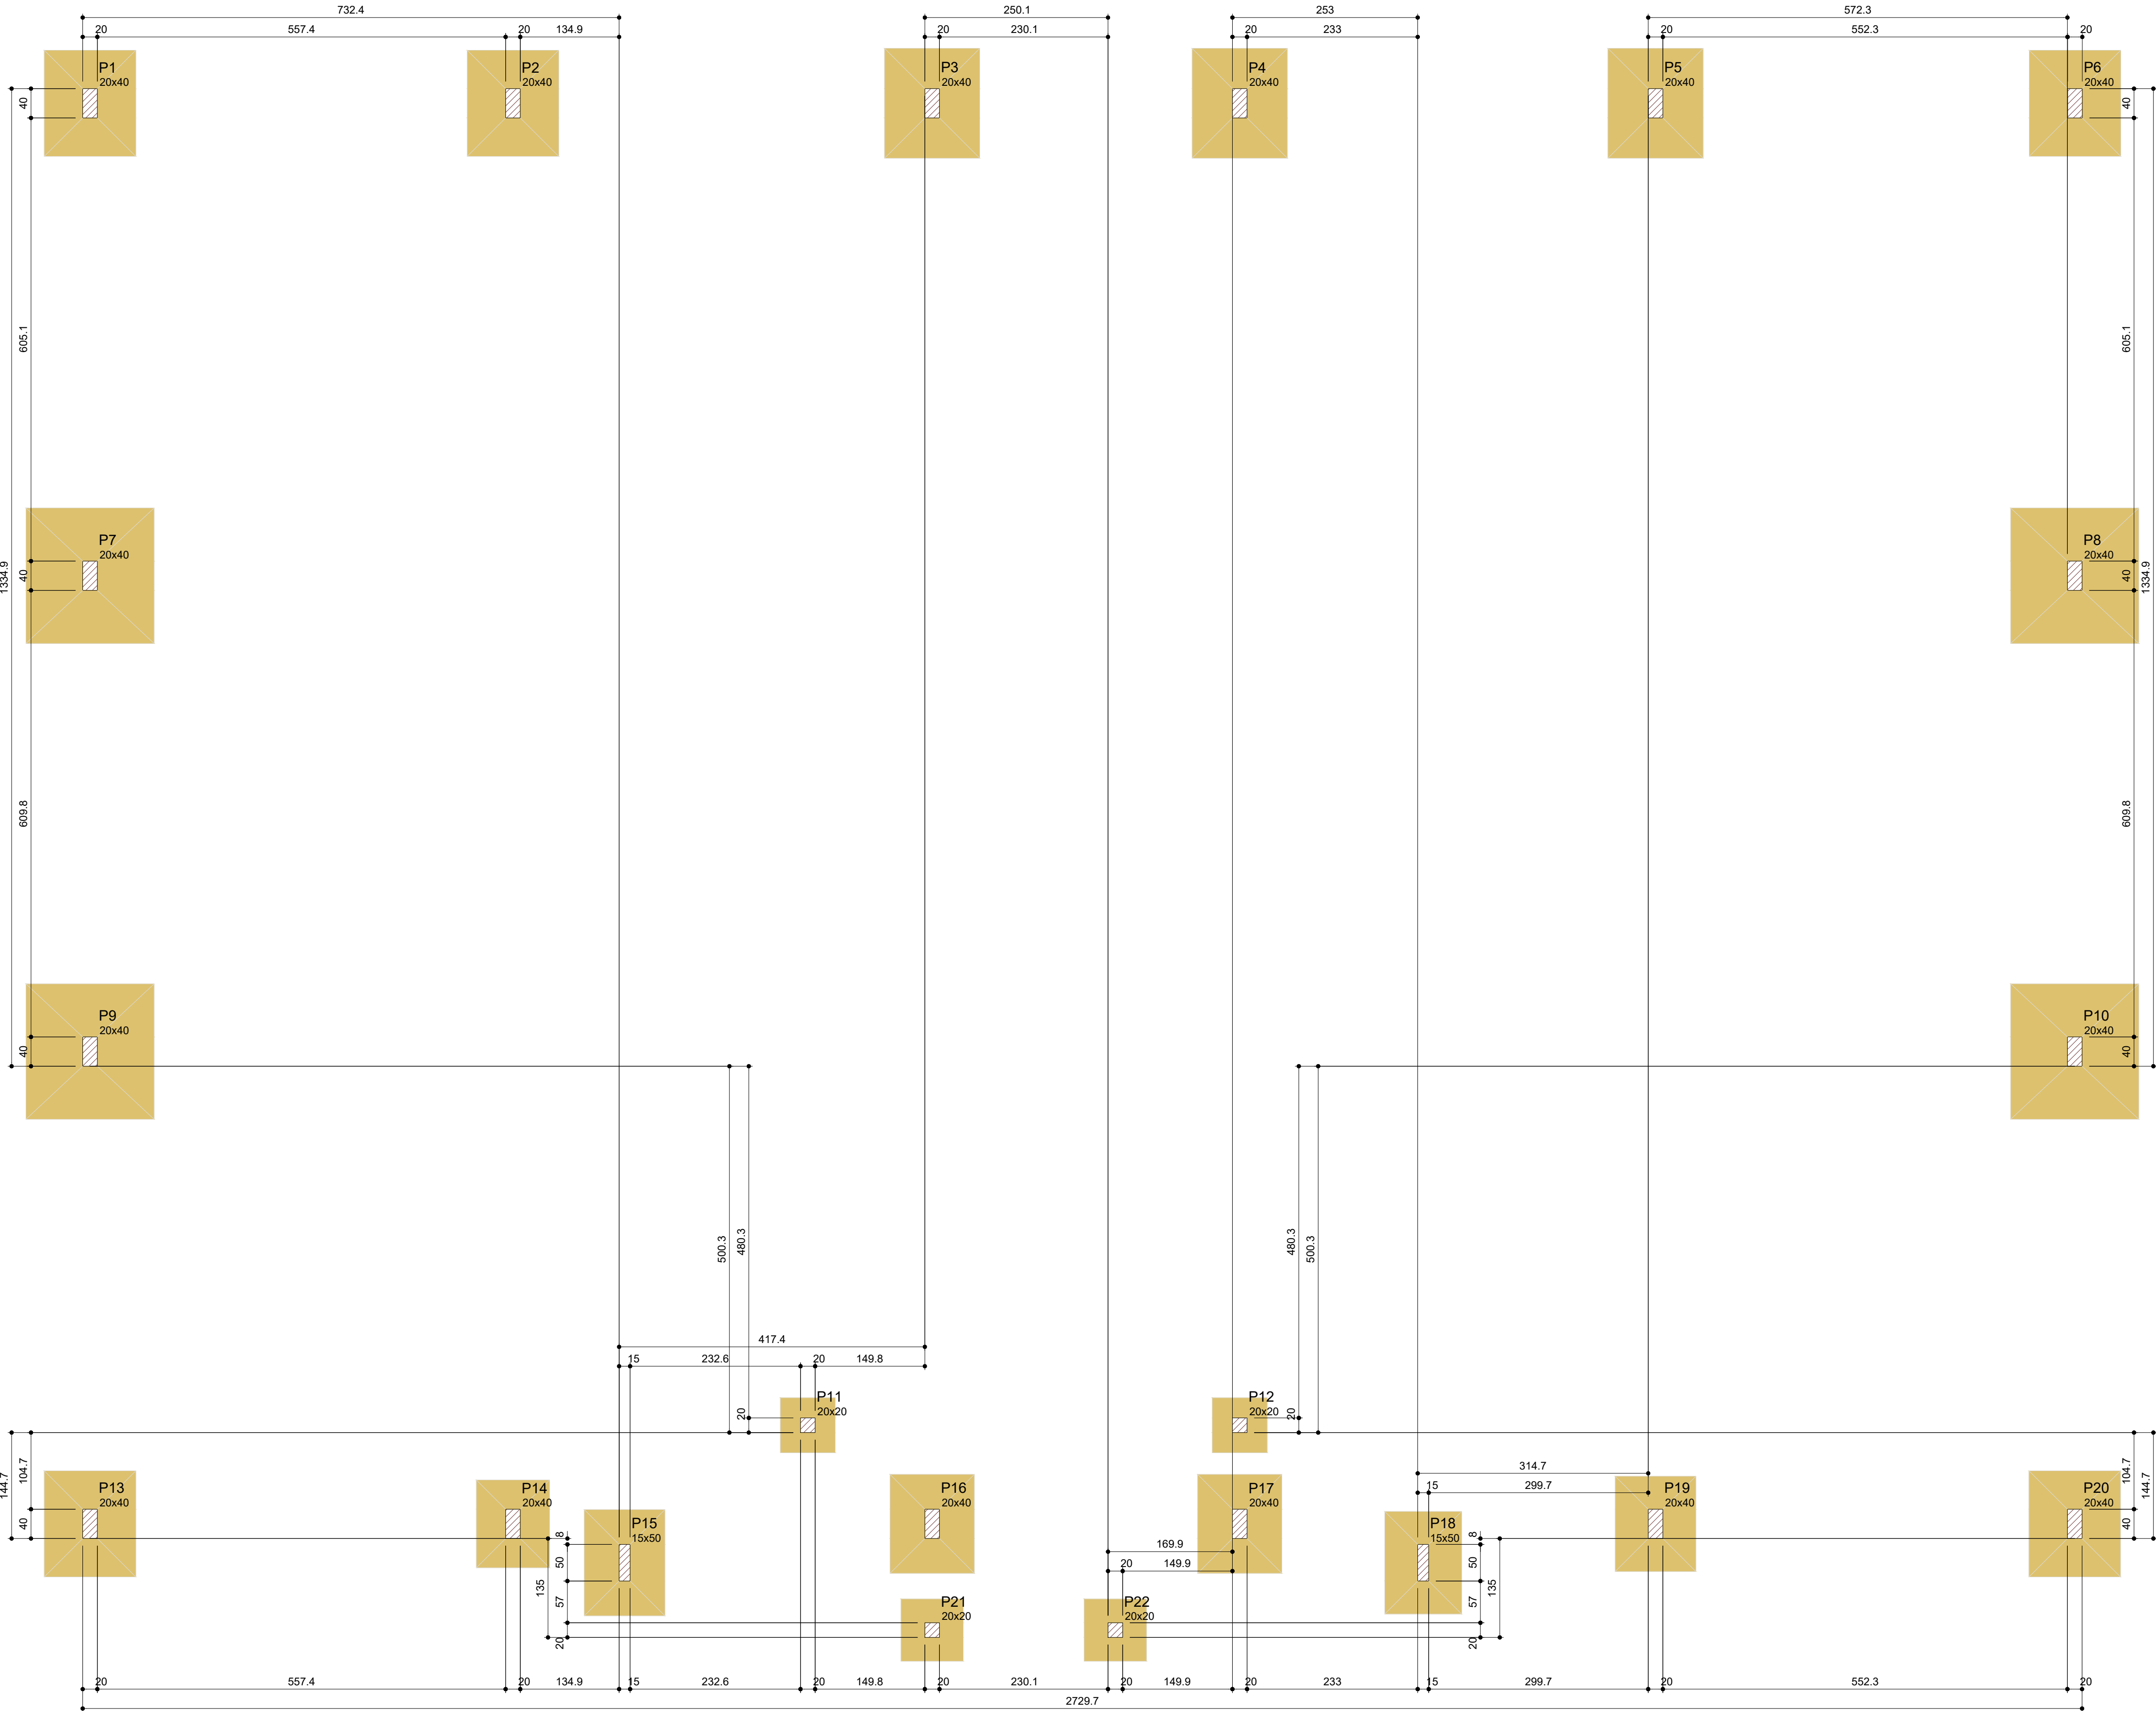

Características dos materiais			
Elemento	1cx	Eco	
	(kgf/cm²)	250	241500
Pilares	250	300	268384
Sapatas	300		

Pilares			
Nome	Seção (cm)	Elevação (cm)	Nível (cm)
P1	20x40	0	0
P2	20x40	0	0
P3	20x40	0	0
P4	20x40	0	0
P5	20x40	0	0
P6	20x40	0	0
P7	20x40	0	0
P8	20x40	0	0
P9	20x40	0	0
P10	20x40	0	0
P11	20x20	0	0
P12	20x20	0	0
P13	20x40	0	0
P14	20x40	0	0
P15	15x50	0	0
P16	20x40	0	0
P17	20x40	0	0
P18	15x50	0	0
P19	20x40	0	0
P20	20x40	0	0
P21	20x20	0	0
P22	20x20	0	0

Legenda dos pilares	
	Pilar que passa

Forma do pavimento Fundação (Nível 0)
escala 1:50

PROPRIETÁRIO: PREFEITURA MUNICIPAL DE COREMAS - PB

LINCOLN CARTAXO DE LIRA JUNIOR:06897861405 Assinado de forma digital por LINCOLN CARTAXO DE LIRA JUNIOR:06897861405
Dados: 2025.08.08 12:17:09 -03'00'

PROJETO: LINCOLN CARTAXO DE LIRA JÚNIOR CREA 160.814.689-8

CONSTRUÇÃO:

FOLHA 02/26

PROJETO: CONSTRUÇÃO DE GINÁSIO POLIESPORTIVO - ESTRUTURAL

CONVENIENTE: PREFEITURA MUNICIPAL DE COREMAS - PB

CONVENIADO: MUNICÍPIO DE COREMAS - PB


LOCALIDADE: COREMAS - PB

DESENHO	DATA	RESPONSÁVEL	RUBRICA	DADOS
CDRA	AGO/2025	LINCOLN CARTAXO		
VISTO				
ESCALAS		DESENHOS		CONVÊNIO
Indicada		- Forma do Pavimento Fundação (Nível 0)		GOVERNO DO ESTADO
				ARQUIVO

Aprovações:

S11=S12


PLANTA
ESC 1:25

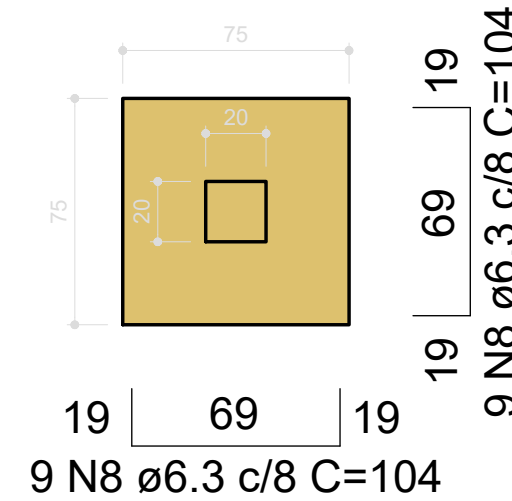

Solo compactado sobre a sapata
peso específico > 1600.00 kgf/m³


P11=P12

CORTE
ESC 1:25

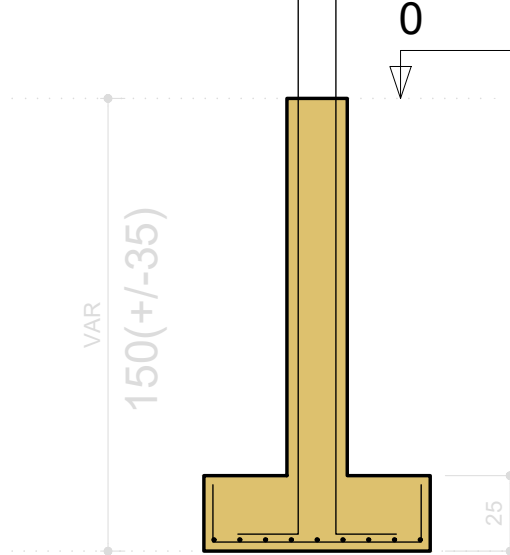


FUNDAÇÃO - L1

SEÇÃO
ESC 1:20

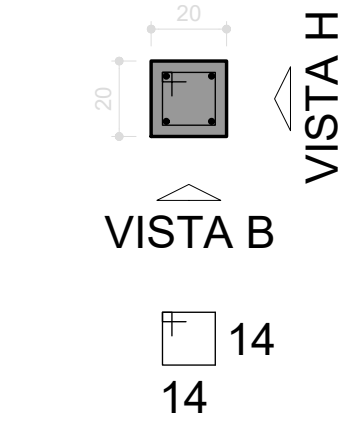


15 N4 ø5.0 C=67

VISTA H
ESC 1:25

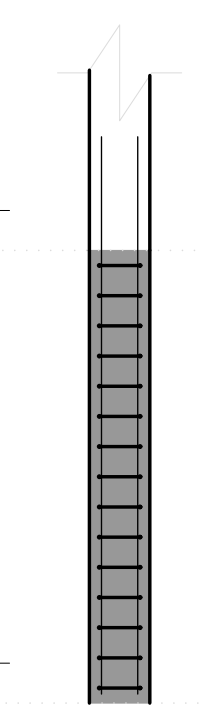


VISTA B
ESC 1:25

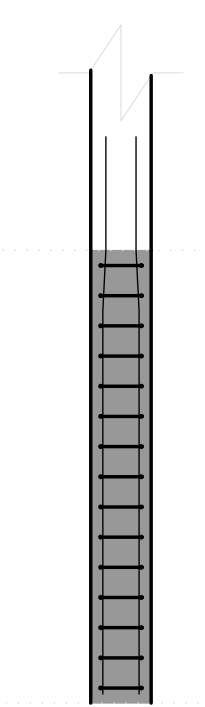

S21=S22


PLANTA
ESC 1:25

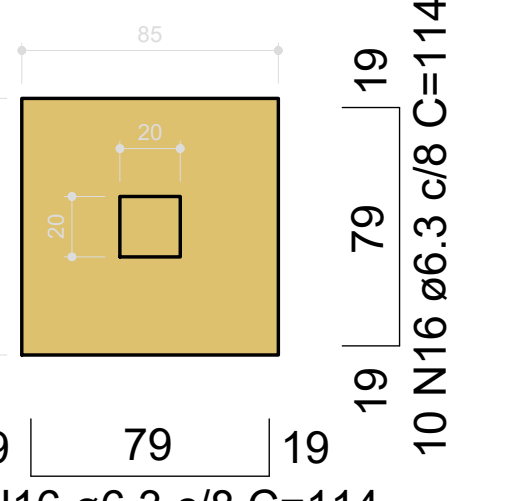


Solo compactado sobre a sapata
peso específico > 1600.00 kgf/m³

P21=P22


VISTA H
ESC 1:25

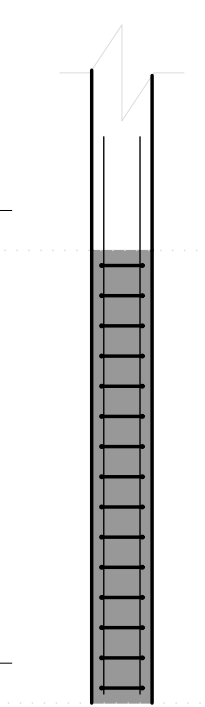

VISTA B
ESC 1:25

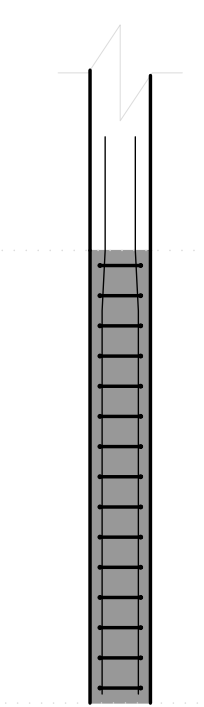


CORTE
ESC 1:25

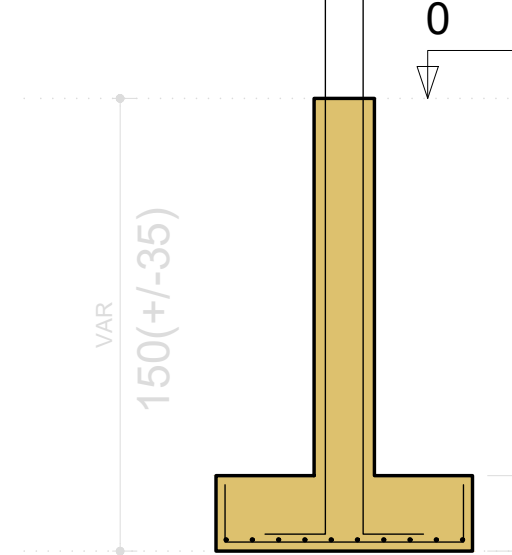

FUNDAÇÃO - L1


SEÇÃO
ESC 1:20

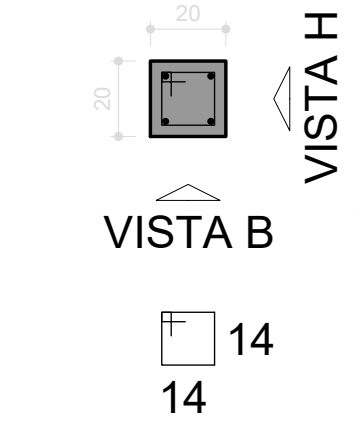

15 N4 ø5.0 C=67


S14

PLANTA
ESC 1:25

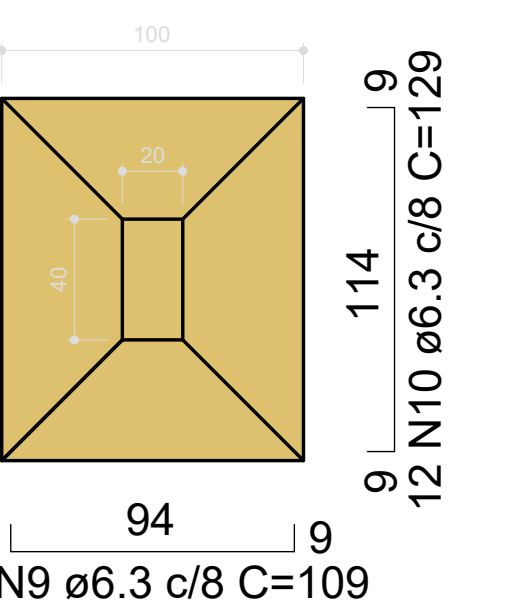


Solo compactado sobre a sapata
peso específico > 1600.00 kgf/m³

CORTE
ESC 1:25

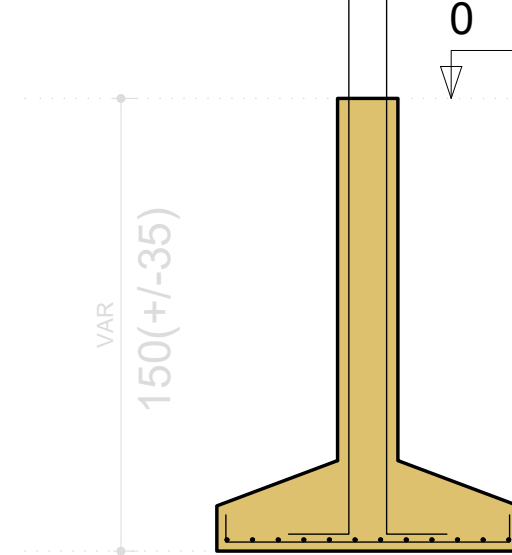


S15

PLANTA
ESC 1:25

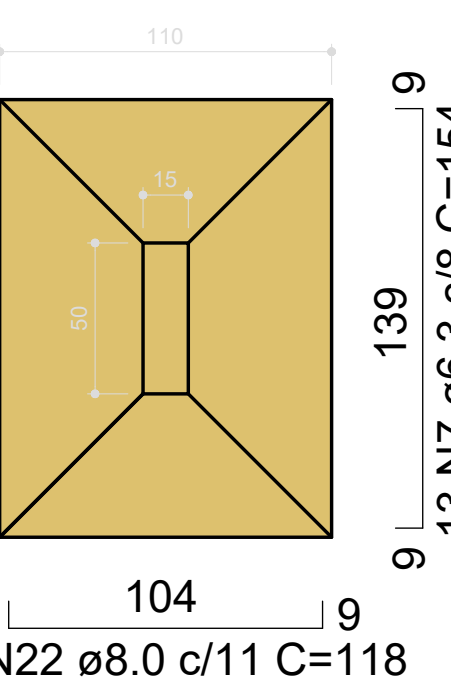

Solo compactado sobre a sapata
peso específico > 1600.00 kgf/m³


CORTE
ESC 1:25

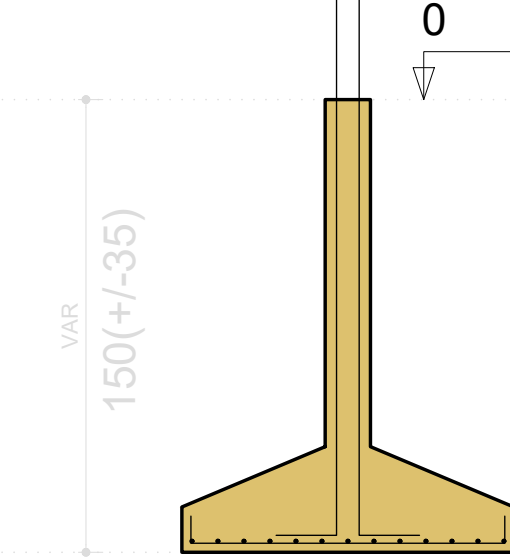

P15


FUNDAÇÃO - L1

SEÇÃO
ESC 1:20

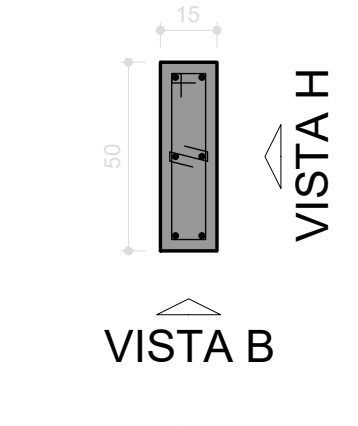


15 N6 ø5.0 C=117
15 N5 ø5.0 C=24

VISTA H
ESC 1:25

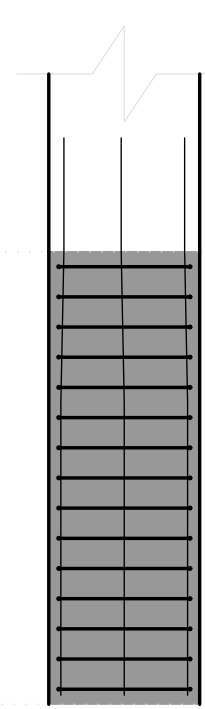


VISTA B
ESC 1:25

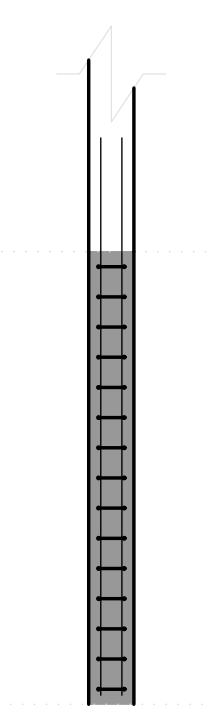


S1=S2=S6=S13=S20

PLANTA
ESC 1:25

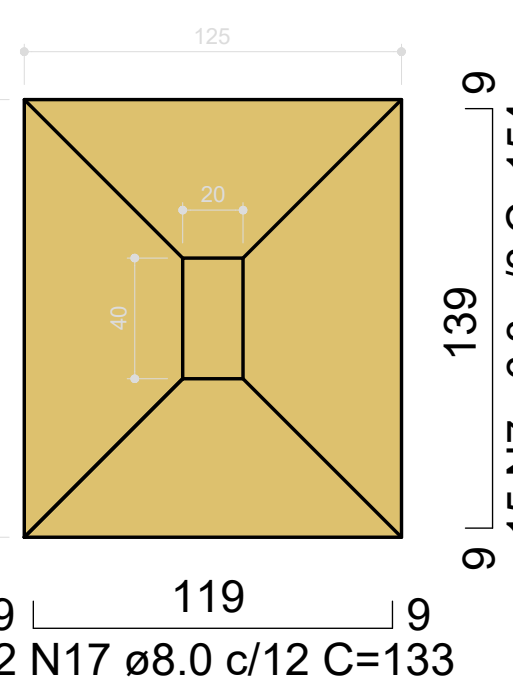

Solo compactado sobre a sapata
peso específico > 1600.00 kgf/m³


CORTE
ESC 1:25

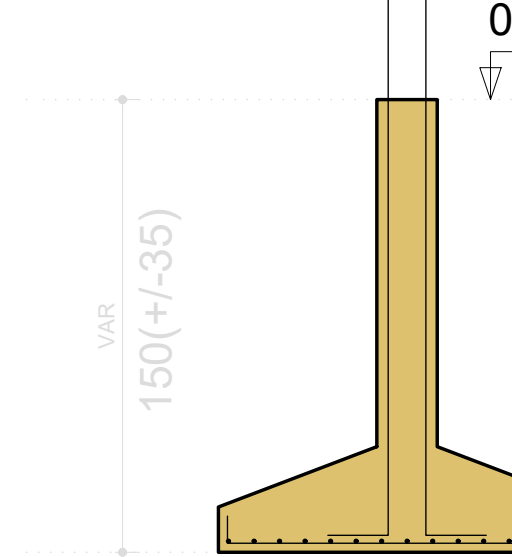

P1=P6=P13=P20


FUNDAÇÃO - L1

SEÇÃO
ESC 1:20

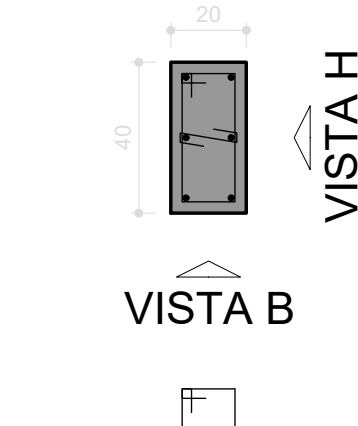


15 N2 ø5.0 C=107
15 N1 ø5.0 C=29

VISTA H
ESC 1:25

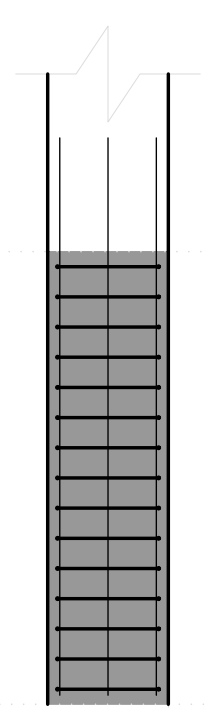


VISTA B
ESC 1:25

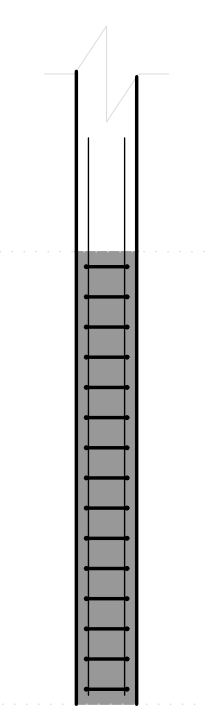

P2


FUNDAÇÃO - L1

SEÇÃO
ESC 1:20

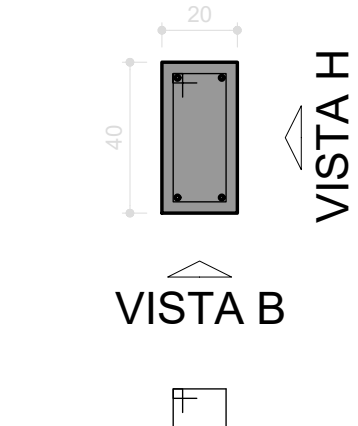


10 N2 ø5.0 C=107

VISTA H
ESC 1:25

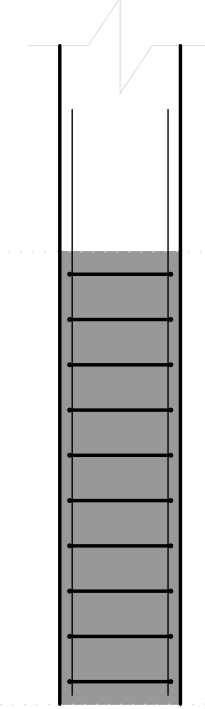

VISTA B
ESC 1:25

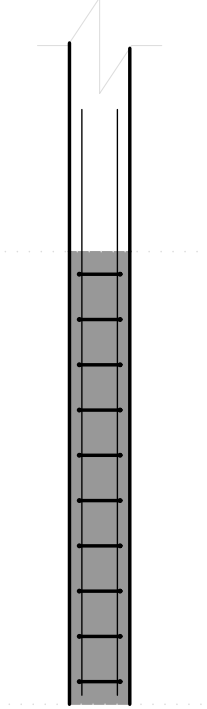

*OBS.: OS QUADROS RESUMO REFERENTES A
ESTA PRANCHA CONSTAM NA PRANCHA 05/26

PROPRIETÁRIO: PREFEITURA MUNICIPAL DE COREMAS - PB
LINCOLN CARTAXO DE LIRA JUNIOR:06897861405
PROJETO: LINCOLN CARTAXO DE LIRA JÚNIOR CREA 160.814.689-8

CONSTRUÇÃO:


FOLHA	PROJETO:	CONSTRUÇÃO DE GINÁSIO POLIESPORTIVO - ESTRUTURAL
03/26	CONVENIENTE:	PREFEITURA MUNICIPAL DE COREMAS - PB
	CONVENIADO:	MUNICÍPIO DE COREMAS - PB
	LOCALIDADE:	COREMAS - PB
DESENHO	DATA	RESPONSÁVEL
CÓPIA	AGO/2025	LINCOLN CARTAXO
VISTO		
ESCALAS	DESENHOS	CONVÊNIO
Indicada	- SAPATAS E PILARES PAV. FUNDAÇÃO (NÍVEL 0)	GOVERNO DO ESTADO
		ARQUIVO

Aprovações:


P18

FUNDAÇÃO - L1

SEÇÃO
ESC 1:20

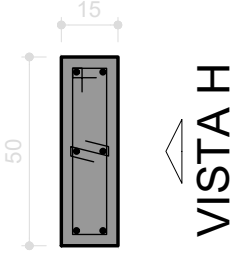


VISTA B

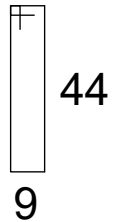


15 N6 ø5.0 C=117
15 N5 ø5.0 C=24

VISTA H
ESC 1:25

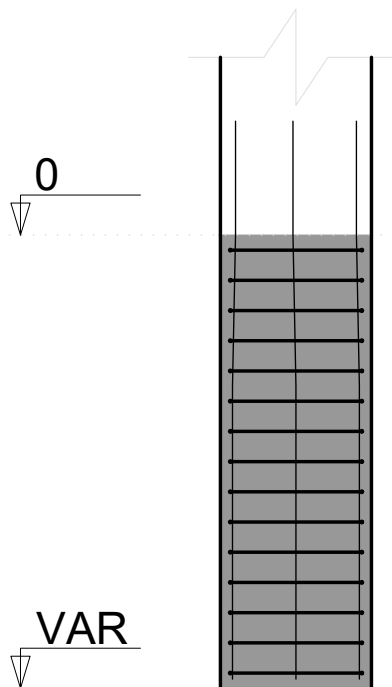


VISTA B
ESC 1:25

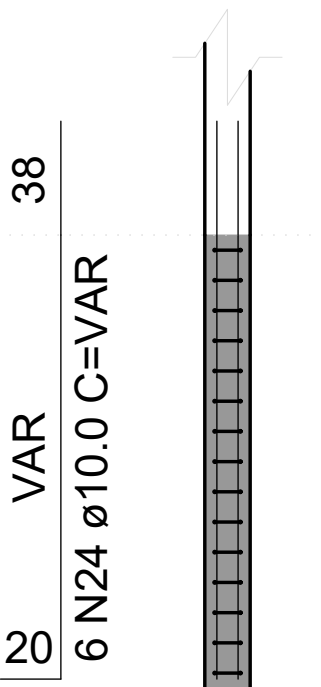

S16=S17

PLANTA
ESC 1:25

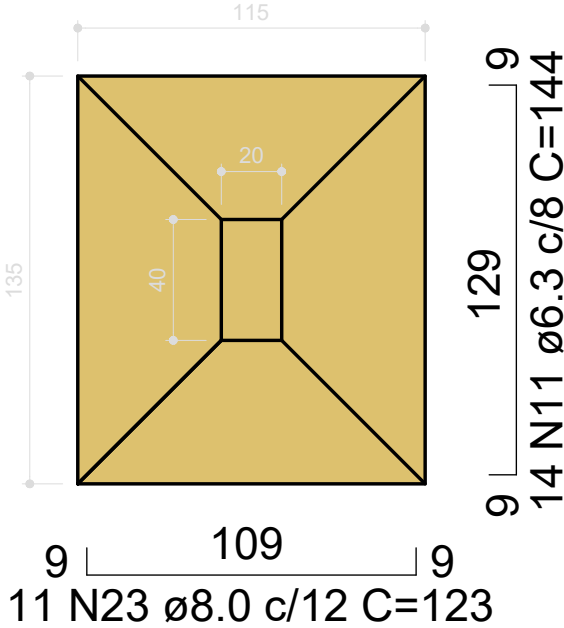


Solo compactado sobre a sapata
peso específico > 1600.00 kgf/m³


P16=P17

FUNDAÇÃO - L1

SEÇÃO
ESC 1:20

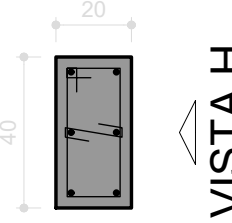


VISTA B

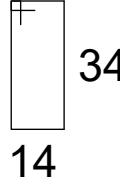


15 N2 ø5.0 C=107
15 N1 ø5.0 C=29


VISTA H
ESC 1:25

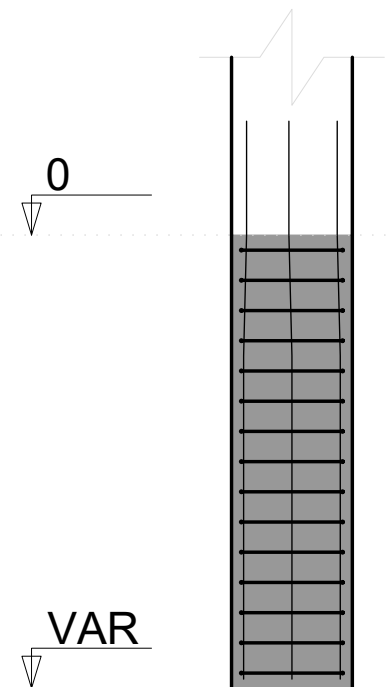

VISTA B
ESC 1:25

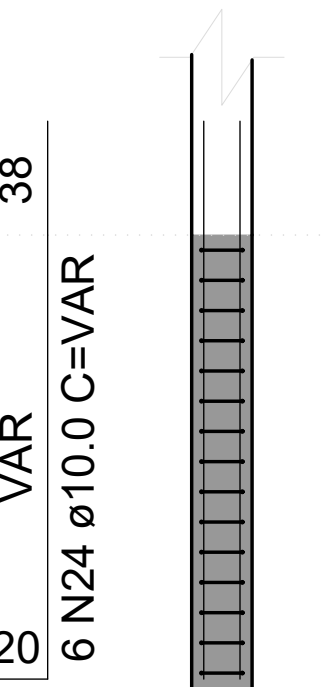

CORTE
ESC 1:25

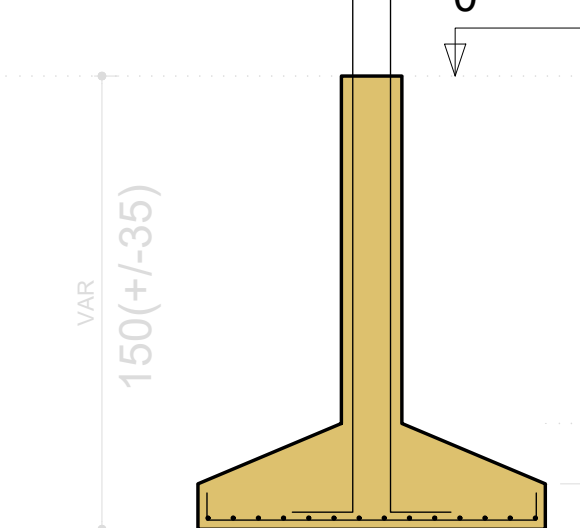

N1

RELAÇÃO DO AÇO

4xP1	P2	2xP3
P5	4xP7	2xP11
P14	P15	2xP16
P18	P19	2xP21
5xS1	3xS3	4xS10
2xS11	S14	S15
2xS16	S18	S19
2xS21		

AÇO	N	DIAM (mm)	QUANT	C.UNIT (cm)	C.TOTAL (cm)
CA60	1	5.0	135	29	3915
	2	5.0	205	107	21935
	3	5.0	80	29	2320
	4	5.0	60	67	4020
	5	5.0	30	24	720
	6	5.0	30	117	3510
CA50	7	6.3	88	154	13552
	8	6.3	36	104	3744
	9	6.3	15	109	1635
	10	6.3	12	129	1548
	11	6.3	28	144	4032
	12	6.3	17	114	1938
	13	6.3	11	149	1639
	14	6.3	16	119	1904
	15	6.3	12	139	1668
	16	6.3	40	114	4560
	17	8.0	60	133	7980
	18	8.0	42	138	5796
	19	8.0	36	158	5688
	20	8.0	92	193	17756
	21	8.0	88	203	17984
	22	8.0	13	118	1534
	23	8.0	22	123	2706
	24	10.0	82	VAR	VAR
	25	10.0	2	VAR	VAR
	26	10.0	16	75	1200
	27	12.5	76	VAR	VAR


RESUMO DO AÇO

AÇO	DIAM (mm)	C.TOTAL (m)	PESO + 10% (kg)
CA50	6.3	362.2	97.5
	8.0	593.2	257.5
	10.0	181.7	123.2
	12.5	160.4	169.9
CA60	5.0	364.2	61.7
PESO TOTAL (kg)			
CA50	648.1		
CA60	61.7		


Volume de concreto (C-25) = 2.38 m³
Volume de concreto (C-30) = 10.60 m³
Área de forma = 57.41 m²

P7=P8=P9=P10

VISTA H
ESC 1:25

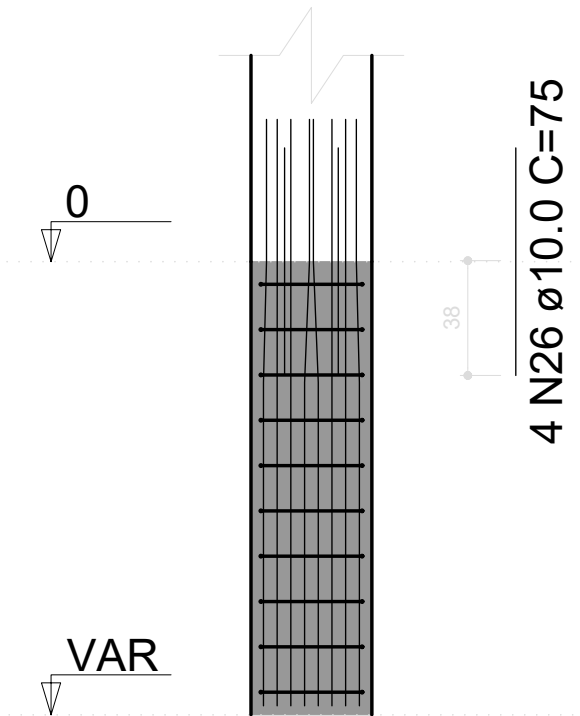


VISTA B
ESC 1:25

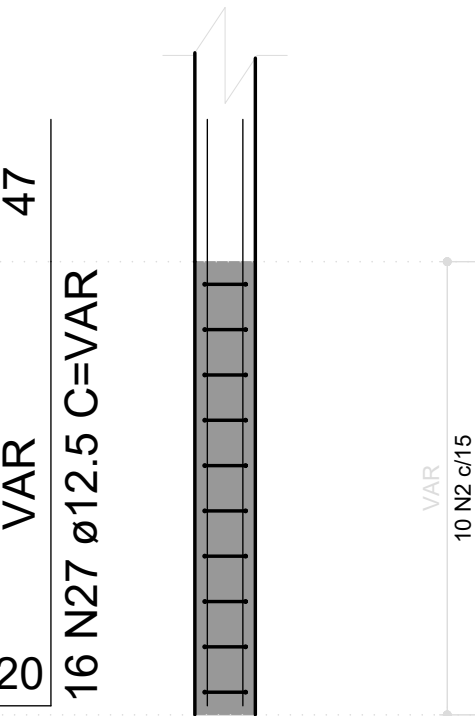

FUNDAÇÃO - L1

SEÇÃO
ESC 1:20

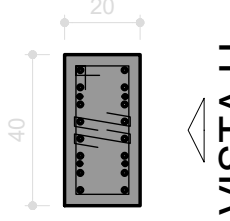


VISTA B



10 N2 ø5.0 C=107
2x10 N3 ø5.0 C=29


S7=S8=S9=S10

PLANTA
ESC 1:25

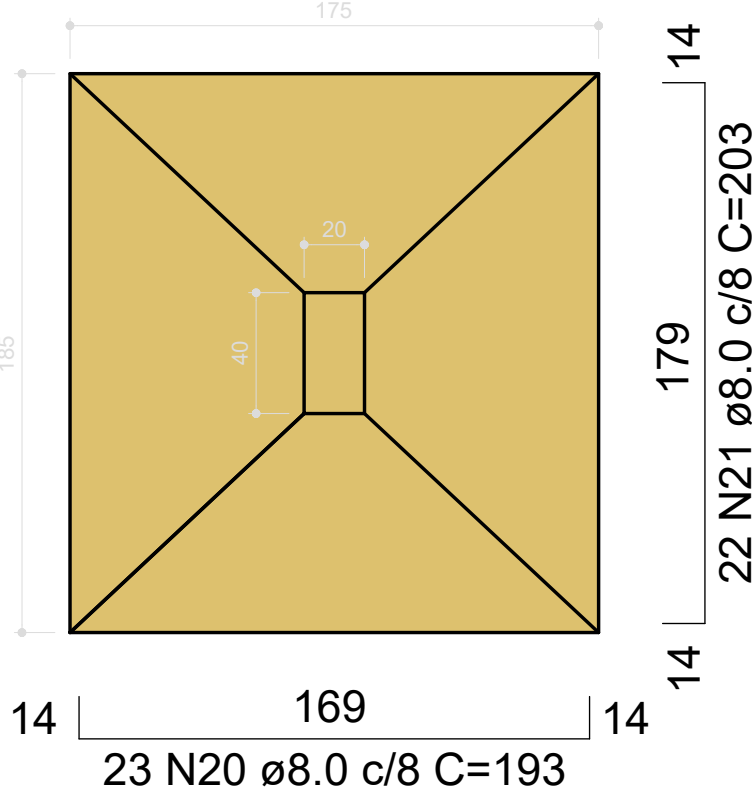

Solo compactado sobre a sapata
peso específico > 1600.00 kgf/m³

CORTE
ESC 1:25

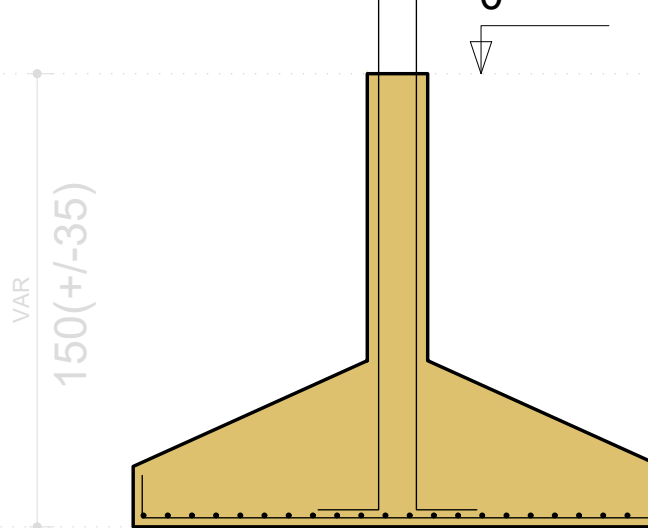

PROPRIETÁRIO: PREFEITURA MUNICIPAL DE COREMAS - PB

LINCOLN CARTAXO DE LIRA
JUNIOR:06897861405

Assinado de forma digital por LINCOLN
CARTAXO DE LIRA JUNIOR:06897861405
Dados: 2025.08.08 12:16:55 -03'00'

PROJETO: LINCOLN CARTAXO DE LIRA JÚNIOR CREA 160.814.689-8

CONSTRUÇÃO:

05/26

PROJETO: CONSTRUÇÃO DE GINÁSIO POLIESPORTIVO - ESTRUTURAL
CONVENIENTE: PREFEITURA MUNICIPAL DE COREMAS - PB
CONVENIADO: MUNICÍPIO DE COREMAS - PB
LOCALIDADE: COREMAS - PB


	DATA	RESPONSÁVEL	RUBRICA	DADOS
DESENHO	AGO/2025	LINCOLN CARTAXO		
CÓPIA				
VISTO				

ESCALAS	DESENHOS	CONVÊNIO
Indicada	- SAPATAS E PILARES PAV. FUNDAÇÃO (NÍVEL 0)	GOVERNO DO ESTADO
		ARQUIVO

Aprovações:

LCL PROJETOS

Av. Gov. Flávio Ribeiro Coutinho, 500, sl. 601
Jardim Oceania, 58037-005 - João Pessoa (PB)
Tel +55 (83) 99924.4447
e-mail: contato@lclprojetos.com

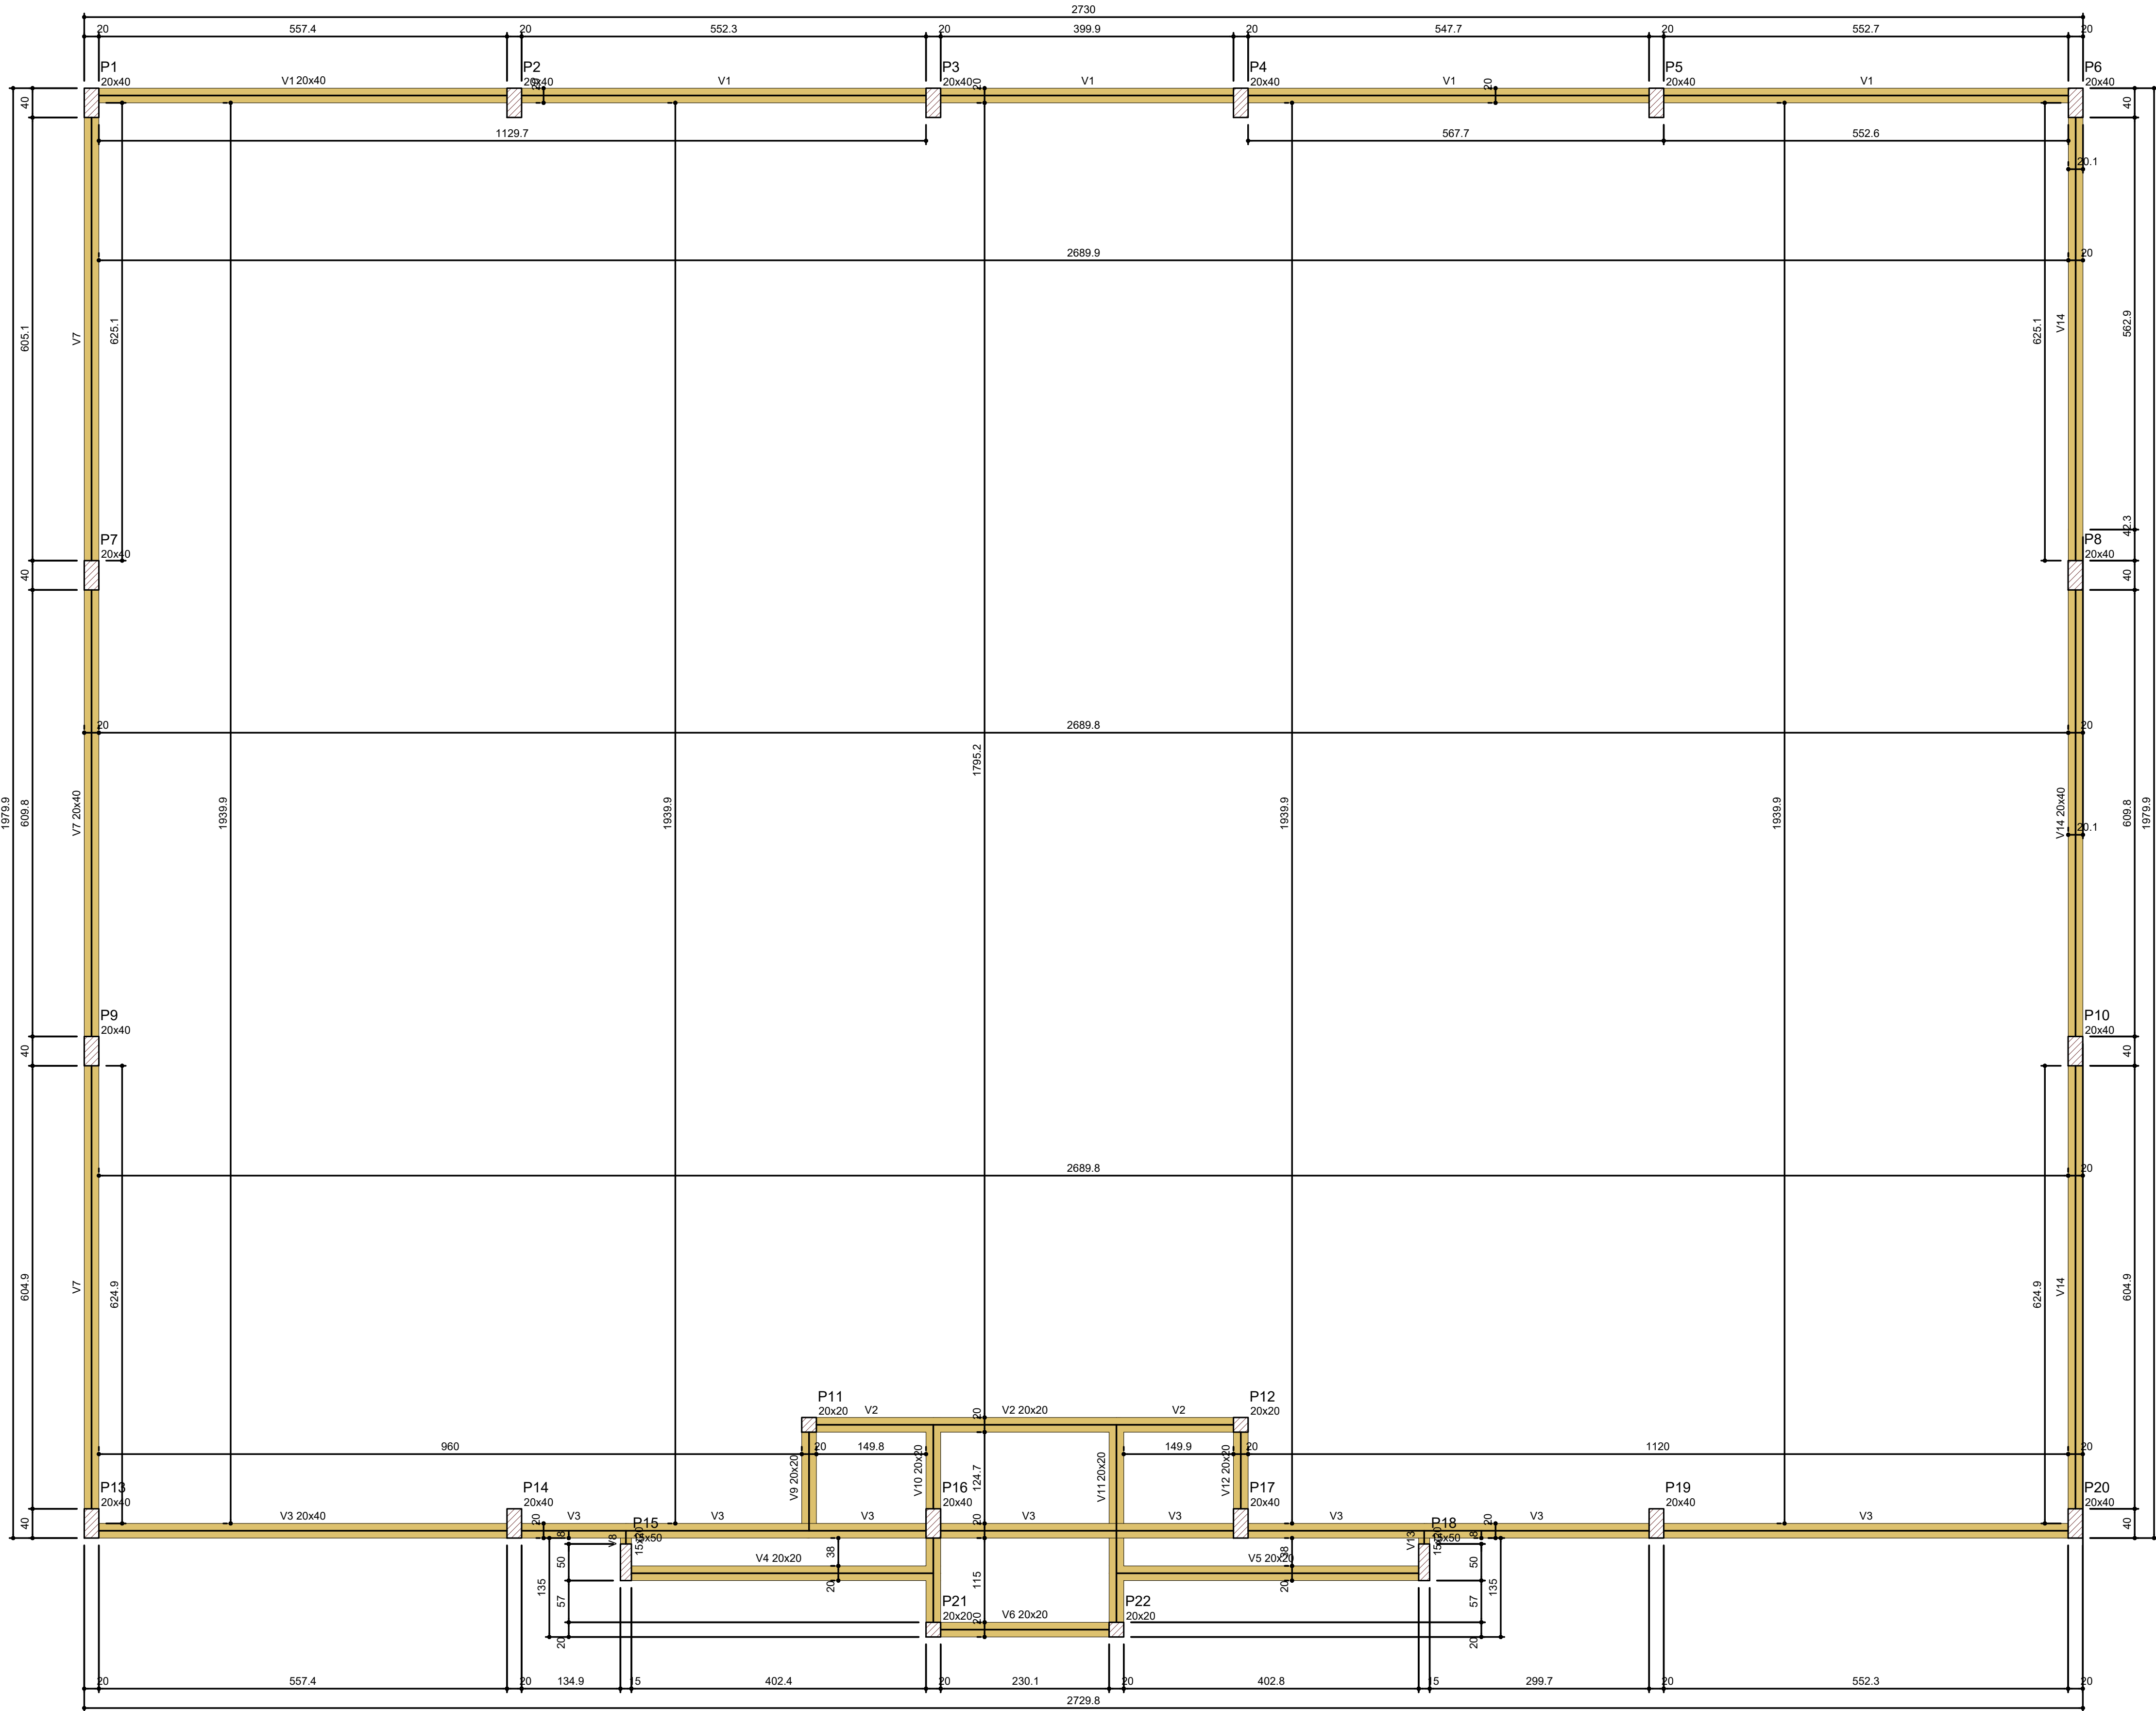

Forma do pavimento Baldrames (Nível 40)
escala 1:50

Vigas			
Nome	Seção (cm)	Elevação (cm)	Nível (cm)
V1	20x40	0	40
V2	20x20	0	40
V3	20x40	0	40
V4	20x20	0	40
V5	20x20	0	40
V6	20x20	0	40
V7	20x40	0	40
V8	15x20	0	40
V9	20x20	0	40
V10	20x20	0	40
V11	20x20	0	40
V12	20x20	0	40
V13	15x20	0	40
V14	20x40	0	40

Características dos materiais	
fck (kgf/cm²)	Ecs (kgf/cm²)
250	241500

Pilares			
Nome	Seção (cm)	Elevação (cm)	Nível (cm)
P1	20x40	0	40
P2	20x40	0	40
P3	20x40	0	40
P4	20x40	0	40
P5	20x40	0	40
P6	20x40	0	40
P7	20x40	0	40
P8	20x40	0	40
P9	20x40	0	40
P10	20x40	0	40
P11	20x20	0	40
P12	20x20	0	40
P13	20x40	0	40
P14	20x40	0	40
P15	15x50	0	40
P16	20x40	0	40
P17	20x40	0	40
P18	15x50	0	40
P19	20x40	0	40
P20	20x40	0	40
P21	20x20	0	40
P22	20x20	0	40

Legenda dos pilares	
	Pilar que passa
	Pilar com mudança de seção

Legenda das vigas e paredes	
	Viga

PROPRIETÁRIO: PREFEITURA MUNICIPAL DE COREMAS - PB
LINCOLN CARTAXO DE LIRA JUNIOR:06897861405 Assinado de forma digital por LINCOLN CARTAXO DE LIRA JUNIOR:06897861405
Dados: 2025.08.08 12:16:26 -03'00'

PROJETO: LINCOLN CARTAXO DE LIRA JÚNIOR CREA 160.814.689-8

CONSTRUÇÃO:

FOLHA 06/26
PROJETO: CONSTRUÇÃO DE GINÁSIO POLIESPORTIVO - ESTRUTURAL
CONVENIENTE: PREFEITURA MUNICIPAL DE COREMAS - PB
CONVENIADO: MUNICÍPIO DE COREMAS - PB
LOCALIDADE: COREMAS - PB

DESENHO	DATA	RESPONSÁVEL	RUBRICA	DADOS
CDMA	AGO/2025	LINCOLN CARTAXO		
VISTO				

ESCALAS	DESENHOS	CONVÊNIO
Indicada	- FORMA DO PAV. BALDRAMES (NÍVEL 40)	GOVERNO DO ESTADO
		ARQUIVO


Aprovações:

P1=P2=P3=P4


VISTA H
ESC 1:1

VISTA B
ESC 1:1

SEÇÃO
ESC 1:20

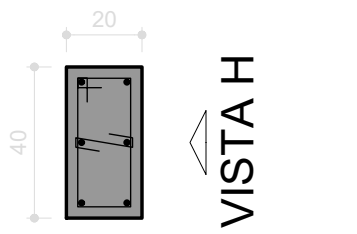

VISTA B

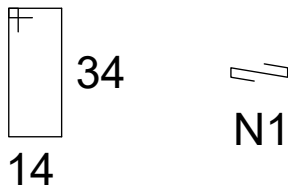

2 N2 ø5.0 C=107
2 N1 ø5.0 C=29

BALDRAMES - L2

40

30

38

10

6 N6 ø10.0 C=48

10

2 N2 ø5

*OBS.: OS QUADROS RESUMO REFERENTES A
ESTA PRANCHA CONSTAM NA PRANCHA 11/26

PROPRIETÁRIO: PREFEITURA MUNICIPAL DE COREMAS - PB
LINCOLN CARTAXO DE LIRA JUNIOR:06897861405
Assinado de forma digital por LINCOLN CARTAXO DE LIRA JUNIOR:06897861405
Dados: 2025.08.08 12:16:43 -03'00'

PROJETO: LINCOLN CARTAXO DE LIRA JÚNIOR CREA 160.814.689-8

CONSTRUÇÃO:

FOLHA 07/26	PROJETO: CONSTRUÇÃO DE GINÁSIO POLIESPORTIVO - ESTRUTURAL			
	CONVENIENTE: PREFEITURA MUNICIPAL DE COREMAS - PB			
	CONVENIADO: MUNICÍPIO DE COREMAS - PB			
	LOCALIDADE: COREMAS - PB			
	DATA	RESPONSÁVEL	RUBRICA	DADOS
DESENHO	AGO/2025	LINCOLN CARTAXO		
CÓPIA				
VISTO				
ESCALAS	DESENHOS			CONVÊNIO
				GOVERNO DO ESTADO
				ARQUIVO

Aprovações:

LCL PROJETOS

Av. Gov. Flávio Ribeiro Coutinho, 500, sl. 601
Jardim Esplanada, 59037-000 - João Pessoa (PB)
Tel. +55 (83) 99924.4447
e-mail: contato@lclprojetos.com

P11=P12=P21=P22

VISTA H
ESC 1:2

VISTA B
ESC 1:2

P15=P18

BALDRAMES - L2

SEÇÃO
ESC 1:20

VISTA H
VISTA B

4 N3 ø5.0 C=67

38

40
4 N7 ø10.0 C=78

BALDRAMES - L2

SEÇÃO
ESC 1:20

4 N5 ø5.0 C=117
4 N4 ø5.0 C=24

40
6 N9 ø10.0 C=78

ESC 1:2

*OBS.: OS QUADROS RESUMO REFERENTES A
ESTA PRANCHA CONSTAM NA PRANCHA 11/26

PROPRIETÁRIO: PREFEITURA MUNICIPAL DE COREMAS - PB
LINCOLN CARTAXO DE LIRA JUNIOR:06897861405
Assinado de forma digital por LINCOLN CARTAXO DE LIRA JUNIOR:06897861405
Dados: 2025.08.08 12:18:06 -03'00'

PROJETO: LINCOLN CARTAXO DE LIRA JÚNIOR CREA 160.814.689-8

CONSTRUÇÃO:

FOLHA 08/26	PROJETO: CONSTRUÇÃO DE GINÁSIO POLIESPORTIVO - ESTRUTURAL			
	CONVENIENTE: PREFEITURA MUNICIPAL DE COREMAS - PB			
	CONVENIADO: MUNICÍPIO DE COREMAS - PB			
	LOCALIDADE: COREMAS - PB			
	DATA	RESPONSÁVEL	RUBRICA	DADOS
DESENHO	AGO/2025	LINCOLN CARTAXO		
CÓPIA				
VISTO				
ESCALAS	DESENHOS			CONVÊNIO
Indicada	- ARMADURAS DOS PILARES PAV. BALDRAMES (NÍVEL 40)			GOVERNO DO ESTADO
				ARQUIVO

Aprovações:


P5=P14=P16=P17=P19

VISTA H
ESC 1:2

VISTA B
ESC 1:2

BALDRAMES - L2

SEÇÃO
ESC 1:20

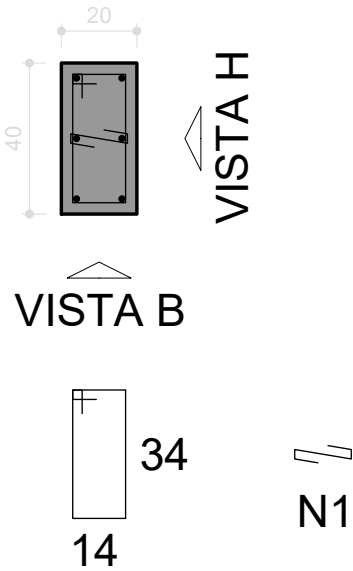

4 N2 ø5.0 C=107
4 N1 ø5.0 C=29

40

0

38

40
6 N7 ø10.0 C=78

40
4 N2 ø10

*OBS.: OS QUADROS RESUMO REFERENTES A
ESTA PRANCHA CONSTAM NA PRANCHA 11/26

PROPRIETÁRIO: PREFEITURA MUNICIPAL DE COREMAS - PB
LINCOLN CARTAXO DE LIRA JUNIOR:06897861405
Assinado de forma digital por LINCOLN CARTAXO DE LIRA JUNIOR:06897861405
Dados: 2025.08.08 12:19:33 -03'00'

PROJETO: LINCOLN CARTAXO DE LIRA JÚNIOR CREA 160.814.689-8

CONSTRUÇÃO:

FOLHA		PROJETO: CONSTRUÇÃO DE GINÁSIO POLIESPORTIVO - ESTRUTURAL		
09/26		CONVENIENTE: PREFEITURA MUNICIPAL DE COREMAS - PB		
		CONVENIADO: MUNICÍPIO DE COREMAS - PB		
		LOCALIDADE: COREMAS - PB		
	DATA	RESPONSÁVEL	RUBRICA	DADOS
DESENHO	AGO/2025	LINCOLN CARTAXO		
CÓPIA				
VISTO				
ESCALAS		DESENHOS		CONVÊNIO
Indicada		- ARMADURAS DOS PILARES PAV. BALDRAMES (NÍVEL 40)		GOVERNO DO ESTADO
				ARQUIVO

Aprovações:


P6=P13=P20

VISTA H
ESC 1:2

VISTA B
ESC 1:2

BALDRAMES - L2

SEÇÃO
ESC 1:20

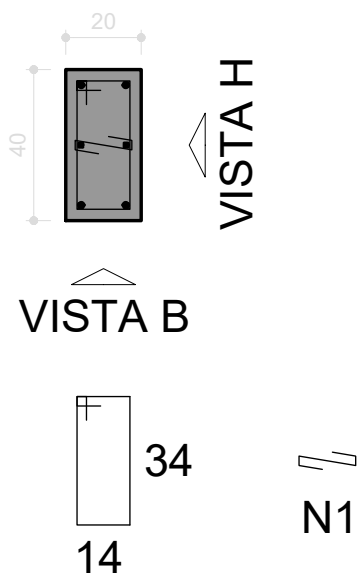

4 N2 ø5.0 C=107
4 N1 ø5.0 C=29

37
6 N8 ø10.0 C=37

4 N10 ø12.5 C=94

4 N2 c/10

*OBS.: OS QUADROS RESUMO REFERENTES A
ESTA PRANCHA CONSTAM NA PRANCHA 11/26

PROPRIETÁRIO: PREFEITURA MUNICIPAL DE COREMAS - PB
Assinado de forma digital por
LINCOLN CARTAXO DE LIRA
LIRA JUNIOR:06897861405 JUNIOR:06897861405
Dados: 2025.08.08 12:19:05 -03'00'
PROJETO: LINCOLN CARTAXO DE LIRA JÚNIOR CREA 160.814.689-8

CONSTRUÇÃO:

FOLHA 10/26
PROJETO: CONSTRUÇÃO DE GINÁSIO POLIESPORTIVO - ESTRUTURAL
CONVENIENTE: PREFEITURA MUNICIPAL DE COREMAS - PB
CONVENIADO: MUNICÍPIO DE COREMAS - PB
LOCALIDADE: COREMAS - PB

DESENHO	DATA	RESPONSÁVEL	RUBRICA	DADOS
CÓPIA	AGO/2025	LINCOLN CARTAXO		
VISTO				

ESCALAS	DESENHOS	CONVÊNIO
Indicada	- ARMADURAS DOS PILARES PAV. BALDRAMES (NÍVEL 40)	GOVERNO DO ESTADO
		ARQUIVO

Aprovações:


P7=P8=P9=P10

VISTA H
ESC 1:2

VISTA B
ESC 1:2

BALDRAMES - L2

SEÇÃO
ESC 1:20

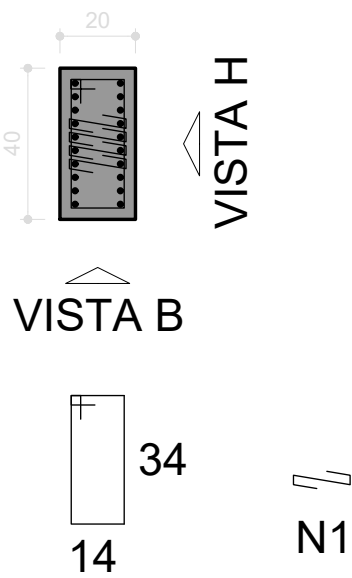

4 N2 ø5.0 C=107
4x4 N1 ø5.0 C=29

0

38

40
20 N7 ø10.0 C=78

40
4 N2 ø10

RELAÇÃO DO AÇO

4xP1 4xP7		5xP5 4xP11		3xP6 2xP15	
AÇO	N	DIAM (mm)	QUANT	C.UNIT (cm)	C.TOTAL (cm)
CA60	1	5.0	104	29	3016
	2	5.0	56	107	5992
	3	5.0	16	67	1072
	4	5.0	8	24	192
	5	5.0	8	117	936
CA50	6	10.0	24	48	1152
	7	10.0	126	78	9828
	8	10.0	18	37	666
	9	10.0	12	78	936
	10	12.5	12	94	1128

RESUMO DO AÇO

AÇO	DIAM (mm)	C.TOTAL (m)	PESO + 10% (kg)
CA50	10.0	125.8	85.3
CA60	5.0	112.1	19
PESO TOTAL (kg)			
CA50	97.3		
CA60	19		

Volume de concreto (C-25) = 0.54 m³
Área de forma = 8.56 m²

PROPRIETÁRIO: PREFEITURA MUNICIPAL DE COREMAS - PB

LINCOLN CARTAXO DE LIRA JUNIOR:06897861405
Assinado de forma digital por LINCOLN CARTAXO DE LIRA JUNIOR:06897861405
Dados: 2025.08.08 12:19:19 -03'00'

PROJETO: LINCOLN CARTAXO DE LIRA JÚNIOR CREA 160.814.689-8

CONSTRUÇÃO:

FOLHA 11/26

PROJETO: CONSTRUÇÃO DE GINÁSIO POLIESPORTIVO - ESTRUTURAL

CONVENIENTE: PREFEITURA MUNICIPAL DE COREMAS - PB

CONVENIADO: MUNICÍPIO DE COREMAS - PB


LOCALIDADE: COREMAS - PB

	DATA	RESPONSÁVEL	RUBRICA	DADOS
DESENHO	AGO/2025	LINCOLN CARTAXO		
CÓPIA				
VISTO				


ESCALAS	DESENHOS	CONVÊNIO
Indicada	- ARMADURAS DOS PILARES PAV. BALDRAMES (NÍVEL 40)	GOVERNO DO ESTADO
		ARQUIVO

Aprovações:


V1
ESC 1:30

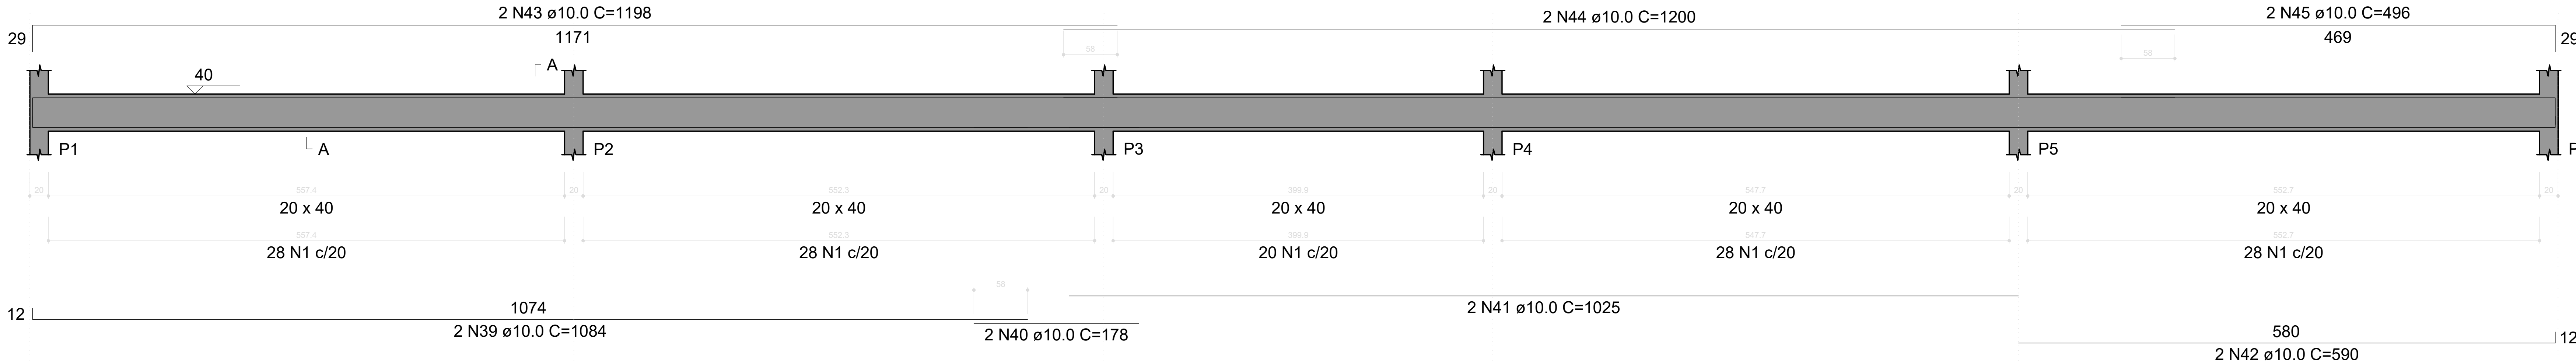


SEÇÃO A-A
ESC 1:25

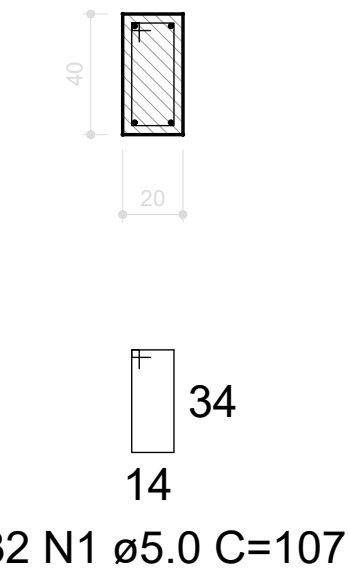


V6
ESC 1:30

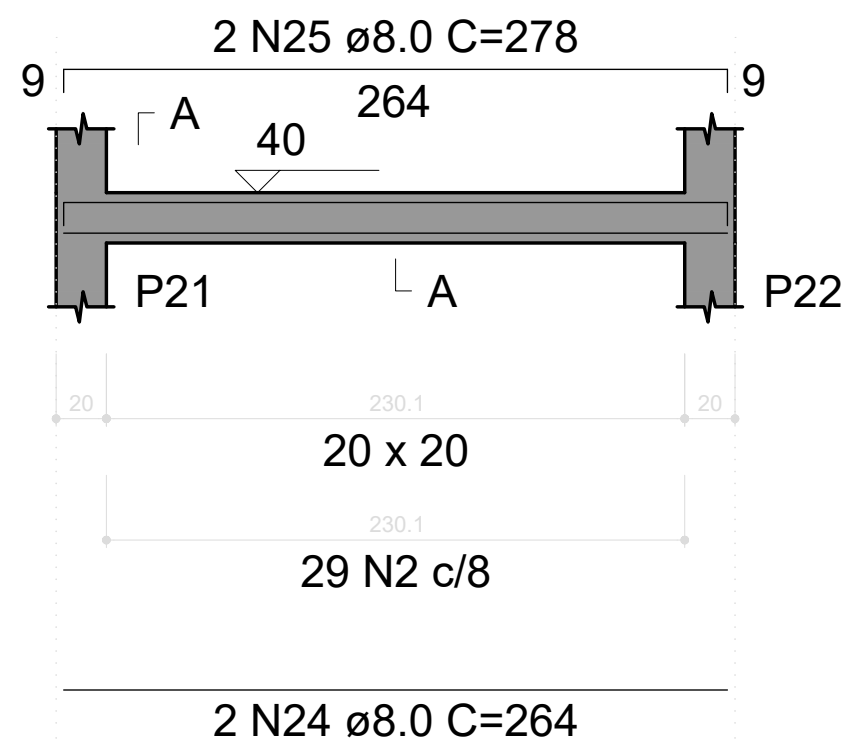


V7
ESC 1:30

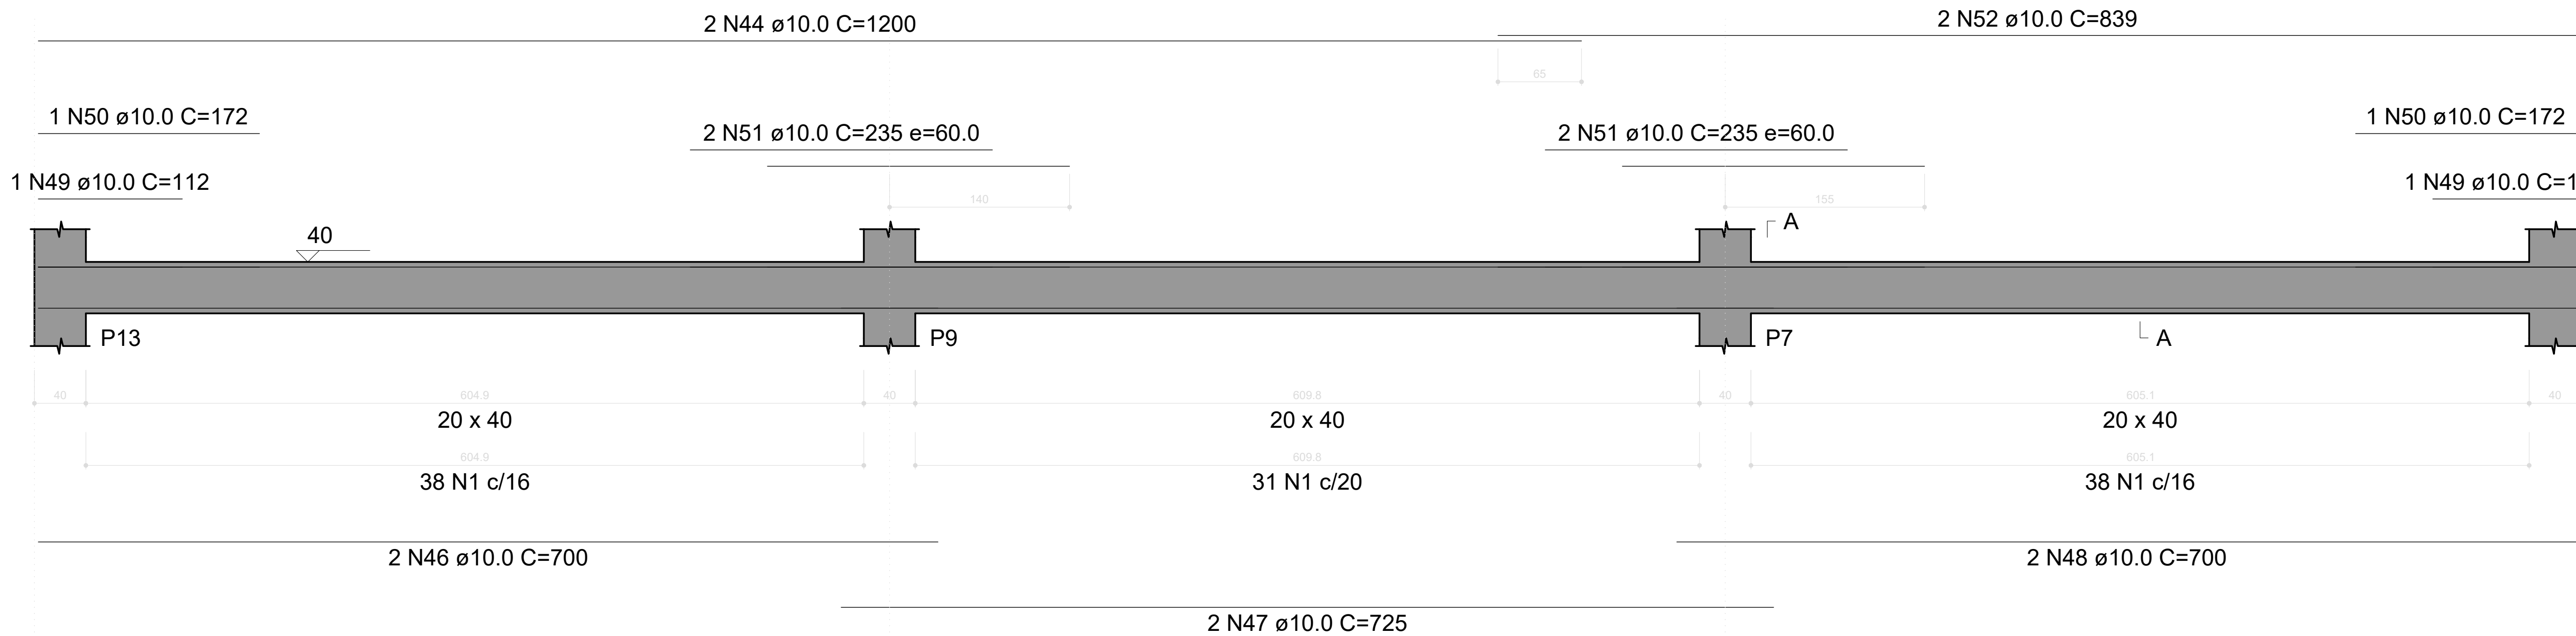

V8
ESC 1:30

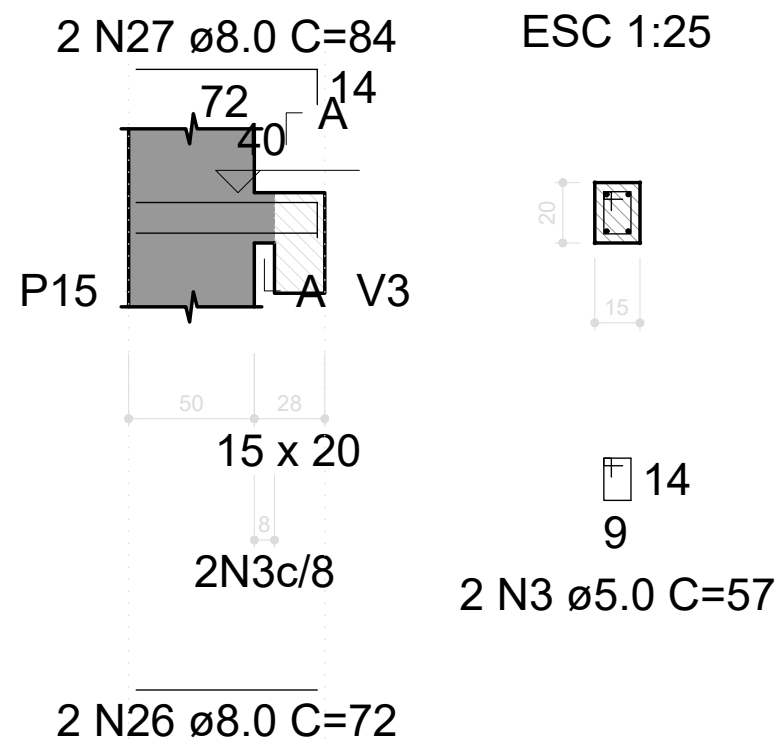

SEÇÃO A-A
ESC 1:25

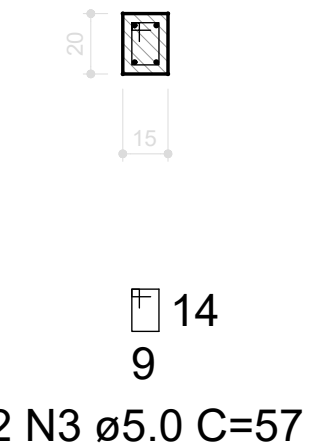

*OBS.: OS QUADROS RESUMO REFERENTES A ESTA PRANCHA CONSTAM NA PRANCHA 14/26


PROPRIETÁRIO: PREFEITURA MUNICIPAL DE COREMAS - PB
LINCOLN CARTAXO DE LIRA
JUNIOR:06897861405
PROJETO: LINCOLN CARTAXO DE LIRA JÚNIOR CREA 160.814.689-8

CONSTRUÇÃO:



FOLHA	PROJETO:	CONSTRUÇÃO DE GINÁSIO POLIESPORTIVO - ESTRUTURAL
12/26	CONVENIENTE:	PREFEITURA MUNICIPAL DE COREMAS - PB
	CONVENIADO:	MUNICÍPIO DE COREMAS - PB
	LOCALIDADE:	COREMAS - PB
DESENHO	DATA	RESPONSÁVEL
CÓPIA	AGO/2025	LINCOLN CARTAXO
VISTO		
ESCALAS	DESENHOS	CONVÊNIO
Indicada	- VIGAS PAV. BALDRAMES (NÍVEL 40)	GOVERNO DO ESTADO
		ARQUIVO

Aprovações:

V3
ESC 1:30

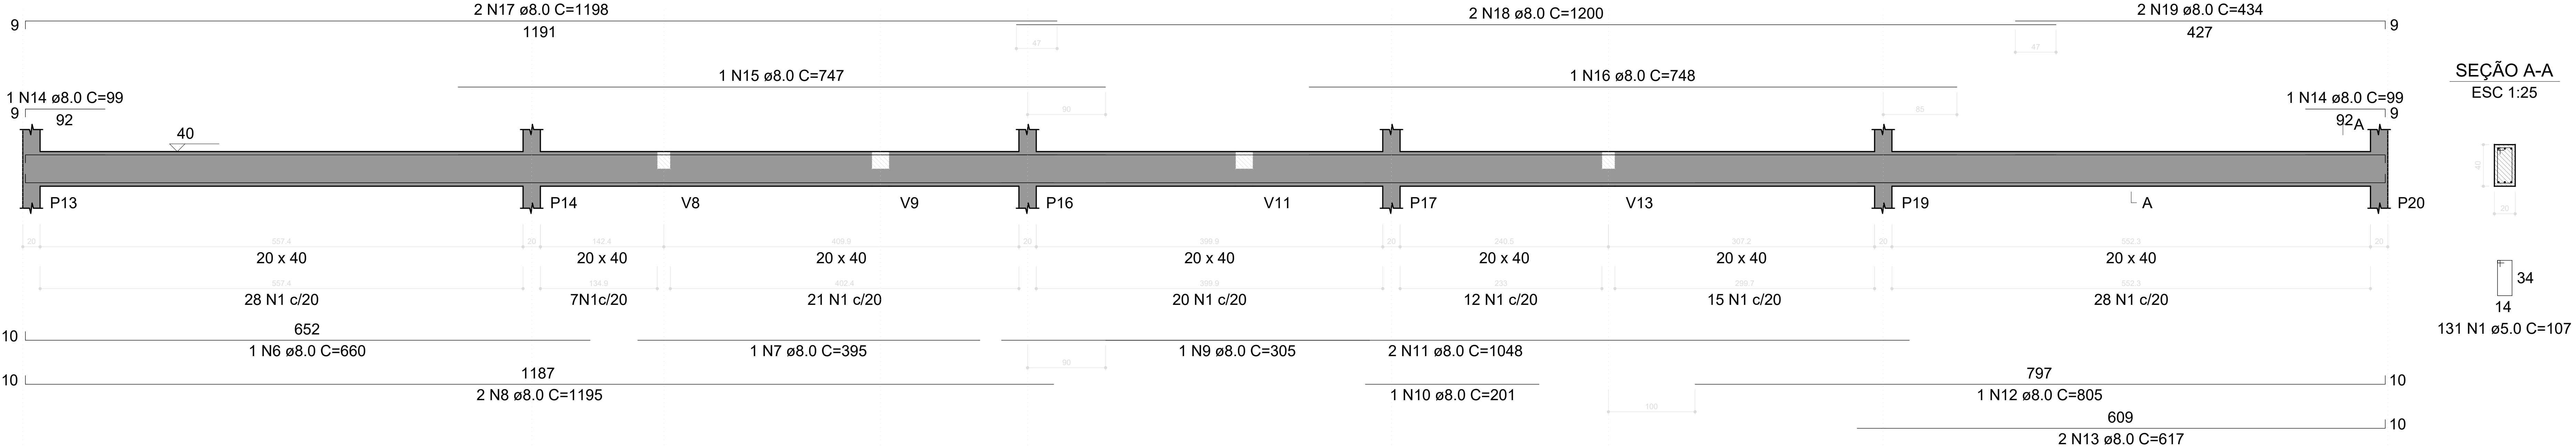


SEÇÃO A-A
ESC 1:25

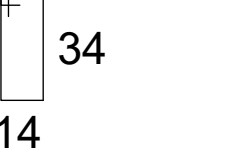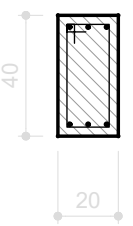


131 N1 ø5.0 C=107

V2
ESC 1:30

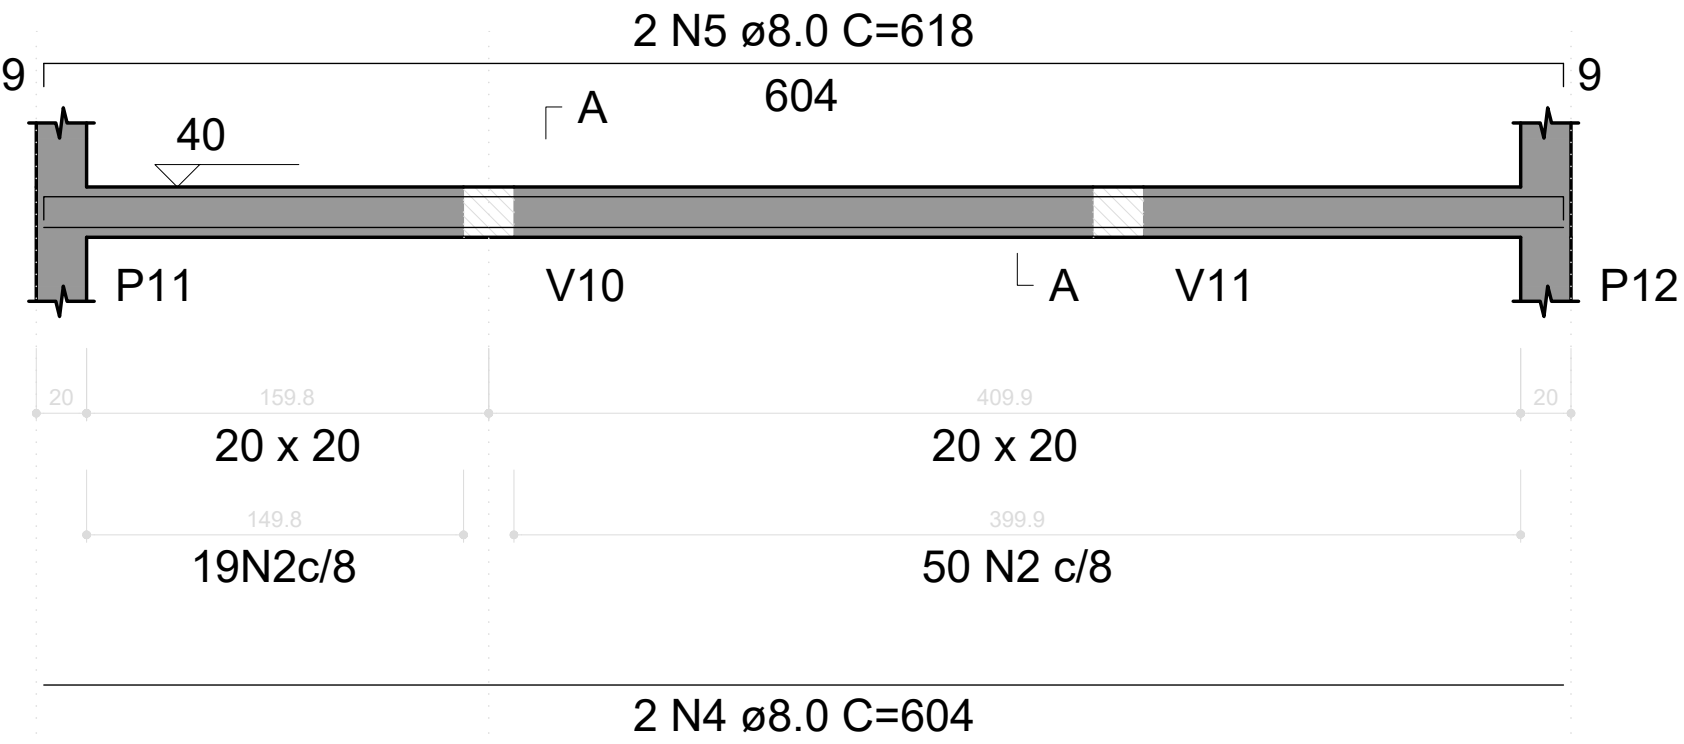


SEÇÃO A-A
ESC 1:25

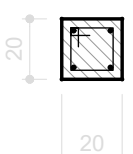


69 N2 ø5.0 C=67

V9
ESC 1:30

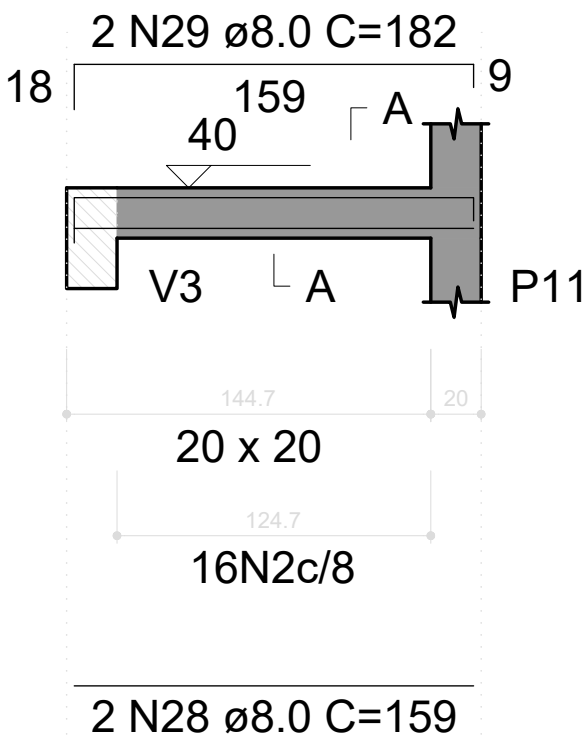


SEÇÃO A-A
ESC 1:25

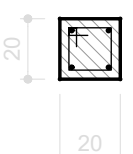


16 N2 ø5.0 C=67

V10
ESC 1:30

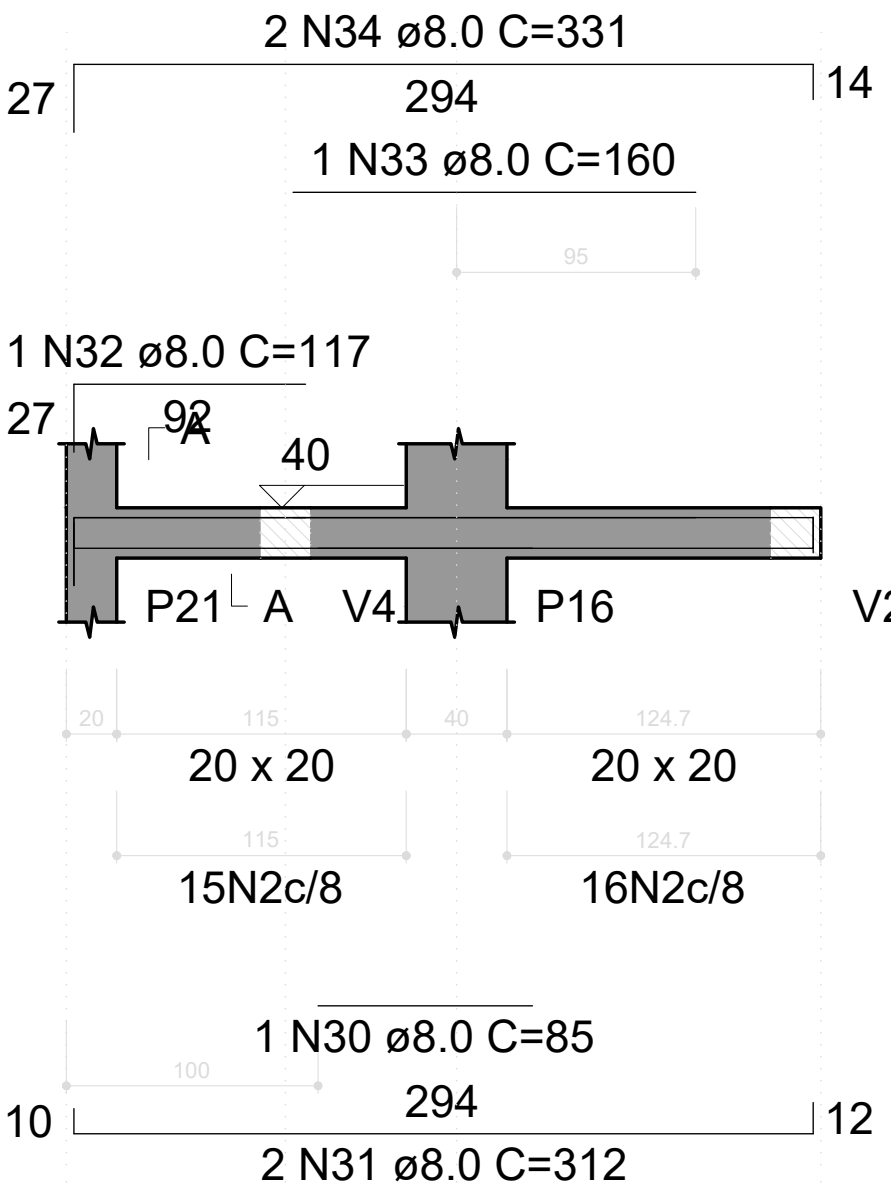


SEÇÃO A-A
ESC 1:25

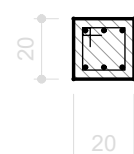


31 N2 ø5.0 C=67

V11
ESC 1:30

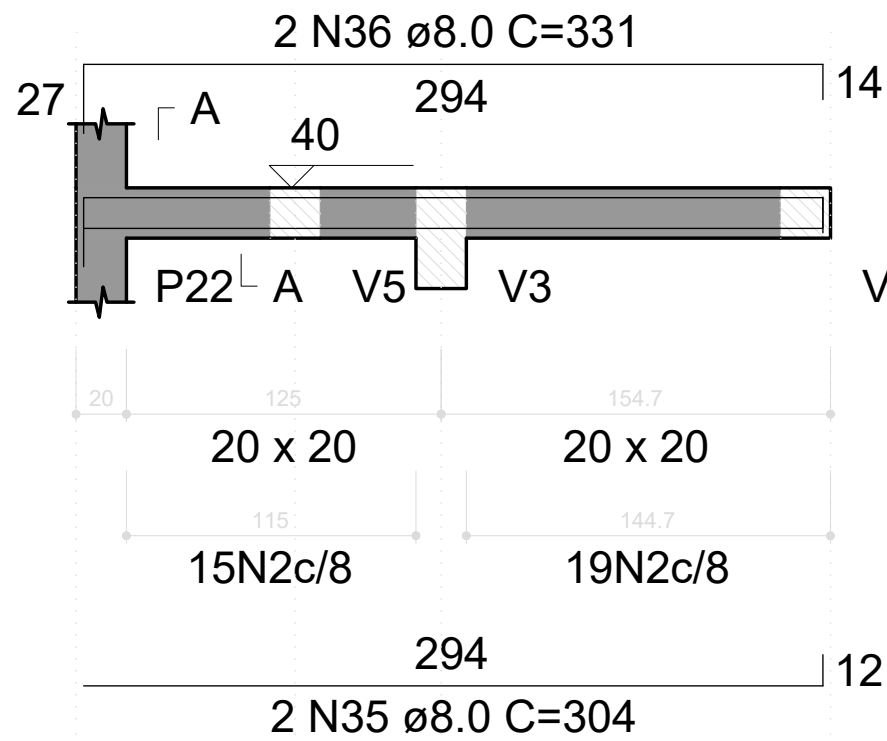


SEÇÃO A-A
ESC 1:25

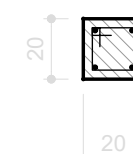


34 N2 ø5.0 C=67

V12
ESC 1:30

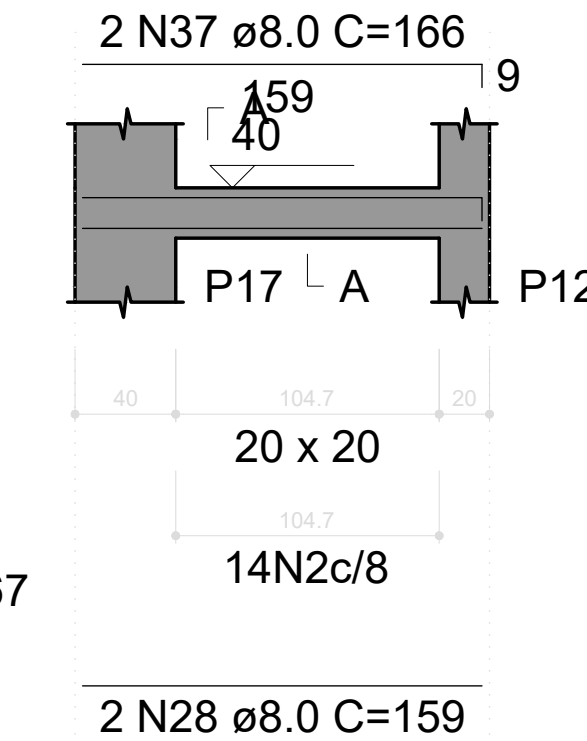


SEÇÃO A-A
ESC 1:25

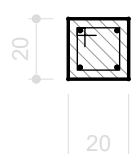


14 N2 ø5.0 C=67

V13
ESC 1:30

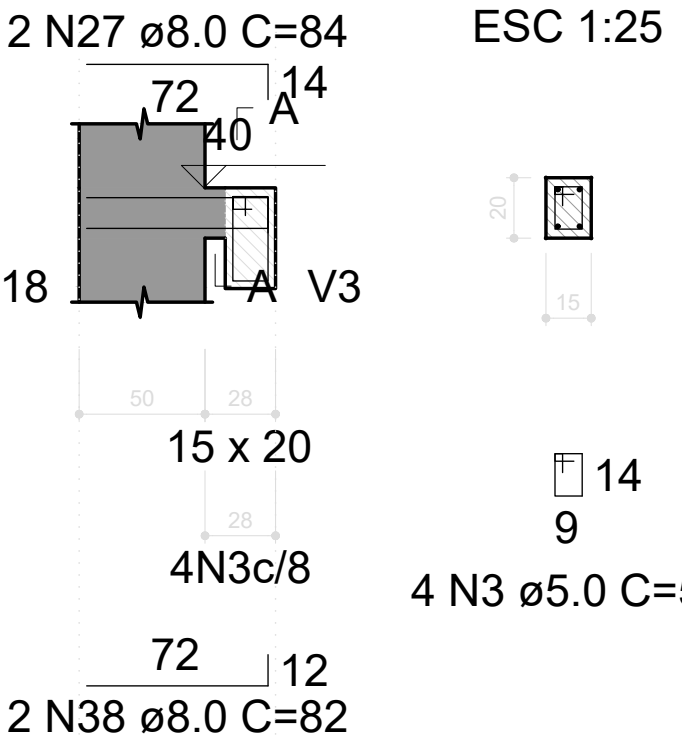


SEÇÃO A-A
ESC 1:25

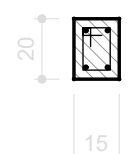

4 N3 ø5.0 C=57

SUSPENSÃO V3
ESC 1:25

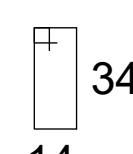

1 N53 ø10.0 C=109

*OBS.: OS QUADROS RESUMO REFERENTES A ESTA PRANCHA CONSTAM NA PRANCHA 14/26

PROPRIETÁRIO: LINCOLN CARTAXO DE LIRA JUNIOR:06897861405
PREFEITURA MUNICIPAL DE COREMAS - PB
Assinado de forma digital por LINCOLN CARTAXO DE LIRA JUNIOR:06897861405
Dados: 2025.08.08 12:21:24 -03'00'

PROJETO: LINCOLN CARTAXO DE LIRA JÚNIOR CREA 160.814.689-8


CONSTRUÇÃO:

FOLHA: 13/26
PROJETO: CONSTRUÇÃO DE GINÁSIO POLIESPORTIVO - ESTRUTURAL
CONVENIENTE: PREFEITURA MUNICIPAL DE COREMAS - PB
CONVENIADO: MUNICÍPIO DE COREMAS - PB
LOCALIDADE: COREMAS - PB


	DATA	RESPONSÁVEL	RUBRICA	DADOS
DESENHO	AGO/2025	LINCOLN CARTAXO		
CÓPIA				
VISTO				
ESCALAS	DESENHOS			CONVÊNIO
Indicada	- VIGAS PAV. BALDRAMES (NÍVEL 40)			GOVERNO DO ESTADO
				ARQUIVO

Aprovações:


V4
ESC 1:30

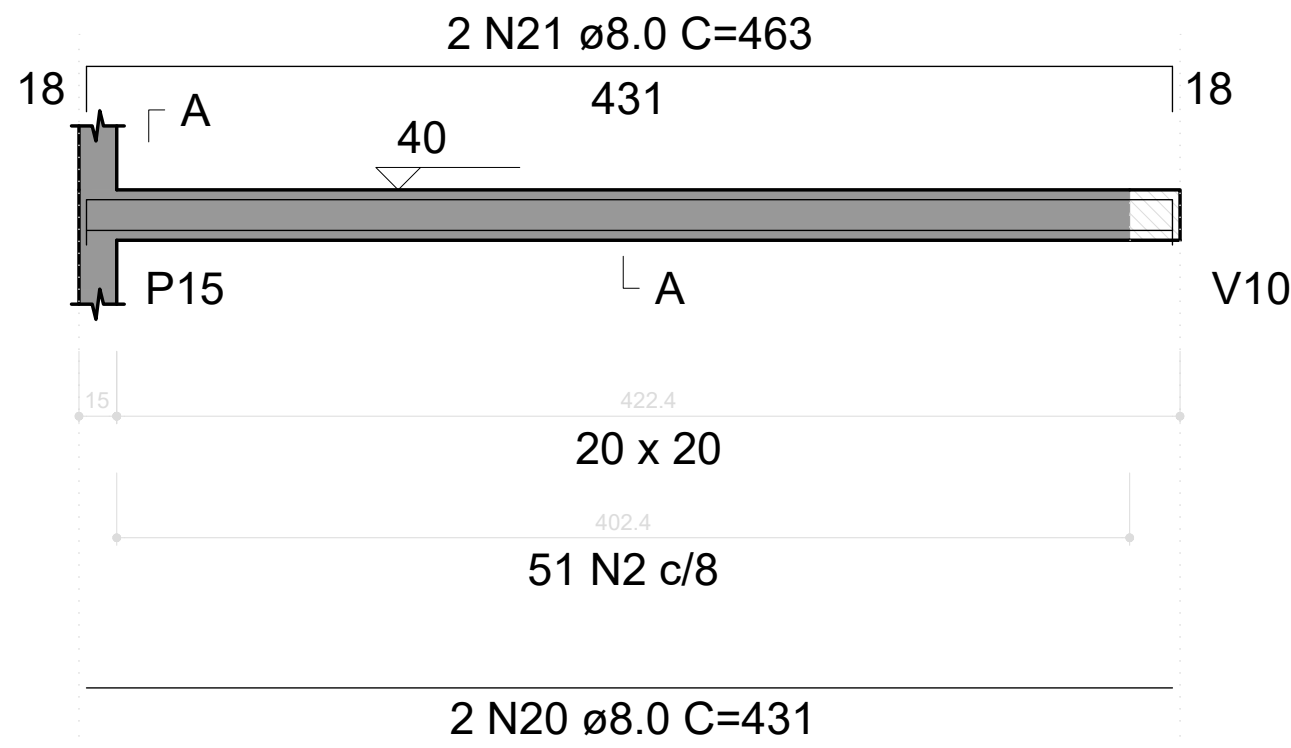


SEÇÃO A-A
ESC 1:25

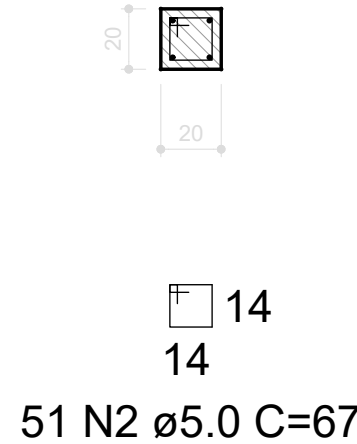


V5
ESC 1:30

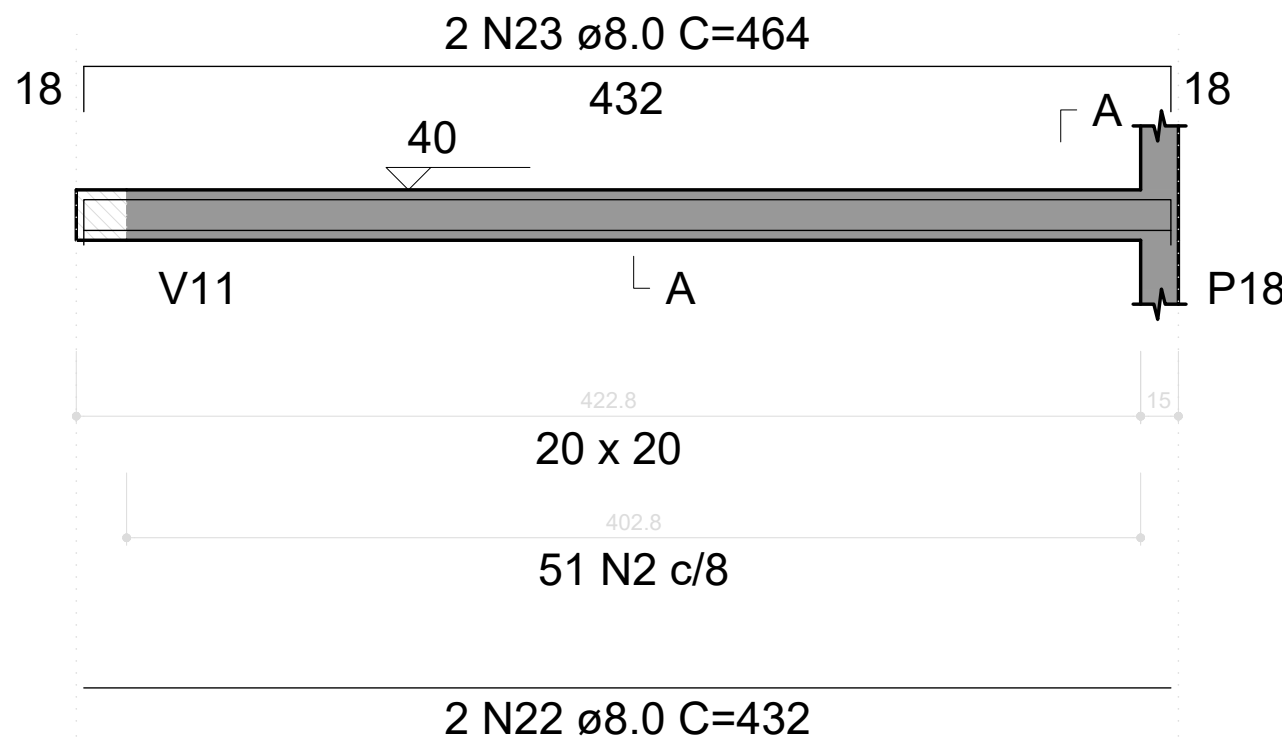


SEÇÃO A-A
ESC 1:25

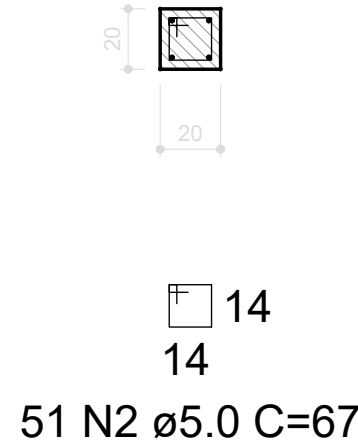

V14
ESC 1:30

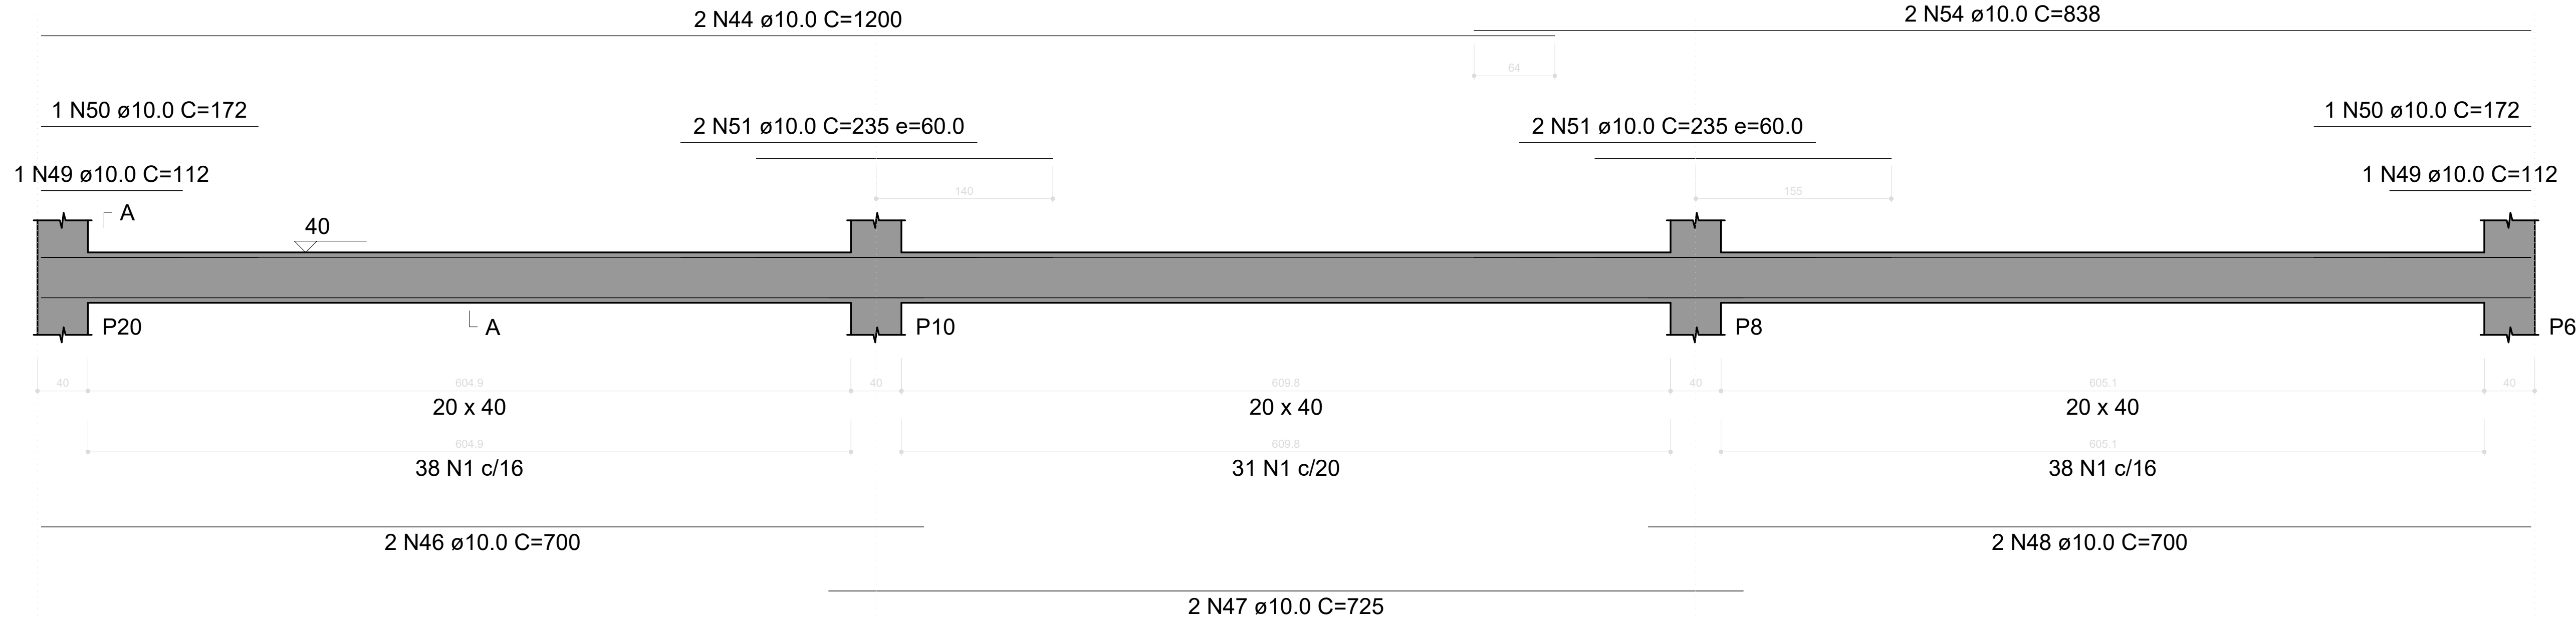

SEÇÃO A-A
ESC 1:25

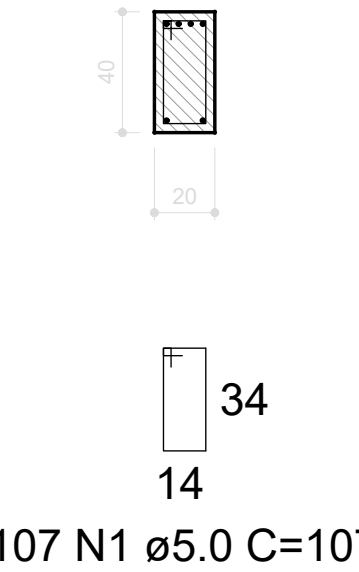

RELAÇÃO DO AÇO					
AÇO	N	DIAM (mm)	QUANT	C.UNIT (cm)	C.TOTAL (cm)
CA60	1	5.0	477	107	51039
	2	5.0	295	67	19765
CA50	3	5.0	6	57	342
	4	8.0	2	604	1208
	5	8.0	2	618	1236
	6	8.0	1	660	660
	7	8.0	1	395	395
	8	8.0	2	1195	2390
	9	8.0	1	305	305
	10	8.0	1	201	201
	11	8.0	2	1048	2096
	12	8.0	1	805	805
	13	8.0	2	617	1234
	14	8.0	2	99	198
	15	8.0	1	747	747
	16	8.0	1	748	748
	17	8.0	2	1198	2396
	18	8.0	2	1200	2400
	19	8.0	2	434	868
	20	8.0	2	431	862
	21	8.0	2	463	926
	22	8.0	2	432	864
	23	8.0	2	464	928
	24	8.0	2	264	528
	25	8.0	2	278	556
	26	8.0	2	72	144
	27	8.0	4	84	336
	28	8.0	4	159	636
	29	8.0	2	182	364
	30	8.0	1	85	85
	31	8.0	2	312	624
	32	8.0	1	117	117
	33	8.0	1	160	160
	34	8.0	2	331	662
	35	8.0	2	304	608
	36	8.0	2	331	662
	37	8.0	2	166	332
	38	8.0	2	82	164
	39	10.0	2	1084	2168
	40	10.0	2	178	356
	41	10.0	2	1025	2050
	42	10.0	2	590	1180
	43	10.0	2	1198	2396
	44	10.0	6	1200	7200
	45	10.0	2	496	992
	46	10.0	4	700	2800
	47	10.0	4	725	2900
	48	10.0	4	700	2800
	49	10.0	4	112	448
	50	10.0	4	172	688
	51	10.0	8	235	1880
	52	10.0	2	839	1678
	53	10.0	1	109	109
	54	10.0	2	838	1676

RESUMO DO AÇO			
AÇO	DIAM (mm)	C.TOTAL (m)	PESO + 10% (kg)
CA50	8.0	274.4	119.1
CA60	10.0	313.2	212.4
CA60	5.0	711.5	120.6
PESO TOTAL (kg)			
CA50	331.5		
CA60	120.6		

Volume de concreto (C-25) = 8.66 m³
Área de forma = 111.16 m²

PROPRIETÁRIO: PREFEITURA MUNICIPAL DE COREMAS - PB
LINCOLN CARTAXO DE LIRA JUNIOR:06897861405
PROJETO: LINCOLN CARTAXO DE LIRA JÚNIOR CREA 160.814.689-8


CONSTRUÇÃO:

14/26

FOLHA: PROJETO: CONSTRUÇÃO DE GINÁSIO POLIESPORTIVO - ESTRUTURAL
CONVENIENTE: PREFEITURA MUNICIPAL DE COREMAS - PB
CONVENIADO: MUNICÍPIO DE COREMAS - PB
LOCALIDADE: COREMAS - PB

DESENHO	DATA	RESPONSÁVEL	RUBRICA	DADOS
CÓPIA	AGO/2025	LINCOLN CARTAXO		
VISTO				

ESCALAS	DESENHOS	CONVÊNIO
Indicada	- VIGAS PAV. BALDRAMES (NÍVEL 40)	GOVERNO DO ESTADO
		ARQUIVO

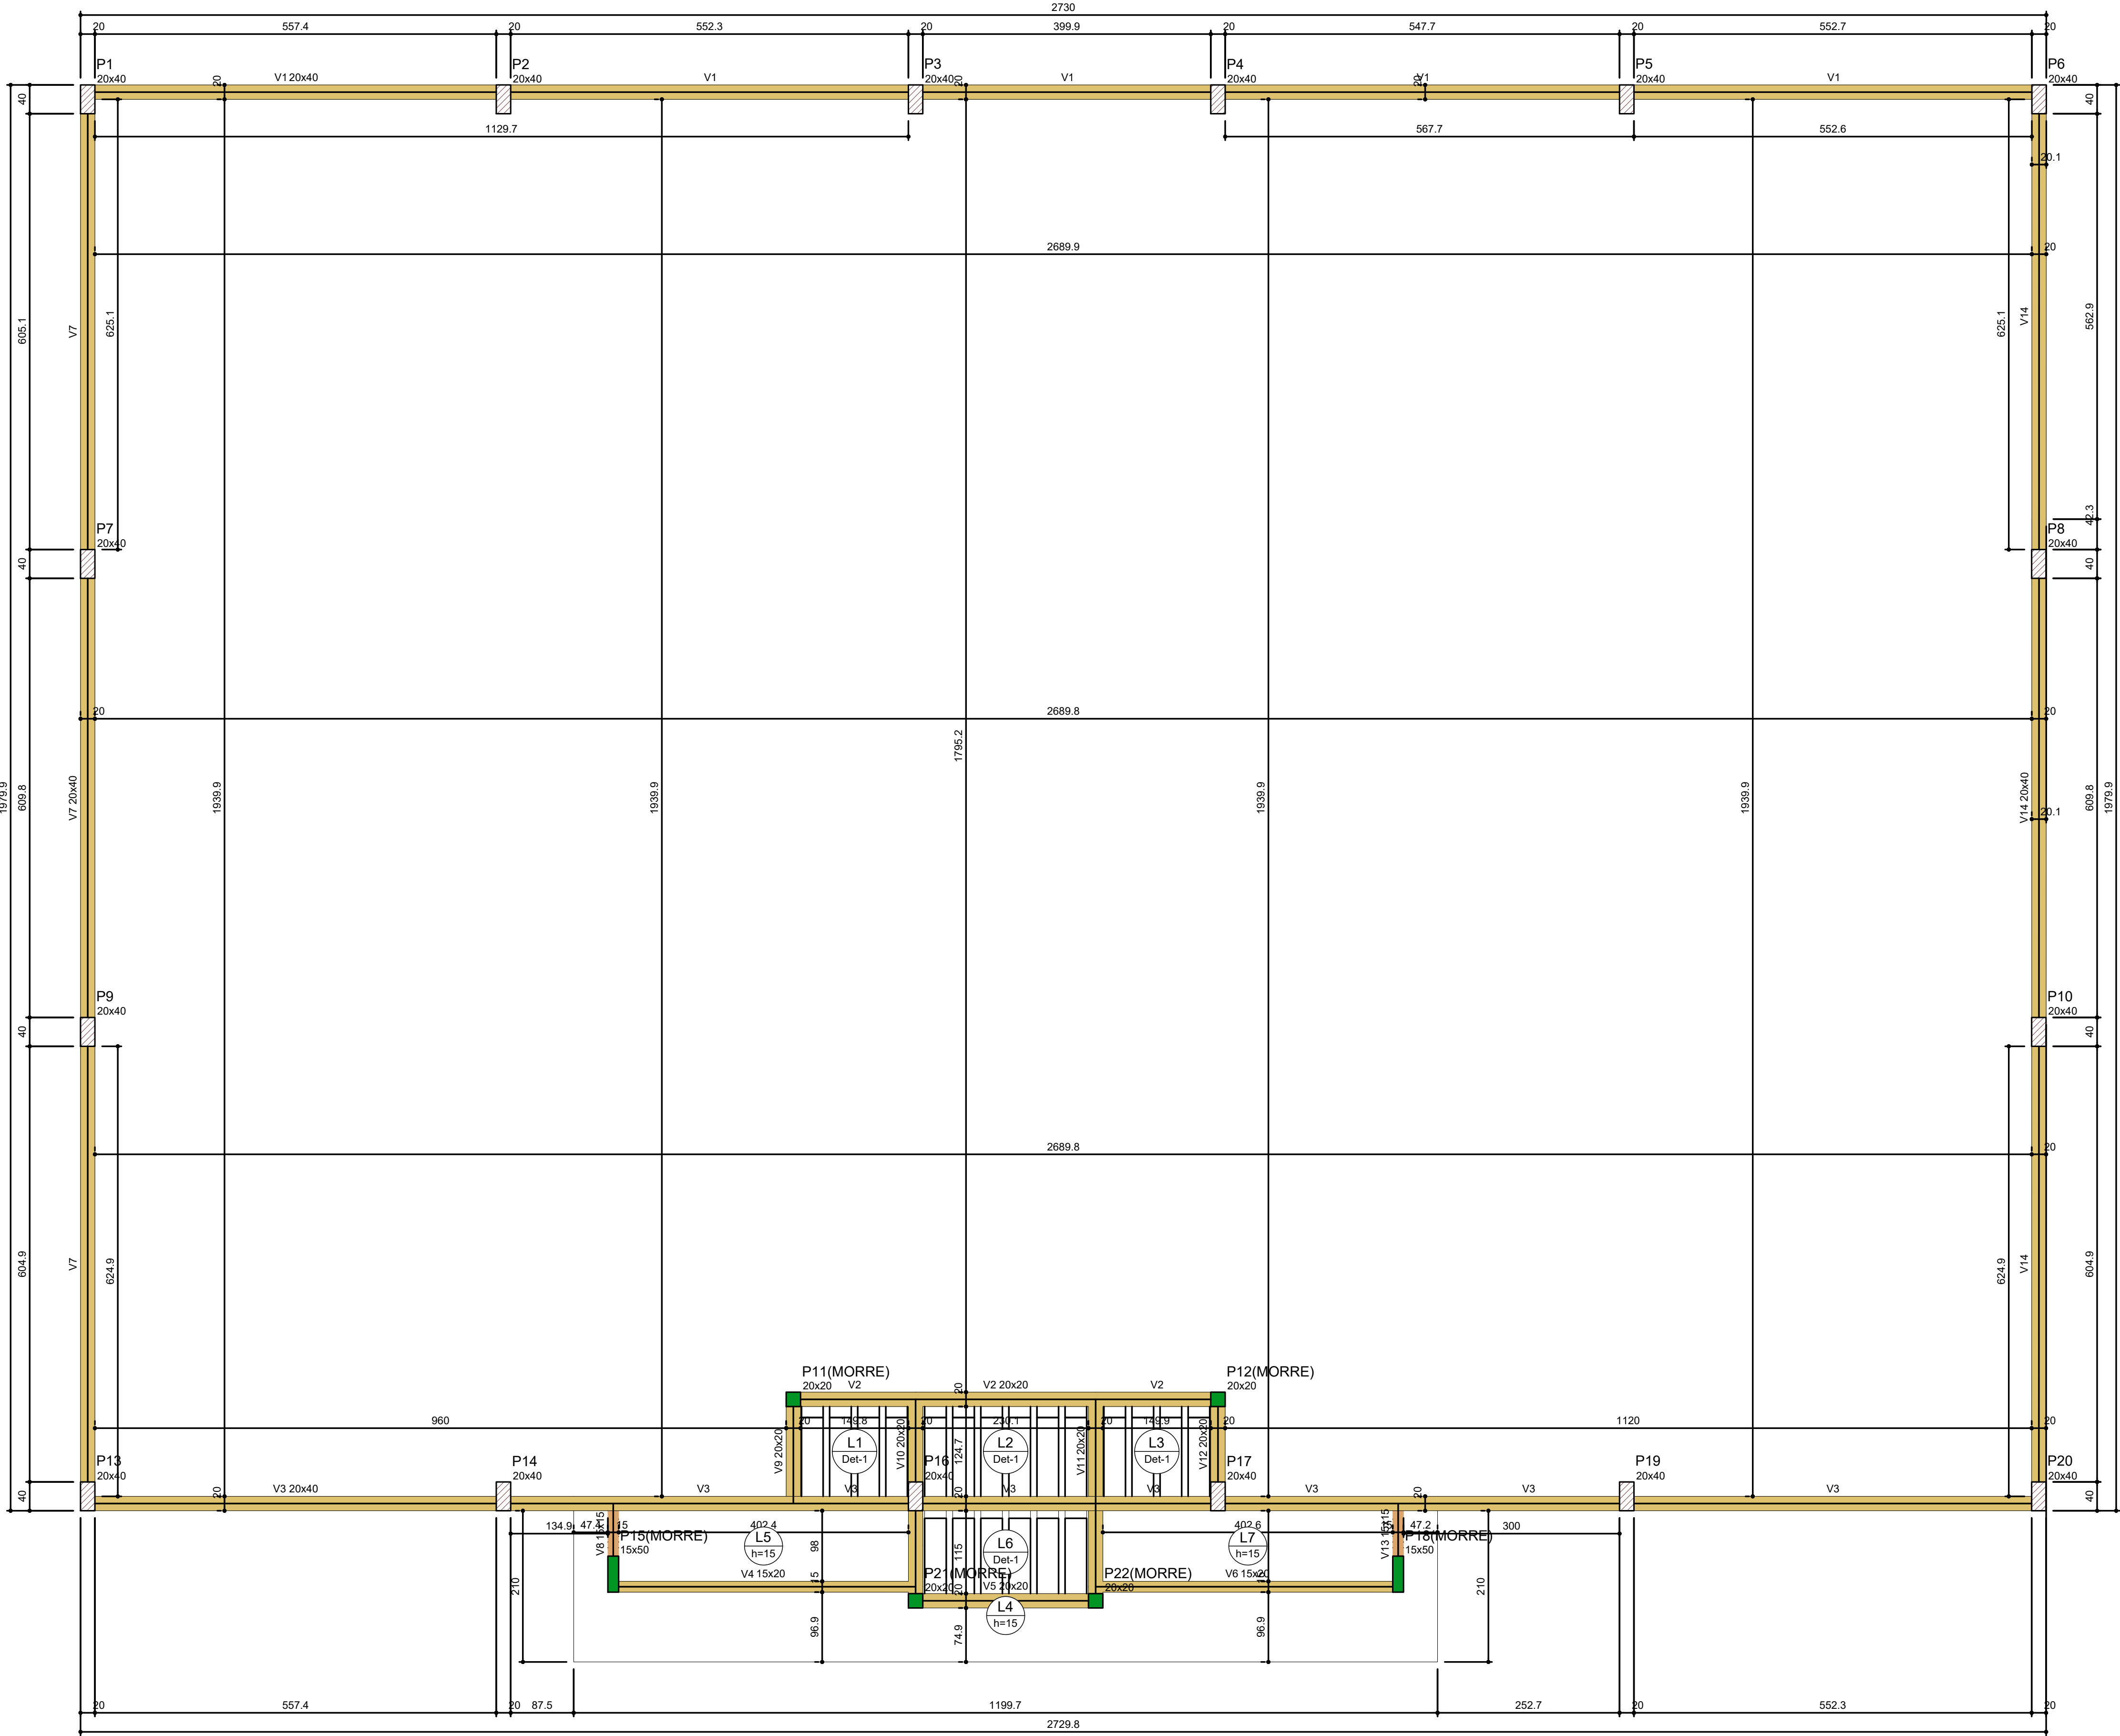

Forma do pavimento Laje (Nível 305)
escala 1:50

Vigas			
Nome	Seção (cm)	Elevação (cm)	Nível (cm)
V1	20x40	0	305
V2	20x20	0	305
V3	20x40	0	305
V4	15x20	0	305
V5	20x20	0	305
V6	15x20	0	305
V7	20x40	0	305
V8	15x15	0	305
V9	20x20	0	305
V10	20x20	0	305
V11	20x20	0	305
V12	20x20	0	305
V13	15x15	0	305
V14	20x40	0	305

Lajes						
Dados				Sobrecarga (kgf/m²)		
Nome	Tipo	Altura (cm)	Elevação (cm)	Nível (cm)	Adicional	Acidental
L1	Trelçada 1D	15	0	305	50	50
L2	Trelçada 1D	15	0	305	50	50
L3	Trelçada 1D	15	0	305	50	50
L4	Maciça	15	0	305	50	50
L5	Maciça	15	0	305	50	50
L6	Trelçada 1D	15	0	305	50	50
L7	Maciça	15	0	305	50	50


Área de lajes			
Tipo	Altura (cm)	Bloco de Enchimento	Área (m²)
Maciça	15	-	20.00
Trelçada 1D	15	B8/30/125	9.25

Características dos materiais	
fck (kgf/cm²)	Ecs (kgf/cm²)
250	241500

Pilares			
Nome	Seção (cm)	Elevação (cm)	Nível (cm)
P1	20x40	0	305
P2	20x40	0	305
P3	20x40	0	305
P4	20x40	0	305
P5	20x40	0	305
P6	20x40	0	305
P7	20x40	0	305
P8	20x40	0	305
P9	20x40	0	305
P10	20x40	0	305
P11	20x20	0	305
P12	20x20	0	305
P13	20x40	0	305
P14	20x40	0	305
P15	15x50	0	305
P16	20x40	0	305
P17	20x40	0	305
P18	15x50	0	305
P19	20x40	0	305
P20	20x40	0	305
P21	20x20	0	305
P22	20x20	0	305

Legenda dos pilares	
	Pilar que morre
	Pilar que passa

Legenda das vigas e paredes	
	Viga
	Viga chata ou invertida

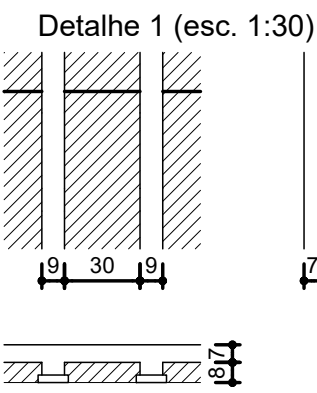

Blocos de enchimento					
Detalhe	Tipo	Nome	Dimensões(cm)		
			hb	bx	by
1	EPS Unidirecional	B8/30/125	8	30	125

Blocos de enchimento					
Detalhe	Tipo	Nome	Dimensões(cm)		
			hb	bx	by
1	EPS Unidirecional	B8/30/125	8	30	125

PROPRIETÁRIO: PREFEITURA MUNICIPAL DE COREMAS - PB

LINCOLN CARTAXO DE LIRA
JUNIOR:06897861405

PROJETO: LINCOLN CARTAXO DE LIRA JÚNIOR CREA 160.814.889-8


CONSTRUÇÃO:

FOLHA 15/26
PROJETO: CONSTRUÇÃO DE GINÁSIO POLIESPORTIVO - ESTRUTURAL
CONVENIENTE: PREFEITURA MUNICIPAL DE COREMAS - PB
CONVENIADO: MUNICÍPIO DE COREMAS - PB
LOCALIDADE: COREMAS - PB


DATA	RESPONSÁVEL	RUBRICA	DADOS
AGO/2025	LINCOLN CARTAXO		
CÓPIA			
VISTO			
ESCALAS	DESENHOS	CONVÊNIO	
Indicada	- FORMA DO PAVIMENTO LAJE (NÍVEL 305)	GOVERNO DO ESTADO	
		ARQUIVO	

Aprovações:


V1
ESC 1:30

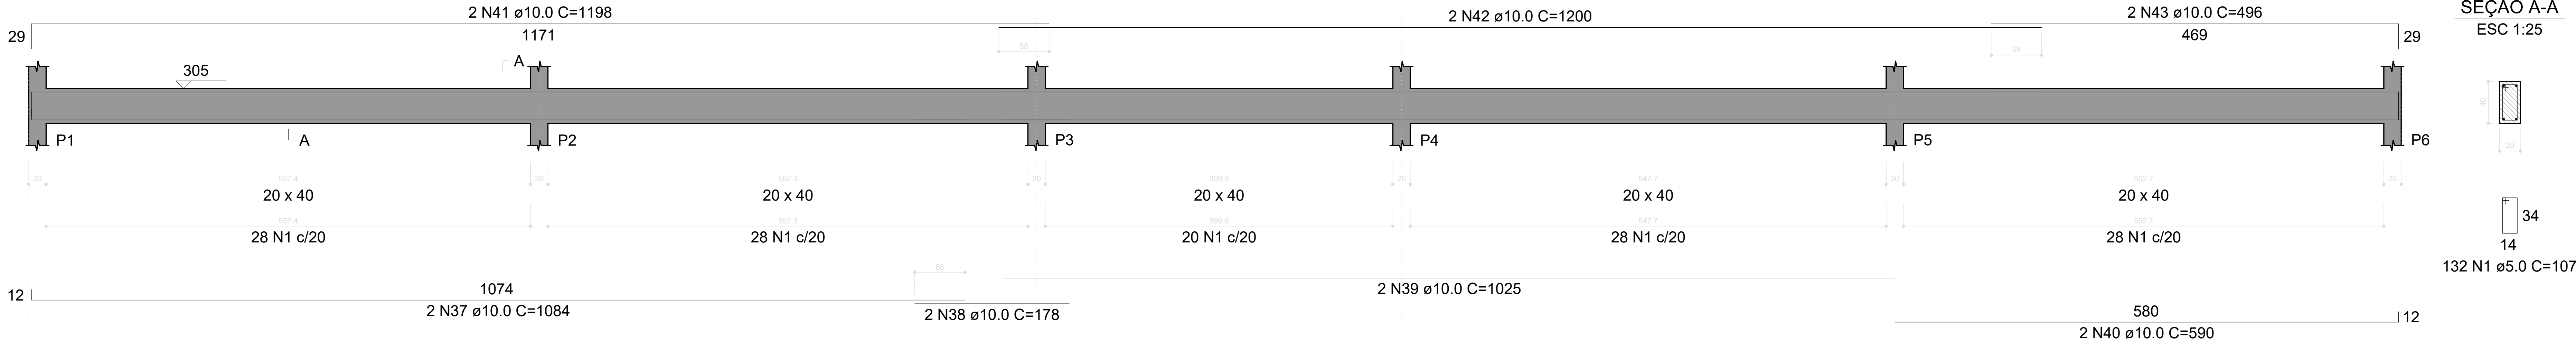


SEÇÃO A-A
ESC 1:25

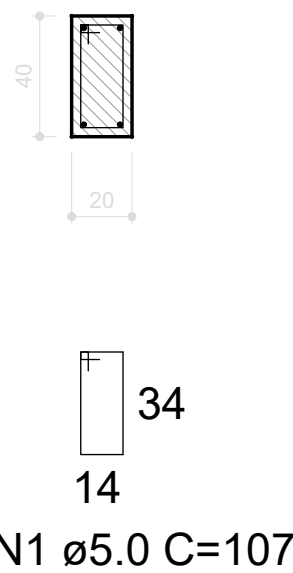


V6
ESC 1:30

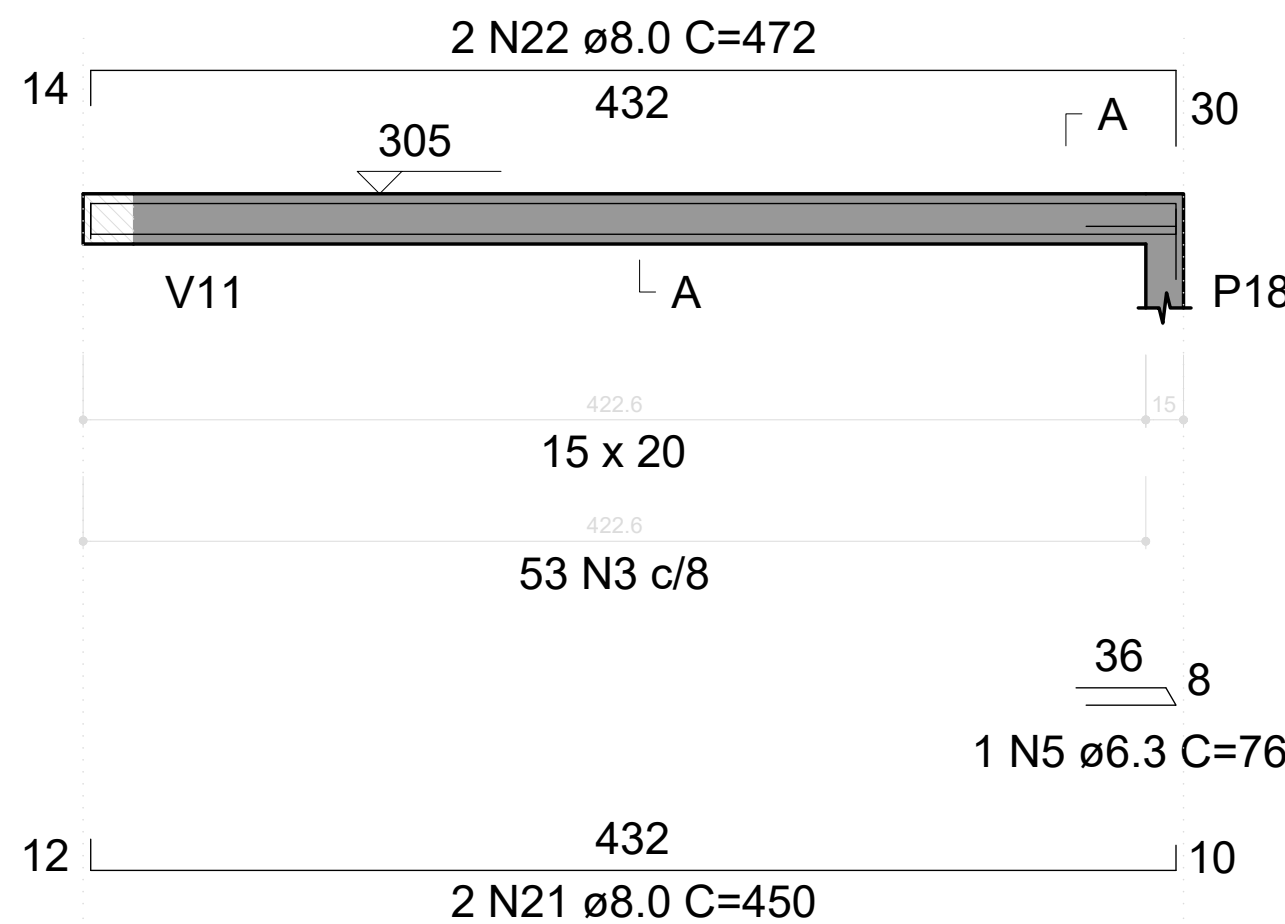


SEÇÃO A-A
ESC 1:25

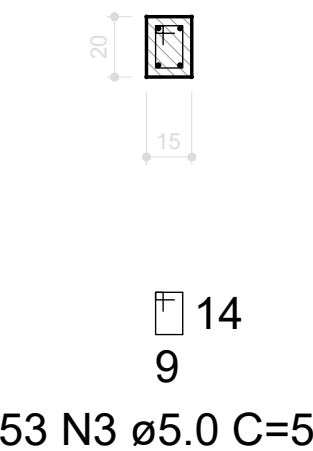

V7
ESC 1:30

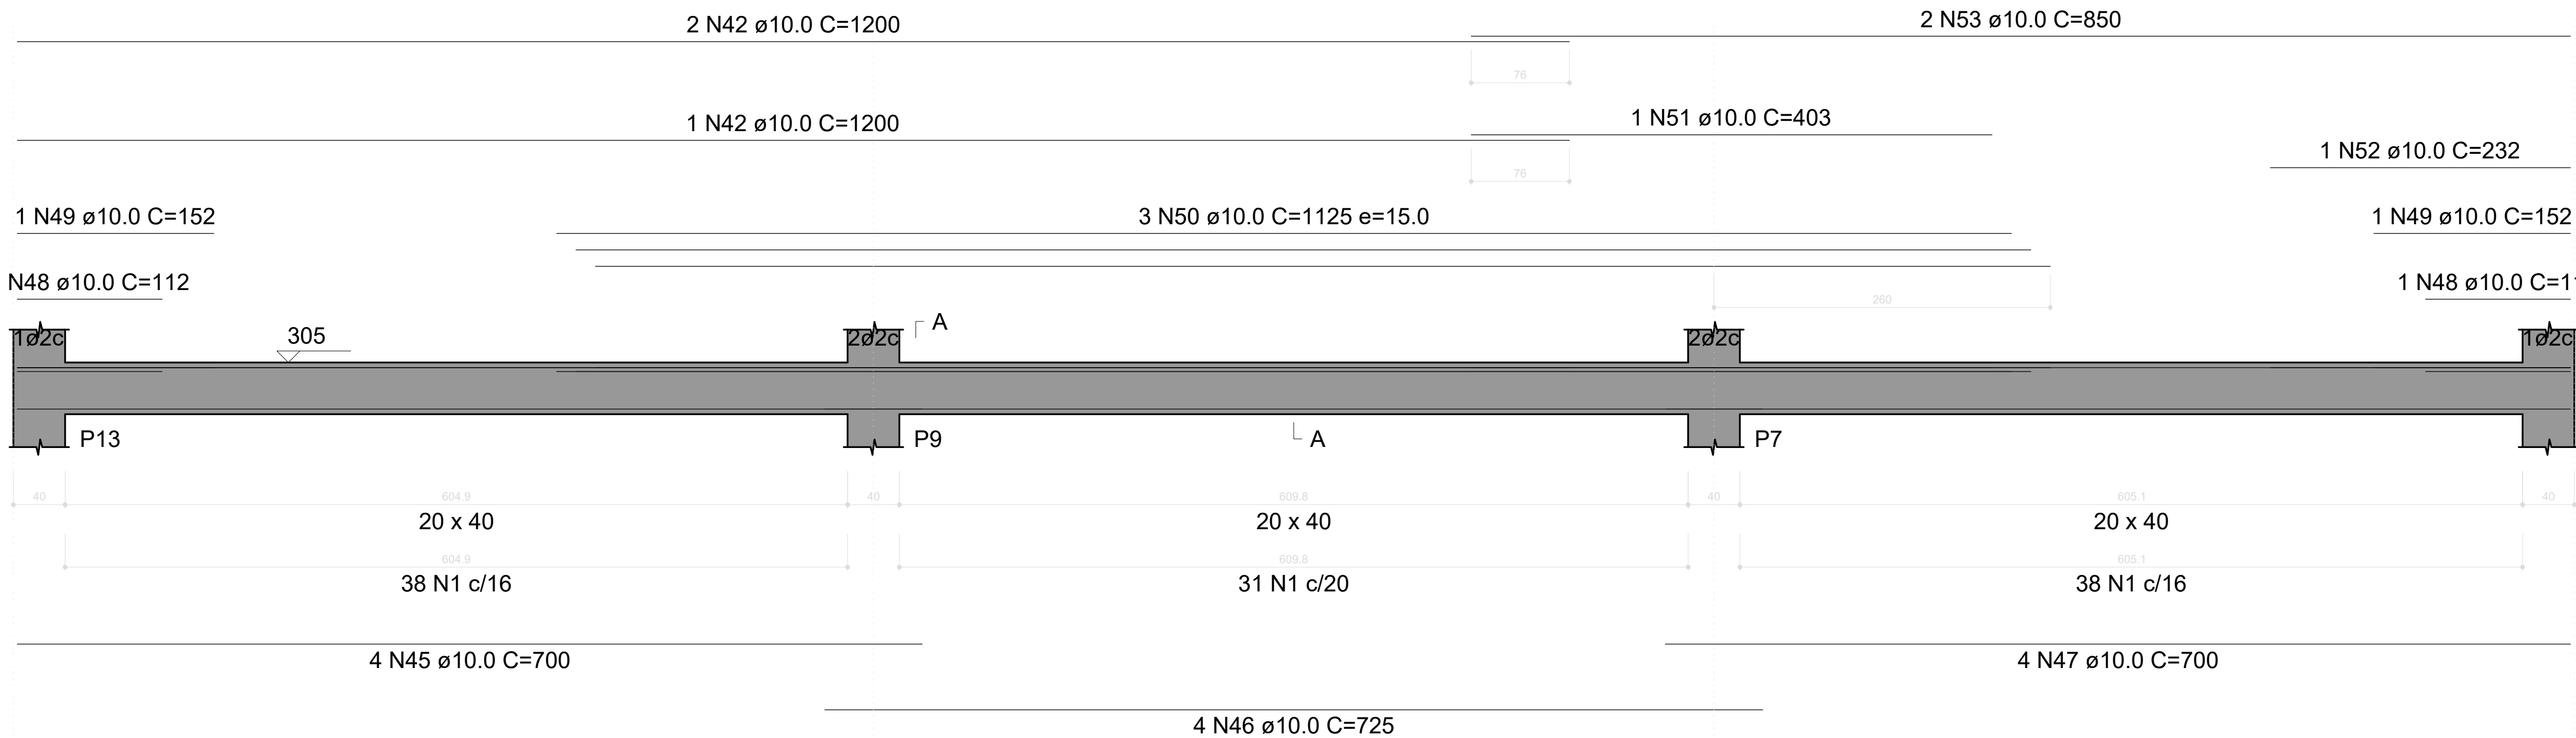

SEÇÃO A-A
ESC 1:25

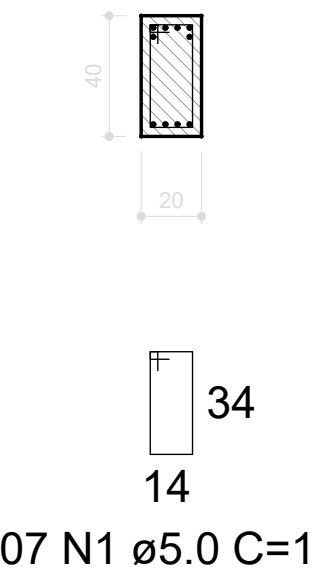

*OBS.: OS QUADROS RESUMO REFERENTES A
ESTA PRANCHA CONSTAM NA PRANCHA 18/26

PROPRIETÁRIO: PREFEITURA MUNICIPAL DE COREMAS - PB
LINCOLN CARTAXO DE
LIRA JUNIOR:06897861405
PROJETO: LINCOLN CARTAXO DE LIRA JÚNIOR CREA 160.814.689-8


CONSTRUÇÃO:

FOLHA
16/26
PROJETO: CONSTRUÇÃO DE GINÁSIO POLIESPORTIVO - ESTRUTURAL
CONVENIENTE: PREFEITURA MUNICIPAL DE COREMAS - PB
CONVENIADO: MUNICÍPIO DE COREMAS - PB
LOCALIDADE: COREMAS - PB


DESENHO	DATA	RESPONSÁVEL	RUBRICA	DADOS
CÓPIA	AGO/2025	LINCOLN CARTAXO		
VISTO				
ESCALAS	DESENHOS			CONVÊNIO
Indicada	- VIGAS DO PAVIMENTO LAJE (NÍVEL 305)			GOVERNO DO ESTADO
				ARQUIVO

Aprovações:

V3
ESC 1:30

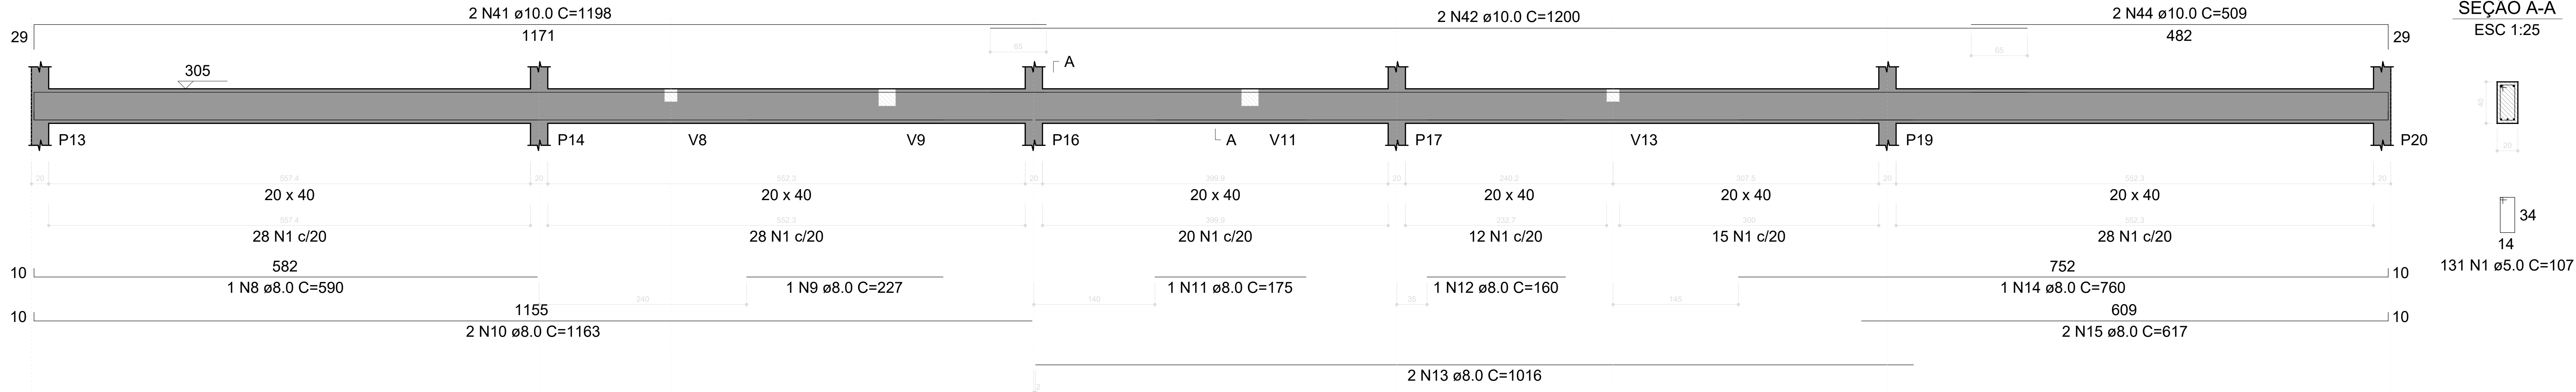


SEÇÃO A-A
ESC 1:25

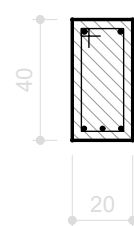


*OBS.: OS QUADROS RESUMO REFERENTES A ESTA PRANCHA CONSTAM NA PRANCHA 18/26

V2
ESC 1:30

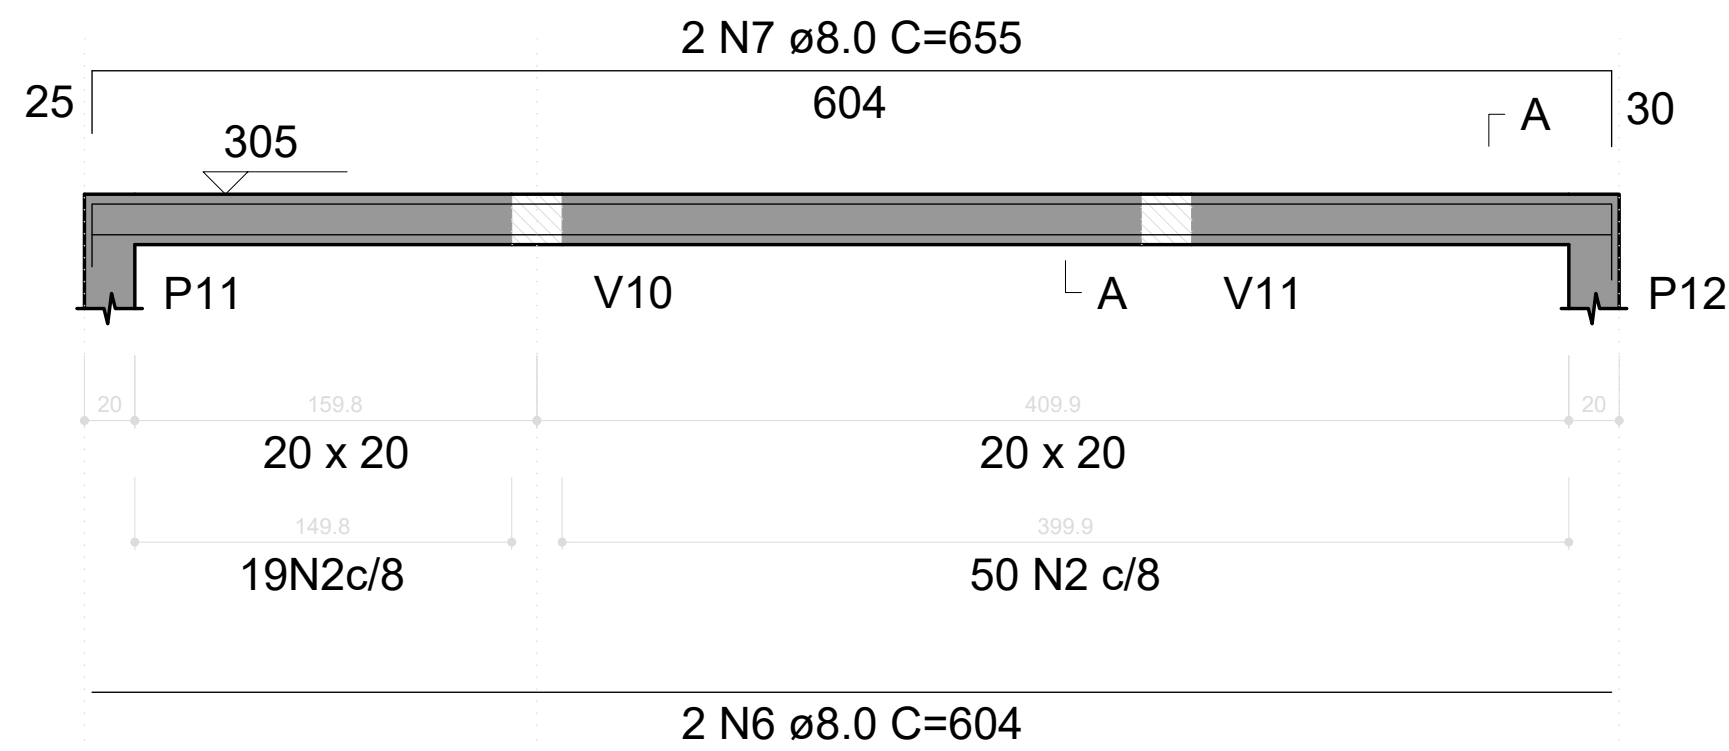


SEÇÃO A-A
ESC 1:25

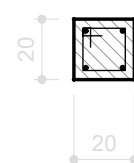


69 N2 ø5.0 C=67

V8
ESC 1:30

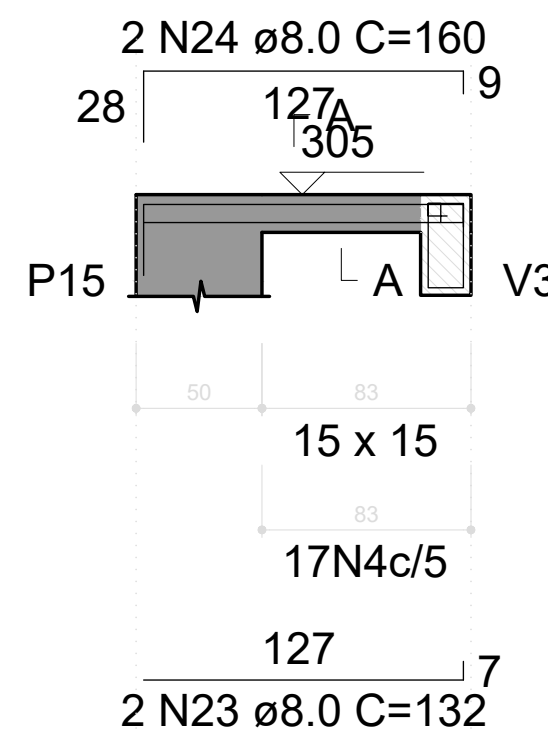

SEÇÃO A-A
ESC 1:25

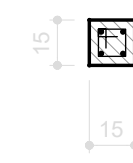


17 N4 ø5.0 C=47

SUSPENSÃO V3
ESC 1:25




1 N54 ø10.0 C=109

V10
ESC 1:30

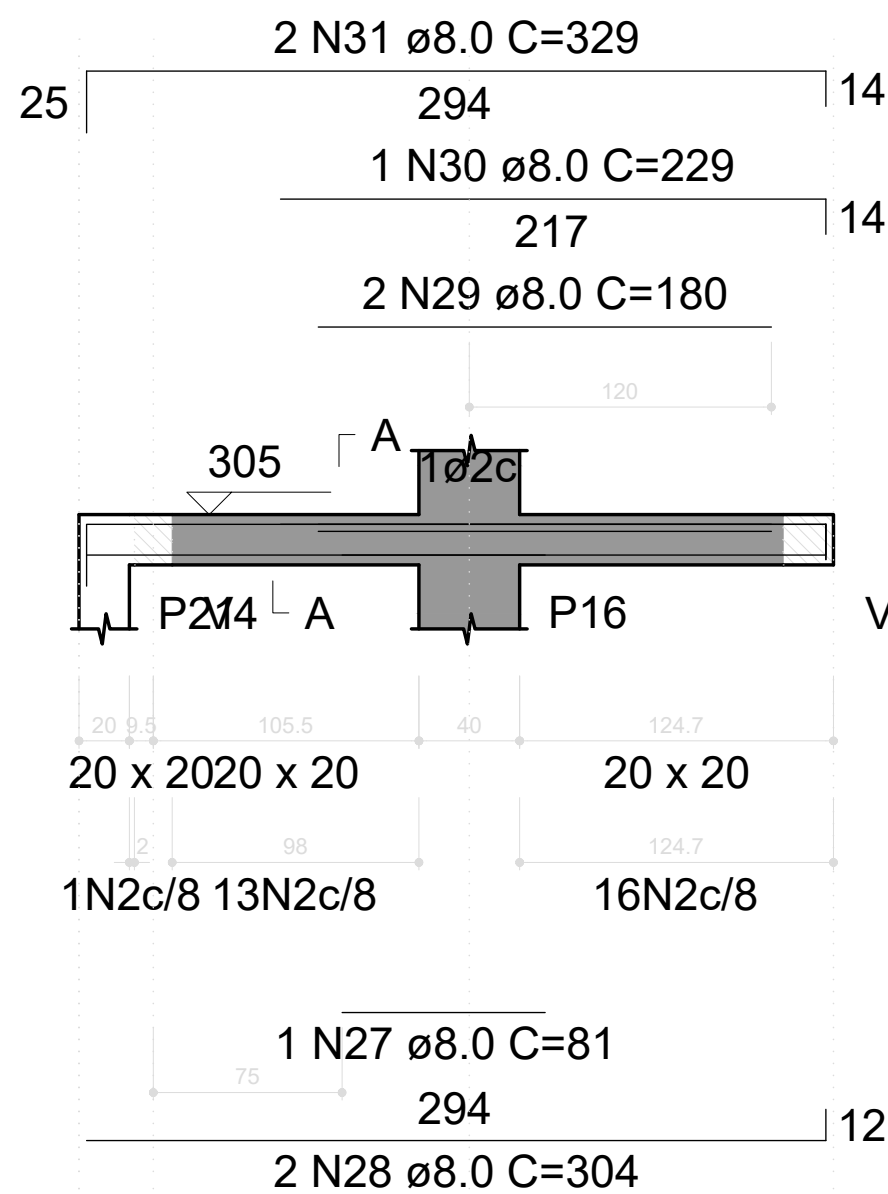


SEÇÃO A-A
ESC 1:25

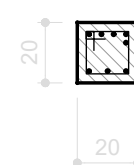


30 N2 ø5.0 C=67

V11
ESC 1:30

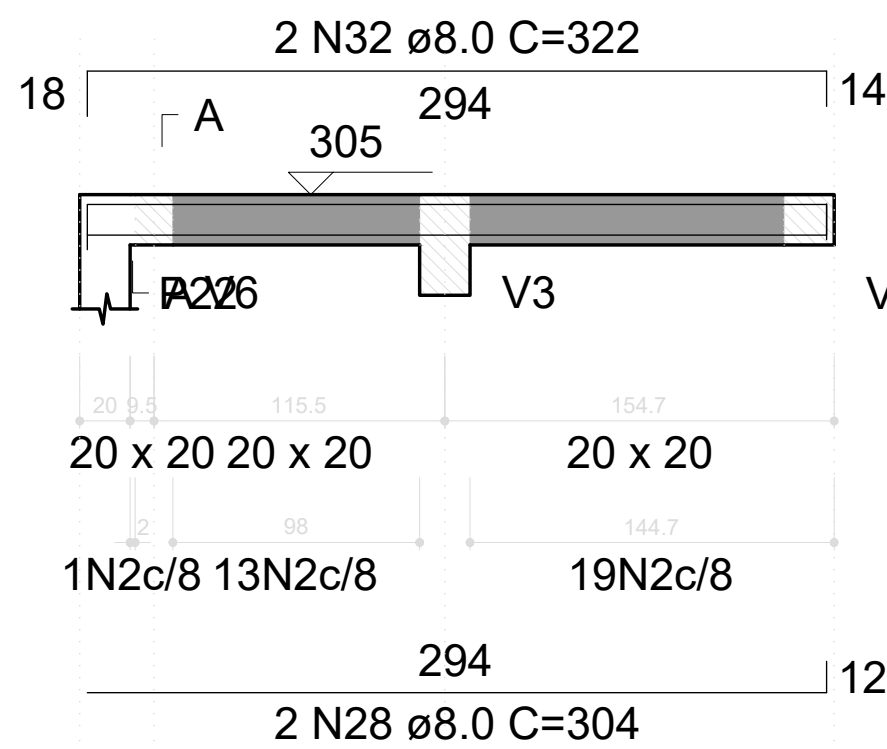


SEÇÃO A-A
ESC 1:25

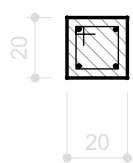


33 N2 ø5.0 C=67

V12
ESC 1:30

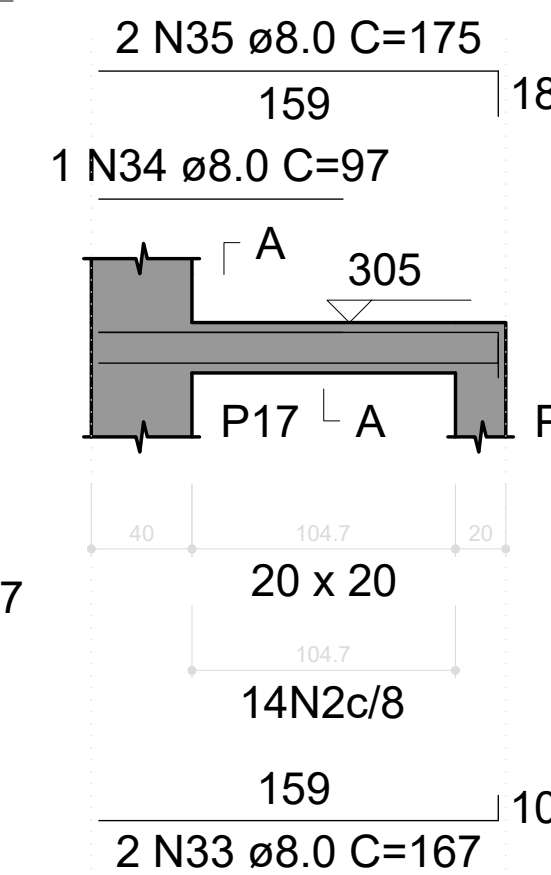

SEÇÃO A-A
ESC 1:25

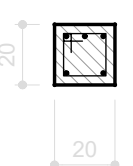

14 N2 ø5.0 C=67

PROPRIETÁRIO: PREFEITURA MUNICIPAL DE COREMAS - PB
LINCOLN CARTAXO DE LIRA
JUNIOR:06897861405
PROJETO: LINCOLN CARTAXO DE LIRA JÚNIOR CREA 160.814.689-8

CONSTRUÇÃO:

FOLHA 17/26
PROJETO: CONSTRUÇÃO DE GINÁSIO POLIESPORTIVO - ESTRUTURAL
CONVENIENTE: PREFEITURA MUNICIPAL DE COREMAS - PB
CONVENIADO: MUNICÍPIO DE COREMAS - PB
LOCALIDADE: COREMAS - PB


DESENHO	DATA	RESPONSÁVEL	RUBRICA	DADOS
CÓPIA	AGO/2025	LINCOLN CARTAXO		
VISTO				

ESCALAS	DESENHOS	CONVÊNIO
Indicada	- VIGAS DO PAVIMENTO LAJE (NÍVEL 305)	GOVERNO DO ESTADO
		ARQUIVO

Aprovações:


V4

ESC 1:30

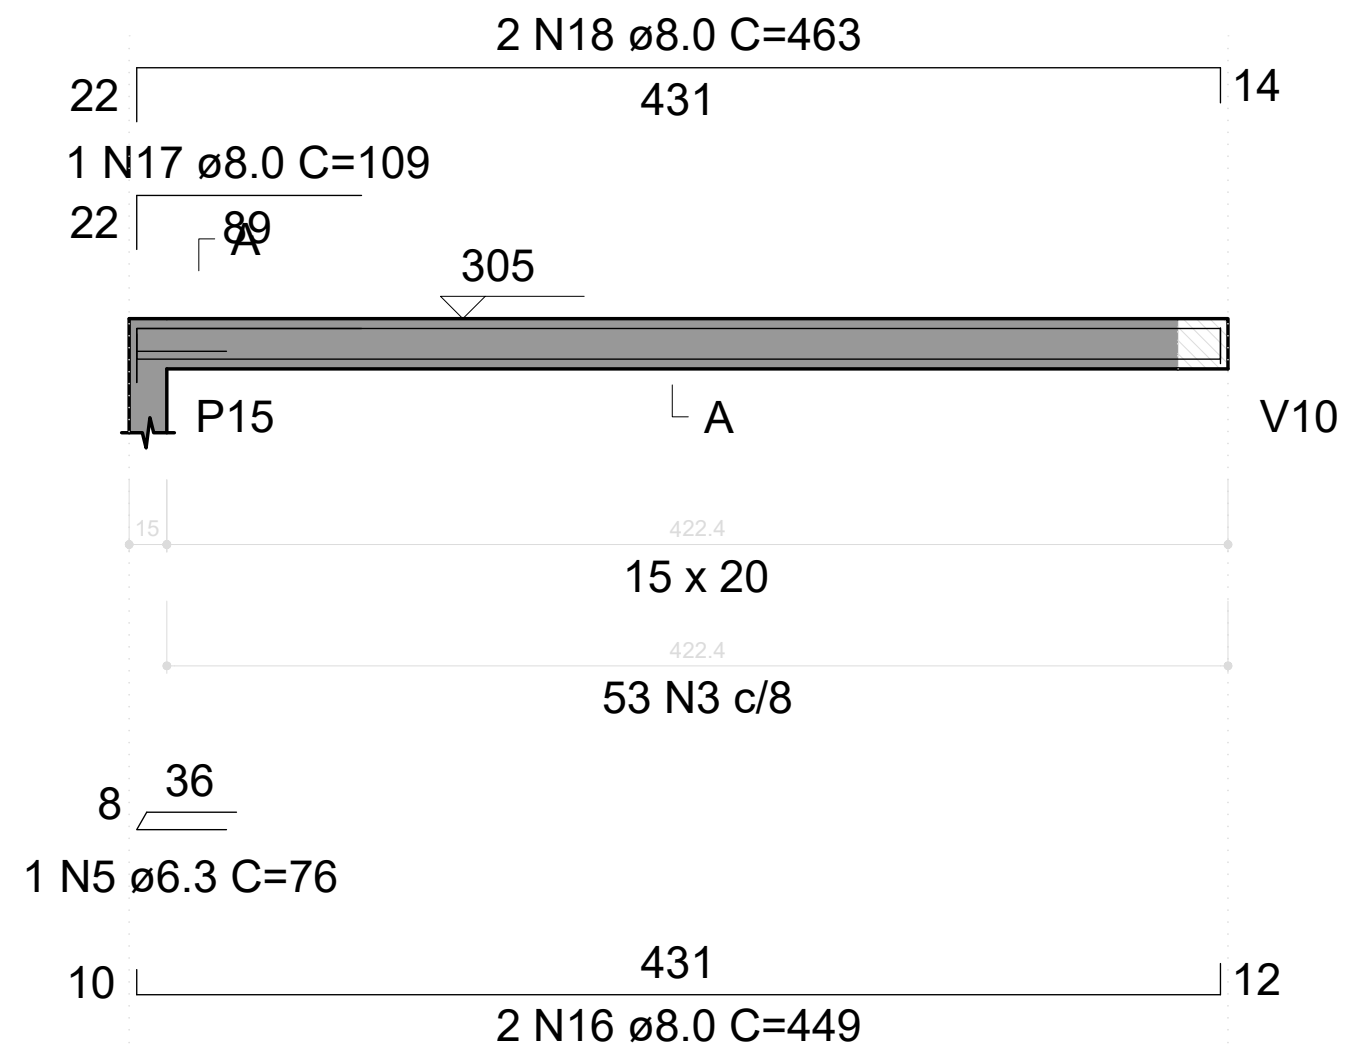


V14

ESC 1:30

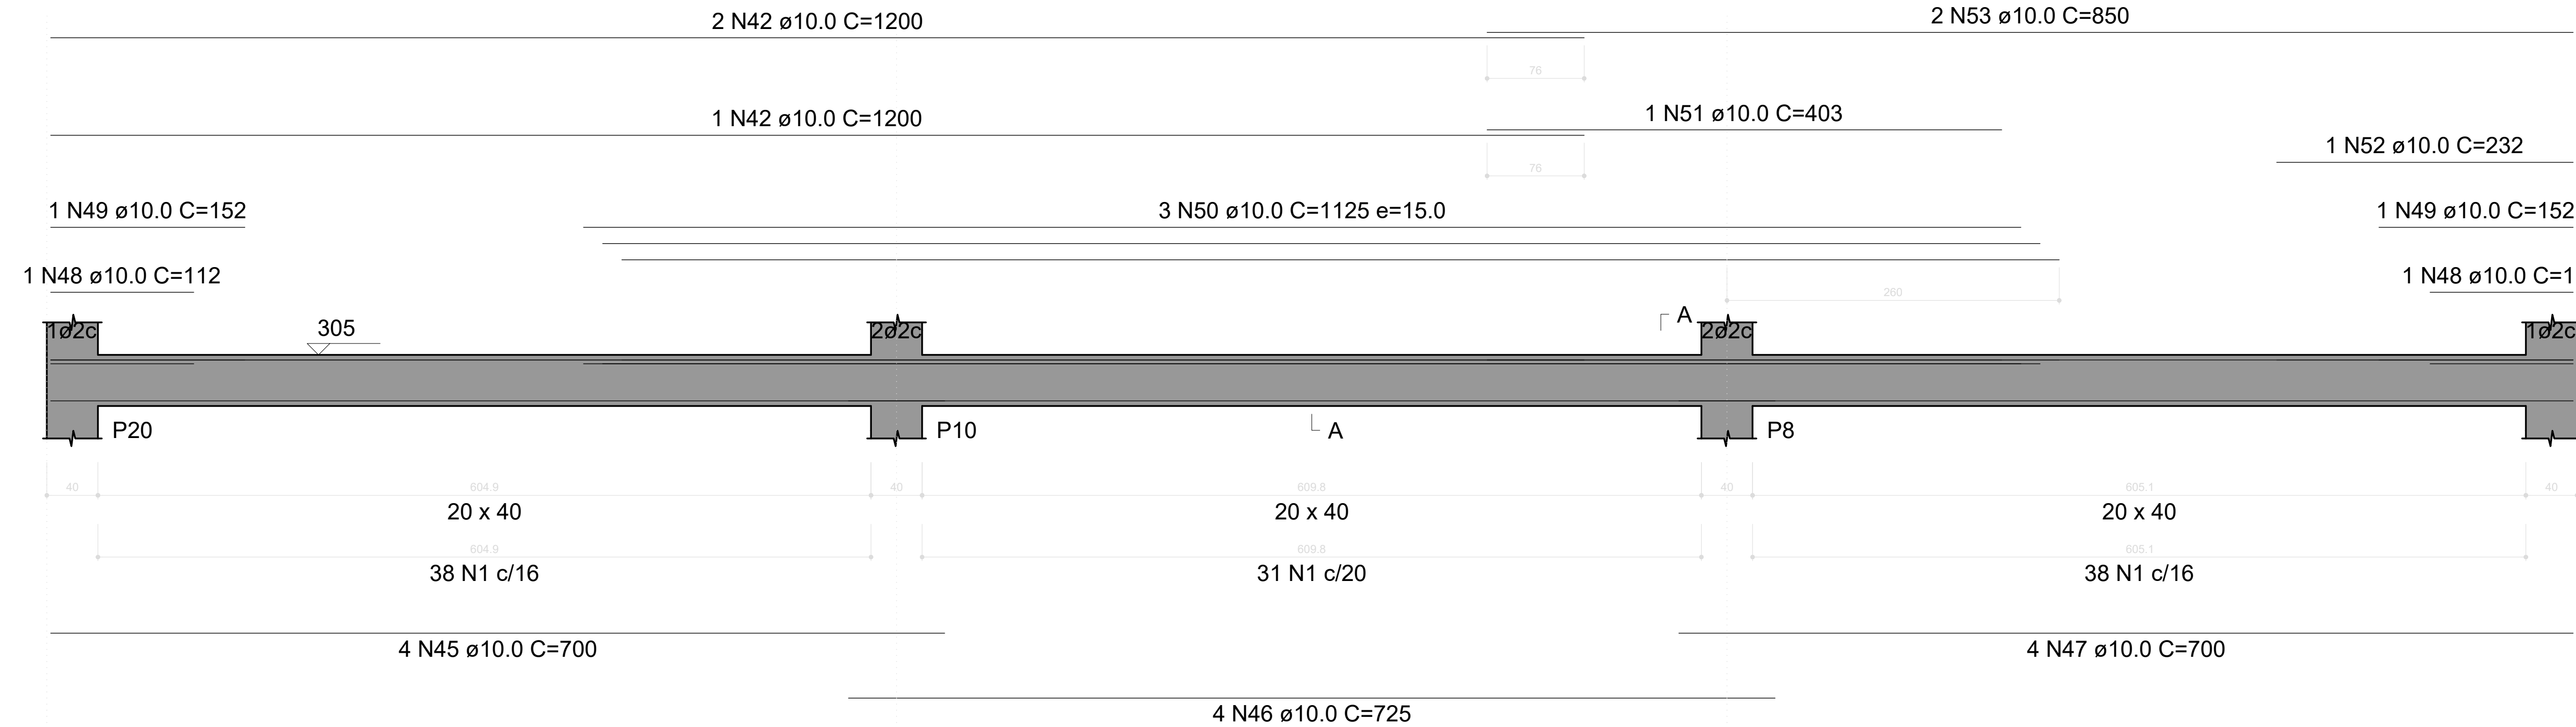


V5

ESC 1:30

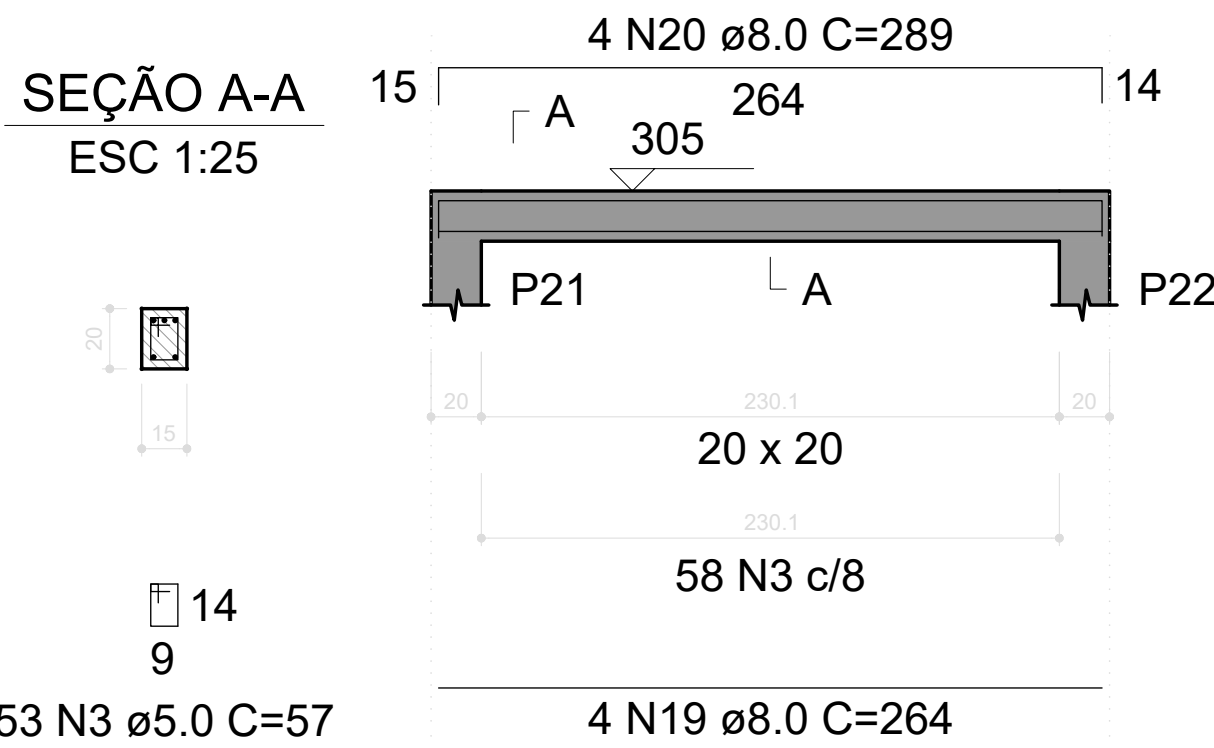


V9

ESC 1:30

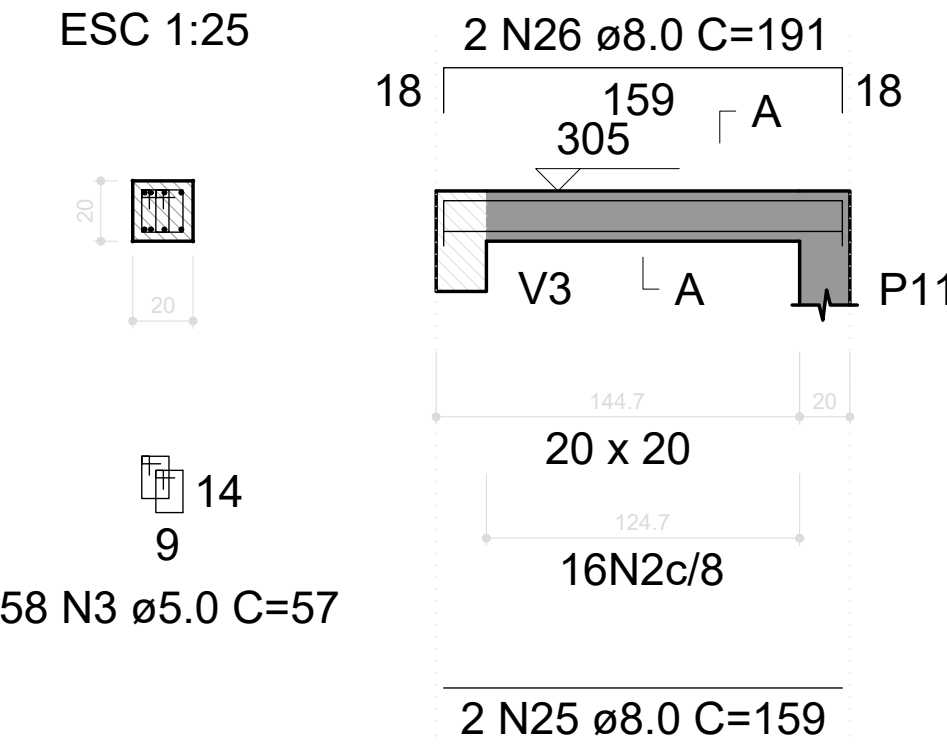


V13

ESC 1:30

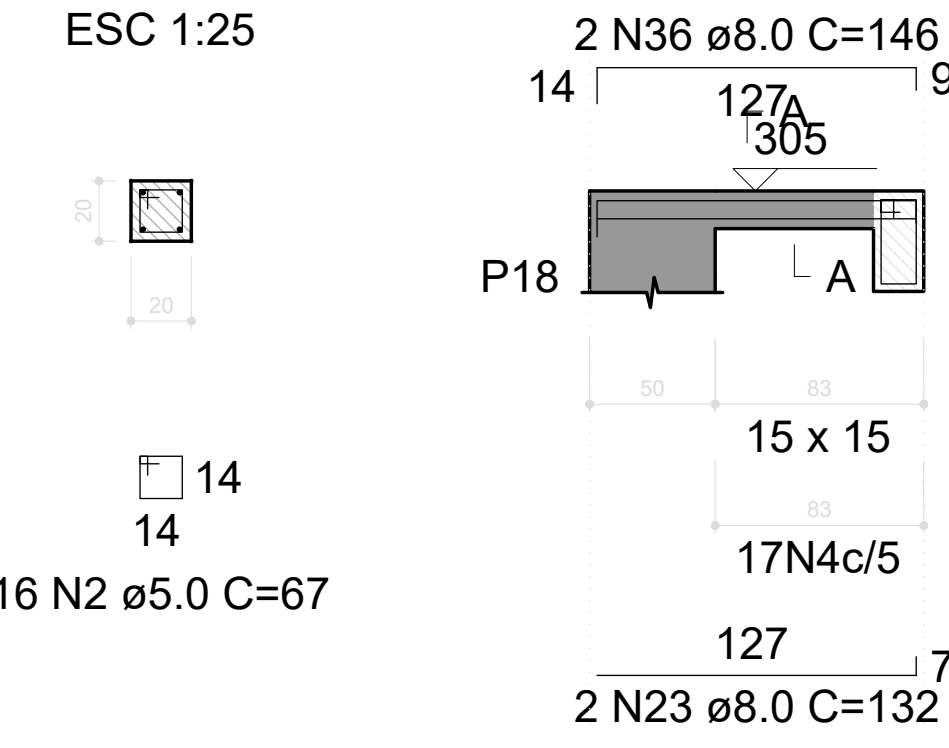


SEÇÃO A-A

ESC 1:25

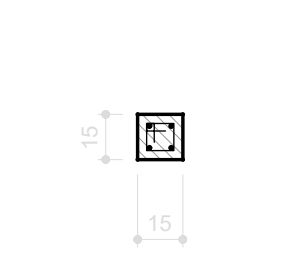

SUSPENSÃO V3

ESC 1:25

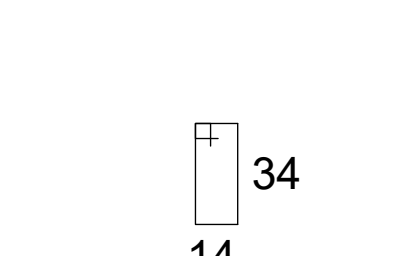


RELAÇÃO DO AÇO					
AÇO	N	DIAM (mm)	QUANT	C.UNIT (cm)	C.TOTAL (cm)
CA60	1	5.0	477	107	51039
	2	5.0	162	67	10854
	3	5.0	164	57	9348
	4	5.0	34	47	1598
	5	6.3	2	76	152
	6	8.0	2	604	1208
	7	8.0	2	655	1310
	8	8.0	1	590	590
	9	8.0	1	227	227
	10	8.0	2	1163	2326
CA50	11	8.0	1	175	175
	12	8.0	1	160	160
	13	8.0	2	1016	2032
	14	8.0	1	760	760
	15	8.0	2	617	1234
	16	8.0	2	449	898
	17	8.0	1	109	109
	18	8.0	2	463	926
	19	8.0	4	264	1056
	20	8.0	4	289	1156
	21	8.0	2	450	900
	22	8.0	2	472	944
	23	8.0	4	132	528
	24	8.0	2	160	320
	25	8.0	2	159	318
	26	8.0	2	191	382
	27	8.0	1	81	81
	28	8.0	4	304	1216
	29	8.0	2	180	360
	30	8.0	1	229	229
	31	8.0	2	329	658
	32	8.0	2	322	644
	33	8.0	2	167	334
	34	8.0	1	97	97
	35	8.0	2	175	350
	36	8.0	2	146	292
	37	10.0	2	1084	2168
	38	10.0	2	178	356
	39	10.0	2	1025	2050
	40	10.0	2	590	1180
	41	10.0	4	1198	4792
	42	10.0	10	1200	12000
	43	10.0	2	495	992
	44	10.0	2	509	1018
	45	10.0	8	700	5600
	46	10.0	8	725	5800
	47	10.0	8	700	5600
	48	10.0	4	112	448
	49	10.0	4	152	608
	50	10.0	6	1125	6750
	51	10.0	2	403	806
	52	10.0	2	232	464
	53	10.0	4	850	3400
	54	10.0	2	109	218

RESUMO DO AÇO			
AÇO	DIAM (mm)	C.TOTAL (m)	PESO + 10% (kg)
CA50	6.3	1.5	0.4
	8.0	218.2	94.7
	10.0	542.5	367.9
CA60	5.0	728.4	123.5
PESO TOTAL (kg)			
CA50	463		
CA60	123.5		
Volume de concreto (C-25) = 8.58 m³			
Área de forma = 111.05 m²			

SEÇÃO A-A

ESC 1:25

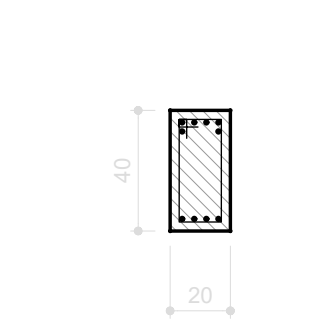

107 N1 ø5.0 C=107

PROPRIETÁRIO: PREFEITURA MUNICIPAL DE COREMAS - PB

LINCOLN CARTAXO DE LIRA JUNIOR:06897861405

PROJETO: LINCOLN CARTAXO DE LIRA JÚNIOR CREA 160.814.689-8

CONSTRUÇÃO:

FOLHA 18/26

PROJETO: CONSTRUÇÃO DE GINÁSIO POLIESPORTIVO - ESTRUTURAL

CONVENIENTE: PREFEITURA MUNICIPAL DE COREMAS - PB

CONVENIADO: MUNICÍPIO DE COREMAS - PB

LOCALIDADE: COREMAS - PB

DATA	RESPONSÁVEL	RUBRICA	DADOS
AGO/2025	LINCOLN CARTAXO		
CÓPIA			
VISTO			
ESCALAS	DESENHOS	CONVÊNIO	
Indicada	- VIGAS DO PAVIMENTO LAJE (NÍVEL 305)	GOVERNO DO ESTADO	
		ARQUIVO	

Aprovações:

LAJE - L3

SEÇÃO
ESC 1:20

20

40

VISTA H


34

295

VISTA B


14

2 N1 ø5.0 C=107

 

47

10
4 N11 ø12.5 C=57

 

10

2 N1 ø5

*OBS.: OS QUADROS RESUMO REFERENTES A
ESTA PRANCHA CONSTAM NA PRANCHA 21/26

PROPRIETÁRIO: PREFEITURA MUNICIPAL DE COREMAS - PB

LINCOLN CARTAXO DE LIRA JUNIOR:06897861405

Assinado de forma digital por LINCOLN CARTAXO DE LIRA JUNIOR:06897861405
Dados: 2025.08.08 12:25:39 -03'00'

PROJETO: LINCOLN CARTAXO DE LIRA JÚNIOR CREA 160.814.689-8

CONSTRUÇÃO:

FOLHA 19/26	PROJETO:	CONSTRUÇÃO DE GINÁSIO POLIESPORTIVO - ESTRUTURAL		
	CONVENIENTE:	PREFEITURA MUNICIPAL DE COREMAS - PB		
	CONVENIADO:	MUNICÍPIO DE COREMAS - PB		
	LOCALIDADE:	COREMAS - PB		
DESENHO	DATA	RESPONSÁVEL	RUBRICA	DADOS
CÓPIA				
VISTO				
ESCALAS	DESENHOS			CONVÊNIO
				GOVERNO DO ESTADO
	Indicada			ARQUIVO

Aprovações:

P2=P3=P4

VISTA H
ESC 1:1

VISTA B
ESC 1:1

*OBS.: OS QUADROS RESUMO REFERENTES A
ESTA PRANCHA CONSTAM NA PRANCHA 21/26

LAJE - L3

305

SEÇÃO

ESC 1:20

20

40

VISTA H

VISTA B

34


14

295

N2


2 N1 ø5.0 C=107

2 N2 ø5.0 C=29

 

38

10
6 N6 ø10.0 C=48

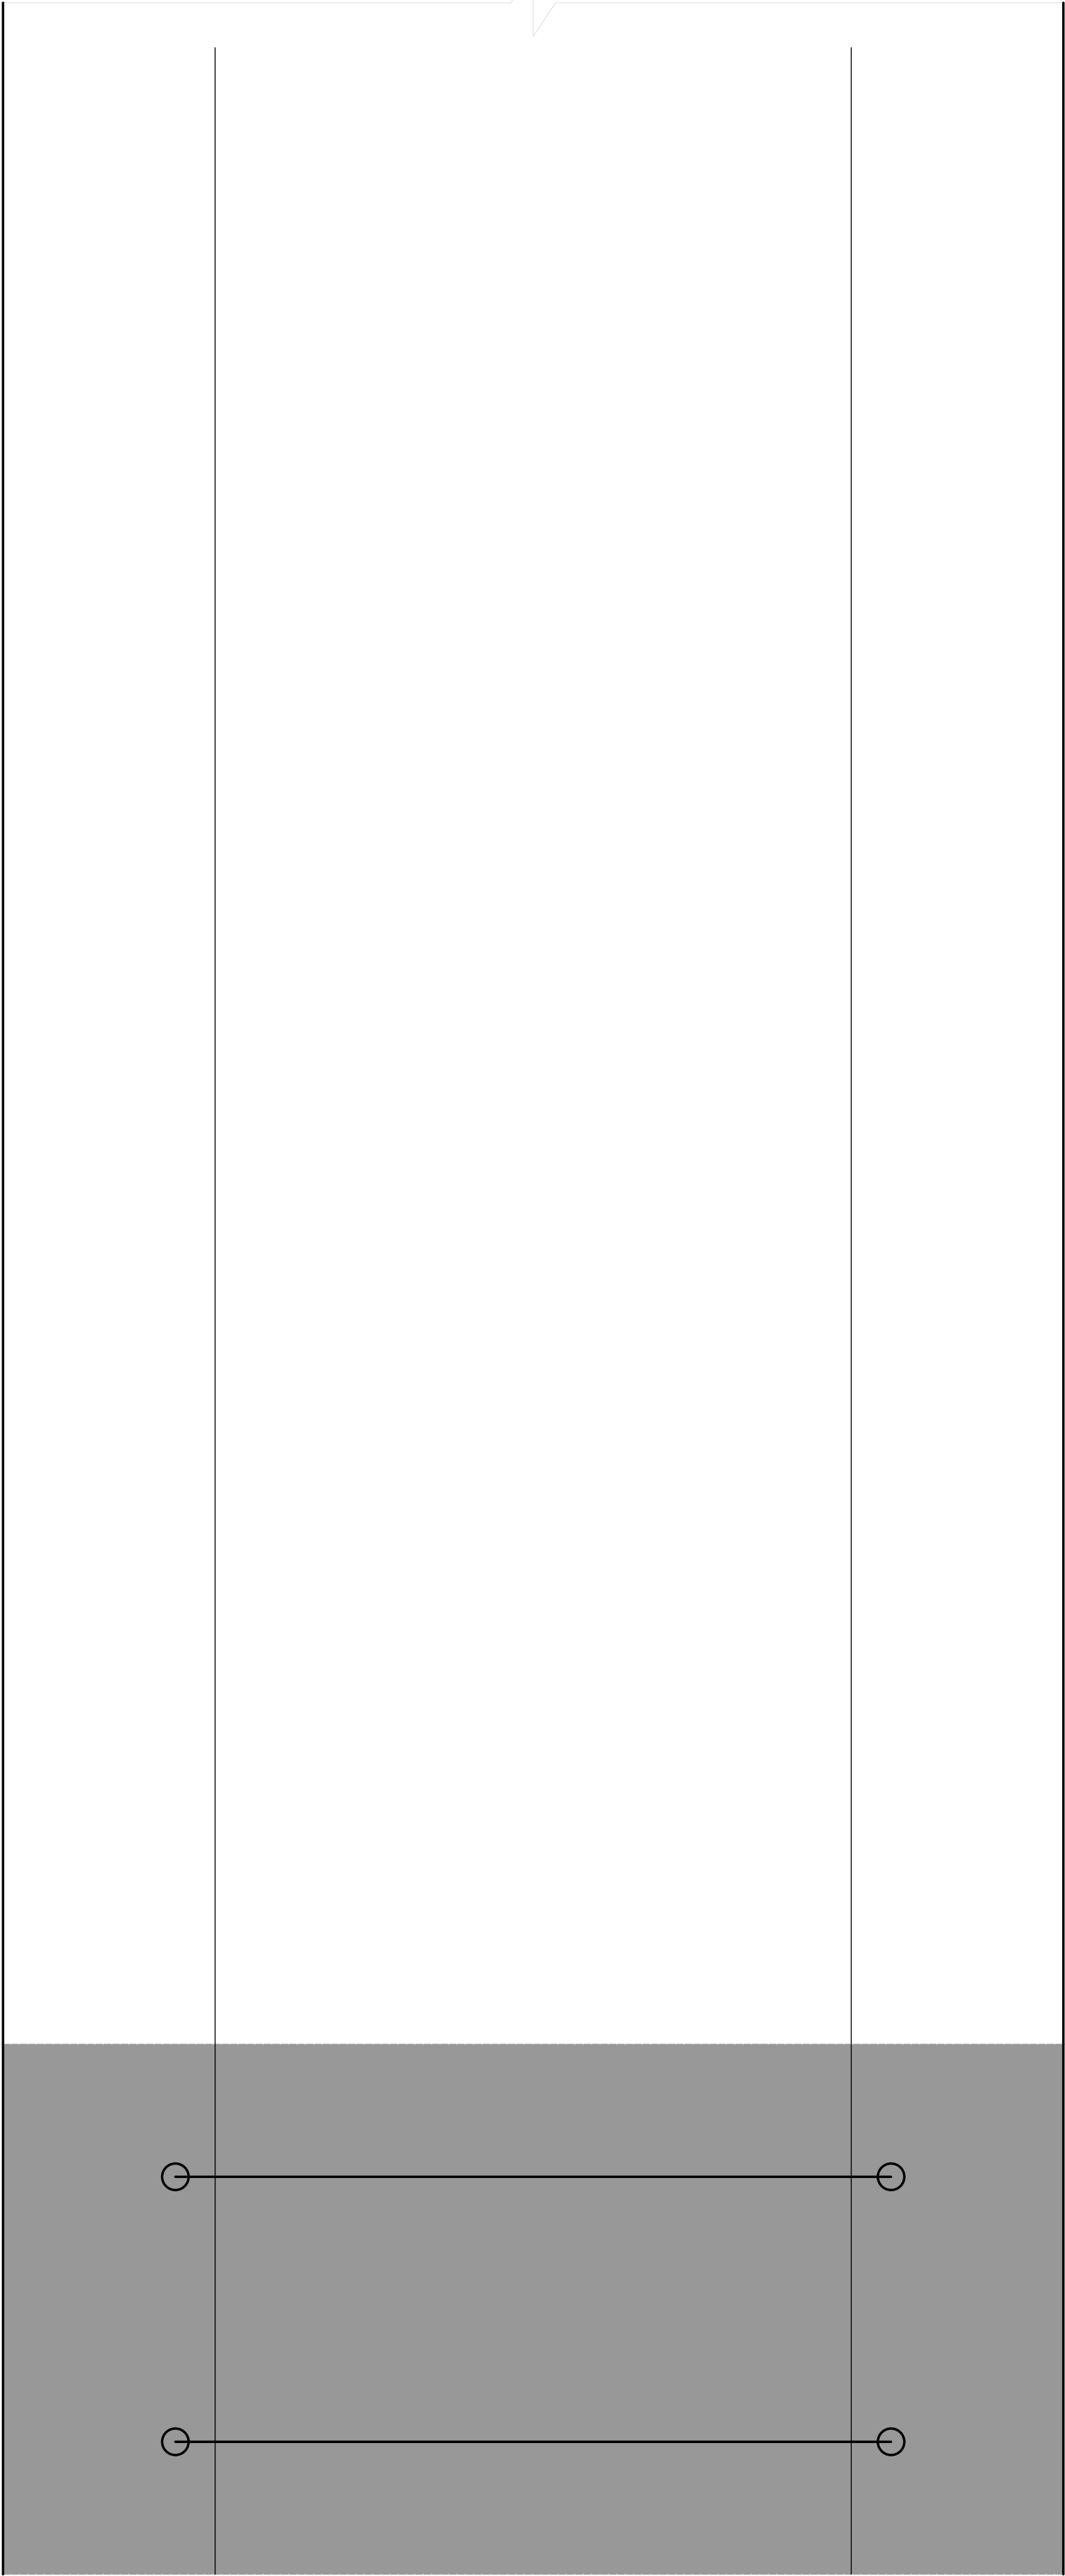

10
2 N1 ø5

PROPRIETÁRIO: PREFEITURA MUNICIPAL DE COREMAS - PB
LINCOLN CARTAXO DE LIRA JÚNIOR:06897861405
Assinado de forma digital por LINCOLN CARTAXO DE LIRA JÚNIOR:06897861405
Dados: 2025.08.08 12:26:58 -03'00'

PROJETO: LINCOLN CARTAXO DE LIRA JÚNIOR CREA 160.814.689-8


CONSTRUÇÃO:

FOLHA
20/26
PROJETO: CONSTRUÇÃO DE GINÁSIO POLIESPORTIVO - ESTRUTURAL
CONVENIENTE: PREFEITURA MUNICIPAL DE COREMAS - PB
CONVENIADO: MUNICÍPIO DE COREMAS - PB
LOCALIDADE: COREMAS - PB


DESENHO	DATA	RESPONSÁVEL	RUBRICA	DADOS
CÓPIA	AGO/2025	LINCOLN CARTAXO		
VISTO				
ESCALAS	DESENHOS			CONVÊNIO
Indicada	- ARMADURAS DOS PILARES PAV. LAJE (NÍVEL 305)			GOVERNO DO ESTADO
				ARQUIVO

Aprovações:

P11=P12=P21=P22

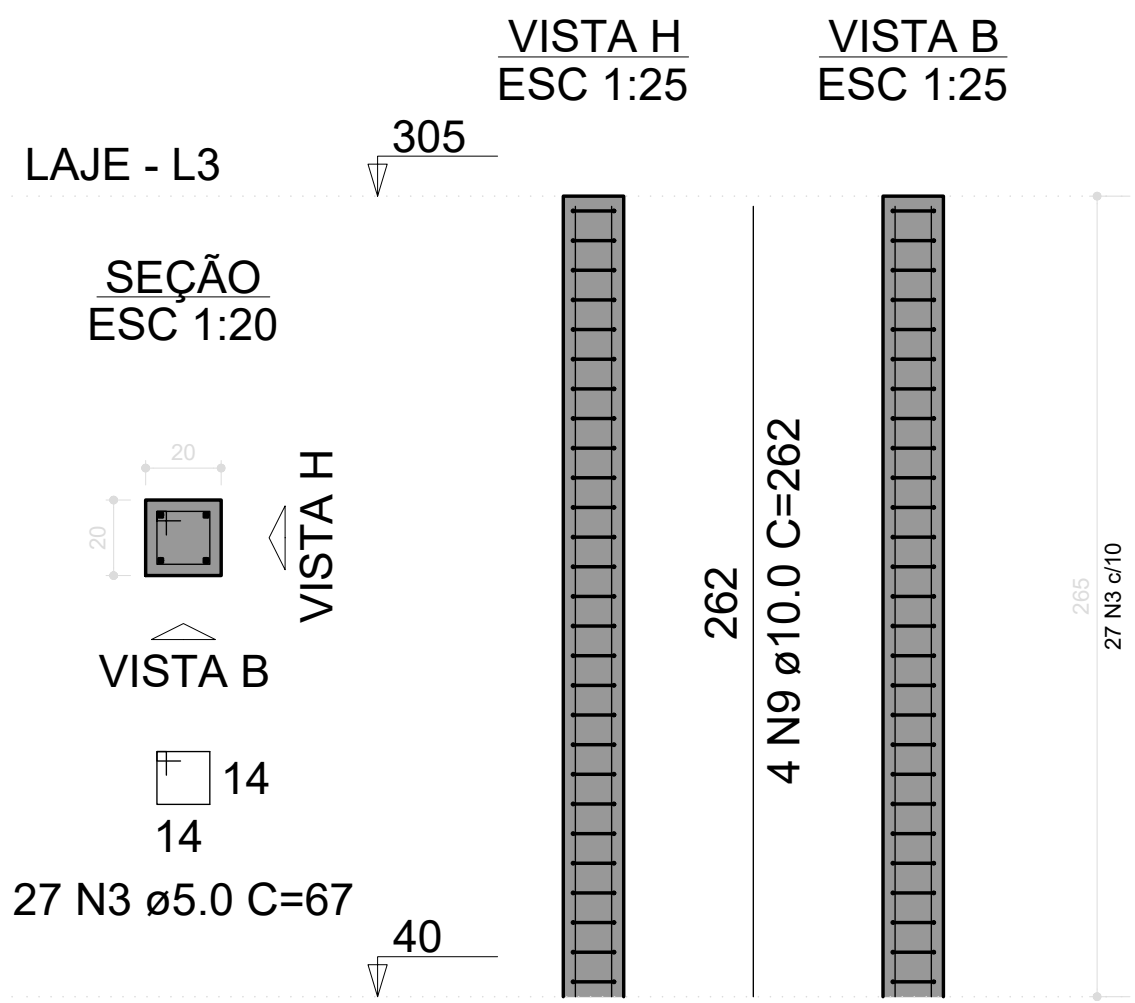

P15=P18

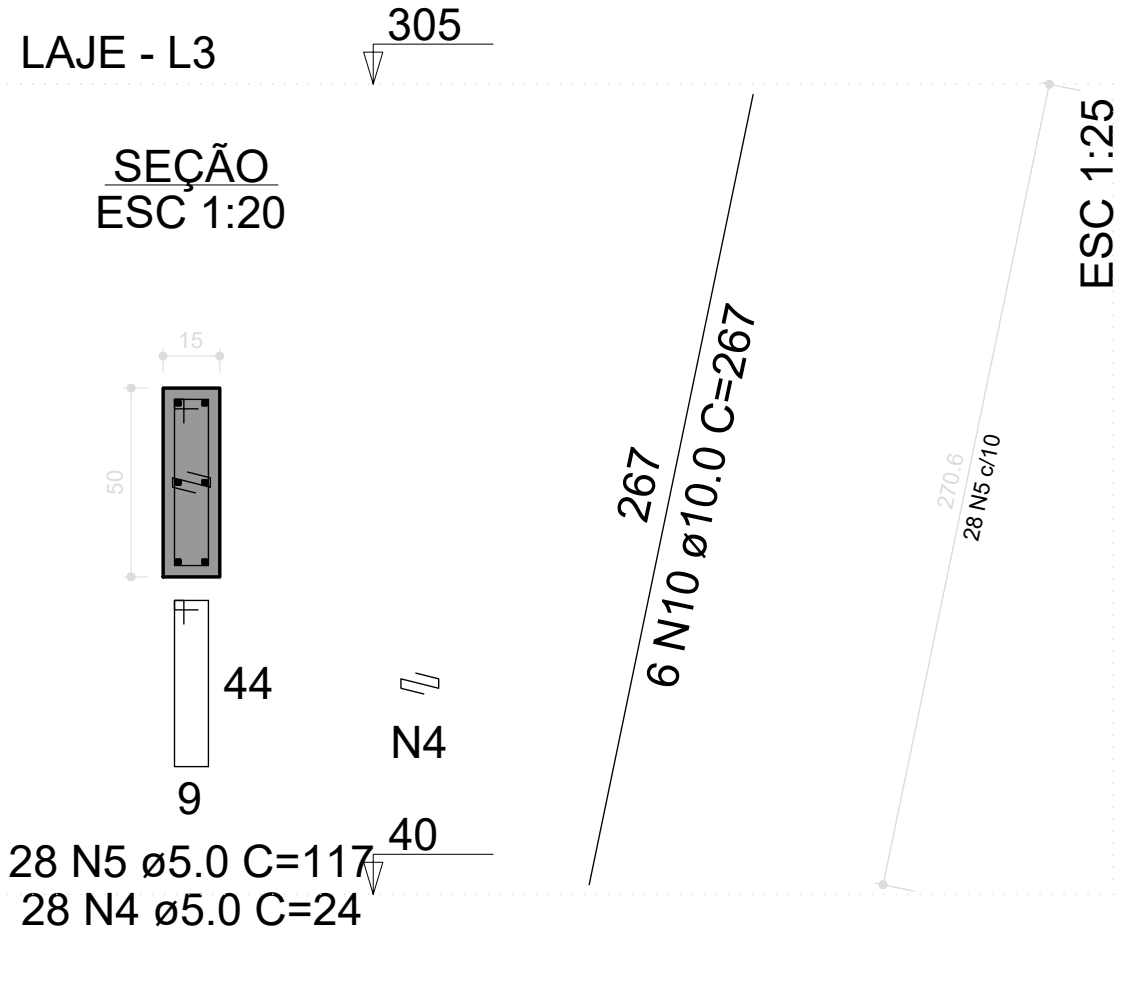


RELAÇÃO DO AÇO					
P1 3xP6 2xP15	3xP2 4xP7	5xP5 4xP11			
AÇO	N	DIAM (mm)	QUANT	C.UNIT (cm)	C.TOTAL (cm)
CA60	1	5.0	305	107	32635
	2	5.0	573	29	16617
	3	5.0	108	67	7236
	4	5.0	56	24	1344
	5	5.0	56	117	6552
	6	10.0	18	48	864
	7	10.0	30	303	9090
	8	10.0	6	75	450
	9	10.0	96	262	25152
	10	10.0	12	267	3204
	11	12.5	4	57	228
	12	12.5	12	312	3744
	13	16.0	40	121	4840


RESUMO DO AÇO			
AÇO	DIAM (mm)	C.TOTAL (m)	PESO + 10% (kg)
CA50	10.0	387.6	262.9
	12.5	39.7	42.1
	16.0	48.4	84
CA60	5.0	643.8	109.2
PESO TOTAL (kg)			
CA50	389		
CA60	109.2		

Volume de concreto (C-25) = 3.41 m³
Área de forma = 54.16 m²


P5=P14=P16=P17=P19

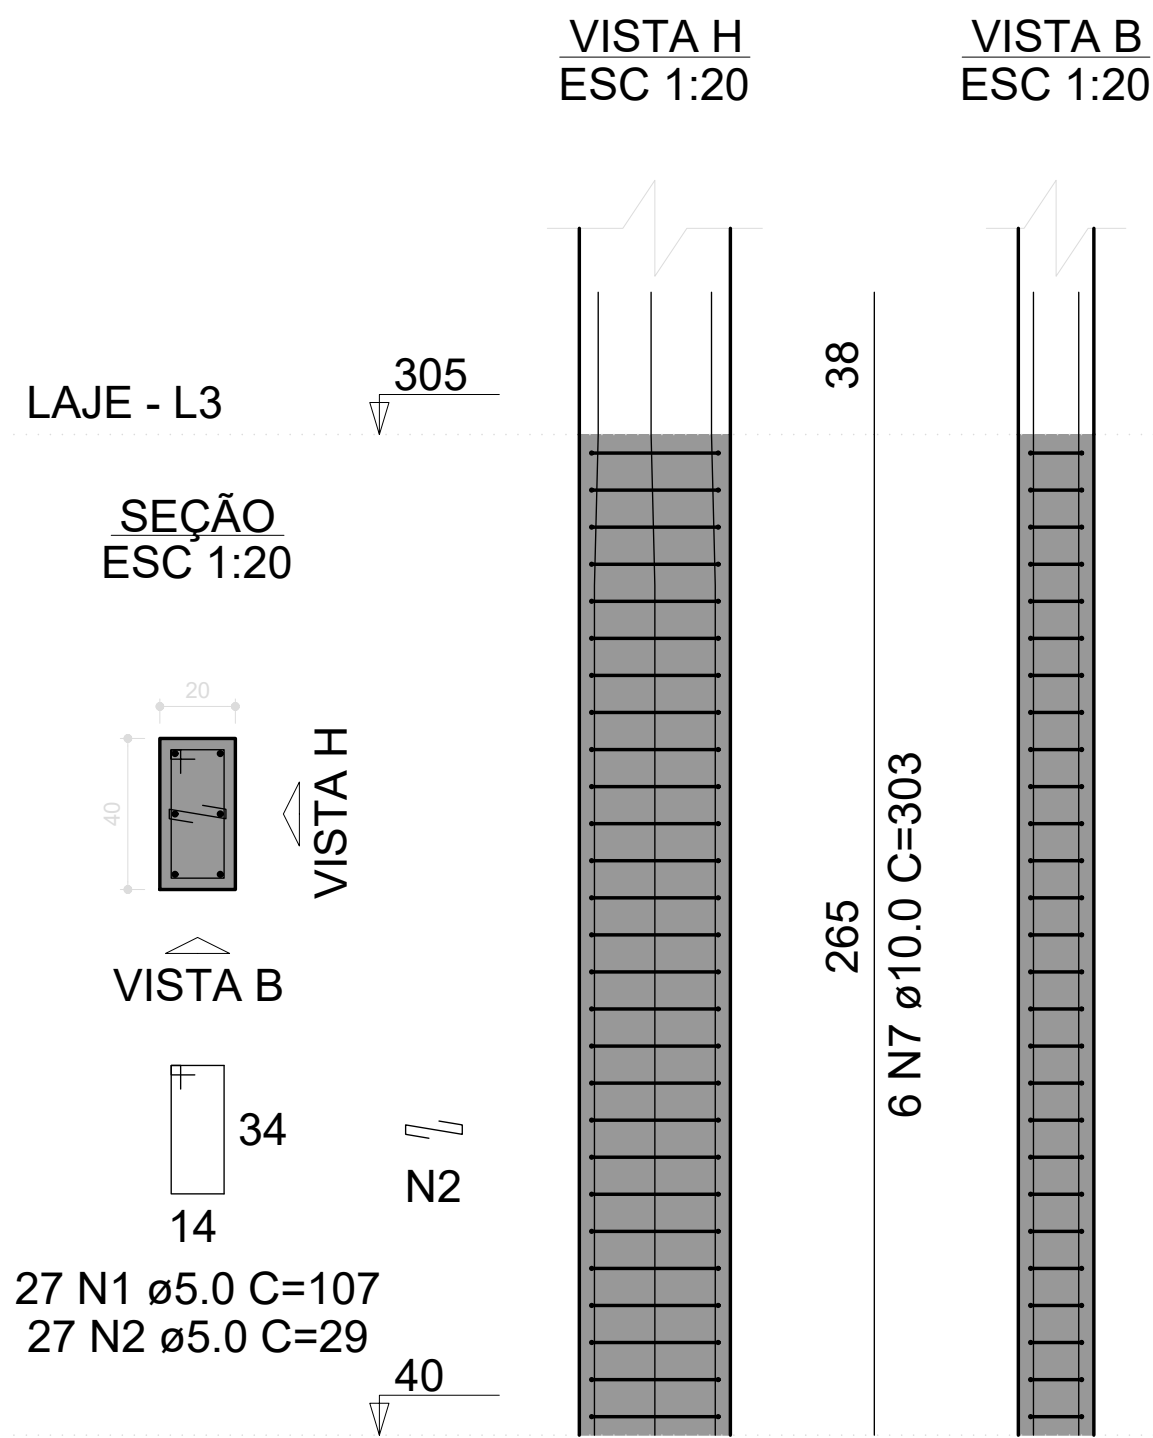

P6=P13=P20

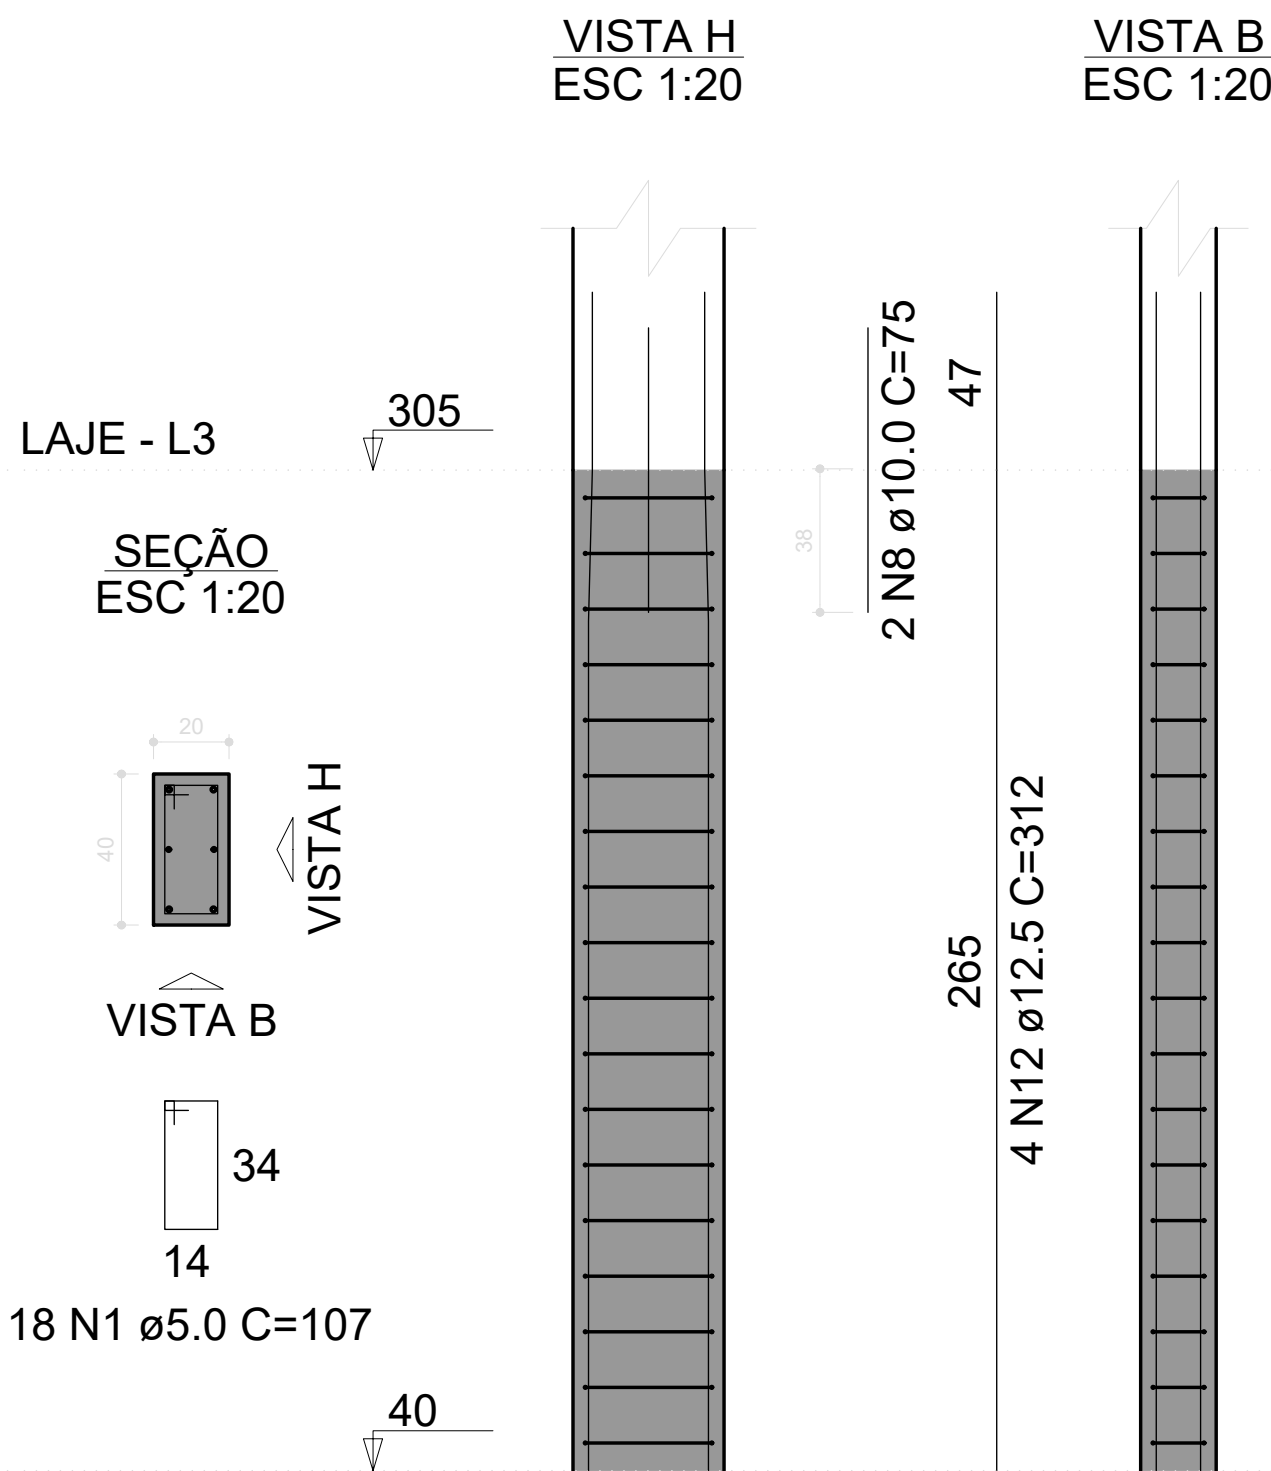

P7=P8=P9=P10

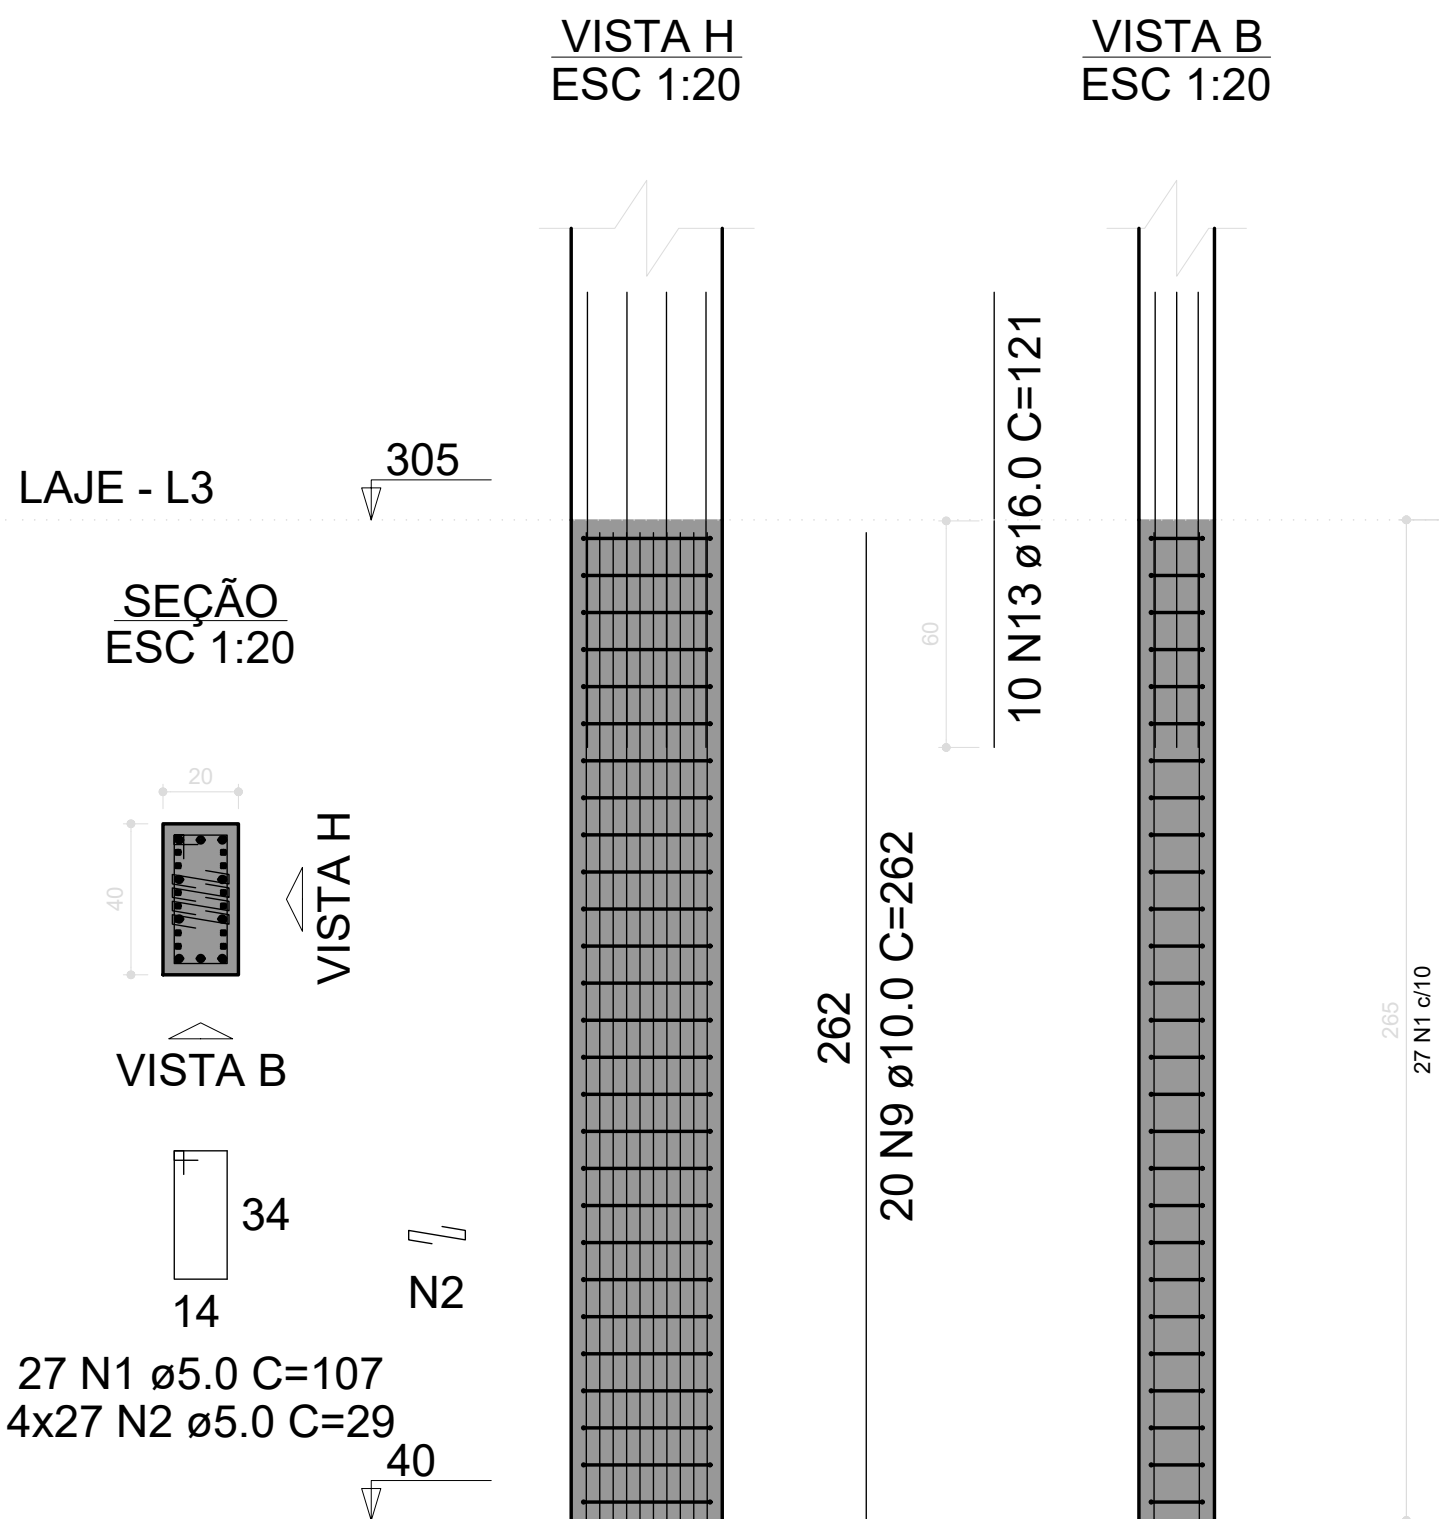

PROPRIETÁRIO: PREFEITURA MUNICIPAL DE COREMAS - PB

LINCOLN CARTAXO DE LIRA JUNIOR:06897861405

Assinado de forma digital por LINCOLN CARTAXO DE LIRA JUNIOR:06897861405
Dados: 2025.08.08 12:26:28 -03'00'

PROJETO: LINCOLN CARTAXO DE LIRA JÚNIOR CREA 160.814.689-8

CONSTRUÇÃO:

FOLHA
21/26

PROJETO: CONSTRUÇÃO DE GINÁSIO POLIESPORTIVO - ESTRUTURAL

CONVENIENTE: PREFEITURA MUNICIPAL DE COREMAS - PB

CONVENIADO: MUNICÍPIO DE COREMAS - PB

LOCALIDADE: COREMAS - PB





DESENHO	DATA	RESPONSÁVEL	RUBRICA	DADOS
CÓPIA	AGO/2025	LINCOLN CARTAXO		
VISTO				

ESCALAS	DESENHOS	CONVÊNIO
Indicada	- ARMADURAS DOS PILARES PAV. LAJE (NÍVEL 305)	GOVERNO DO ESTADO
		ARQUIVO


Aprovações:

LCL PROJETOS


Av. Gov. Flávio Ribeiro Coutinho, 500, sl. 601
Jardim Oceania, 58037-005 - João Pessoa (PB)
Tel +55 (83) 99924.4447
e-mail: contato@lclprojetos.com

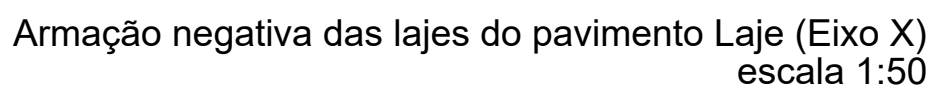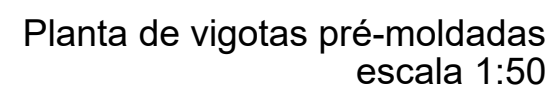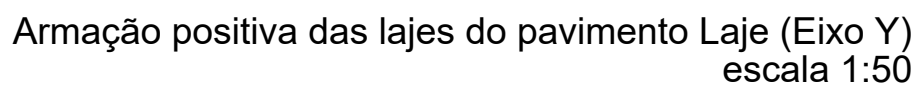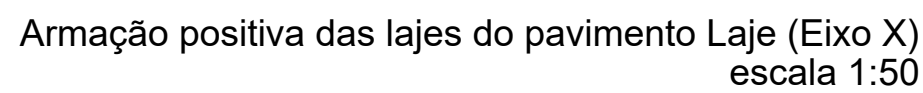

DETALHE DA ARMADURA DE SUPERIOR DE CONTINUIDADE DA LAJE
E MONTAGEM DA ARMADURA DE DISTRIBUIÇÃO

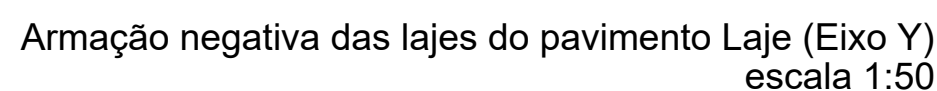


DETALHE DA ARMADURA DE SUPERIOR DE CONTINUIDADE DA LAJE
E MONTAGEM DA ARMADURA DE DISTRIBUIÇÃO

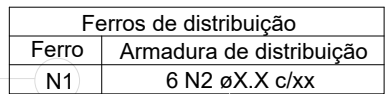

CONSTRUÇÃO:

Απονομή:

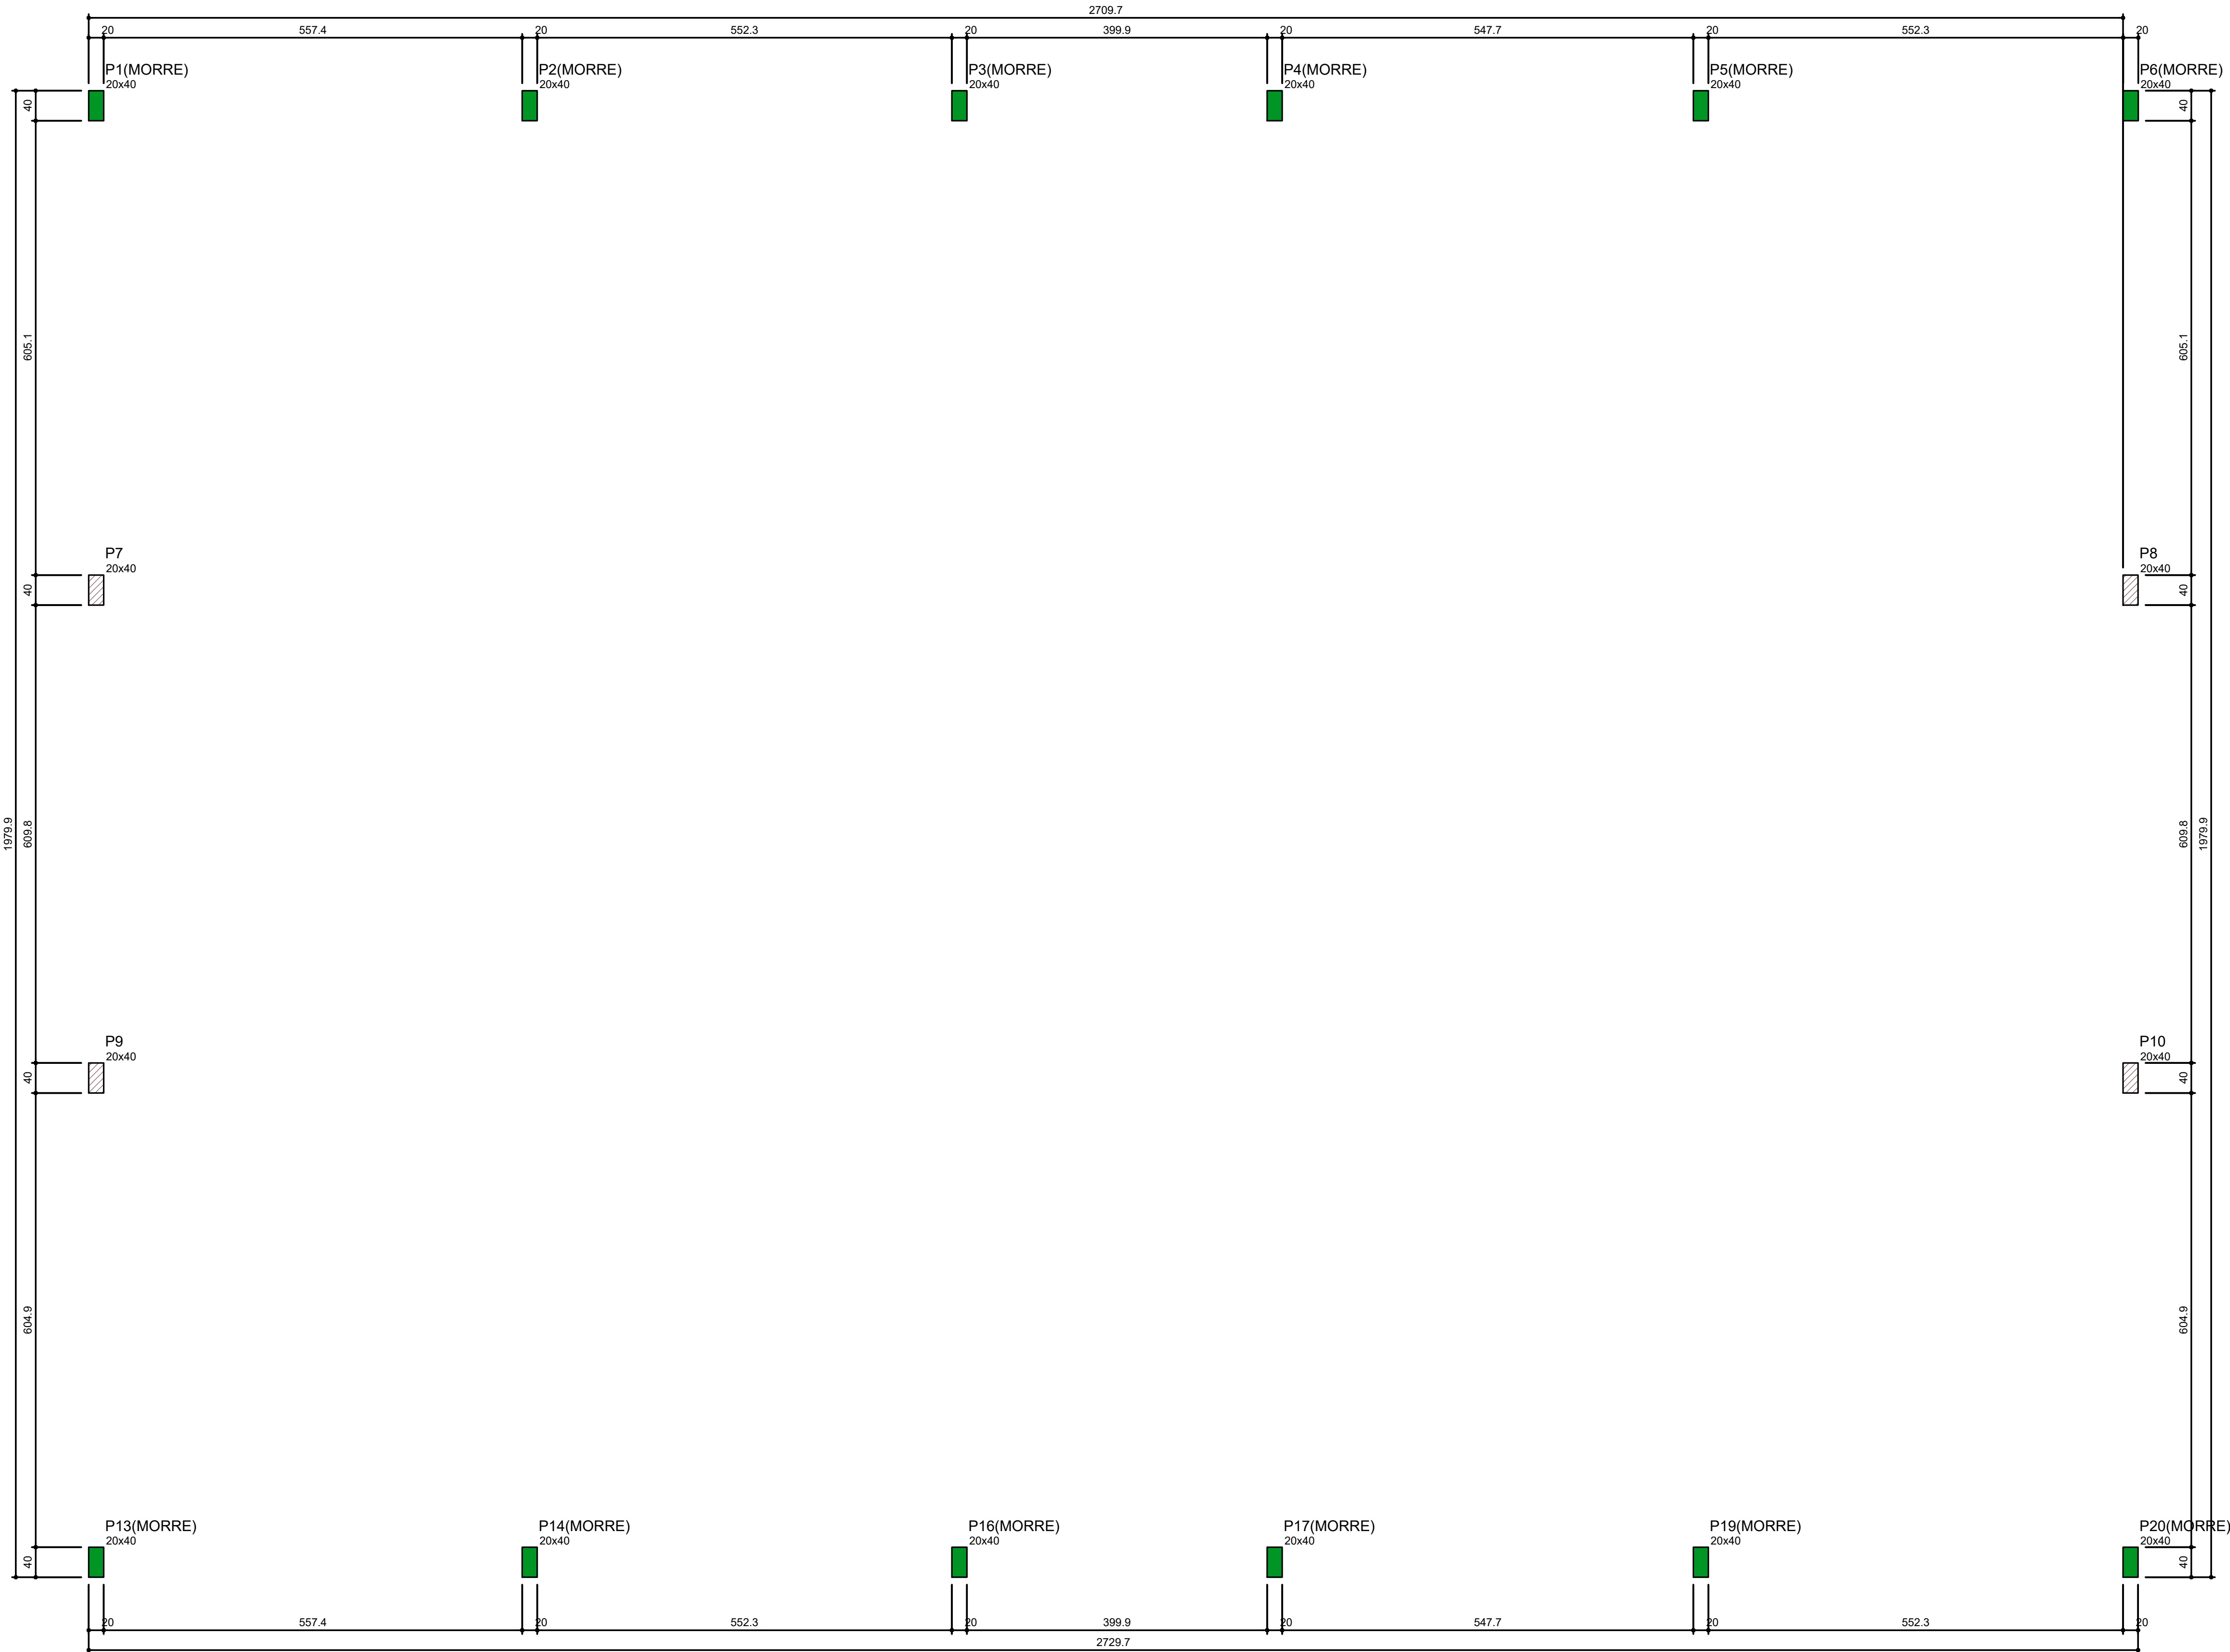

Características dos materiais	
fck (kgf/cm²)	Ecs (kgf/cm³)
250	241500

Pilares			
Nome	Seção (cm)	Elevação (cm)	Nível (cm)
P1	20x40	0	330
P2	20x40	0	330
P3	20x40	0	330
P4	20x40	0	330
P5	20x40	0	330
P6	20x40	0	330
P7	20x40	0	330
P8	20x40	0	330
P9	20x40	0	330
P10	20x40	0	330
P13	20x40	0	330
P14	20x40	0	330
P16	20x40	0	330
P17	20x40	0	330
P19	20x40	0	330
P20	20x40	0	330

Legenda dos pilares	
	Pilar que morre
	Pilar que passa

Forma do pavimento Térreo (Nível 330)
escala 1:50

PROPRIETÁRIO: PREFEITURA MUNICIPAL DE COREMAS - PB
LINCOLN CARTAXO DE LIRA JUNIOR:06897861405
Assinado de forma digital por LINCOLN CARTAXO DE LIRA JUNIOR:06897861405
Dados: 2025.08.08 12:25:00 -03'00'

PROJETO: LINCOLN CARTAXO DE LIRA JÚNIOR CREA 160.814.689-8

CONSTRUÇÃO:

FOLHA 23/26
PROJETO: CONSTRUÇÃO DE GINÁSIO POLIESPORTIVO - ESTRUTURAL
CONVENIENTE: PREFEITURA MUNICIPAL DE COREMAS - PB
CONVENIADO: MUNICÍPIO DE COREMAS - PB
LOCALIDADE: COREMAS - PB


DESENHO	DATA	RESPONSÁVEL	RUBRICA	DADOS
CÓPIA	AGO/2025	LINCOLN CARTAXO		
VISTO				
ESCALAS	DESENHOS			CONVÊNIO
Indicada	- FORMA DO PAVIMENTO TÉRREO (NÍVEL 330)			GOVERNO DO ESTADO
				ARQUIVO

Aprovações:

P1=P2=P3=P4



TÉRREO - L4

SEÇÃO
ESC 1:20

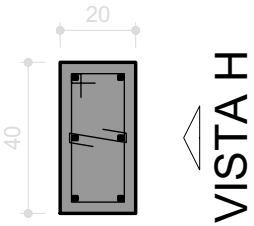


VISTA H

VISTA B

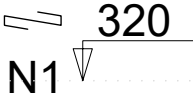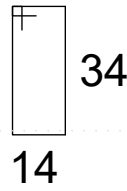

2 N2 ø5.0 C=107
2 N1 ø5.0 C=29

VISTA H
ESC 1:1

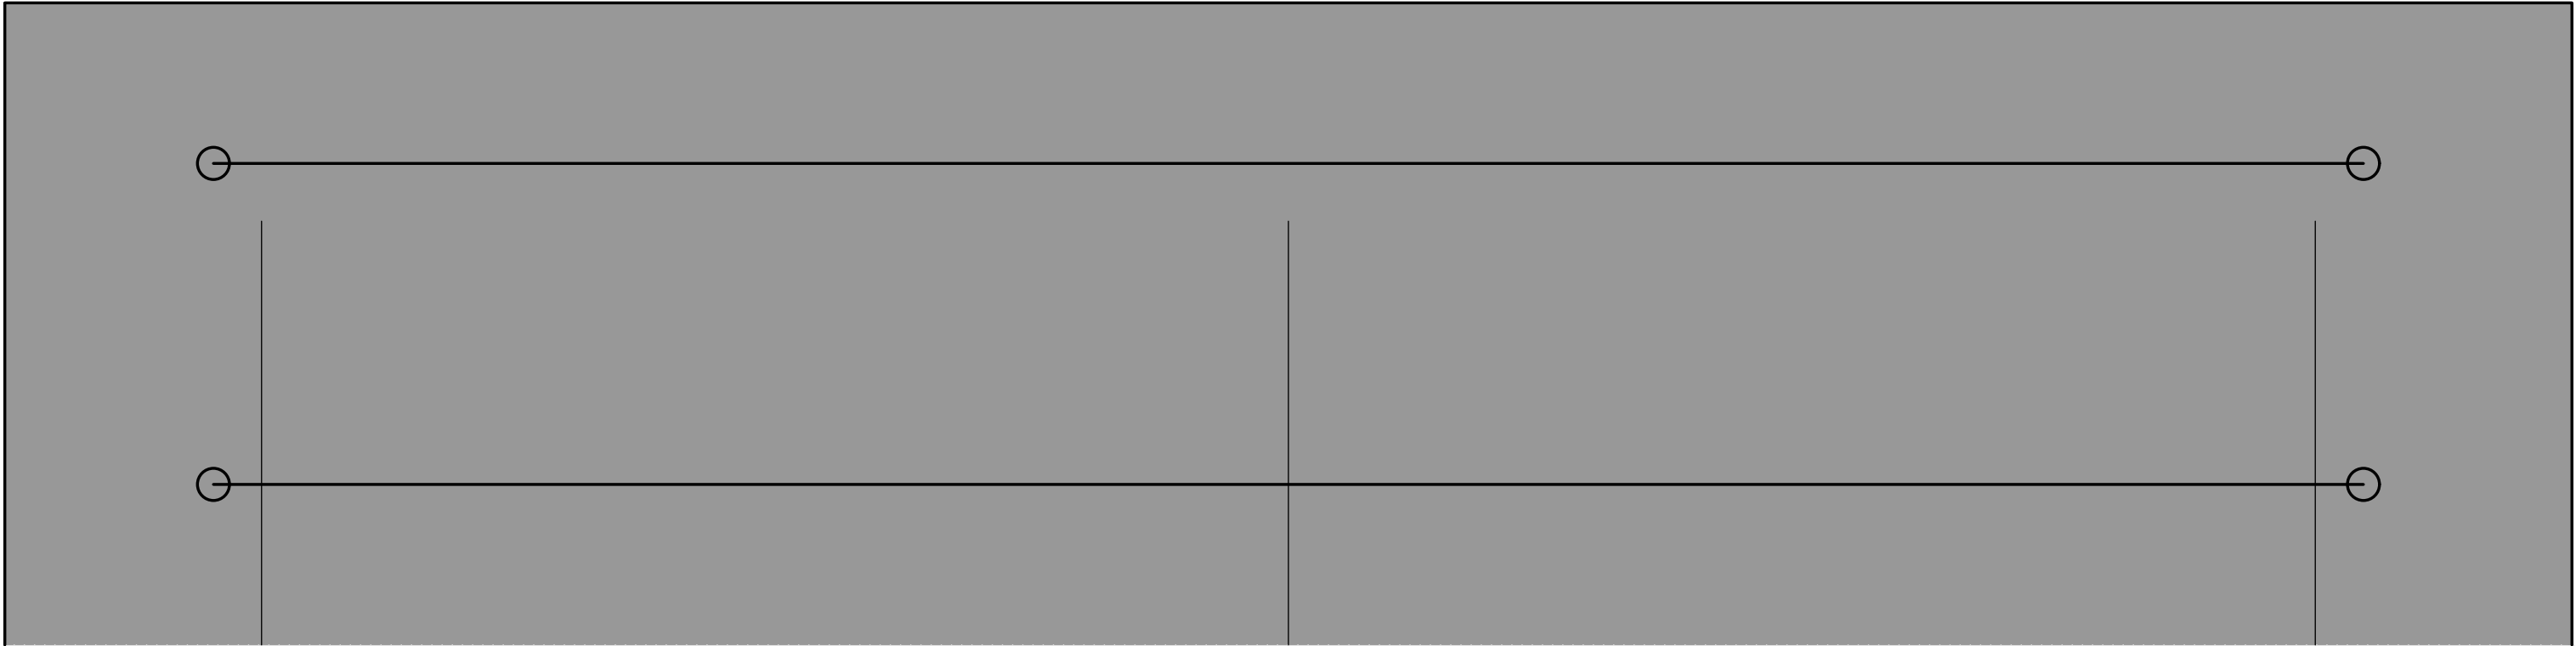

7
6 N4 ø10.0 C=7

VISTA B
ESC 1:1




10
2 N2 ø5

P5=P6=P13=P14=P16=P17=P19=P20


TÉRREO - L4

SEÇÃO
ESC 1:20

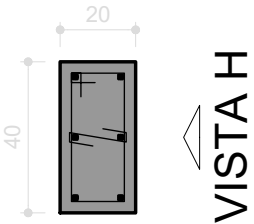


VISTA H

VISTA B

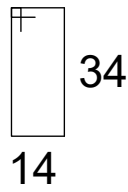


3 N2 ø5.0 C=107
3 N1 ø5.0 C=29

VISTA H
ESC 1:2

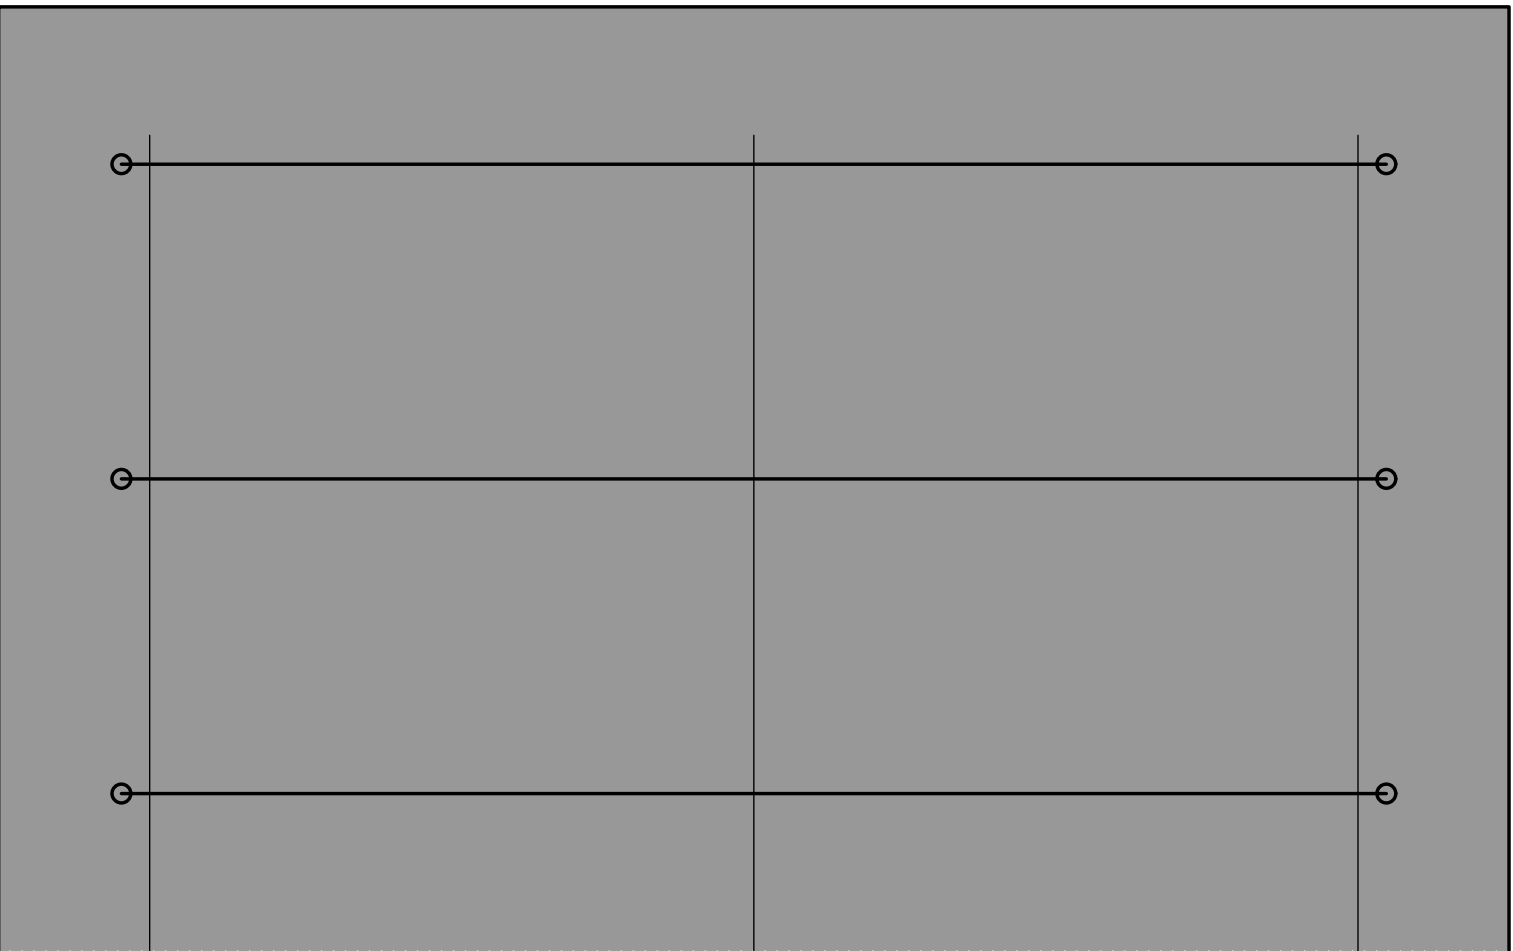

22
6 N5 ø10.0 C=22

VISTA B
ESC 1:2

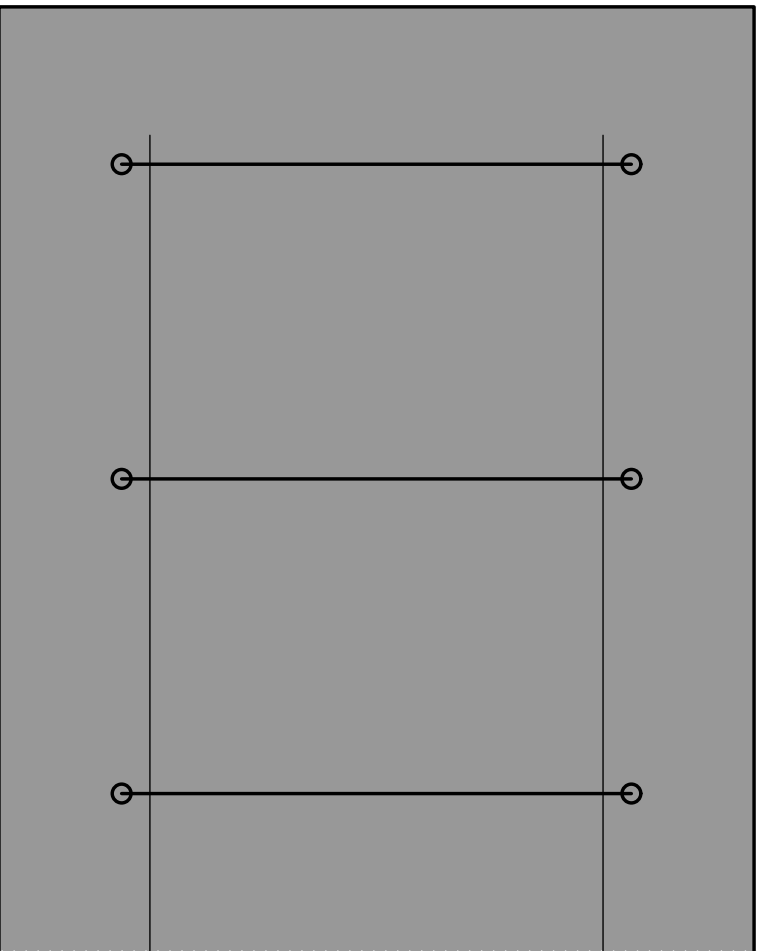

25
3 N2 ø10

*OBS.: OS QUADROS RESUMO REFERENTES A
ESTA PRANCHA CONSTAM NA PRANCHA 25/26

PROPRIETÁRIO: PREFEITURA MUNICIPAL DE COREMAS - PB
LINCOLN CARTAXO DE
LIRA JÚNIOR:06897861405
Assinado de forma digital por LINCOLN
CARTAXO DE LIRA JÚNIOR:06897861405
Dados: 2025.08.08 12:24:45 -03'00'

PROJETO: LINCOLN CARTAXO DE LIRA JÚNIOR CREA 160.814.689-8

CONSTRUÇÃO:

FOLHA 24/26	PROJETO: CONSTRUÇÃO DE GINÁSIO POLIESPORTIVO - ESTRUTURAL			
	CONVENIENTE: PREFEITURA MUNICIPAL DE COREMAS - PB			
	CONVENIADO: MUNICÍPIO DE COREMAS - PB			
	LOCALIDADE: COREMAS - PB			
DESENHO	DATA	RESPONSÁVEL	RUBRICA	DADOS
CÓPIA	AGO/2025	LINCOLN CARTAXO		
VISTO				
ESCALAS	DESENHOS			CONVÊNIO
	Indicada			GOVERNO DO ESTADO
				ARQUIVO

Aprovações:

P7=P8=P9=P10

VISTA H
ESC 1:2

VISTA B
ESC 1:2

TÉRREO - L4

330

SEÇÃO
ESC 1:20

20

40

VISTA H


VISTA B

34

14

N3

2 N2 ø5.0 C=107
2x2 N3 ø5.0 C=29

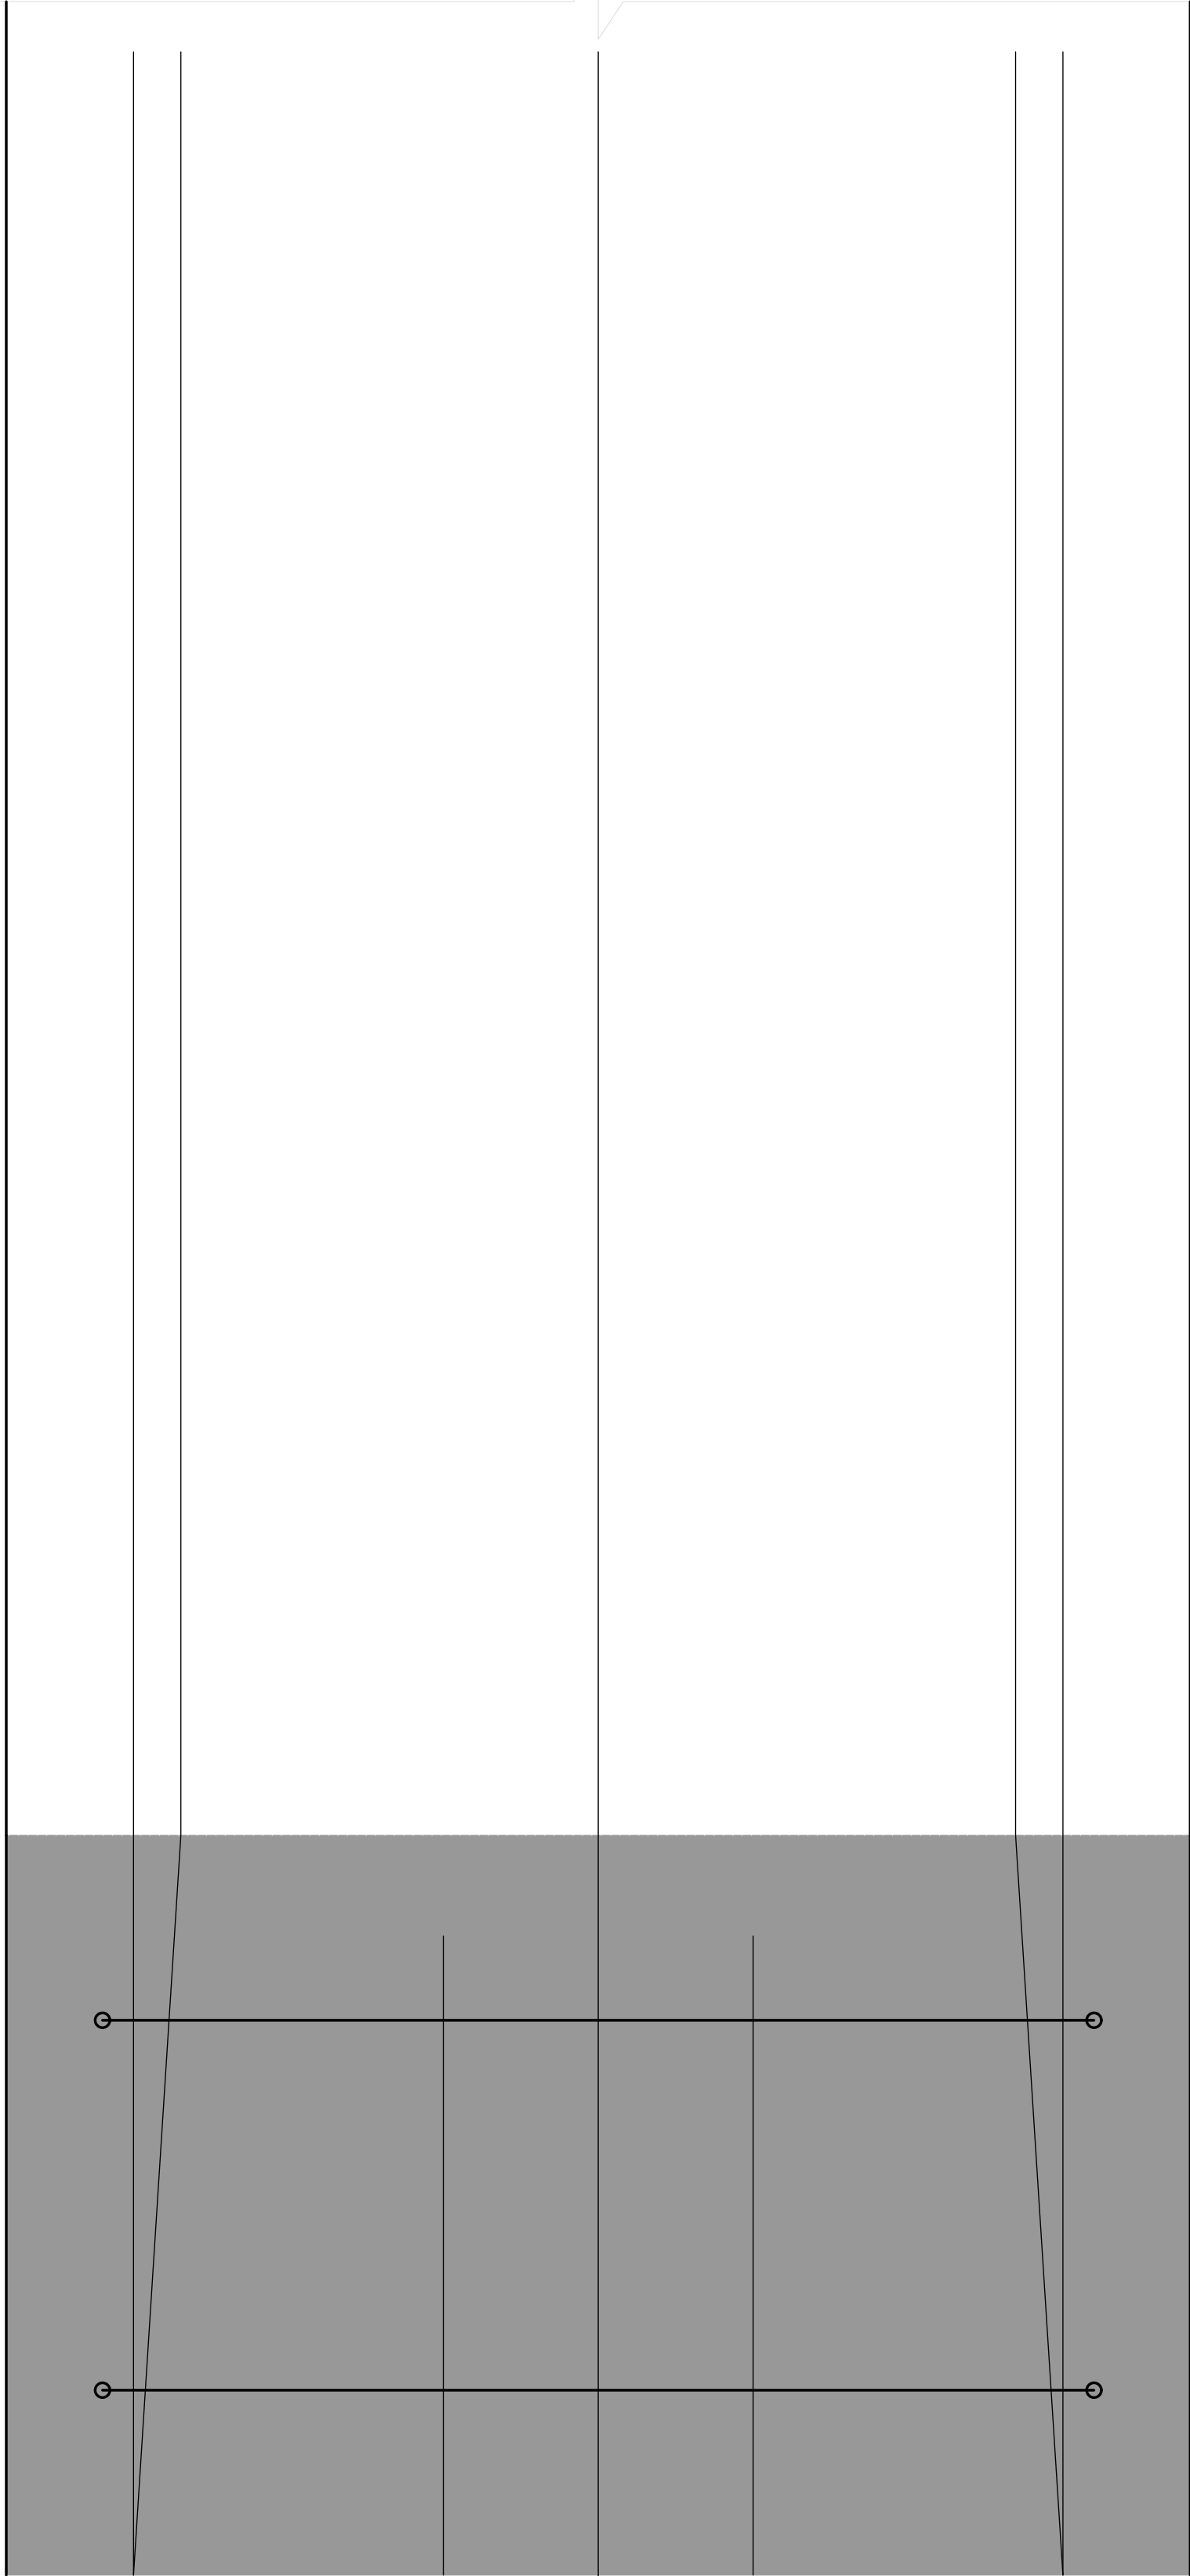


22
4 N6 ø16.0 C=22

2 N7 ø16.0 C=121

60

25

6 N8 ø16.0 C=85

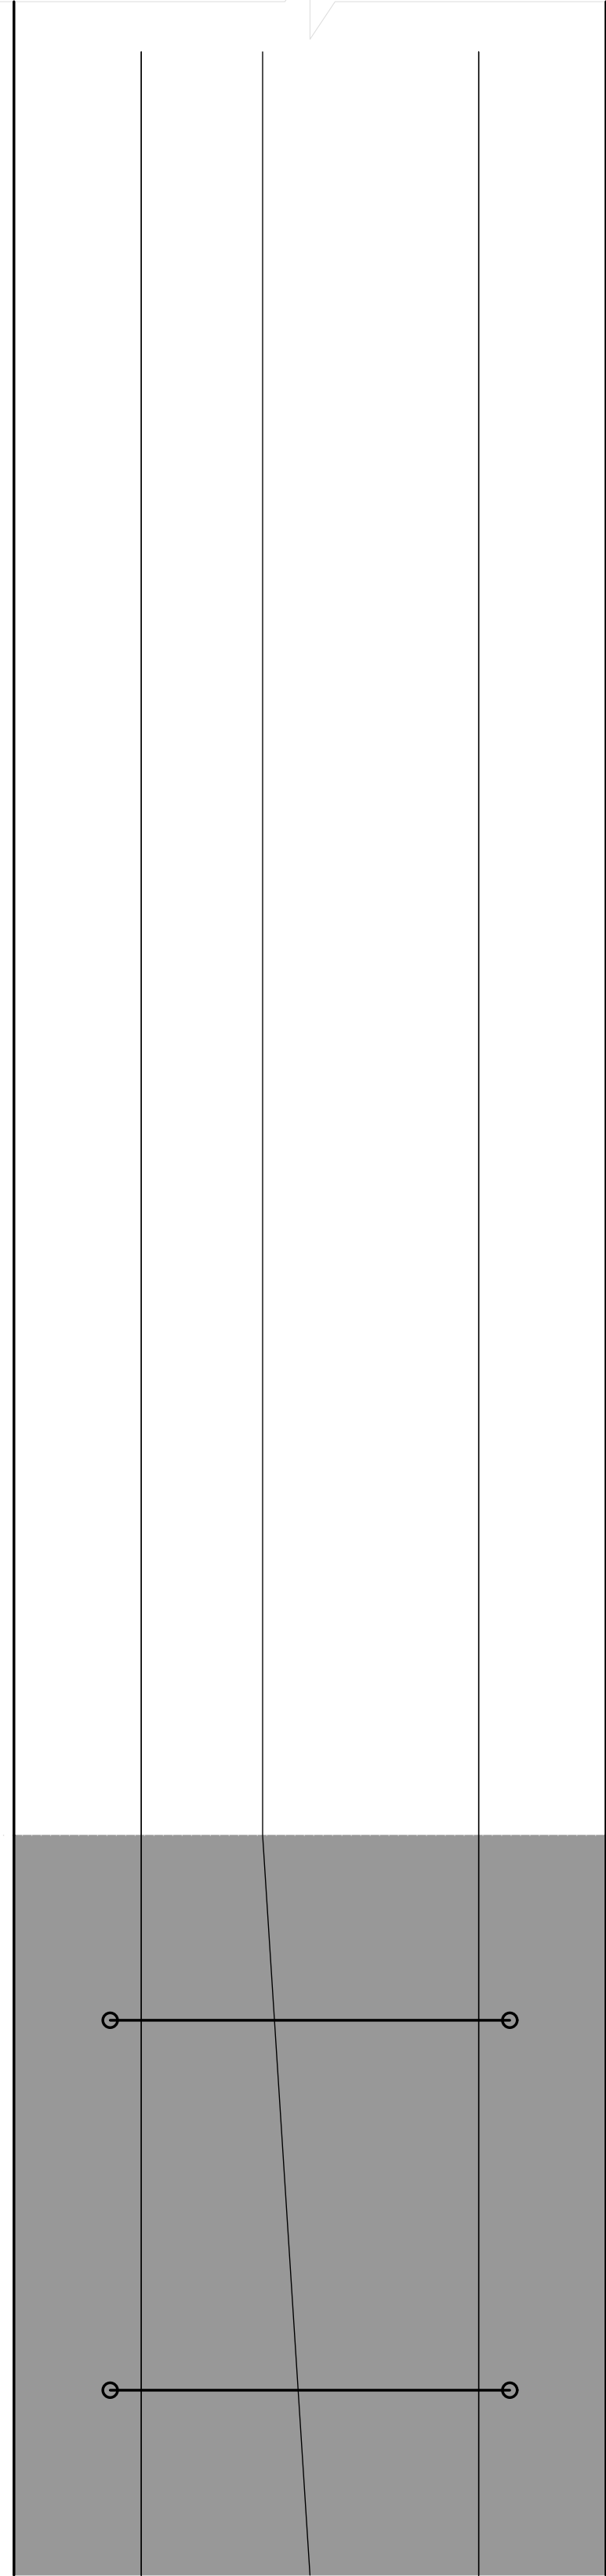

25
2 N2 ø17.5

RELAÇÃO DO AÇO					
4xP1		8xP5		4xP7	
AÇO	N	DIAM (mm)	QUANT	C.UNIT (cm)	C.TOTAL (cm)
CA60	1	5.0	32	29	928
	2	5.0	40	107	4280
	3	5.0	16	29	464
CA50	4	10.0	24	7	168
	5	10.0	48	22	1056
	6	16.0	16	22	352
	7	16.0	8	121	968
	8	16.0	24	85	2040

RESUMO DO AÇO			
AÇO	DIAM (mm)	C.TOTAL (m)	PESO + 10% (kg)
CA50	10.0	12.2	8.3
CA60	16.0	33.6	58.3
PESO TOTAL (kg)			9.6
CA50	66.6		
CA60	9.6		

Volume de concreto (C-25) = 0.27 m³
Área de forma = 4.08 m²


PROPRIETÁRIO: PREFEITURA MUNICIPAL DE COREMAS - PB
LINCOLN CARTAXO DE LIRA JUNIOR:06897861405
Assinado de forma digital por LINCOLN CARTAXO DE LIRA JUNIOR:06897861405
Dados: 2025.08.08 12:24:14 -03'00'

PROJETO: LINCOLN CARTAXO DE LIRA JÚNIOR CREA 160.814.689-8


CONSTRUÇÃO:

FOLHA 25/26	PROJETO:	CONSTRUÇÃO DE GINÁSIO POLIESPORTIVO - ESTRUTURAL		
	CONVENIENTE:	PREFEITURA MUNICIPAL DE COREMAS - PB		
	CONVENIADO:	MUNICÍPIO DE COREMAS - PB		
	LOCALIDADE:	COREMAS - PB		
	DATA	RESPONSÁVEL	RUBRICA	DADOS
DESENHO	AGO/2025	LINCOLN CARTAXO		
CÓPIA				
VISTO				
ESCALAS	DESENHOS			CONVÊNIO
Indicada	- ARMADURAS DOS PILARES PAV. TÉRREO (NÍVEL 330)			GOVERNO DO ESTADO
				ARQUIVO

Aprovações:

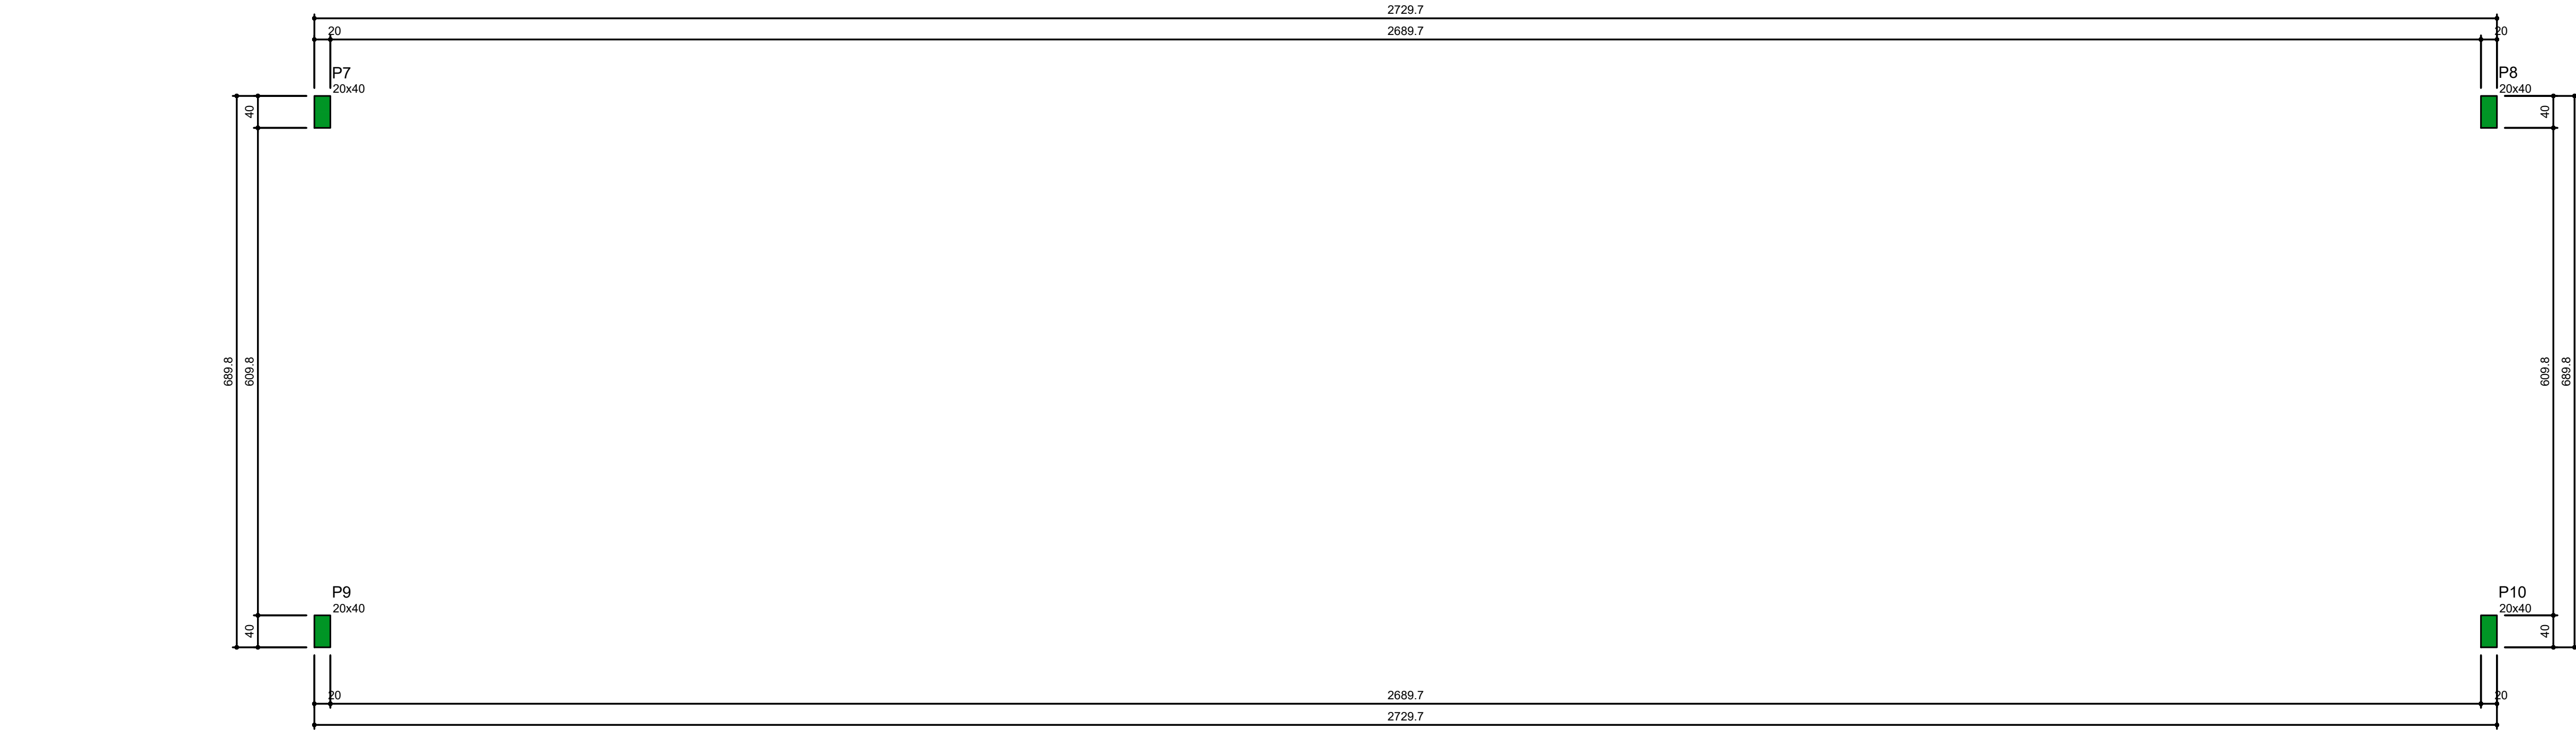

Forma do pavimento Pilares testada (Nível 830)
escala 1:50


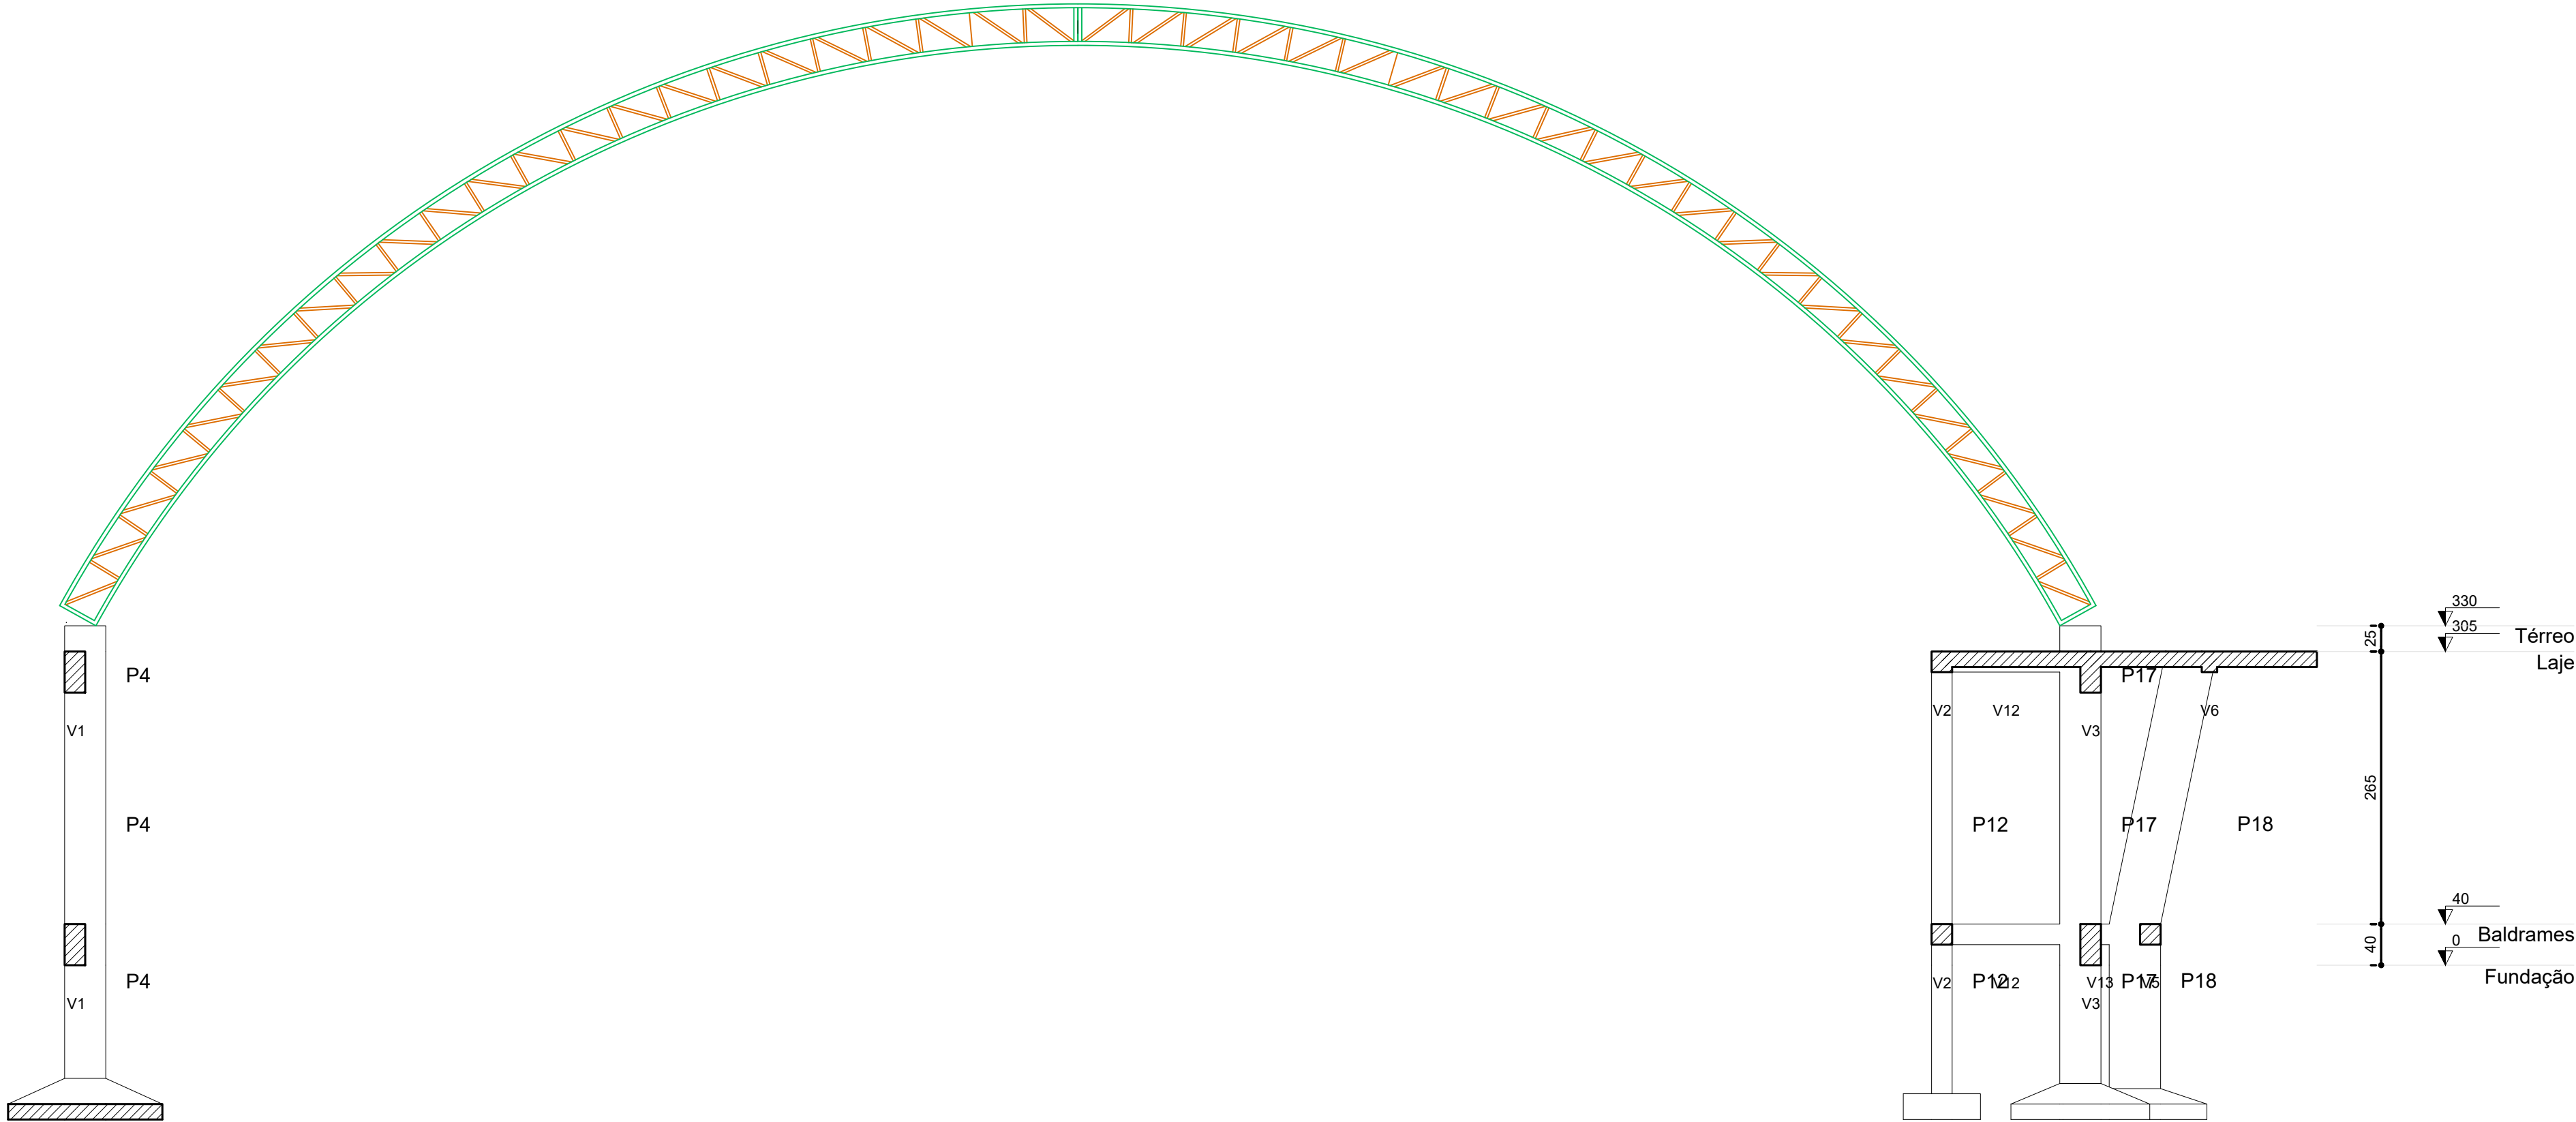


Corte A-A
escala 1:50

P7=P8=P9=P10

PILARES TESTADA - L5

SEÇÃO
ESC 1:20

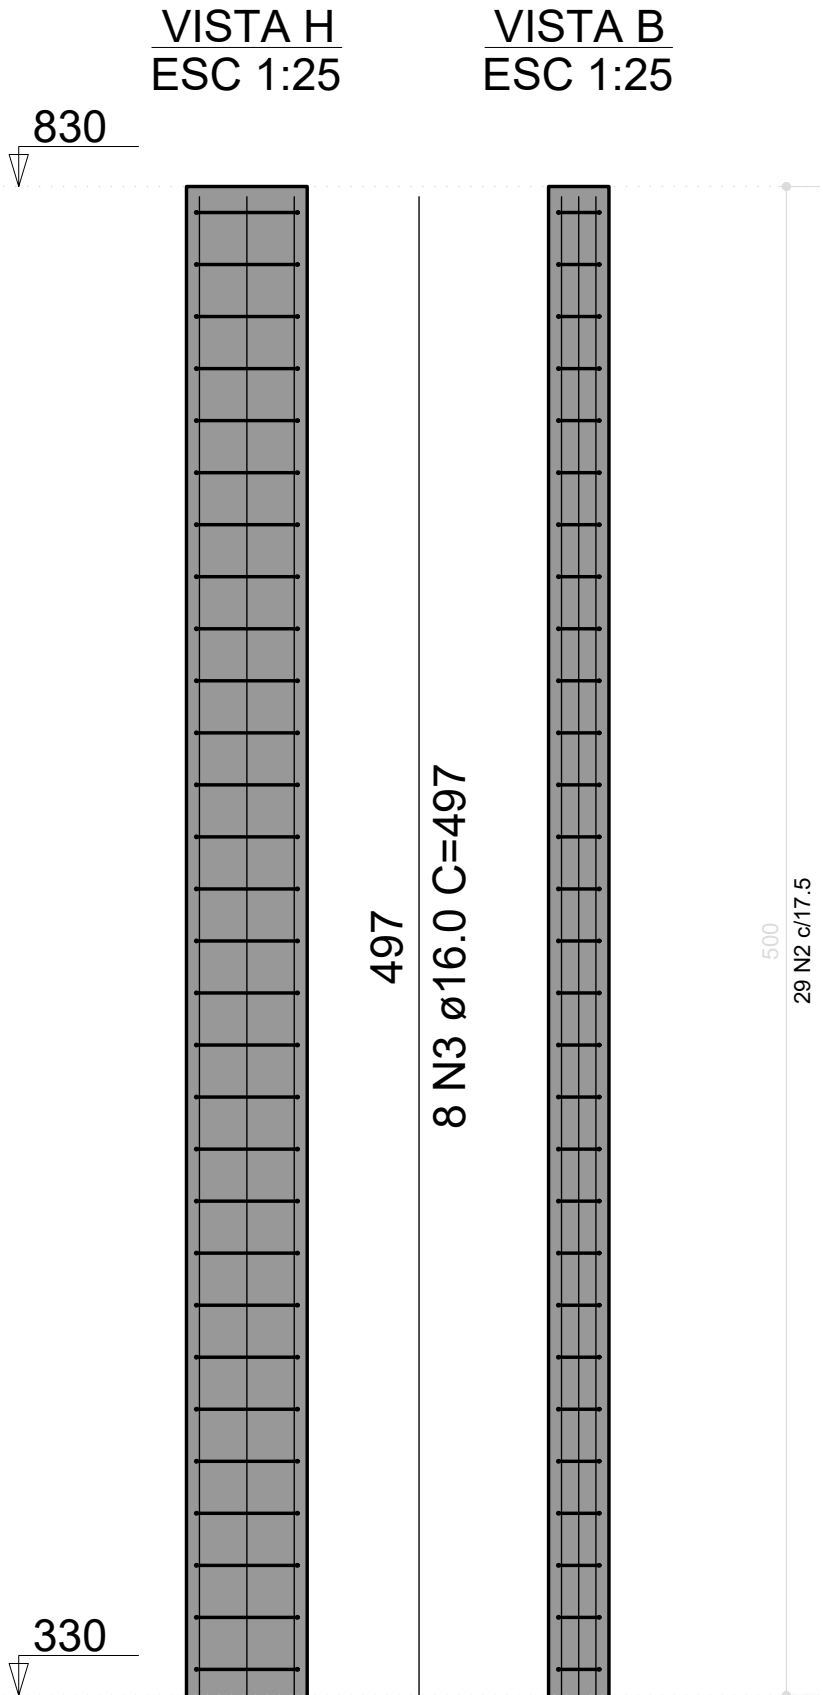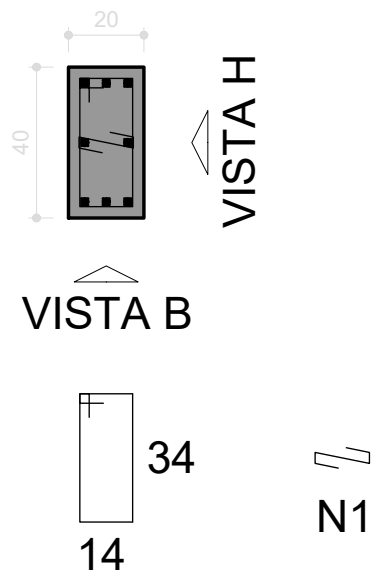

RELAÇÃO DO AÇO

4xP7

AÇO	N	DIAM (mm)	QUANT	C.UNIT (cm)	C.TOTAL (cm)
CA60	1	5.0	116	29	3364
	2	5.0	116	107	12412
CA50	3	16.0	32	497	15904

RESUMO DO AÇO

AÇO	DIAM (mm)	C.TOTAL (m)	PESO + 10% (kg)
CA50	16.0	159	276.1
CA60	5.0	157.8	26.7

PESO TOTAL (kg)

CA50	276.1
CA60	26.7

Volume de concreto (C-25) = 1.60 m³
Área de forma = 24.00 m²

PROPRIETÁRIO: PREFEITURA MUNICIPAL DE COREMAS - PB

LINCOLN CARTAXO DE LIRA JUNIOR:06897861405 Assinado de forma digital por LINCOLN CARTAXO DE LIRA JUNIOR:06897861405
Dados: 2025.08.08 12:26:15 -03'00'

PROJETO: LINCOLN CARTAXO DE LIRA JÚNIOR CREA 160.814.689-8

CONSTRUÇÃO:

FOLHA 26/26

PROJETO: CONSTRUÇÃO DE GINÁSIO POLIESPORTIVO - ESTRUTURAL

CONVENIENTE: PREFEITURA MUNICIPAL DE COREMAS - PB

CONVENIADO: MUNICÍPIO DE COREMAS - PB

LOCALIDADE: COREMAS - PB

	DATA	RESPONSÁVEL	RUBRICA	DADOS
DESENHO	AGO/2025	LINCOLN CARTAXO		
COPIA				
VISTO				
ESCALAS	DESENHOS			CONVÊNIO
Indicada	- FORMA DO PAV. PILARES TESTADA (NÍVEL 830) - ARMADURAS PILARES PAV. PILARES TESTADAS (NÍVEL 830) - CORTE AA			GOVERNO DO ESTADO
				ARQUIVO

Aprovações: