



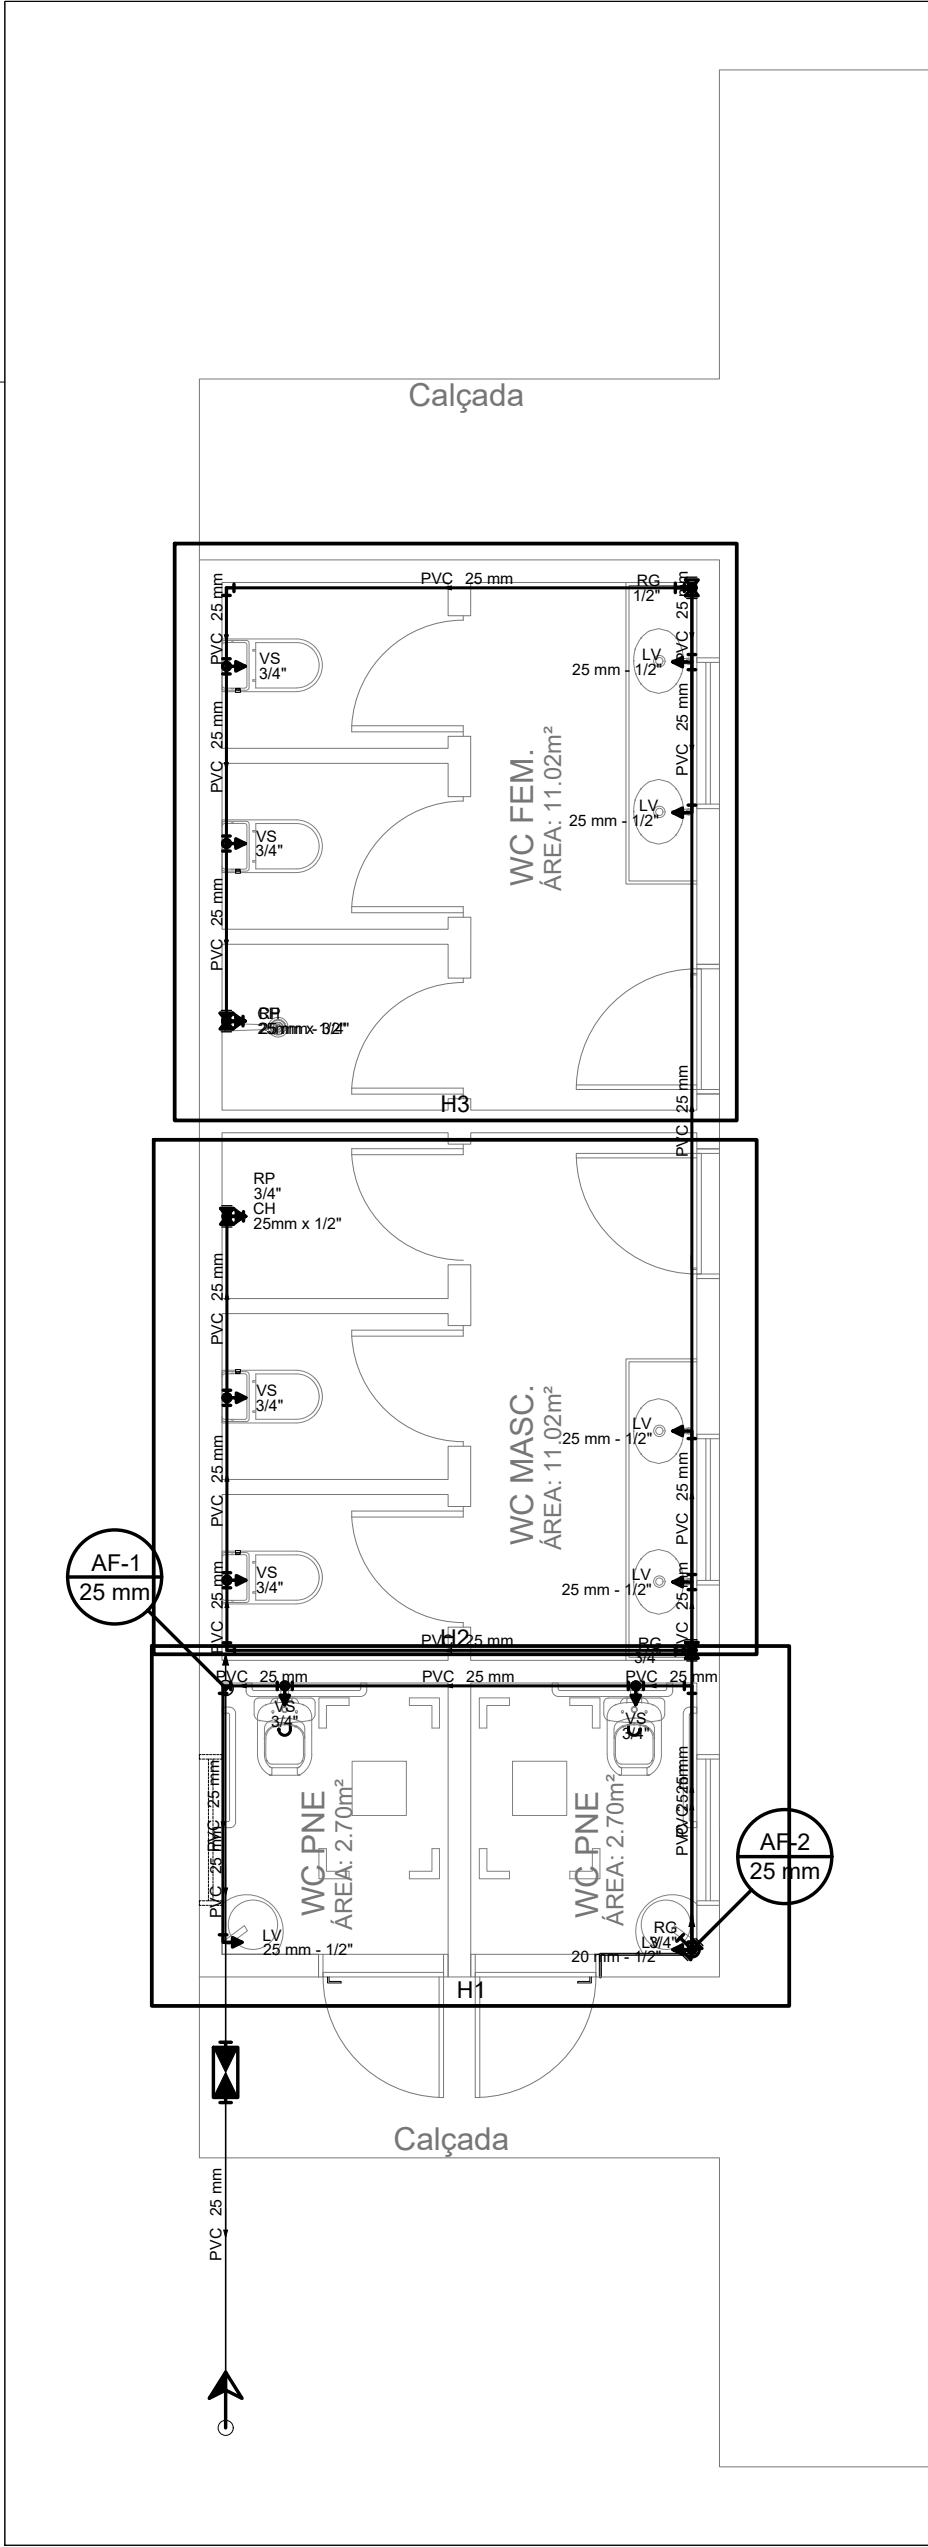

Lista de Materiais		
Aparelho		
Chuveiro 25mm x 1/2"	2	pç
Torneira de lavatório 20 mm - 1/2"	1	pç
Vaso Sanitário c/ cx. acoplada 1/2"	5	pç
Ferro maleável classe 10 Colar de tomada de f" f 1 1/2"	1	pç
Metais		
Registro de Chuveiro branco PVC 3/4"	1	pç
Registro de esfera 1 1/2"	1	pç
Registro de gaveta bruto ABNT 1/2"	1	pç
Registro de pressão c/ canopla cromada 3/4"	2	pç
Registro esfera borboleta bruto PVC 3/4"	1	pç
PVC Acessórios		
Engate flexível cobre cromado com canopla 1/2 - 30cm	6	pç
Engate flexível plástico 1/2 - 30cm	6	pç
PVC misto soldável		
Joelho 90 soldável c/ rosca 25 mm - 3/4"	3	pç
Joelho de redução soldável c/ rosca 25 mm - 1/2"	6	pç
Luva soldável c/ rosca 25 mm - 3/4"	1	pç
PVC rígido roscável		
Curva 90 c/ rosca 1.1/2"	1	pç
Tubos 3/4"	0.28	m
PVC rígido soldável		
Adapt sold.c/roscas p registro 20 mm - 1/2"	2	pç
25 mm - 3/4"	6	pç
50 mm - 1.1/2"	1	pç
Curva 90 soldável 25 mm	6	pç
Joelho 90° soldável 25 mm	1	pç
Tubos 25 mm	48.62	m
Tê 90 soldável 25 mm	7	pç
PVC soldável azul c/ bucha latão		
Joelho 90° soldável com bucha de latão 20 mm - 1/2"	1	pç
Joelho de redução 90° soldável com bucha de latão 25 mm - 1/2"	5	pç
Tê red.90 sold c/ bucha latão B central 25 mm - 1/2"	2	pç


Legenda das indicações	
CH	Chuveiro - 25mm x 1/2"
LV	Lavatório com Tê de 90° - 25 mm - 1/2"
LV	Lavatório com joelho de 90° - 20 mm - 1/2"
LV	Lavatório com joelho de 90° - 25 mm - 1/2"
RG	Registro bruto gaveta ABNT c/PVC soldável - 1/2"
RG	Registro bruto gaveta ABNT c/PVC soldável - 3/4"
RP	Registro de Pressão com PVC soldável - 25 mm - 3/4"
RP	Registro de chuveiro branco - 3/4"
VS	Vaso sanitário com caixa acoplada - 3/4"

Legenda	
	Alimentador Predial
	Hidrômetros
	Registro bruto gaveta ABNT c/PVC soldável
	Registro de Pressão com PVC soldável
	Registro de chuveiro branco

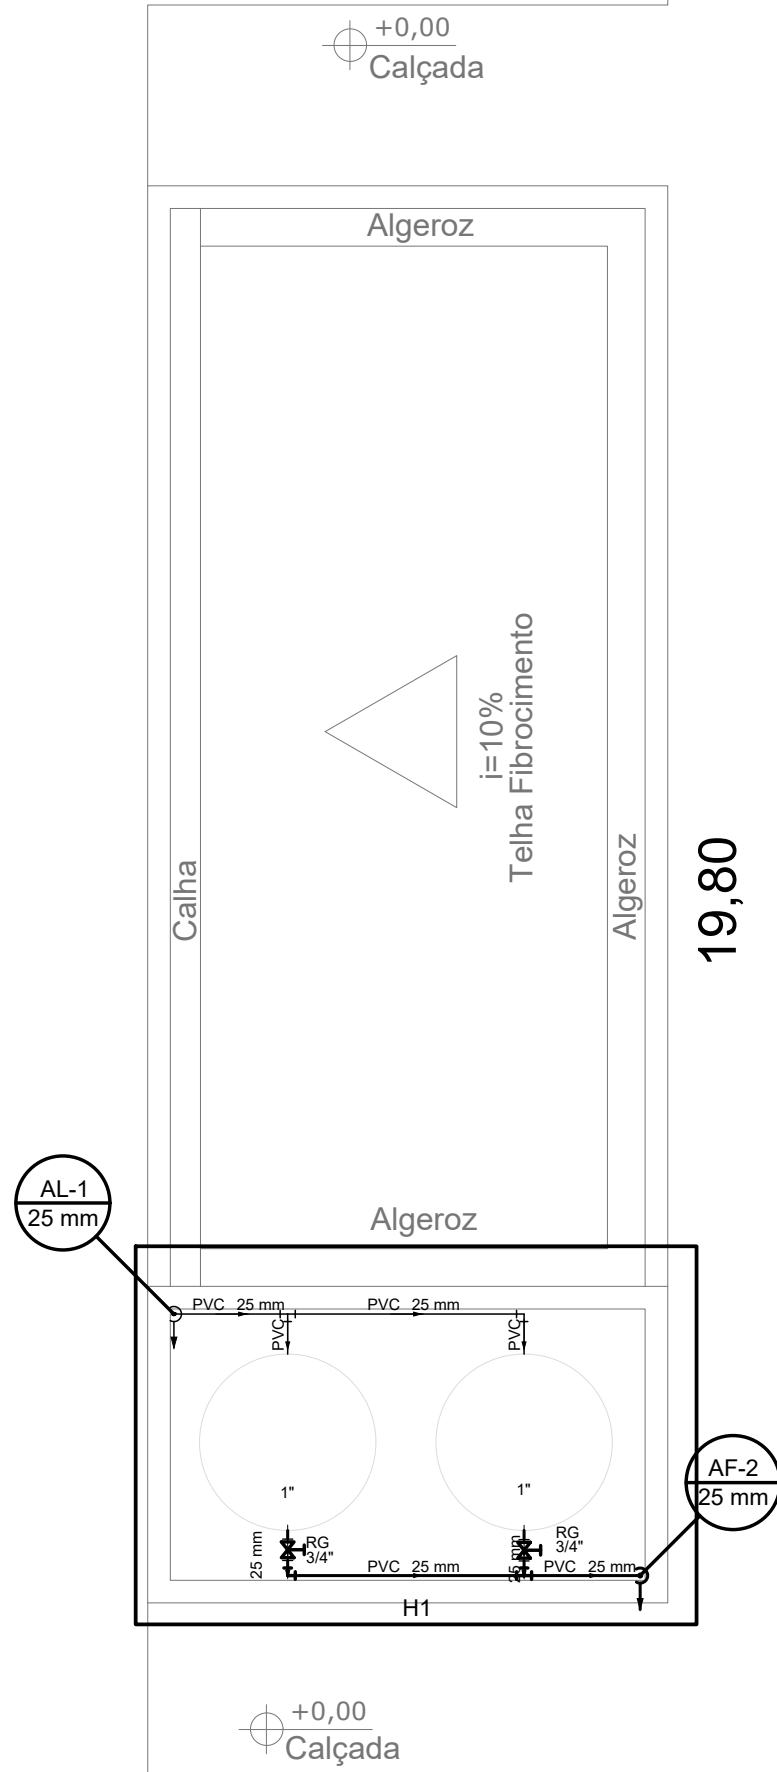

Lista de Materiais		
Metais		
Registro de gaveta bruto ABNT 3/4"		2 pçs
PVC rígido soldável		
Adapt sold. c/ flange livre p/ cx. d' água 32 mm - 1"		2 pçs
Adapt sold.curto c/bolsa-rosca p registro 25 mm - 3/4"		4 pçs
Curva 90 soldável 25 mm		2 pçs
Tubos 25 mm	11.01 m	
Tê 90 soldável 25 mm		1 pçs
Reservatório cilíndrico		
Poliétileno 500 L		2 pçs

Legenda das indicações	
RG	Registro bruto gaveta ABNT c/PVC soldável - 3/4"

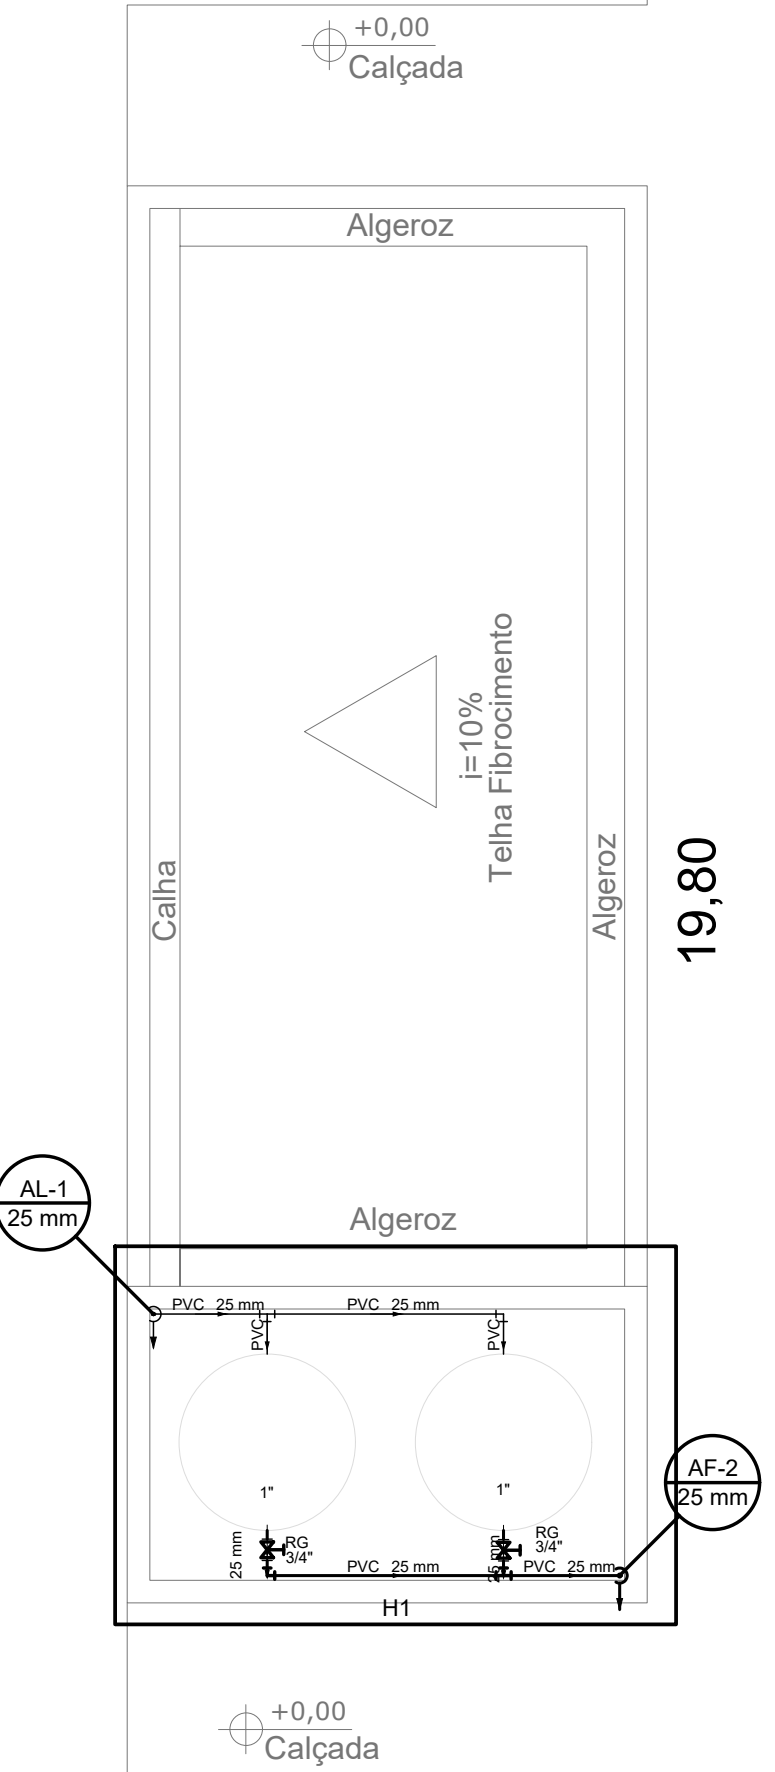

Lista de Materiais		
Metais		
Registro de gaveta bruto ABNT 3/4"	2	pç
PVC rígido soldável		
Adapt sold. c/ flange livre p/ cx. d'água 32 mm - 1"	2	pç
Adapt sold.curto c/bolsa-rosca p registro 25 mm - 3/4"	4	pç
Curva 90 soldável 25 mm	2	pç
Tubos 25 mm	11.01	m
Tê 90 soldável 25 mm	1	pç
Reservatório cilíndrico		
Poliétileno 500 L	2	pç

Legenda das indicações	
RG	Registro bruto gaveta ABNT c/PVC soldável - 3/4"


PROPRIETÁRIO: PREFEITURA MUNICIPAL DE COREMAS - PB
LINCOLN CARTAXO DE LIRA JUNIOR:06897861405
Assinado digitalmente por LINCOLN CARTAXO DE LIRA JUNIOR:06897861405
Dados: 2025.08.08 13:34:54 -03'00'

PROJETO: LINCOLN CARTAXO DE LIRA JÚNIOR CREA 160.814.689-8


FOLHA	PROJETO:	CONSTRUÇÃO DE GINÁSIO POLIESPORTIVO
01/02	CONVENIENTE:	PREFEITURA MUNICIPAL DE COREMAS - PB
	CONVENIADO:	MUNICÍPIO DE COREMAS - PB
	LOCALIDADE:	COREMAS - PB

	DATA	RESPONSÁVEL	RUBRICA	DADOS
DESENHO	AGO/2025	LINCOLN CARTAXO		CREA 160.814.689-8
CÓPIA				
VISTO				


ESCALAS	DESENHOS	CONVÊNIO
INDICADO	- PROJETO HIDRÁULICO	ARQUIVO

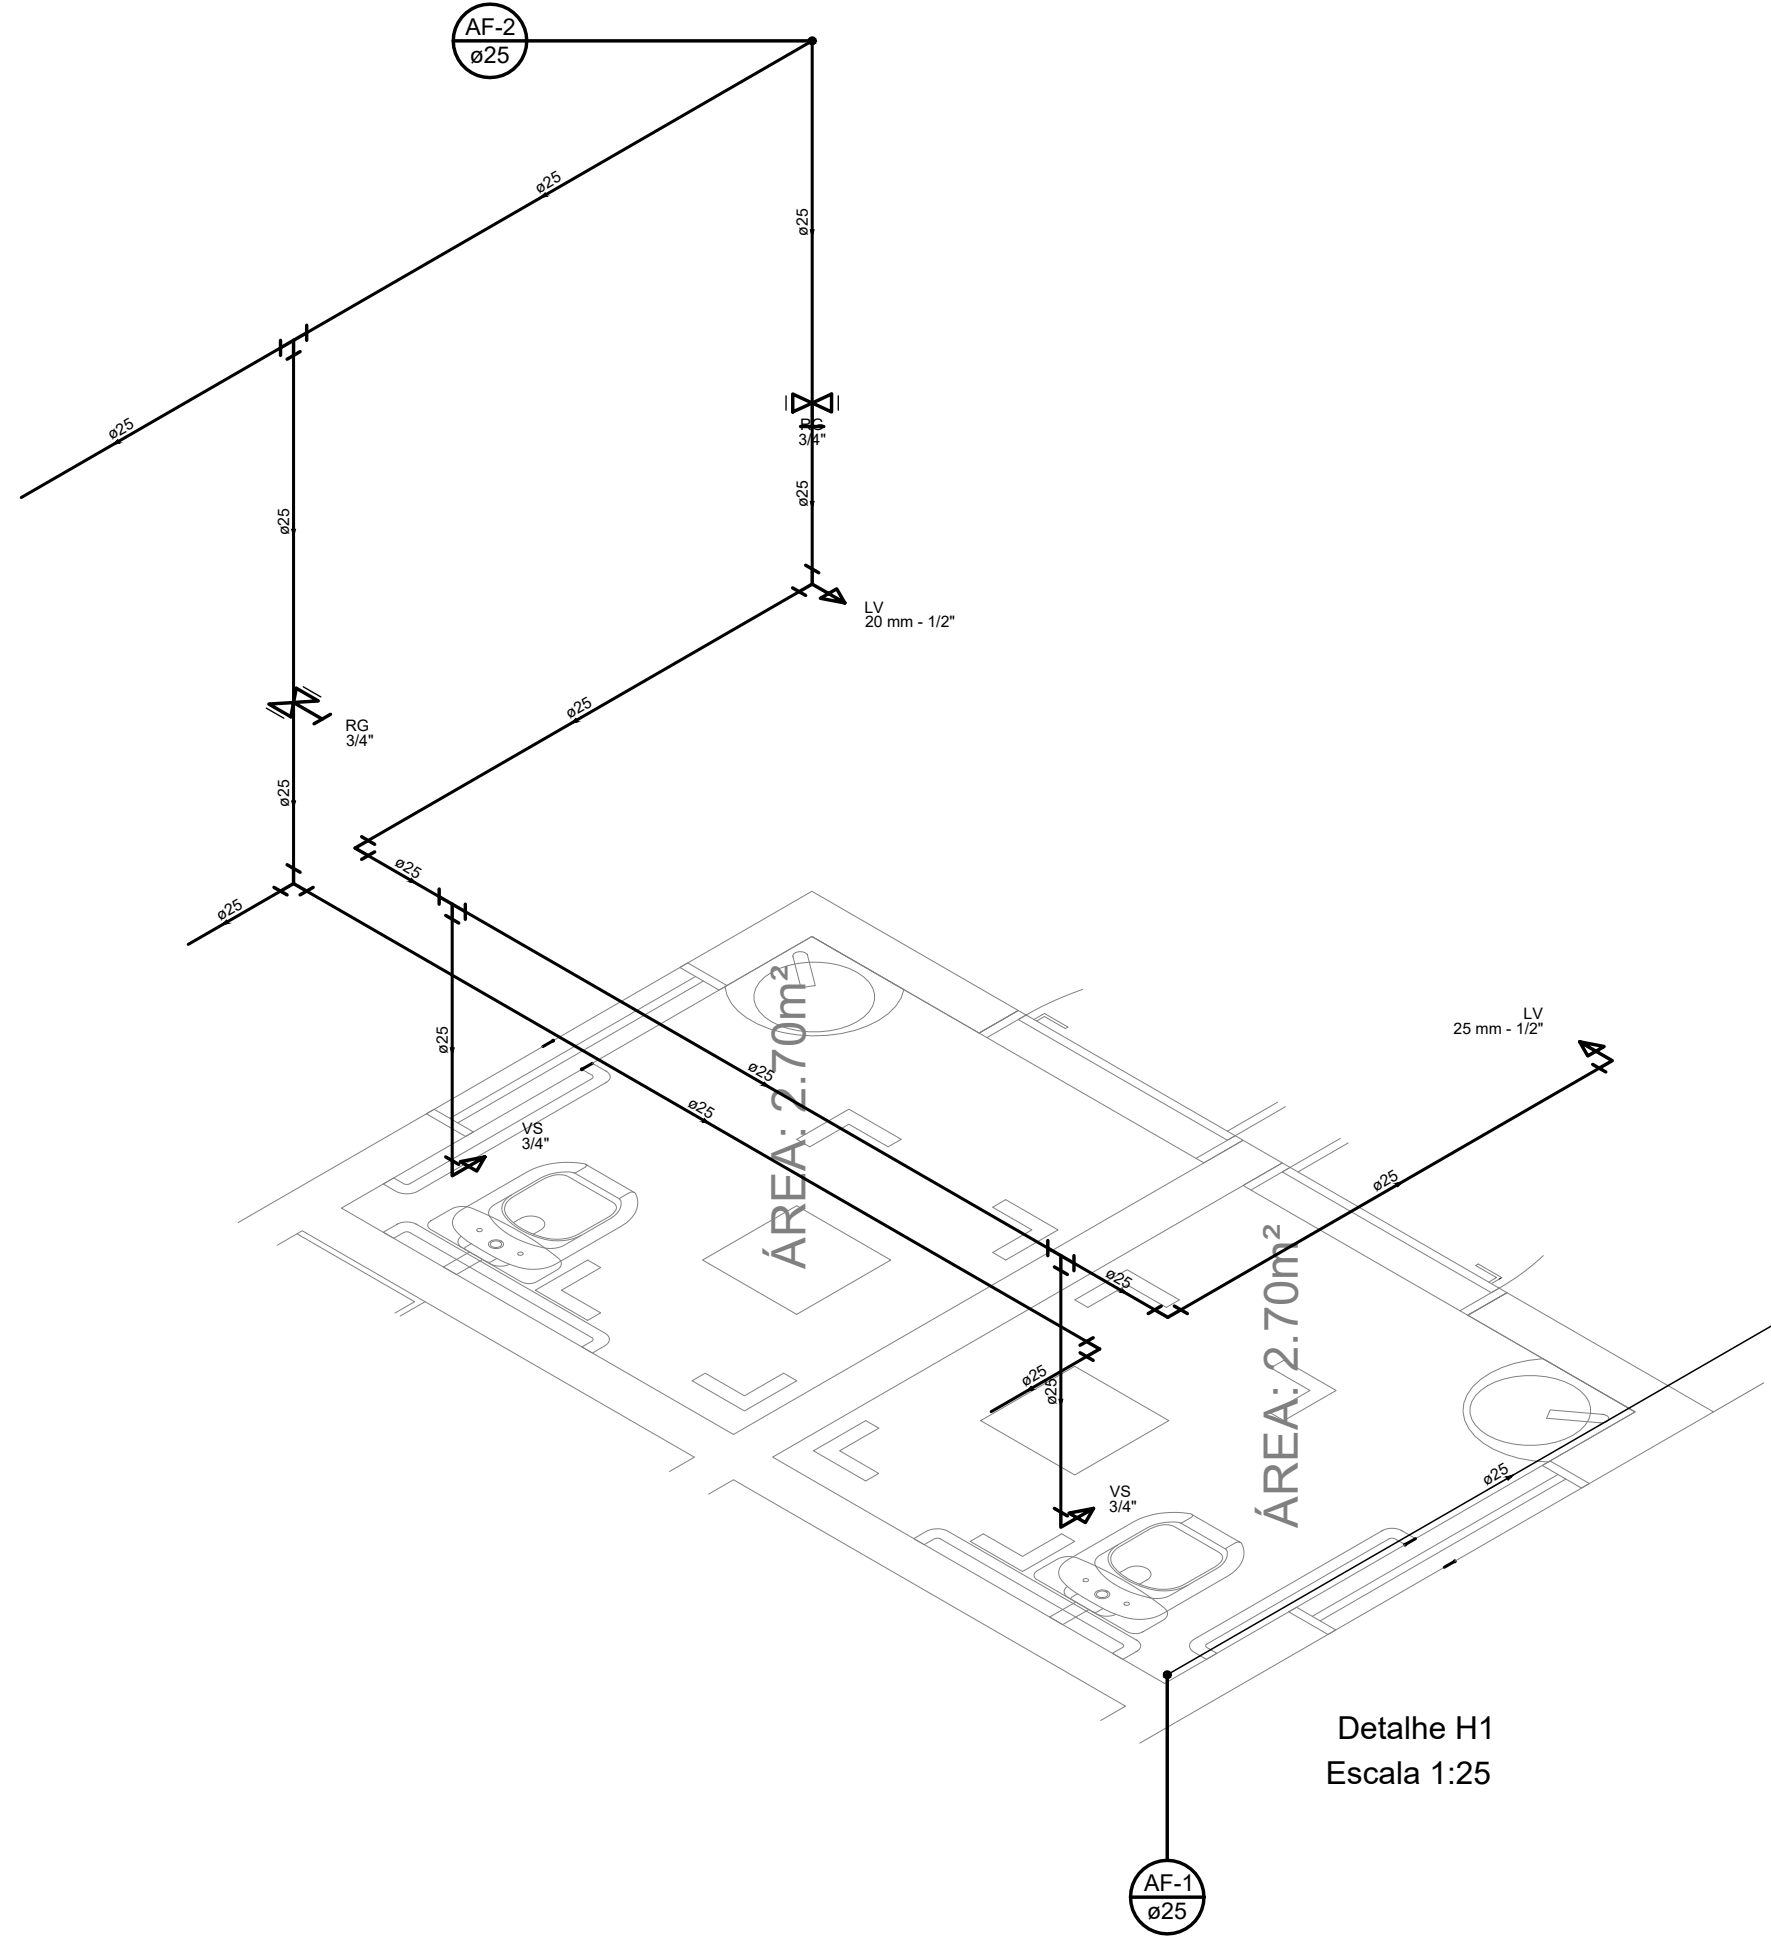


Detalhe H1
Escala 1:25

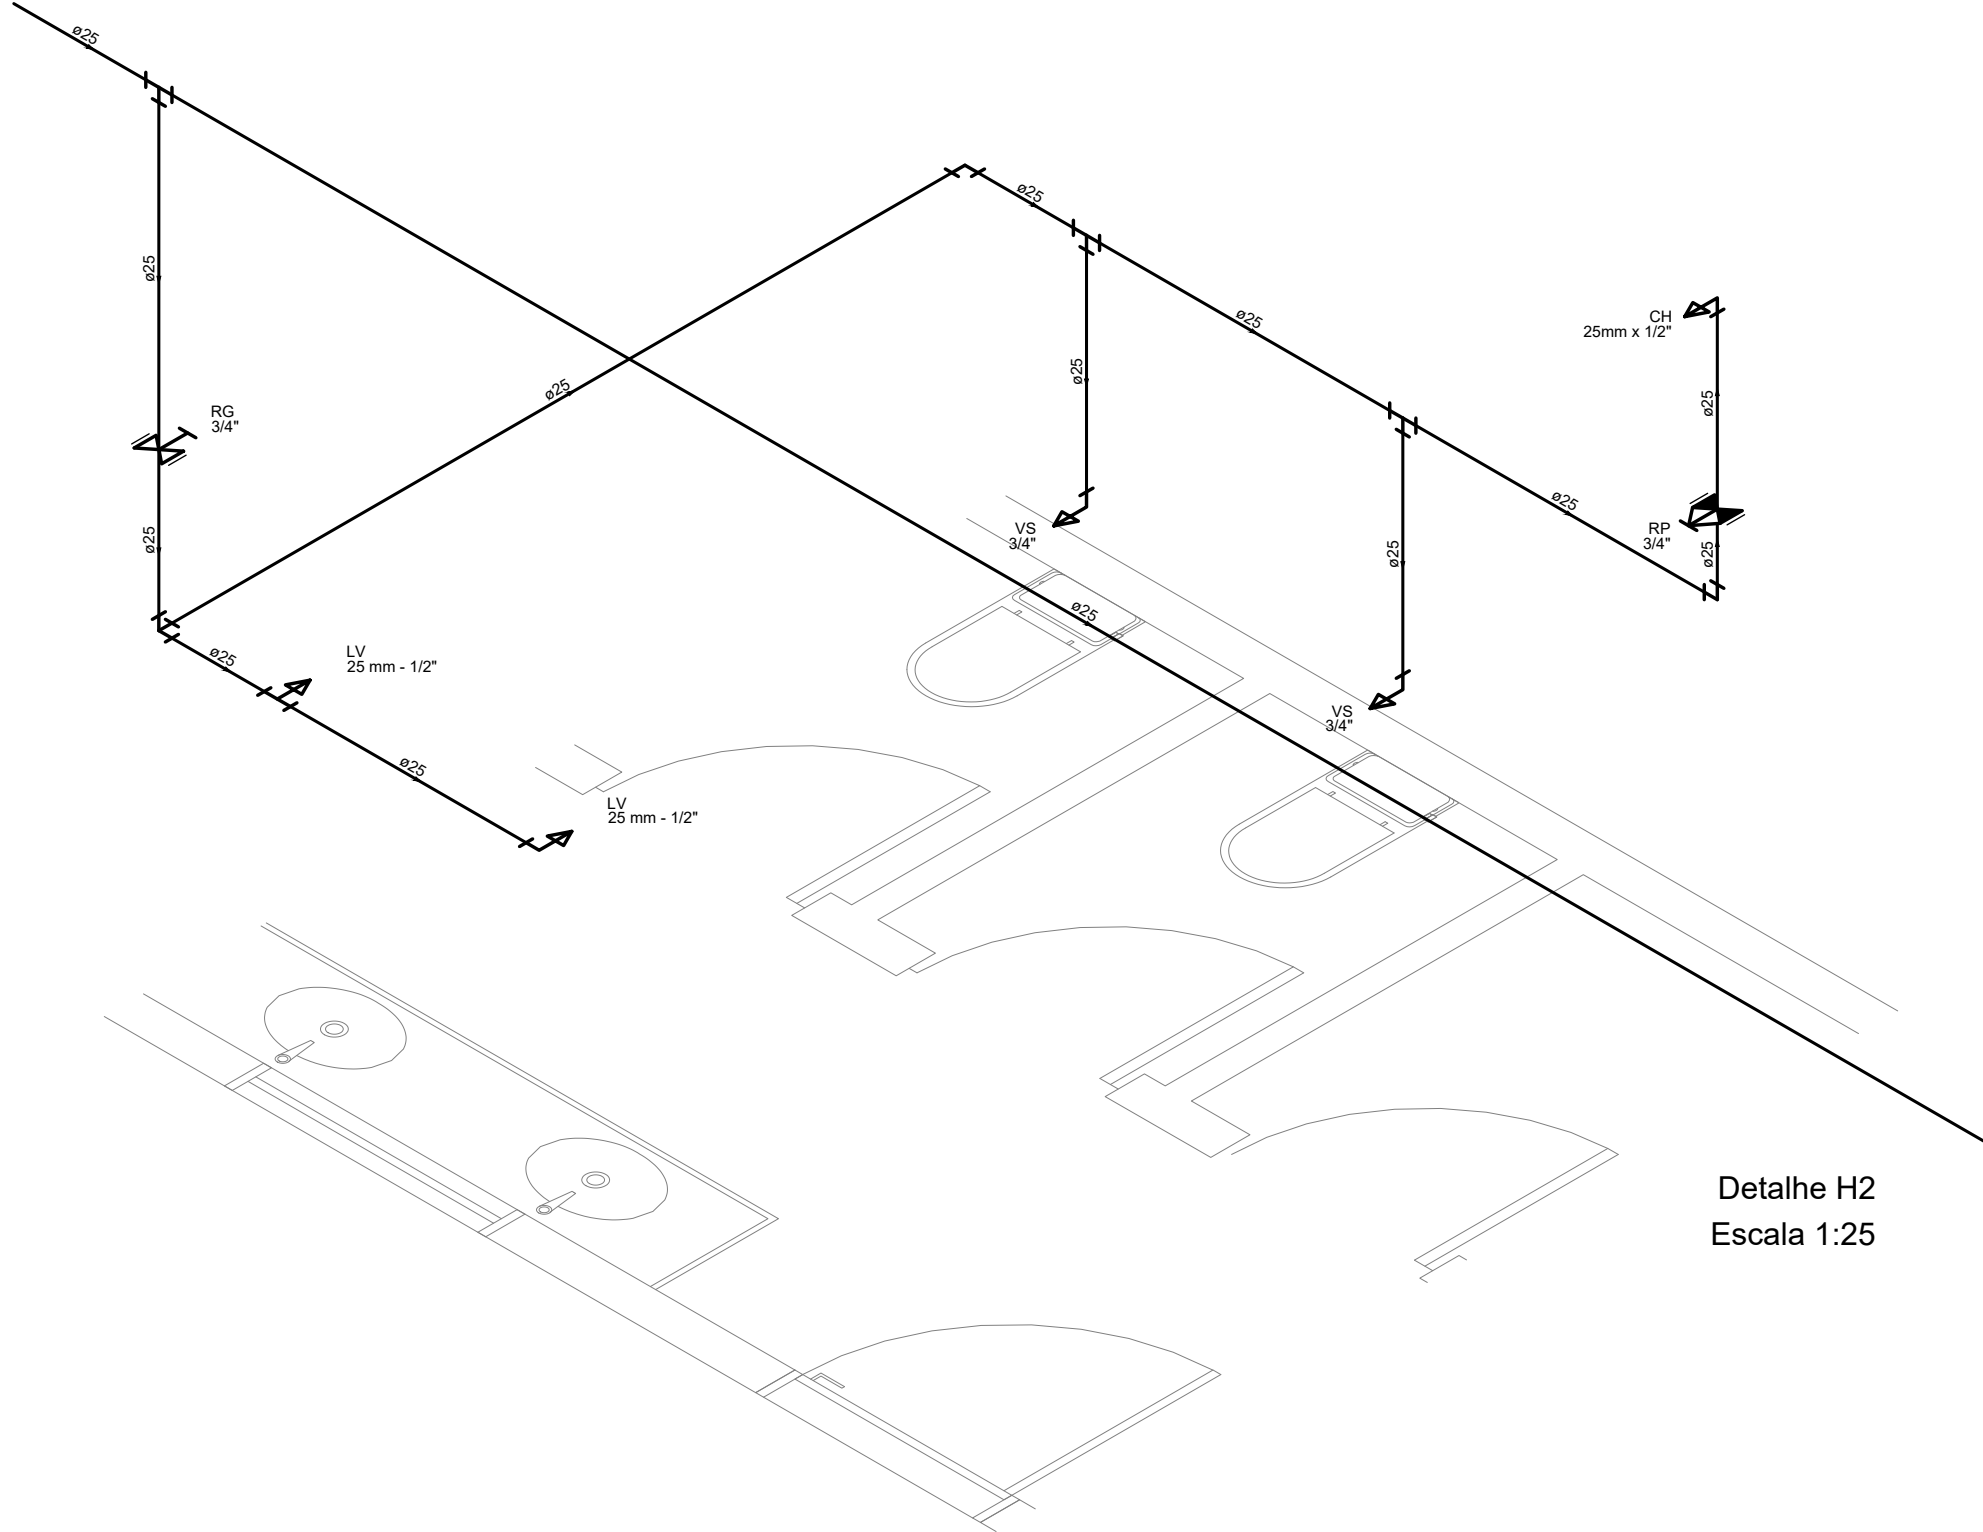

Detalhe H2
Escala 1:25

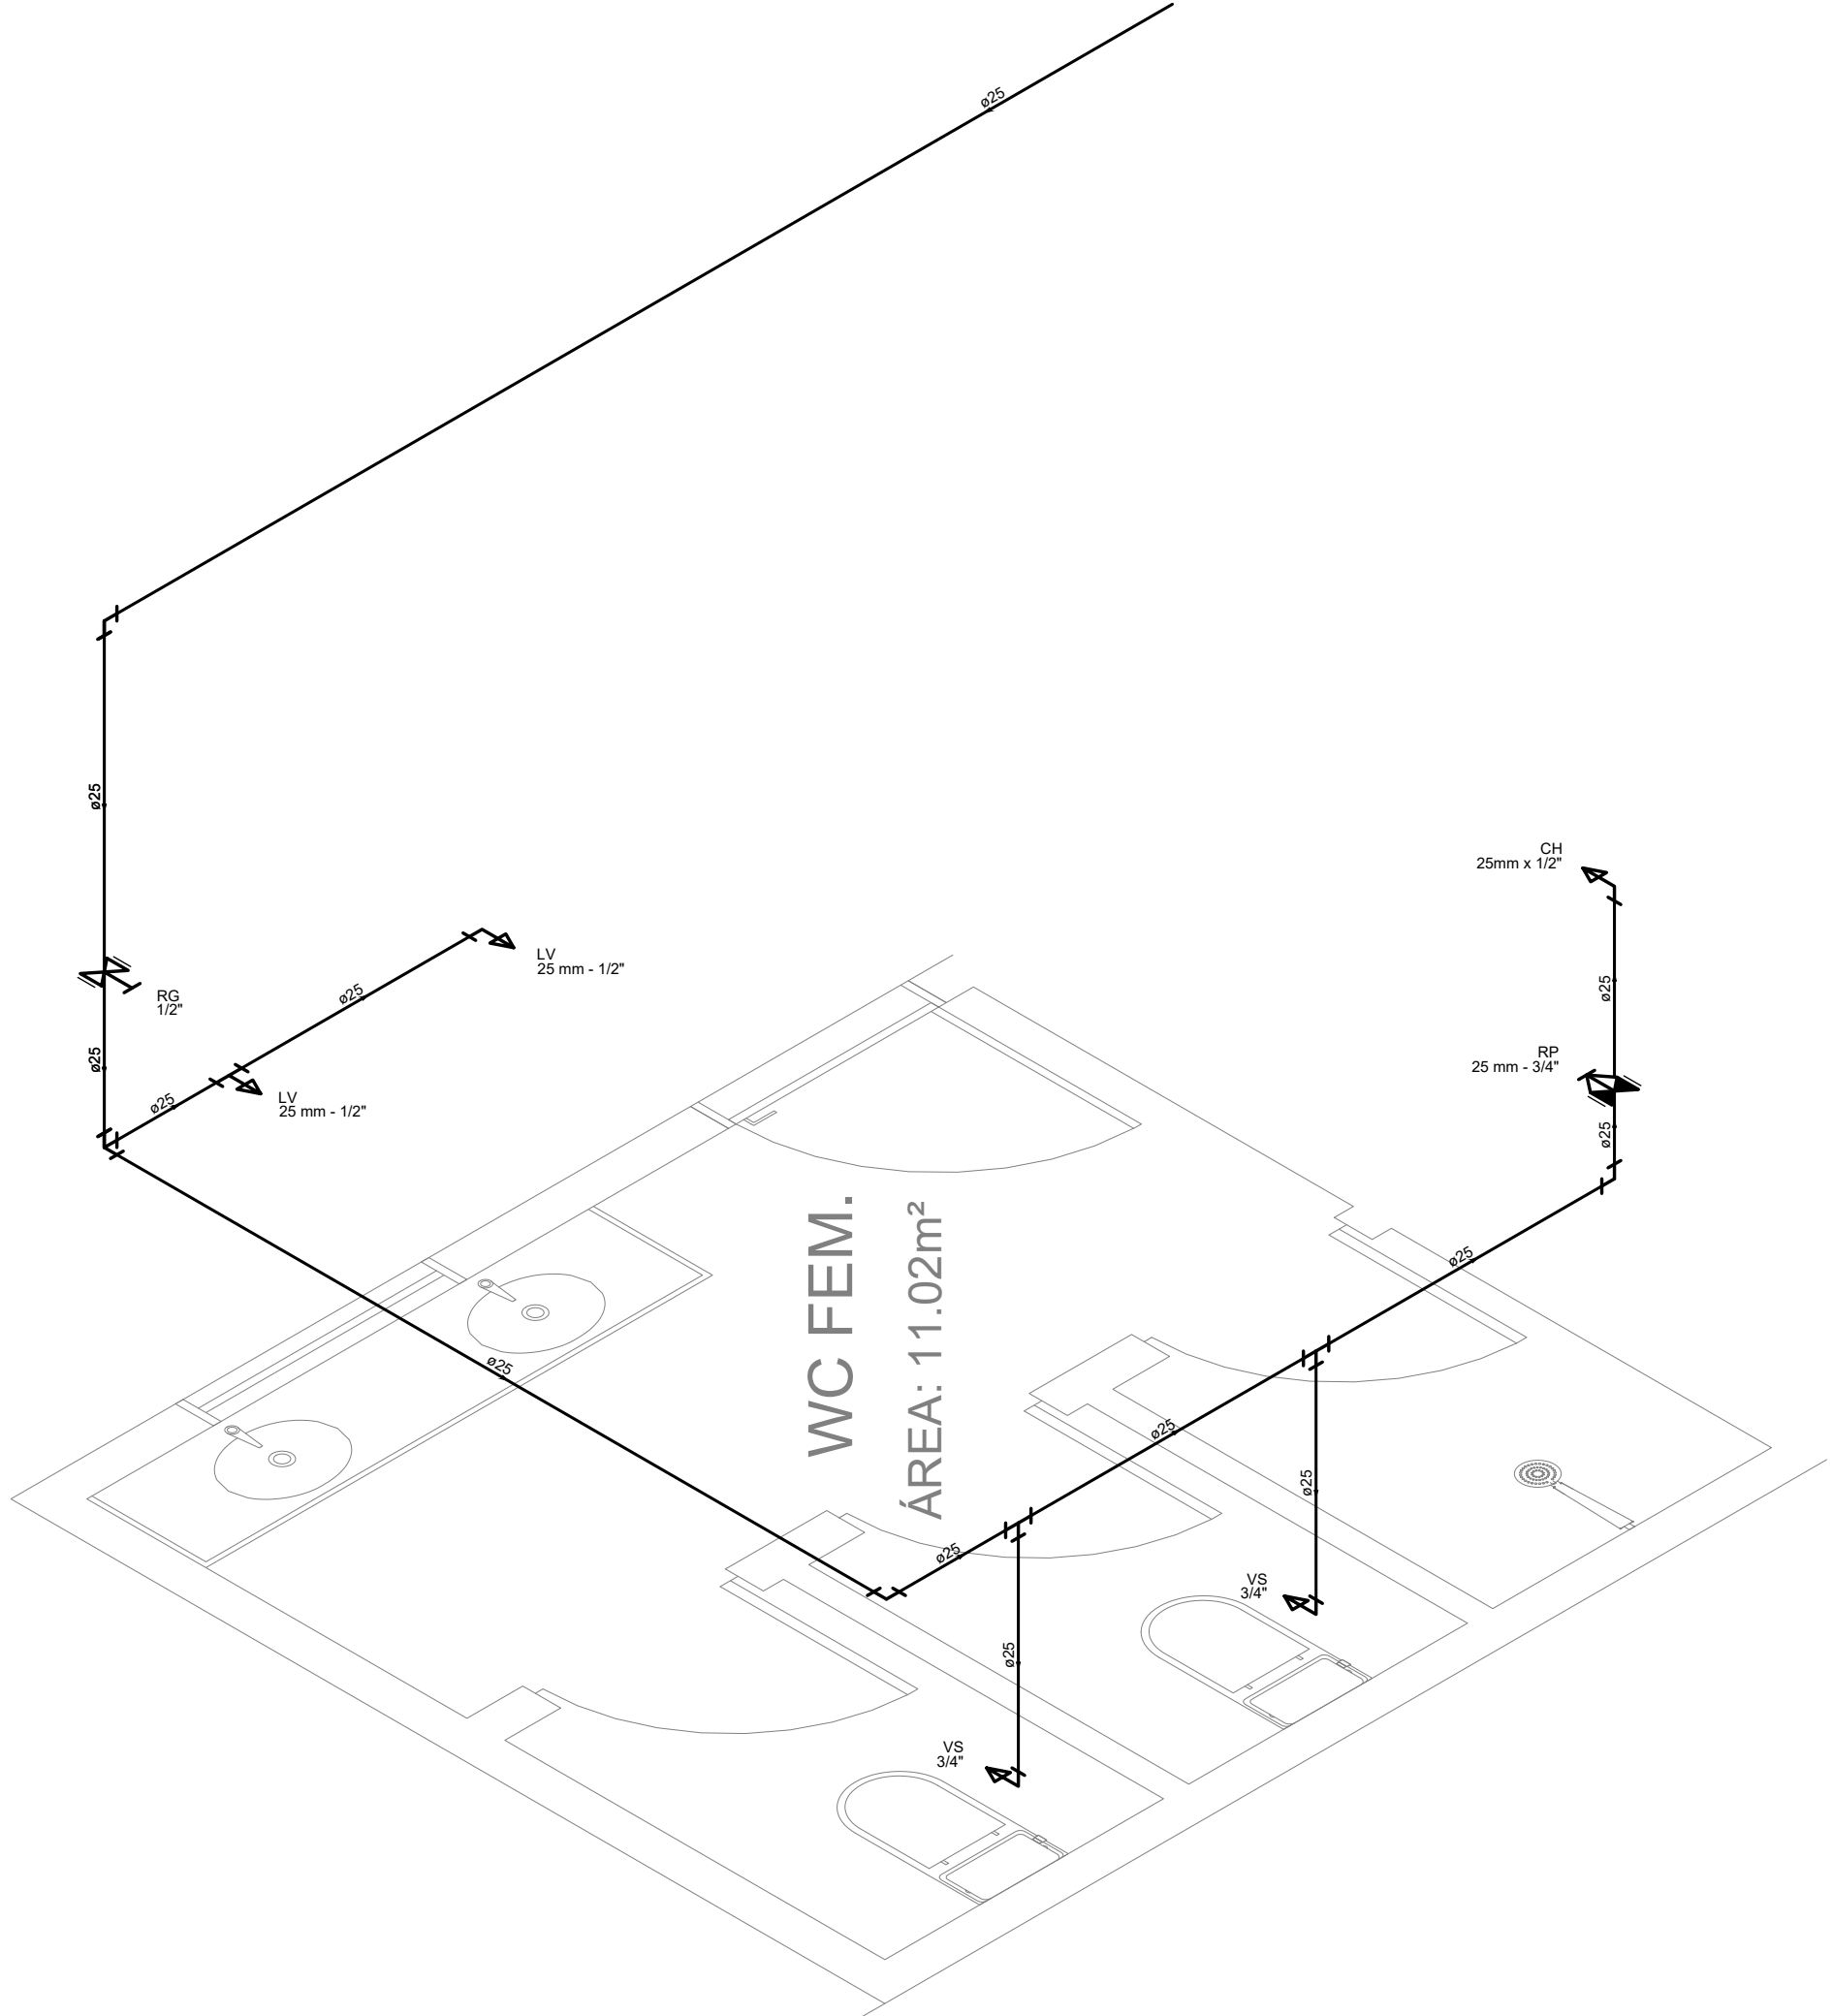

Detalhe H3
Escala 1:25

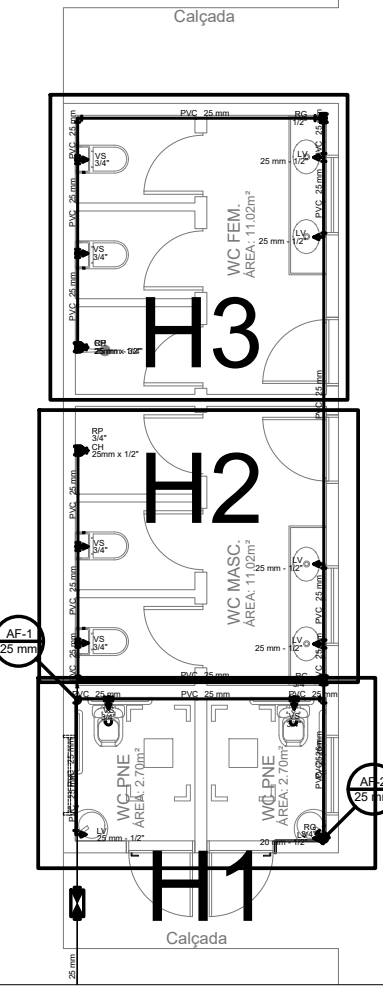

PROPRIETÁRIO: PREFEITURA MUNICIPAL DE COREMAS - PB

LINCOLN CARTAXO DE LIRA JÚNIOR:06897861405 Assinado de forma digital por LINCOLN CARTAXO DE LIRA JÚNIOR:06897861405
Dados: 2025.08.08 13:35:09 -03'00'

PROJETO: LINCOLN CARTAXO DE LIRA JÚNIOR CREA 160.814.689-8

FOLHA

02/02

PROJETO:

CONVENIENTE:

CONVENIADO:

LOCALIDADE:

CONSTRUÇÃO DE GINÁSIO POLIESPORTIVO

PREFEITURA MUNICIPAL DE COREMAS - PB

MUNICÍPIO DE COREMAS - PB

COREMAS - PB

DESENHO	DATA	RESPONSÁVEL	RUBRICA	DADOS
CÓPIA	AGO/2025	LINCOLN CARTAXO		CREA 160.814.689-8
VISTO				

ESCALAS

INDICADO

DESENHOS

- PROJETO HIDRÁULICO

DETALHE H1

DETALHE H2

DETALHE H3

CONVÊNIO

ARQUIVO

Aprovações:

LCL

PROJETOS

Av. Gov. Flavio R. Coutinho, 500, sl. 601

Jd. Osonaria, 58037-905 - João Pessoa (PB)

Tel +55 (83) 99624.4447

e-mail: lclprojetos@hotmail.com