


A

A

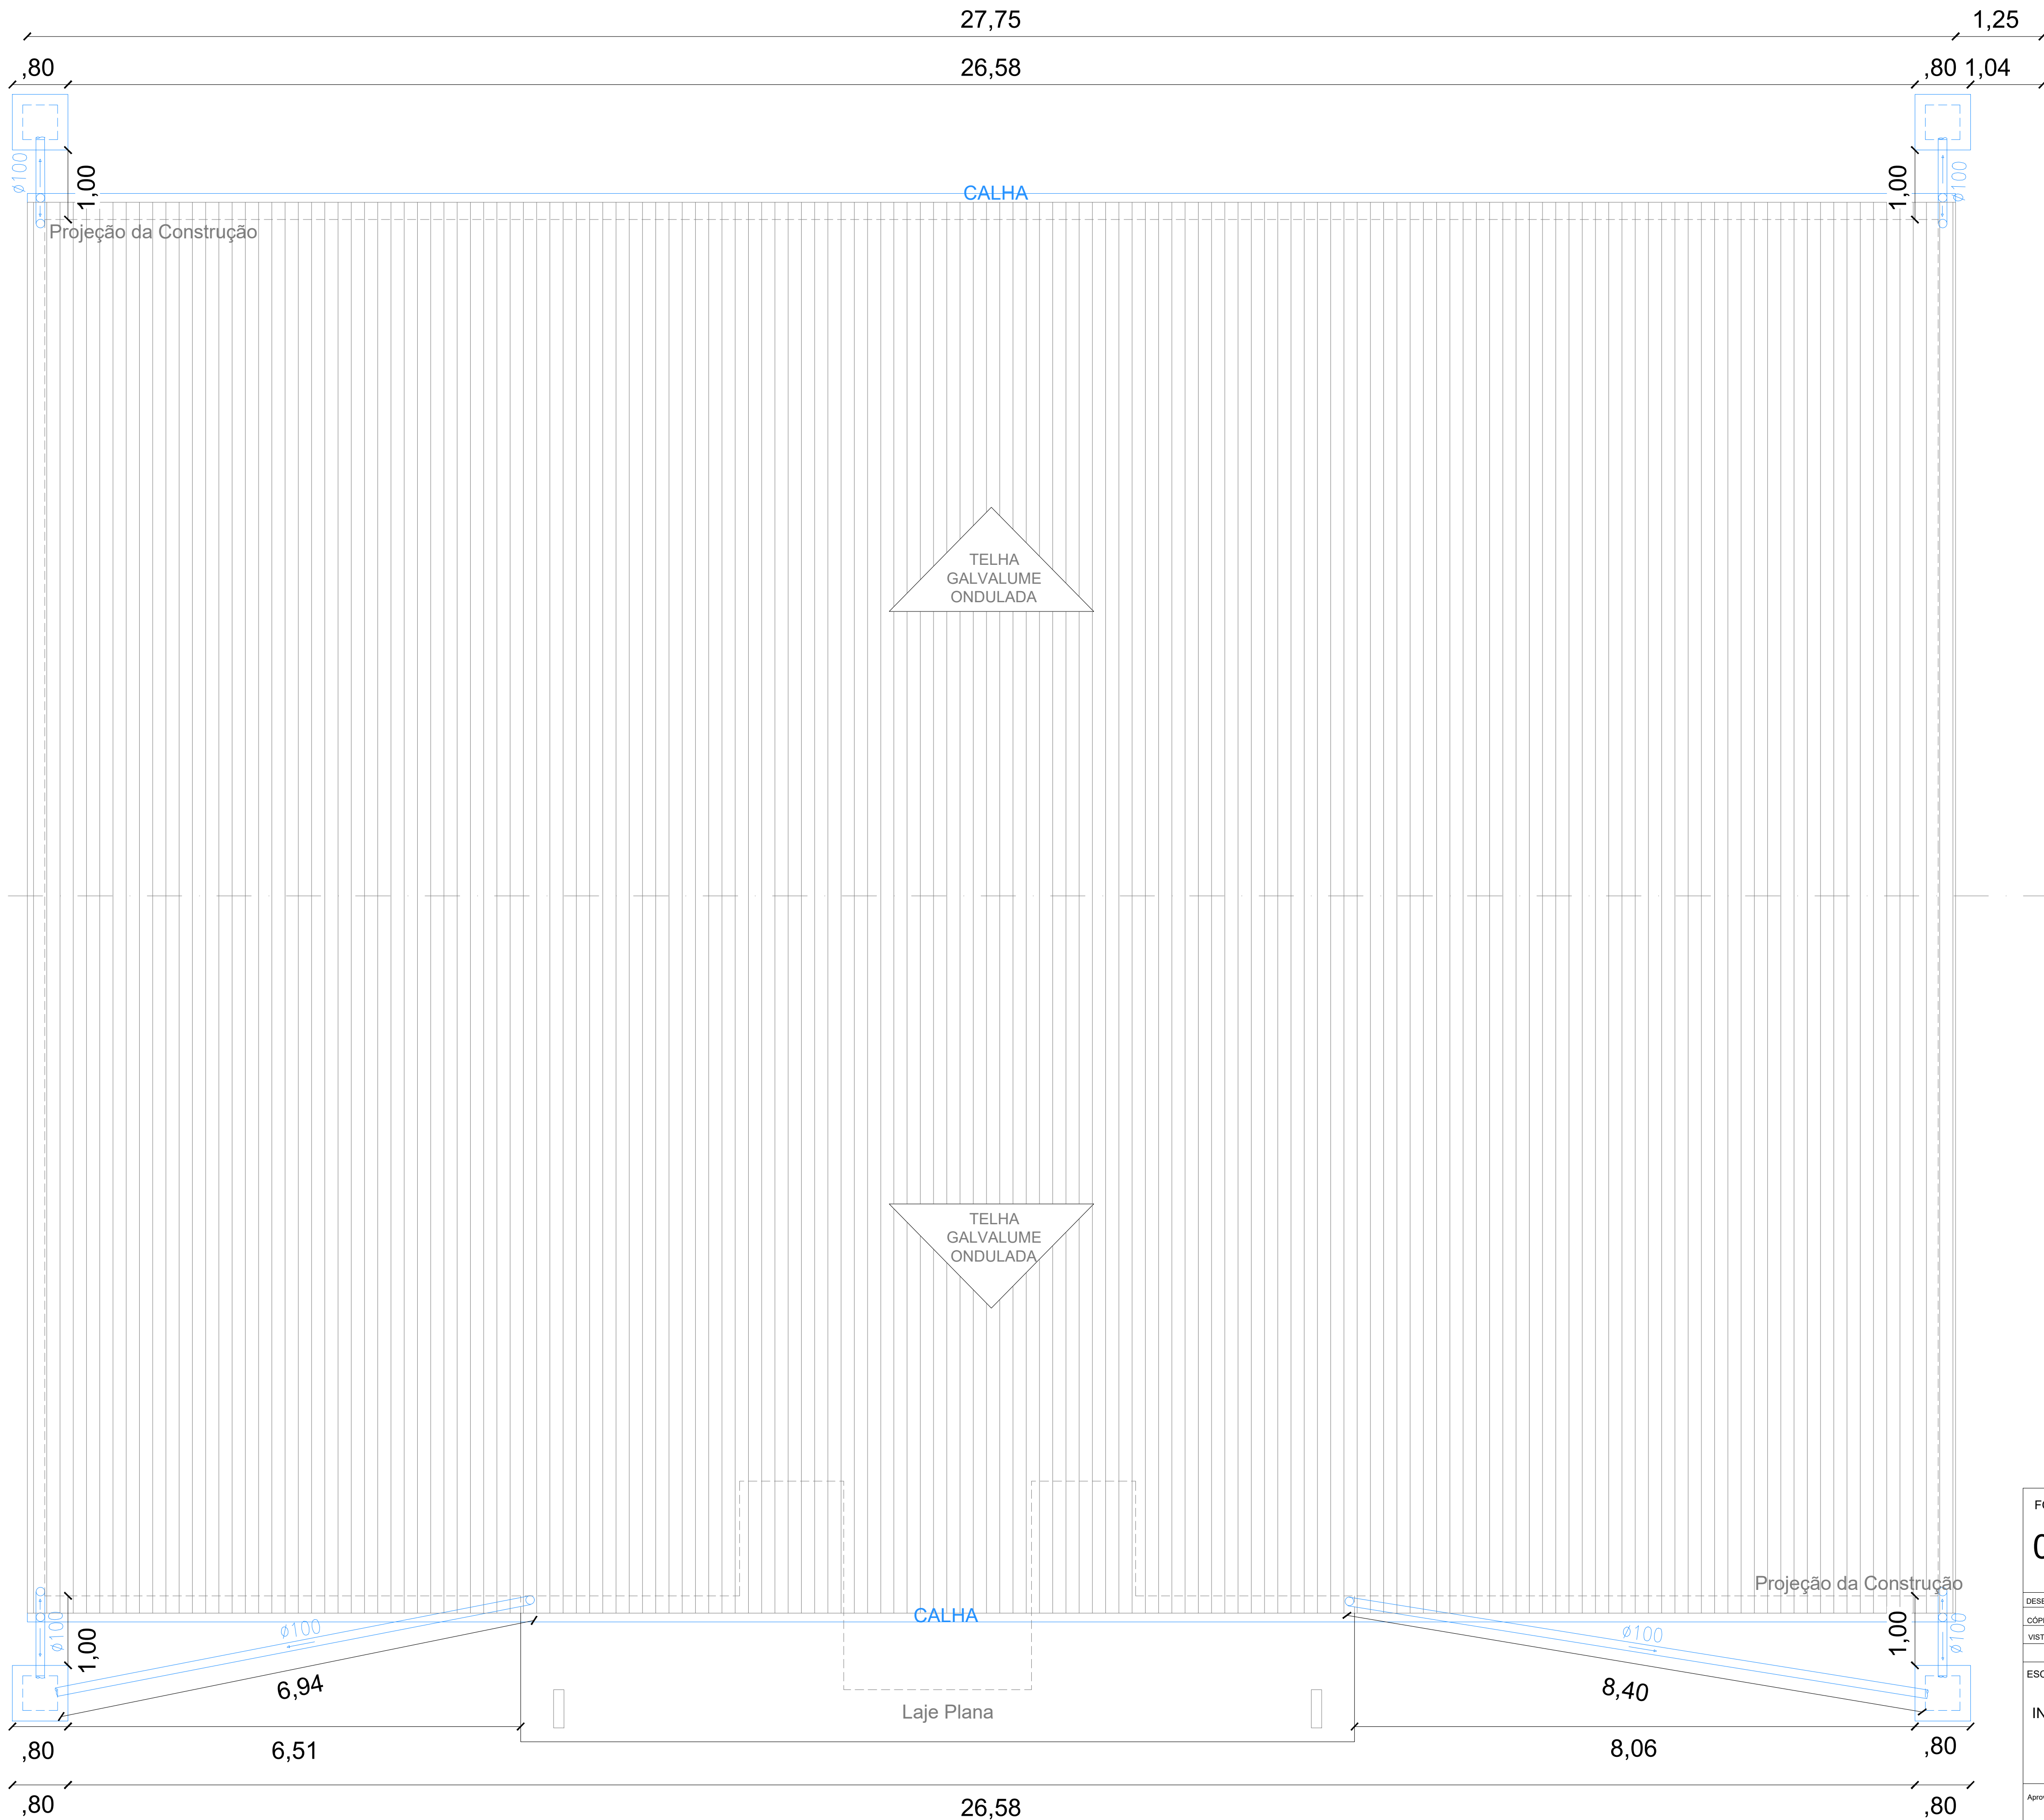

PROPRIETÁRIO: PREFEITURA MUNICIPAL DE COREMAS - PB
Assinado de forma digital por
LINCOLN CARTAXO DE LIRA JUNIOR:06897861405
Assinado em 2025.08.08 12:27:59 -03'00'
Dados: 2025.08.08 12:27:59 -03'00'

PROJETO: LINCOLN CARTAXO DE LIRA JÚNIOR CREA 160.814.689-8


FOLHA		PROJETO: CONSTRUÇÃO DE QUADRA POLIESPORTIVA		
01/02		CONVENIENTE: PREFEITURA MUNICIPAL DE COREMAS - PB		
		CONVENIADO: MUNICIPIO DE COREMAS - PB		
		LOCALIDADE: COREMAS - PB		
DESENHO	DATA	RESPONSÁVEL	RUBRICA	DADOS
CÓPIA	AGO/2025	LINCOLN CARTAXO		CREA 160.814.689-8
VISTO				
ESCALAS		DESENHOS		CONVÊNIO
INDICADO		PROJETO DE COLETA E DESTINAÇÃO DAS ÁGUAS PLUVIAIS		GOVERNO DO ESTADO
				ARQUIVO
Aprovações:				
 LCL PROJETOS Av. Gov. Flavio R. Coutinho, 500, sl. 601 Jd. Oceania, 58037-005 - João Pessoa (PB) Tel +55 (83) 99924.4447 e-mail: lclprojetos@hotmail.com				



Av. Gov. Flavio R. Coutinho, 500, sl. 601
Jd. Oceania, 58037-005 - João Pessoa (PB)
Tel: +55 (83) 99924-4447
e-mail: lclprojetos@hotmail.com

Projeto de coleta e detinação das águas pluviais
Escala 1/50

Nota: Considerar inclinação de 0,5% na regularização das lajes impermeabilizadas.

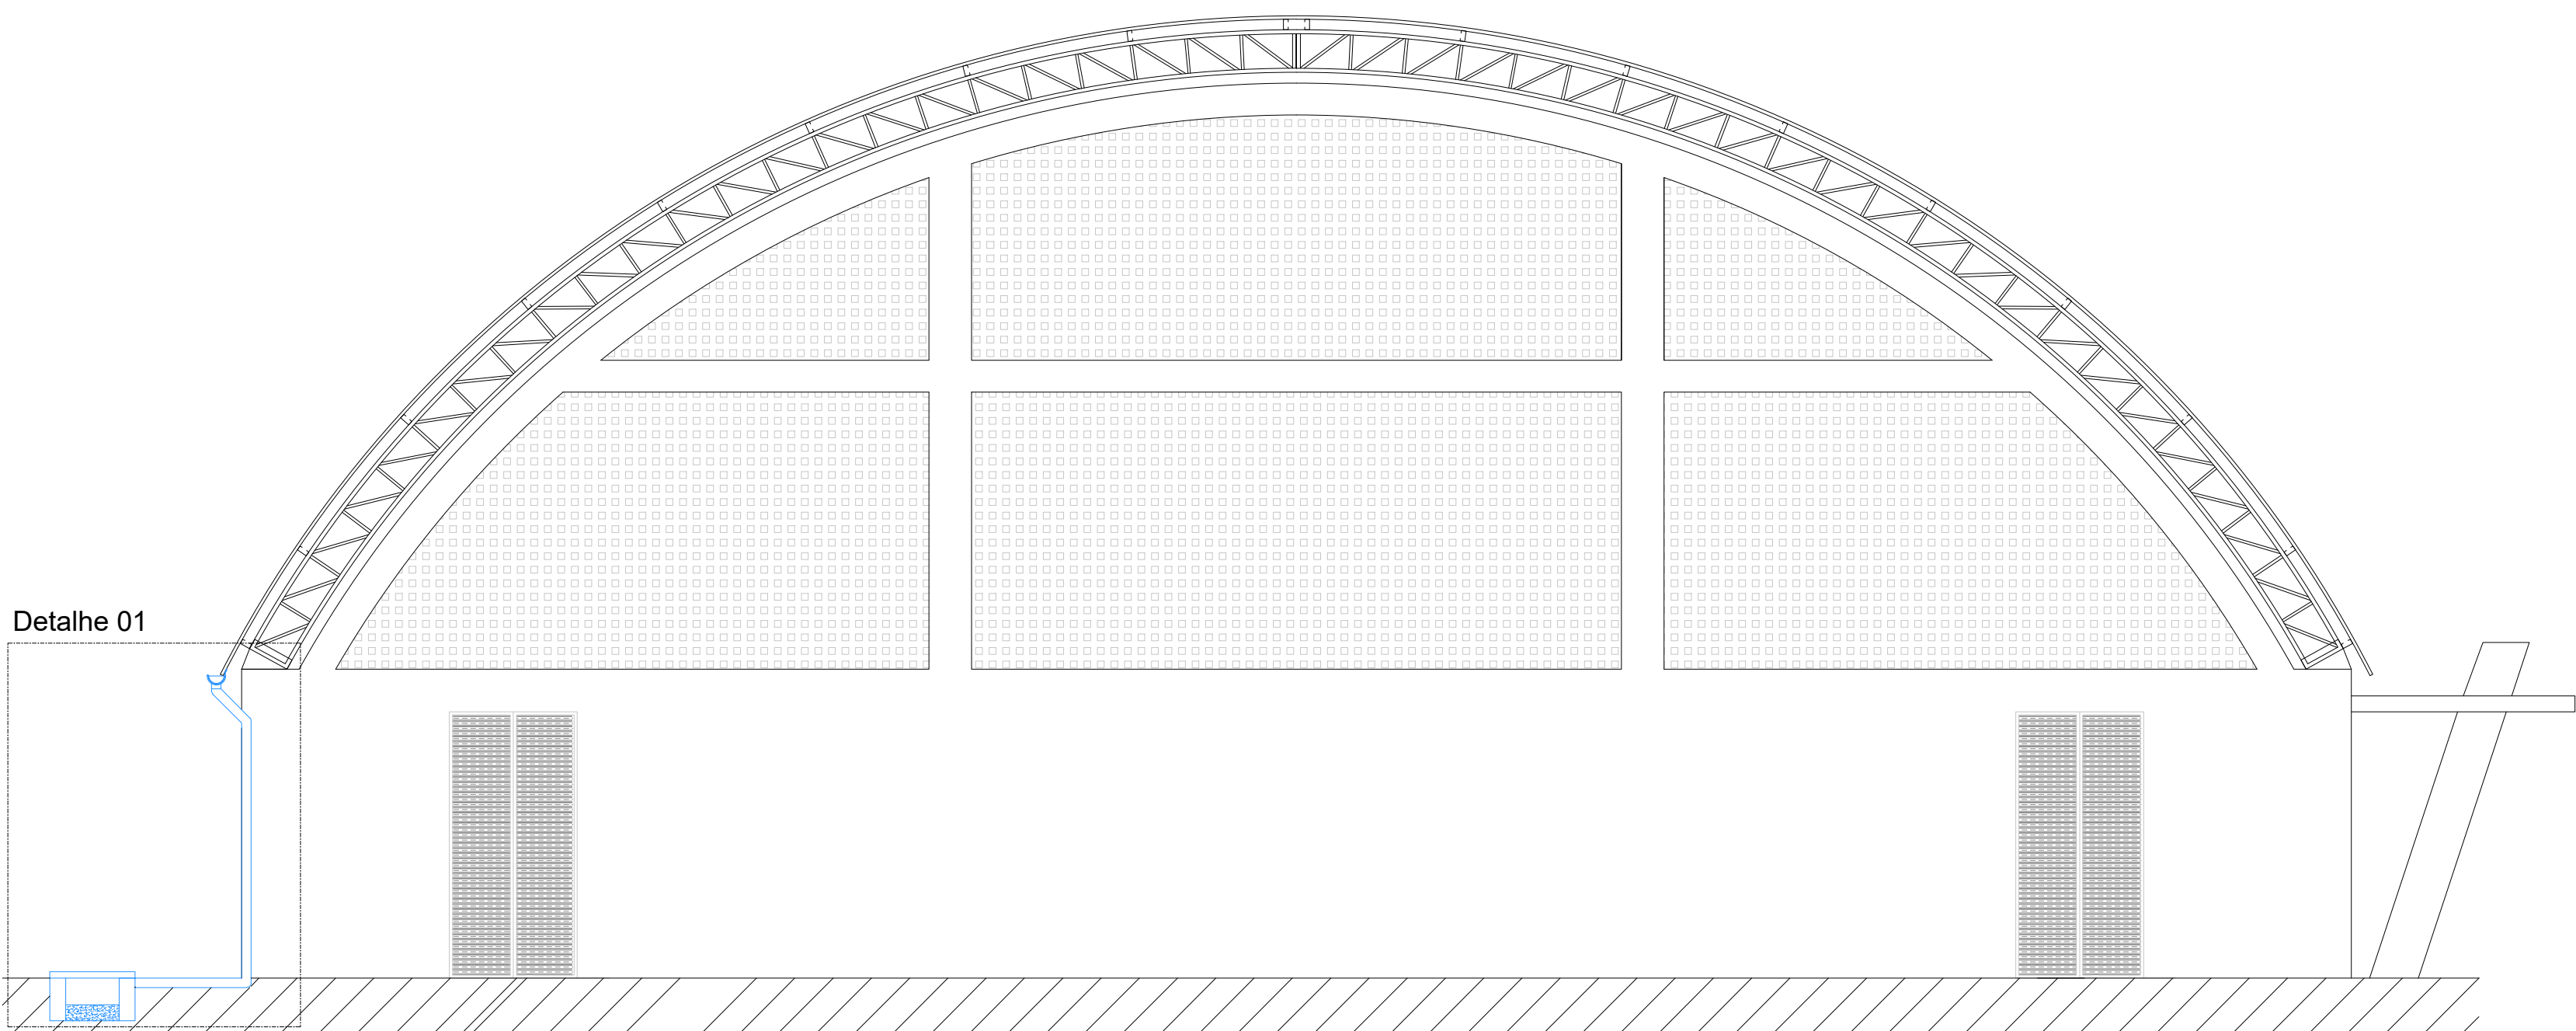

FACHADA

Escala _____ SEM

Suporte de calha em PVC

Calha semicircular de PVC Ø 125 mm


Joelho 45° Ø 100 mm

Joelho 45° Ø 100 mm

Condutor vertical PVC Ø100 mm


Joelho 90° Ø 100 mm

Caixa pluvial com fundo de brita

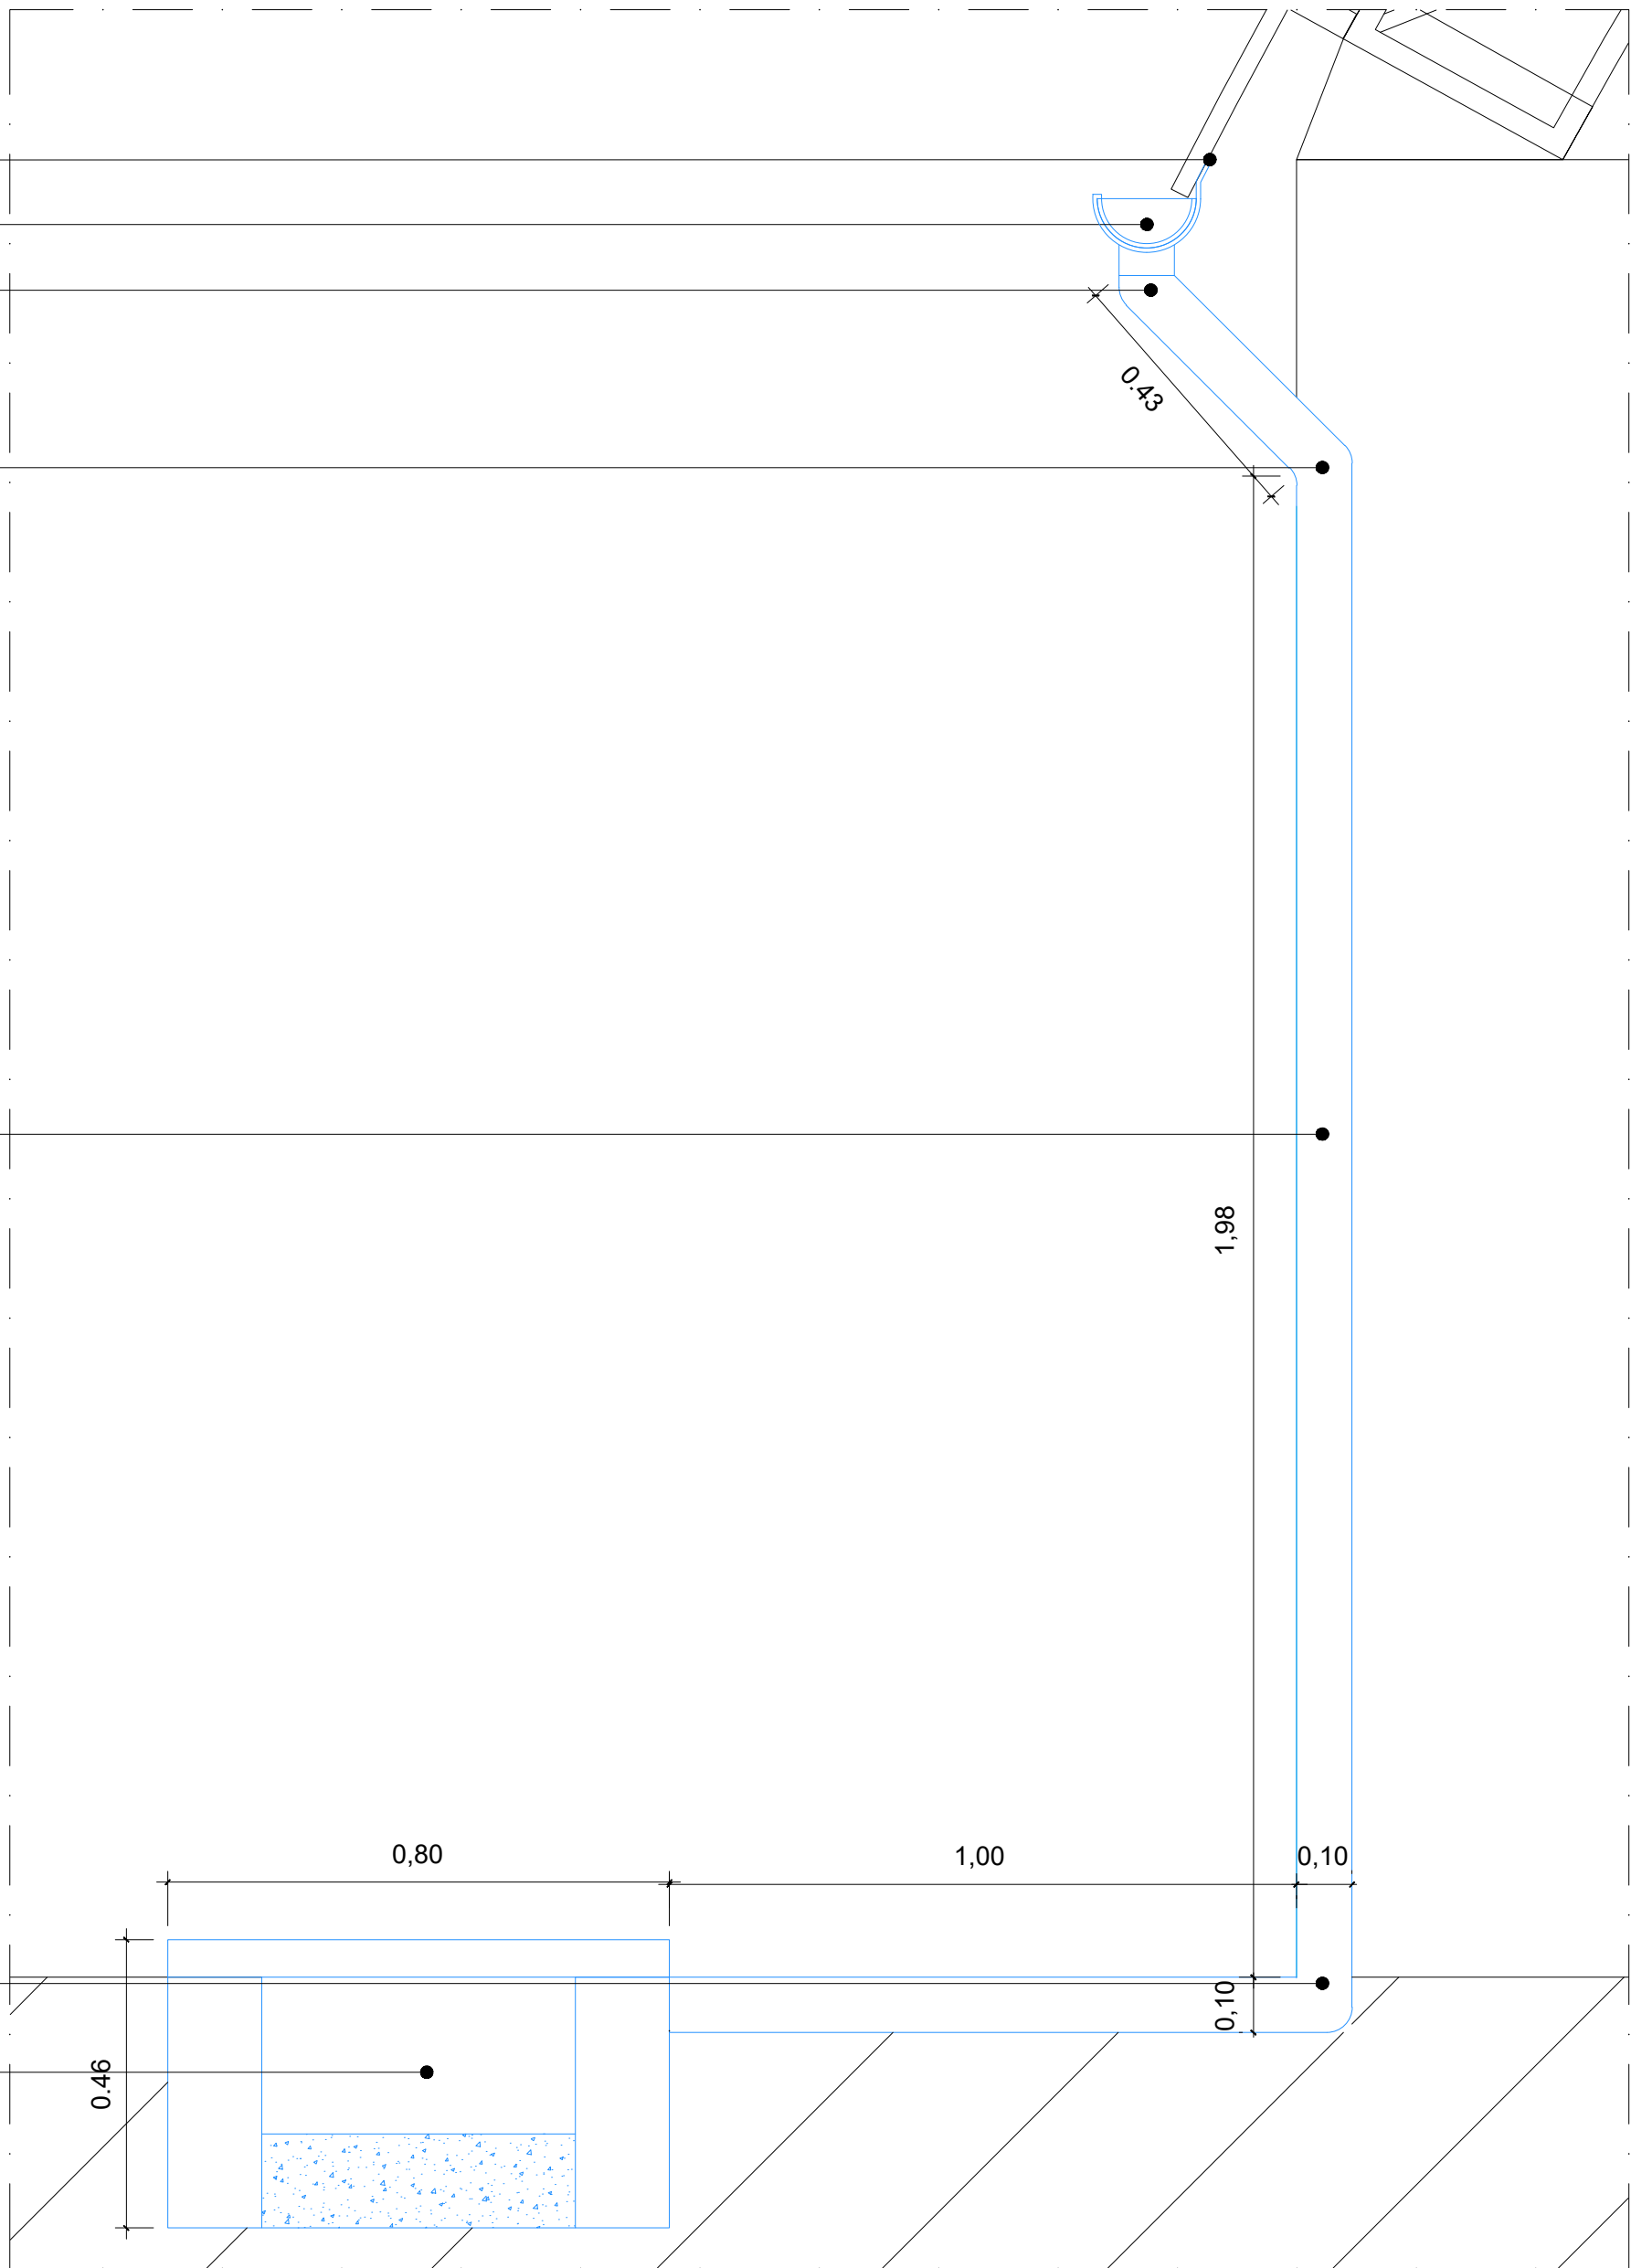


Detalhe 01

Escala _____ SEM

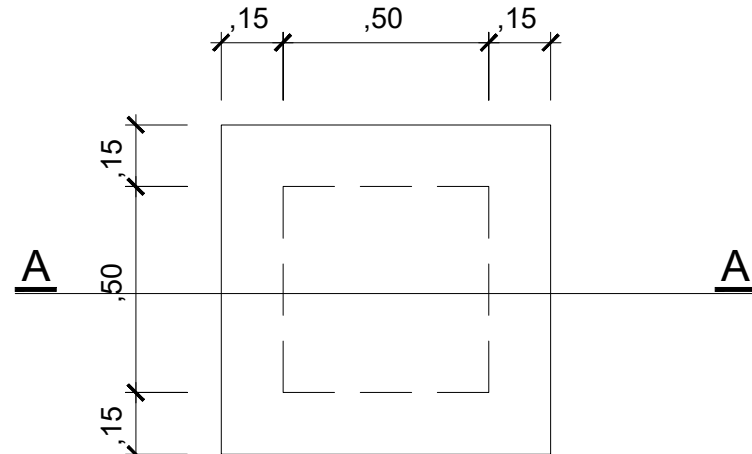

PLANTA BAIXA

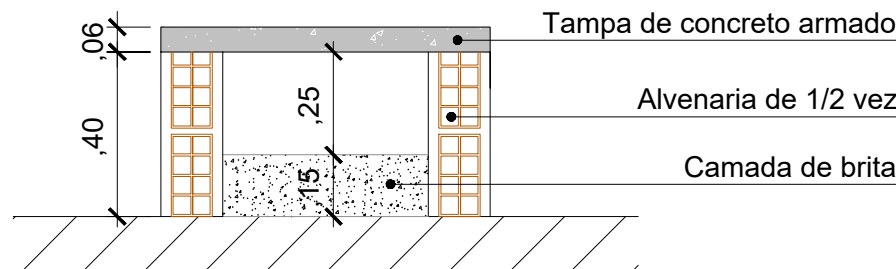

CORTE AA

Detalhe 02 - Caixa pluvial com fundo de brita

Escala _____ SEM

PROPRIETÁRIO: PREFEITURA MUNICIPAL DE COREMAS - PB
LINCOLN CARTAXO DE LIRA JUNIOR:06897861405
Assinado de forma digital por LINCOLN CARTAXO DE LIRA JUNIOR:06897861405
Dados: 2025.08.08 12:27:40 -03'00'

PROJETO: LINCOLN CARTAXO DE LIRA JÚNIOR CREA 160.814.689-8

FOLHA		PROJETO: CONSTRUÇÃO DE QUADRA POLIESPORTIVA		
02/02		CONVENIENTE: PREFEITURA MUNICIPAL DE COREMAS - PB		
		CONVENIADO: MUNICIPIO DE COREMAS - PB		
		LOCALIDADE: COREMAS - PB		
DESENHO	DATA	RESPONSÁVEL	RUBRICA	DADOS
CÓPIA	AGO/2025	LINCOLN CARTAXO		CREA 160.814.689-8
VISTO				
ESCALAS	DESENHOS			CONVÊNIO
	FACHADA DETALHE DA COLETA DE ÁGUAS PLUVIAIS			GOVERNO DO ESTADO
				ARQUIVO
Aprovações:				



LCL PROJETOS

Av. Gov. Flavio R. Coutinho, 500, sl. 601
Jd. Oceania, 58037-005 - João Pessoa (PB)
Tel +55 (83) 99924 4447
e-mail: lclprojetos@hotmail.com