

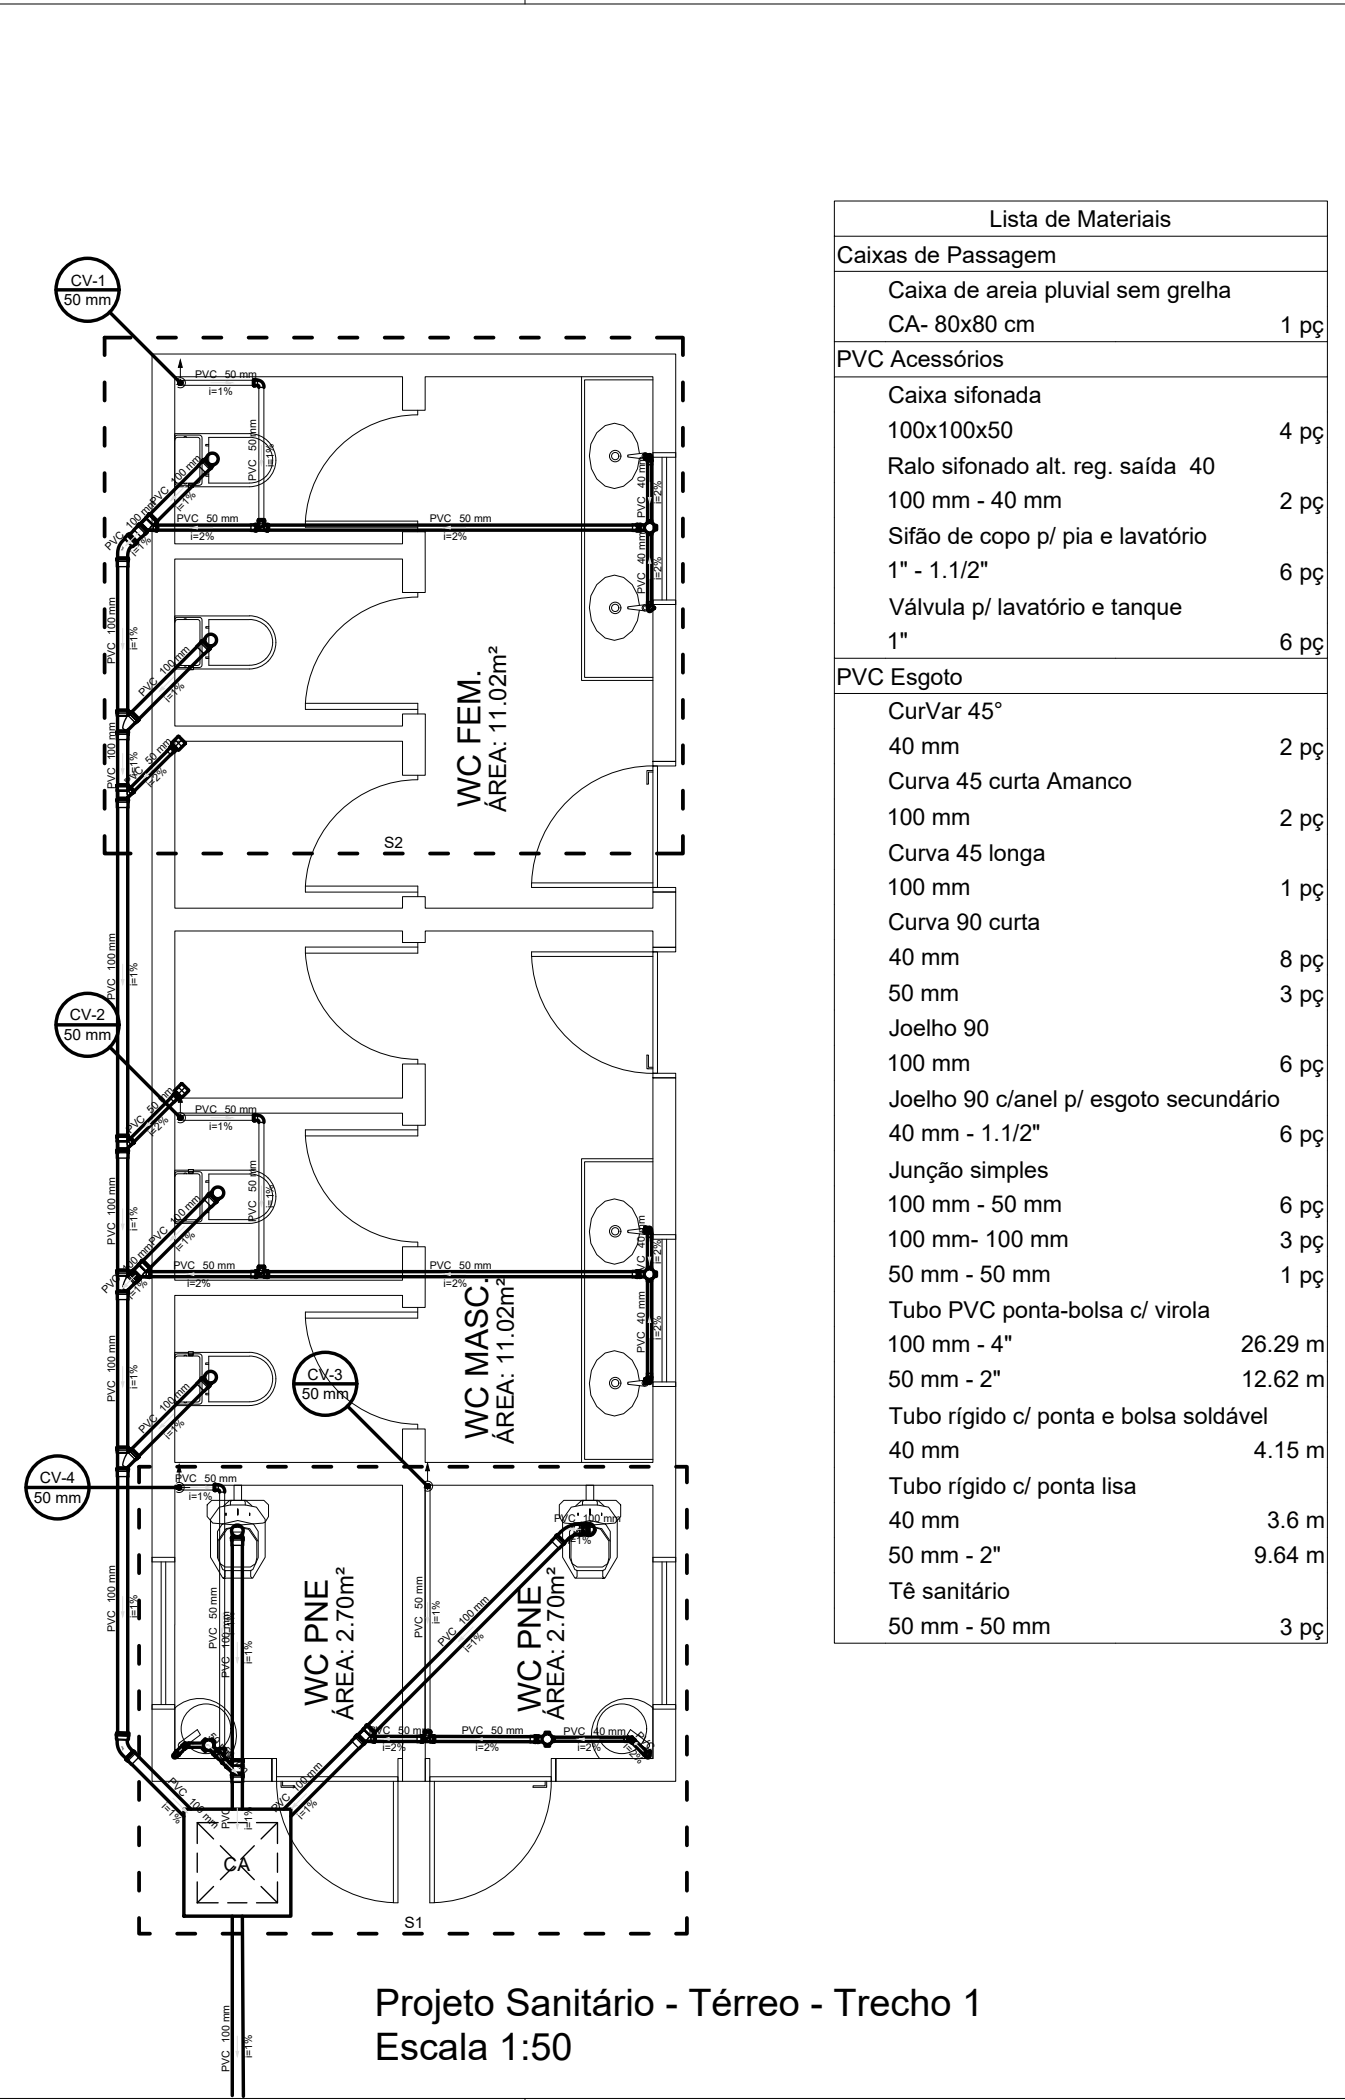


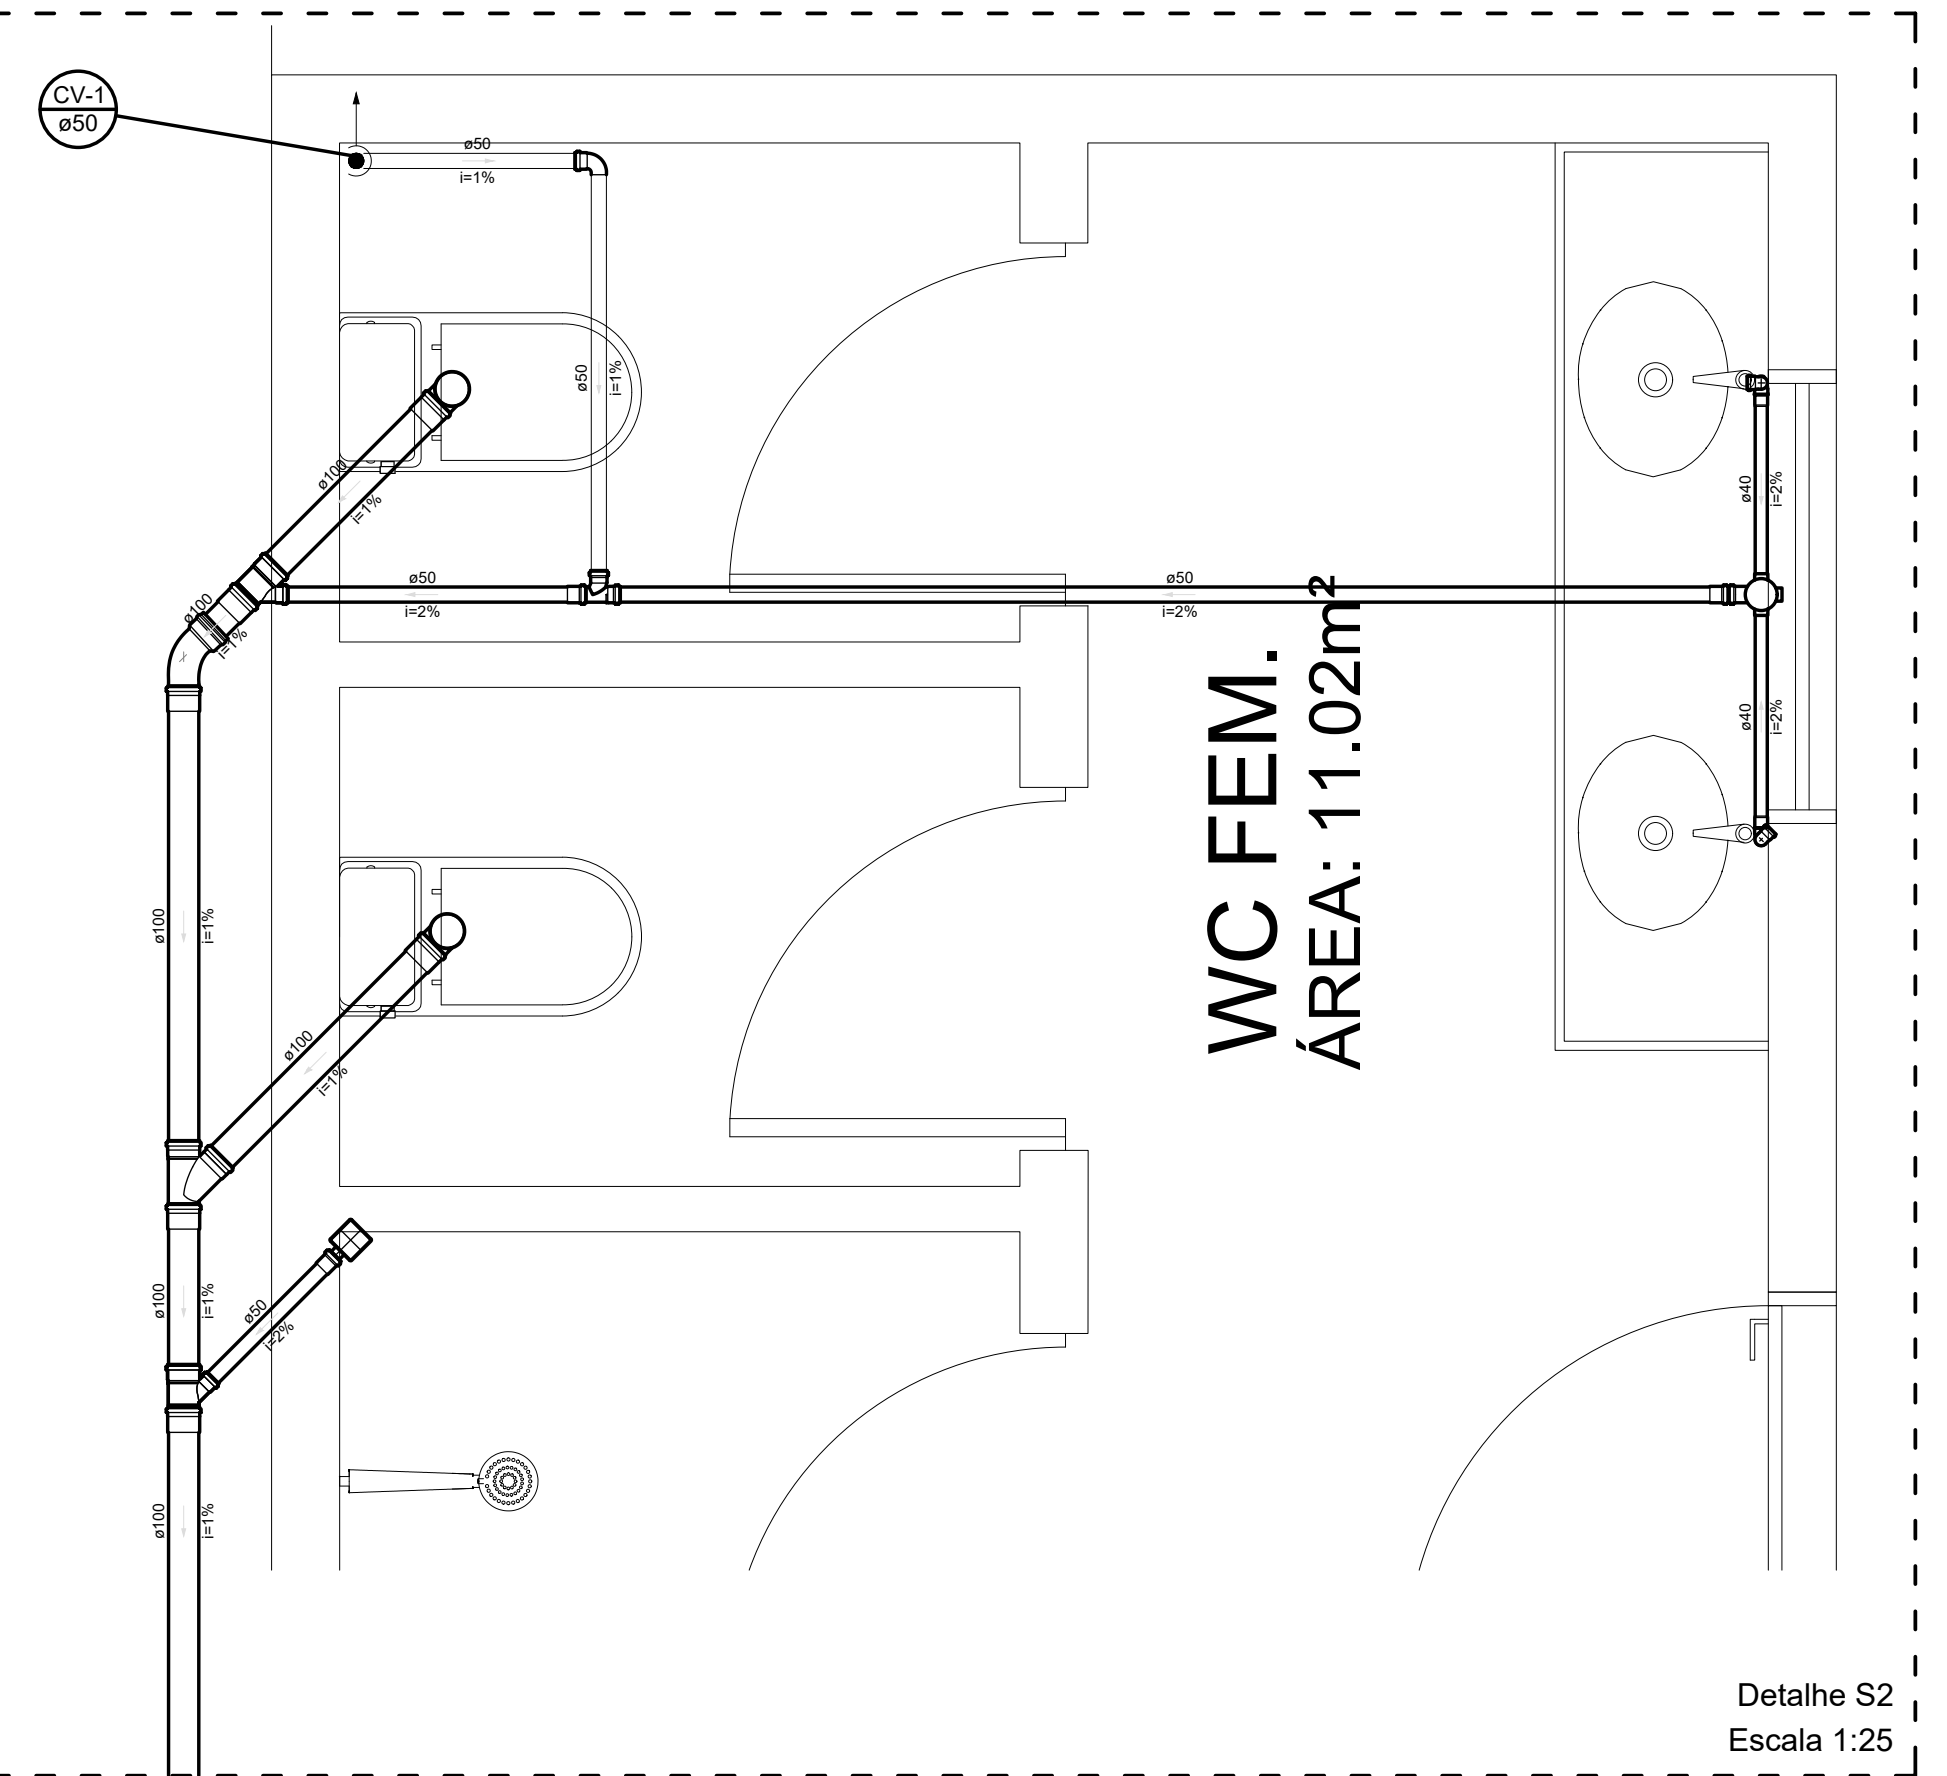

| Lista de Materiais                                      |         |
|---------------------------------------------------------|---------|
| Caixas de Passagem                                      |         |
| Caixa de areia pluvial sem grelha<br>CA- 80x80 cm       | 1 pç    |
| PVC Acessórios                                          |         |
| Caixa sifonada<br>100x100x50                            | 4 pç    |
| Ralo sifonado alt. reg. saída 40<br>100 mm - 40 mm      | 2 pç    |
| Sifão de copo p/ pia e lavatório<br>1" - 1.1/2"         | 6 pç    |
| Válvula p/ lavatório e tanque<br>1"                     | 6 pç    |
| PVC Esgoto                                              |         |
| CurVar 45°<br>40 mm                                     | 2 pç    |
| Curva 45 curta Amanco<br>100 mm                         | 2 pç    |
| Curva 45 longa<br>100 mm                                | 1 pç    |
| Curva 90 curta<br>40 mm                                 | 8 pç    |
| 50 mm                                                   | 3 pç    |
| Joelho 90<br>100 mm                                     | 6 pç    |
| Joelho 90 c/anel p/ esgoto secundário<br>40 mm - 1.1/2" | 6 pç    |
| Junção simples<br>100 mm - 50 mm                        | 6 pç    |
| 100 mm- 100 mm                                          | 3 pç    |
| 50 mm - 50 mm                                           | 1 pç    |
| Tubo PVC ponta-bolsa c/ virola<br>100 mm - 4"           | 26.29 m |
| 50 mm - 2"                                              | 12.62 m |
| Tubo rígido c/ ponta e bolsa soldável<br>40 mm          | 4.15 m  |
| Tubo rígido c/ ponta lisa<br>40 mm                      | 3.6 m   |
| 50 mm - 2"                                              | 9.64 m  |
| Tê sanitário<br>50 mm - 50 mm                           | 3 pç    |

| Legenda                              |                                |
|--------------------------------------|--------------------------------|
| CA                                   | Caixa Sifonada                 |
| CA                                   | Caixa de areia pluvial simples |
| Chuveiro Coletivo                    |                                |
| CurVar 45°                           |                                |
| Curva 45 Longa para Esgoto Sanitário |                                |
| Curva 45° curta Amanco               |                                |
| Curva 90 curta                       |                                |
| Junção simples                       |                                |
| Lavatório Residencial com sifão      |                                |
| Lavatório de Uso Geral               |                                |
| Tê sanitário                         |                                |
| Vaso Sanitário c/ J90°               |                                |

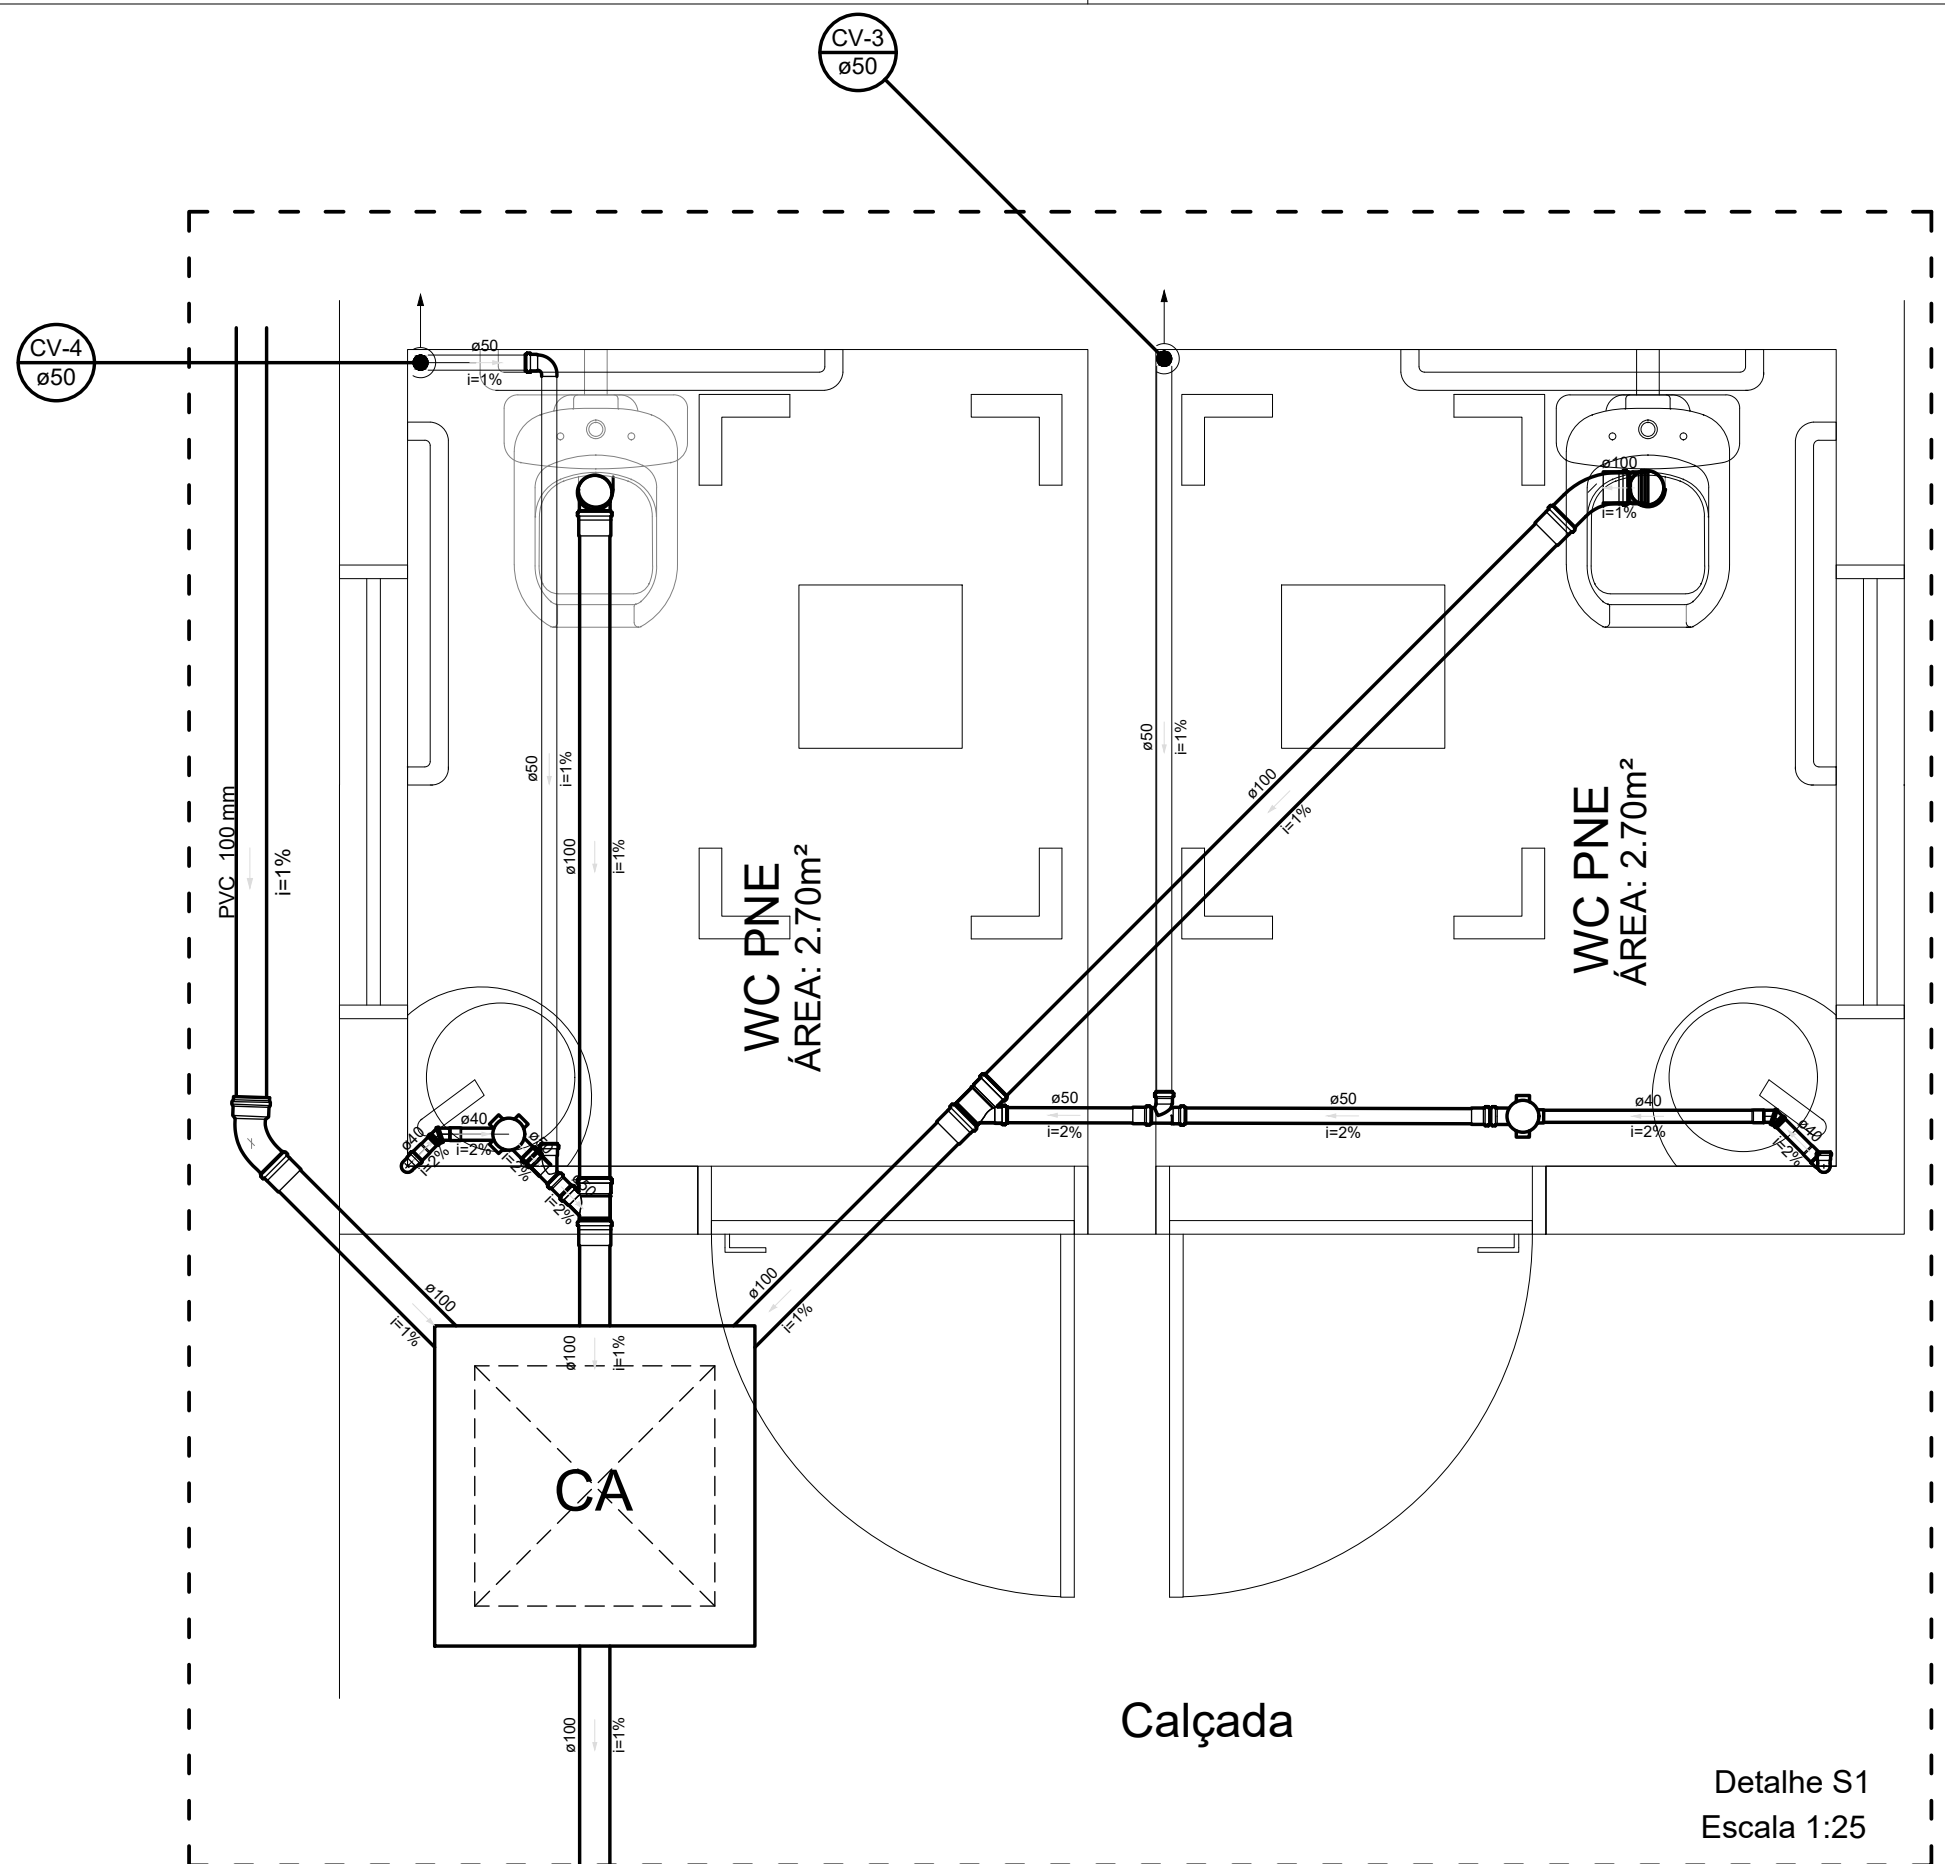

| Lista de Materiais                      |        |
|-----------------------------------------|--------|
| PVC Esgoto                              |        |
| Terminal de ventilação<br>50 mm         | 4 pç   |
| Tubo rígido c/ ponta lisa<br>50 mm - 2" | 12.4 m |
| Legenda                                 |        |
| Terminal de ventilação- coluna          |        |

Projeto Sanitário - Coberta - Trecho 1  
Escala 1:50

PROPRIETÁRIO: PREFEITURA MUNICIPAL DE COREMAS - PB

PROJETO: LINCOLN CARTAXO DE LIRA JÚNIOR CREA 160.814.689-8

CONSTRUÇÃO:

FOLHA  
01/01  
PROJETO: CONSTRUÇÃO DE GINÁSIO POLIESPORTIVO  
CONCEDENTE: PREFEITURA MUNICIPAL DE COREMAS - PB  
CONVENIENTE: MUNICÍPIO DE COREMAS - PB  
LOCALIDADE: COREMAS - PB

| DESENHO  | DATA            | RESPONSÁVEL | RUBRICA | DADOS |
|----------|-----------------|-------------|---------|-------|
| AGO/2025 | LINCOLN CARTAXO |             |         |       |

| ESCALAS  | DESENHOS          | CONVÊNIO   |
|----------|-------------------|------------|
|          | Projeto Sanitário | 1082984-07 |
| INDICADA |                   | REVISÃO    |
|          |                   | ARQUIVO    |

Aprovações: