


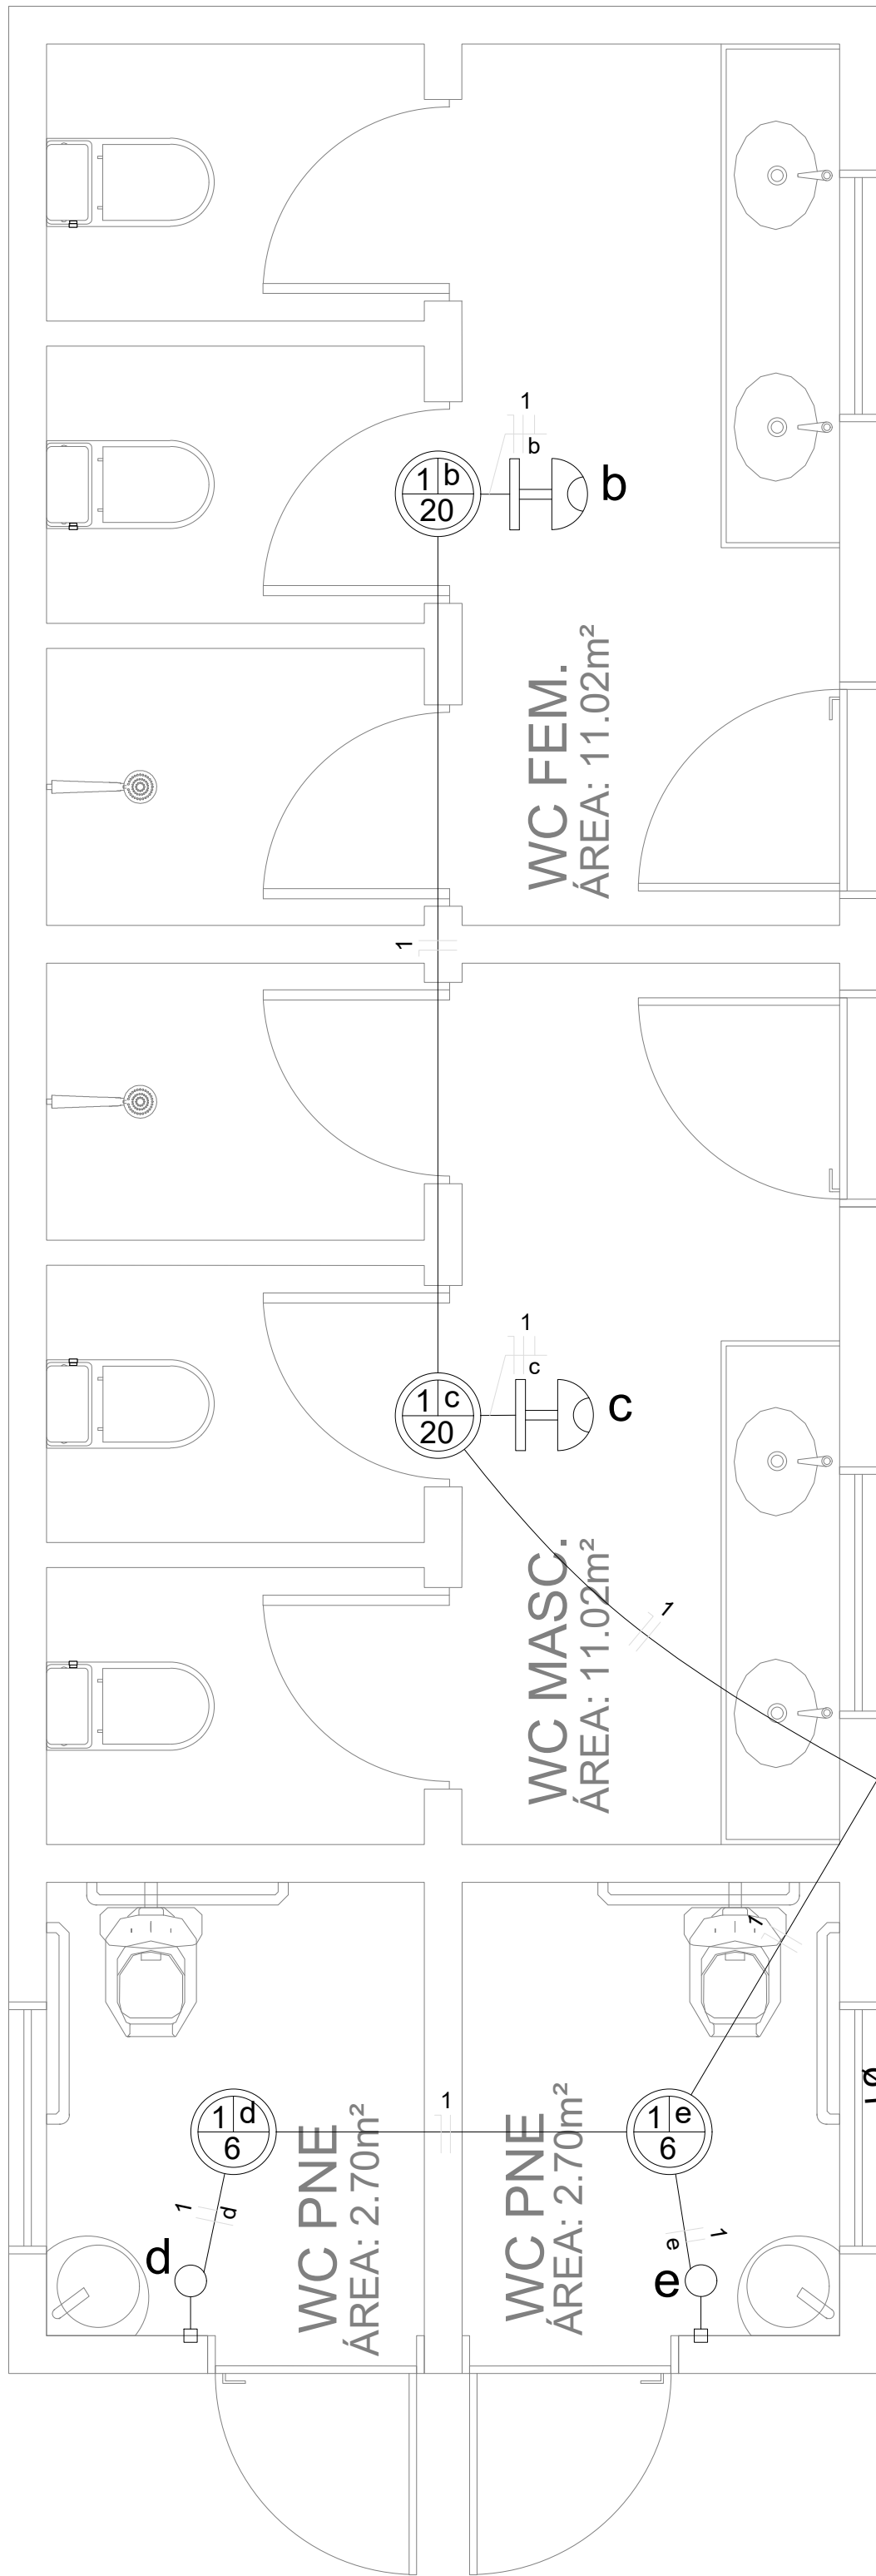


Projeto Elétrico
Escala 1:50

Lista de Materiais	
Acessórios p/ eletrodutos	
Caixa PVC 4x2"	5 pç
Caixa PVC octogonal 3x3"	4 pç
Cabo Unipolar (cobre)	
Isol. PVC - 0,6/1kV (ref. Inbrac Polivinil Antichama)	
1,5 mm²	53,70 m
2,5 mm²	20,80 m
Caixa de passagem - embutir	
Aço pintada (ref Brum)	
150x150x80 mm	1 pç
Dispositivo Elétrico - embutido	
Placa 2x4"	
Placa p/ 1 função retangular	2 pç
S/ placa	
Interruptor 1 tecla simples	2 pç
Dispositivo de Comando	
Interruptor autom. por presença	
220V - 1200W resistivo	2 pç
Dispositivo de Proteção	
Disjuntor Unipolar Termomagnético - norma DIN	
10 A	1 pç
Eletroduto PVC flexível	
Eletroduto leve 3/4"	24,30 m
Eletroduto PVC rosca	
Braçadeira galvan. tipo cunha 1"	
Eletroduto, vara 3,0m 1"	10,40 m
Lâmpada LED	
Uso geral	
20 w	2 pç
6 w	2 pç
Quadro distrib. chapa pintada - embutir	
Sem barr. - UL (Ref. Cemar)	
Cap. 6 disj. unip.	1 pç

Legenda	
	Caixa de passagem de embutir na parede
	Interruptor autom. por presença a 2,20m do piso
	Interruptor simples 1 tecla - 1,10m do piso
	Luminária p/ lâmp. incand. comum - embutir
	Quadro de distribuição - embutir a 1,50m do piso
	Quadro de medição a 2,00m do piso

QD1 (Iluminação)

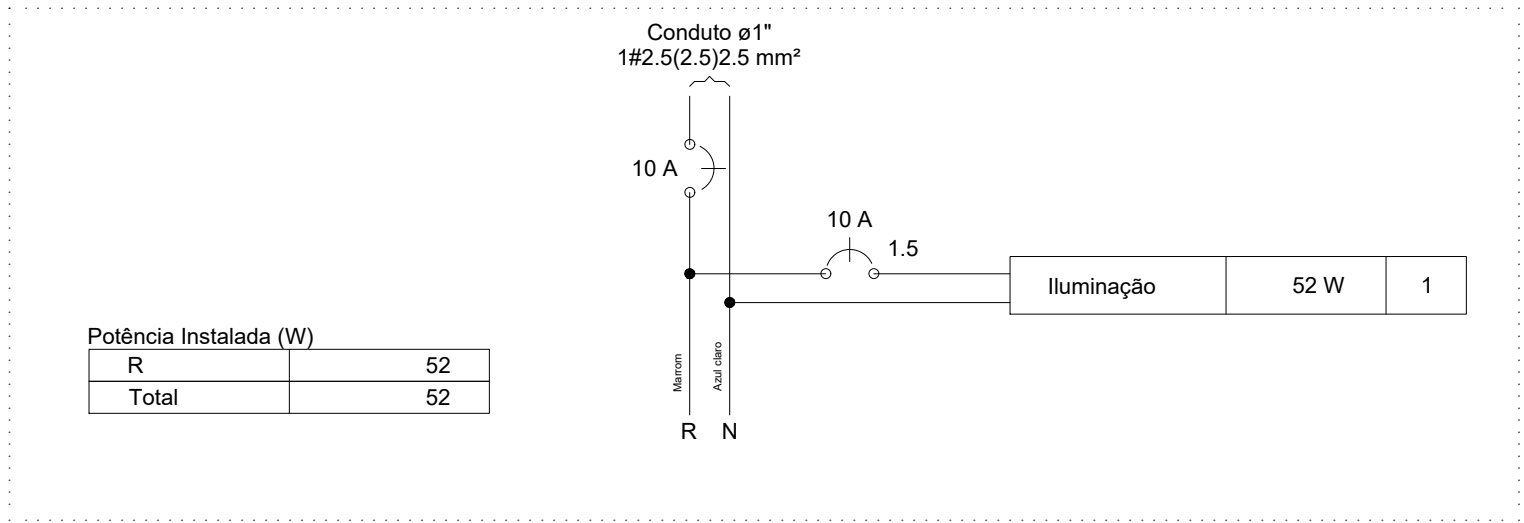


Quadro de Cargas (QD1)																
Circuito	Descrição	Esquema	Método de inst.	V (V)	Iluminação (W)			Pot. total. (VA)	Pot. total. (W)	Fases	Pot. - R (W)	Pot. - S (W)	Pot. - T (W)	FCT	FCA	In' (A)
1	Iluminação	F+N	B1	220 V	2	0	2	52	52	R	52			1,00	1,00	0,2
	b						1	20	20	R	20				1,00	0,1
	c						1	20	20	R	20				1,00	0,2
	d				1		6	6	6	R	6				1,00	0,1
	e				1		6	6	6	R	6				1,00	0,0
TOTAL					2	0	2	52	52	R	52		0			

Quadro de Demanda (QD1)			
Tipo de carga	Potência instalada (kVA)	Fator de demanda (%)	Demanda (kVA)
Iluminação Condomínio (Residencial)		0,06	100
			TOTAL 0,06

Quadro de Cargas (QM1)																
Circuito	Descrição	Esquema	Método de inst.	V (V)	Pot. total. (VA)	Pot. total. (W)	Fases	Pot. - R (W)	Pot. - S (W)	Pot. - T (W)	FCT	FCA	In' (A)	Seção (mm2)	Ic (A)	Disj (A)
QD1	Iluminação	F+N	B1	220 V	52	52	R	52			1,00	1,00	0,3	2,5	24,0	10,0
TOTAL					52	52	R	52	0	0						

Quadro de Demanda (QM1)			
Tipo de carga	Potência instalada (kVA)	Fator de demanda (%)	Demanda (kVA)
Iluminação Condomínio (Residencial)		0,06	100
			TOTAL 0,06

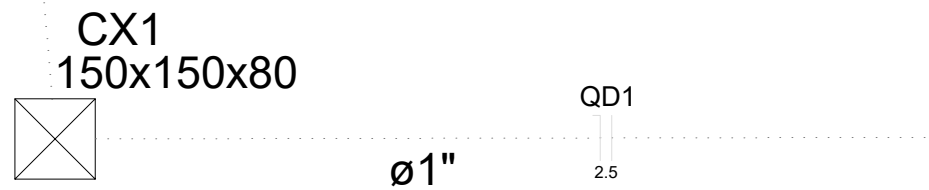

PROPRIETÁRIO: PREFEITURA MUNICIPAL DE COREMAS - PB
LINCOLN CARTAXO DE LIRA
JUNIOR:06897861405
Assinado de forma digital por LINCOLN CARTAXO DE LIRA
Dados: 2026.09.25 11:41:01 -03'00'

PROJETO: LINCOLN CARTAXO DE LIRA JÚNIOR CREA 160.814.689-8

CONSTRUÇÃO:

FOLHA 01/01
PROJETO: CONSTRUÇÃO DE GINÁSIO POLIESPORTIVO
CONCEDENTE: PREFEITURA MUNICIPAL DE COREMAS - PB
CONVENIENTE: MUNICÍPIO DE COREMAS - PB
LOCALIDADE: MUNICÍPIO DE COREMAS - PB

	DATA	RESPONSÁVEL	RUBRICA	DADOS
DESENHO	FEV/2024	LINCOLN CARTAXO		
CÓPIA				
VISTO				

ESCALAS	DESENHOS	CONVÊNIO
	Projeto elétrico	1082984-07
INDICADA		REVISÃO
		ARQUIVO

Aprovações: