


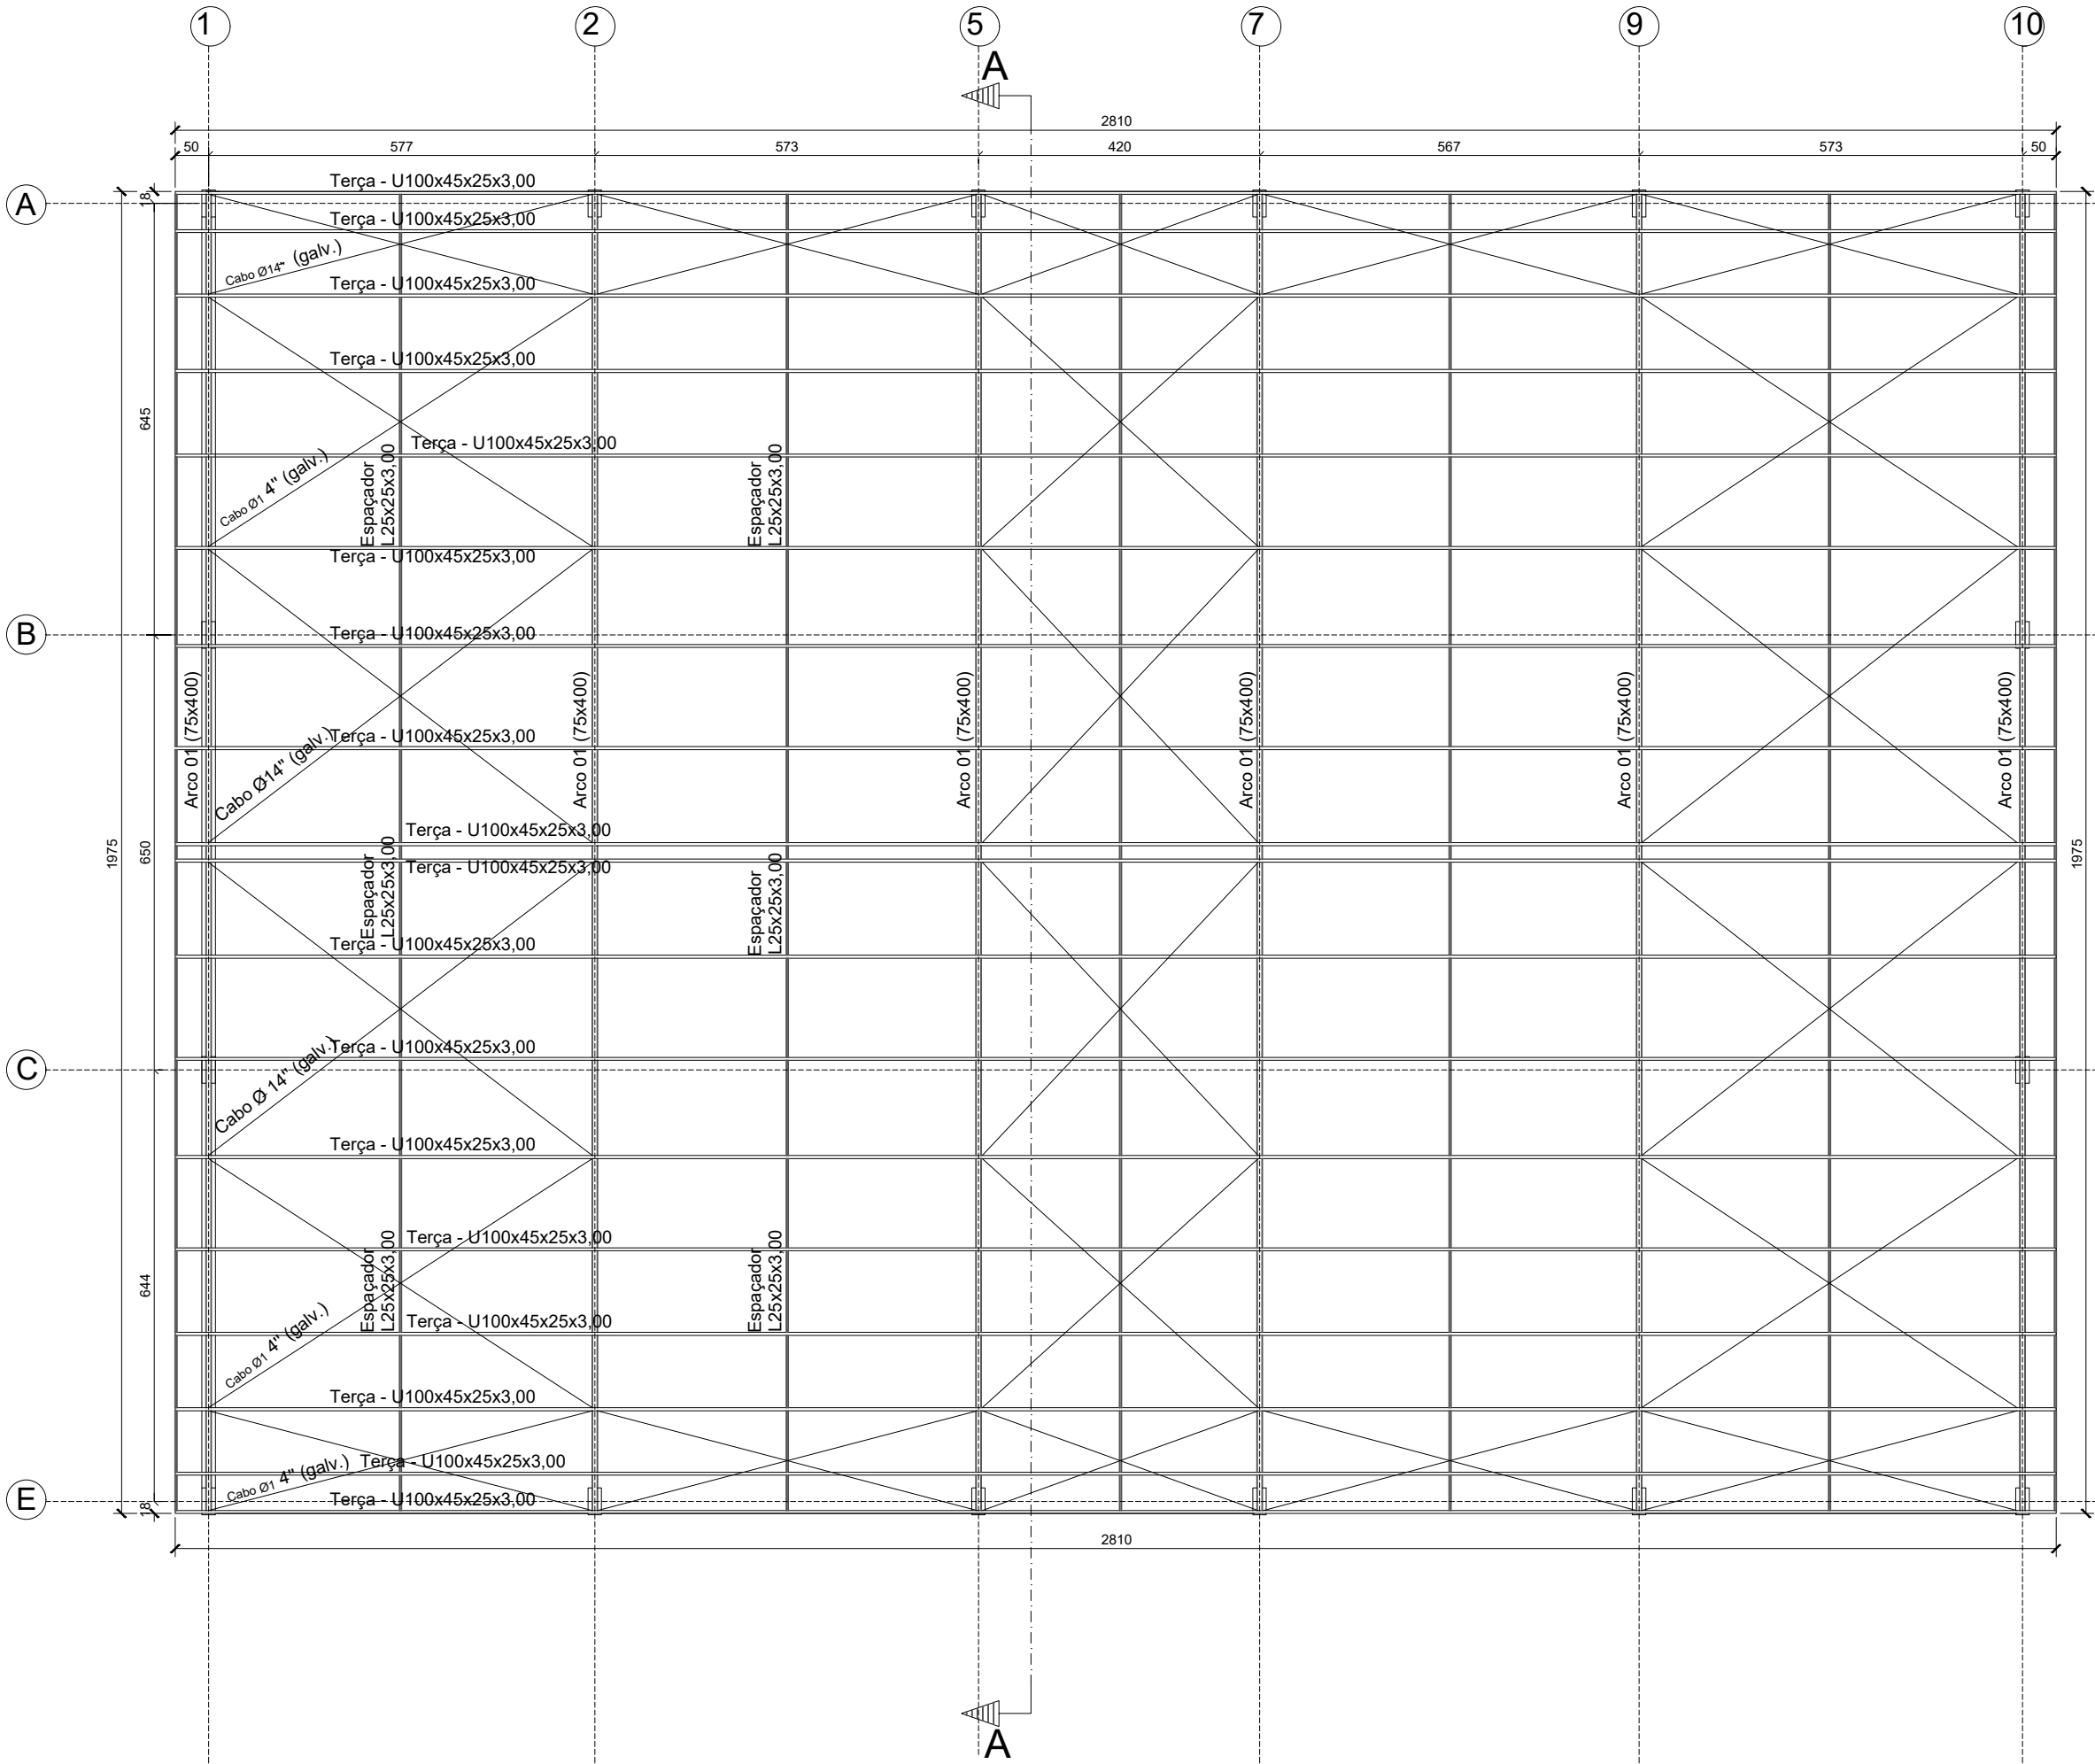

QUANTITATIVO DE MATERIAIS

ELEMENTO	Quantidade	Peso
U75x37.5x3.00	291m	1020kg
L25x25x3.00	600m	690kg
U100x45x25x3.00	530m	2862kg
Chapa 12.7mm (apoios)	4m²	400kg
Telha ondulada (e=0.5mm)	120 und	-
Tamanho: 1.06x6.40m		
Parafuso autobrocante p/ telha	1900 und	-
Cabo Ø14mm	320m²	-
Conjunto p/ Esticador Ø14	44 und	-
Barra rosca Ø10 (1m)	14 und	-
Área total de pintura	450m²	-

OBS: Quantidades e pesos s/ perdas

CONSIDERAÇÕES DE PROJETO:

Tipo de aço: ASTM A-36;
Soldas feitas na fábrica: MIG ER 70 S6;
Soldas feitas in loco: E7016;
Categoria de corrosividade considerada: C2;
Proteção contra corrosão: Pintura com preparação da superfície padrão Si3, tinta de utilização de fundo a base de epóxi (50 microns) e tinta de utilização de acabamento alquídica (50 microns);
Intervalo de manutenção: 10 anos;
Sobrecarga considerada: 25kg/m²;
Tipo de telha: Galvalume ondulada (e=0.50mm);
Barras rosca SAE 1020;

CONSIDERAÇÕES DE PROJETO:
CONCRETO

Classe de Agressividade: III
Cobrimento: 3cm (vigas e pilares), 4cm (fundações), 2.5cm (lajes).
Resistência característica (fck): 25Mpa
Fator água/cimento (em massa): 0.55 (NBR 6118/2014)
Tipo de fundação: Sapatas e Blocos
Retirada total dos escoramentos: 28 dias
Tipo de aço: CA 50/60

NBR's BÁSICAS UTILIZADAS:

Para elaboração deste projeto estrutural, foram utilizadas com rigor as seguintes normas:

- NBR 6118 – 2014 - Projeto de Estruturas de Concreto Armado
- NBR 14931 – 2004 - Execução de Estruturas de Concreto
- NBR 6122 – 1996 - Projeto e Execução de Fundações
- NBR 6120 – 1980 - Cargas para o cálculo de estruturas de edificações
- NBR 8681 – 2003 - Ações e segurança nas estruturas
- NBR 10067 – Princípios Gerais de Representação em Desenho Técnico
- NBR 8800 - 2008 - Projeto de estruturas em aço e de estruturas e mistas em aço e concreto
- NBR 14762 - 2010 - Dimensionamento de estruturas de aço constituídas por perfis formados a frio

PROPRIETÁRIO: PREFEITURA MUNICIPAL DE COREMAS - PB
LINCOLN CARTAXO DE LIRA JÚNIOR:06897861405
Assinado de forma digital por LINCOLN CARTAXO DE LIRA JÚNIOR:06897861405
Dados: 2026.09.22 15:54:07 -03'00'
PROJETO: LINCOLN CARTAXO DE LIRA JÚNIOR CREA 160.814.689-8

FOLHA	PROJETO:	CONSTRUÇÃO DE GINÁSIO POLIESPORTIVO - ESTRUTURAL
01/02	CONVENIENTE:	PREFEITURA MUNICIPAL DE COREMAS - PB
	CONVENIADO:	MUNICÍPIO DE COREMAS - PB
	LOCALIDADE:	COREMAS - PB
DESENHO	DATA	RESPONSÁVEL
CÓPIA	AGOSTO/2025	LINCOLN CARTAXO
VISTO		
ESCALAS	DESENHOS	CONVÊNIO
INDICADO	PLANTA DE ESTRUTURA DE COBERTA	GOVERNO DO ESTADO
		ARQUIVO

PLANTA ESTRUTURA DE COBERTA (GINÁSIO)
(Escala 1:50)