

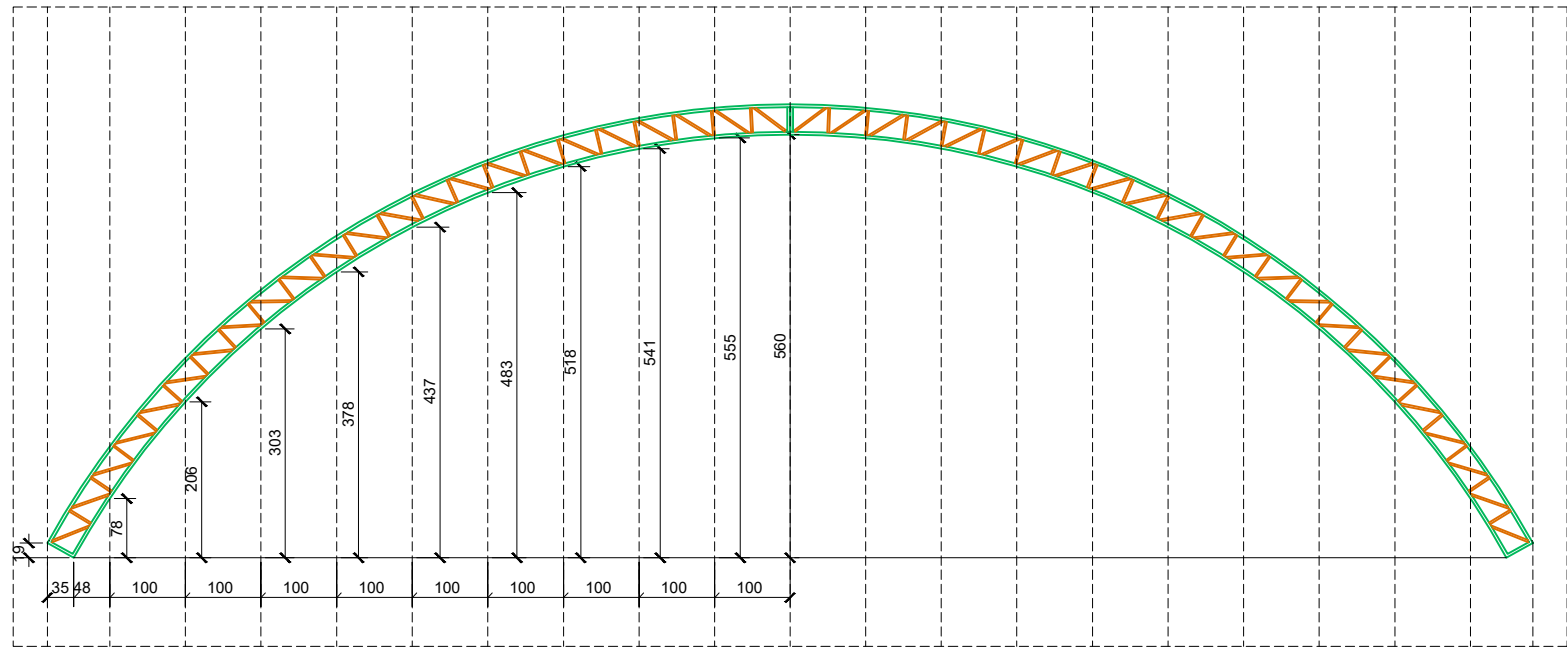


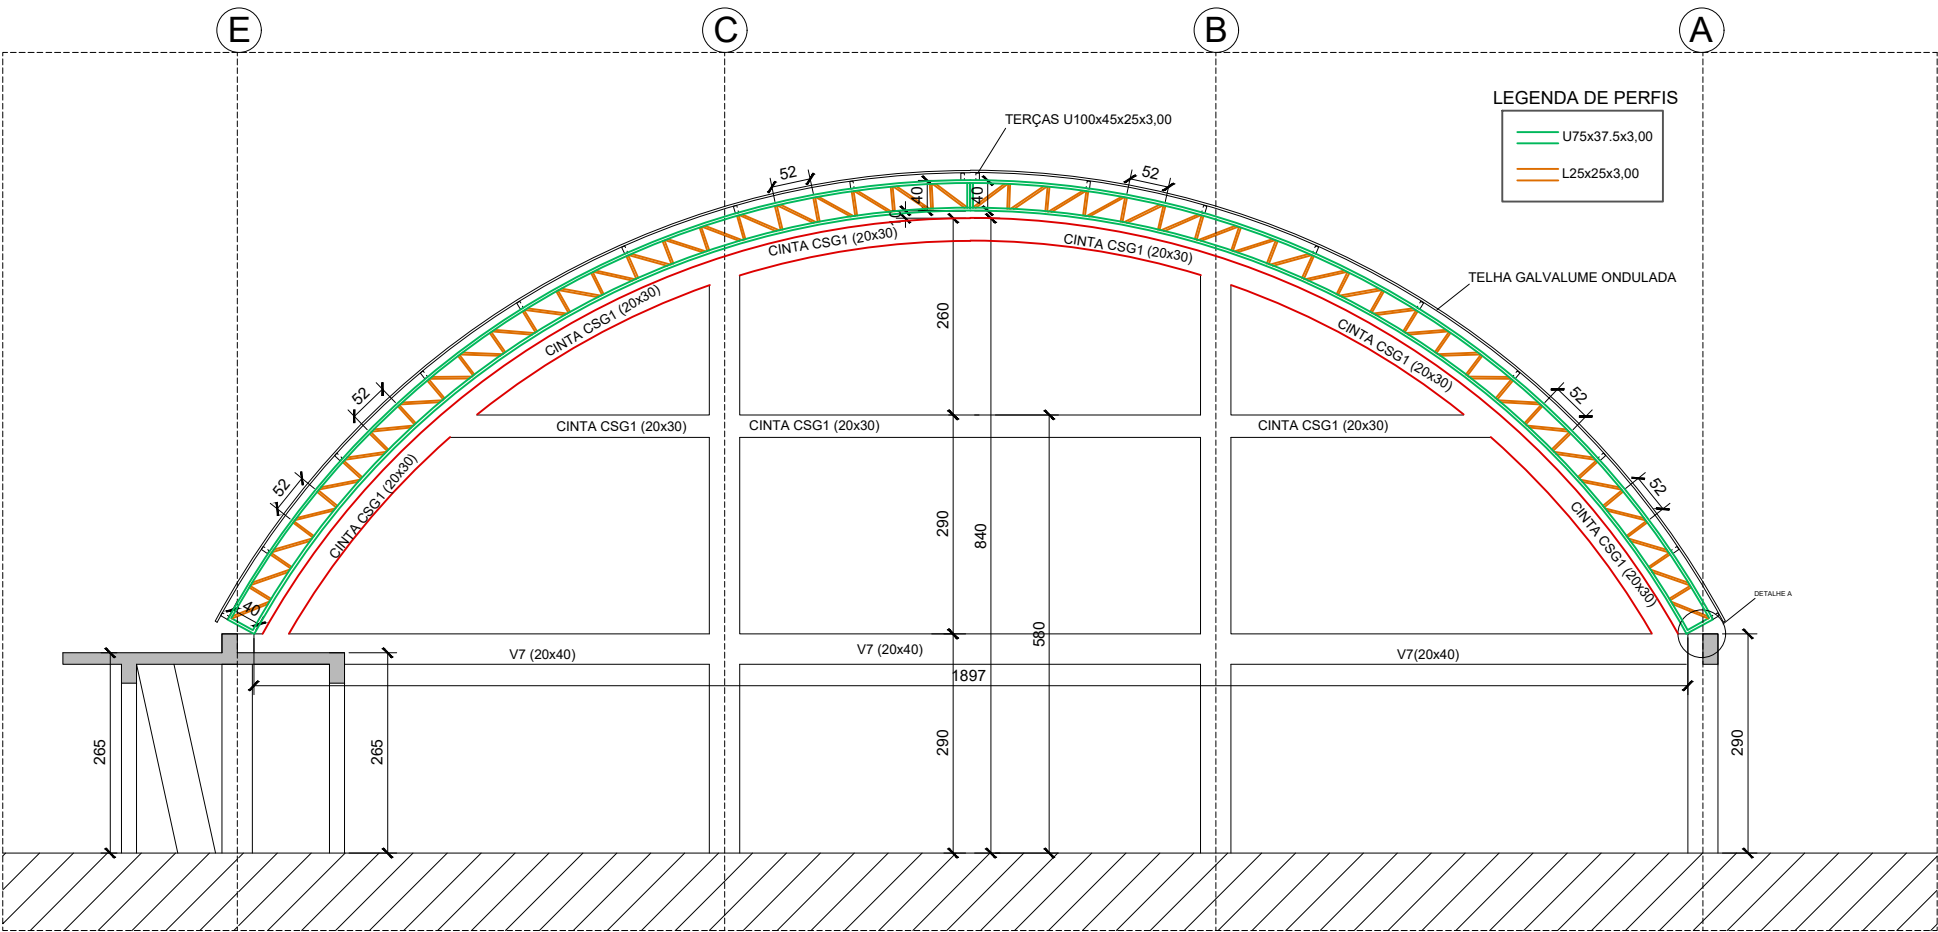

DETALHE DE FABRICAÇÃO DO ARCO (6x)


(Escala 1:50)

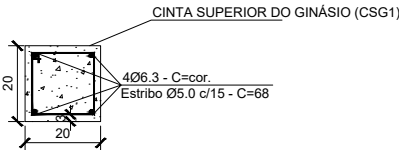

RESUMO AÇO CA 50			
AÇO	BIT (mm)	COMP. (m)	PESO (kg)
50A	6.3	340	85
60A	5.0	365	52
Peso Total =			137 kg


Volume de concreto s/ perdas (cintas do ginásio): 3.2m³
Área de forma (cintas do ginásio): 32m²

DETALHE CINTA SUPERIOR (Escala 1:10)

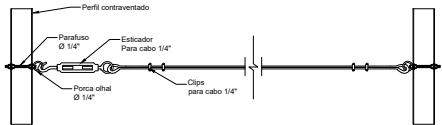


CONSIDERAÇÕES DE PROJETO:


Tipo de aço: ASTM A-36;
Soldas feitas na fábrica: MIG ER 70 S6;
Soldas feitas in loco: E7016;
Categoria de corrosividade considerada: C2;
Proteção contra corrosão: Pintura com preparação da superfície padrão S13, tinta de utilização de fundo a base de epóxi (50 microns) e tinta de utilização de acabamento alquídica (50 microns);
Intervalo de manutenção: 10 anos;
Sobrecarga considerada: 25kg/m²;
Tipo de telha: Galvalume ondulada (e=0.50mm);
Barras rosçadas: SAE 1020;

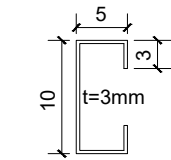


U100x45x25x3,00

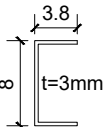


U75x37.5x3,00

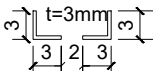

L25x25x3,00

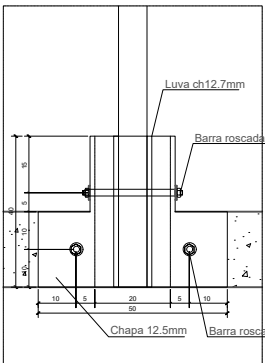

PLANTA

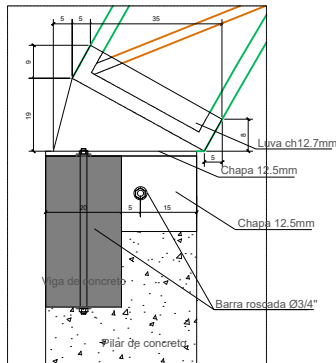

CORTE

DETALHE A (12x)

(Escala 1:5)

CONSIDERAÇÕES DE PROJETO: CONCRETO

Classe de Agressividade: III
Cobrimento: 3cm (vigas e pilares), 4cm (fundações), 2.5cm (lajes).
Resistência característica (fck): 25Mpa
Fator água/cimento (em massa): 0.55 (NBR 6118/2014)
Tipo de fundação: Sapatas e Blocos
Retirada total dos escoramentos: 28 dias
Tipo de aço: CA 50/60

NBR's BÁSICAS UTILIZADAS:

Para elaboração deste projeto estrutural, foram utilizadas com rigor as seguintes normas:

- NBR 6118 – 2014 - Projeto de Estruturas de Concreto Armado
- NBR 14931 – 2004 - Execução de Estruturas de Concreto
- NBR 6122 – 1996 - Projeto e Execução de Fundações
- NBR 6120 – 1980 - Cargas para o cálculo de estruturas de edificações
- NBR 8681 – 2003 - Ações e segurança nas estruturas
- NBR 10067 – Princípios Gerais de Representação em Desenho Técnico
- NBR 8800 - 2008 - Projeto de estruturas em aço e de estruturas e mistas em aço e concreto
- NBR 14762 - 2010 - Dimensionamento de estruturas de aço constituídas por perfis formados a frio

PROPRIETÁRIO: PREFEITURA MUNICIPAL DE COREMAS - PB
LINCOLN CARTAXO DE LIRA JUNIOR:06897861405
Assinado de forma digital por LINCOLN CARTAXO DE LIRA JUNIOR:06897861405
Dados: 2026.09.22 15:54:31 -03'00'

PROJETO: LINCOLN CARTAXO DE LIRA JÚNIOR CREA 160.814.689-8

FOLHA		PROJETO: CONSTRUÇÃO DE GINÁSIO POLIESPORTIVO - ESTRUTURAL	
02/02		CONVENIENTE: PREFEITURA MUNICIPAL DE COREMAS - PB	
		CONVENIADO: MUNICÍPIO DE COREMAS - PB	
		LOCALIDADE: COREMAS - PB	
DESENHO	DATA	RESPONSÁVEL	RUBRICA
CÓPIA	AGOSTO/2025	LINCOLN CARTAXO	
VISTO			
ESCALAS		DESENHOS	
		CORTE AA	
		INDICADO	
INDICADO		DETALHE DE FABRICAÇÃO DO AÇO	
		DETALHE DE CINTA SUPERIOR	
		DETALHES DE PERFIS ESTRUTURAIS	
		DETALHE A	
		CONVÊNIO	
		GOVERNO DO ESTADO	
		ARQUIVO	
Aprovações:			



LCL PROJÉTOS

Av. Gov. Flavio R. Coutinho, 500, sl. 601
Jd. Oliveira, 80037-005 - João Pessoa (PB)
Tel +55 (83) 99924.4447
e-mail: lclprojetos@hotmail.com