RUA OFICIAL DE JUSTIÇA VICENTE GREGORIO ANTÃO

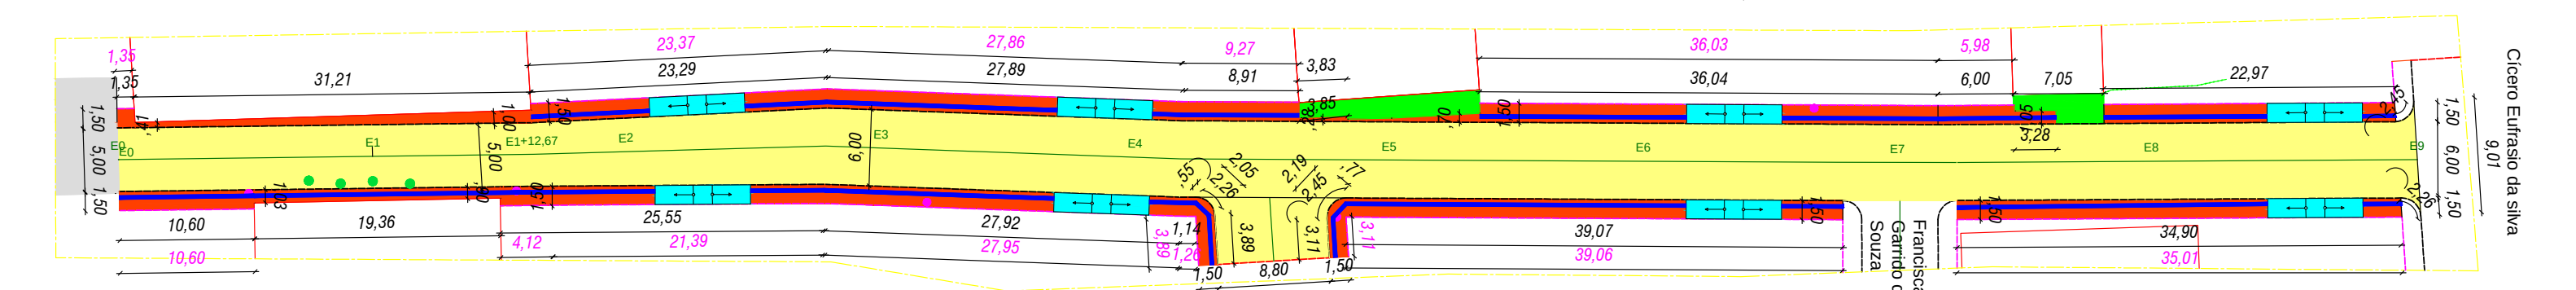
1,35
31,21
23,37
23,29
27,86
27,89
9,27
8,91
3,83
36,03
36,04
5,98
6,00
7,05
22,97
3,28
10,60
19,36
25,55
27,92
4,12
21,39
27,95
1,14
3,89
1,50
8,80
39,07
39,06
34,90
35,01
1,50 5,00 1,50
1,50 6,00 1,50
9,01
Cicero Eufrasio da silva
Francisca Garrido de Souza
E0
E1
E1+12,67
E2
E3
E4
E5
E6
E7
E8
E9

PLANTA BAIXA - CALÇADAS E MEIO-FIO
Escala: 1:300

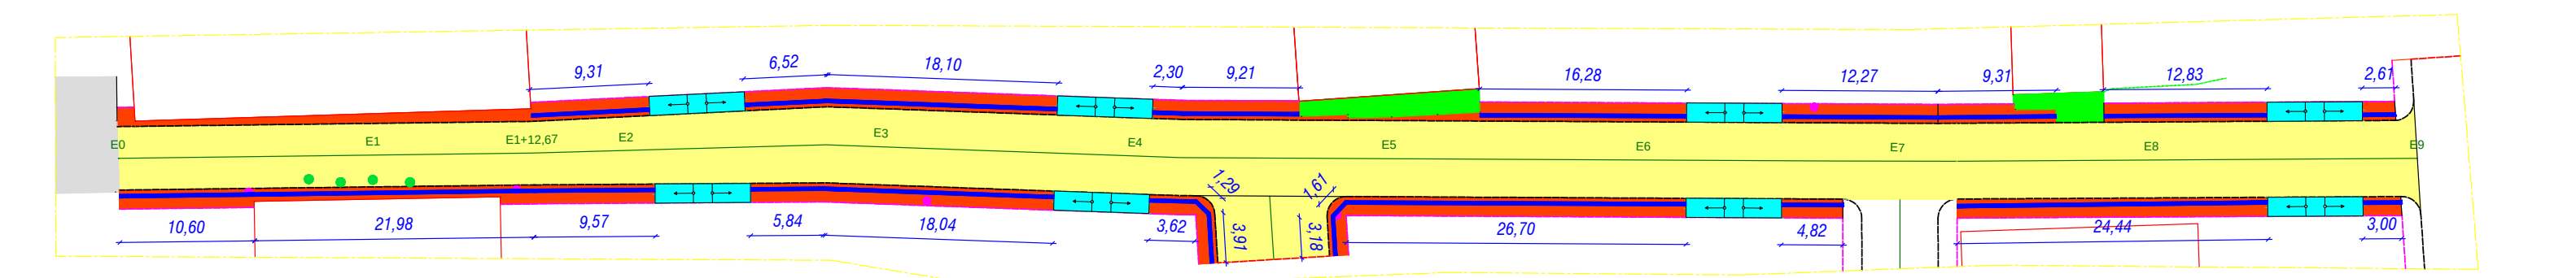
9,31
6,52
18,10
2,30
9,21
16,28
12,27
9,31
12,83
2,61
10,60
21,98
9,57
5,84
18,04
3,62
3,91
3,18
26,70
4,82
24,44
3,00
E0
E1
E1+12,67
E2
E3
E4
E5
E6
E7
E8
E9

PLANTA BAIXA - ROTAS ACESSIVEIS E SINALIZAÇÃO
Escala: 1:300

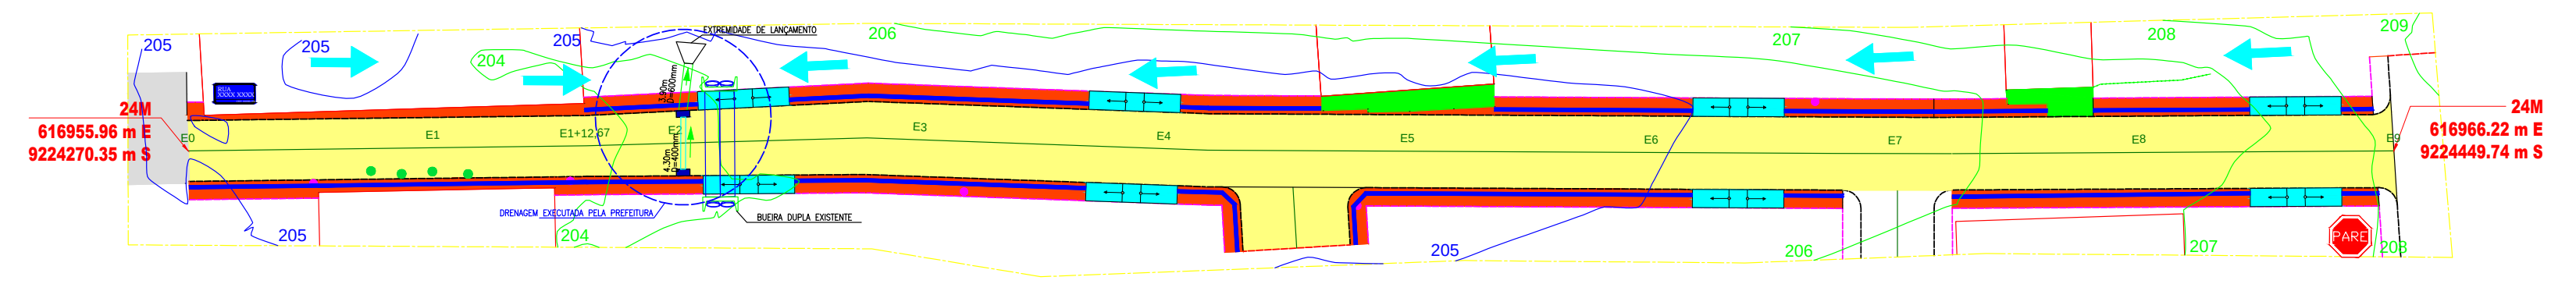
205
204
205
206
207
208
209
24M
616955.96 m E
9224270.35 m S
24M
616966.22 m E
9224449.74 m S
EXTREMIDADE DE LANÇAMENTO
DRENAGEM EXECUTADA PELA PREFEITURA
BUEIRA DUPLA EXISTENTE
PARE

PLANTA BAIXA - ROTAS ACESSIVEIS E SINALIZAÇÃO
Escala: 1:300

RUA OFICIAL DE JUSTIÇA VICENTE GREGORIO ANTÃO - SEÇÕES
ESC.: 1:200

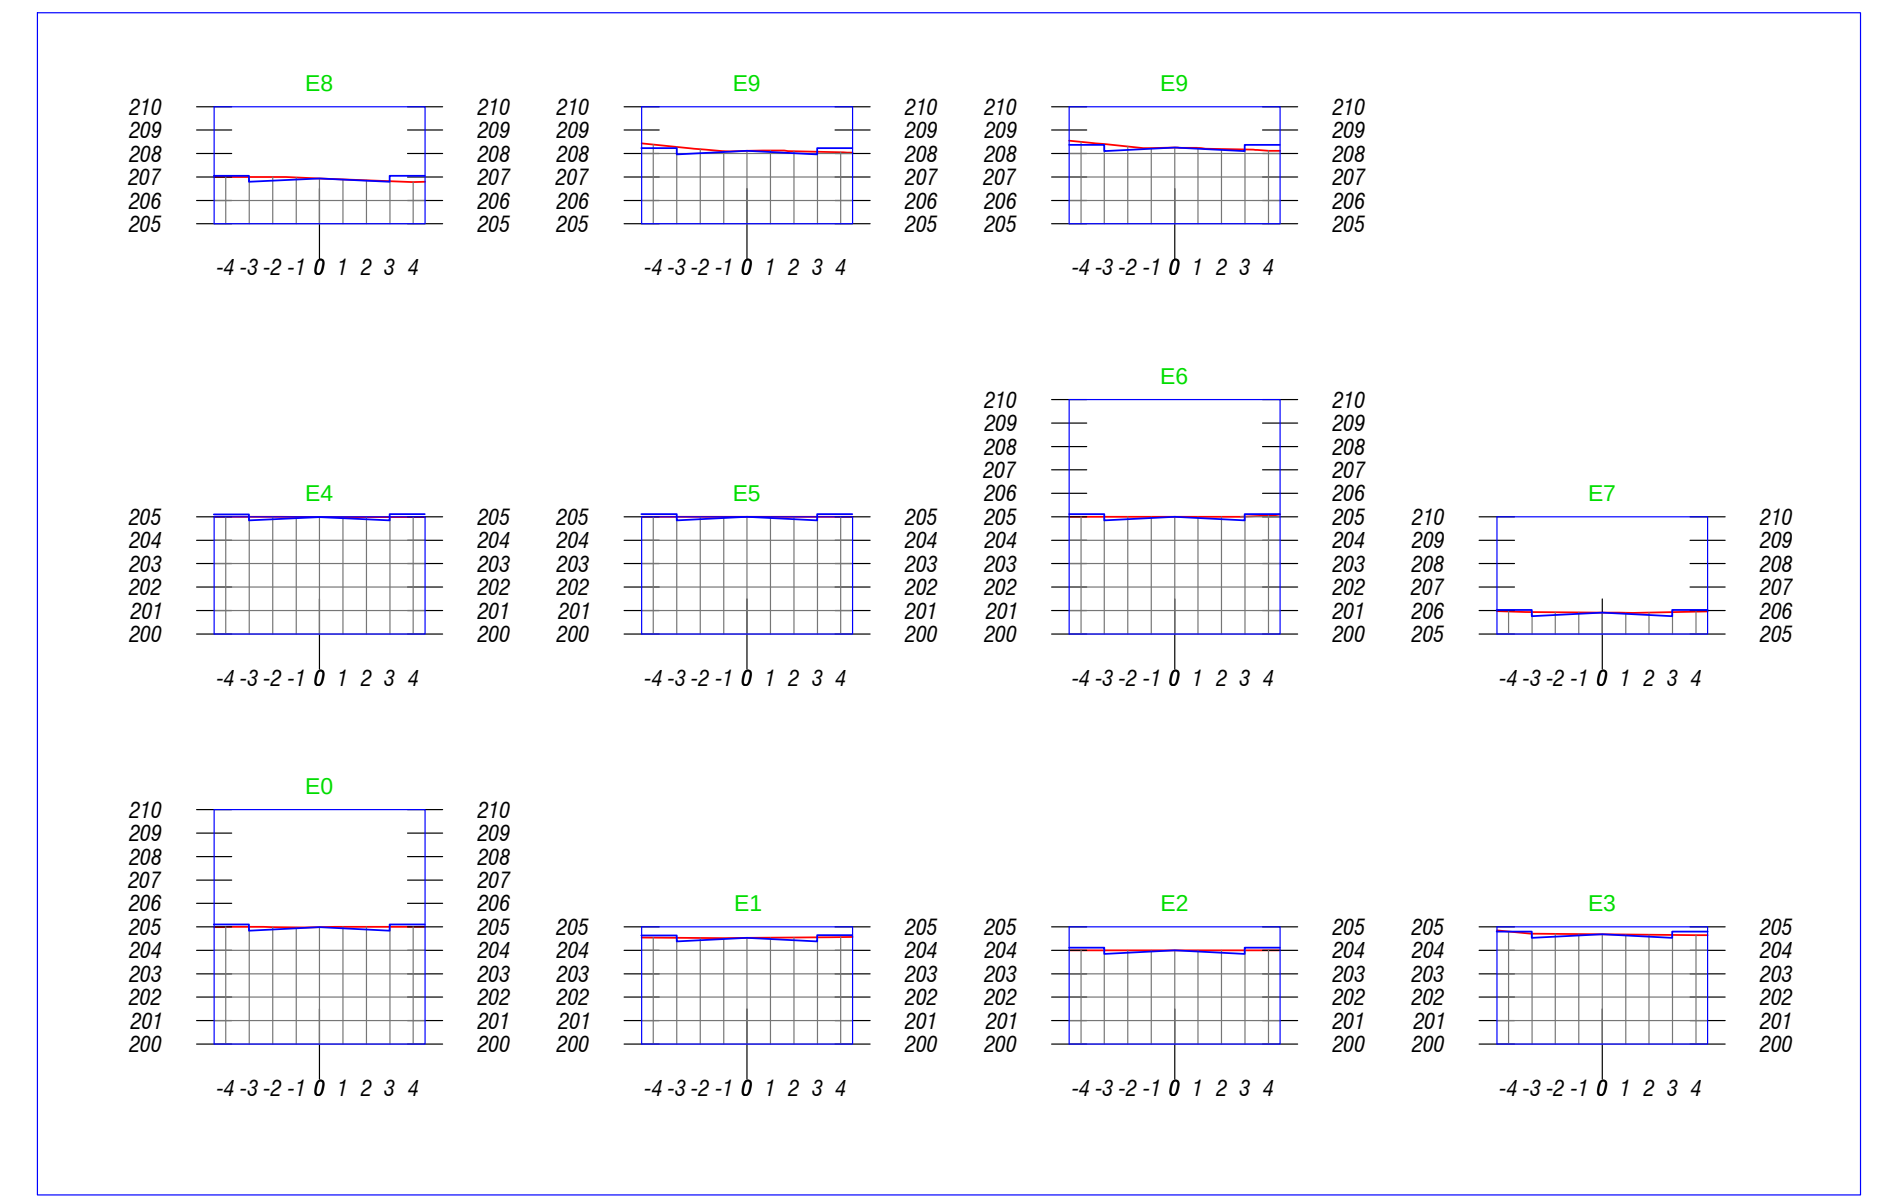

RUA OFICIAL DE JUSTIÇA VICENTE GREGORIO ANTÃO - PERFIL
ESC.: 1:300

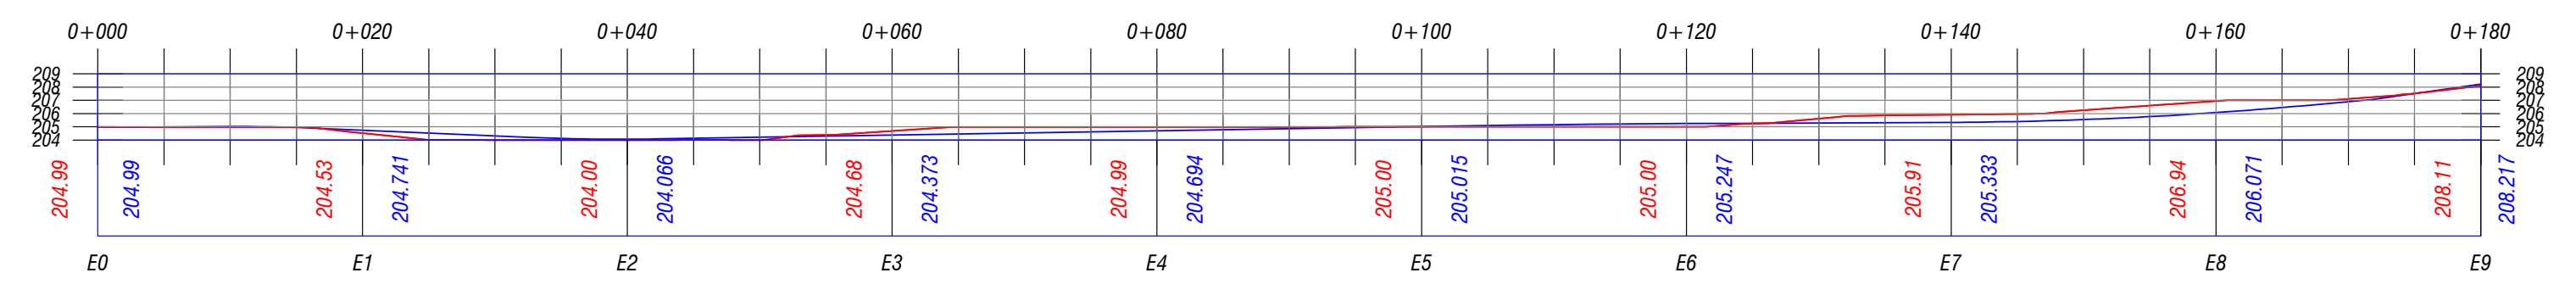

Legenda

Pavimentação

- 🟨 Pavimentação à Construir
- ▨ Pavimento Existente
- Meio-fio Existente
- Meio-fio Projetado
- Cordão em Granito
- Alvenaria de 1 vez
- Cerca
- Sentido do Caimento da água

Passeio

- 🟥 Calçadas à Construir
- 🟩 Calçadas Existentes
- 🟦 Piso Tátil
- Rampa de Acesso
- ● Poste Existente
- ● Poço de Visita (PV)
- ● Árvore
- Edificação Existente
- Lote Projetado

Sinalização

- Placa de Parada Obrigatória
- Placa com Nome da rua

Boca de Lobo (BLS01)
ESCALA : 1/25

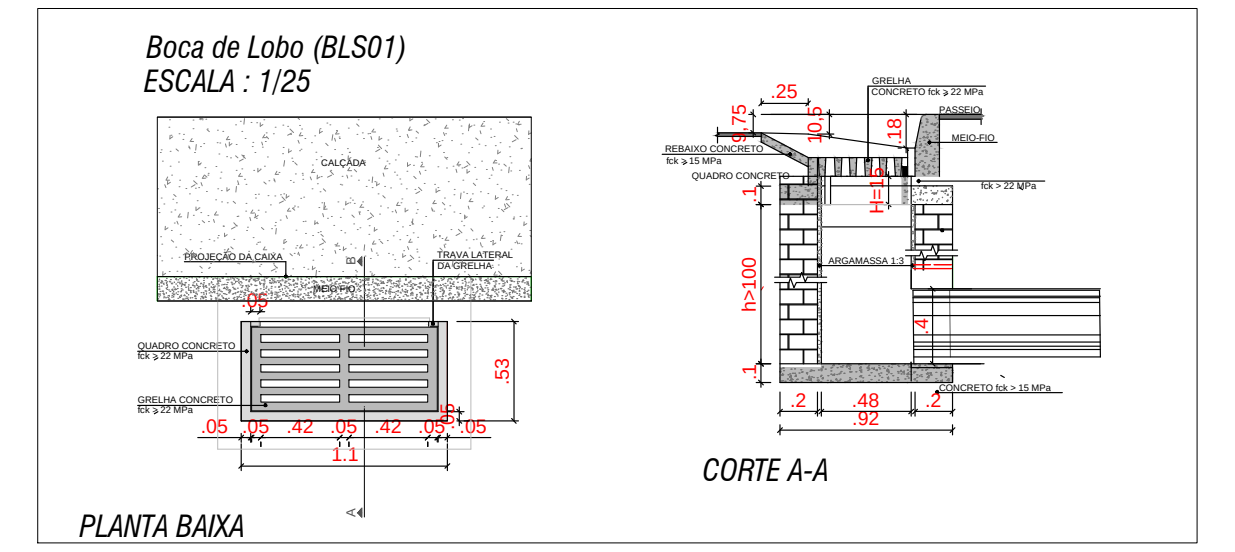
CALÇADA
PROJEÇÃO DA CAIXA
TRAVA LATERAL DA GRELHA
MEIO-FIO
QUADRO CONCRETO fck ≥ 22 MPa
GRELHA CONCRETO fck ≥ 22 MPa
.05 .05 .42 .05 .42 .05 .05
1.1
.53
PLANTA BAIXA
PASSEIO
MEIO-FIO
REBAIXO CONCRETO fck ≥ 15 MPa
QUADRO CONCRETO
fck > 22 MPa
ARGAMASSA 1:3
CONCRETO fck > 15 MPa
H=15
h>100
.2 .48 .2
.92
CORTE A-A

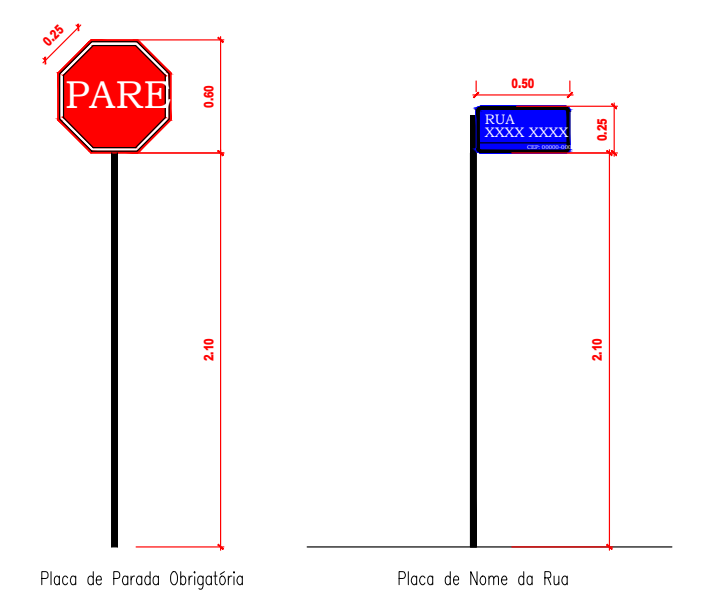
PARE
0.60
2.10
RUA XXXX XXXX
0.50
0.25
2.10

Placa de Parada Obrigatória

Placa de Nome da Rua

Detalhe – Sinalização Vertical
1:25

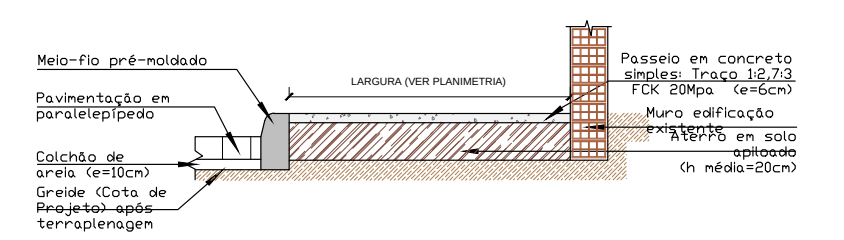
Meio-fio pré-moldado
Pavimentação em paralelepípedo
Colchão de areia (e=10cm)
Greide (Cota de Projeto) após terraplenagem
LARGURA (VER PLANIMETRIA)
Passeio em concreto simples: Traço 1:2,7:3 FCK 20Mpa (e=6cm)
Muro edificação existente
Aterro em solo apiloado (h média=20cm)

Detalhe 01 – Passeio Para Trechos s/ Alvenaria de 1 Vez
escala 25

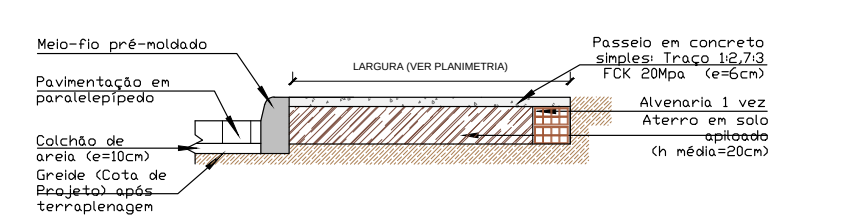
Meio-fio pré-moldado
Pavimentação em paralelepípedo
Colchão de areia (e=10cm)
Greide (Cota de Projeto) após terraplenagem
LARGURA (VER PLANIMETRIA)
Passeio em concreto simples: Traço 1:2,7:3 FCK 20Mpa (e=6cm)
Alvenaria 1 vez
Aterro em solo apiloado (h média=20cm)

Detalhe 02 – Passeio Para Trechos c/ Alvenaria de 1 Vez
escala 25

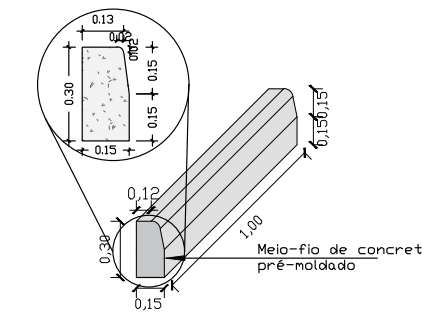
0.13
0.30
0.15
0.15
0.15
0,12
0,30
0,15
1,00
0,15
Meio-fio de concreto pré-moldado

Detalhe – Meio-fio
escala 25

Nota: Para o cálculo do quantitativo de concreto do passeio público, considera-se a dimensão da largura conforme indicado nos detalhe dos passeios.

Seção-Tipo de Pavimentação

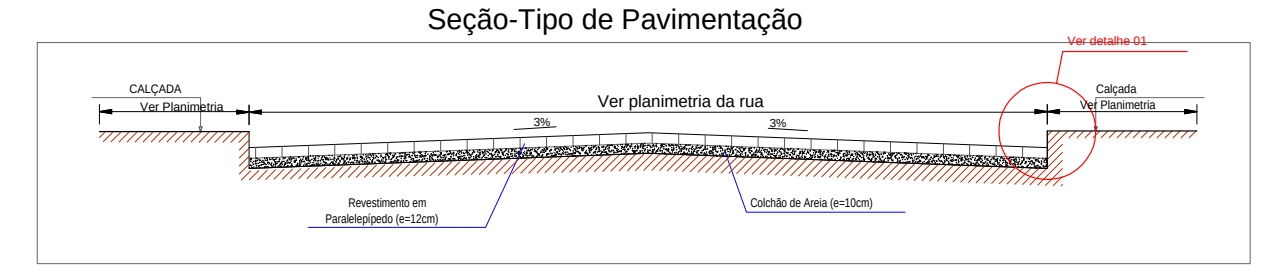
CALÇADA
Ver Planimetria
Ver planimetria da rua
2%
2%
Ver detalhe 01
Calçada
Ver Planimetria
Revestimento em Paralelepípedo (e=12cm)
Colchão de Areia (e=10cm)

Sem Escala

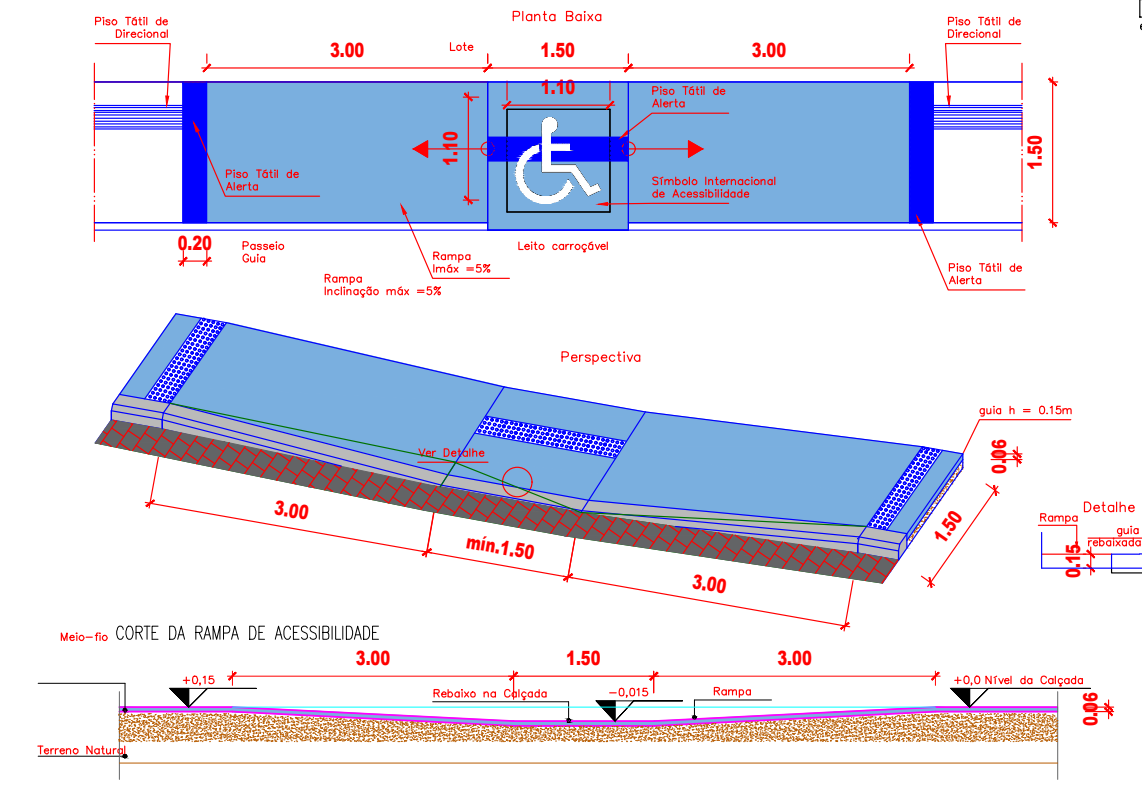
Planta Baixa
Piso Tátil de Direcional
3.00
Lote
1.50
3.00
Piso Tátil de Direcional
1.10
Piso Tátil de Alerta
1.10
1.50
Piso Tátil de Alerta
Símbolo Internacional de Acessibilidade
0.20
Passeio Guia
Rampa i máx =5%
Rampa inclinação máx =5%
Leito carroçável
Piso Tátil de Alerta
Perspectiva
3.00
min.1,50
3.00
1.50
Detalhe
Meio-fio CORTE DA RAMPA DE ACESSIBILIDADE
3.00
1.50
3.00
Rebaixo no Calçada
Rampa
Terreno Natural

Detalhe – Rampa de Acessibilidade
1:50

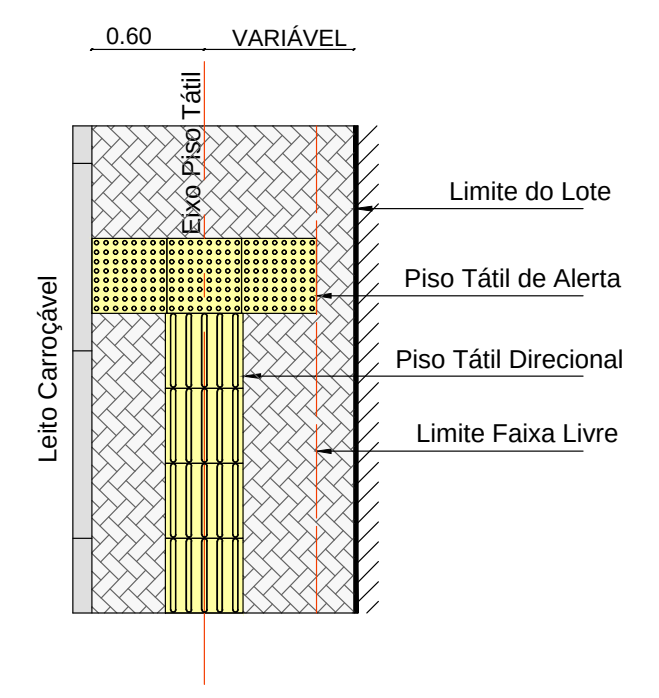
0.60
VARIÁVEL
Eixo Piso Tátil
Limite do Lote
Piso Tátil de Alerta
Piso Tátil Direcional
Limite Faixa Livre
Leito Carroçável

Detalhe 01 – Início/Fim Piso Tátil (D01-IFPT)
escala 25

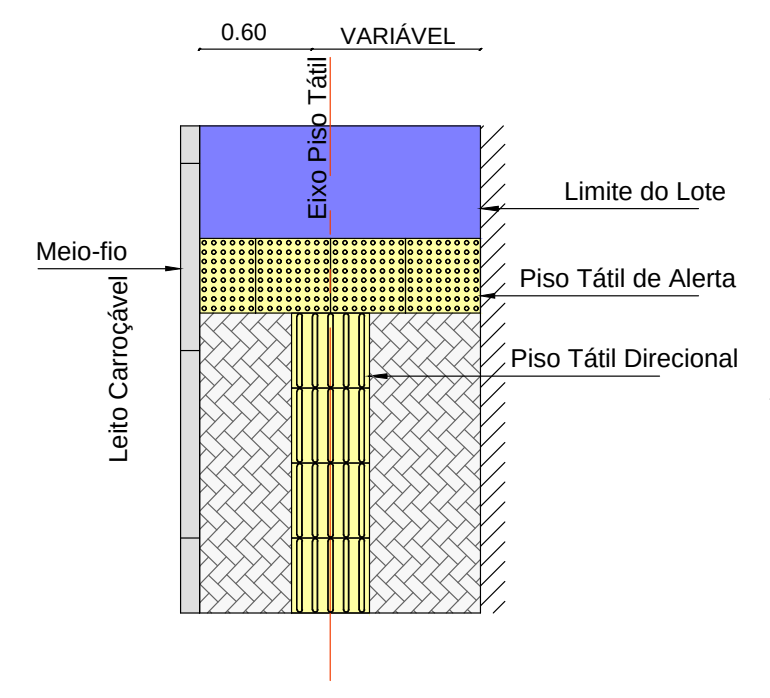
0.60
VARIÁVEL
Eixo Piso Tátil
Limite do Lote
Meio-fio
Piso Tátil de Alerta
Piso Tátil Direcional
Leito Carroçável

Detalhe 02 – Encontro Piso Tátil com Rampa (D02-EPTR)
escala 25

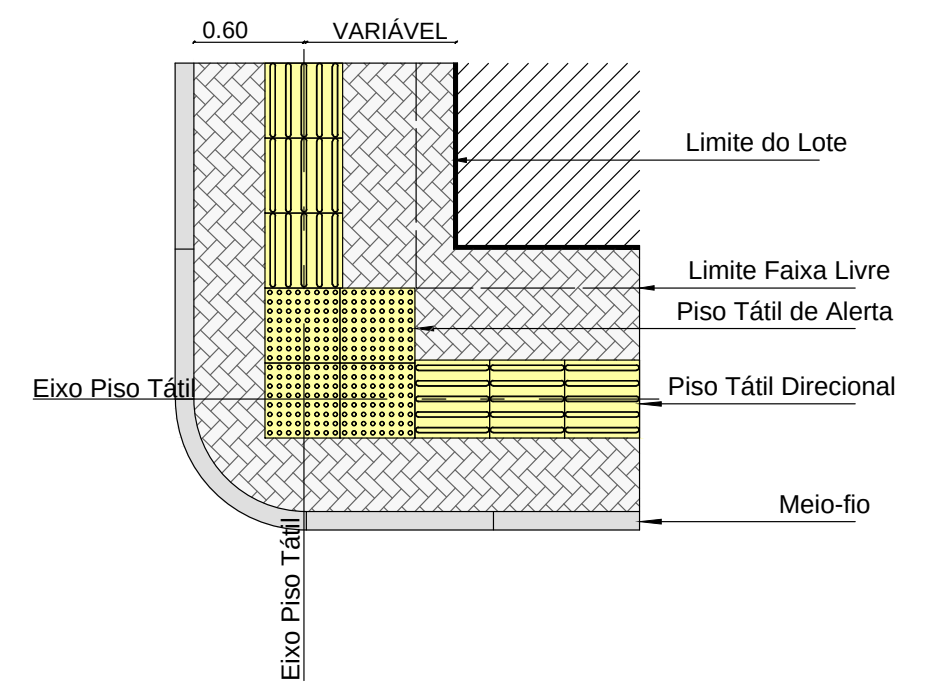
0.60
VARIÁVEL
Limite do Lote
Limite Faixa Livre
Piso Tátil de Alerta
Eixo Piso Tátil
Piso Tátil Direcional
Meio-fio
Eixo Piso Tátil

Detalhe 03 – Mudança de direção – Entre 90° e 150° (D03-MD)
escala 25

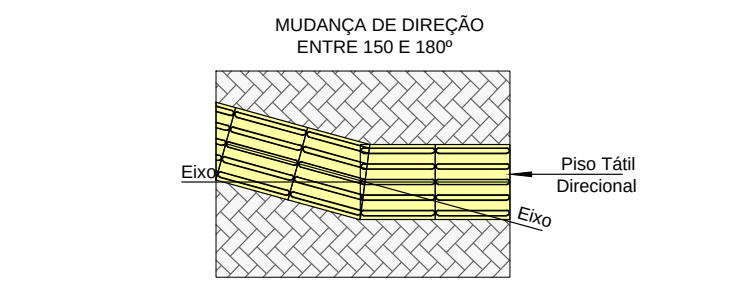
MUDANÇA DE DIREÇÃO ENTRE 150 E 180°
Eixo
Piso Tátil Direcional
Eixo

Detalhe 04 – Mudança de direção entre 150° e 180° (D04-MD)
escala 25

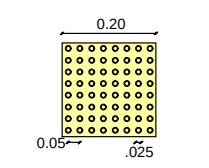

Detalhe 05 – Piso Tátil de Alerta
escala 25

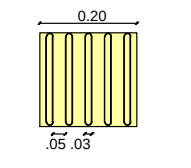

Detalhe 06 – Piso Tátil Direcional
escala 25

PROPRIETÁRIO Prefeitura Municipal de Coremas- PB

Kleber Sá de Oliveira
Engenheiro Civil
CREA 1602682780

PROJETISTA Kleber Sá de Oliveira

EPE EMPRESA PARAIBA DE ENGENHARIA	PROJETO: PAVIMENTAÇÃO DE RUAS E VIAS LOCAL: MUNICÍPIO DE COREMAS - PB PROPRIETÁRIO: PREFEITURA MUNICIPAL DE COREMAS - PB

FOLHA 01/07	ESCALA: Indicadas	DESENHOS: Indicados	RESPONSÁVEL TÉCNICO: Kleber Sá de Oliveira Crea: 160391676-8
ARQUIVO: PAV_COREMAS_FINAL P+B_2022.dwg	DESENHO: Diego Medeiros		ANOTAÇÕES: DATA: SET - 2022

Francisca Garrido de Souza

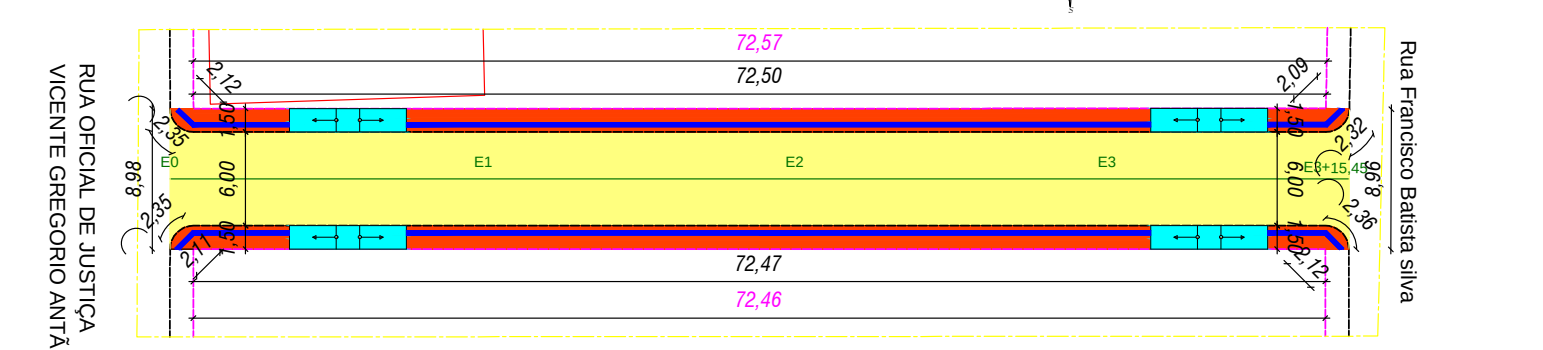
72,57
72,50
72,47
72,46
RUA OFICIAL DE JUSTIÇA VICENTE GREGORIO ANTÃO
Rua Francisco Batista silva
E0
E1
E2
E3
E3+15,45

PLANTA BAIXA - CALÇADAS E MEIO-FIO
Escala: 1:300

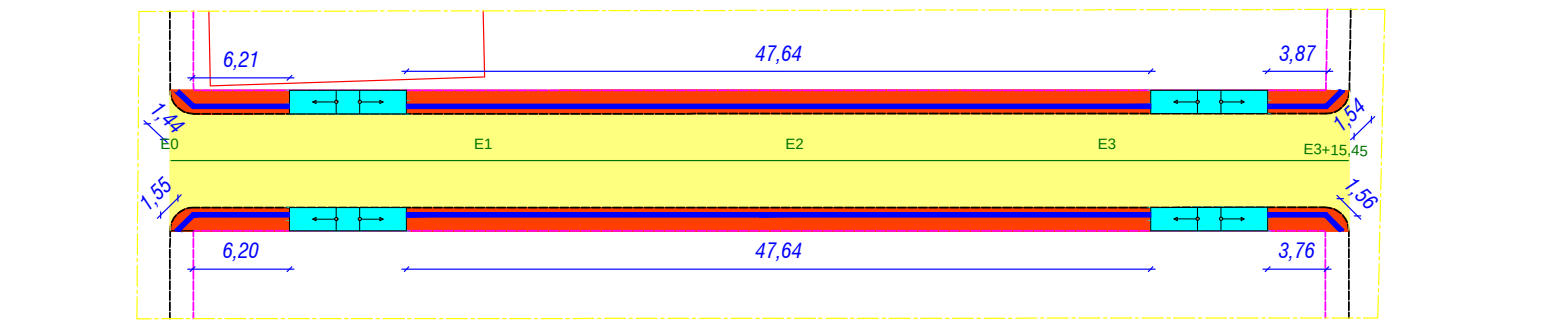
6,21
47,64
3,87
6,20
47,64
3,76
E0
E1
E2
E3
E3+15,45

PLANTA BAIXA - ROTAS ACESSIVEIS E SINALIZAÇÃO
Escala: 1:300

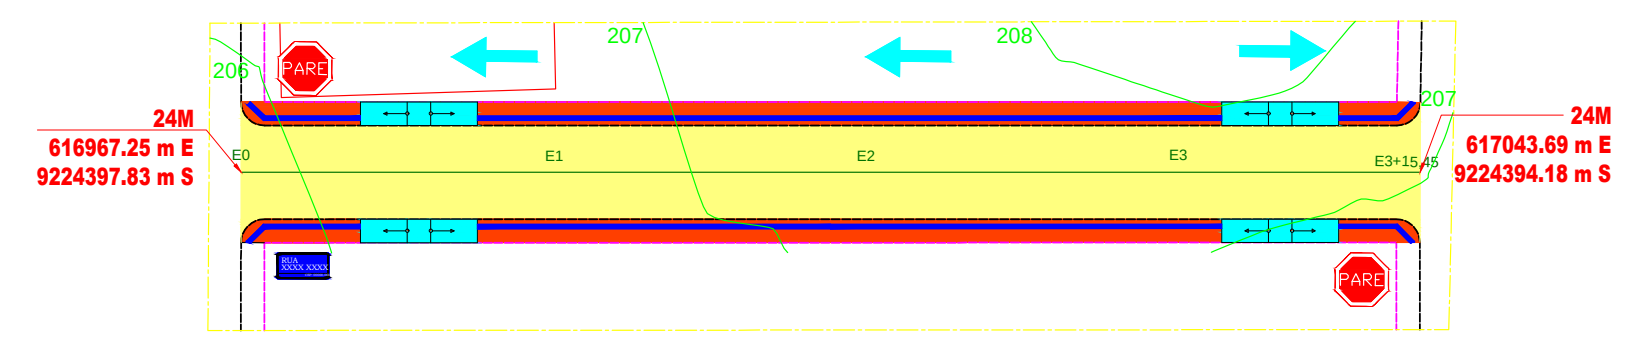
PARE
206
207
208
207
24M
616967.25 m E
9224397.83 m S
24M
617043.69 m E
9224394.18 m S
E0
E1
E2
E3
E3+15,45
PARE

PLANTA BAIXA - ROTAS ACESSIVEIS E SINALIZAÇÃO
Escala: 1:300

Legenda

Pavimentação

- 🟨 Pavimentação à Construir
- ▨ Pavimento Existente
- Meio-fio Existente
- Meio-fio Projetado
- Cordão em Granito
- Alvenaria de 1 vez
- Cerca
- Sentido do Caimento da água

Passeio

- 🟥 Calçadas à Construir
- 🟩 Calçadas Existentes
- 🟦 Piso Tátil
- Rampa de Acesso
- ● Poste Existente
- ● Poço de Visita (PV)
- ● Árvore
- Edificação Existente
- Lote Projetado

Sinalização

- Placa de Parada Obrigatória
- Placa com Nome da rua

FRANCISCA GARRIDO DE SOUZA - PERFIL
ESC.: 1:300

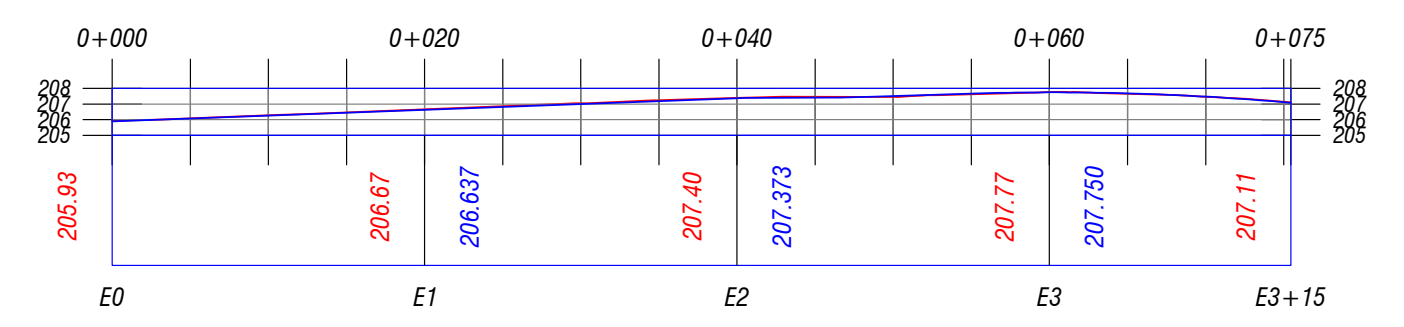

RUA OFICIAL DE JUSTIÇA VICENTE GREGORIO ANTÃO - SEÇÕES
ESC.: 1:200

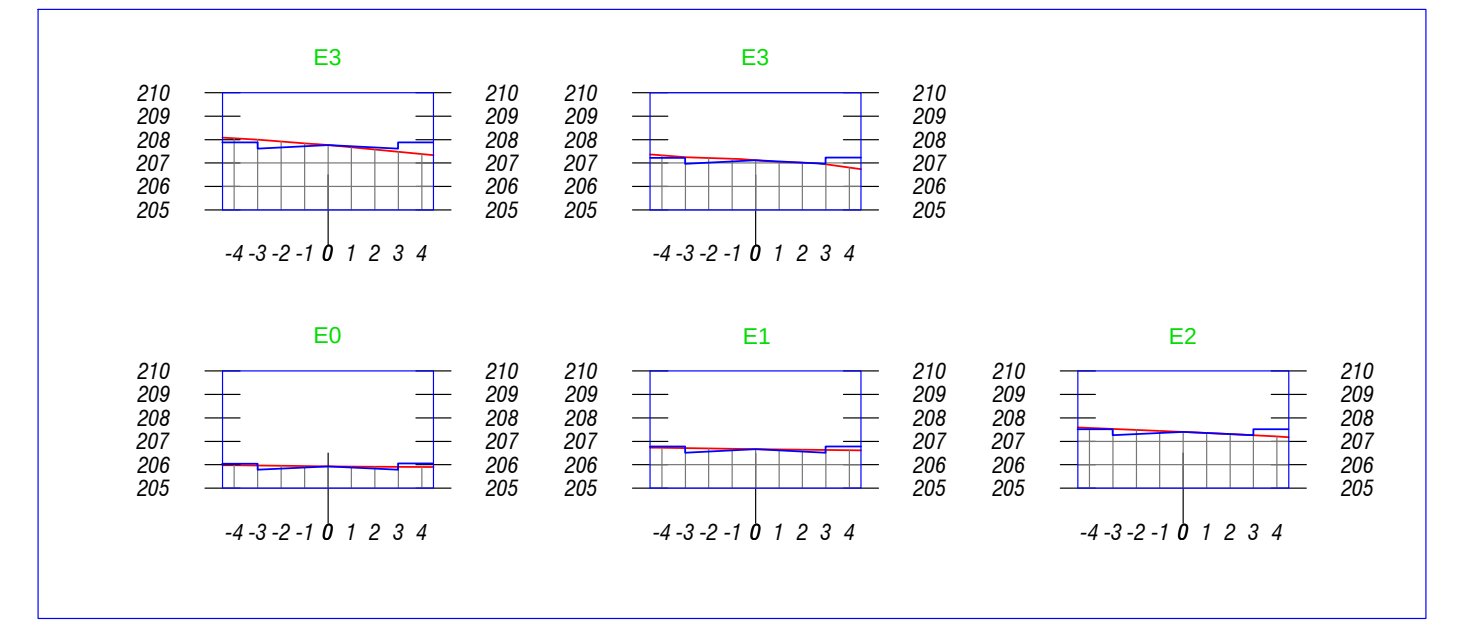

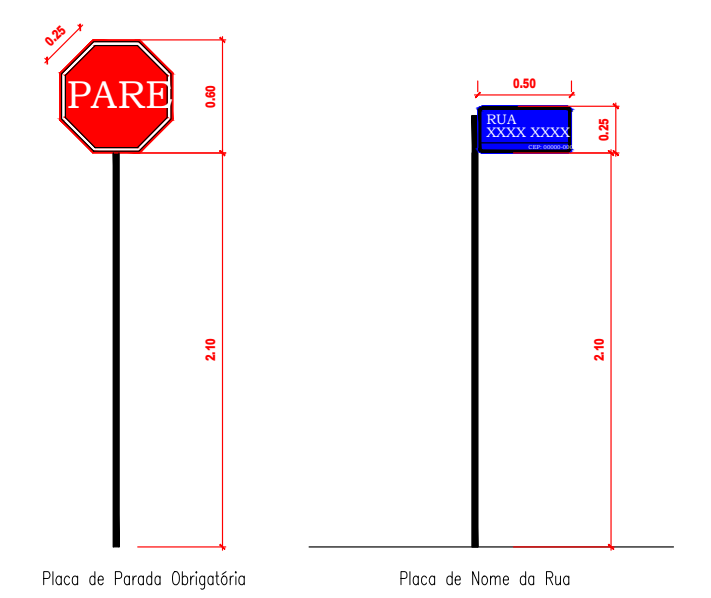
PARE
RUA XXXX XXXX

Placa de Parada Obrigatória

Placa de Nome da Rua

Detalhe – Sinalização Vertical
1:25

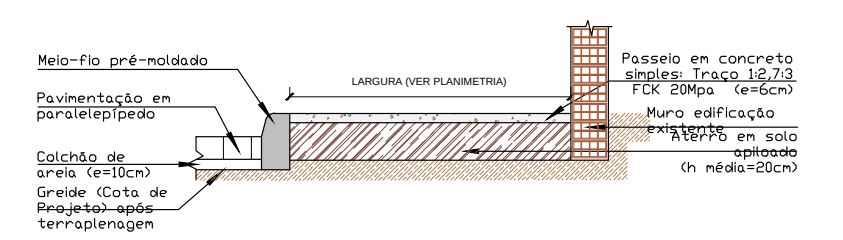
Meio-fio pré-moldado
Pavimentação em paralelepípedo
Colchão de areia (e=10cm)
Greide (Cota de Projeto) após terraplenagem
LARGURA (VER PLANIMETRIA)
Passeio em concreto simples: Traço 1:2,7:3 FCK 20Mpa (e=6cm)
Muro edificação existente
Aterro em solo apiloado (h média=20cm)

Detalhe 01 – Passeio Para Trechos s/ Alvenaria de 1 Vez
escala 25

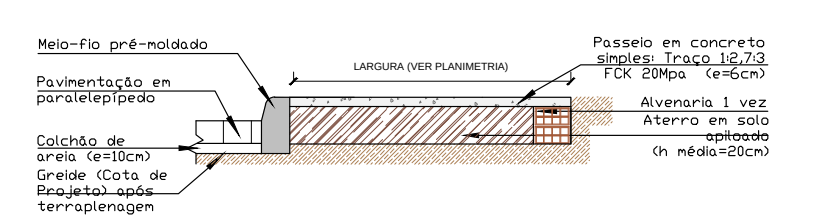
Meio-fio pré-moldado
Pavimentação em paralelepípedo
Colchão de areia (e=10cm)
Greide (Cota de Projeto) após terraplenagem
LARGURA (VER PLANIMETRIA)
Passeio em concreto simples: Traço 1:2,7:3 FCK 20Mpa (e=6cm)
Alvenaria 1 vez
Aterro em solo apiloado (h média=20cm)

Detalhe 02 – Passeio Para Trechos c/ Alvenaria de 1 Vez
escala 25

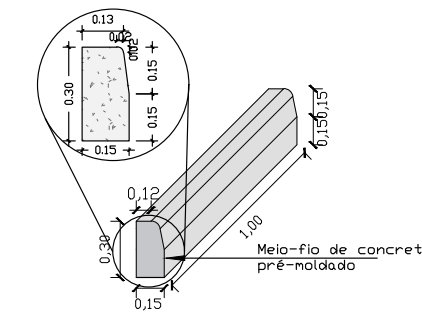
Meio-fio de concreto pré-moldado

Detalhe – Meio-fio
escala 25

Nota: Para o cálculo do quantitativo de concreto do passeio público, considera-se a dimensão da largura conforme indicado nos detalhe dos passeios.

Seção-Tipo de Pavimentação

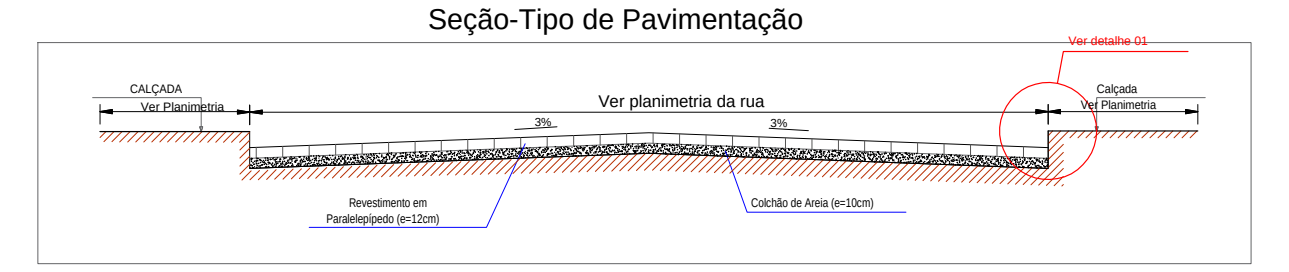
CALÇADA
Ver Planimetria
Ver planimetria da rua
2%
2%
Calçada
Ver Planimetria

Sem Escala

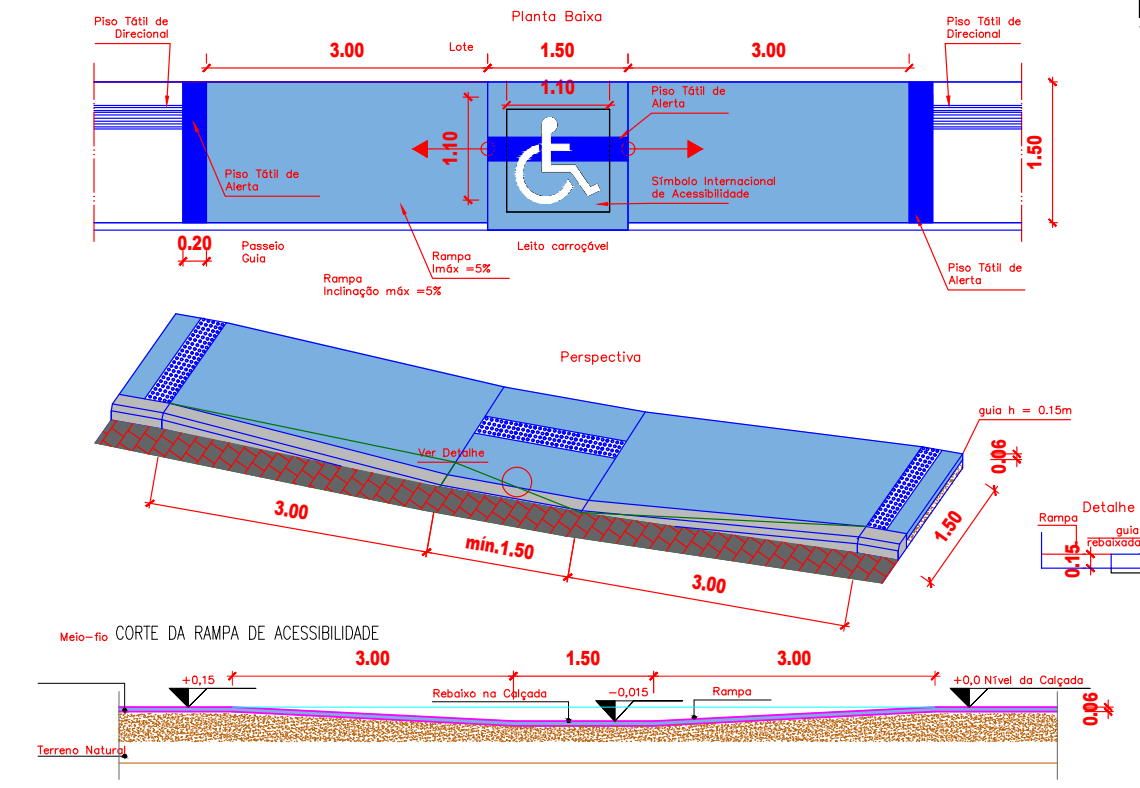
Planta Baixa
3.00
1.50
3.00
Perspectiva
3.00
min.1,50
3.00
CORTE DA RAMPA DE ACESSIBILIDADE

Detalhe – Rampa de Acessibilidade
1:50

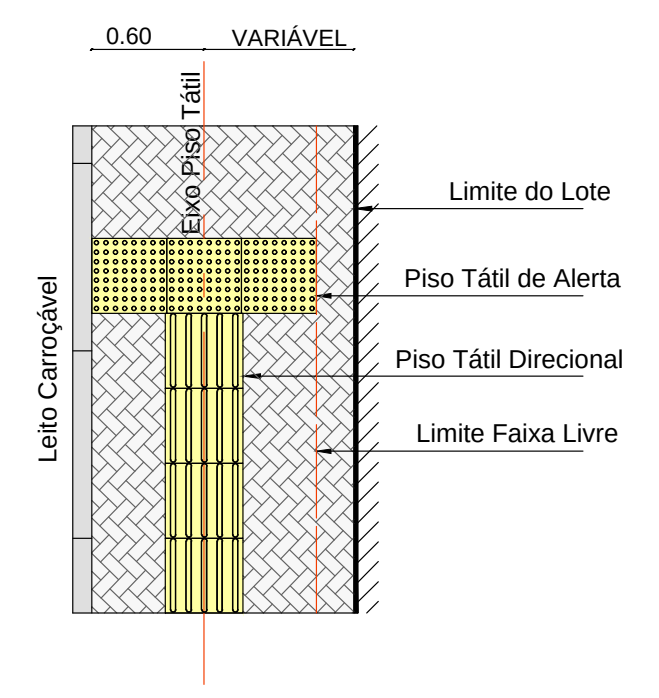
0.60
VARIÁVEL
Eixo Piso Tátil
Limite do Lote
Piso Tátil de Alerta
Piso Tátil Direcional
Limite Faixa Livre
Leito Carroçável

Detalhe 01 – Início/Fim Piso Tátil (D01-IFPT)
escala 25

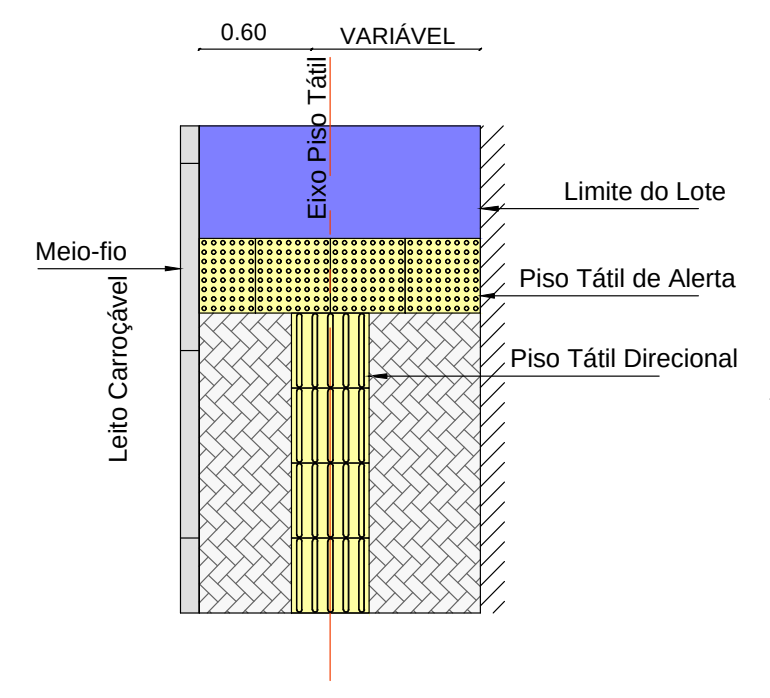
0.60
VARIÁVEL
Eixo Piso Tátil
Limite do Lote
Meio-fio
Piso Tátil de Alerta
Piso Tátil Direcional
Leito Carroçável

Detalhe 02 – Encontro Piso Tátil com Rampa (D02-EPTR)
escala 25

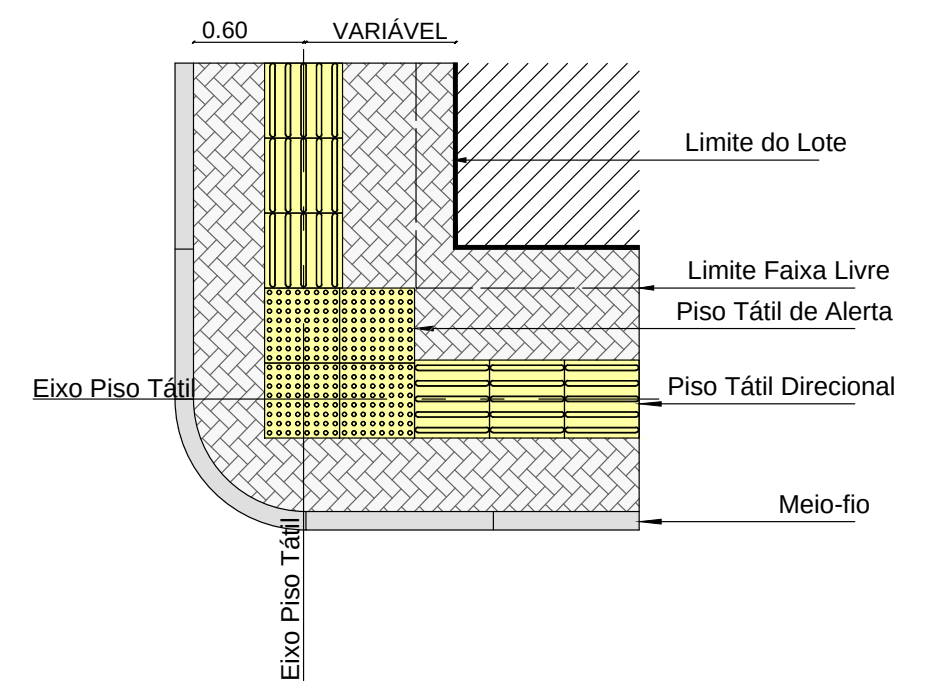
0.60
VARIÁVEL
Limite do Lote
Limite Faixa Livre
Piso Tátil de Alerta
Eixo Piso Tátil
Piso Tátil Direcional
Meio-fio
Eixo Piso Tátil

Detalhe 03 – Mudança de direção – Entre 90° e 150° (D03-MD)
escala 25

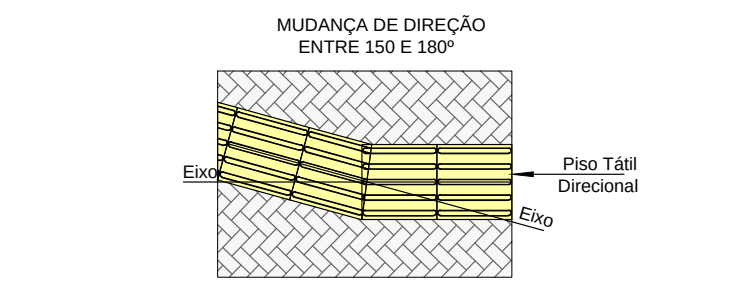
MUDANÇA DE DIREÇÃO ENTRE 150 E 180°
Eixo
Piso Tátil Direcional
Eixo

Detalhe 04 – Mudança de direção entre 150° e 180° (D04-MD)
escala 25

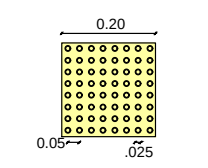

Detalhe 05 – Piso Tátil de Alerta
escala 25

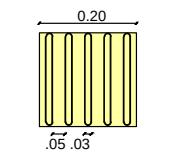

Detalhe 06 – Piso Tátil Direcional
escala 25

PROPRIETÁRIO Prefeitura Municipal de Coremas- PB

Kleber Sá de Oliveira
Engenheiro Civil
CREA 1602682780

PROJETISTA Kleber Sá de Oliveira

EPE EMPRESA PARAIBA DE ENGENHARIA	PROJETO: PAVIMENTAÇÃO DE RUAS E VIAS LOCAL: MUNICÍPIO DE COREMAS - PB PROPRIETÁRIO: PREFEITURA MUNICIPAL DE COREMAS - PB

FOLHA 02/07	ESCALA: Indicadas	DESENHOS: Indicados	RESPONSÁVEL TÉCNICO: Kleber Sá de Oliveira Crea: 160391676-8
ARQUIVO: PAV_COREMAS_FINAL P+B_2022.dwg	DESENHO: Diego Medeiros		ANOTAÇÕES: DATA: SET - 2022

Rua Francisco Batista Silva

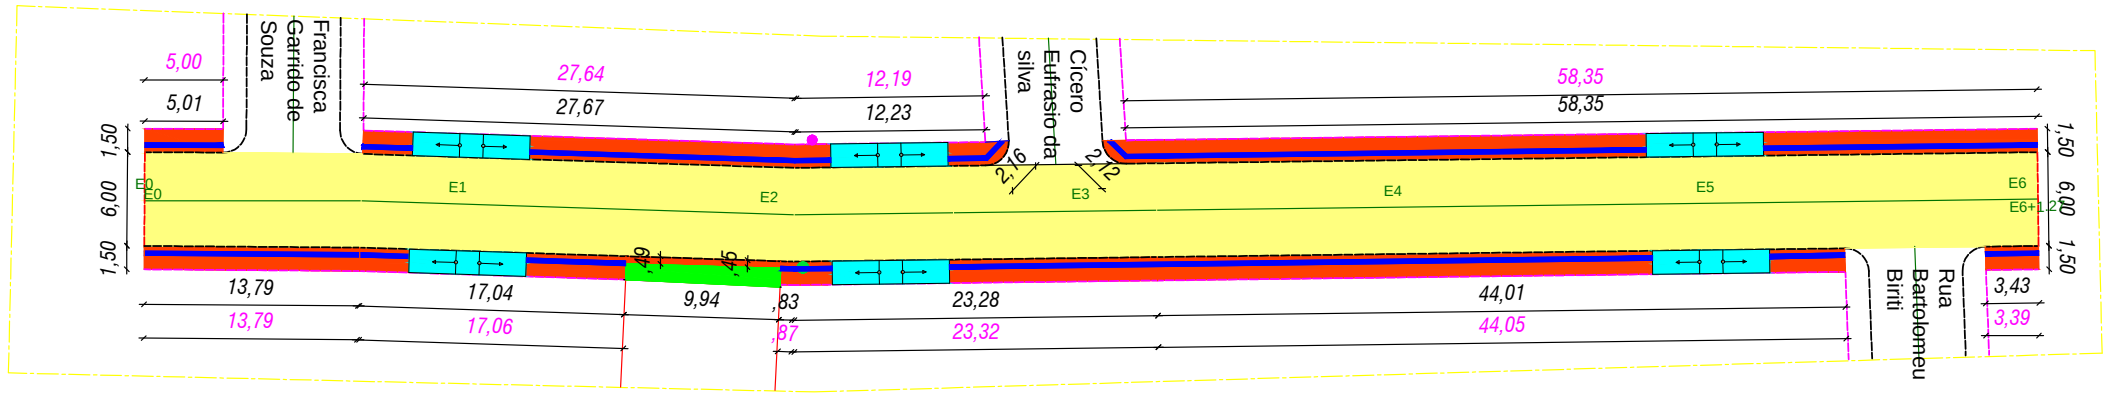
Francisca Garrido de Souza
Cicero Eufresio da Silva
Rua Bartolomeu Bim
5,00
5,01
27,64
27,67
12,19
12,23
58,35
58,35
1,50 6,00 1,50
13,79
13,79
17,04
17,06
9,94
23,28
23,32
44,01
44,05
3,43
3,39
E0
E1
E2
E3
E4
E5
E6
E6+1,27

PLANTA BAIXA - CALÇADAS E MEIO-FIO
Escala: 1:300

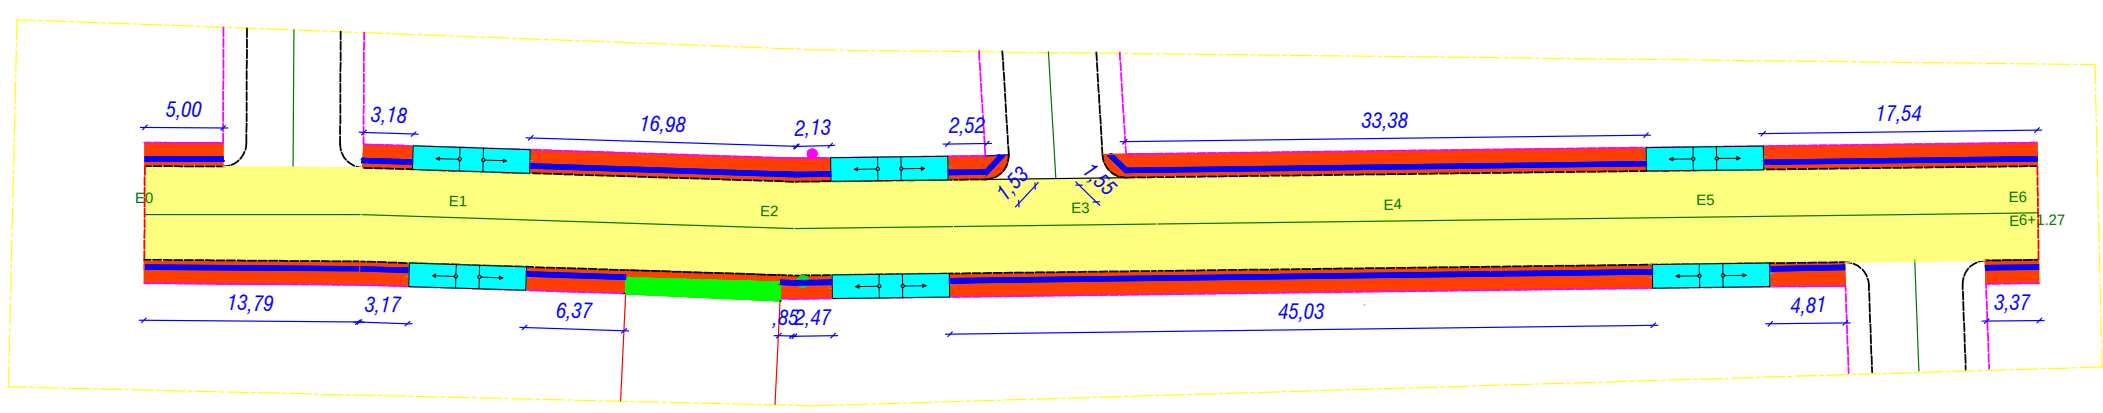
5,00
3,18
16,98
2,13
2,52
33,38
17,54
13,79
3,17
6,37
2,47
45,03
4,81
3,37
E0
E1
E2
E3
E4
E5
E6
E6+1,27

PLANTA BAIXA - ROTAS ACESSIVEIS E SINALIZAÇÃO
Escala: 1:300

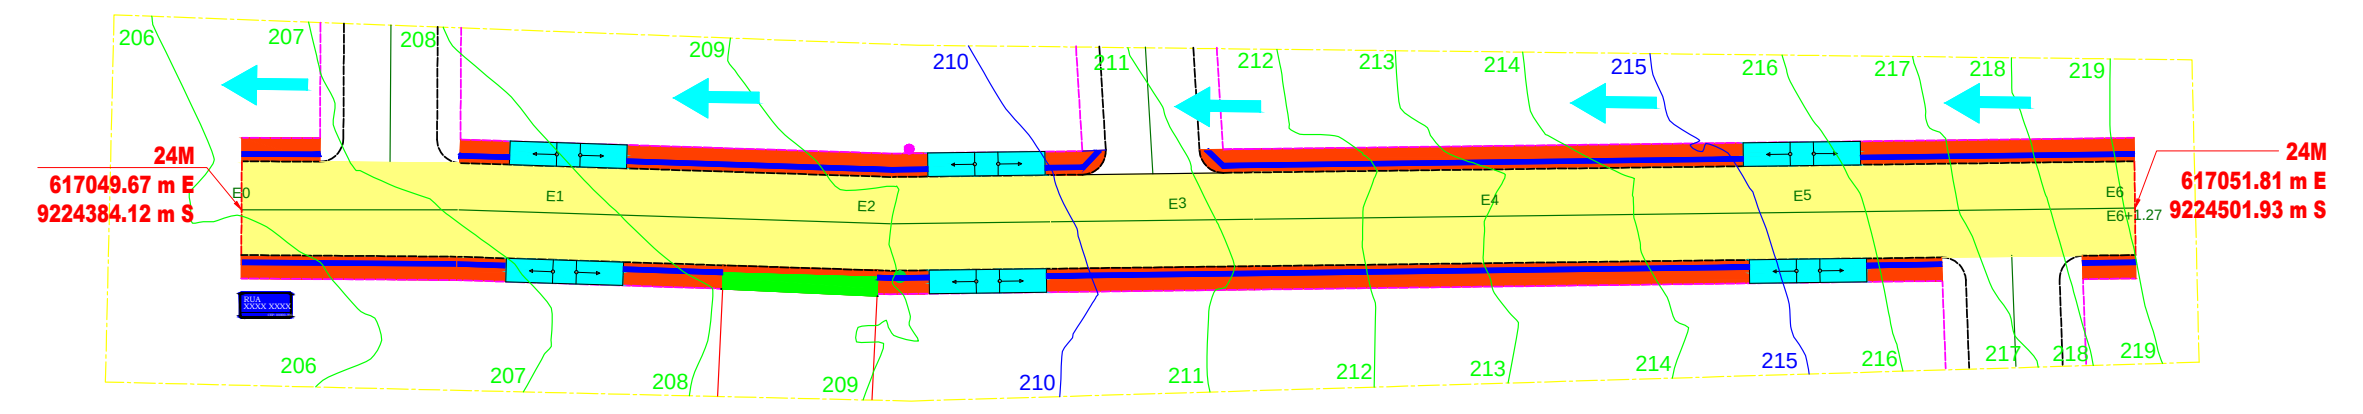
206
207
208
209
210
211
212
213
214
215
216
217
218
219
24M
617049.67 m E
9224384.12 m S
24M
617051.81 m E
9224501.93 m S
E0
E1
E2
E3
E4
E5
E6
E6+1.27

PLANTA BAIXA - ROTAS ACESSIVEIS E SINALIZAÇÃO
Escala: 1:300

RUA FRANCISCO BATISTA SILVA - SEÇÕES
ESC.: 1:200

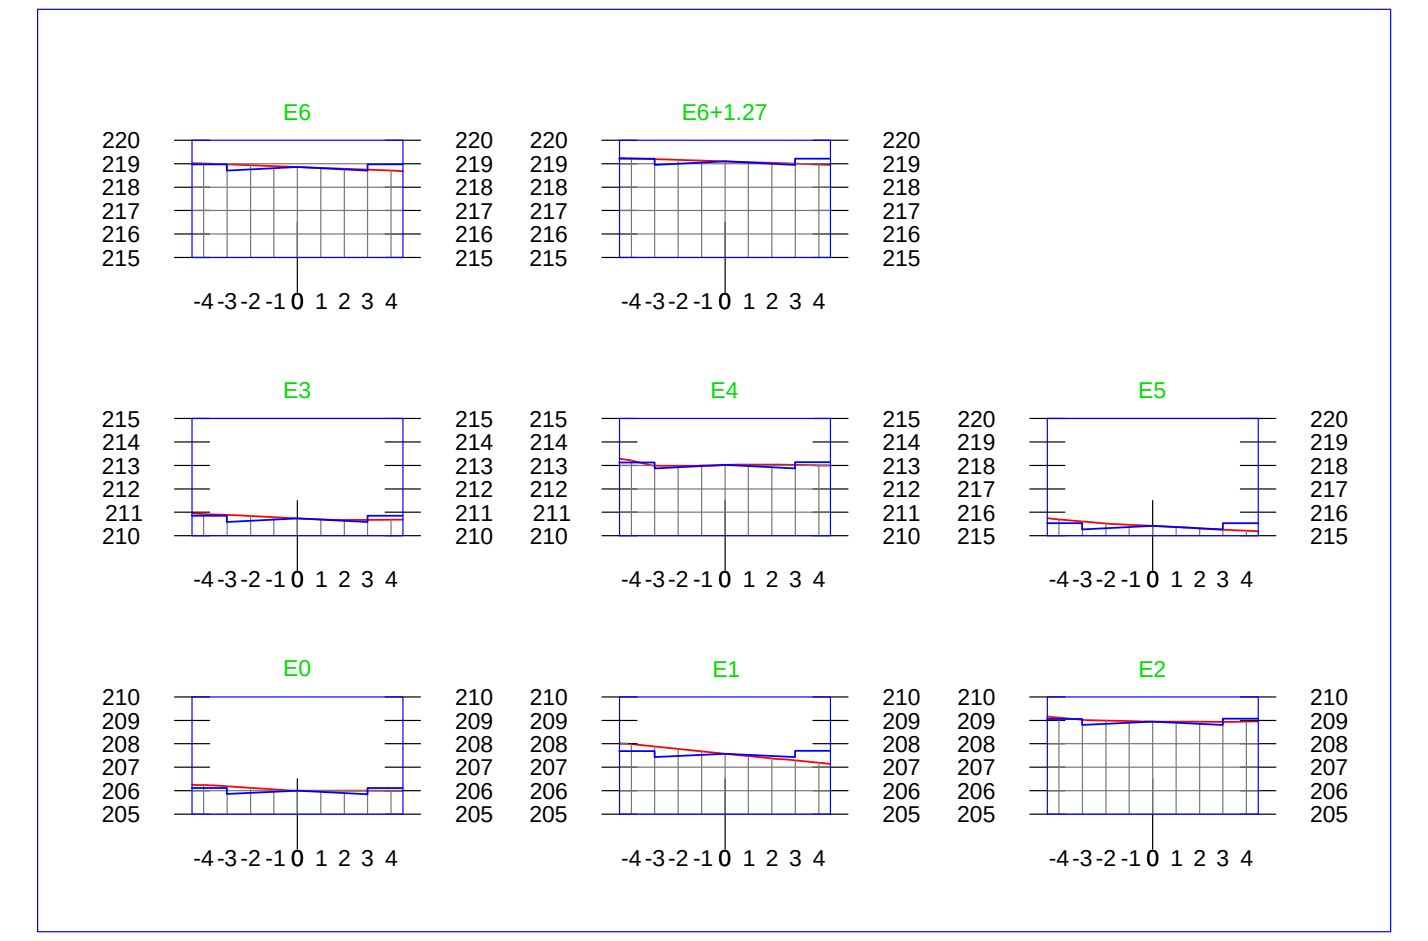

Legenda

Pavimentação

- 🟨 Pavimentação à Construir
- ▨ Pavimento Existente
- Meio-fio Existente
- Meio-fio Projetado
- Cordão em Granito
- Alvenaria de 1 vez
- Cerca
- Sentido do Caimento da água

Passeio

- 🟥 Calçadas à Construir
- 🟩 Calçadas Existentes
- 🟦 Piso Tátil
- Rampa de Acesso
- ● Poste Existente
- ● Poço de Visita (PV)
- ● Árvore
- Edificação Existente
- Lote Projetado

Sinalização

- Placa de Parada Obrigatória
- Placa com Nome da rua

RUA FRANCISCO BATISTA SILVA - PERFIL
ESC.: 1:300

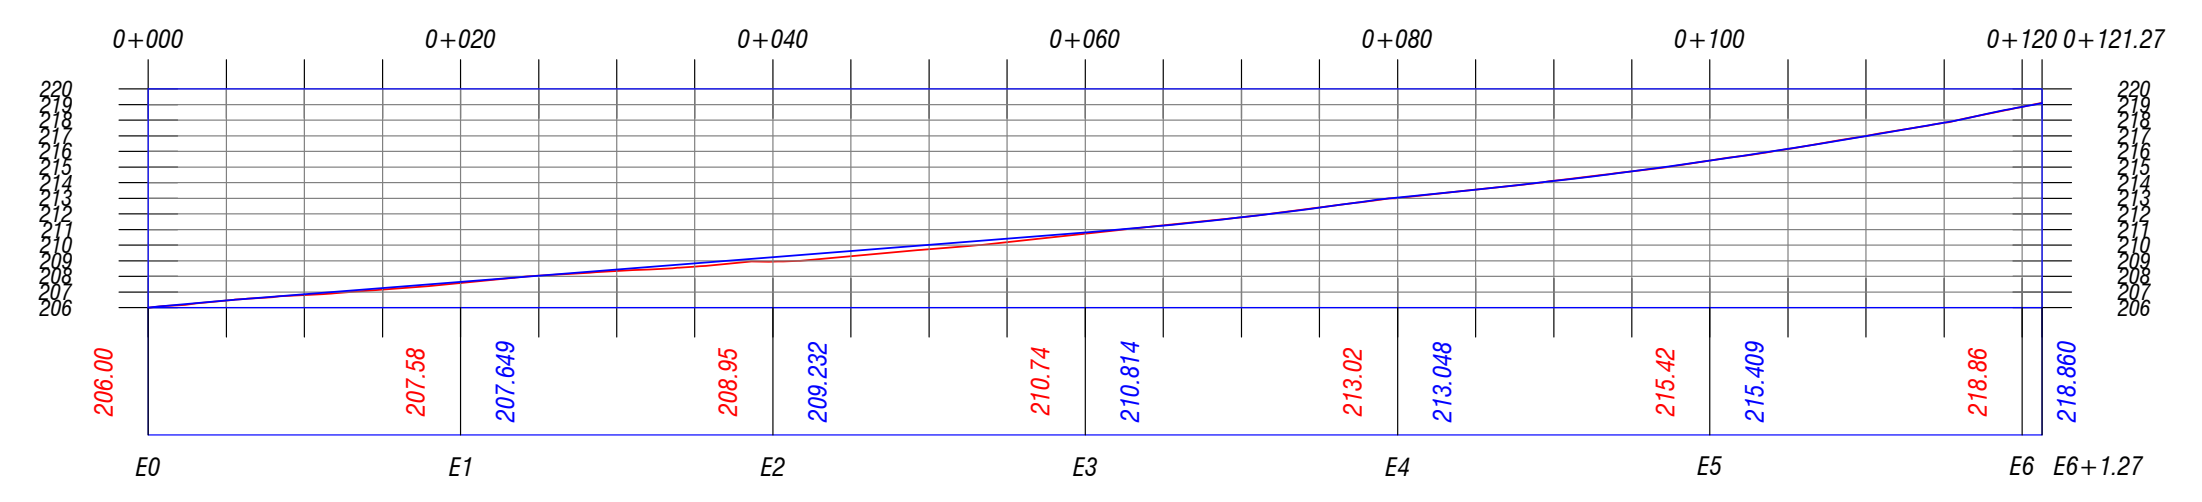

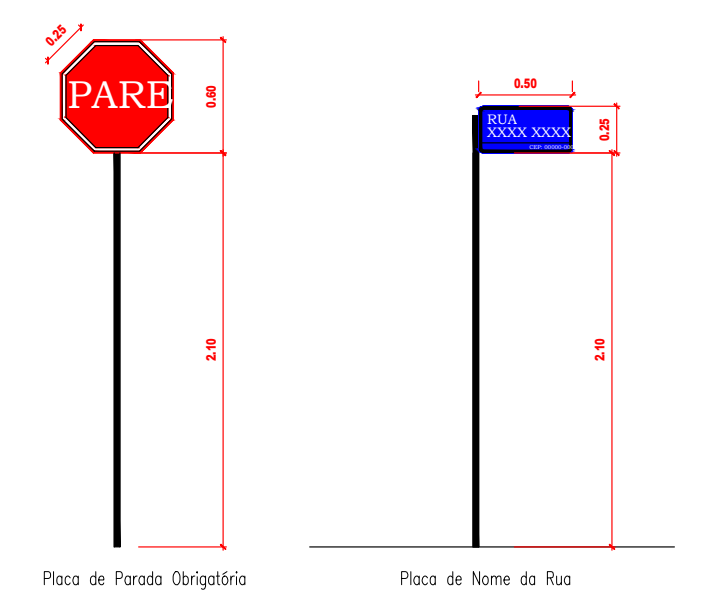
PARE
RUA XXXX XXXX

Placa de Parada Obrigatória

Placa de Nome da Rua

Detalhe – Sinalização Vertical
1:25

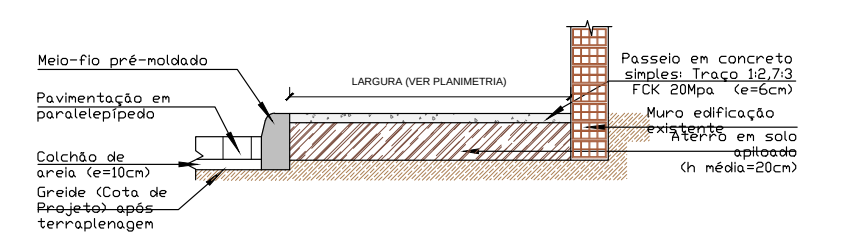
Meio-fio pré-moldado
Pavimentação em paralelepípedo
Colchão de areia (e=10cm)
Greide (Cota de Projeto) após terraplenagem
LARGURA (VER PLANIMETRIA)
Passeio em concreto simples: Traço 1:2,7:3 FCK 20Mpa (e=6cm)
Muro edificação existente
Aterro em solo apiloado (h média=20cm)

Detalhe 01 – Passeio Para Trechos s/ Alvenaria de 1 Vez
escala 25

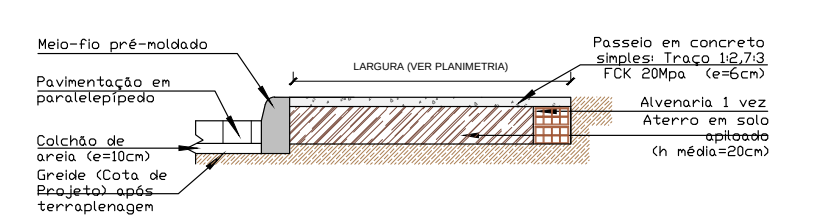
Meio-fio pré-moldado
Pavimentação em paralelepípedo
Colchão de areia (e=10cm)
Greide (Cota de Projeto) após terraplenagem
LARGURA (VER PLANIMETRIA)
Passeio em concreto simples: Traço 1:2,7:3 FCK 20Mpa (e=6cm)
Alvenaria 1 vez
Aterro em solo apiloado (h média=20cm)

Detalhe 02 – Passeio Para Trechos c/ Alvenaria de 1 Vez
escala 25

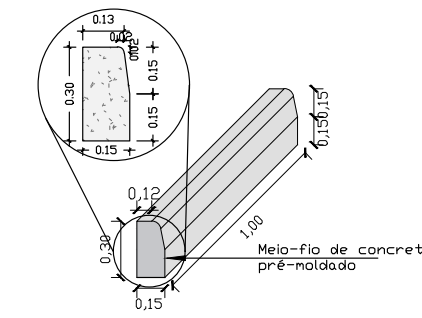
Meio-fio de concreto pré-moldado

Detalhe – Meio-fio
escala 25

Nota: Para o cálculo do quantitativo de concreto do passeio público, considera-se a dimensão da largura conforme indicado nos detalhe dos passeios.

Seção-Tipo de Pavimentação

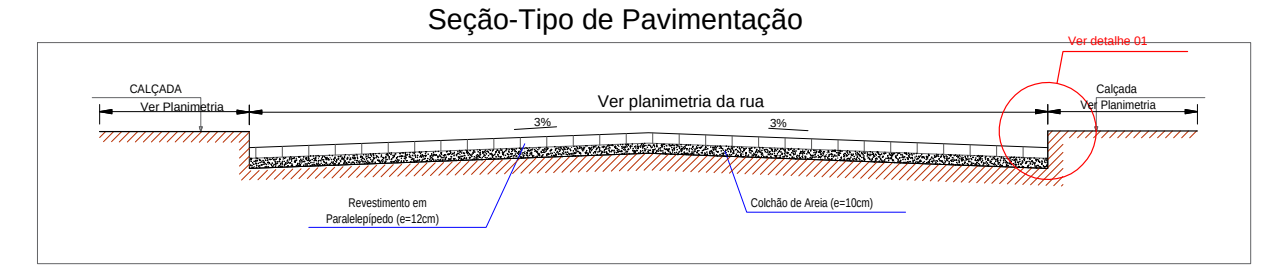
CALÇADA
Ver Planimetria
Ver planimetria da rua
2%
2%
Calçada
Ver Planimetria

Sem Escala

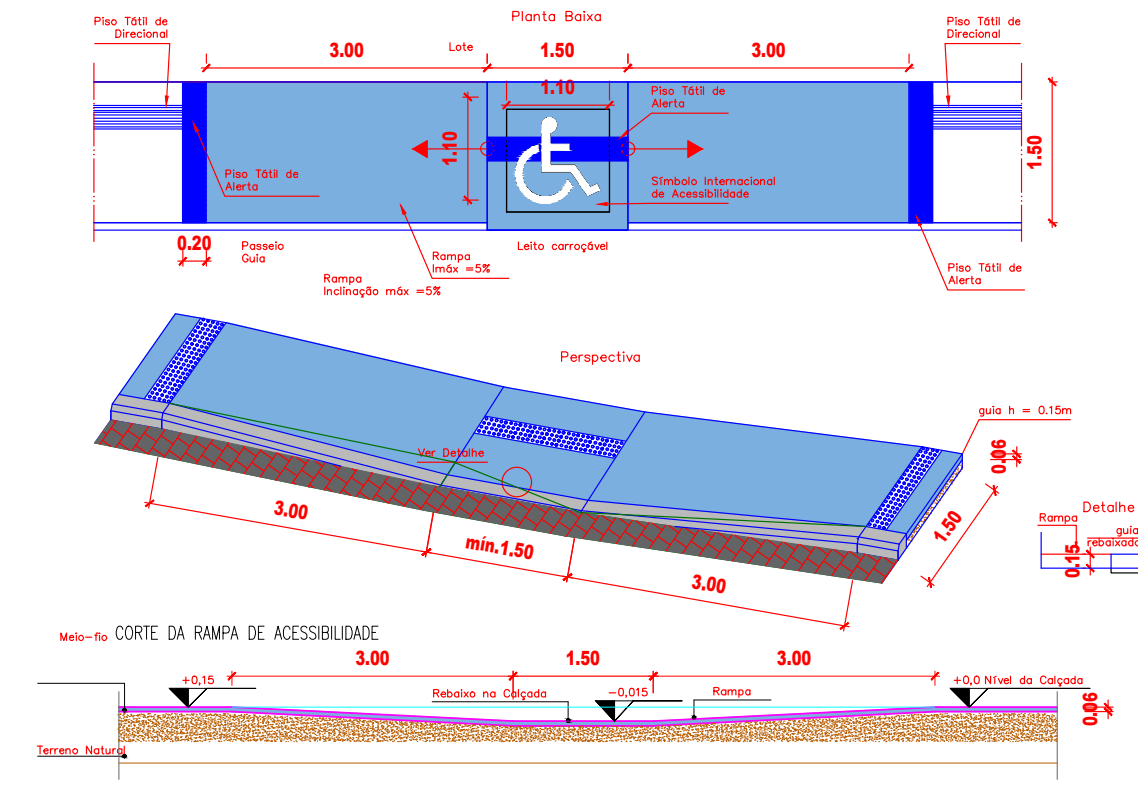
Planta Baixa
3.00
1.50
3.00
Perspectiva
3.00
min.1,50
3.00
CORTE DA RAMPA DE ACESSIBILIDADE

Detalhe – Rampa de Acessibilidade
1:50

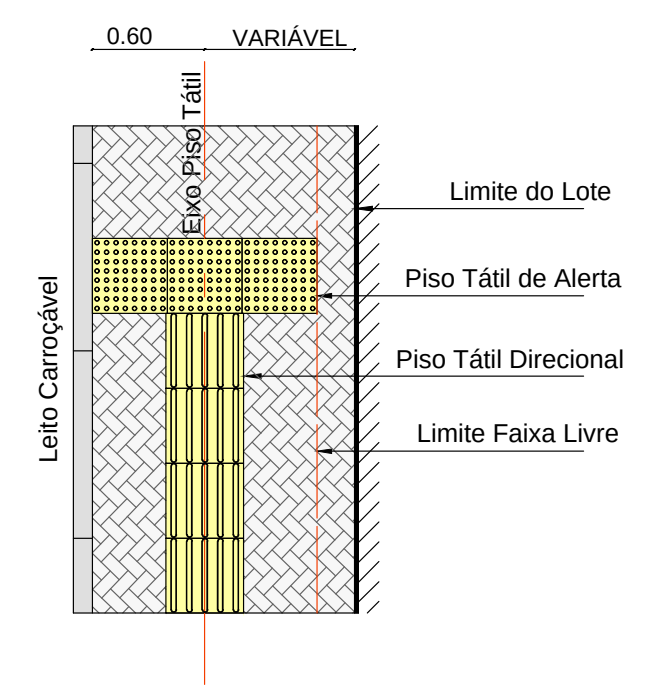
0.60
VARIÁVEL
Eixo Piso Tátil
Limite do Lote
Piso Tátil de Alerta
Piso Tátil Direcional
Limite Faixa Livre
Leito Carroçável

Detalhe 01 – Início/Fim Piso Tátil (D01-IFPT)
escala 25

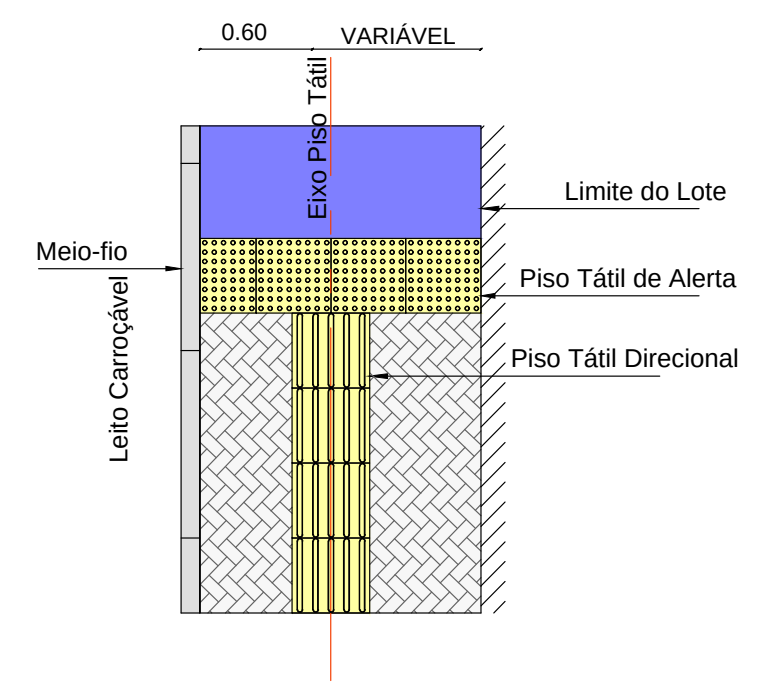
0.60
VARIÁVEL
Eixo Piso Tátil
Limite do Lote
Meio-fio
Piso Tátil de Alerta
Piso Tátil Direcional
Leito Carroçável

Detalhe 02 – Encontro Piso Tátil com Rampa (D02-EPTR)
escala 25

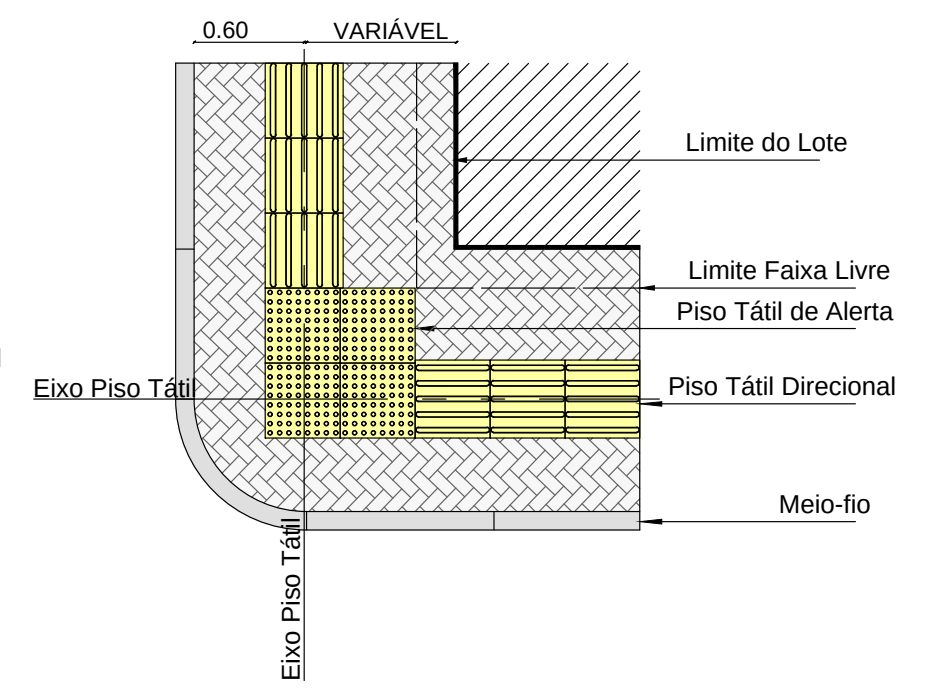
0.60
VARIÁVEL
Limite do Lote
Limite Faixa Livre
Piso Tátil de Alerta
Eixo Piso Tátil
Piso Tátil Direcional
Meio-fio
Eixo Piso Tátil

Detalhe 03 – Mudança de direção – Entre 90° e 150° (D03-MD)
escala 25

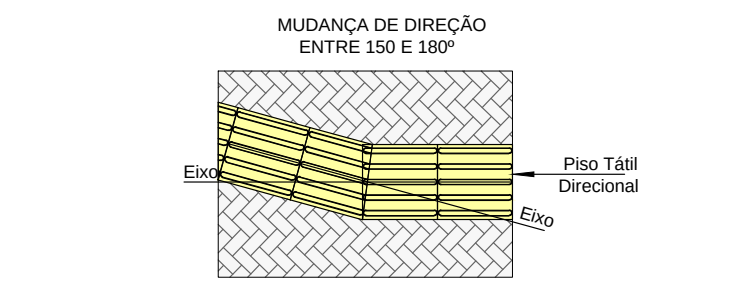
MUDANÇA DE DIREÇÃO ENTRE 150 E 180°
Eixo
Piso Tátil Direcional
Eixo

Detalhe 04 – Mudança de direção entre 150° e 180° (D04-MD)
escala 25

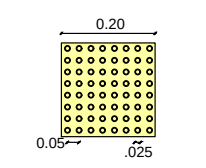

Detalhe 05 – Piso Tátil de Alerta
escala 25

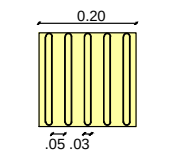

Detalhe 06 – Piso Tátil Direcional
escala 25

PROPRIETÁRIO Prefeitura Municipal de Coremas- PB

Kleber Sá de Oliveira
Engenheiro Civil
CREA 1602682780

PROJETISTA Kleber Sá de Oliveira

EPE EMPRESA PARAIBA DE ENGENHARIA	PROJETO: PAVIMENTAÇÃO DE RUAS E VIAS LOCAL: MUNICÍPIO DE COREMAS - PB PROPRIETÁRIO: PREFEITURA MUNICIPAL DE COREMAS - PB

FOLHA 03/07	ESCALA: Indicadas	DESENHOS: Indicados	RESPONSÁVEL TÉCNICO: Kleber Sá de Oliveira Crea: 160391676-8
ARQUIVO: PAV_COREMAS_FINAL P+B_2022.dwg	DESENHO: Diego Medeiros		ANOTAÇÕES: DATA: SET - 2022

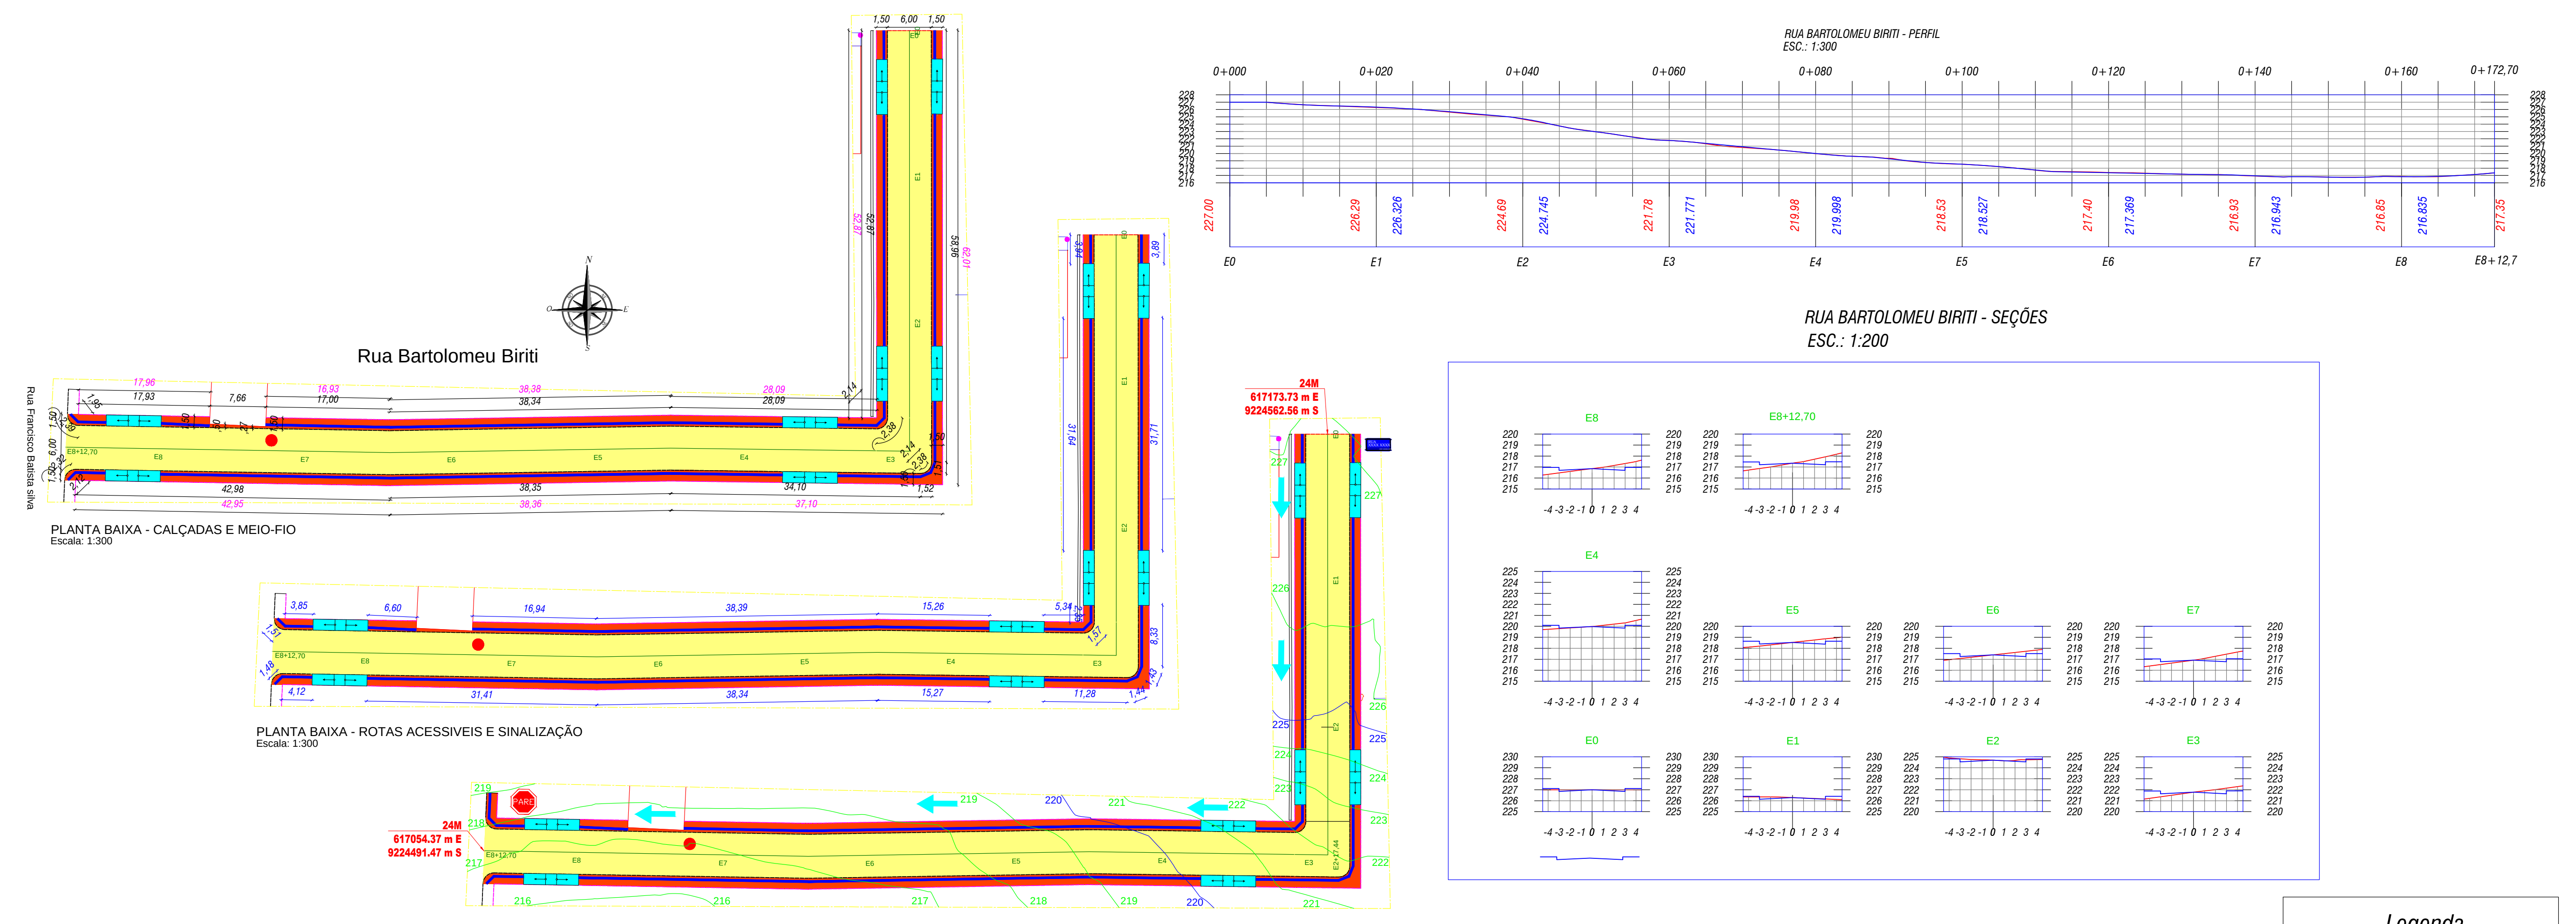
Rua Bartolomeu Biriti
Rua Francisco Batista silva
N
S
O
E
PARE
24M
617173.73 m E
9224562.56 m S
24M
617054.37 m E
9224491.47 m S
PLANTA BAIXA - CALÇADAS E MEIO-FIO
Escala: 1:300
PLANTA BAIXA - ROTAS ACESSIVEIS E SINALIZAÇÃO
Escala: 1:300
PLANTA BAIXA - ROTAS ACESSIVEIS E SINALIZAÇÃO
Escala: 1:300
RUA BARTOLOMEU BIRITI - PERFIL
ESC.: 1:300
0+000
0+020
0+040
0+060
0+080
0+100
0+120
0+140
0+160
0+172,70
227.00
226.29
226.326
224.69
224.745
221.78
221.771
219.98
219.998
218.53
218.527
217.40
217.369
216.93
216.943
216.85
216.835
217.35
E0
E1
E2
E3
E4
E5
E6
E7
E8
E8+12,7
RUA BARTOLOMEU BIRITI - SEÇÕES
ESC.: 1:200
E8
E8+12,70
E4
E5
E6
E7
E0
E1
E2
E3
-4 -3 -2 -1 0 1 2 3 4

Legenda

Pavimentação

🟨	Pavimentação à Construir
▒	Pavimento Existente
—	Meio-fio Existente
– – –	Meio-fio Projetado
– – –	Cordão em Granito
– – –	Alvenaria de 1 vez
—	Cerca
➡	Sentido do Caimento da água

Passeio

🟥	Calçadas à Construir
🟩	Calçadas Existentes
🟦	Piso Tátil
▭	Rampa de Acesso
●	Poste Existente
●	Poço de Visita (PV)
●	Árvore
—	Edificação Existente
—	Lote Projetado

Sinalização

PARE	Placa de Parada Obrigatória
🟦	Placa com Nome da rua

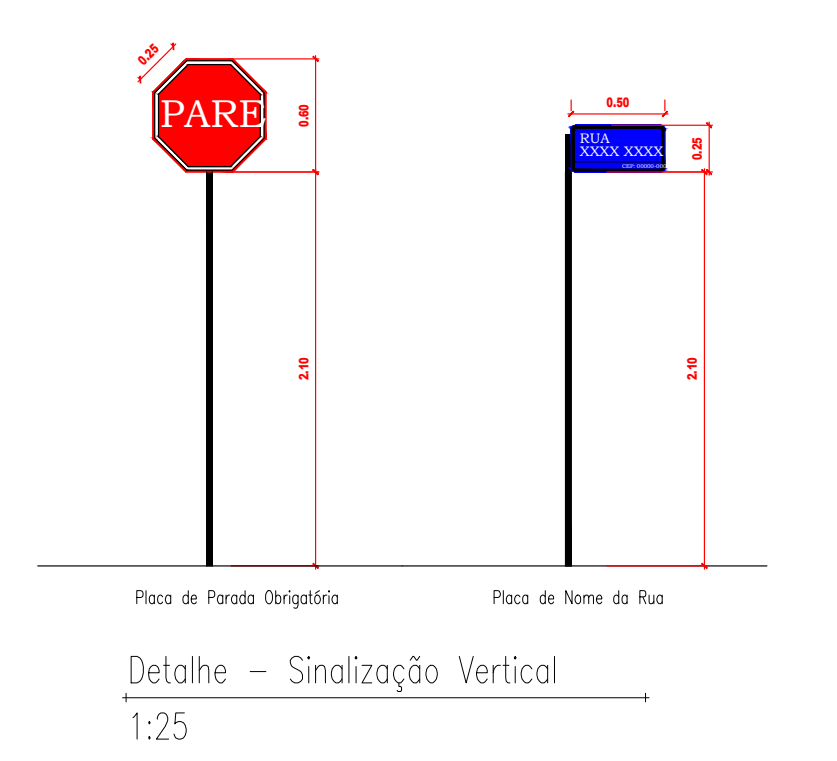
PARE
RUA XXXX XXXX
0.50
0.25
2.10
Placa de Parada Obrigatória
Placa de Nome da Rua

Detalhe – Sinalização Vertical
1:25

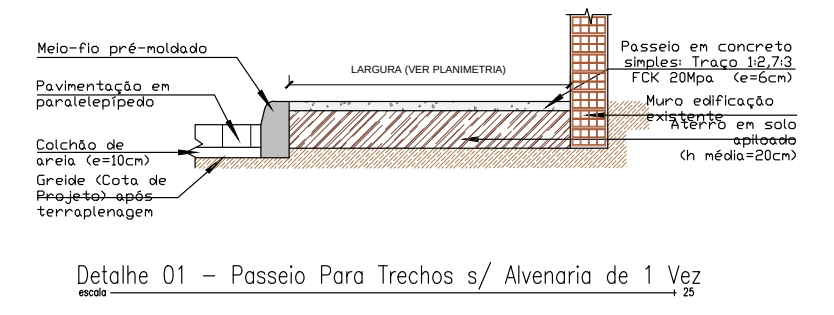
Meio-fio pré-moldado
Pavimentação em paralelepípedo
Colchão de areia (e=10cm)
Greide (Cota de Projeto) após terraplenagem
LARGURA (VER PLANIMETRIA)
Passeio em concreto simples: Traço 1:2,7:3 FCK 20Mpa (e=6cm)
Muro edificação existente
Aterro em solo apiloado (h média=20cm)

Detalhe 01 – Passeio Para Trechos s/ Alvenaria de 1 Vez

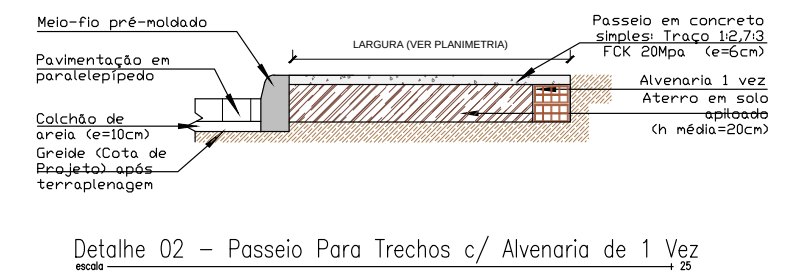
Meio-fio pré-moldado
Pavimentação em paralelepípedo
Colchão de areia (e=10cm)
Greide (Cota de Projeto) após terraplenagem
LARGURA (VER PLANIMETRIA)
Passeio em concreto simples: Traço 1:2,7:3 FCK 20Mpa (e=6cm)
Alvenaria 1 vez
Aterro em solo apiloado (h média=20cm)

Detalhe 02 – Passeio Para Trechos c/ Alvenaria de 1 Vez

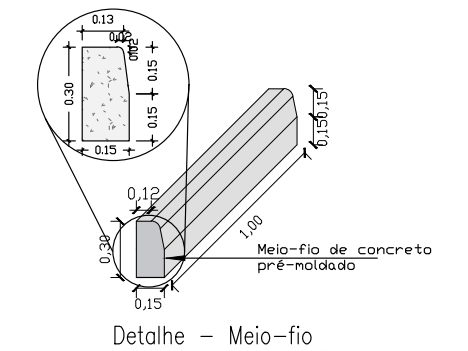
0.13
0.02
0.15
0.15
0.30
0.15
0,12
0,30
0,15
1,00
0,15
0,15
Meio-fio de concreto pré-moldado

Detalhe – Meio-fio

Nota: Para o cálculo do quantitativo de concreto do passeio público, considera-se a dimensão da largura conforme indicado nos detalhe dos passeios.

Seção-Tipo de Pavimentação

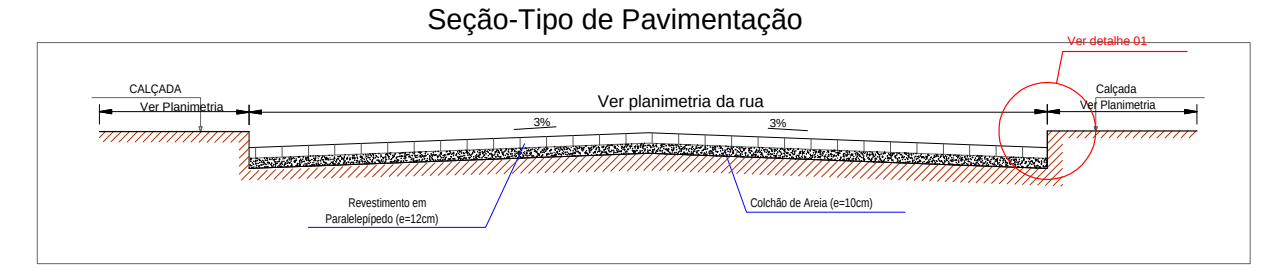
CALÇADA
Ver Planimetria
Ver planimetria da rua
2%
2%
Ver detalhe 01
Calçada
Ver Planimetria
Revestimento em Paralelepípedo (e=12cm)
Colchão de Areia (e=10cm)

Sem Escala

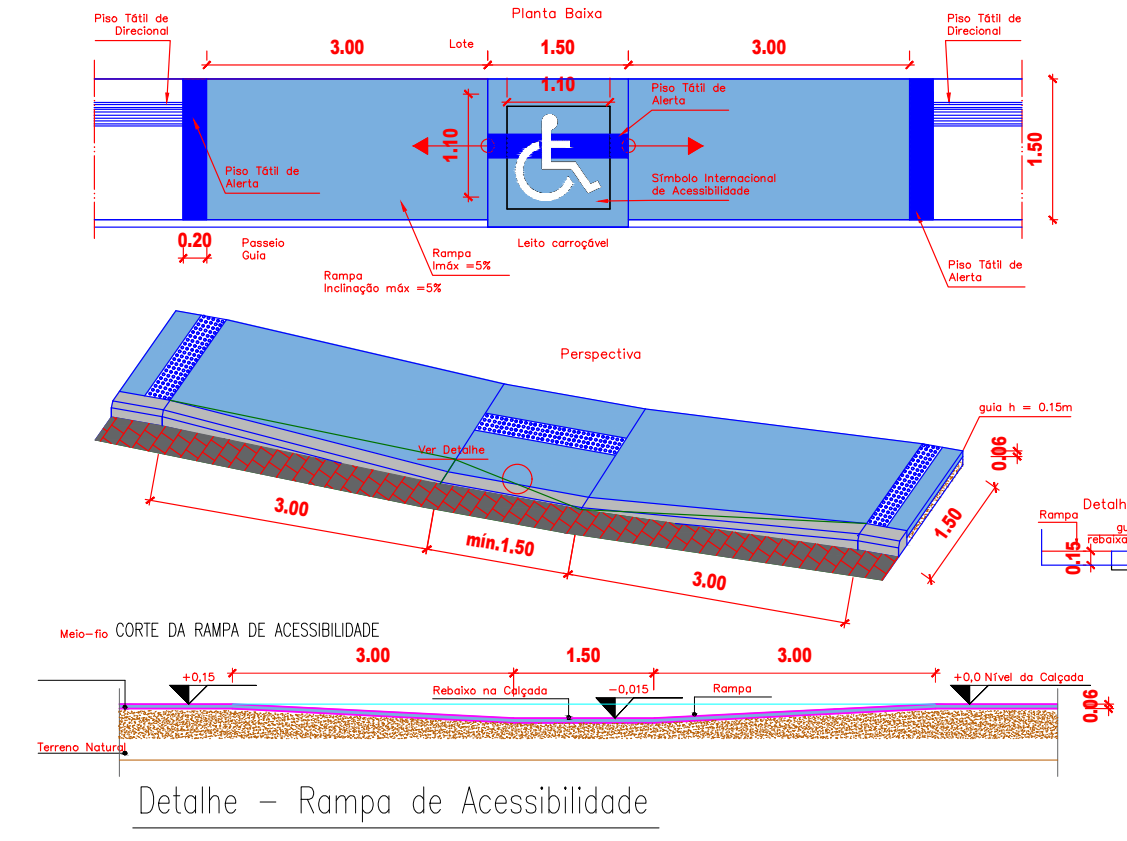
Planta Baixa
Piso Tátil de Direcional
3.00
Lote
1.50
3.00
1.10
Piso Tátil de Alerta
1.50
Símbolo Internacional de Acessibilidade
0.20
Passeio
Guia
Rampa
Leito carroçável
Perspectiva
3.00
min.1,50
3.00
1.50
Detalhe
CORTE DA RAMPA DE ACESSIBILIDADE
Meio-fio
3.00
1.50
3.00
Rebaixo na Calçada
Rampa
Terreno Natural

Detalhe – Rampa de Acessibilidade
1:50

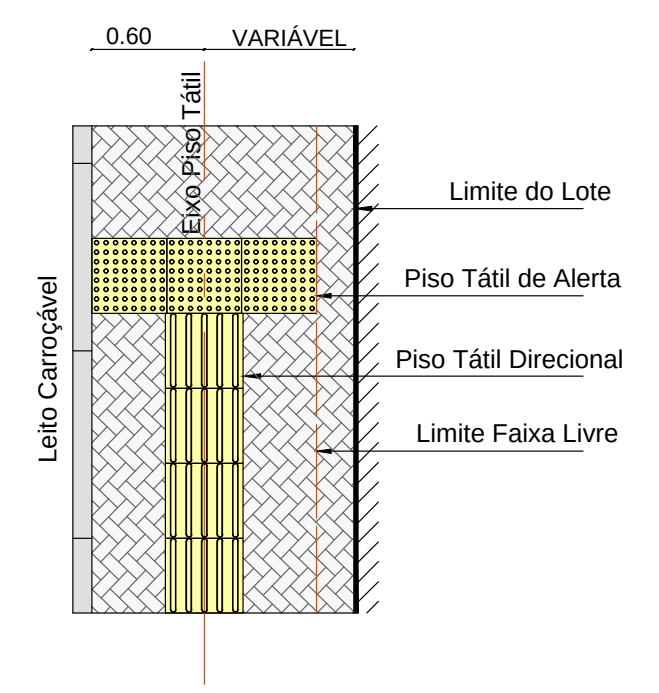
0.60
VARIÁVEL
Eixo Piso Tátil
Limite do Lote
Piso Tátil de Alerta
Piso Tátil Direcional
Limite Faixa Livre
Leito Carroçável

Detalhe 01 – Início/Fim Piso Tátil (D01-IFPT)

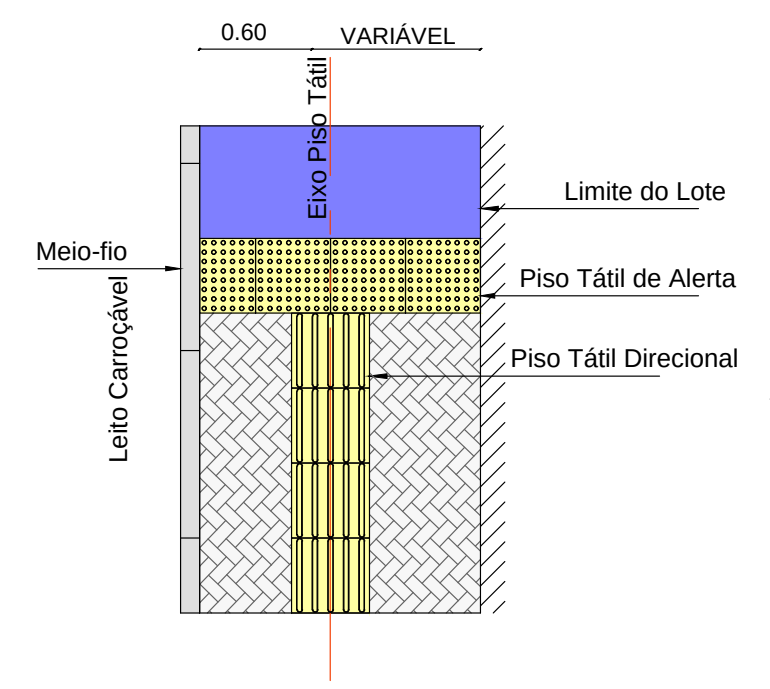
0.60
VARIÁVEL
Eixo Piso Tátil
Meio-fio
Limite do Lote
Piso Tátil de Alerta
Piso Tátil Direcional
Leito Carroçável

Detalhe 02 – Encontro Piso Tátil com Rampa (D02-EPTR)

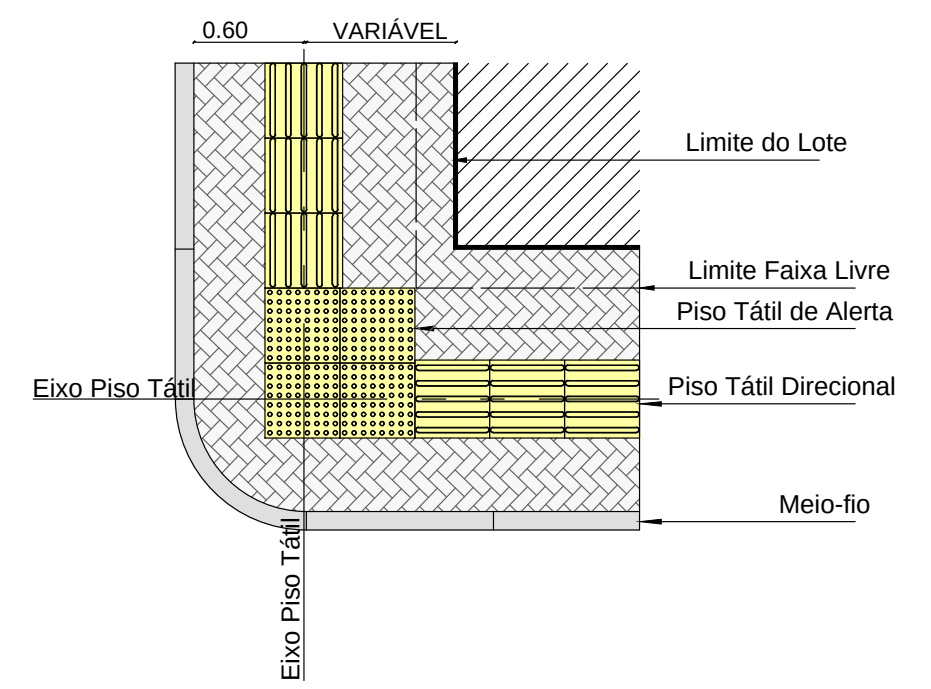
0.60
VARIÁVEL
Limite do Lote
Limite Faixa Livre
Piso Tátil de Alerta
Piso Tátil Direcional
Eixo Piso Tátil
Meio-fio
Eixo Piso Tátil

Detalhe 03 – Mudança de direção – Entre 90° e 150° (D03-MD)

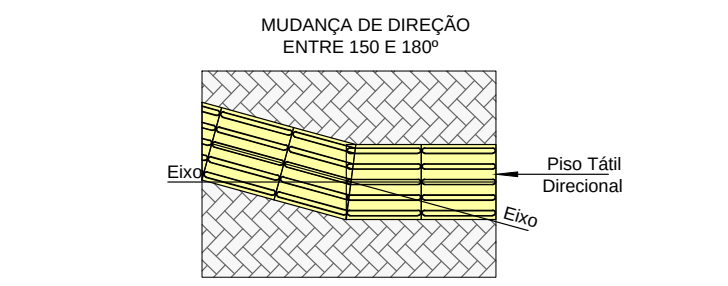
MUDANÇA DE DIREÇÃO ENTRE 150 E 180°
Eixo
Piso Tátil Direcional
Eixo

Detalhe 04 – Mudança de direção entre 150° e 180° (D04-MD)

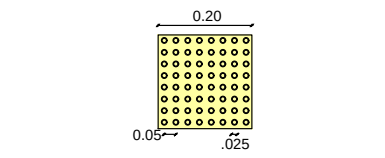

Detalhe 05 – Piso Tátil de Alerta

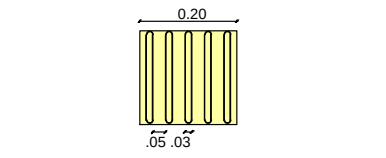

Detalhe 06 – Piso Tátil Direcional

PROPRIETÁRIO Prefeitura Municipal de Coremas- PB

Kleber Sá de Oliveira
Engenheiro Civil
CREA 1602682780

PROJETISTA Kleber Sá de Oliveira

EPE
EMPRESA PARAIBA DE ENGENHARIA

PROJETO: PAVIMENTAÇÃO DE RUAS E VIAS
LOCAL: MUNICÍPIO DE COREMAS - PB
PROPRIETÁRIO: PREFEITURA MUNICIPAL DE COREMAS - PB
FOLHA 04/07
ESCALA: Indicadas
DESENHOS: Indicados
RESPONSÁVEL TÉCNICO: Kleber Sá de Oliveira Crea: 160391676-8
ANOTAÇÕES:
ARQUIVO: PAV_COREMAS_FINAL_2022.dwg
DESENHO: Diego Medeiros
DATA: SET - 2022

RUA MARIA FARIAS DE ASSIS

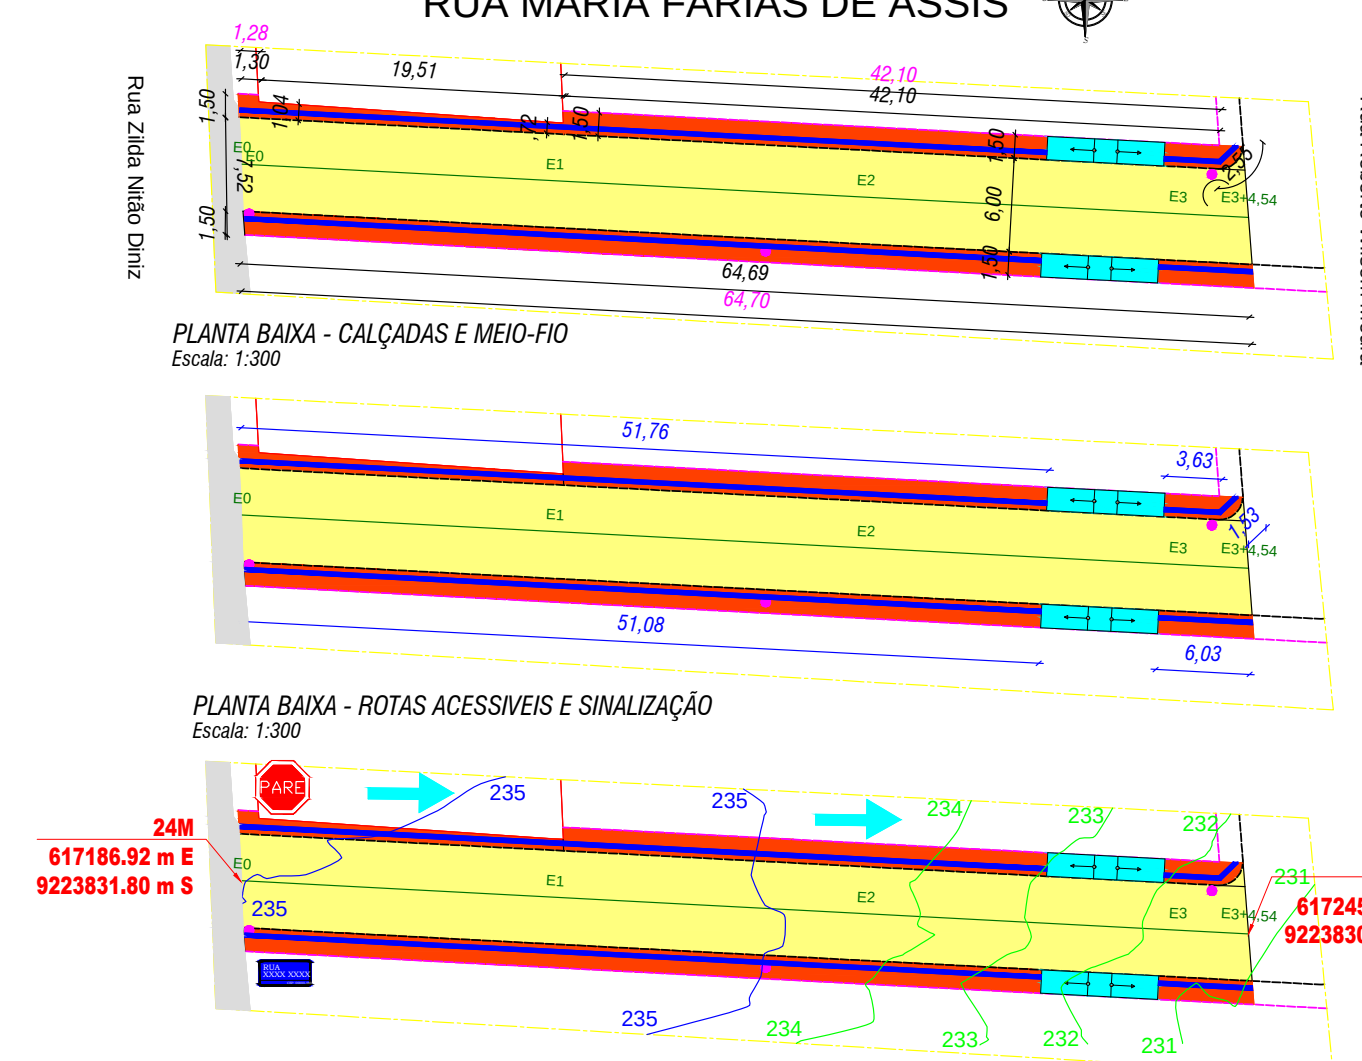
Rua Zilda Nildo Diniz
Rua Roberto Wilsom Moura
PARE
24M
617186.92 m E
9223831.80 m S
24M
617245.68 m E
9223830.02 m S
PLANTA BAIXA - CALÇADAS E MEIO-FIO
Escala: 1:300
PLANTA BAIXA - ROTAS ACESSIVEIS E SINALIZAÇÃO
Escala: 1:300
PLANTA BAIXA - ROTAS ACESSIVEIS E SINALIZAÇÃO
Escala: 1:300

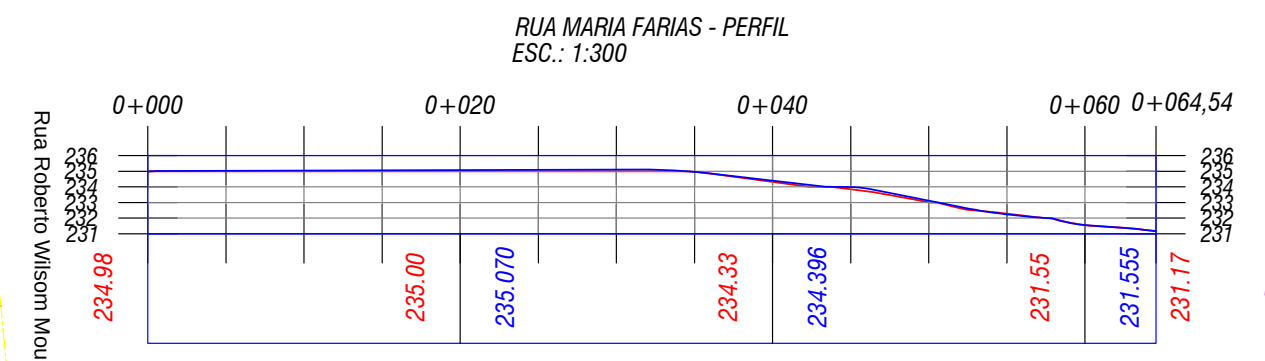

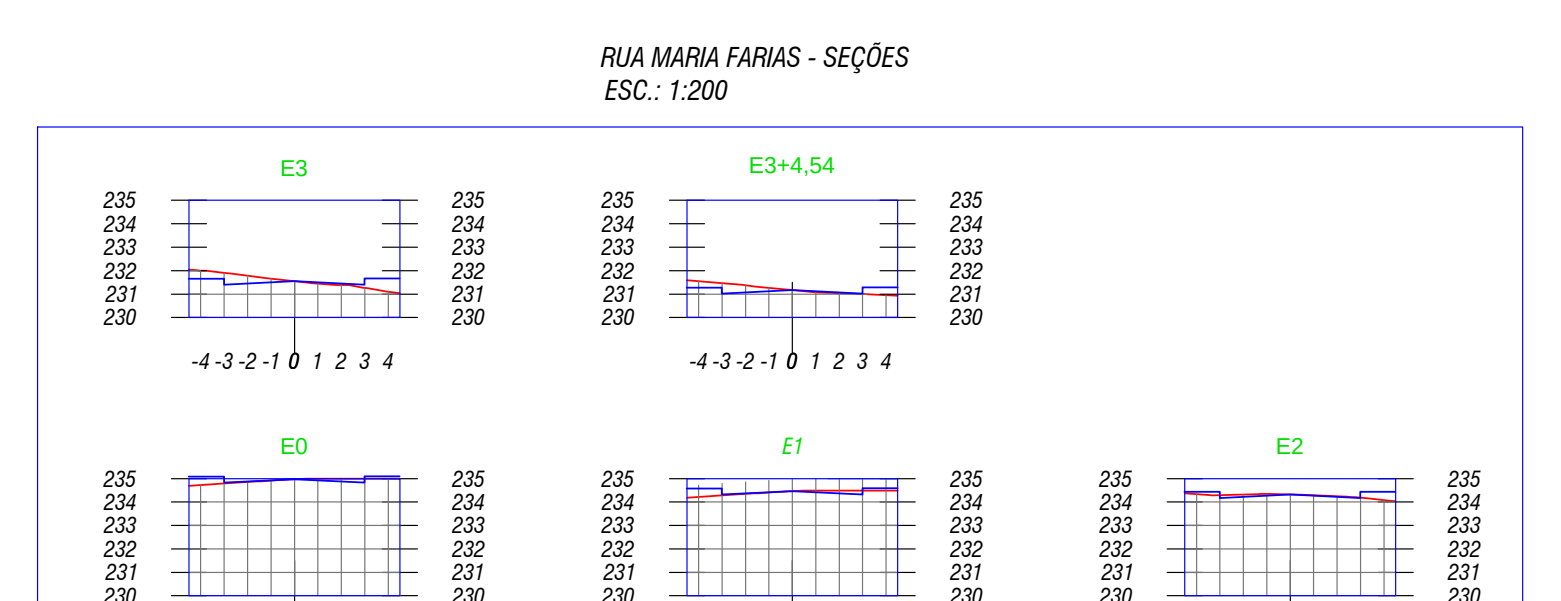
RUA MARIA FARIAS - SEÇÕES
ESC.: 1:200
E3
E3+4,54
E0
E1
E2
-4 -3 -2 -1 0 1 2 3 4

RUA ROBERTO WILSOM MOURA

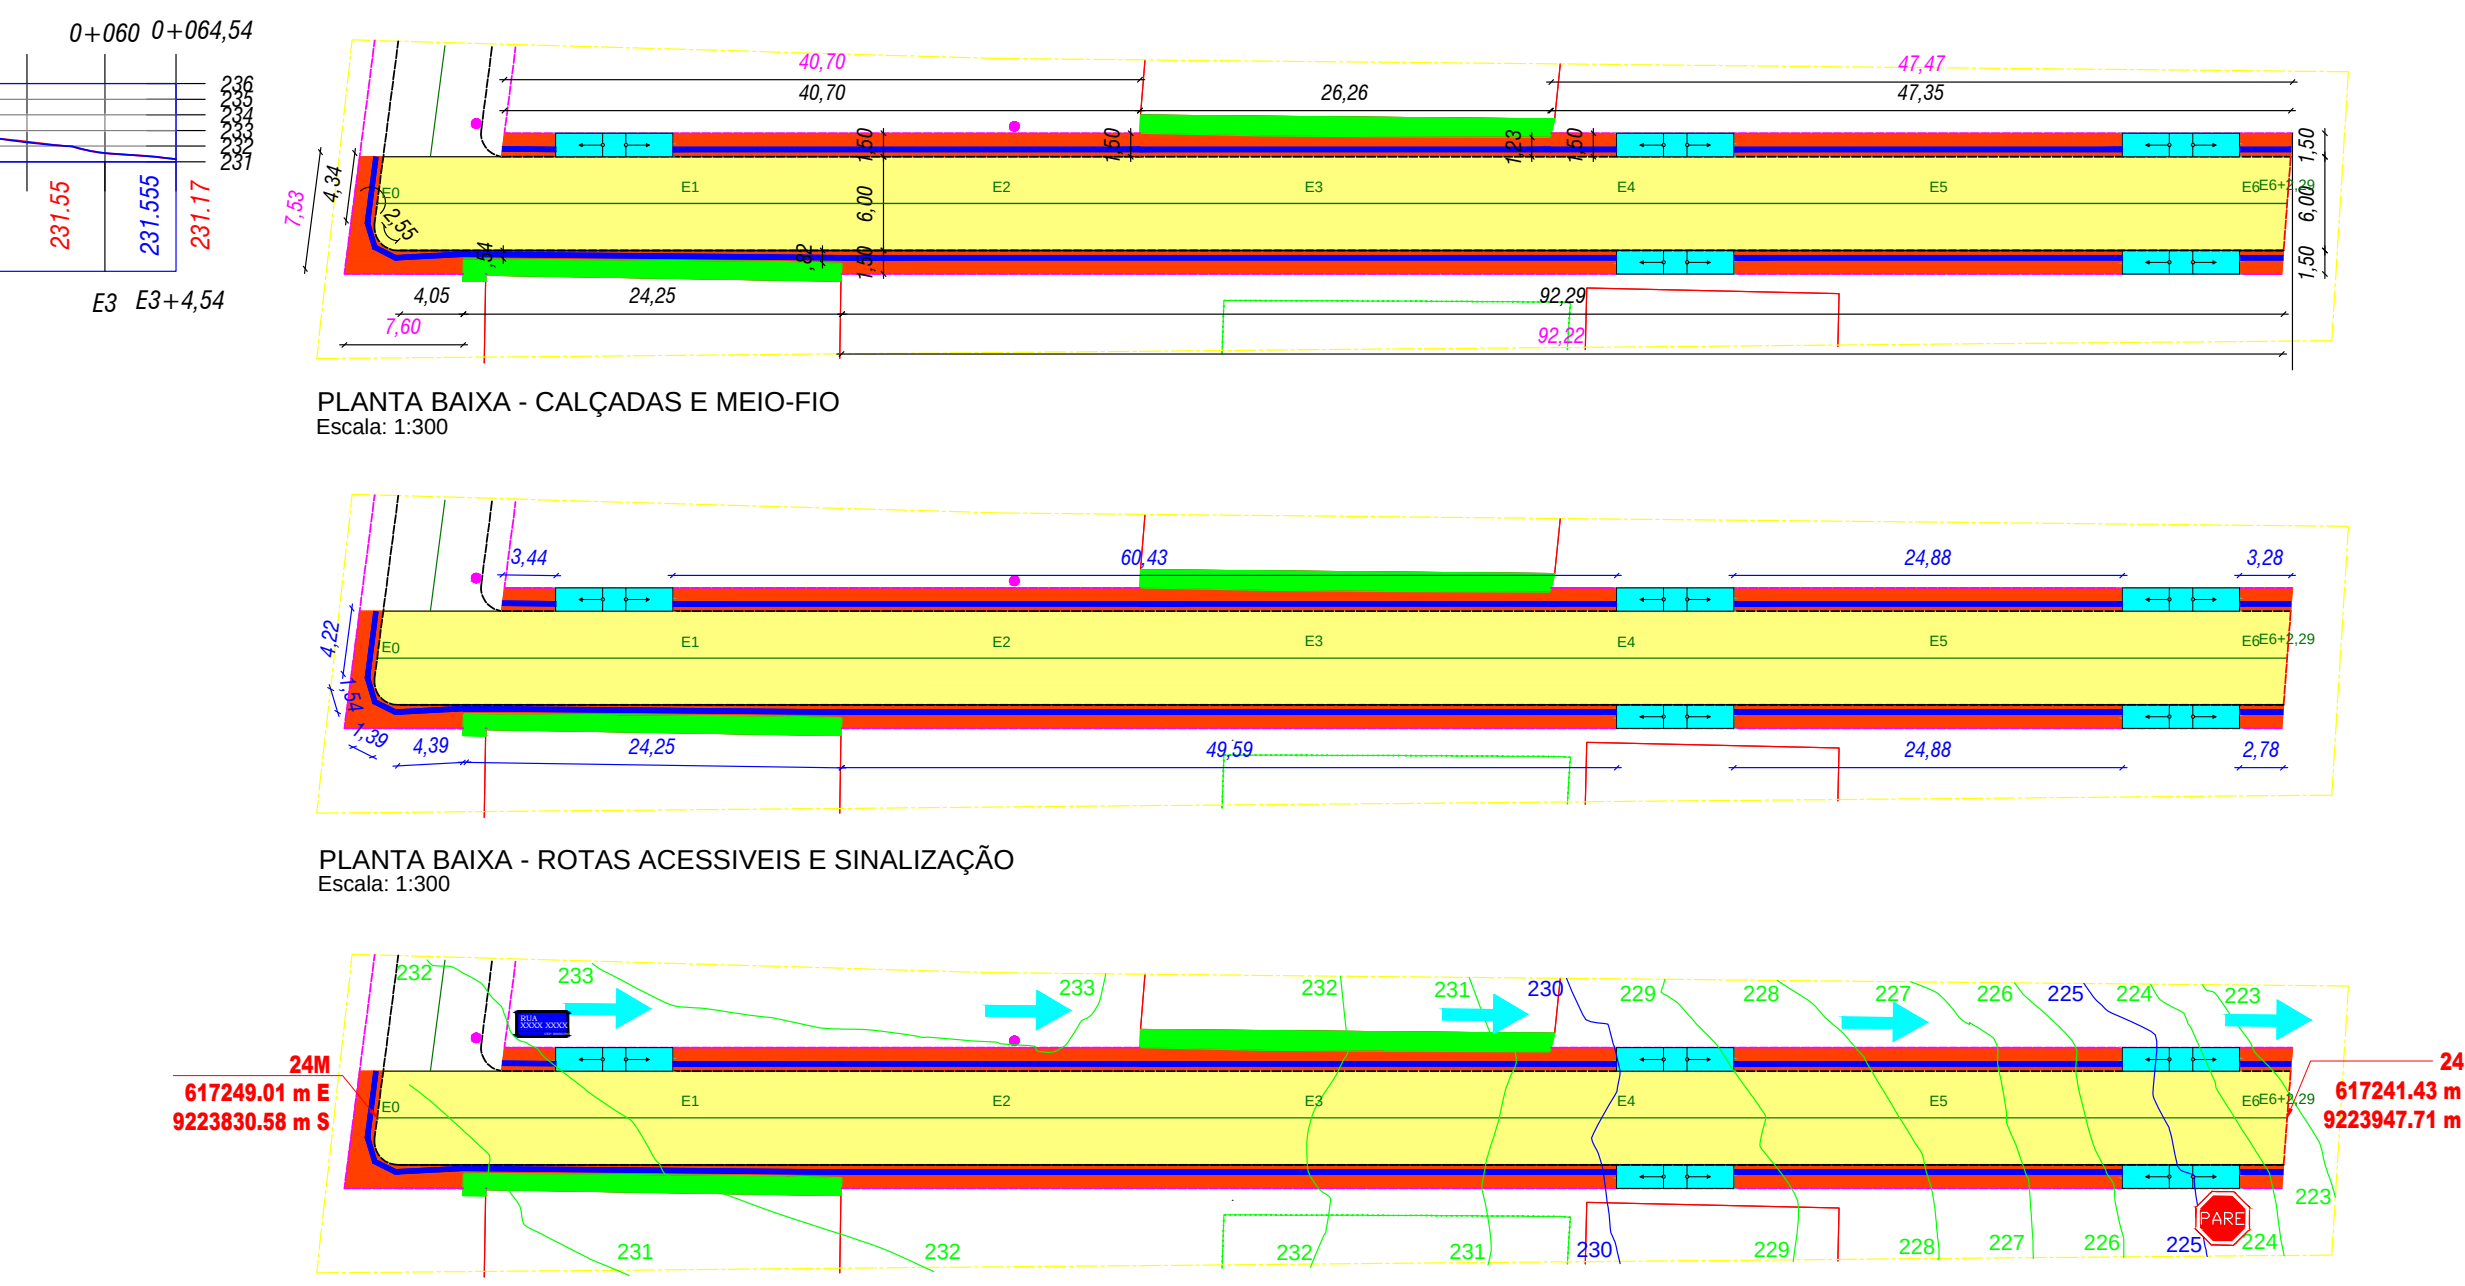
PARE
24M
617249.01 m E
9223830.58 m S
24M
617241.43 m E
9223947.71 m S
PLANTA BAIXA - CALÇADAS E MEIO-FIO
Escala: 1:300
PLANTA BAIXA - ROTAS ACESSIVEIS E SINALIZAÇÃO
Escala: 1:300
PLANTA BAIXA - ROTAS ACESSIVEIS E SINALIZAÇÃO
Escala: 1:300

Legenda

Pavimentação

🟨	Pavimentação à Construir
▒	Pavimento Existente
—	Meio-fio Existente
– – –	Meio-fio Projetado
– – –	Cordão em Granito
– – –	Alvenaria de 1 vez
—	Cerca
➡	Sentido do Caimento da água

Passeio

🟥	Calçadas à Construir
🟩	Calçadas Existentes
🟦	Piso Tátil
▭	Rampa de Acesso
●	Poste Existente
●	Poço de Visita (PV)
●	Árvore
—	Edificação Existente
—	Lote Projetado

Sinalização

PARE	Placa de Parada Obrigatória
🟦	Placa com Nome da rua

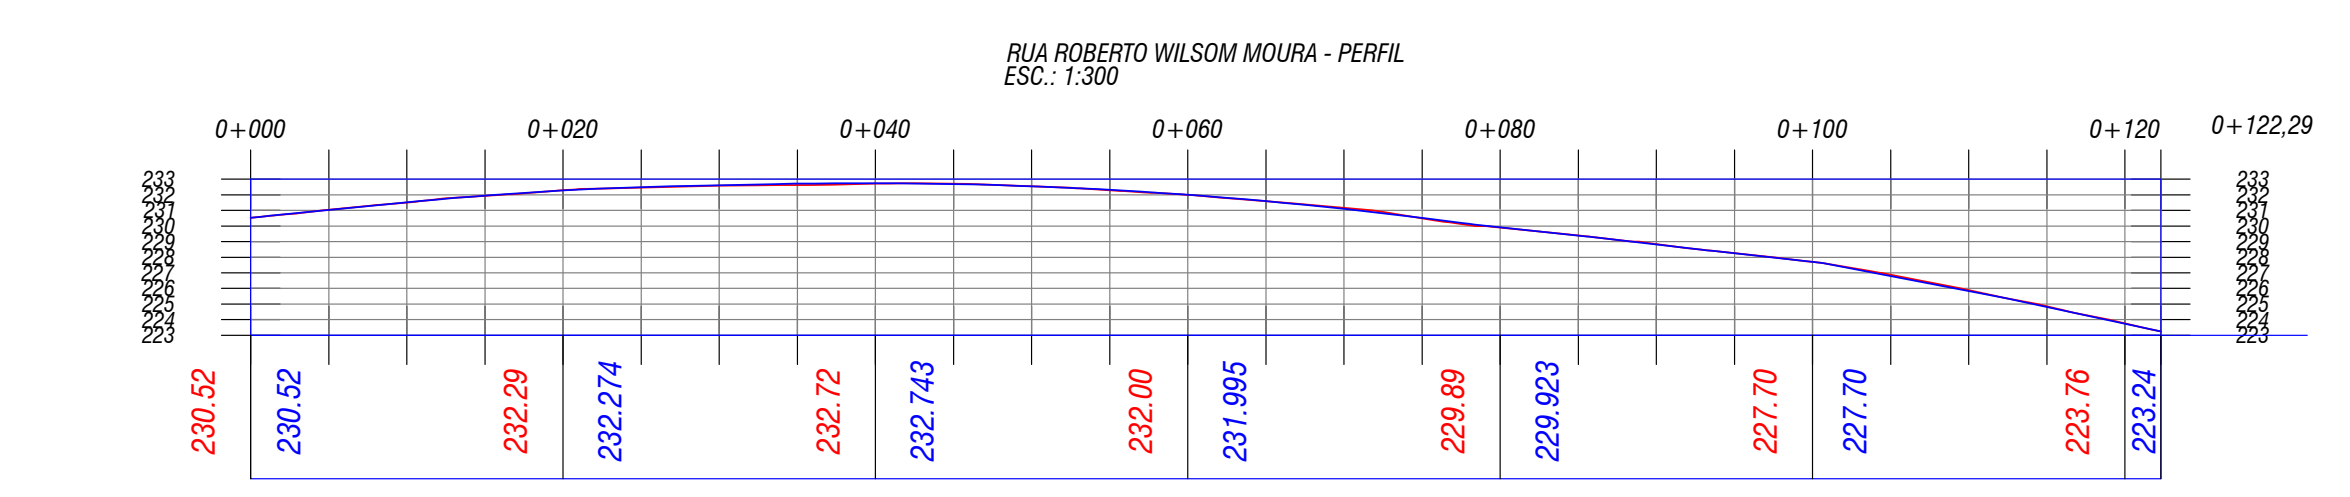

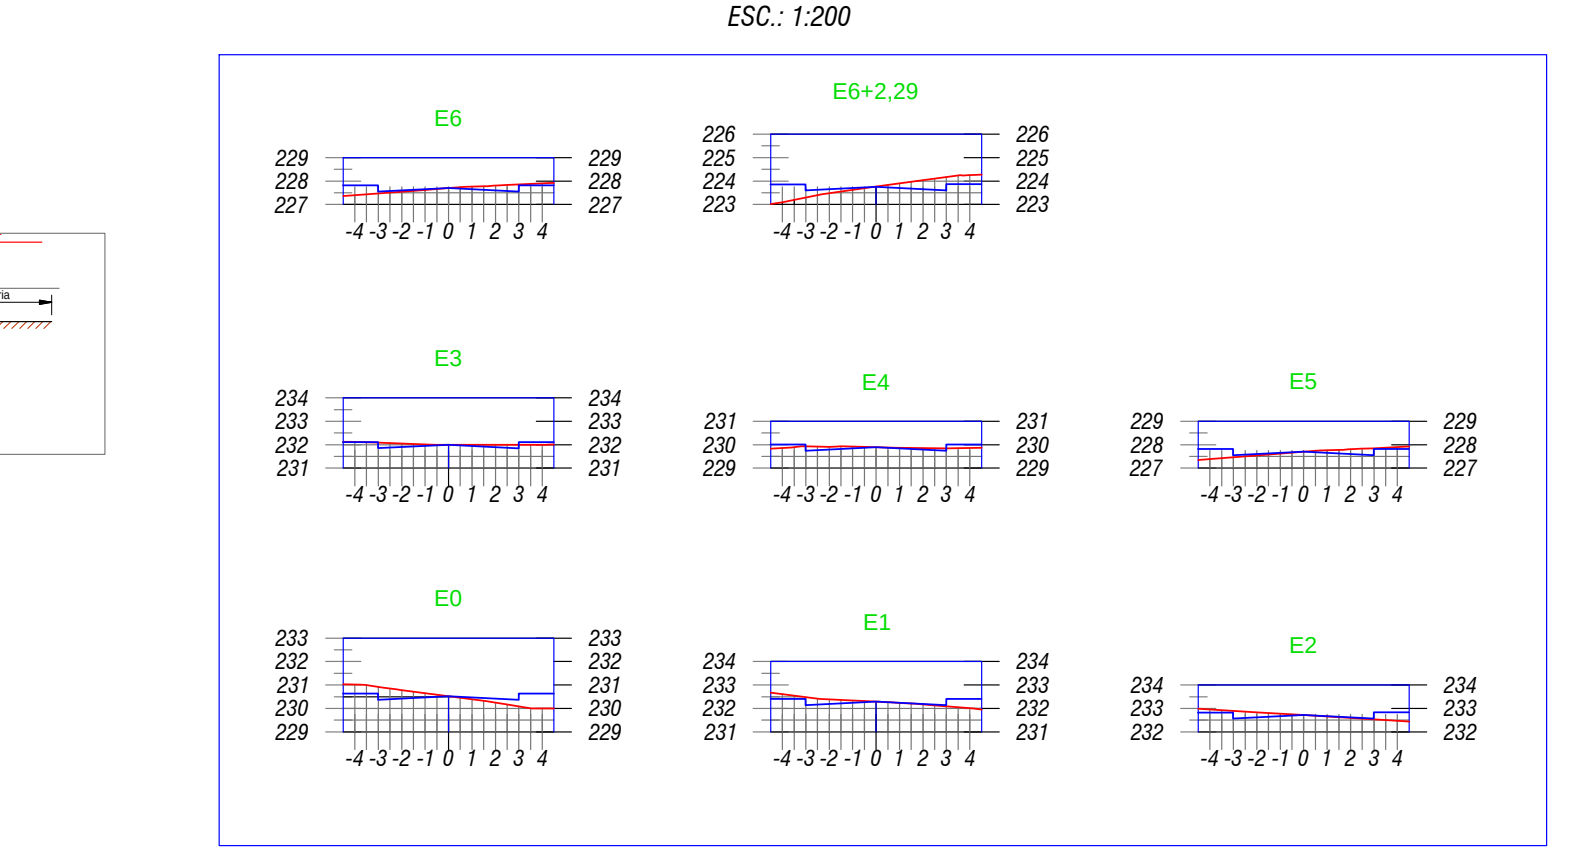
RUA ROBERTO WILSOM MOURA - SEÇÕES
ESC.: 1:200
E6
E6+2,29
E3
E4
E5
E0
E1
E2
-4 -3 -2 -1 0 1 2 3 4

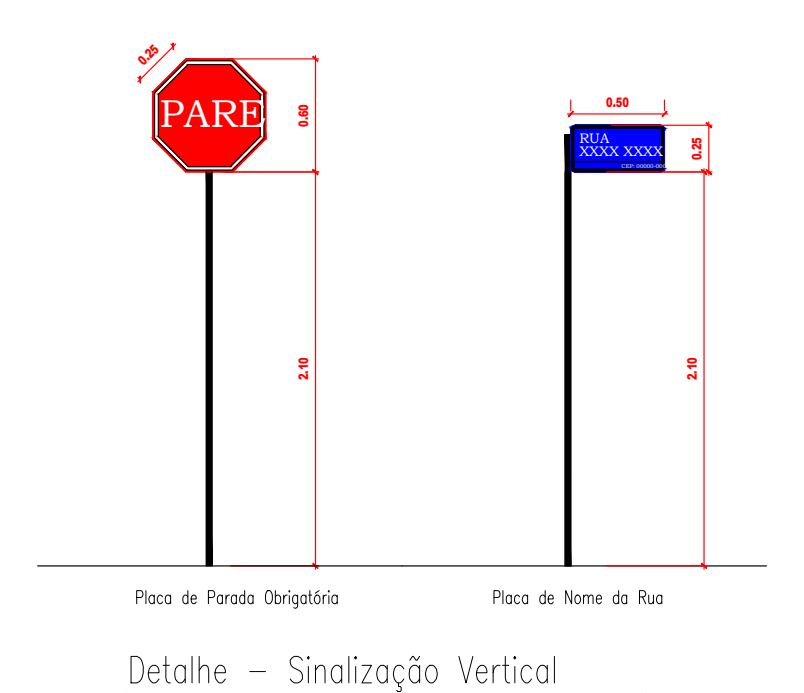
PARE
RUA XXXX XXXX
2.10
Placa de Parada Obrigatória
Placa de Nome da Rua

Detalhe – Sinalização Vertical
1:25

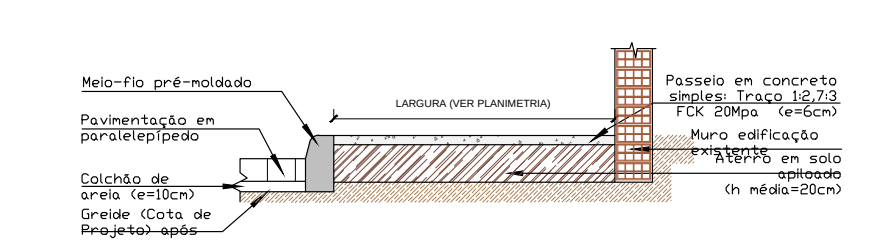
Meio-fio pré-moldado
Pavimentação em paralelepípedo
Colchão de areia (e=10cm)
Greide (Cota de Projeto) após terraplenagem
LARGURA (VER PLANIMETRIA)
Passeio em concreto simples: Traço 1:2,7:3 FCK 20Mpa (e=6cm)
Muro edificação existente
Aterro em solo apiloado (h média=20cm)

Detalhe 01 – Passeio Para Trechos s/ Alvenaria de 1 Vez

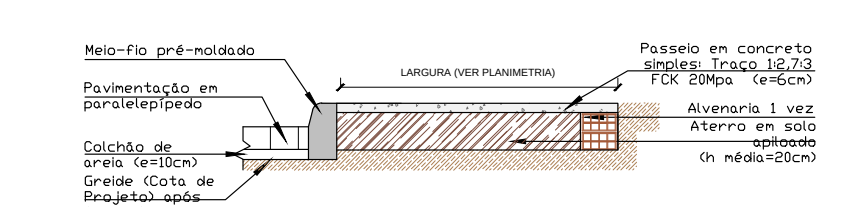
Meio-fio pré-moldado
Pavimentação em paralelepípedo
Colchão de areia (e=10cm)
Greide (Cota de Projeto) após terraplenagem
LARGURA (VER PLANIMETRIA)
Passeio em concreto simples: Traço 1:2,7:3 FCK 20Mpa (e=6cm)
Alvenaria 1 vez
Aterro em solo apiloado (h média=20cm)

Detalhe 02 – Passeio Para Trechos c/ Alvenaria de 1 Vez

Seção-Tipo de Pavimentação

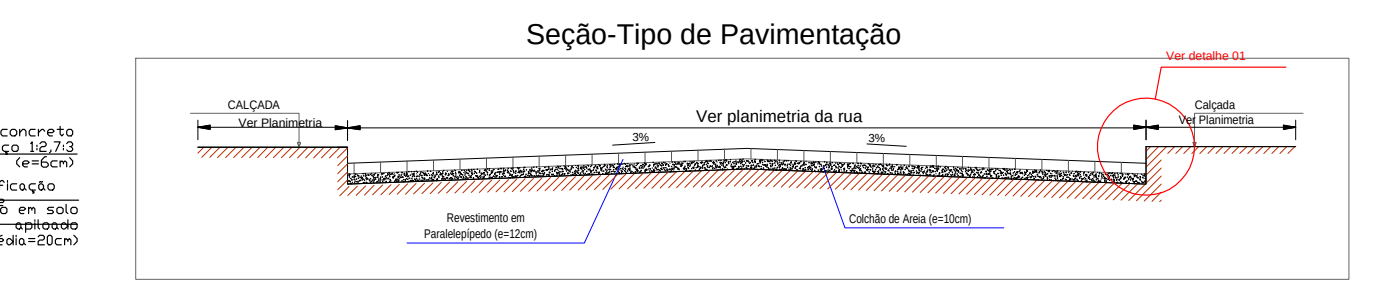
CALÇADA
Ver Planimetria
Ver planimetria da rua
2%
2%
Ver detalhe 01
Calçada
Ver Planimetria
Revestimento em Paralelepípedo (e=12cm)
Colchão de Areia (e=10cm)

Sem Escala

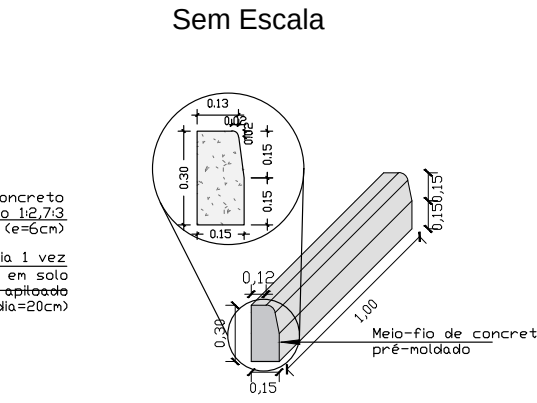
0,12
1,00
Meio-fio de concreto pré-moldado

Detalhe – Meio-fio

Nota: Para o cálculo do quantitativo de concreto do passeio público, considera-se a dimensão da largura conforme indicado nos detalhe dos passeios.

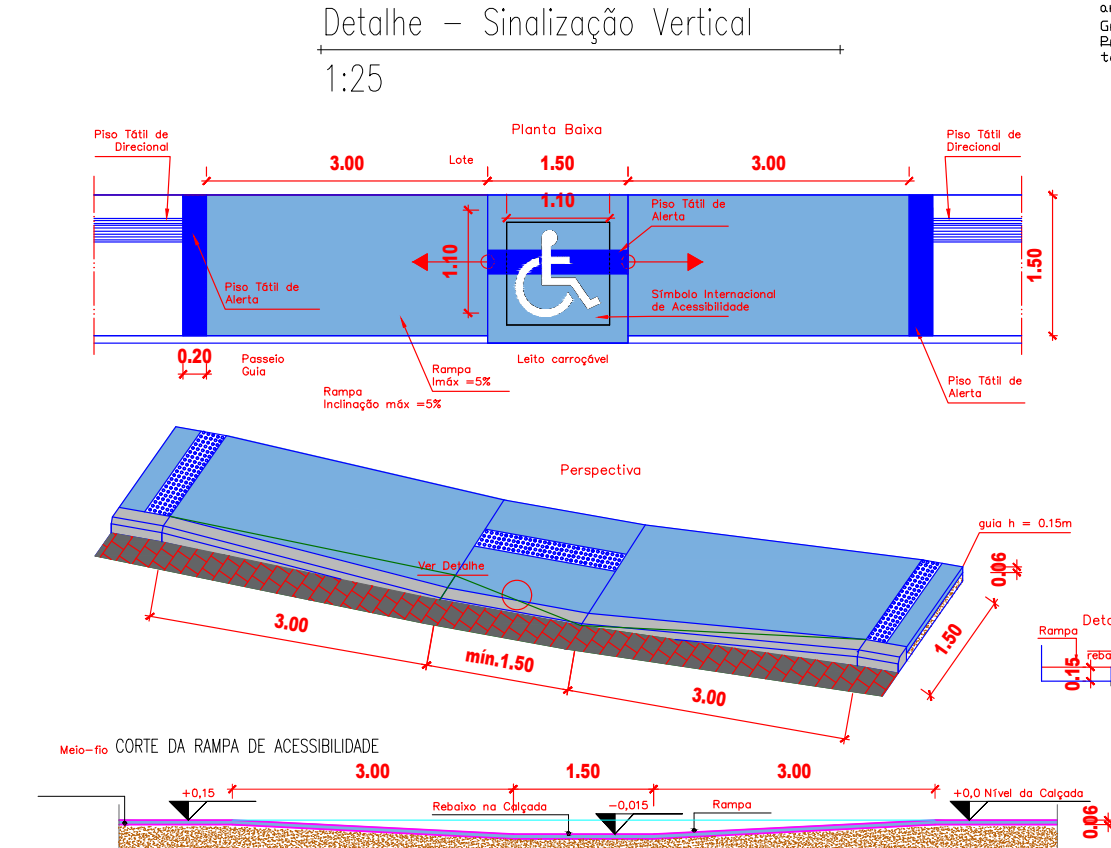
Planta Baixa
3.00
Lote
1.50
3.00
1.10
Perspectiva
3.00
min.1,50
3.00
CORTE DA RAMPA DE ACESSIBILIDADE
Meio-fio
3.00
1.50
3.00
Terreno Natural

Detalhe – Rampa de Acessibilidade
1:50

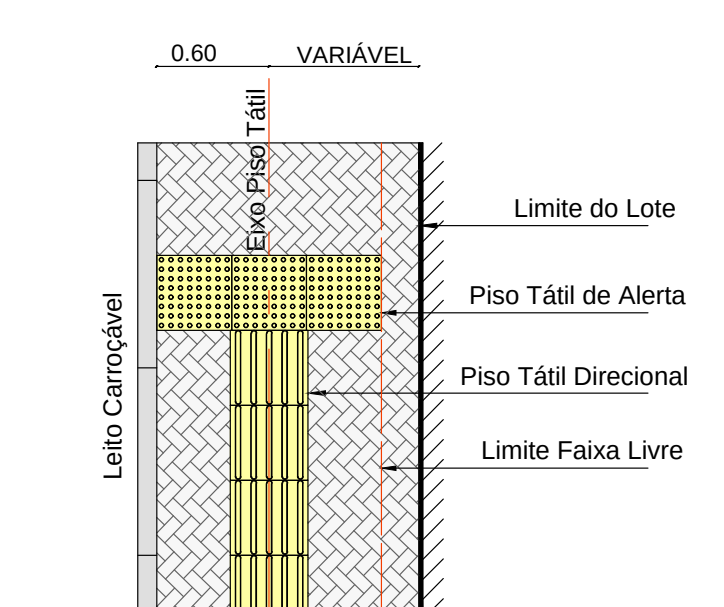
0.60
VARIÁVEL
Eixo Piso Tátil
Limite do Lote
Piso Tátil de Alerta
Piso Tátil Direcional
Limite Faixa Livre
Leito Carroçável

Detalhe 01 – Início/Fim Piso Tátil (D01-IFPT)

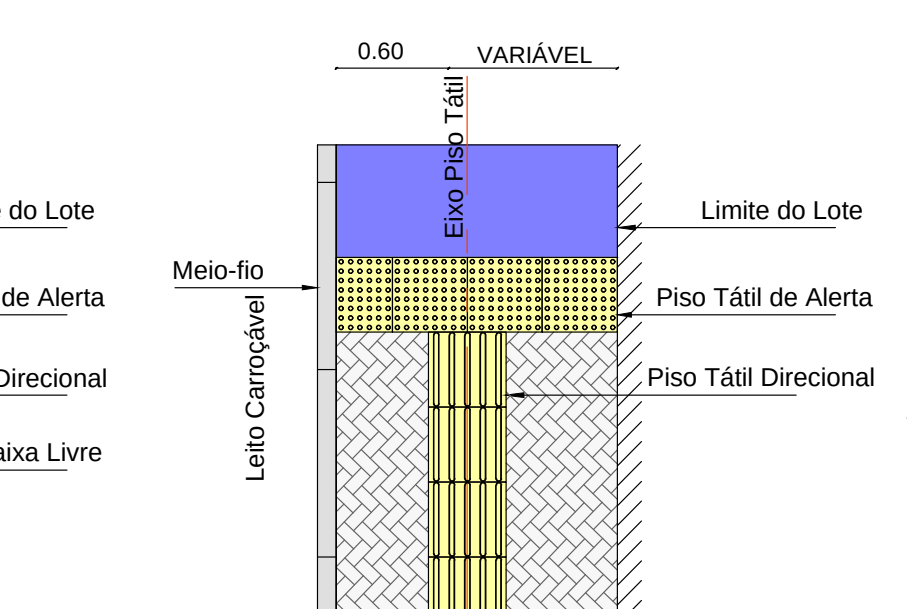
0.60
VARIÁVEL
Eixo Piso Tátil
Meio-fio
Limite do Lote
Piso Tátil de Alerta
Piso Tátil Direcional
Leito Carroçável

Detalhe 02 – Encontro Piso Tátil com Rampa (D02-EPTR)

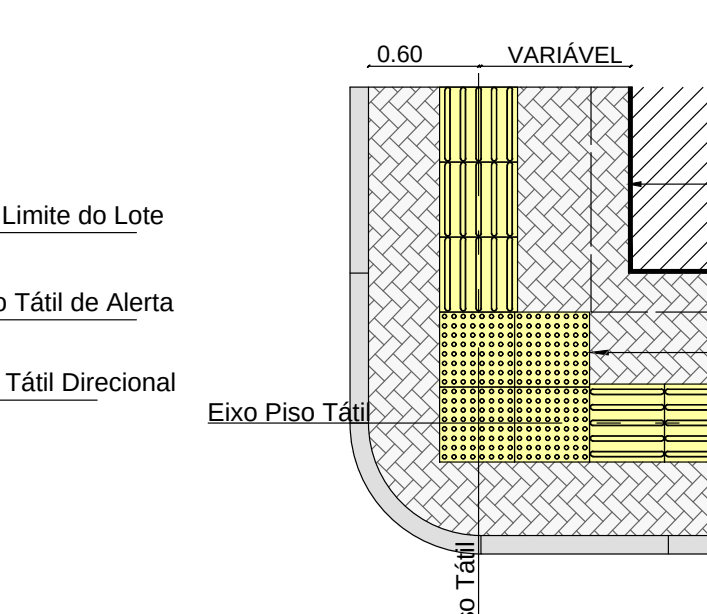
0.60
VARIÁVEL
Limite do Lote
Limite Faixa Livre
Piso Tátil de Alerta
Piso Tátil Direcional
Eixo Piso Tátil
Meio-fio
Eixo Piso Tátil

Detalhe 03 – Mudança de direção – Entre 90° e 150° (D03-MD)

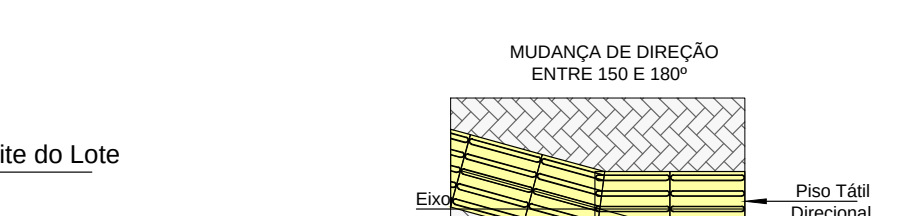
MUDANÇA DE DIREÇÃO ENTRE 150 E 180°
Eixo
Piso Tátil Direcional
Eixo

Detalhe 04 – Mudança de direção entre 150° e 180° (D04-MD)

Detalhe 05 – Piso Tátil de Alerta

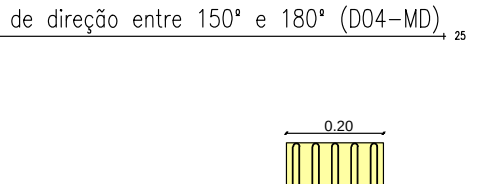

Detalhe 06 – Piso Tátil Direcional

PROPRIETÁRIO Prefeitura Municipal de Coremas- PB

Kleber Sá de Oliveira
Engenheiro Civil
CREA 1602682780

PROJETISTA Kleber Sá de Oliveira

EPE
EMPRESA PARAIBA DE ENGENHARIA

PROJETO: PAVIMENTAÇÃO DE RUAS E VIAS
LOCAL: MUNICÍPIO DE COREMAS - PB
PROPRIETÁRIO: PREFEITURA MUNICIPAL DE COREMAS - PB
FOLHA 05/07
ESCALA: Indicadas
DESENHOS: Indicados
RESPONSÁVEL TÉCNICO: Kleber Sá de Oliveira Crea: 160391676-8
ANOTAÇÕES:
ARQUIVO: PAV_COREMAS_FINAL_2022.dwg
DESENHO: Diego Medeiros
DATA: SET - 2022

CÍCERO EUFRASIO DA SILVA

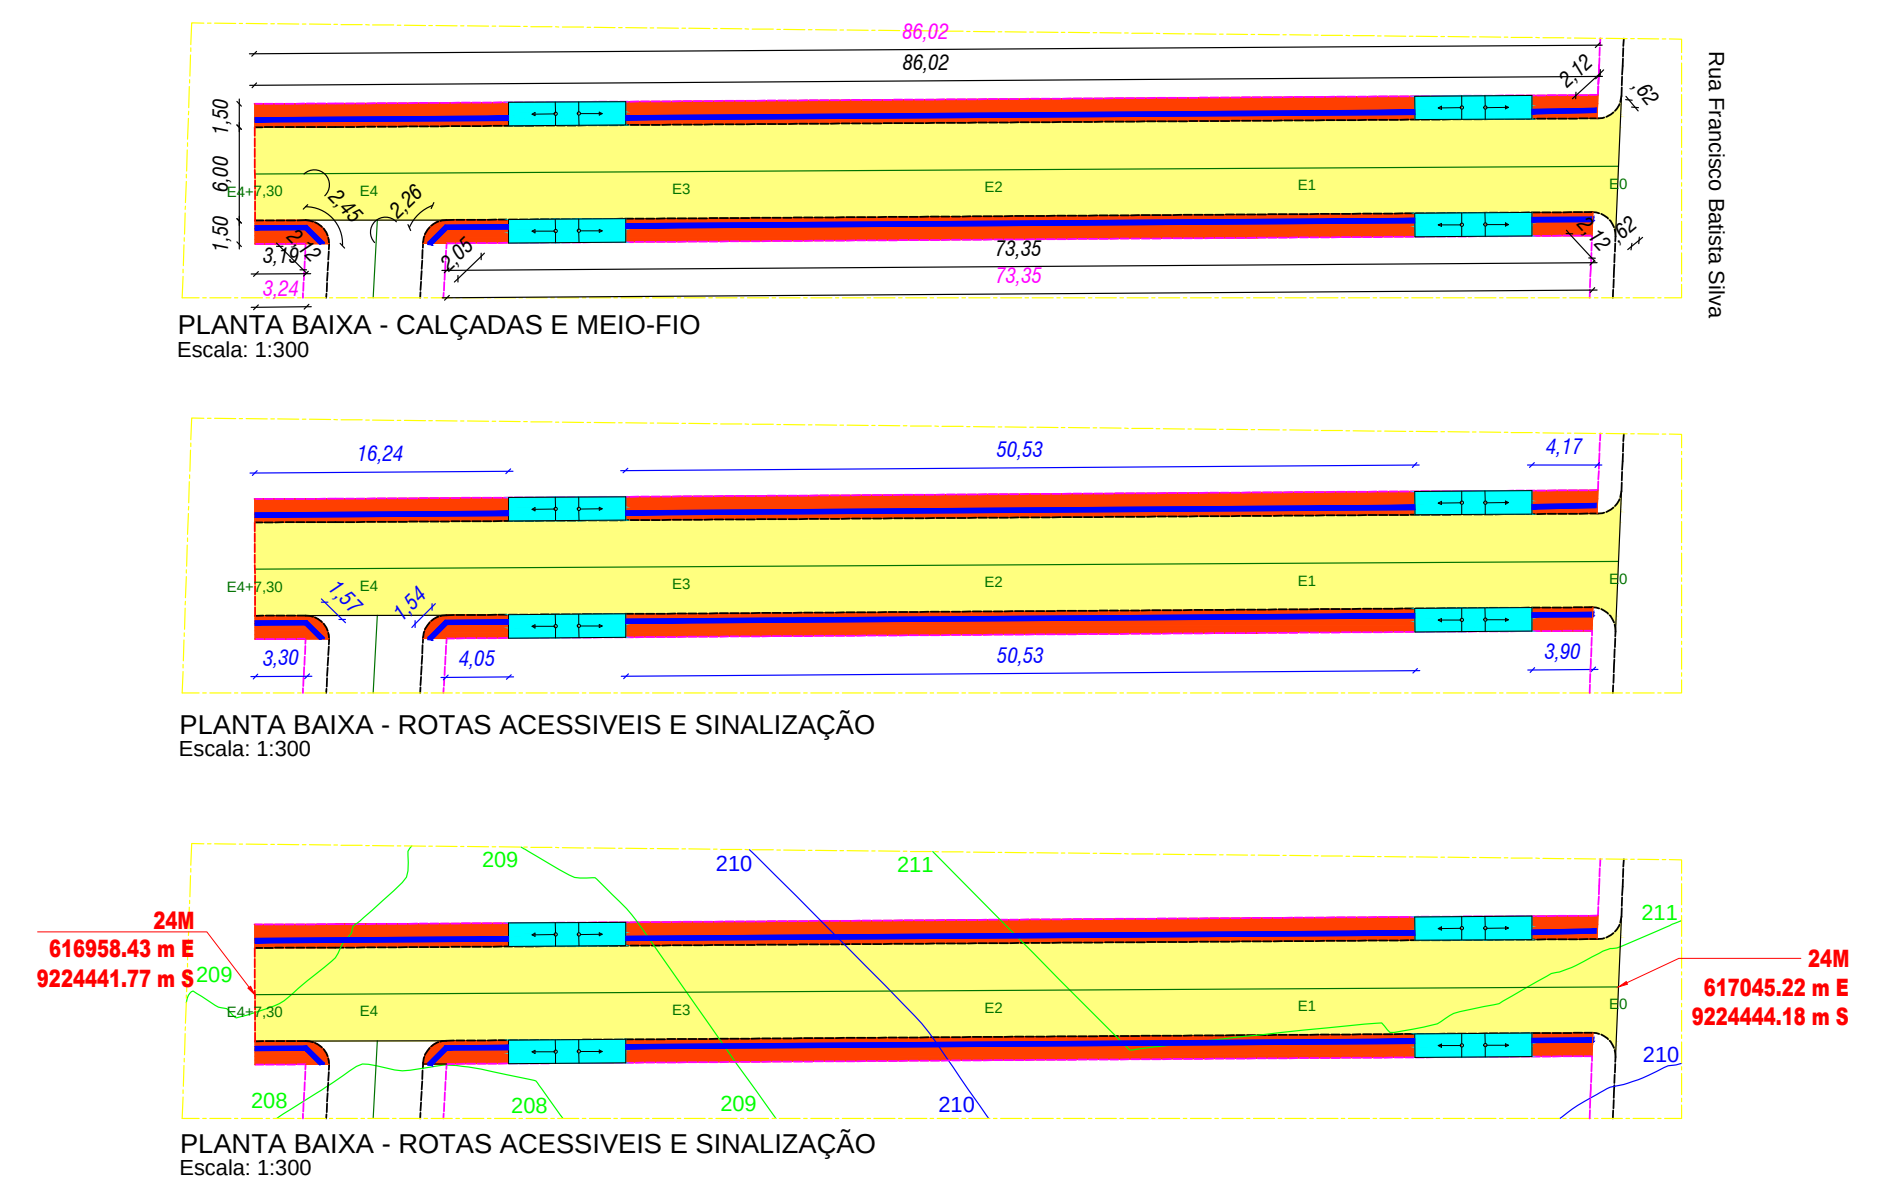
Rua Francisco Batista Silva
24M
616958.43 m E
9224441.77 m S
24M
617045.22 m E
9224444.18 m S
PLANTA BAIXA - CALÇADAS E MEIO-FIO
Escala: 1:300
PLANTA BAIXA - ROTAS ACESSIVEIS E SINALIZAÇÃO
Escala: 1:300
PLANTA BAIXA - ROTAS ACESSIVEIS E SINALIZAÇÃO
Escala: 1:300

RUA FIRMINO DA SILVA LACERDA

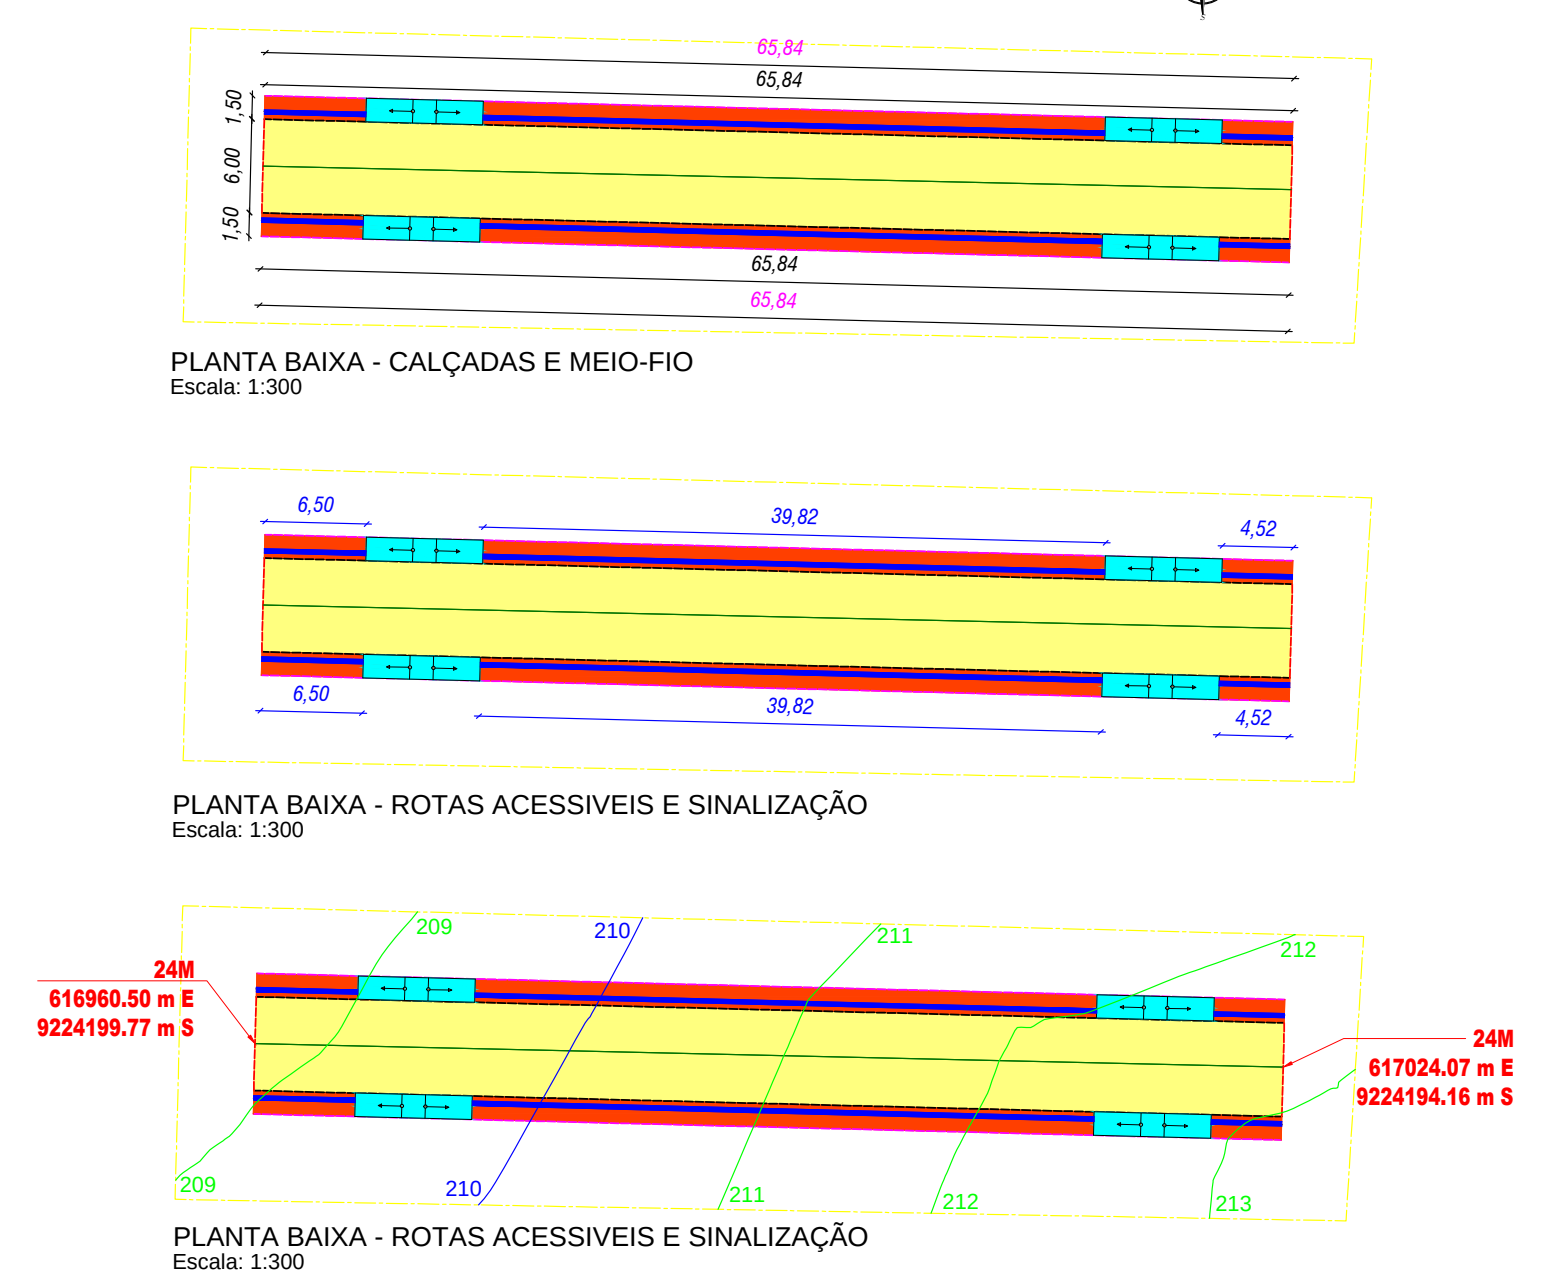
24M
616960.50 m E
9224199.77 m S
24M
617024.07 m E
9224194.16 m S
PLANTA BAIXA - CALÇADAS E MEIO-FIO
Escala: 1:300
PLANTA BAIXA - ROTAS ACESSIVEIS E SINALIZAÇÃO
Escala: 1:300
PLANTA BAIXA - ROTAS ACESSIVEIS E SINALIZAÇÃO
Escala: 1:300

Legenda

Pavimentação

🟨	Pavimentação à Construir
▒	Pavimento Existente
—	Meio-fio Existente
– – –	Meio-fio Projetado
– – –	Cordão em Granito
– – –	Alvenaria de 1 vez
—	Cerca
➡	Sentido do Caimento da água

Passeio

🟥	Calçadas à Construir
🟩	Calçadas Existentes
🟦	Piso Tátil
▭	Rampa de Acesso
●	Poste Existente
●	Poço de Visita (PV)
●	Árvore
—	Edificação Existente
—	Lote Projetado

Sinalização

PARE	Placa de Parada Obrigatória
🟦	Placa com Nome da rua

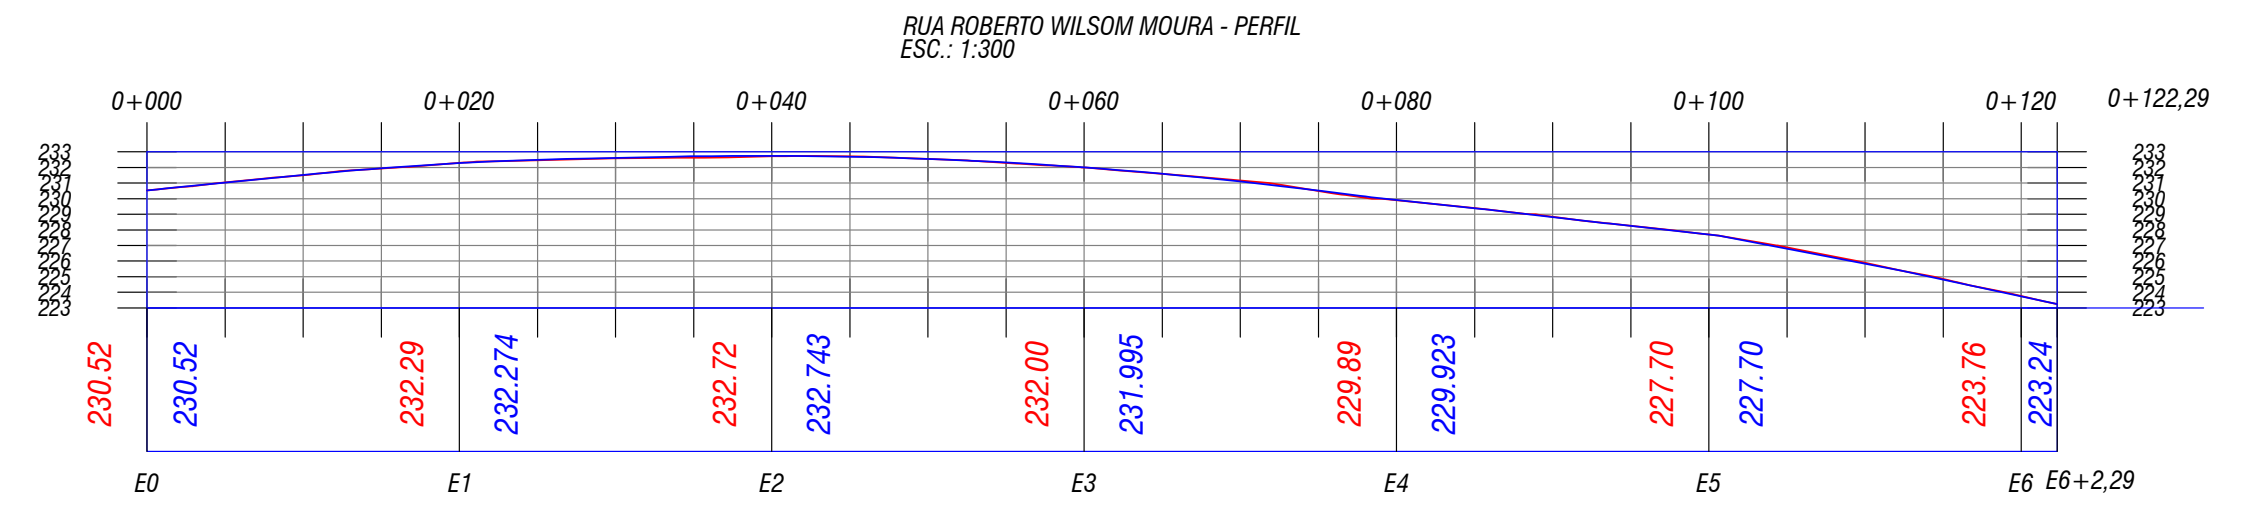

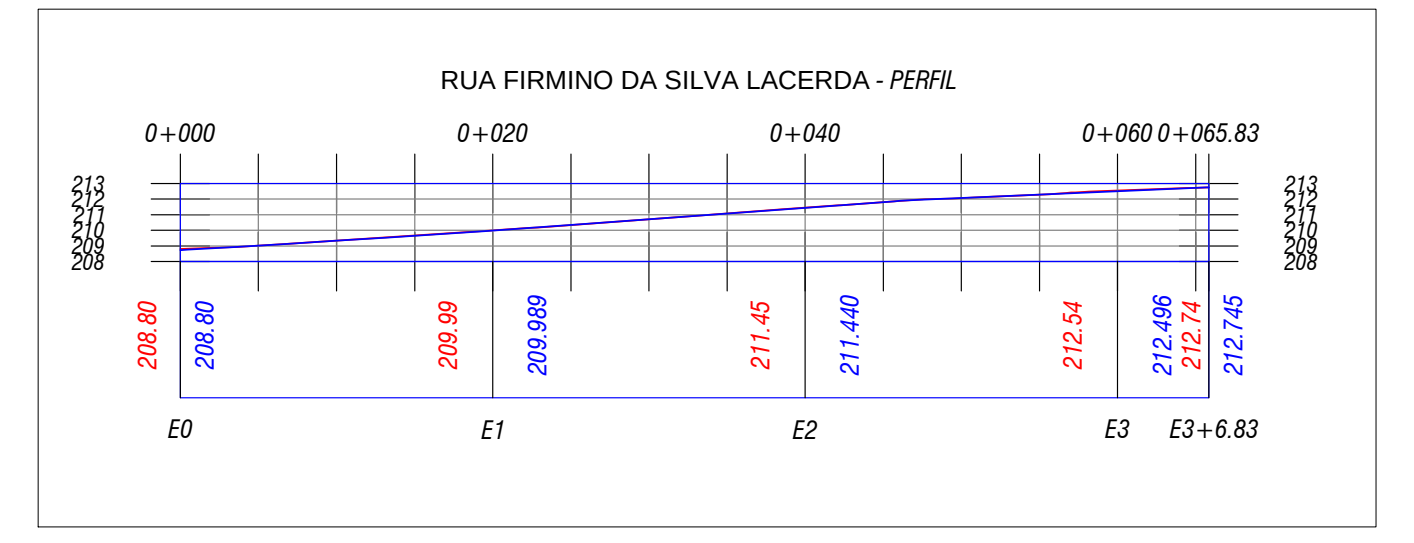

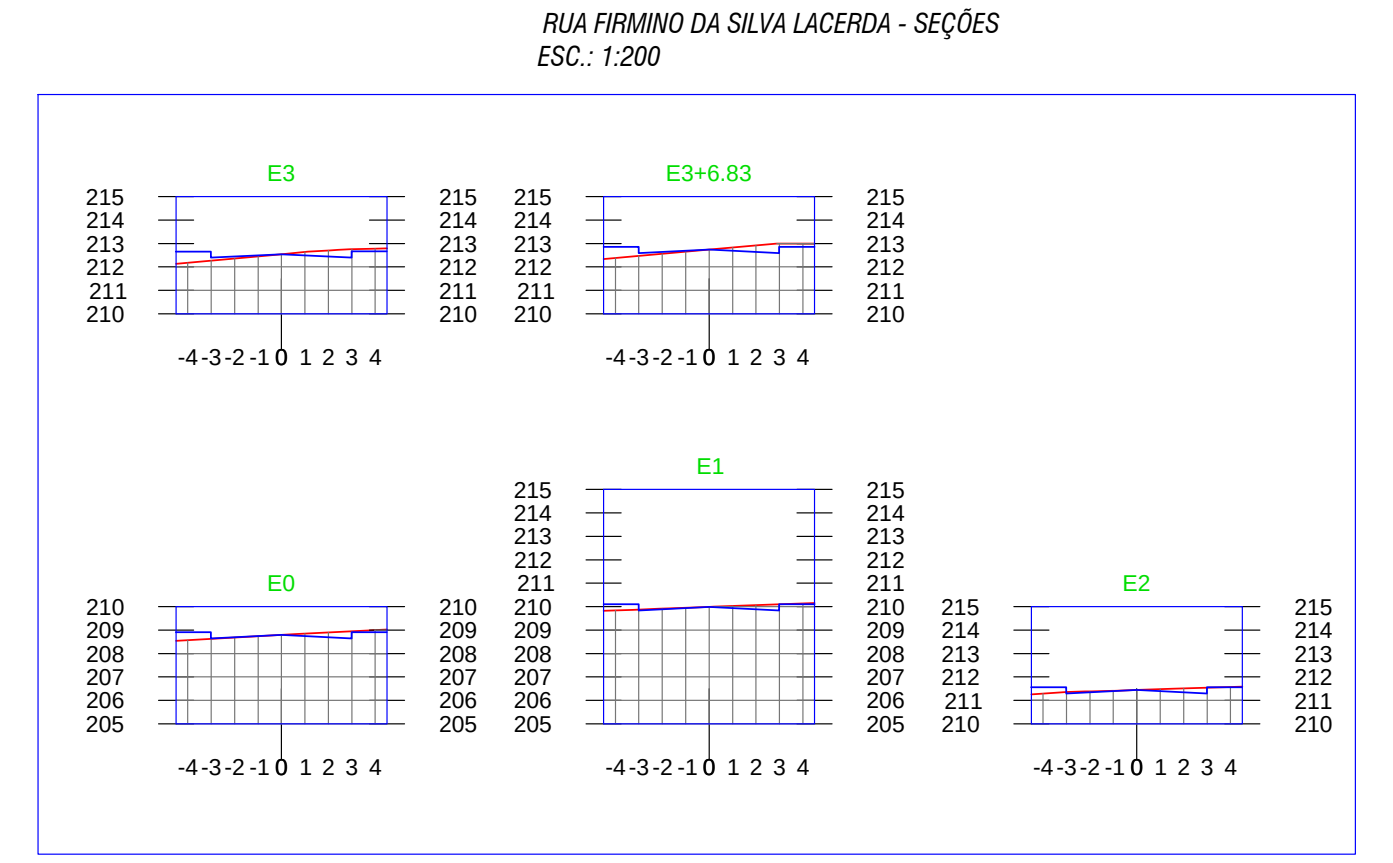
RUA FIRMINO DA SILVA LACERDA - SEÇÕES
ESC.: 1:200
E3
E3+6.83
E0
E1
E2
-4 -3 -2 -1 0 1 2 3 4

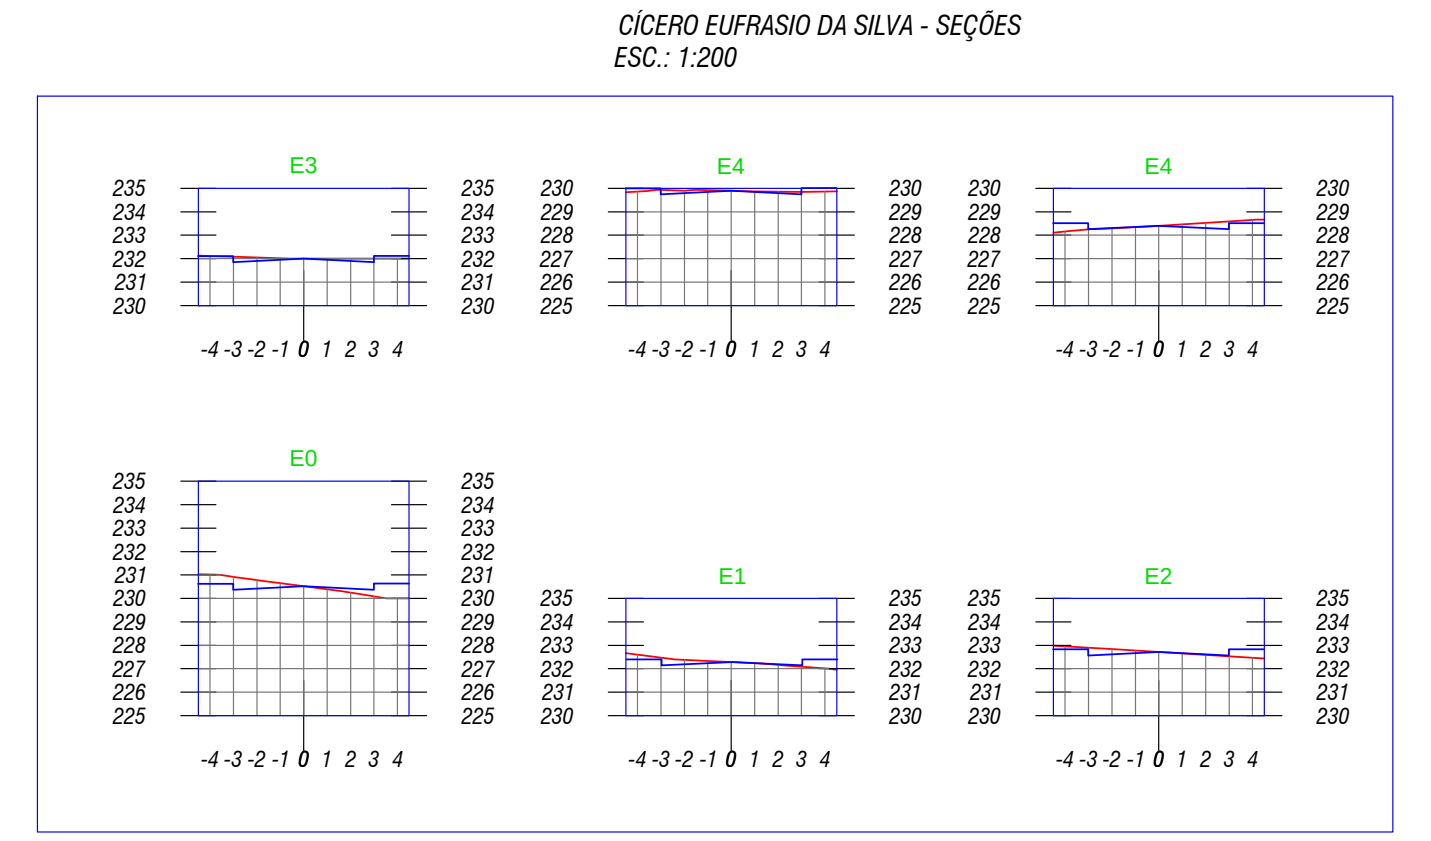
CÍCERO EUFRASIO DA SILVA - SEÇÕES
ESC.: 1:200
E3
E4
E4
E0
E1
E2
-4 -3 -2 -1 0 1 2 3 4

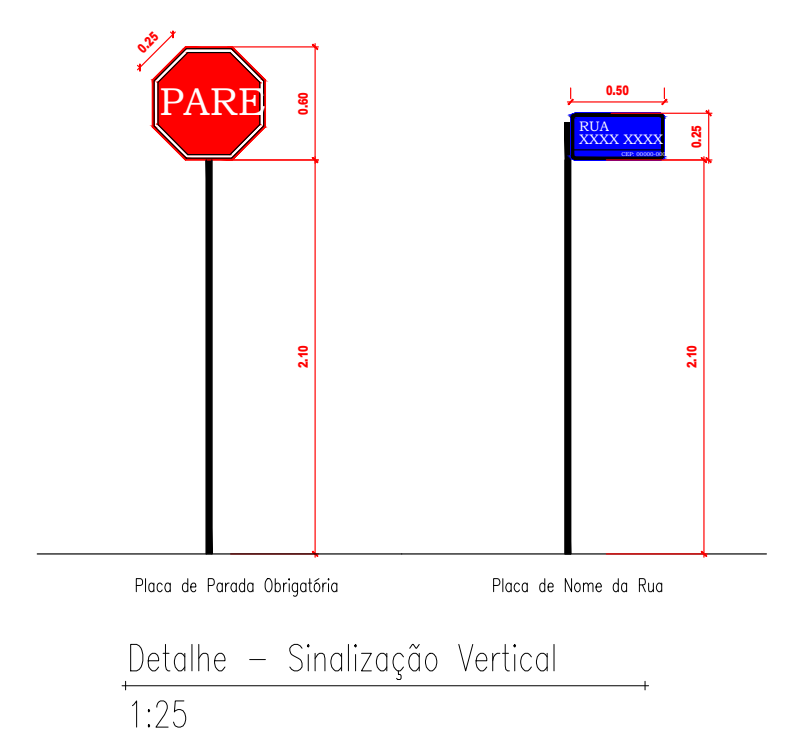
PARE
RUA XXXX XXXX
2.10
Placa de Parada Obrigatória
Placa de Nome da Rua

Detalhe – Sinalização Vertical
1:25

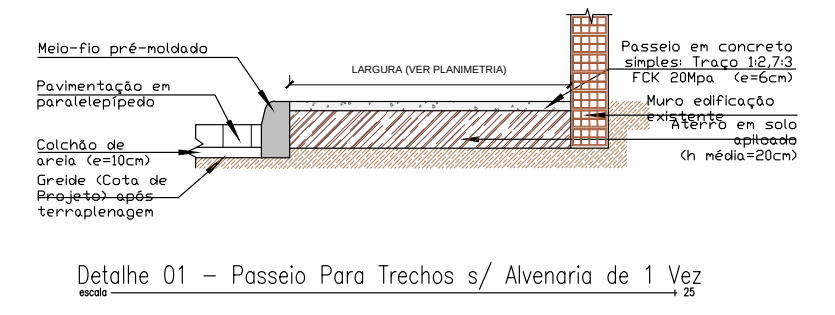
Meio-fio pré-moldado
Pavimentação em paralelepípedo
Colchão de areia (e=10cm)
Greide (Cota de Projeto) após terraplenagem
LARGURA (VER PLANIMETRIA)
Passeio em concreto simples: Traço 1:2,7:3 FCK 20Mpa (e=6cm)
Muro edificação existente
Aterro em solo apiloado (h média=20cm)

Detalhe 01 – Passeio Para Trechos s/ Alvenaria de 1 Vez

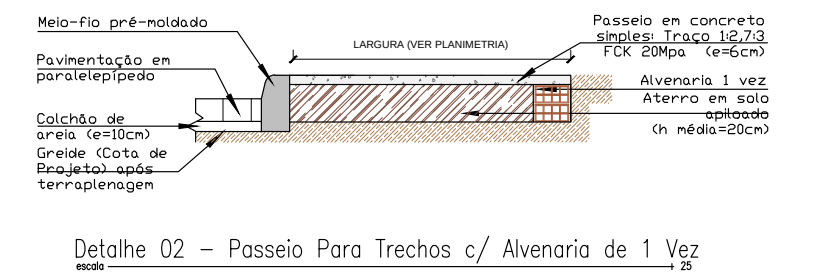
Meio-fio pré-moldado
Pavimentação em paralelepípedo
Colchão de areia (e=10cm)
Greide (Cota de Projeto) após terraplenagem
LARGURA (VER PLANIMETRIA)
Passeio em concreto simples: Traço 1:2,7:3 FCK 20Mpa (e=6cm)
Alvenaria 1 vez
Aterro em solo apiloado (h média=20cm)

Detalhe 02 – Passeio Para Trechos c/ Alvenaria de 1 Vez

Seção-Tipo de Pavimentação

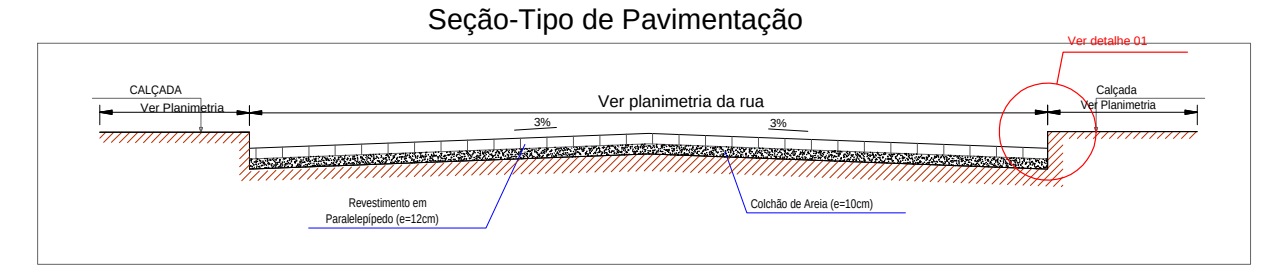
CALÇADA
Ver Planimetria
Ver planimetria da rua
2%
2%
Ver detalhe 01
Calçada
Ver Planimetria
Revestimento em Paralelepípedo (e=12cm)
Colchão de Areia (e=10cm)

Sem Escala

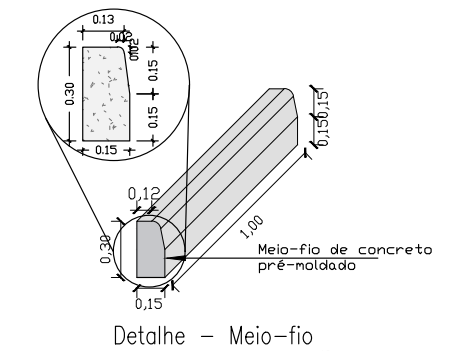
0,12
1,00
Meio-fio de concreto pré-moldado

Detalhe – Meio-fio

Nota: Para o cálculo do quantitativo de concreto do passeio público, considera-se a dimensão da largura conforme indicado nos detalhe dos passeios.

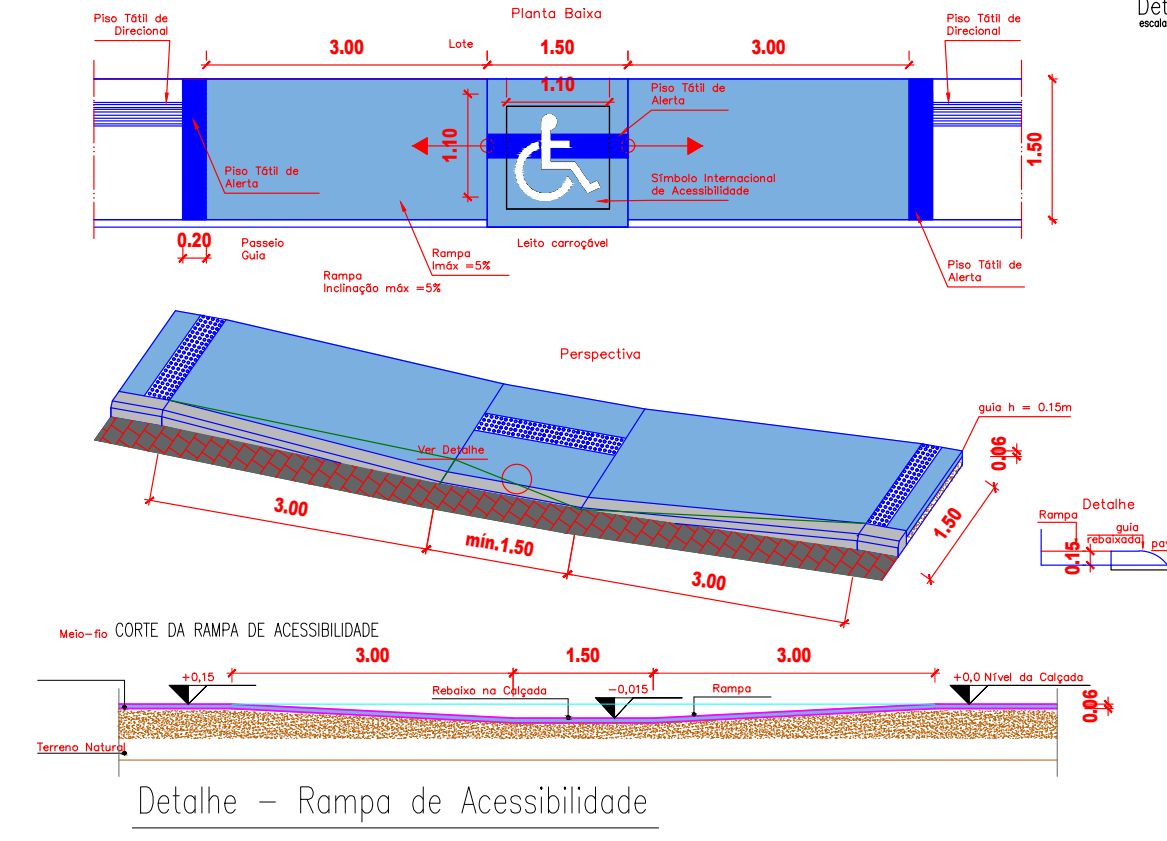
Planta Baixa
3.00
Lote
1.50
3.00
1.10
Perspectiva
3.00
min.1,50
3.00
CORTE DA RAMPA DE ACESSIBILIDADE
Meio-fio
3.00
1.50
3.00
Terreno Natural

Detalhe – Rampa de Acessibilidade
1:50

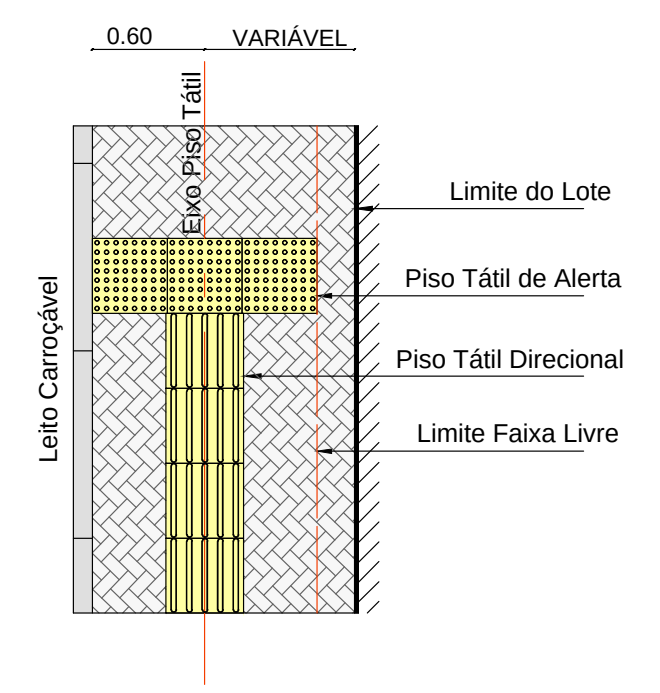
0.60
VARIÁVEL
Eixo Piso Tátil
Limite do Lote
Piso Tátil de Alerta
Piso Tátil Direcional
Limite Faixa Livre
Leito Carroçável

Detalhe 01 – Início/Fim Piso Tátil (D01-IFPT)

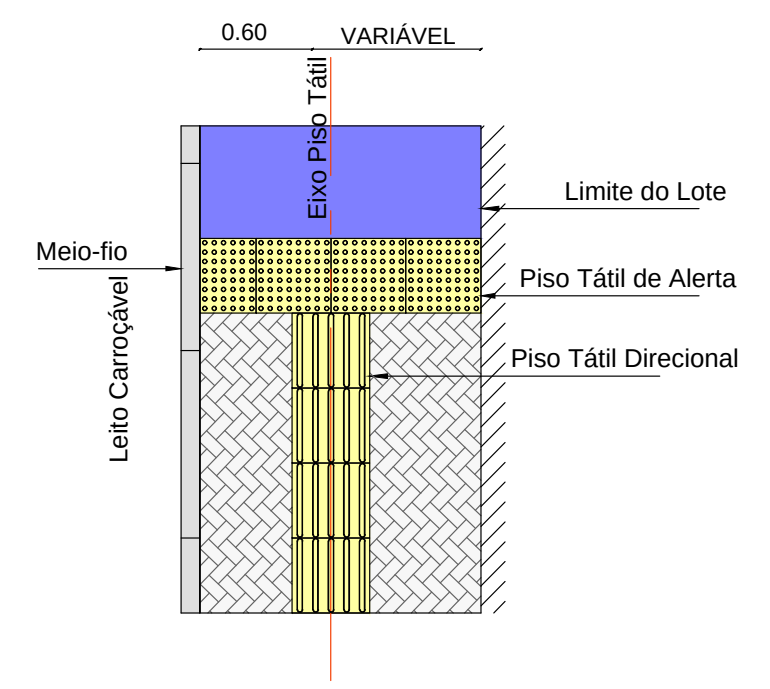
0.60
VARIÁVEL
Eixo Piso Tátil
Meio-fio
Limite do Lote
Piso Tátil de Alerta
Piso Tátil Direcional
Leito Carroçável

Detalhe 02 – Encontro Piso Tátil com Rampa (D02-EPTR)

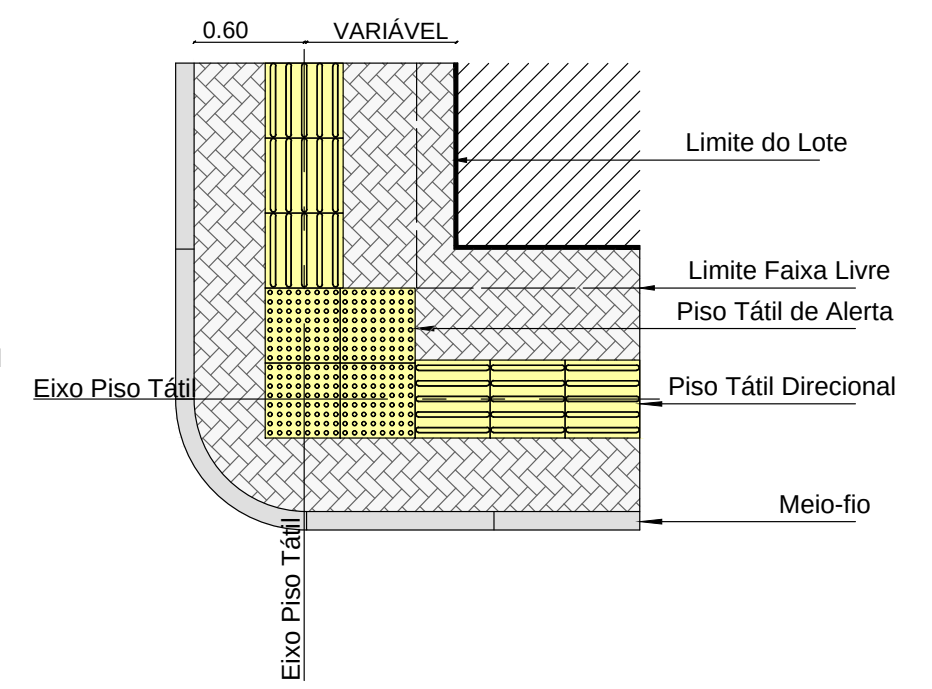
0.60
VARIÁVEL
Limite do Lote
Limite Faixa Livre
Piso Tátil de Alerta
Piso Tátil Direcional
Eixo Piso Tátil
Meio-fio
Eixo Piso Tátil

Detalhe 03 – Mudança de direção – Entre 90° e 150° (D03-MD)

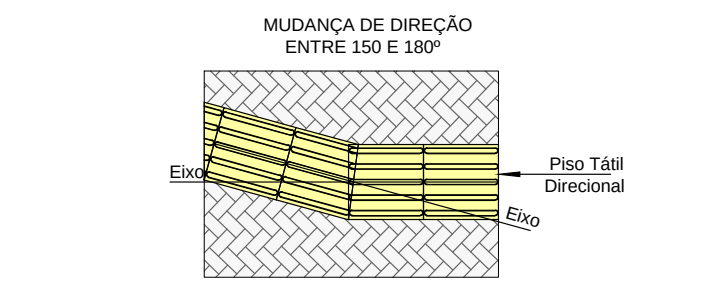
MUDANÇA DE DIREÇÃO ENTRE 150 E 180°
Eixo
Piso Tátil Direcional
Eixo

Detalhe 04 – Mudança de direção entre 150° e 180° (D04-MD)

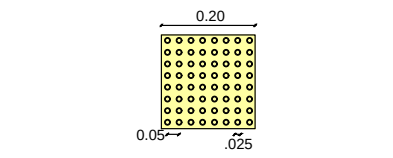

Detalhe 05 – Piso Tátil de Alerta

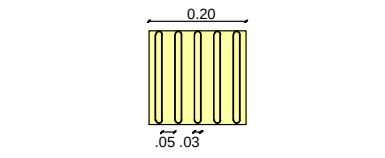

Detalhe 06 – Piso Tátil Direcional

PROPRIETÁRIO Prefeitura Municipal de Coremas- PB

Kleber Sá de Oliveira
Engenheiro Civil
CREA 1602682780

PROJETISTA Kleber Sá de Oliveira

EPE
EMPRESA PARAIBA DE ENGENHARIA

PROJETO: PAVIMENTAÇÃO DE RUAS E VIAS
LOCAL: MUNICÍPIO DE COREMAS - PB
PROPRIETÁRIO: PREFEITURA MUNICIPAL DE COREMAS - PB
FOLHA 06/07
ESCALA: Indicadas
DESENHOS: Indicados
RESPONSÁVEL TÉCNICO: Kleber Sá de Oliveira Crea: 160391676-8
ANOTAÇÕES:
ARQUIVO: PAV_COREMAS_FINAL_2022.dwg
DESENHO: Diego Medeiros
DATA: SET - 2022

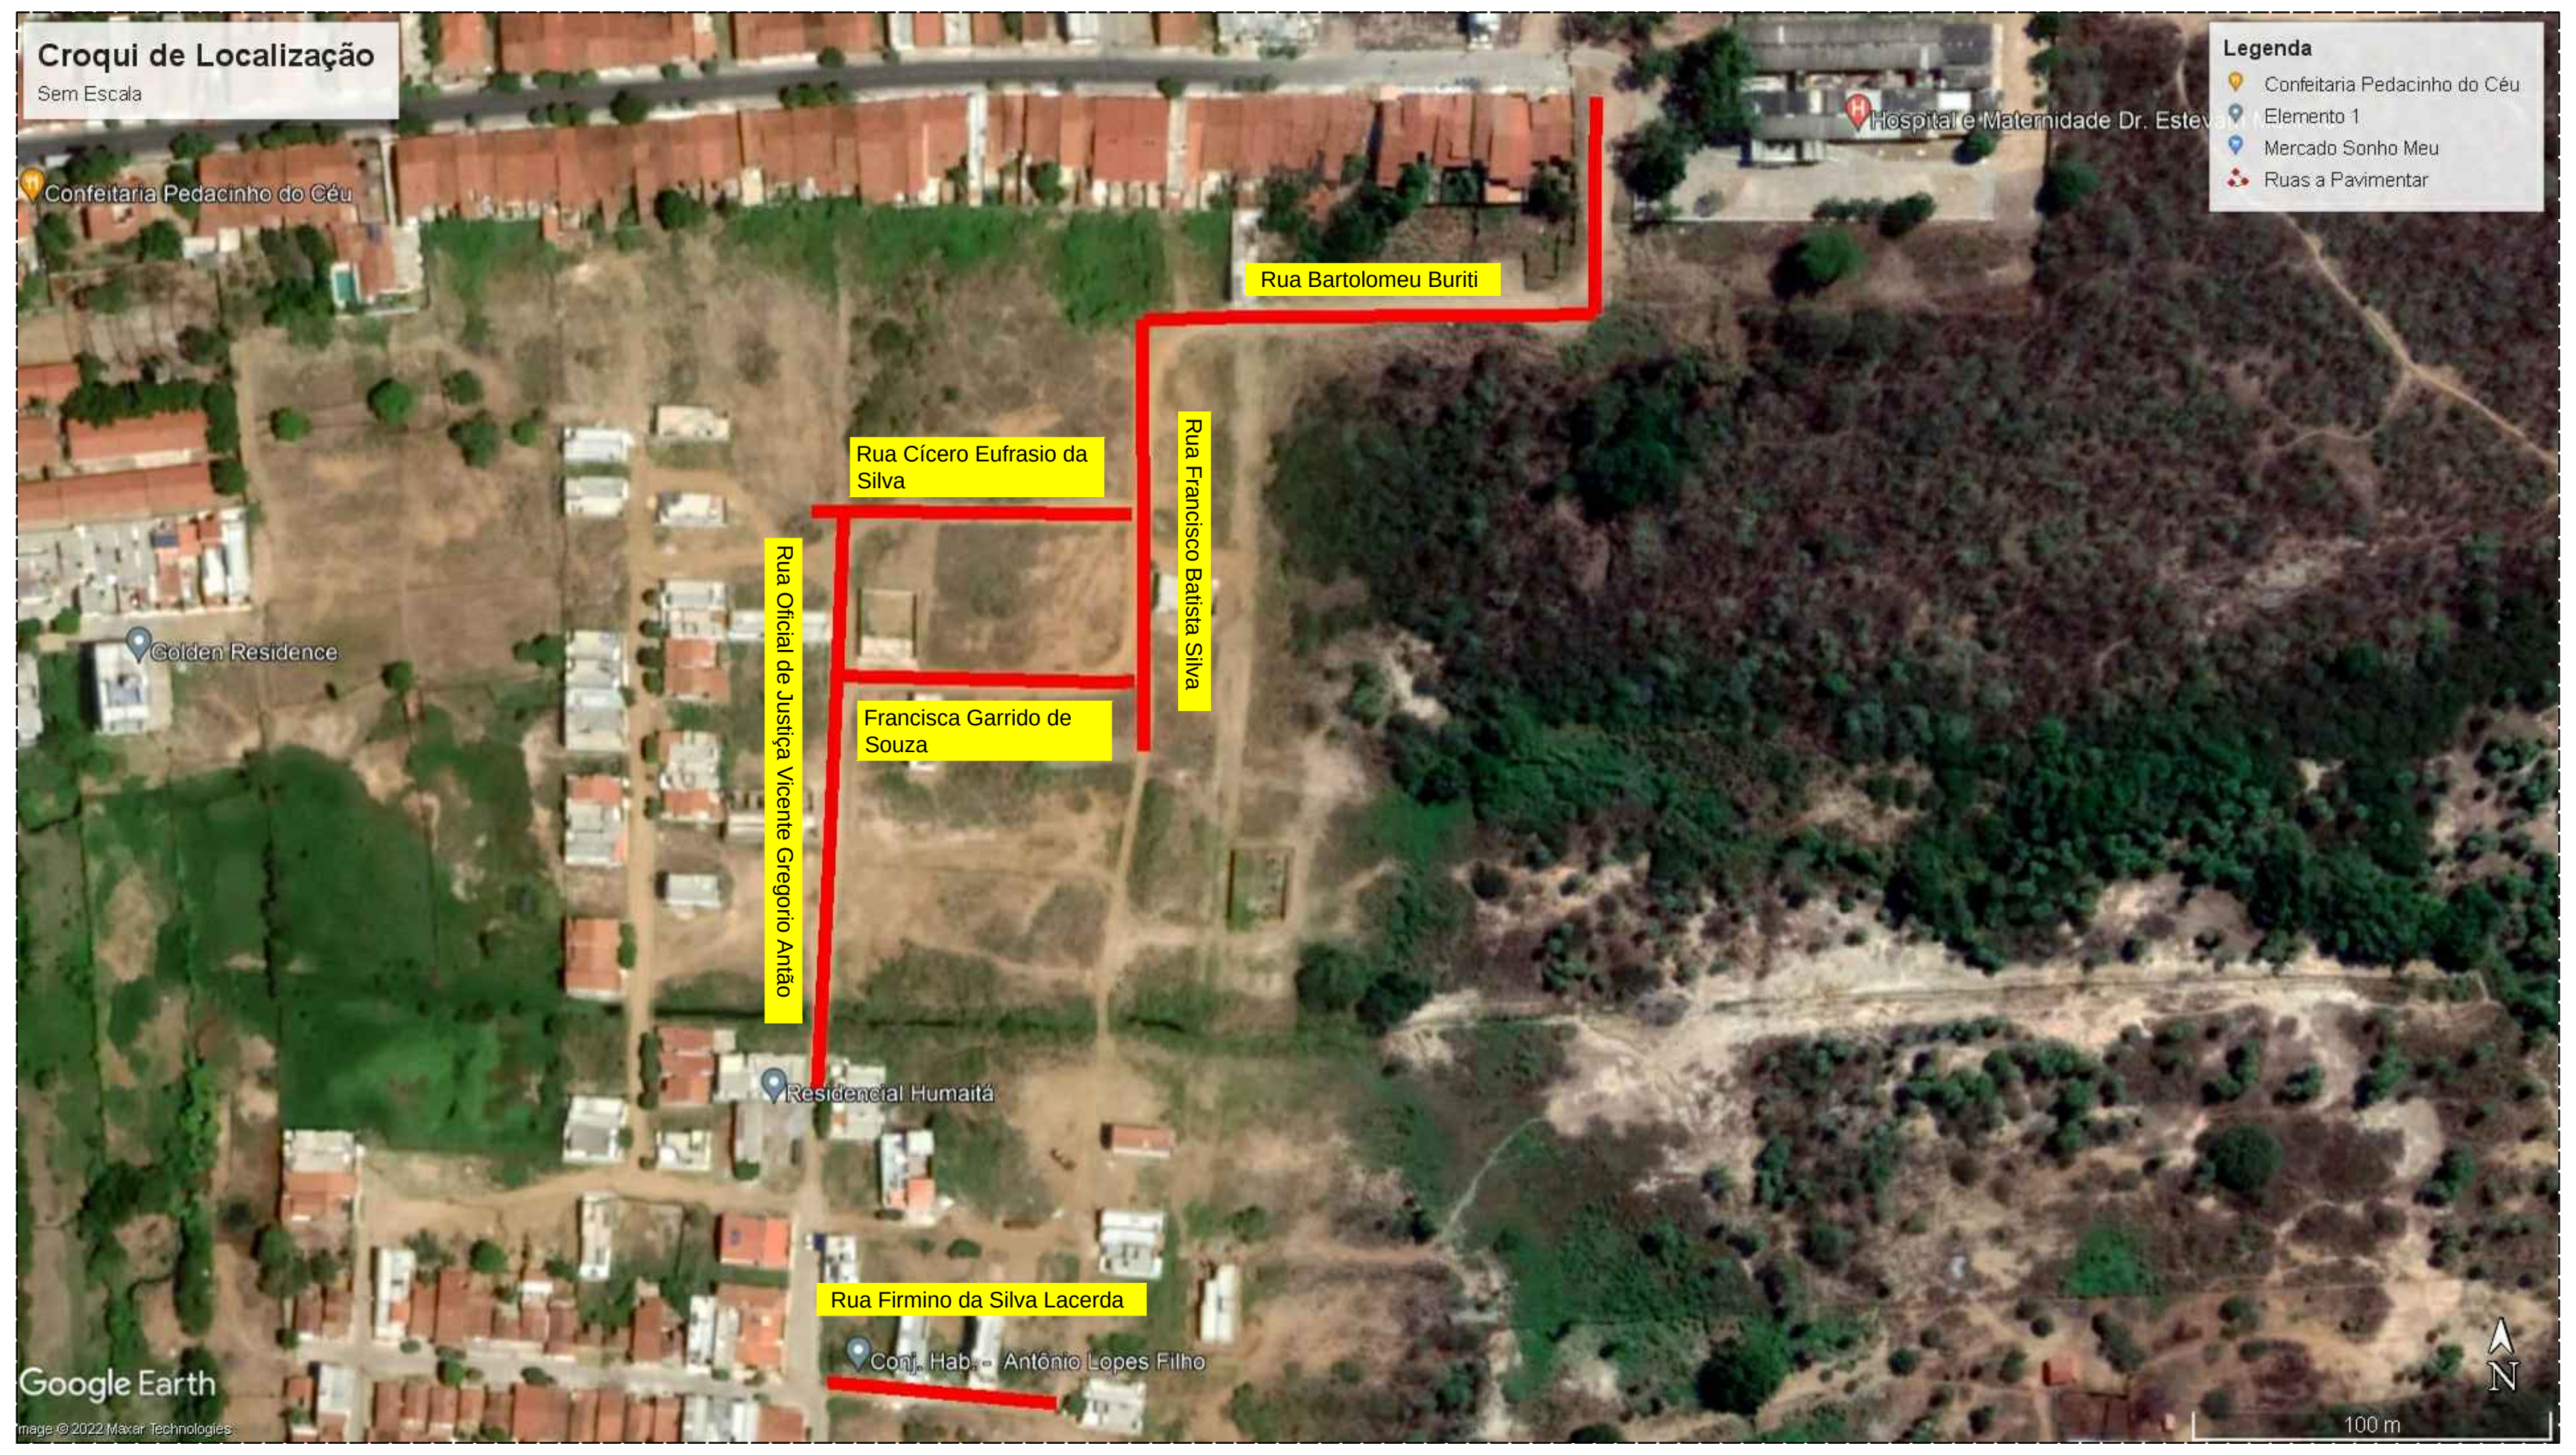
Croqui de Localização
Sem Escala
Legenda
Confeitaria Pedacinho do Céu
Elemento 1
Mercado Sonho Meu
Ruas a Pavimentar
Confeitaria Pedacinho do Céu
Hospital e Maternidade Dr. Estev
Rua Bartolomeu Buriti
Rua Cícero Eufrasio da Silva
Rua Francisco Batista Silva
Golden Residence
Rua Oficial de Justiça Vicente Gregorio Antão
Francisca Garrido de Souza
Residencial Humaitá
Rua Firmino da Silva Lacerda
Conj. Hab. - Antônio Lopes Filho
Google Earth
Image © 2022 Maxar Technologies
100 m
N

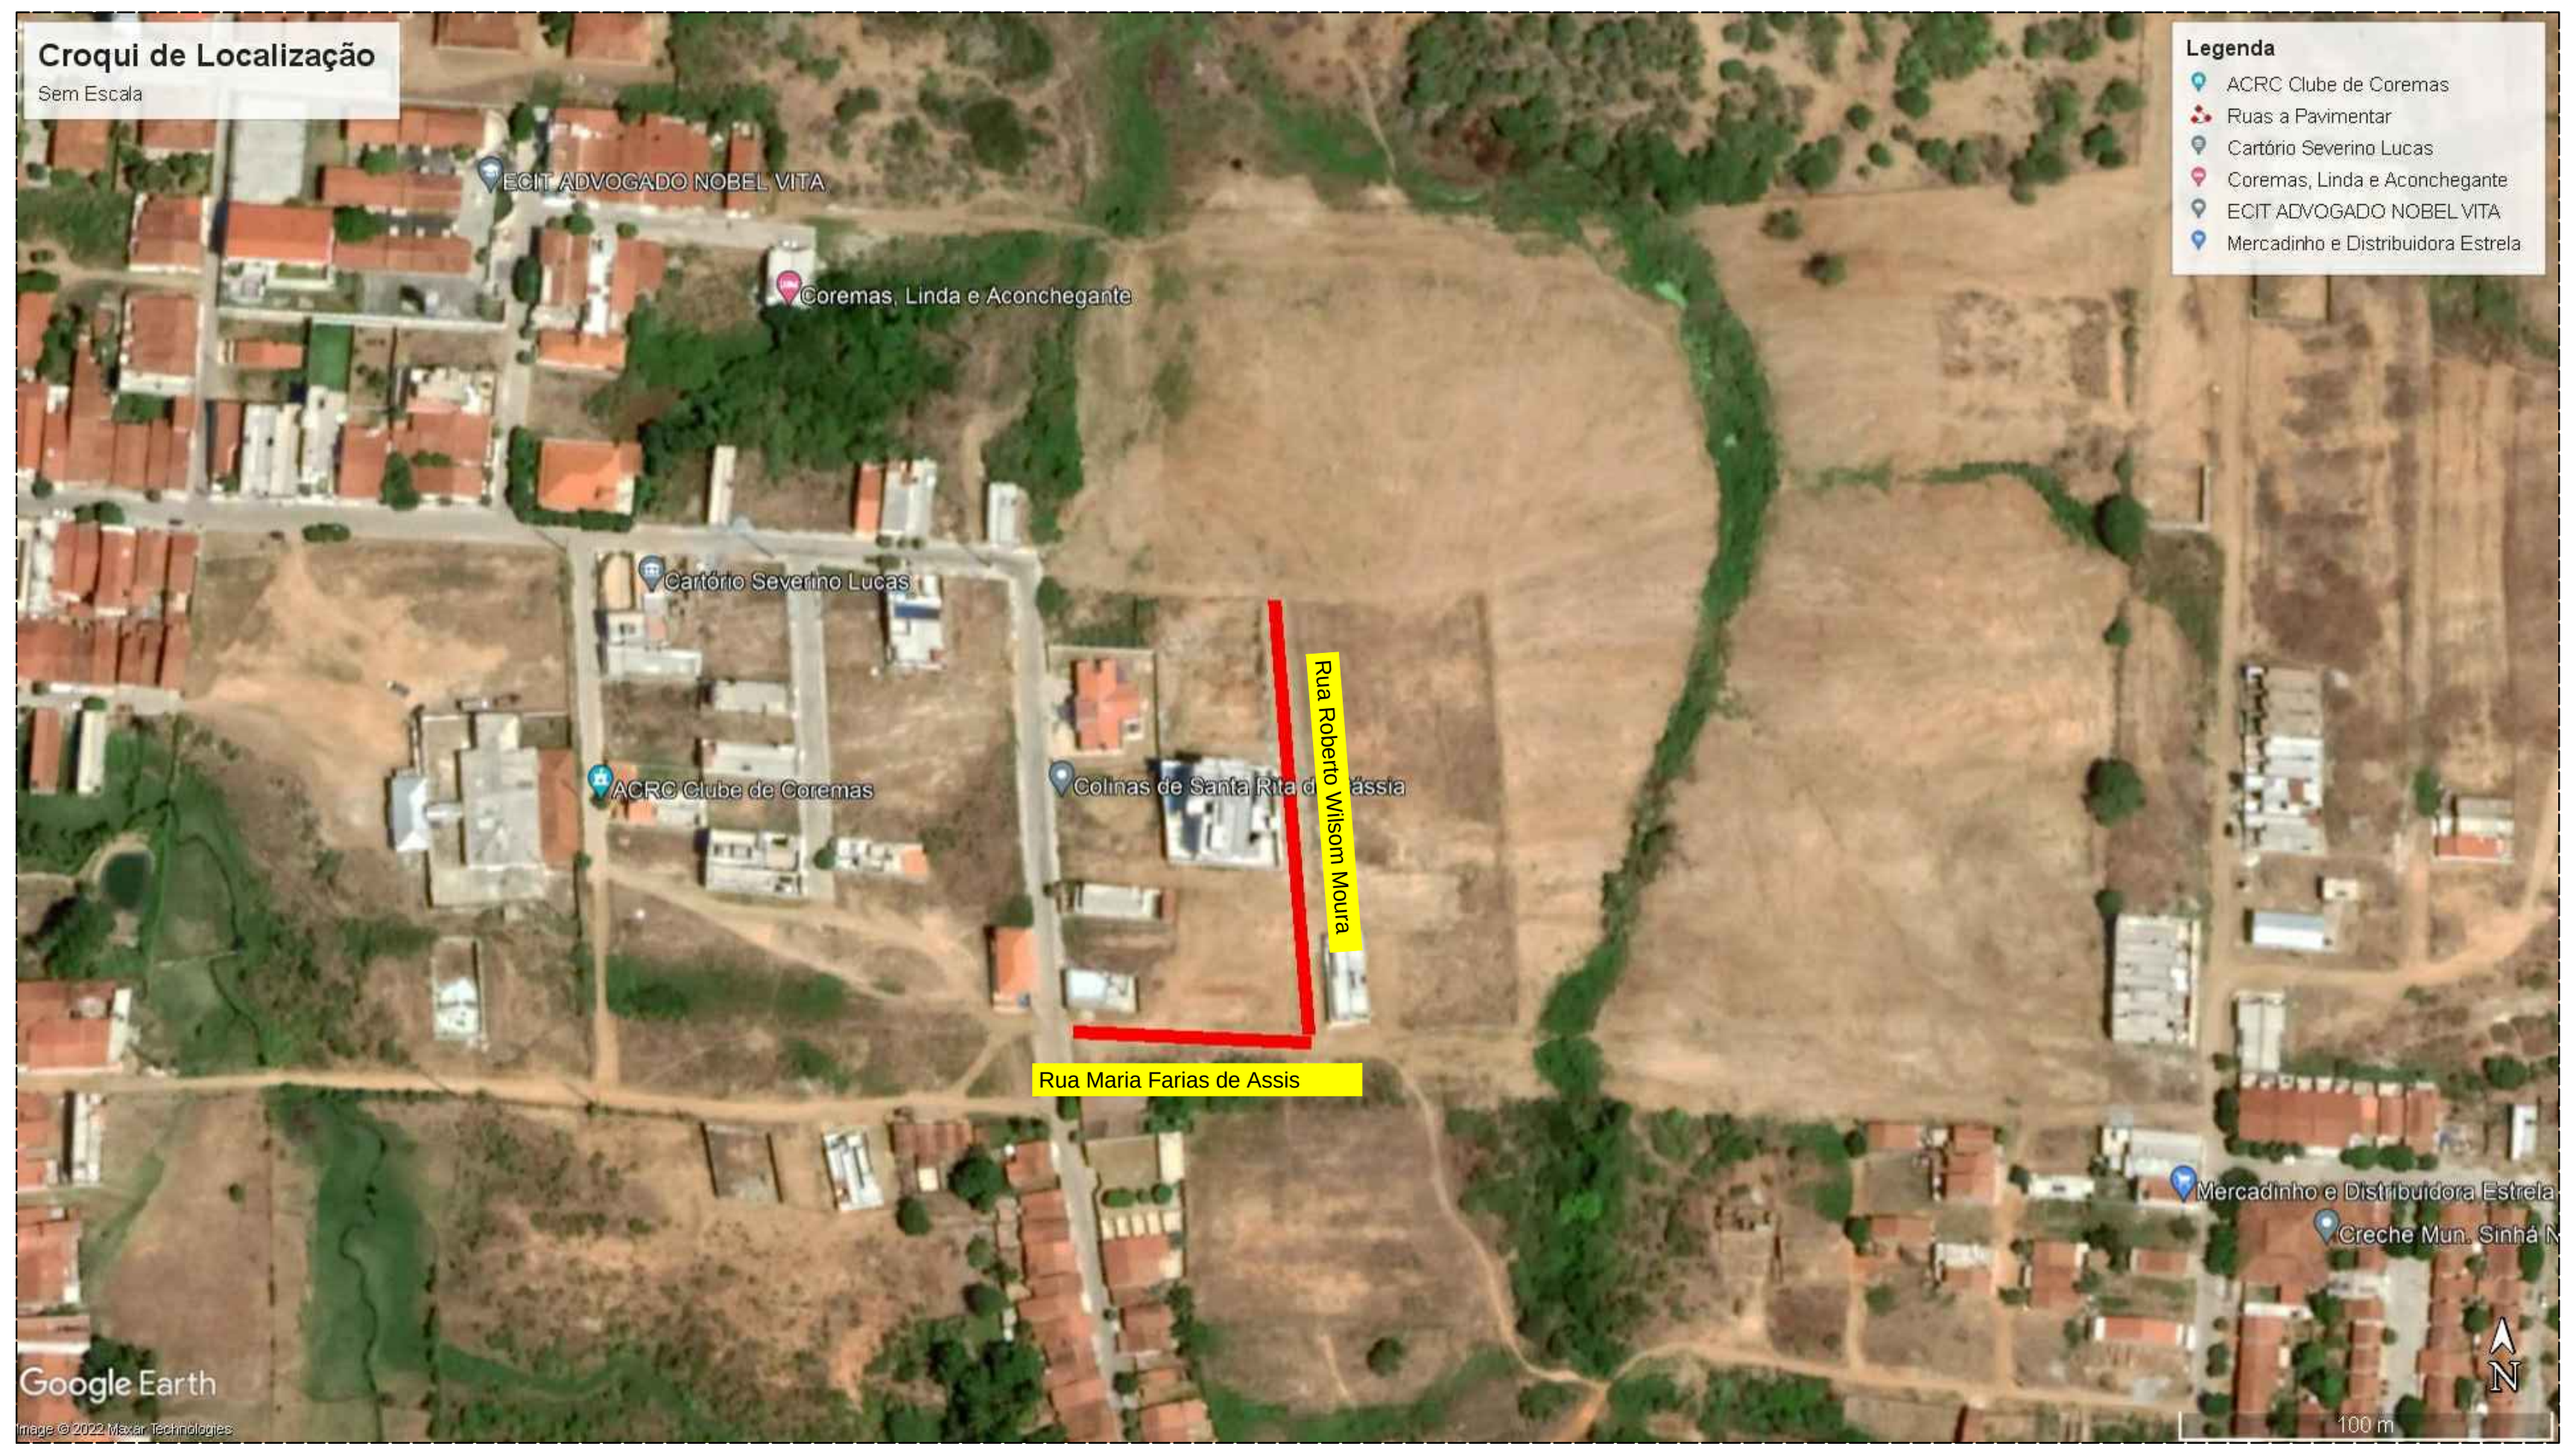
Croqui de Localização
Sem Escala
Legenda
ACRC Clube de Coremas
Ruas a Pavimentar
Cartório Severino Lucas
Coremas, Linda e Aconchegante
ECIT ADVOGADO NOBEL VITA
Mercadinho e Distribuidora Estrela
ECIT ADVOGADO NOBEL VITA
Coremas, Linda e Aconchegante
Cartório Severino Lucas
ACRC Clube de Coremas
Colinas de Santa Rita de Cássia
Rua Roberto Wilsom Moura
Rua Maria Farias de Assis
Mercadinho e Distribuidora Estrela
Creche Mun. Sinhá N
Google Earth
Image © 2022 Maxar Technologies
100 m
N

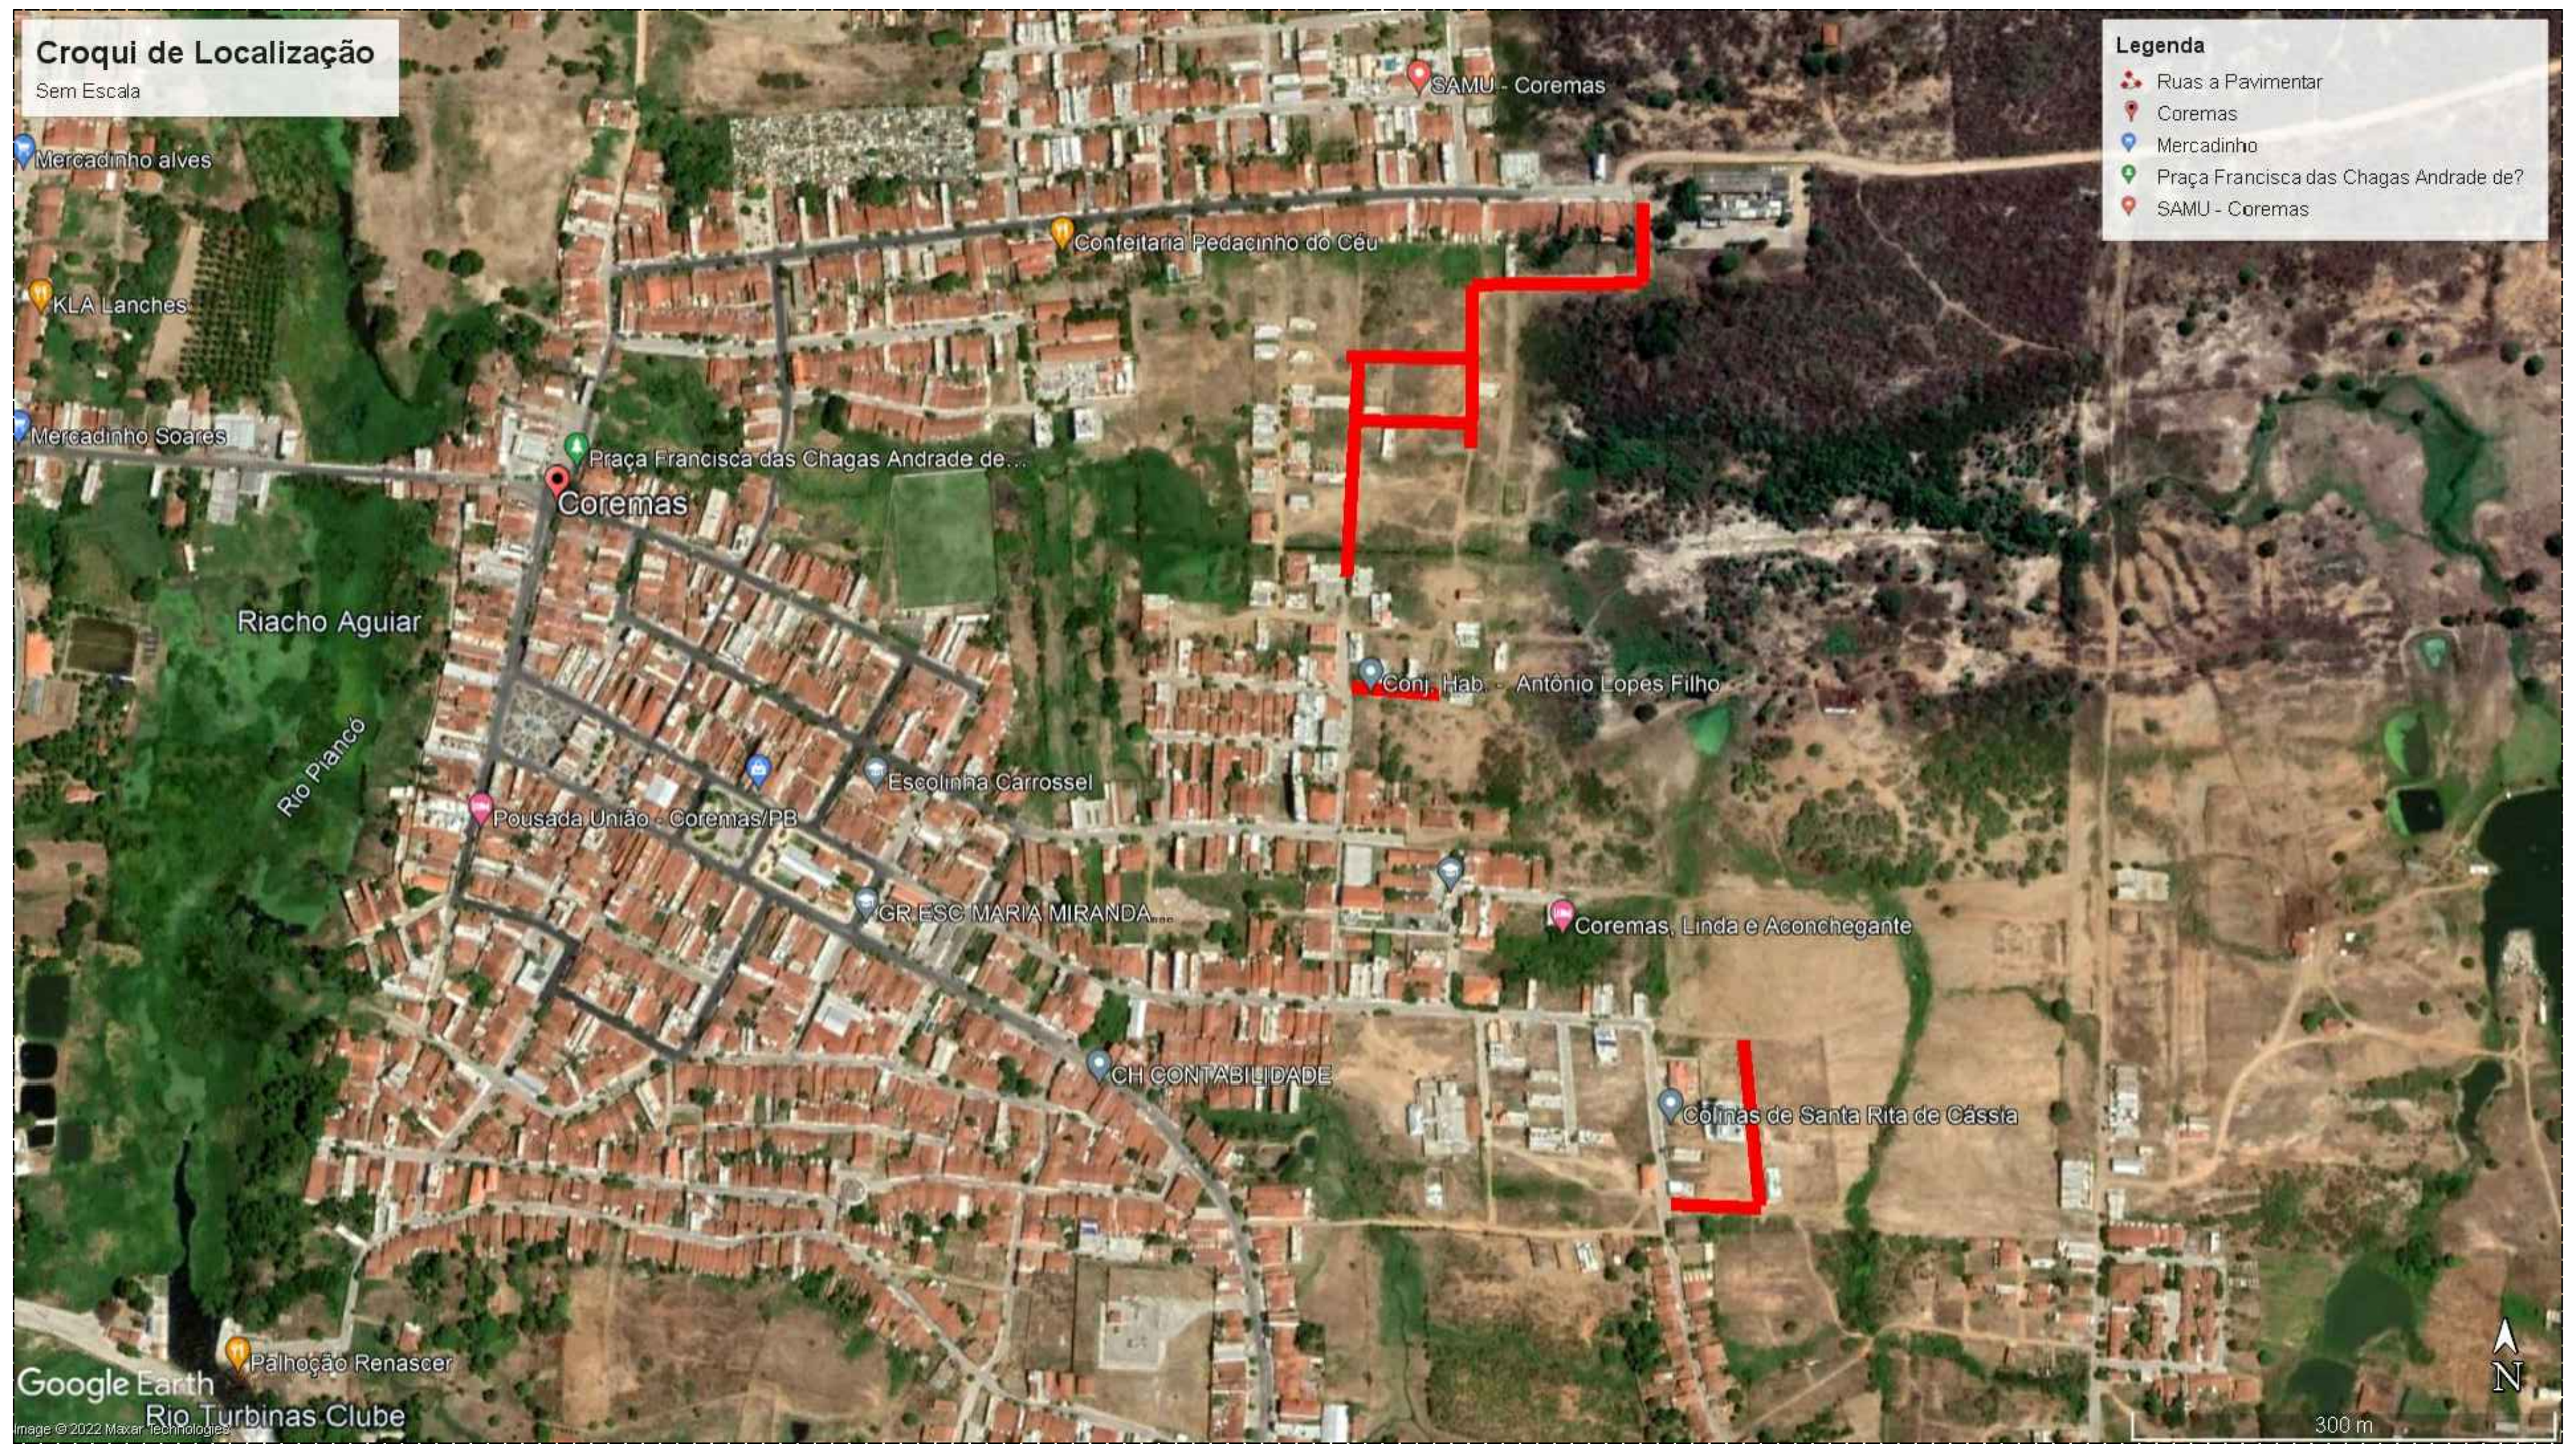
Croqui de Localização
Sem Escala
Legenda
Ruas a Pavimentar
Coremas
Mercadinho
Praça Francisca das Chagas Andrade de?
SAMU - Coremas
Mercadinho alves
KLA Lanches
Mercadinho Soares
SAMU - Coremas
Confeitaria Pedacinho do Céu
Praça Francisca das Chagas Andrade de...
Coremas
Riacho Aguiar
Rio Piancó
Conj. Hab. - Antônio Lopes Filho
Escolinha Carrossel
Pousada União - Coremas/PB
GR ESC MARIA MIRANDA...
Coremas, Linda e Aconchegante
CH CONTABILIDADE
Colinas de Santa Rita de Cássia
Palhoção Renascer
Rio Turbinas Clube
Google Earth
Image © 2022 Maxar Technologies
300 m
N

PROPRIETÁRIO Prefeitura Municipal de Coremas- PB

Kleber Sá de Oliveira
Engenheiro Civil
CREA 1602682780

PROJETISTA Kleber Sá de Oliveira

EPE
EMPRESA PARAIBA DE ENGENHARIA

PROJETO:
PAVIMENTAÇÃO DE RUAS E VIAS
LOCAL:
MUNICÍPIO DE COREMAS - PB
PROPRIETÁRIO:
PREFEITURA MUNICIPAL DE COREMAS - PB

FOLHA
07/07
ESCALA:
Indicadas
DESENHOS:
Indicados
RESPONSÁVEL TÉCNICO:
Kleber Sá de Oliveira
Crea: 160391676-8
ANOTAÇÕES:

ARQUIVO:
PAV_COREMAS_FINAL_2022.dwg
DESENHO:
Diego Medeiros
DATA:
SET - 2022