


Legenda

Pavimentação

- Pavimentação a Construir
- - - Meio-fio Projetado
- - - Cordão em Granito

Rua Maria José de Leite Andrade (Pombalzinho)			
PAVIMENTAÇÃO EM PARALELEPÍPEDO			
Objeto: Planta baixa e detalhamento da pavimentação e meio-fio			
Endereço:	Coremas/PB	Coordenadas:	
Localidade:	Prefeitura Municipal de Coremas	UF/PAÍS:	08 938.936/0001-94
Responsável Técnico:	Fernando Matias Mamude	Função:	Engenheiro Civil
Registro:		Encha:	162056275-8
Desenho: FERNANDO MATIAS MAMUDE Data: 10.04.2023 13:40:00 Via: Digite em: 10/04/2023 13:40:00		Planta baixa de um trecho de estrada localizado na cidade de Coremas. Contendo coordenadas do local, indicação do estacamento quando necessário a cada 20 metros, cotas indicando o comprimento do meio-fio e largura do trecho a ser pavimentado.	
01/01			

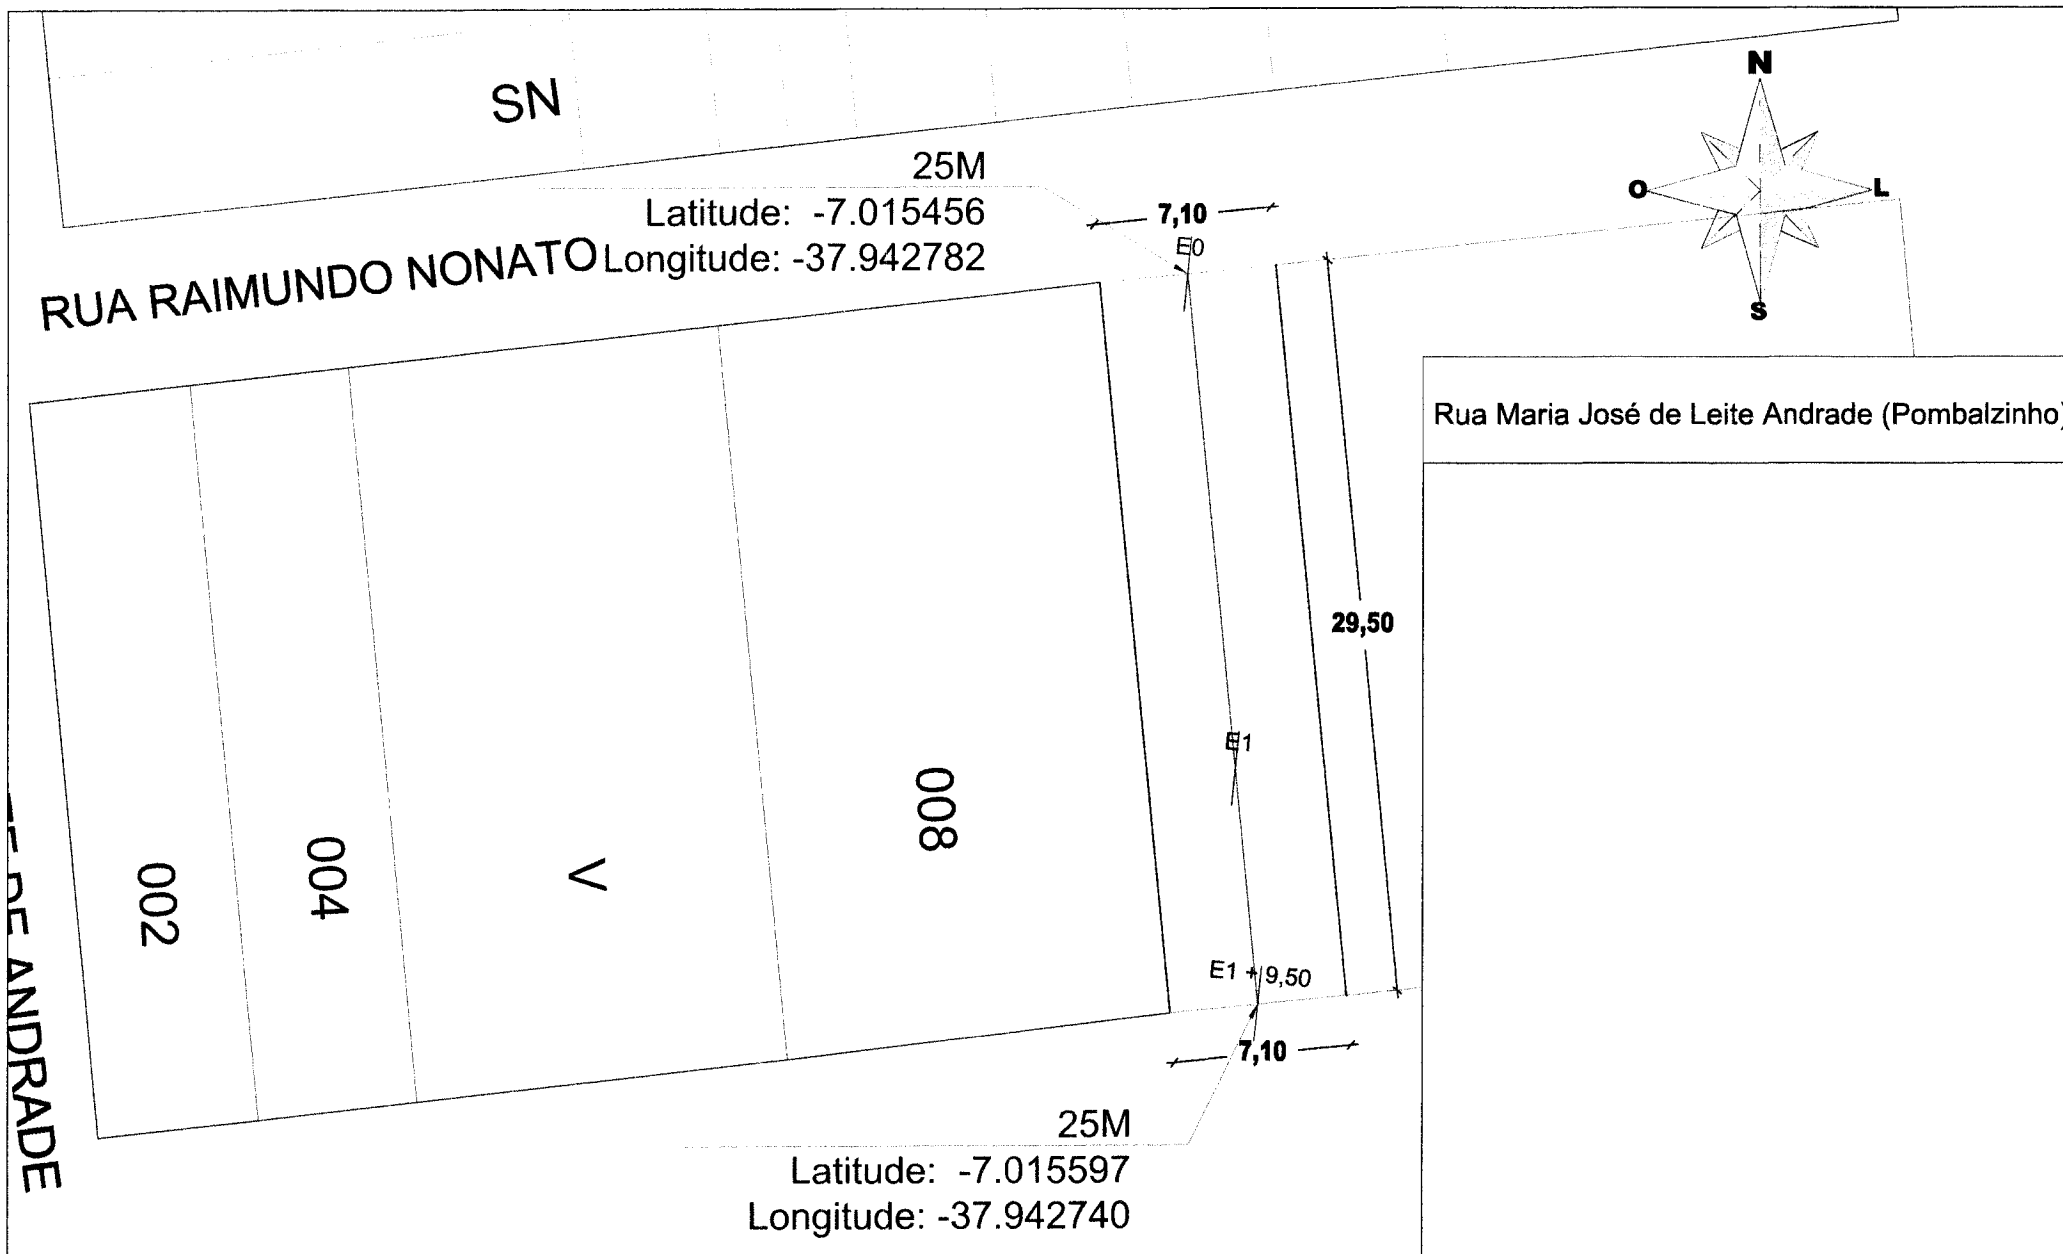