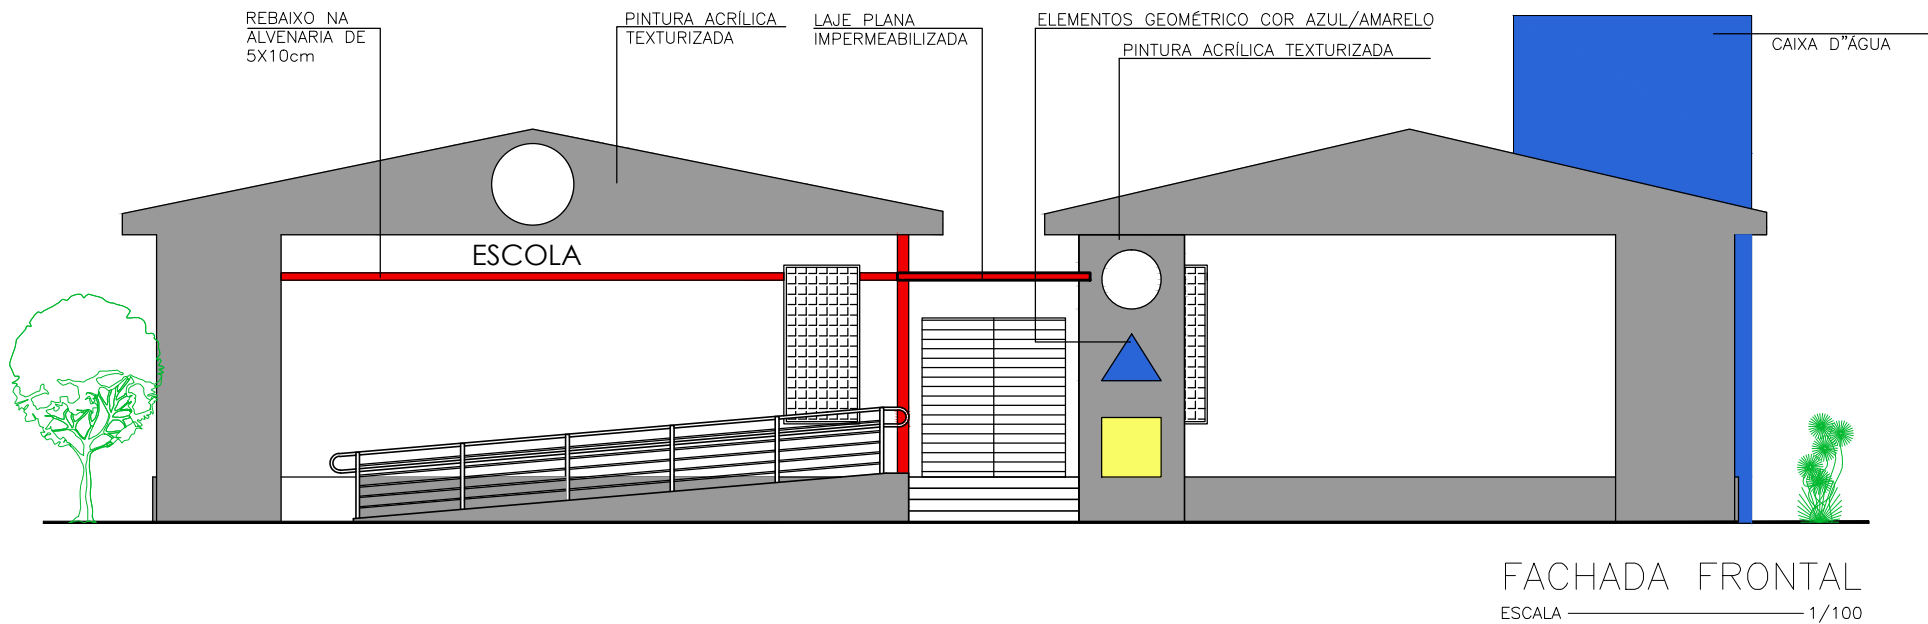
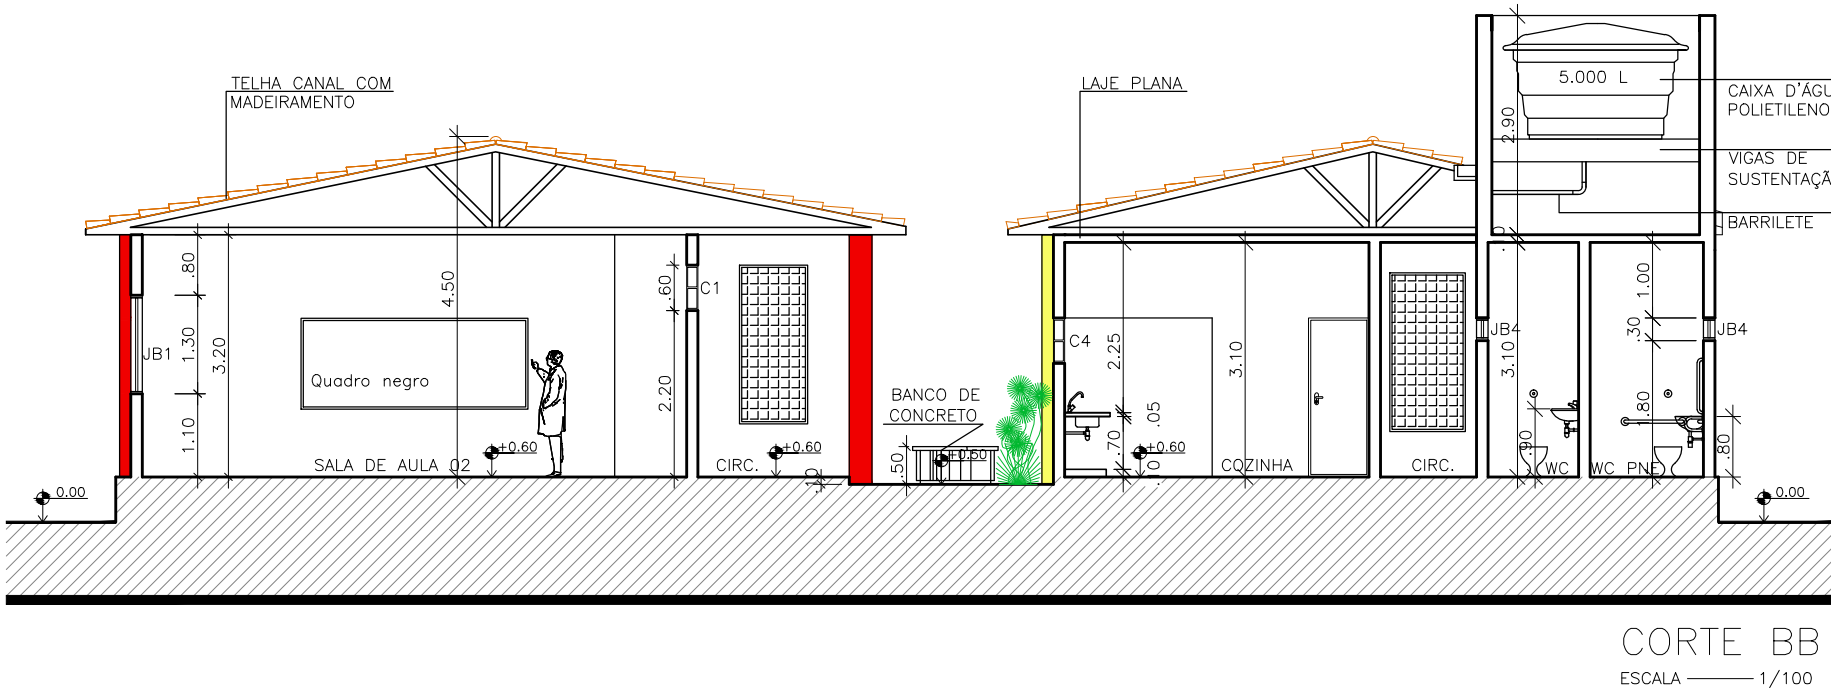
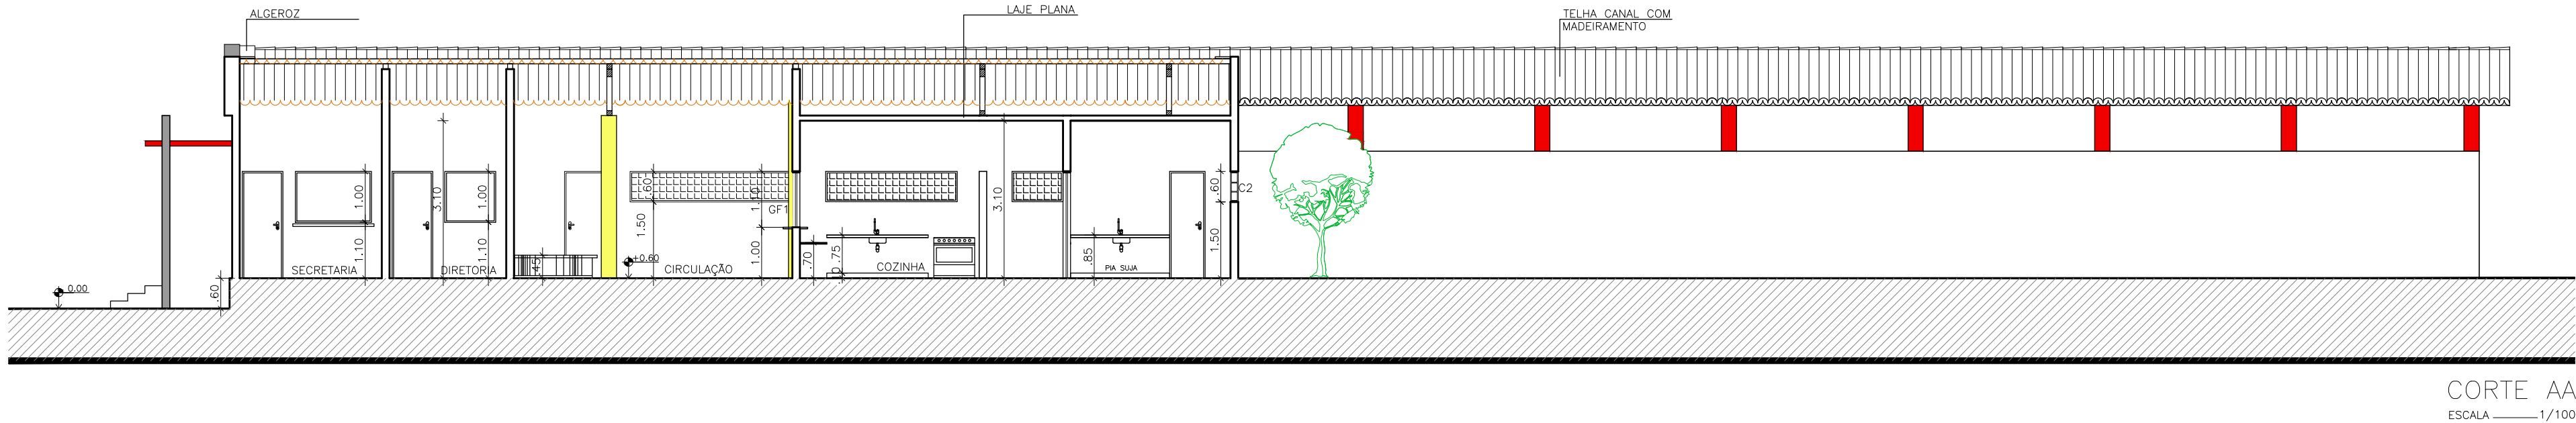


Convenções:					
Discriminação	L x h:	Qt.	Discriminação	L x h:	Qt.
Portas:	P1 0.80X2.10	12	Elemento Vazado	C1 4.85X0.60	06
	P2 0.70X2.10	09		C2 1.00X2.10	06
	P3 1.90X2.10	01		C3 1.20X0.60	01
				C4 2.40X0.60	01
				C5 3.37X2.10	01
Janelas:	JB1 3.37X1.30	10	Grades de Ferro:	C6 1.00X0.60	02
	JB2 3.30X1.30	02		C7 0.90X0.60	02
	JB3 1.20X1.30	03		PF1 0.80X2.10	02
	JB4 1.20X0.30	05		GF1 1.50X1.00	02
	JB5 1.00X0.30	02			
	J1 1.00X1.00	01			

GOVERNO DO ESTADO DA PARAÍBA

GERÊNCIA DE ACOMPANHAMENTO E MANUTENÇÃO DE OBRAS * COTESE

Projeto: UNIDADE ESCOLAR 6 SALAS

Local:

Este Projeto todos os direitos reservados ao Governo do Estado/PB

Arquiteto: ROSANE TOSCANO DE THEORGA FREIRE CAU – A10259–8		Engenheiros:		
Resp. CAD:	CAD: JOÃO PAULO FALCÃO ALINE KELLEN	Insc.:	Escalas: 1:100	Data: 01/2018
Prancha:	Desenhos:	Áreas:		
03/04	CORTES E FACHADAS	ÁREA CONSTRUÍDA = 466,00 m2 TERRENO MÍNIMO NECESSÁRIO = 30 X 50m		