

[illegible]

Quadro de Cargas (CM1)																
Circuito	Descrição	Esquema	Método	Tensão (V)	Pot. total (VA)	Pot. total (W)	Fases	Pot. - R (W)	Pot. - T (W)	Pot. - FCA (W)	Ip Sécção (A)	Ip Sécção (A)	Disj. dv. pare. dv. total	Status		
				de 120V							(A)	(A)	(A)			
Q01	3F+N+T	B1	380/220V	10782	17804	R+S+T	6000	5984	5960	100,7	70,43	30,33	160,32	0,82	97	OK
Q02	3F+N+T	B1	380/220V	15336	25138	R+S+T	1560	1562	1588	100,7	70,43	28,33	160,32	0,75	90	OK
Q03	3F+N+T	B1	380/220V	12924	21228	R+S+T	1320	1320	1356	100,7	70,43	30,33	160,32	0,64	88	OK
TOTAL				27634	45170	R+S+T	1560	1562	1624					1,64	180	OK





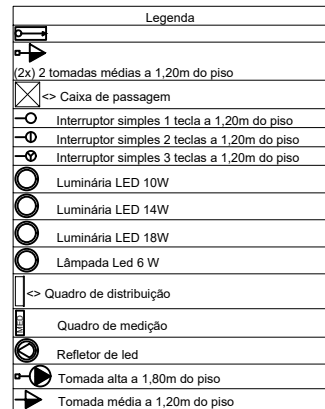
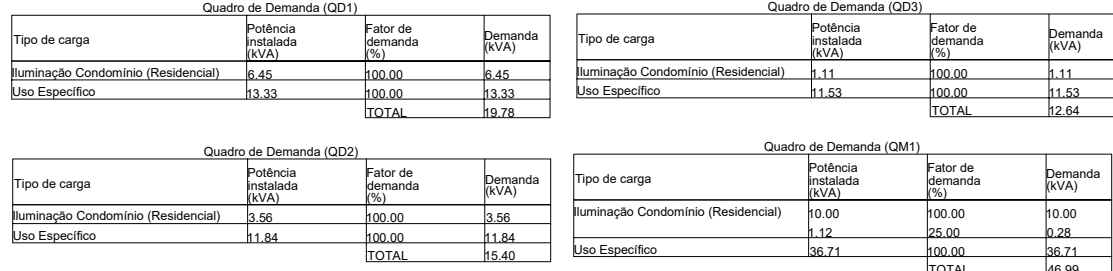


Luminária a acessórios	
Luminária Led Embutir	
Ledvance Downlight 14W	4 pe
Ledvance Insert 18W	100 pe

PROJETO: FERNANDO MATIAS MAMEDE - CREA: 162056275-8

		ARQUIVO
Aprovações:		

Aprovações

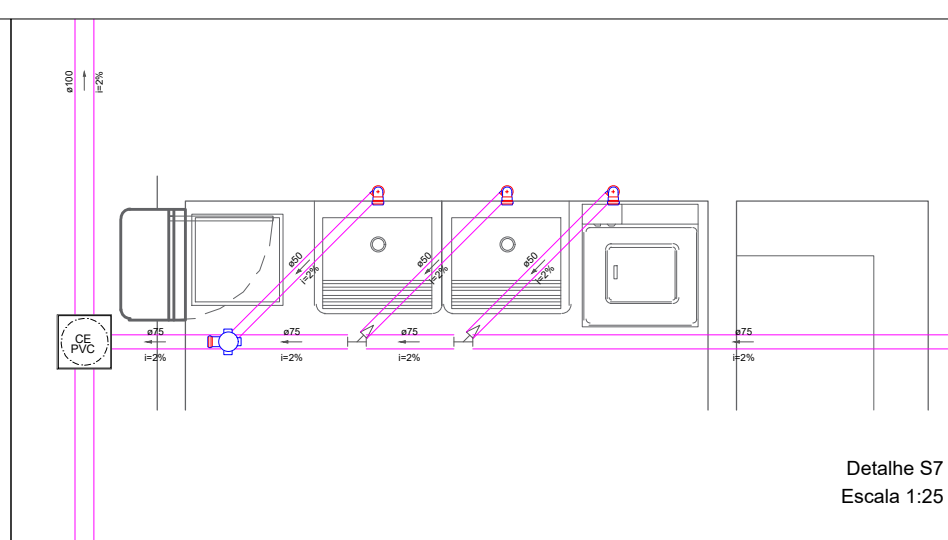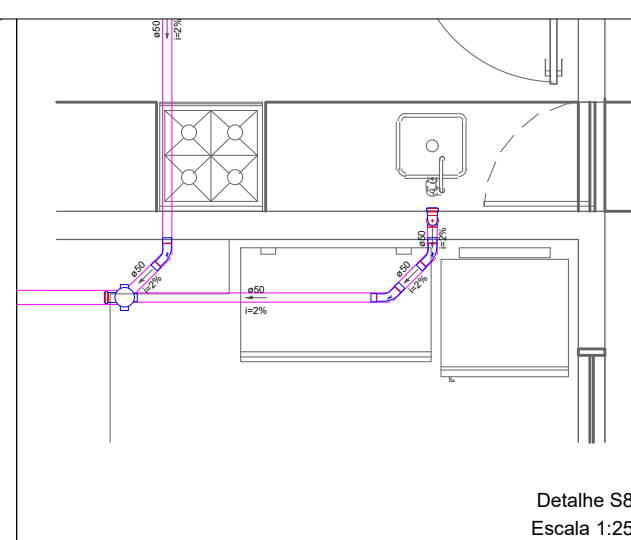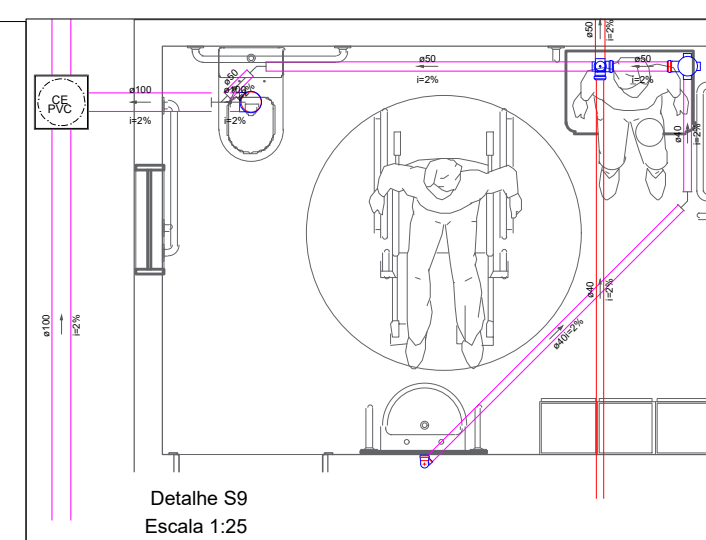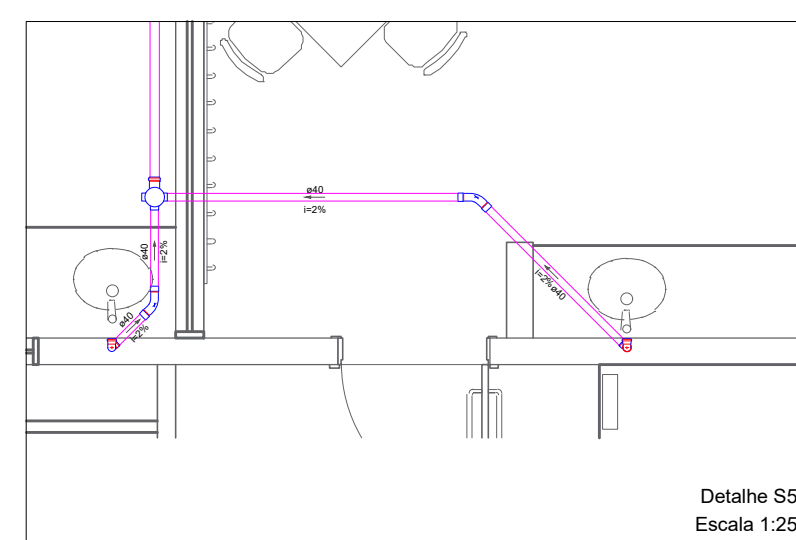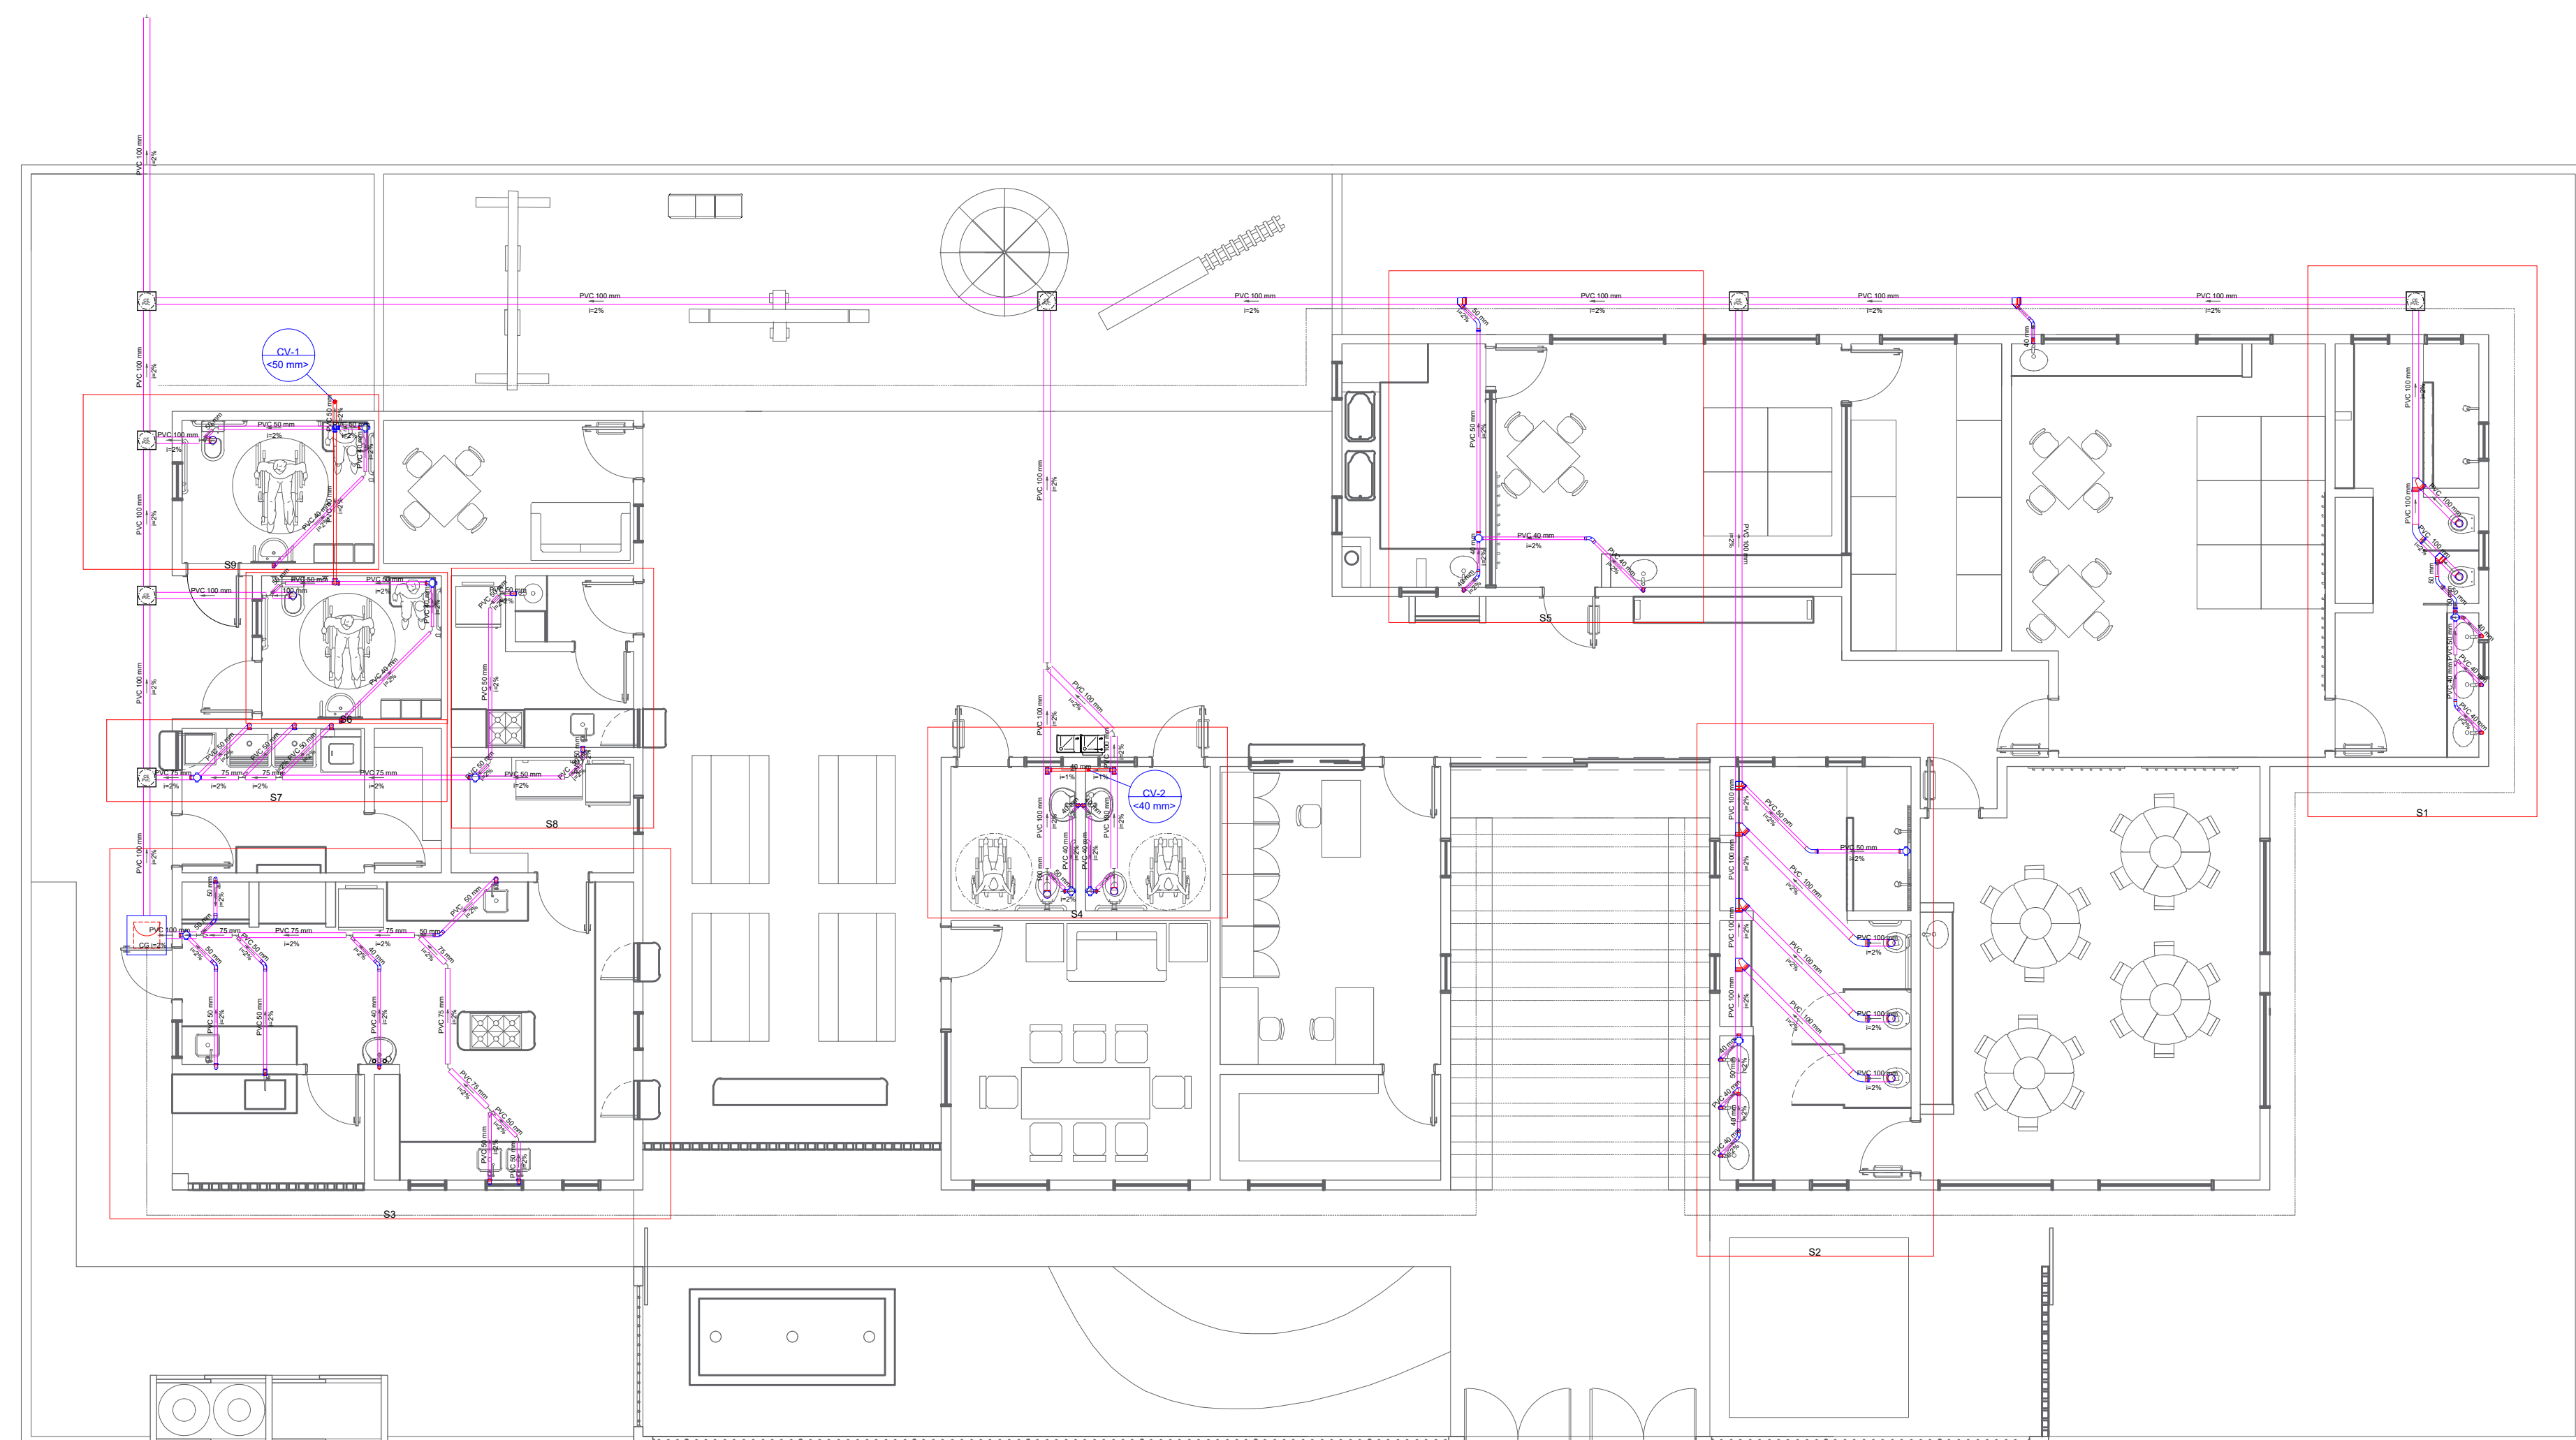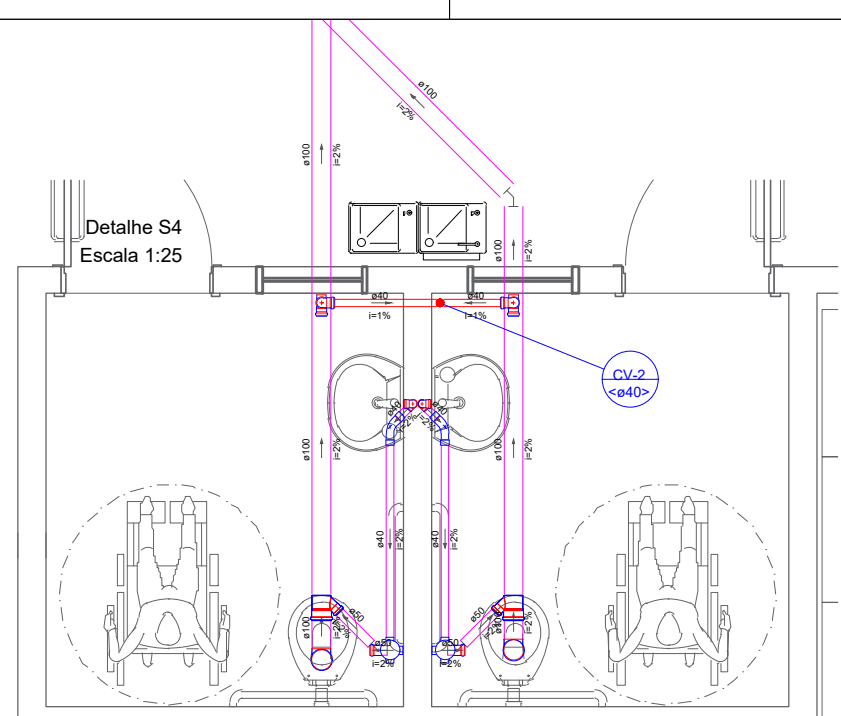





Lista de Materiais	
Caixas / Despejos	
Caixa de porta	1
Caixa de passagem	1
Caixa de passagem PVC	2,90
PVC Acessórios	
Caixa esfumada	
100x100x40	11,90
50% de corte p/ pia e lavatório	1
1" - 1/2"	8,90
1" - 1/2"	8,90
1" - 1/2" - 2"	2,90
Válvula p/ Adaptador e tanque	1
Válvula p/ pia	1
Válvula p/ tanque	1
40 mm	2,80
PVC Esgoto	
Caixa 45 longa	
100 mm	1
50 mm	1
Caixa 45 longa Amarelo	
40 mm	10,90
Caixa 90 curta	
40 mm	14,90
40 mm	1
Caixa 90 - Jêto	
50 mm	50,90
50 mm	1
Jêto 90 Jêto curto p/ esgoto secundário	
40 mm x 1,12"	14,90
Jêto 90 - Jêto	
100 mm - 50 mm	4,90
100 mm - 100 mm	4,90
50 mm - 50 mm	1
Tubo registro p/ porta-lua	
40 mm	88,00
40 mm	21,00
40 mm	21,00
75 mm - 2"	11,20
75 mm - 2"	37,00
75 mm - 2"	37,00
75 mm - 2"	11,20
75 mm - 2"	37,00

PROPRIETÁRIO: PREFEITURA MUNICIPAL DE COREMAS - PB

PROJETO: FERNANDO MATIAS MAMEDE - CREA: 162056275-8

FOLHA		PROJETO: CONSTRUÇÃO DE CRECHE COM CAPACIDADE PARA 50 CRIANÇAS		
01/01		CONCEDENTE:		
		CONVENIENTE: PREFEITURA MUNICIPAL DE COREMAS - PB		
		LOCALIDADE: MUNICÍPIO DE COREMAS - PB		
	DATA	RESPONSÁVEL	RUBRICA	DADOS
CESSADO				
COPIA				
EXENTO				
ESCALAS	DESENVOLVIMENTO			PROPOSTA
	Projeto Sanitário - Térreo			
	Planta Baixa			REVISÃO
	Detalhes			
INDICADA				ARQUIVO

Aprovações:

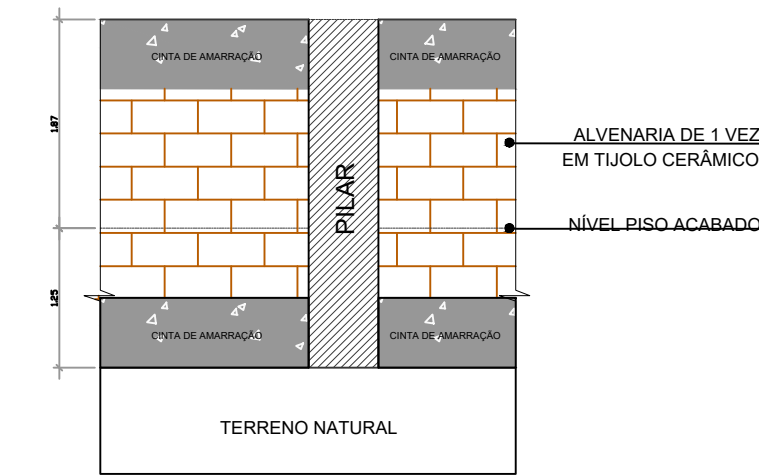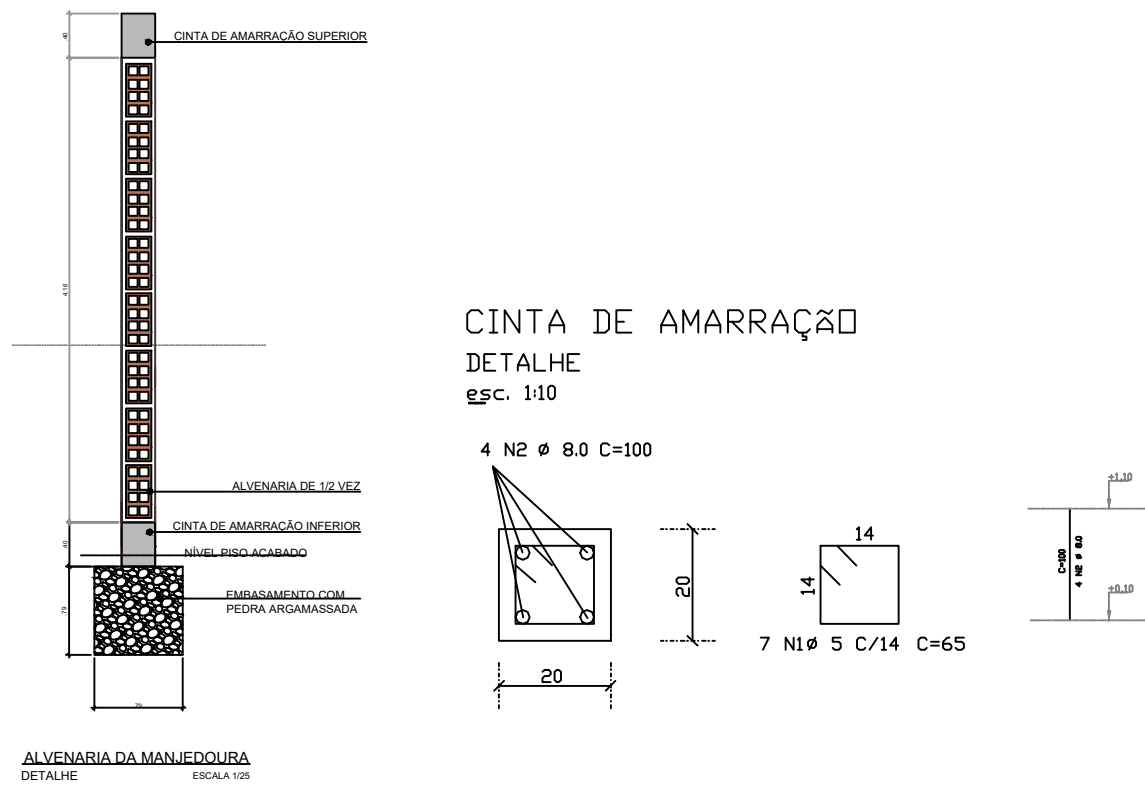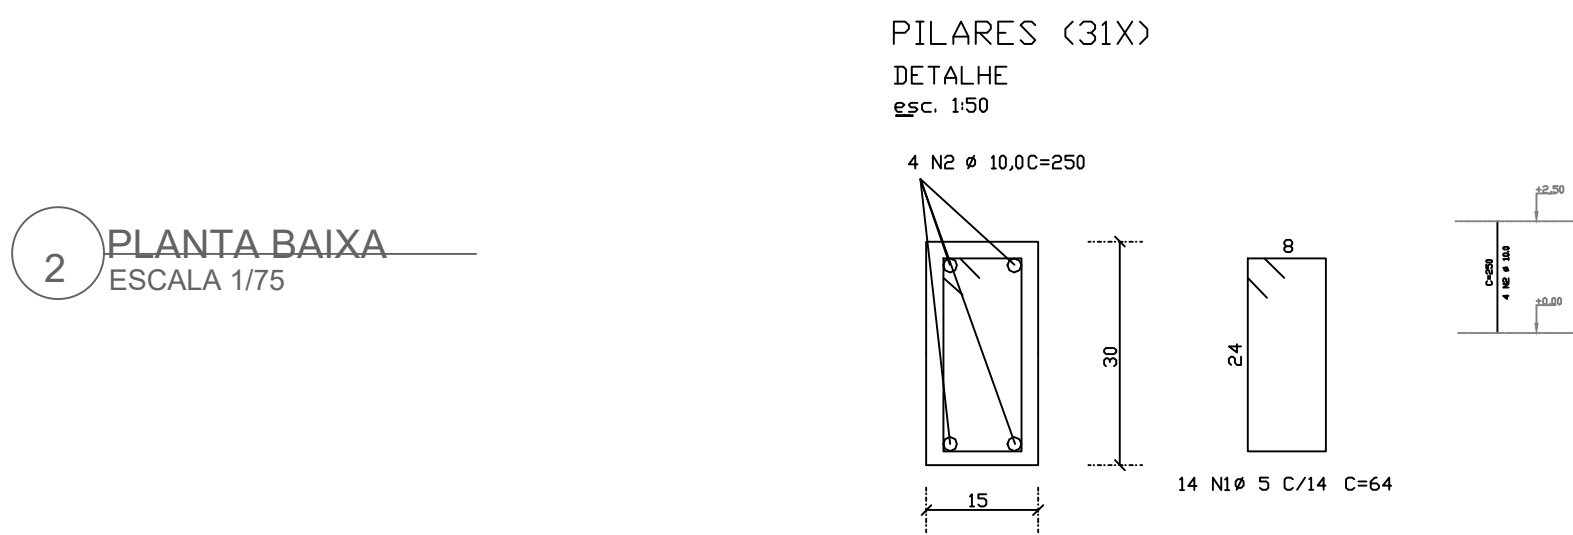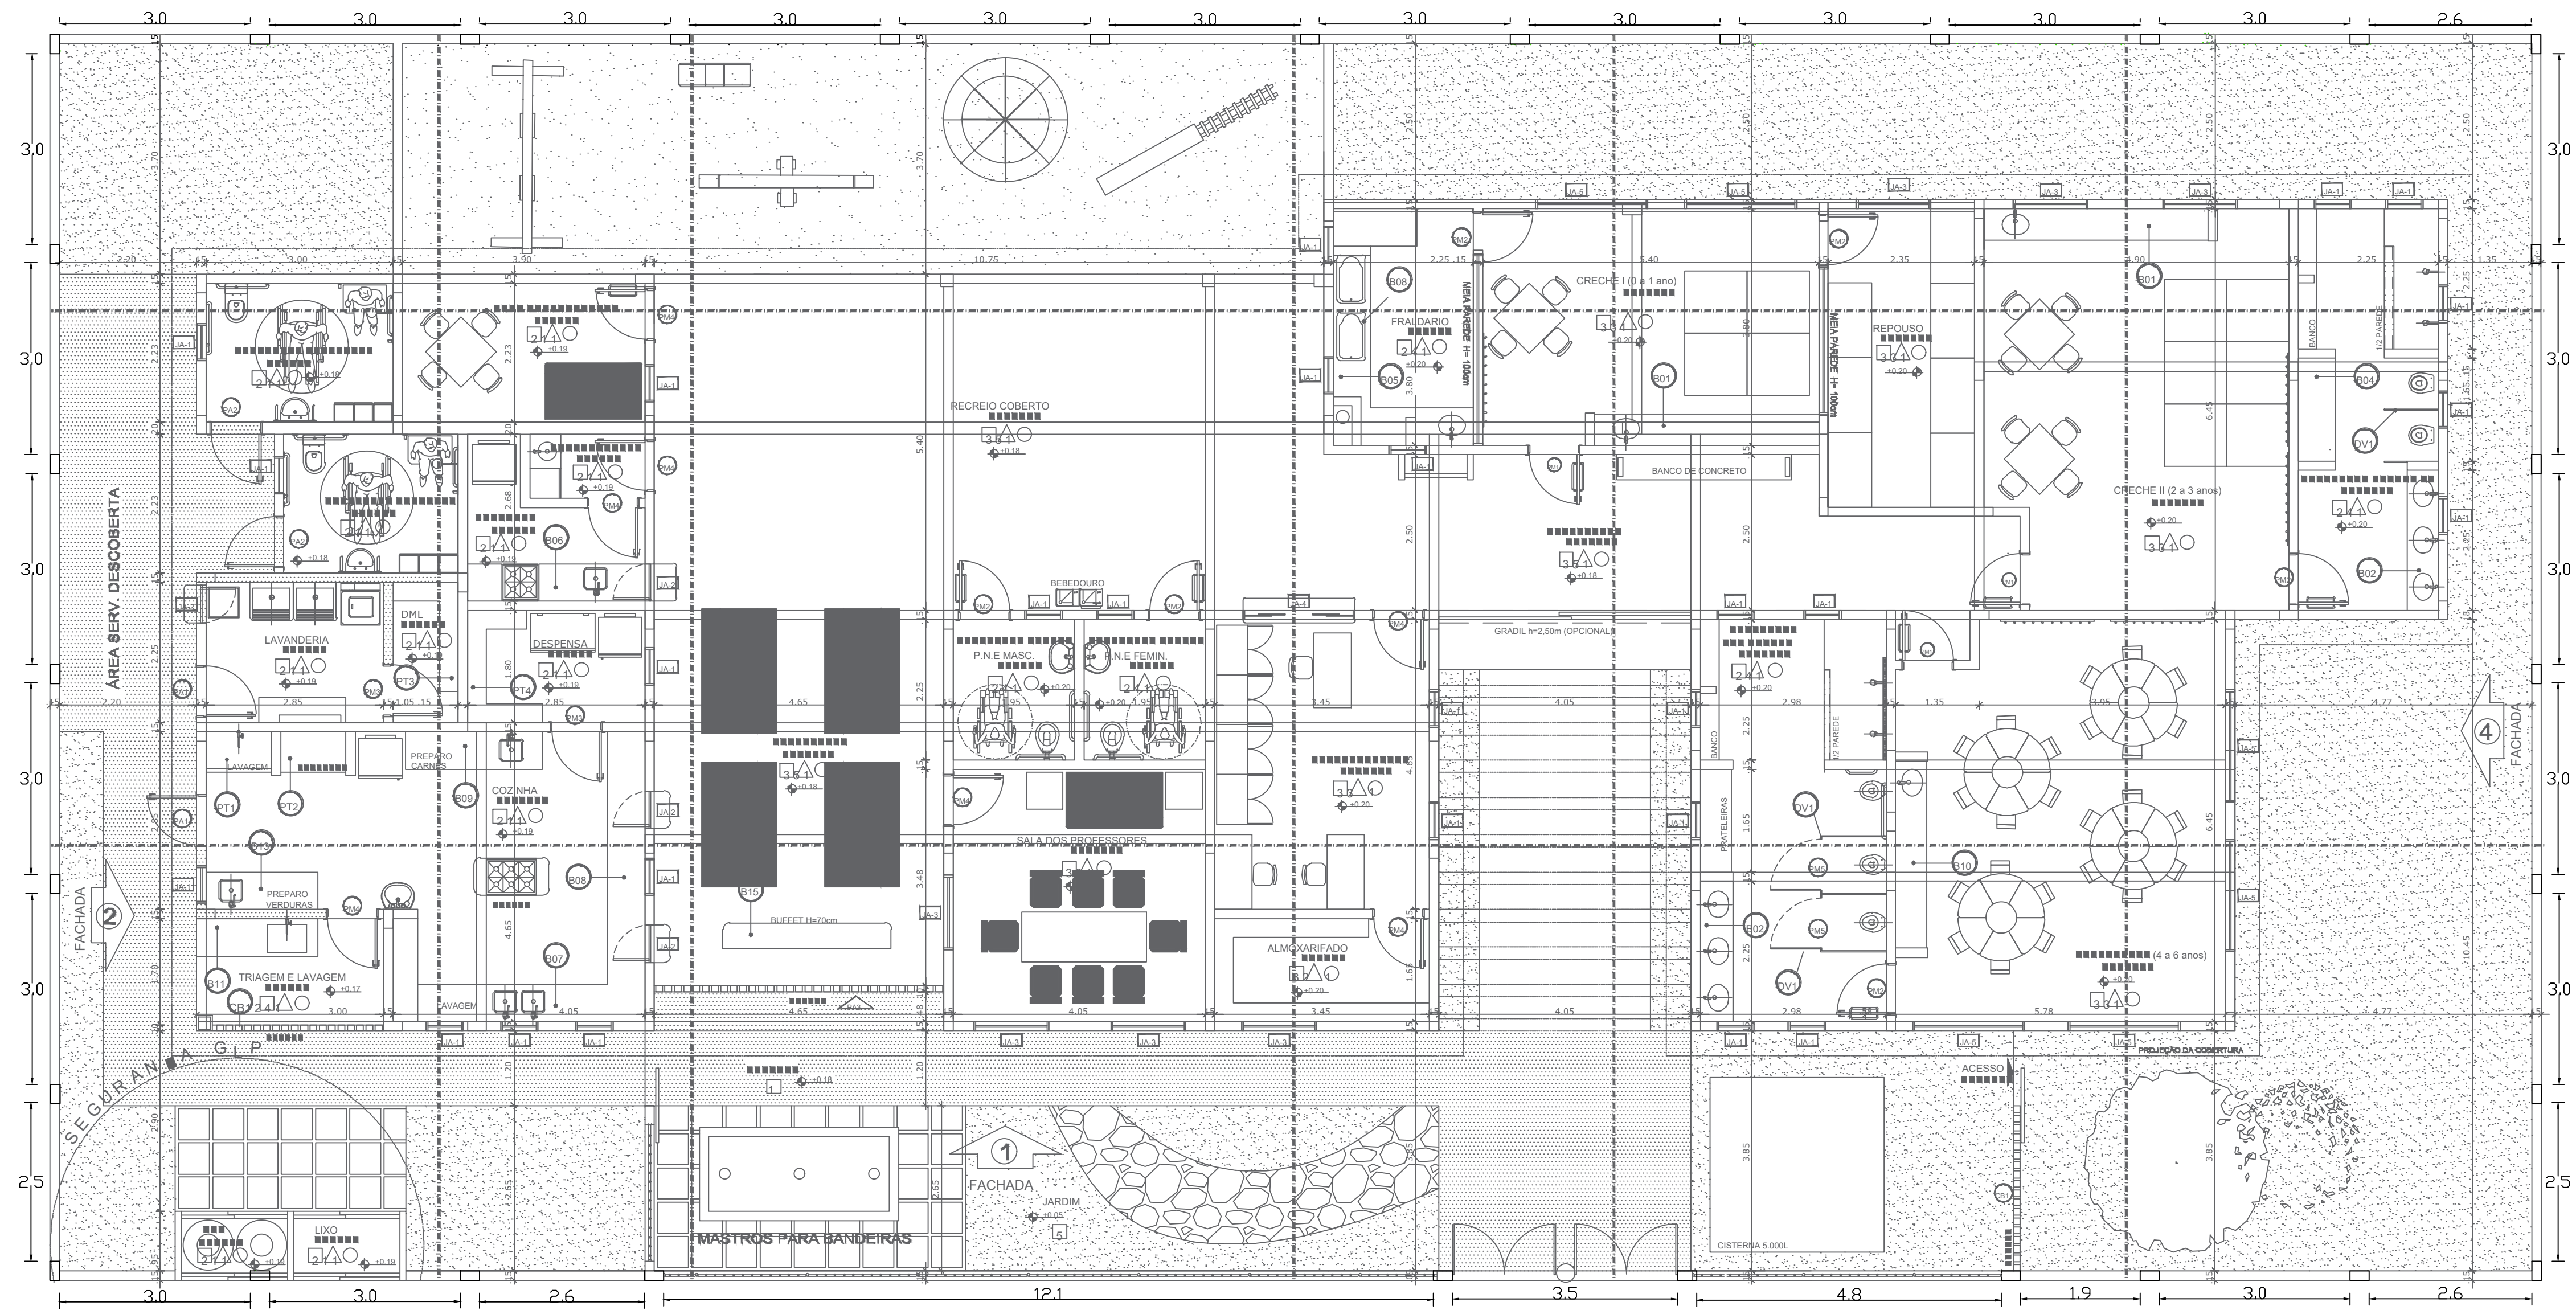


PROPRIETÁRIO: PREFEITURA MUNICIPAL DE COREMAS

PROJETO: FERNANDO MATIAS MAMEDE CREA 162056275-8

FOLHA	PROJETO: CONSTRUÇÃO DE CRECHE COM CAPACIDADE PARA 50 CRIANÇAS			
	CONVENIENTE: PREFEITURA MUNICIPAL DE COREMAS			
14/14	LOCALIDADE: MUNICÍPIO DE COREMAS - PB			
	DESENHO	DATA	RESPONSÁVEL	RUBRICA
ESCALAS	ABRIL/2022			
INDICADO	DESENHOS			CONVÊNIO
	- Muro - Legenda			ARQUIVO

Aprovações:



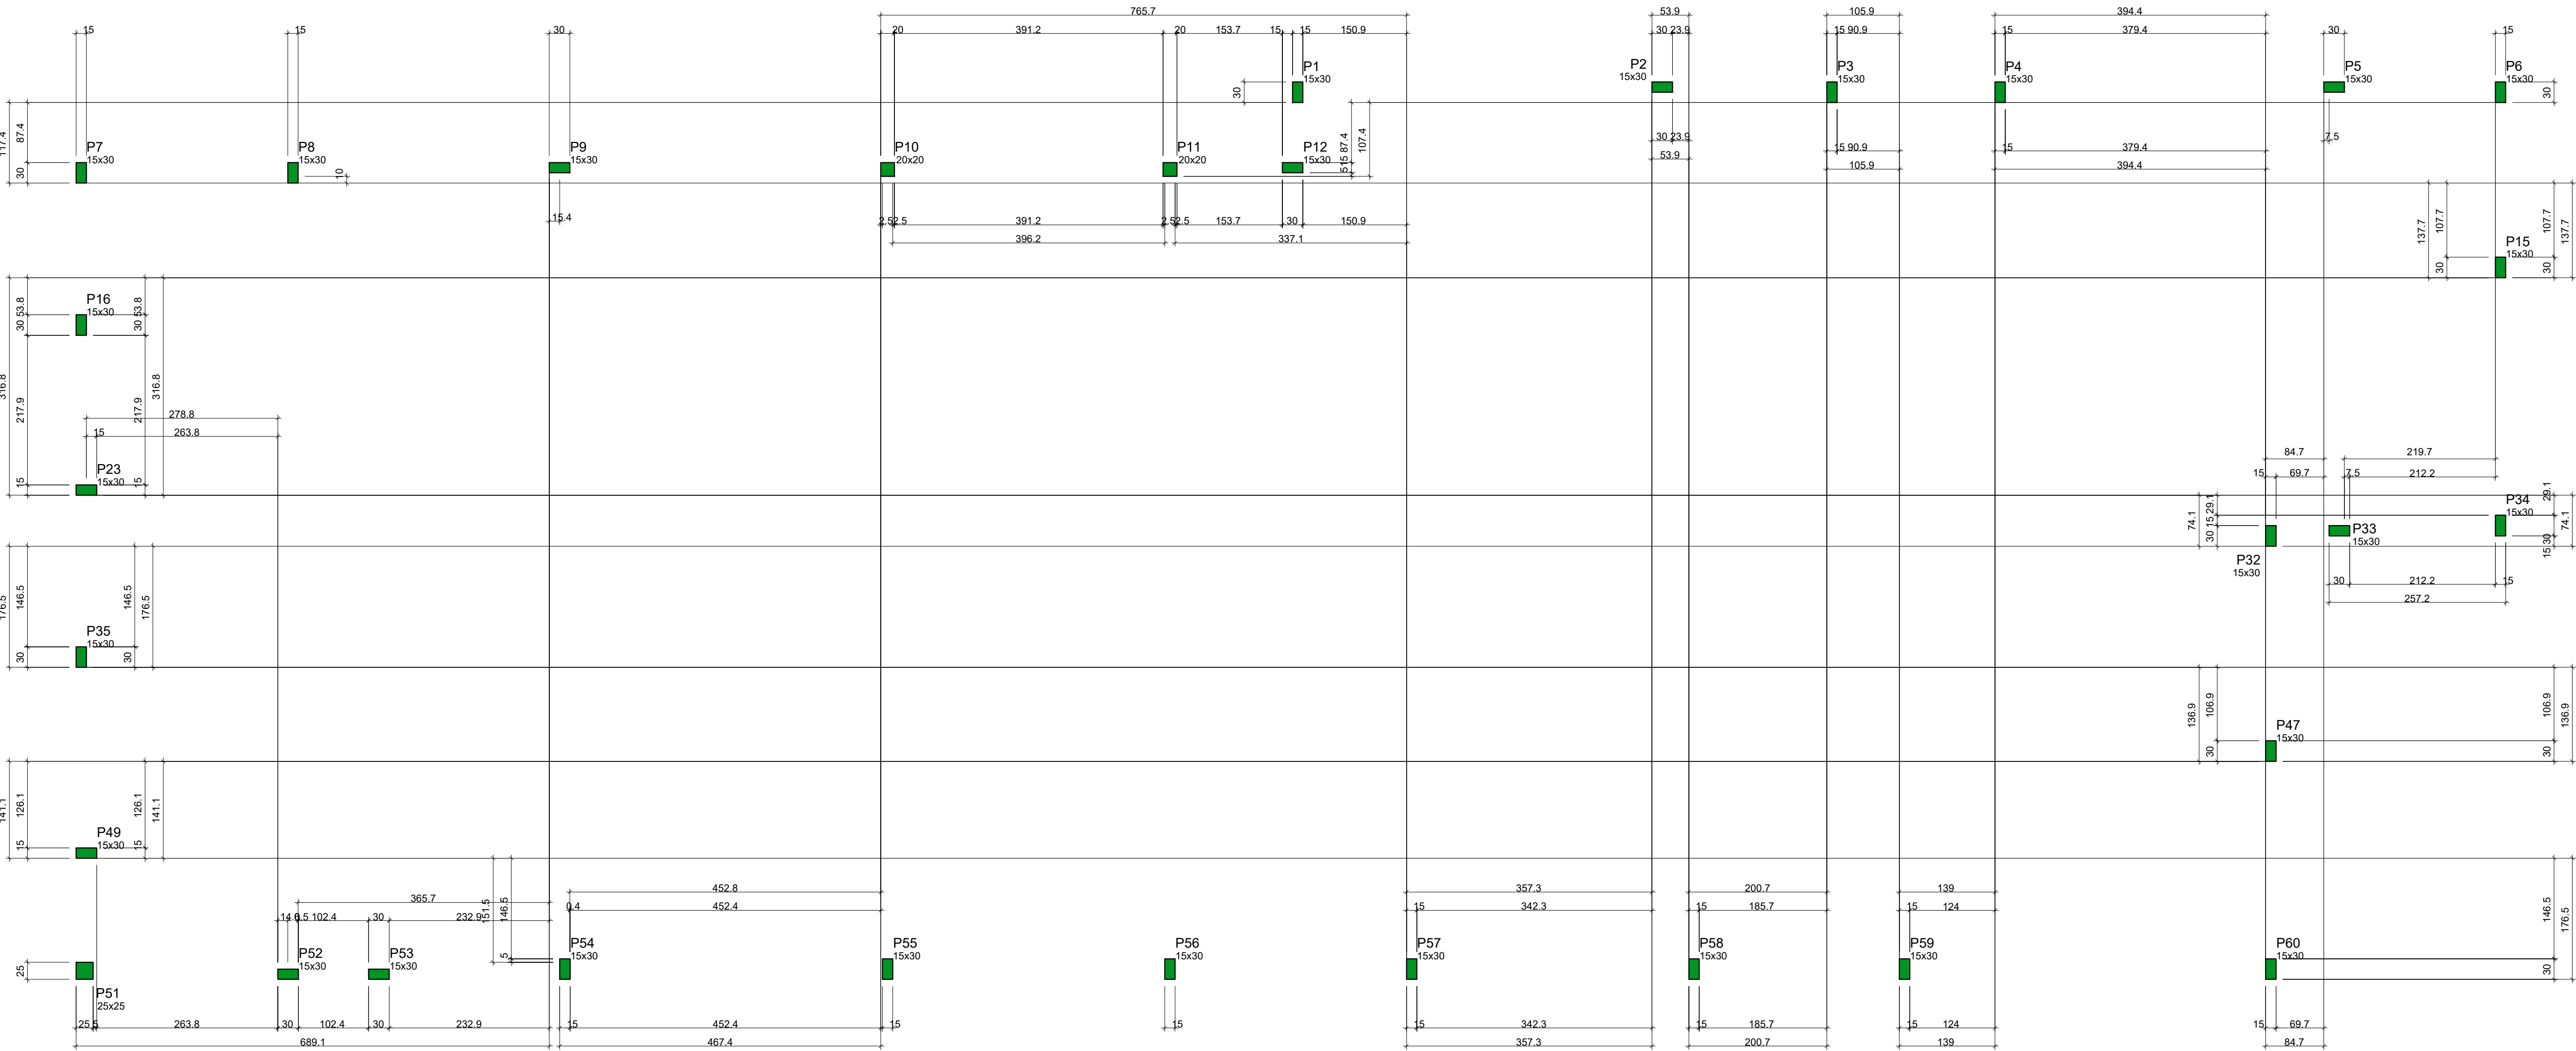


Características dos materiais		
	fck (kgf/cm²)	Ecs (kgf/cm²)
	250	241500

Pilares		
Nome	Seção Elevação (cm)	Nível (cm)
P1	15x30	0 430
P2	15x30	0 430
P3	15x30	0 430
P4	15x30	0 430
P5	15x30	0 430
P6	15x30	0 430
P7	15x30	0 430
P8	15x30	0 430
P9	15x30	0 430
P10	20x20	0 430
P11	20x20	0 430
P12	15x30	0 430
P15	15x30	0 430
P16	15x30	0 430
P23	15x30	0 430
P32	15x30	0 430
P33	15x30	0 430
P34	15x30	0 430
P35	15x30	0 430
P47	15x30	0 430
P49	15x30	0 430
P51	25x25	0 430
P52	15x30	0 430
P53	15x30	0 430
P54	15x30	0 430
P55	15x30	0 430
P56	15x30	0 430
P57	15x30	0 430
P58	15x30	0 430
P59	15x30	0 430
P60	15x30	0 430

Legenda dos pilares	
	Pilar que morre

Forma do pavimento Platibanda
escala 1:50

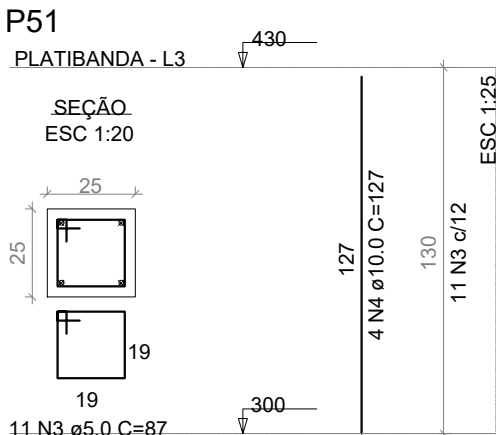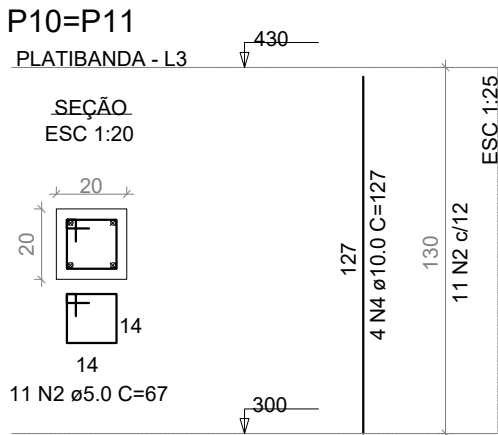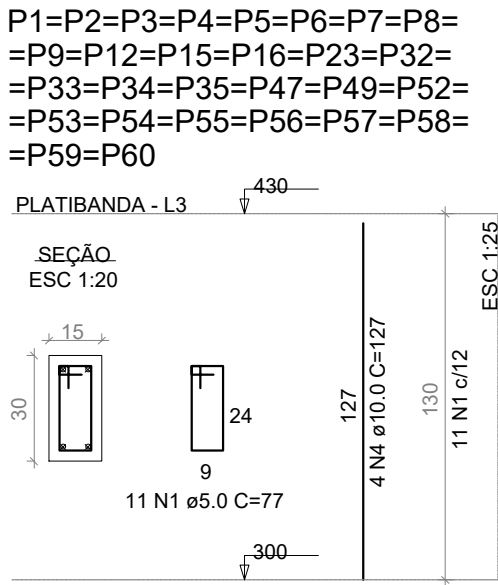

RELAÇÃO DO AÇO					
AÇO	N	DIAM (mm)	QUANT	C UNIT (cm)	C TOTAL (cm)
CA60	1	5.0	308	77	23716
CA60	2	5.0	22	67	1474
CA60	3	5.0	11	87	957
CA50	4	10.0	124	127	15748


RESUMO DO AÇO			
AÇO	DIAM (mm)	C TOTAL (m)	PESO + 0% (kg)
CA50	10.0	157.5	97.1
CA60	5.0	261.5	40.3
PESO TOTAL (kg)			
CA50		97.1	
CA60		40.3	

Volume de concreto (C-25) = 1.82 m³
Área de forma = 36.14 m²


PROPRIETÁRIO: PREFEITURA MUNICIPAL DE COREMAS

PROJETO: FERNANDO MATIAS MAMEDE CREA 162056275-8

FOLHA		PROJETO: CONSTRUÇÃO DE CRECHE COM CAPACIDADE PARA 50 CRIANÇAS			
13/14		CONVENIENTE:			
		CONVENIADO: PREFEITURA MUNICIPAL DE COREMAS			
		LOCALIDADE: MUNICÍPIO DE COREMAS - PB			
DESENHO	DATA ABRIL/2022	RESPONSÁVEL	RUBRICA	DADOS	
ESCALAS		DESENHOS			CONVÊNIO
INDICADO		- Pilares platibanda - Lista de Materiais - Legenda			
					ARQUIVO
Aprovações:					

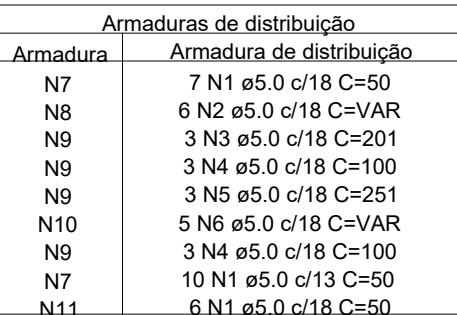

Aprovações:

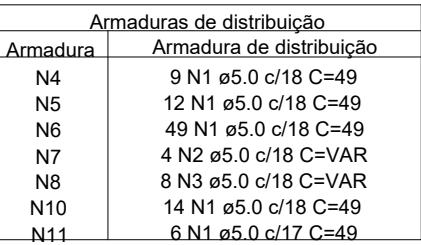


RELAÇÃO DO AÇO

Negativos X

AÇO	N	DIAM	QUANT C	UNIT C	TOTAL	
		(mm)			(cm)	(cm)
CA60	1	5.0		90	49	4410
	2	5.0		4	VAR	VAR
	3	5.0		8	VAR	VAR
CA50	4	10.0		3	165	495
	5	10.0		3	215	645
	6	10.0		3	380	2670
	7	10.0		3	VAR	VAR
	8	10.0		3	VAR	VAR
	9	10.0		2	365	730
	10	10.0		3	265	795
	11	10.0		6	114	684

AÇO	DIAM (mm)	C.TOTAL (m)	PESO + 0% (kg)
CA50	10.0	67.5	41.6
CA60	5.0	48.1	7.4
PESO TOTAL (kg)			
CA50	41.6		
CA60	7.4		

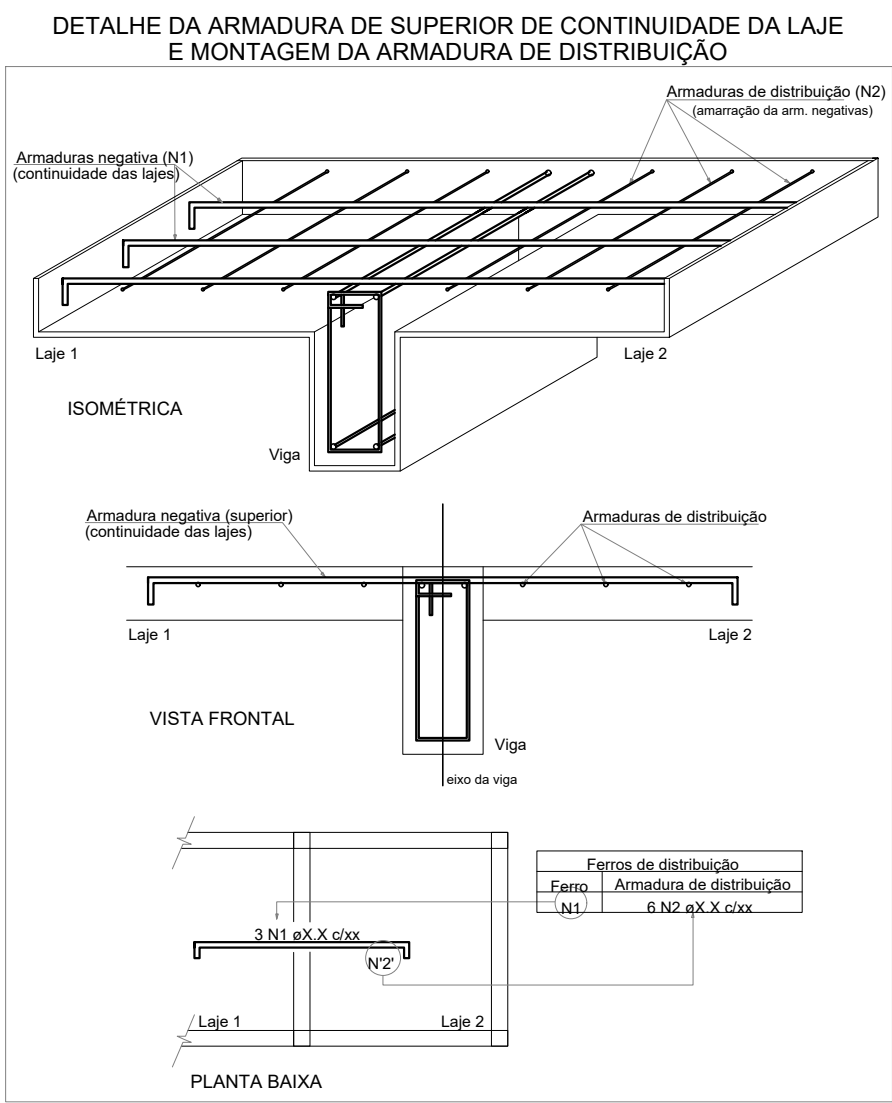


PROPRIETÁRIO: PREFEITURA MUNICIPAL DE COREMAS

PROJETO: FERNANDO MATIAS MAMEDE CREA 162056275-8

FOLHA	PROJETO: CONSTRUÇÃO DE CRECHE COM CAPACIDADE DE 50 CRIANÇAS		
11/14	CONVENIENTE:		
CONVENIADO: PREFEITURA MUNICIPAL DE COREMAS			
LOCALIDADE: MUNICÍPIO DE COREMAS - PB			
DESENHO	DATA	RESPONSÁVEL	RUBRICA
ABRIL/2022			
ESCALAS			CONVÊNIO
INDICADO - Lajes muiças - Lista de Materiais - Legenda			ARQUIVO

Aprovações

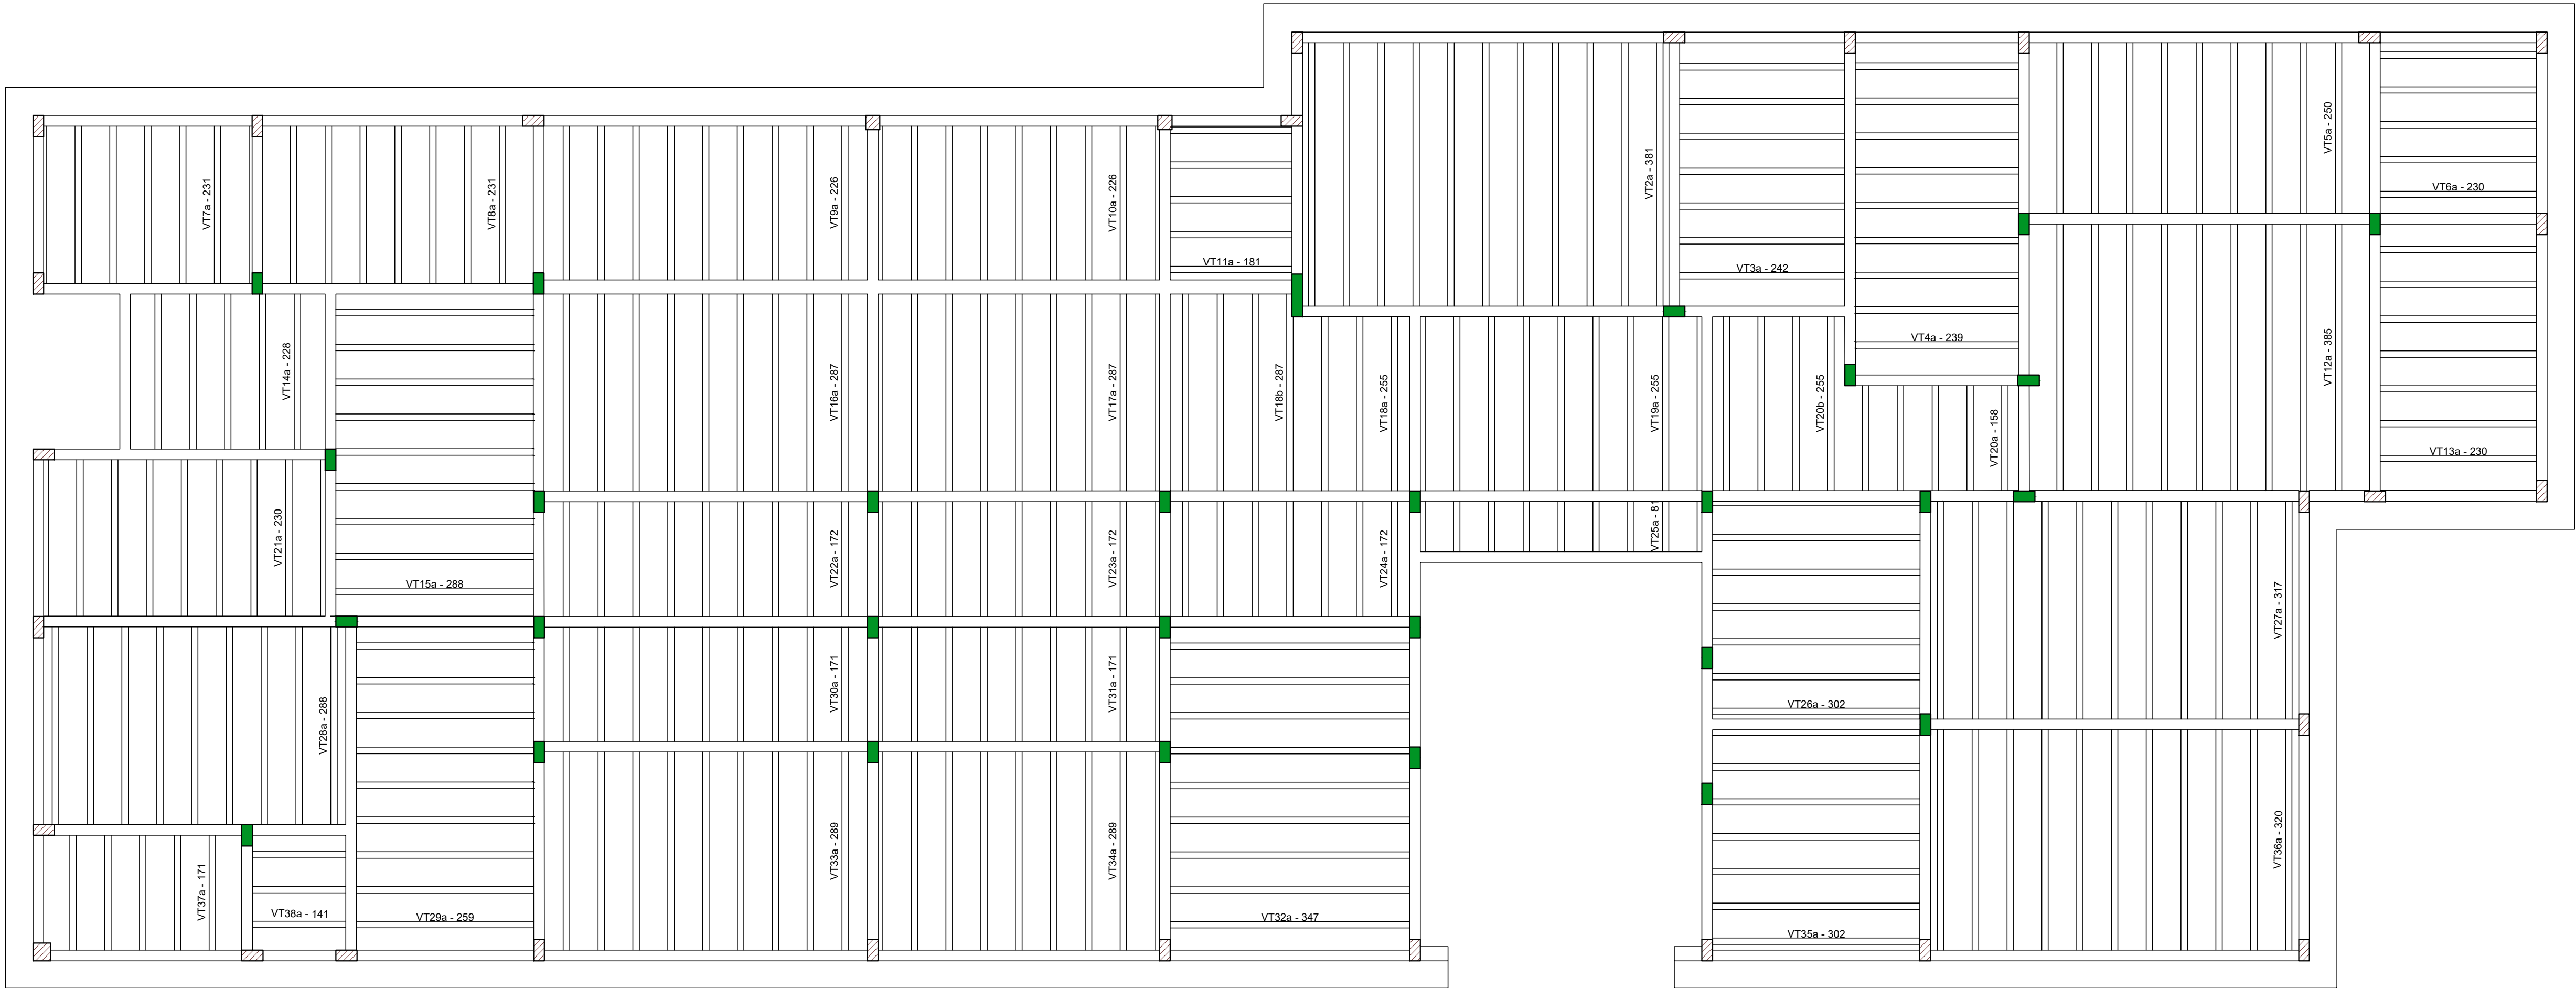


Planta de vigotas pré-moldadas
escala 1:50

RELAÇÃO DO AÇO				
1xVT2a	7xVT3a	9xVT4a		
9xVT5a	5xVT6a	5xVT7a		
7xVT8a	9xVT9a	7xVT10a		
5xVT11a	9xVT12a	7xVT13a		
9xVT14a	9xVT15a	9xVT16a		
7xVT17a	3xVT18a	4xVT18b		
7xVT19a	5xVT20a	4xVT20b		
7xVT21a	9xVT22a	7xVT23a		
7xVT24a	7xVT25a	6xVT26a		
1xVT27a	9xVT28a	9xVT29a		
9xVT30a	7xVT31a	9xVT32a		
9xVT33a	7xVT34a	6xVT35a		
1xVT36a	5xVT37a	3xVT38a		

AÇO	N	DIAM	(mm)	QUANT	C	UNIT	C	TOTAL	(cm)
CA60	1	TR 08646		11	387			4257	
	2	TR 08646		7	248			1736	
	3	TR 08646		9	245			2205	
	4	TR 08646		9	256			2304	
	5	TR 08646		12	236			2832	
	6	TR 08646		12	237			2844	
	7	TR 08646		16	232			3712	
	8	TR 08646		5	187			935	
	9	TR 08646		9	391			3519	
	10	TR 08646		5	234			1170	
	11	TR 08646		9	294			2646	
	12	TR 08646		9	493			2637	
	13	TR 08646		11	293			3223	
	14	TR 08646		3	261			783	
	15	TR 08646		11	261			2871	
	16	TR 08646		5	164			820	
	17	TR 08646		7	236			1652	
	18	TR 08646		9	178			1602	
	19	TR 08646		7	178			1246	
	20	TR 08646		7	178			1246	
	21	TR 08646		7	87			609	
	22	TR 08646		6	308			1848	
	23	TR 08646		11	323			3553	
	24	TR 08646		9	294			2646	
	25	TR 08646		9	295			2395	
	26	TR 08646		16	177			2832	
	27	TR 08646		9	353			3177	
	28	TR 08646		16	295			4720	
	29	TR 08646		6	308			1848	
	30	TR 08646		11	328			3586	
	31	TR 08646		5	177			885	
	32	TR 08646		3	147			441	
CA50	33		10,0	12	327			3924	

RESUMO DO AÇO			
AÇO	DIAM (mm)	C.TOTAL (m)	PESO + 0% (kg)
CA50	10,0	39,2	24,2
CA60	TR 08646	727,7	699,3
PESO TOTAL (kg)			
CA50	24,2		
CA60	699,3		

Volume de concreto (C-25) = 0.00 m³
Área da laje pré moldada = 395.11 m²

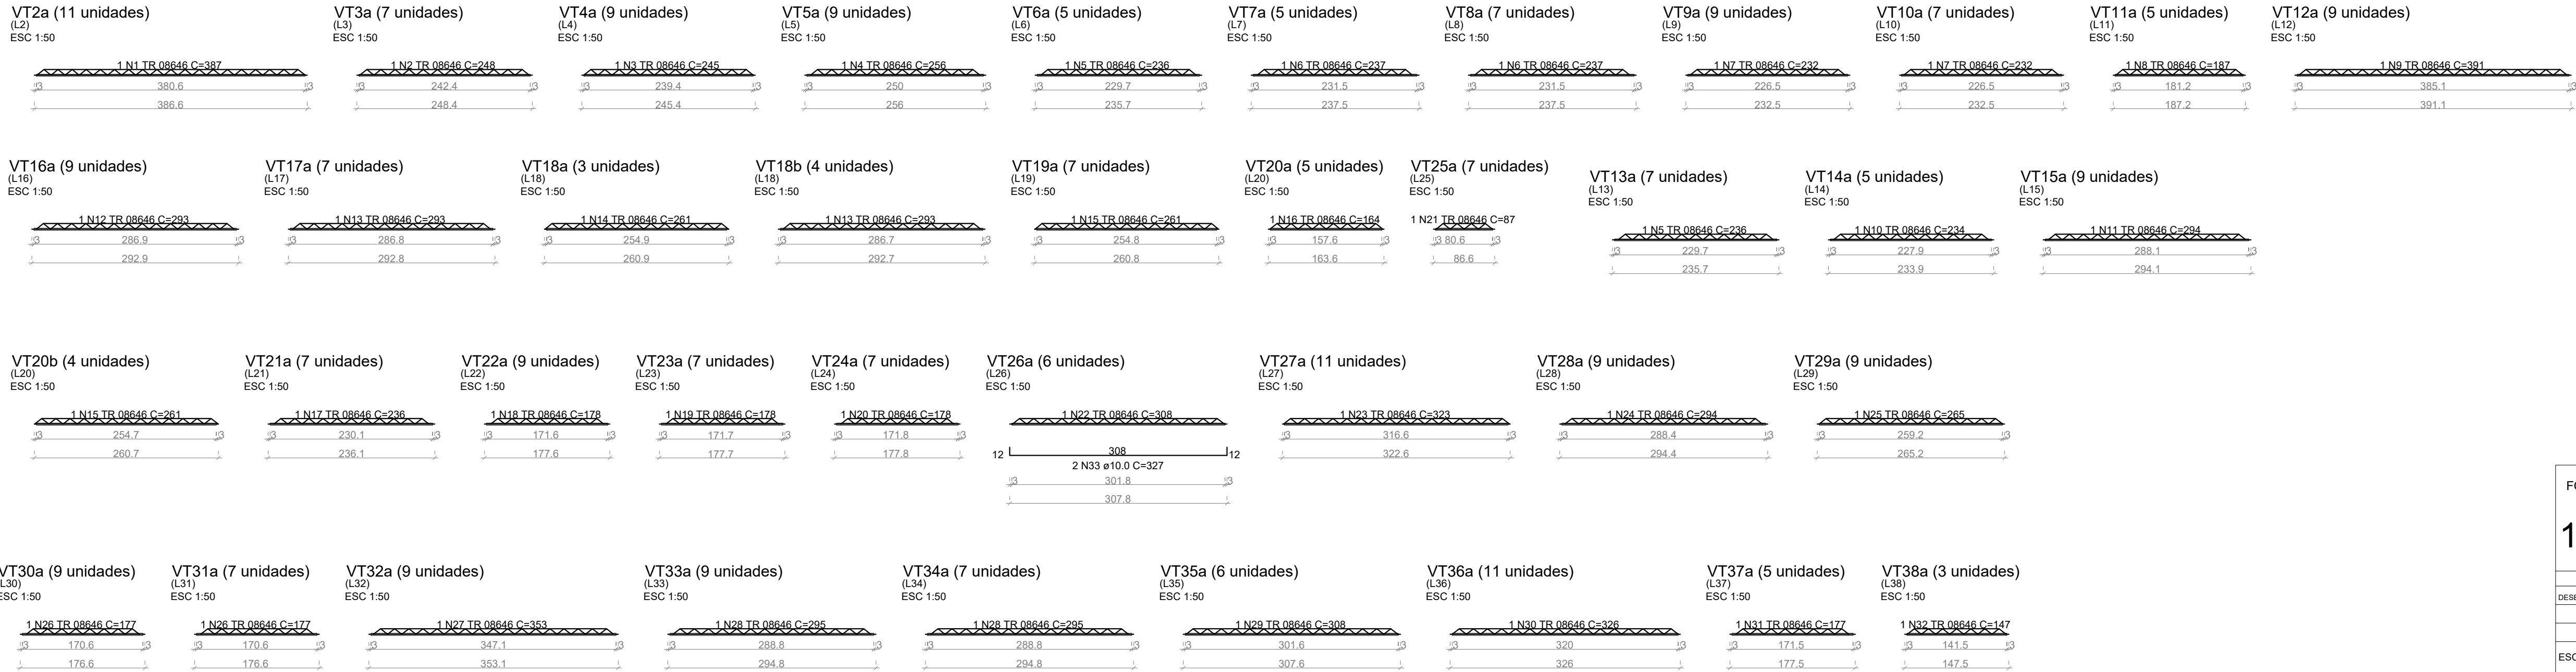

PROPRIETÁRIO: PREFEITURA MUNICIPAL DE COREMAS

PROJETO: FERNANDO MATIAS MAMEDE CREA 162056275-8

FOLHA

10/14

PROJETO: CONSTRUÇÃO DE CRECHE COM CAPACIDADE PARA 50 CRIANÇAS


CONVENIENTE:

CONVENIADO: PREFEITURA MUNICIPAL DE COREMAS


LOCALIDADE: MUNICÍPIO DE COREMAS - PB

DATA	RESPONSÁVEL	RUBRICA	DADOS
DESENHO	ABRIL/2022		
ESCALAS	DESENHOS		CONVÊNIO
INDICADO	- Lajes vigotas pré moldadas - Lista de Materiais - Legenda		
			ARQUIVO

Aprovações:

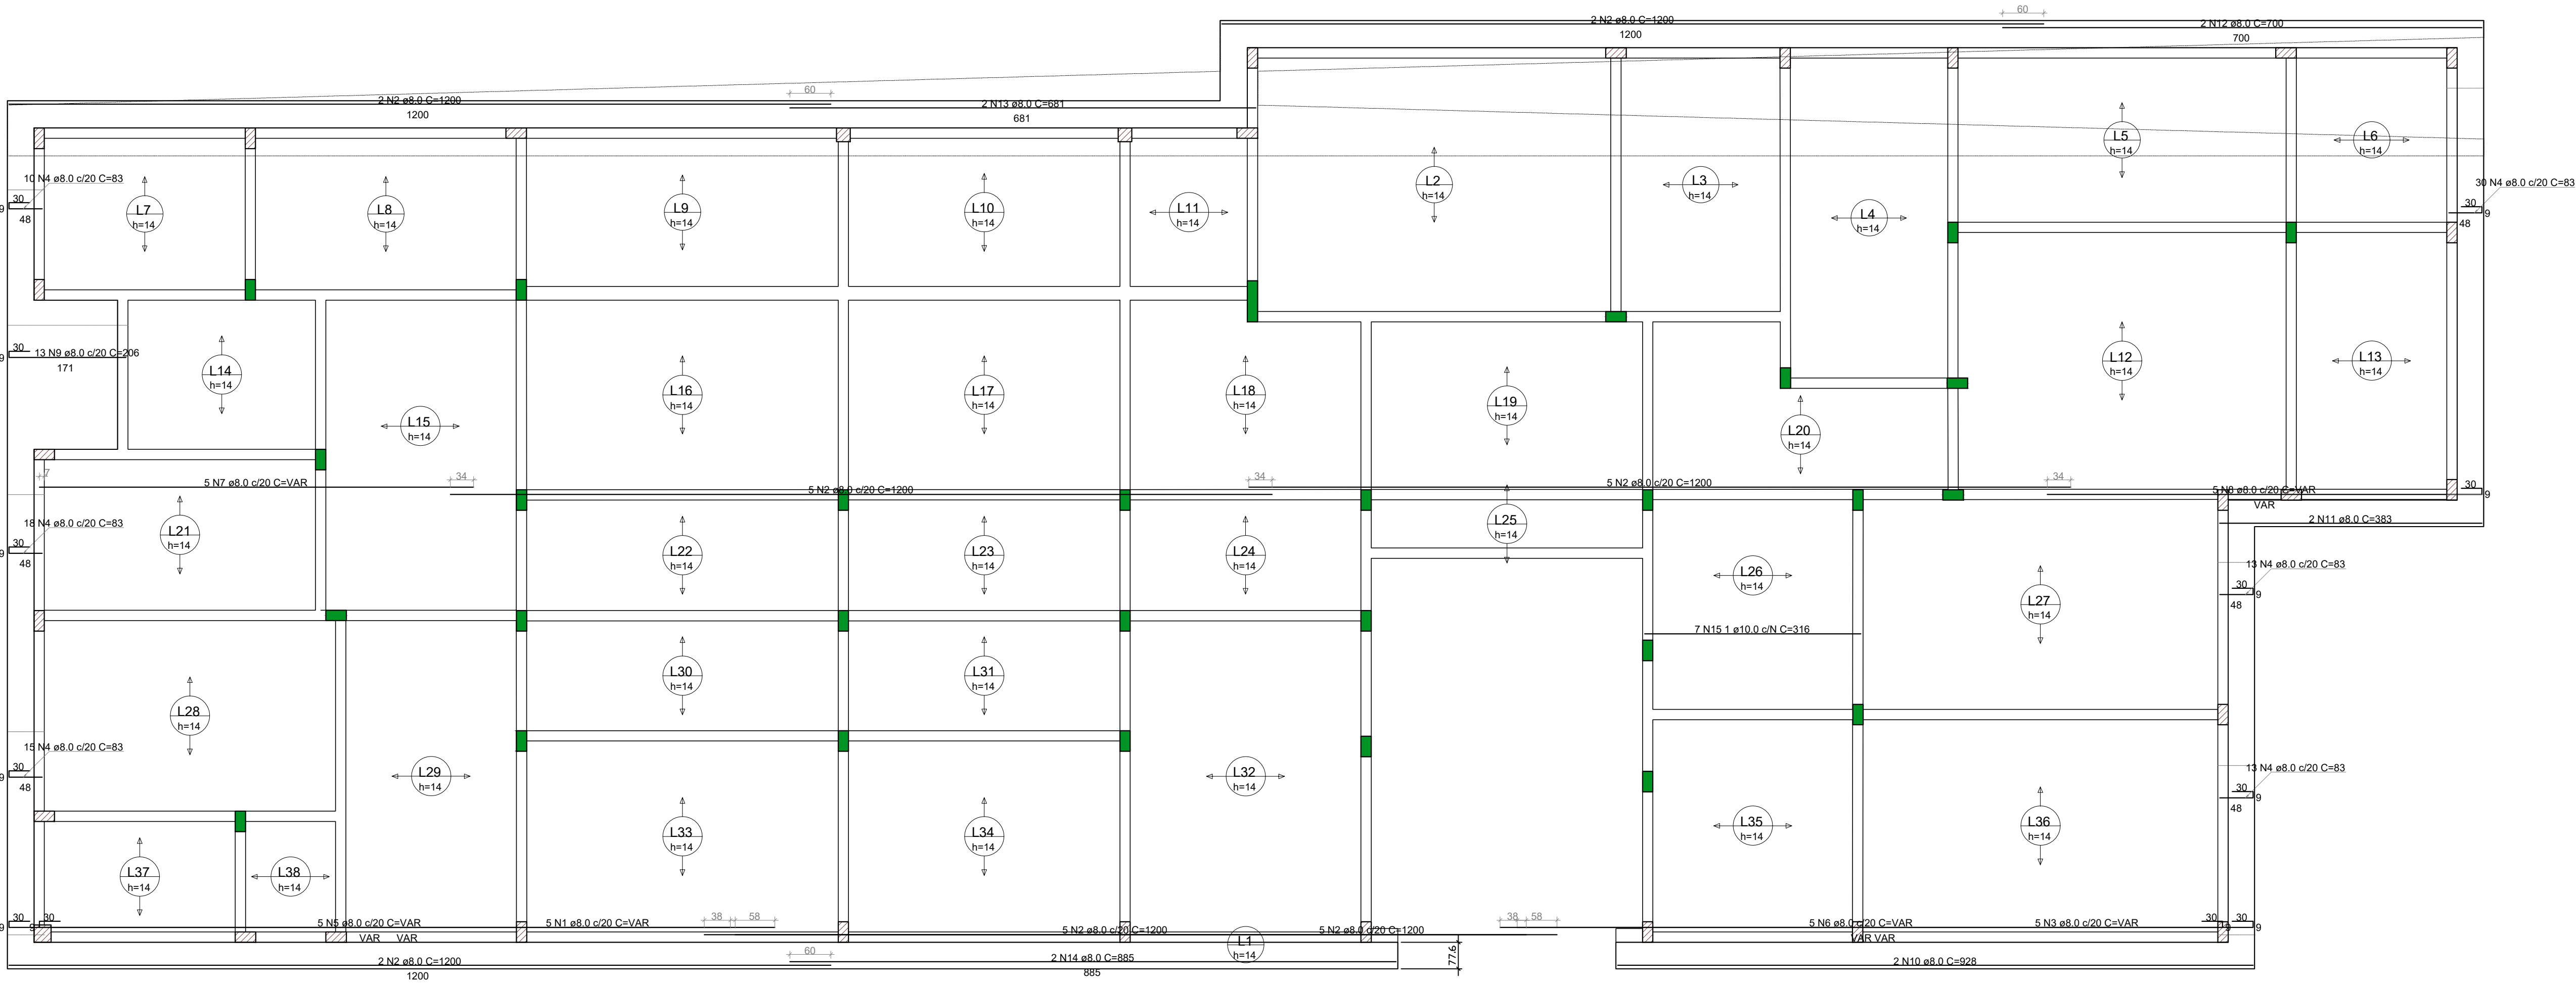

Armação positiva das lajes do pavimento Coberta (Eixo X)
escala 1:50

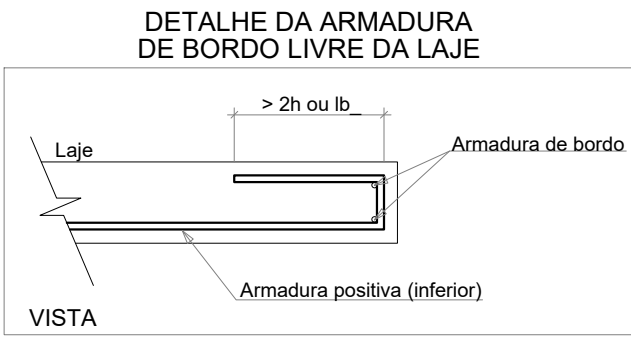

RELAÇÃO DO AÇO

Positivos X					
CA50	AÇO	N	DIAM (mm)	QUANT	C.UNIT C. TOTAL (cm) (cm)
1	8.0	5	VAR	VAR	VAR
2	8.0	26	1200	31200	31200
3	8.0	5	VAR	83	8217
4	8.0	99	VAR	83	8217
5	8.0	5	VAR	VAR	VAR
6	8.0	5	VAR	VAR	VAR
7	8.0	5	VAR	VAR	VAR
8	8.0	5	VAR	VAR	VAR
9	8.0	13	206	2678	2678
10	8.0	2	928	1856	1856
11	8.0	2	383	766	766
12	8.0	2	700	1400	1400
13	8.0	2	881	1762	1762
14	8.0	2	885	1770	1770
15	10.0	7	316	2212	2212

RESUMO DO AÇO

AÇO	DIAM (mm)	C.TOTAL (m)	PESO + 0% (kg)
CA50	8.0	777.5	306.8
CA50	10.0	22.1	13.8

PESO TOTAL (kg)
CA50.320.4

Volume de concreto da laje maciça (C-25) = 11.19 m³
Área de forma = 54.10 m²

PROPRIETÁRIO: PREFEITURA MUNICIPAL DE COREMAS

PROJETO: FERNANDO MATIAS MAMEDE CREA 162056275-8


FOLHA
08/14
PROJETO: CONSTRUÇÃO DE CRECHE COM CAPACIDADE PARA 50 CRIANÇAS
CONVENIENTE:
CONVENIADO: PREFEITURA MUNICIPAL DE COREMAS
LOCALIDADE: MUNICÍPIO DE COREMAS - PB

DESENHO	DATA	RESPONSÁVEL	RUBRICA	DADOS
ABRIL/2022				


ESCALAS	DESENHOS	CONVÊNIO
INDICADO	- Lajes maciças - Lista de Materiais - Legenda	ARQUIVO

Aprovações:


V39

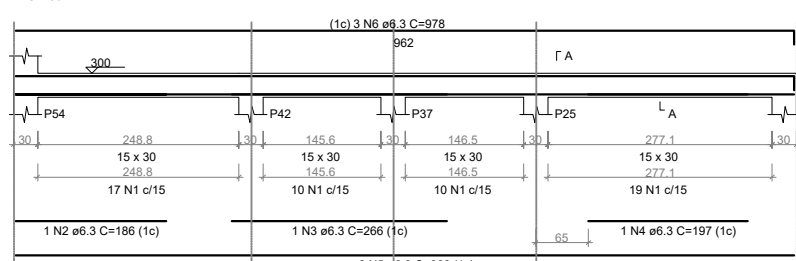


V40

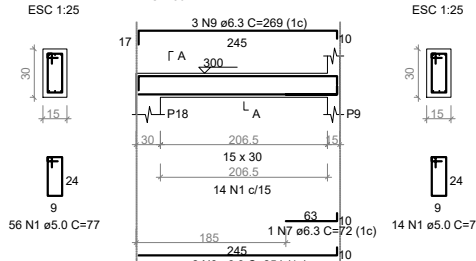


V41

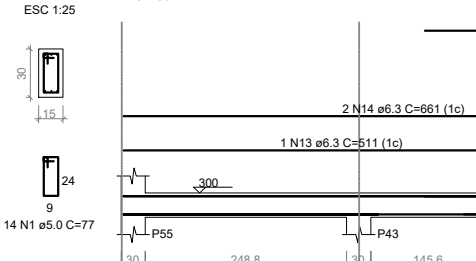


V42

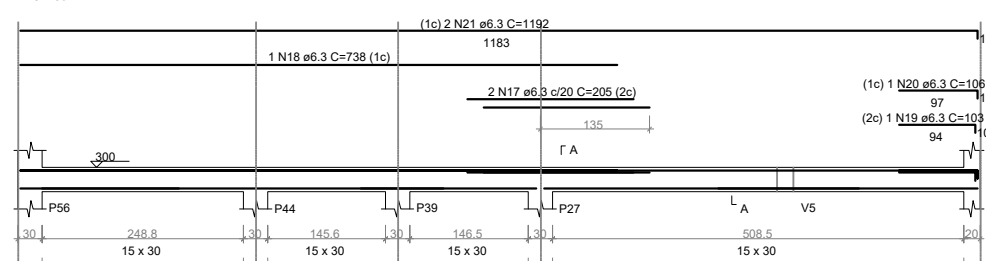


V43

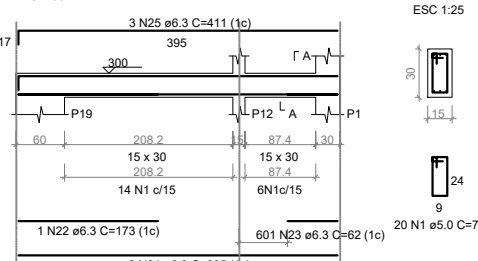


V44

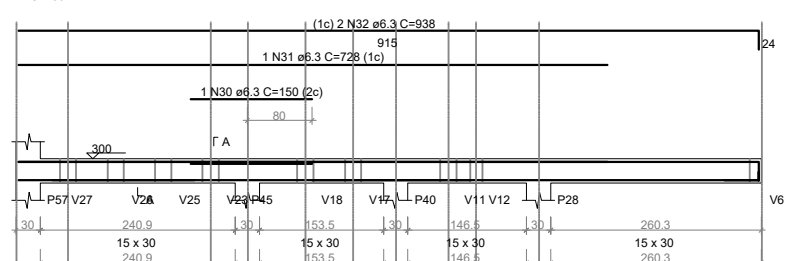


V46

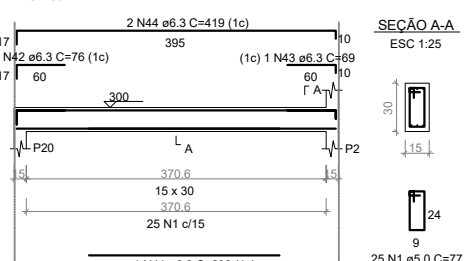


V45

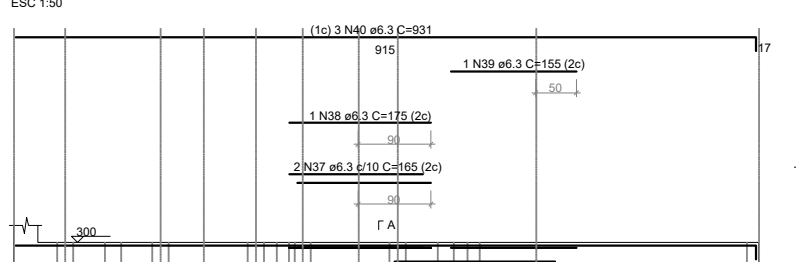


V47

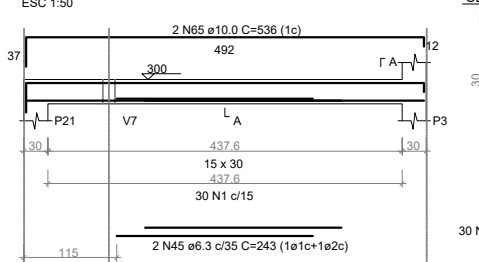


V48

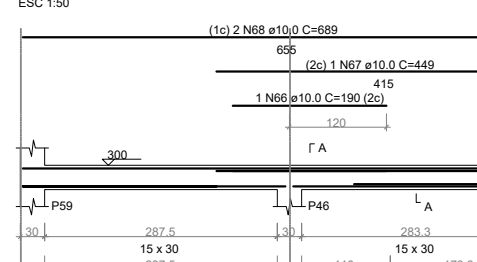


V50

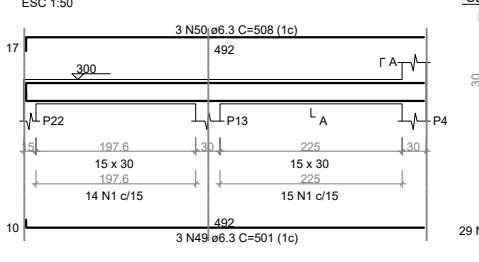


V51

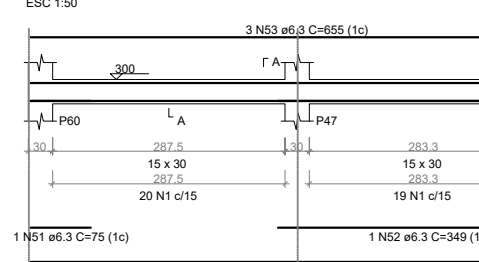


V52

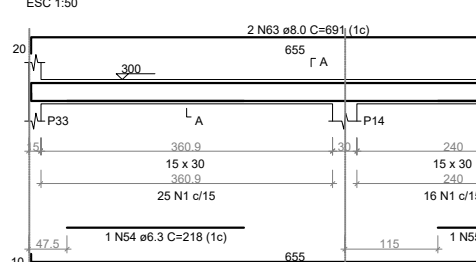


V53

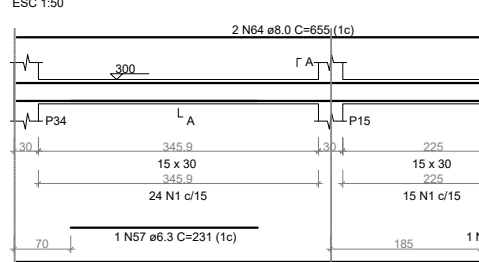


P1

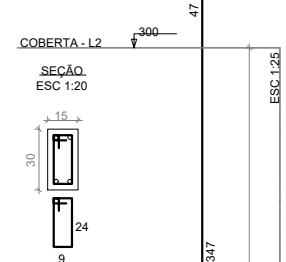


P10

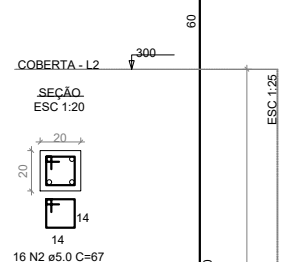


P11

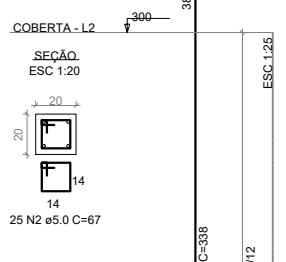


P13=P46

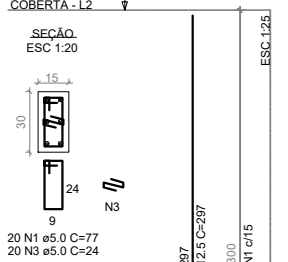


P14=P17=P20=P22=P24=

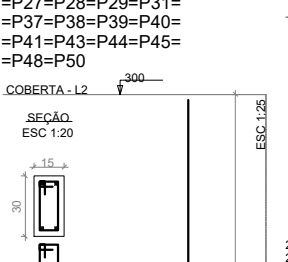


P18=P36=P42

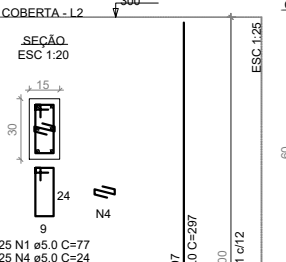


P19

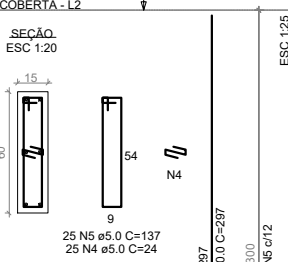


P2=P4=P5=P6=P7=P8=

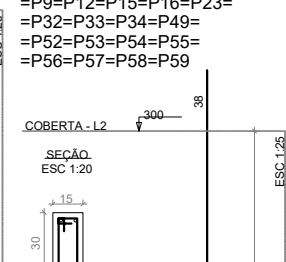


P21=P26=P30

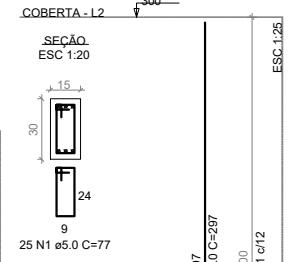


P25

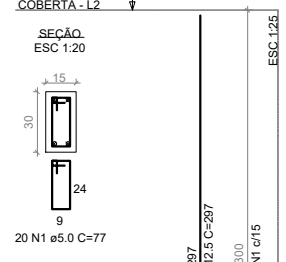


P3

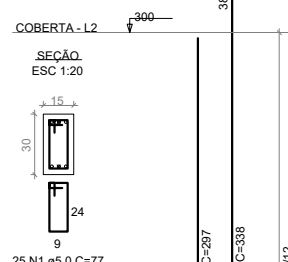


P35

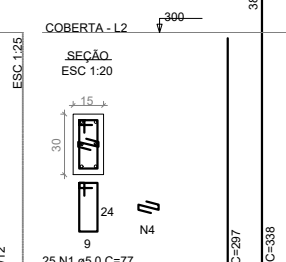


P47

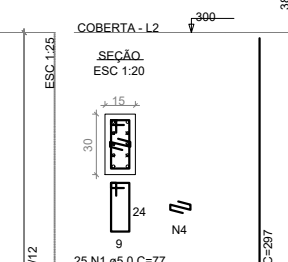

P51

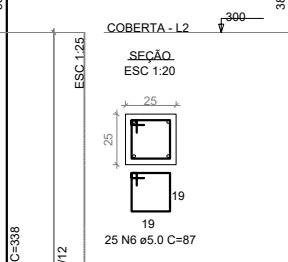

P60

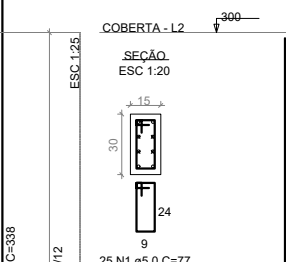

RELAÇÃO DO AÇO				
P1	23P2	P3		
P10	P11	P13		
P10P14	P1P18	P15		
P17P7	P21	P22		
AÇO BOMBAJUNT C/INT C TOTAL				
CAR	4	0,0	0,0	27
5	0,0	41	0,0	210
6	0,0	40	24	160
7	0,0	60	24	360
8	0,0	25	24	310
9	0,0	60	24	310
10	102	87	4	347
11	11	16,2	16,37	470
				1646

RESUMO DO AÇO			
ADO	DIAM	C TOTAL	PESO ± 0%
CAR	10,0	784,1	85,6
CAR	10,0	14,4	2,7
PESO TOTAL			188,7
CAR 99,3			
CAR 188,7			

Volume de concreto (C-35) = 8,26 m³
Área de forma = 163,50 m²

PROPRIETÁRIO: PREFEITURA MUNICIPAL DE COREMAS

PROJETO: FERNANDO MATIAS MAMDEI CREA 16206275-8

FOLHA 07/14

PROJETO: CONSTRUÇÃO DE CRECHE COM CAPACIDADE PARA 50 CRIANÇAS

CONVENIENTE: PREFEITURA MUNICIPAL DE COREMAS


LOCALIDADE: MUNICÍPIO DE COREMAS - PB

DATA: RESPOSTA: SUBSCRIÇÃO: DADOS:

ESCALAS: DESENHOS: CONVÊNIO:

INDICADO: - Vigas cobertas - Pilares - Lista de Materiais - Legenda ARQUIVO

Assinatura:

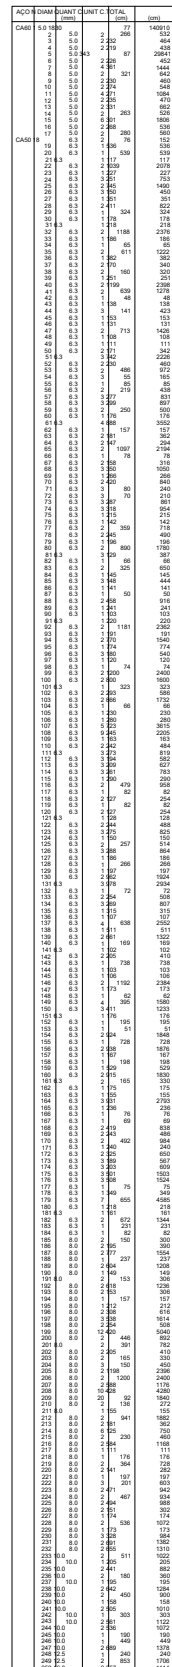



Vigas				Pilares			
Nome	Seção	Elevação (cm)	Nível (cm)	Nome	Seção	Elevação (cm)	Nível (cm)
V1	15x30	0.300	0.300	P1	15x30	0.300	0.300
V2	15x30	0.300	0.300	P2	15x30	0.300	0.300
V3	15x30	0.300	0.300	P3	15x30	0.300	0.300
V4	15x30	0.300	0.300	P4	15x30	0.300	0.300
V5	20x30	0.300	0.300	P5	15x30	0.300	0.300
V6	15x30	0.300	0.300	P6	15x30	0.300	0.300
V7	15x30	0.300	0.300	P7	15x30	0.300	0.300
V8	15x30	0.300	0.300	P8	15x30	0.300	0.300
V9	15x30	0.300	0.300	P9	15x30	0.300	0.300
V10	15x30	0.300	0.300	P10	20x20	0.300	0.300
V11	20x30	0.300	0.300	P11	20x20	0.300	0.300
V12	15x30	0.300	0.300	P12	15x30	0.300	0.300
V13	15x30	0.300	0.300	P13	15x30	0.300	0.300
V14	15x30	0.300	0.300	P14	15x30	0.300	0.300
V15	15x30	0.300	0.300	P15	15x30	0.300	0.300
V16	20x30	0.300	0.300	P16	15x30	0.300	0.300
V17	20x30	0.300	0.300	P17	15x30	0.300	0.300
V18	20x30	0.300	0.300	P18	15x30	0.300	0.300
V19	15x30	0.300	0.300	P19	15x30	0.300	0.300
V20	20x30	0.300	0.300	P20	15x30	0.300	0.300
V21	15x30	0.300	0.300	P21	15x30	0.300	0.300
V22	15x30	0.300	0.300	P22	15x30	0.300	0.300
V23	20x30	0.300	0.300	P23	15x30	0.300	0.300
V24	15x30	0.300	0.300	P24	15x30	0.300	0.300
V25	20x30	0.300	0.300	P25	15x30	0.300	0.300
V26	20x30	0.300	0.300	P26	15x30	0.300	0.300
V27	20x30	0.300	0.300	P27	15x30	0.300	0.300
V28	15x30	0.300	0.300	P28	15x30	0.300	0.300
V29	20x30	0.300	0.300	P29	15x30	0.300	0.300
V30	15x30	0.300	0.300	P30	15x30	0.300	0.300
V31	15x30	0.300	0.300	P31	15x30	0.300	0.300
V32	15x30	0.300	0.300	P32	15x30	0.300	0.300
V33	15x30	0.300	0.300	P33	15x30	0.300	0.300
V34	15x30	0.300	0.300	P34	15x30	0.300	0.300
V35	15x30	0.300	0.300	P35	15x30	0.300	0.300
V36	15x30	0.300	0.300	P36	15x30	0.300	0.300
V37	15x30	0.300	0.300	P37	15x30	0.300	0.300
V38	15x30	0.300	0.300	P38	15x30	0.300	0.300
V39	15x30	0.300	0.300	P39	15x30	0.300	0.300
V40	15x30	0.300	0.300	P40	15x30	0.300	0.300
V41	15x30	0.300	0.300	P41	15x30	0.300	0.300
V42	15x30	0.300	0.300	P42	15x30	0.300	0.300
V43	15x30	0.300	0.300	P43	15x30	0.300	0.300
V44	15x30	0.300	0.300	P44	15x30	0.300	0.300
V45	15x30	0.300	0.300	P45	15x30	0.300	0.300
V46	15x30	0.300	0.300	P46	15x30	0.300	0.300
V47	15x30	0.300	0.300	P47	15x30	0.300	0.300
V48	15x30	0.300	0.300	P48	15x30	0.300	0.300
V49	15x30	0.300	0.300	P49	15x30	0.300	0.300
V50	15x30	0.300	0.300	P50	15x30	0.300	0.300
V51	15x30	0.300	0.300	P51	25x25	0.300	0.300
V52	15x30	0.300	0.300	P52	15x30	0.300	0.300
V53	15x30	0.300	0.300	P53	15x30	0.300	0.300
V54	15x30	0.300	0.300	P54	15x30	0.300	0.300
V55	15x30	0.300	0.300	P55	15x30	0.300	0.300
V56	15x30	0.300	0.300	P56	15x30	0.300	0.300
V57	15x30	0.300	0.300	P57	15x30	0.300	0.300
V58	15x30	0.300	0.300	P58	15x30	0.300	0.300
V59	15x30	0.300	0.300	P59	15x30	0.300	0.300
V60	15x30	0.300	0.300	P60	15x30	0.300	0.300


Forma do pavimento Coberta (Nível 300)
escala 1:50

Lajes					Sobrecarga (kgf/m²)		
Nome	Tipo	Altura (cm)	Elevação (cm)	Nível (cm)	Peso próprio (kgf/m²)	Adicional	Apresentada Localizada
L1	Maciça	14	0.300	350	50	50	-
L2	Trelçada 1D	14	0.300	148	50	50	-
L3	Trelçada 1D	14	0.300	148	50	50	-
L4	Trelçada 1D	14	0.300	148	50	50	-
L5	Trelçada 1D	14	0.300	148	50	50	-
L6	Trelçada 1D	14	0.300	148	50	50	-
L7	Trelçada 1D	14	0.300	148	50	50	-
L8	Trelçada 1D	14	0.300	148	50	50	-
L9	Trelçada 1D	14	0.300	148	50	50	-
L10	Trelçada 1D	14	0.300	148	50	50	-
L11	Trelçada 1D	14	0.300	148	50	50	-
L12	Trelçada 1D	14	0.300	148	50	50	-
L13	Trelçada 1D	14	0.300	148	50	50	-
L14	Trelçada 1D	14	0.300	148	50	50	-
L15	Trelçada 1D	14	0.300	148	50	50	-
L16	Trelçada 1D	14	0.300	148	50	50	-
L17	Trelçada 1D	14	0.300	148	50	50	-
L18	Trelçada 1D	14	0.300	148	50	50	-
L19	Trelçada 1D	14	0.300	148	50	50	-
L20	Trelçada 1D	14	0.300	148	50	50	-
L21	Trelçada 1D	14	0.300	148	50	50	-
L22	Trelçada 1D	14	0.300	148	50	50	-
L23	Trelçada 1D	14	0.300	148	50	50	-
L24	Trelçada 1D	14	0.300	148	50	50	-
L25	Trelçada 1D	14	0.300	148	50	50	-
L26	Trelçada 1D	14	0.300	148	50	1630	-
L27	Trelçada 1D	14	0.300	148	50	50	-
L28	Trelçada 1D	14	0.300	148	50	50	-
L29	Trelçada 1D	14	0.300	148	50	50	-
L30	Trelçada 1D	14	0.300	148	50	50	-
L31	Trelçada 1D	14	0.300	148	50	50	-
L32	Trelçada 1D	14	0.300	148	50	50	-
L33	Trelçada 1D	14	0.300	148	50	50	-
L34	Trelçada 1D	14	0.300	148	50	50	-
L35	Trelçada 1D	14	0.300	148	50	50	-
L36	Trelçada 1D	14	0.300	148	50	50	-
L37	Trelçada 1D	14	0.300	148	50	50	-
L38	Trelçada 1D	14	0.300	148	50	50	-

Blocos de enchimento				
Detalhe	Tipo	Nome	Dimensões (cm)	Quantidade
1	EPS Unidirecional	B10/40/48	10.40.48	1598

Legenda dos pilares		Legenda das vigas e paredes	
	Pilar que morre		Viga
	Pilar que passa		

Características dos materiais	
fck	Ecs
(kgf/cm²)	(kgf/cm²)
250	241500

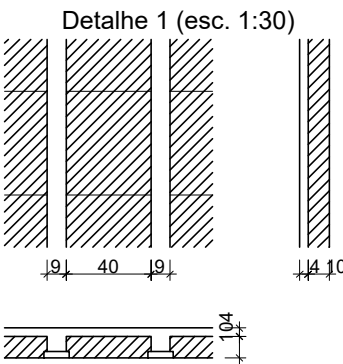

PROPRIETÁRIO: PREFEITURA MUNICIPAL DE COREMAS

PROJETO: FERNANDO MATIAS MAMEDE CREA 162056275-8


FOLHA		PROJETO: CONSTRUÇÃO DE CRECHE COM CAPACIDADE PARA 50 CRIANÇAS		
05/11	CONVENIENTE:			
	CONVENIADO: PREFEITURA MUNICIPAL DE COREMAS			
	LOCALIDADE: MUNICÍPIO DE COREMAS - PB			
	DATA	RESPONSÁVEL	RUBRICA	DADOS
DESENHO	ABRIL/2022			
ESCALAS		DESENHOS		CONVÊNIO
INDICADO	- Forma Coberta - Lista de Materiais - Legenda			
			ARQUIVO	






RELACIONAMENTO					TOTAL	
ITEM	QUANTIDADE	UNIDADE	VALOR	VALOR	VALOR	VALOR
1	1	m	1,00	1,00	1,00	1,00
2	1	m	1,00	1,00	1,00	1,00
PROPRIETÁRIO: PREFEITURA MUNICIPAL DE COREMAS	
PROJETO: FERNANDO MATIAS MAMEDI CREA 16205275-B	
FOLHA 04/14	
CONVENIENTE: PREFEITURA MUNICIPAL DE COREMAS	
LOCALIDADE: MUNICÍPIO DE COREMAS - PB	
DATA: 10/05/2024	RUBRICA: DADOR
RESPONSÁVEL: [Assinatura]	
ESCALAS: [Escala]	CONVÊNIO: [Convênio]
INDICADO: [Indicador]	ARQUIVO: [Arquivo]

ACQ	DAM	C	TOTAL	RESQ	%
1	1	1	1	1	100
2	1	1	1	1	100
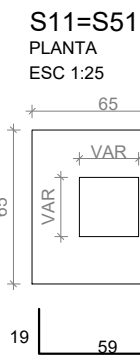


Solo com capacidade de suporte > 1.50 kgf/cm²
Solo compactado sobre a sapata
peso específico > 1600.00 kg/m³

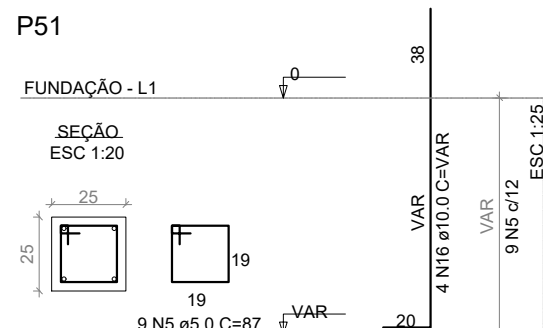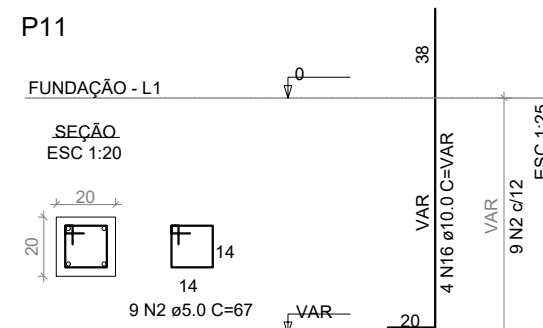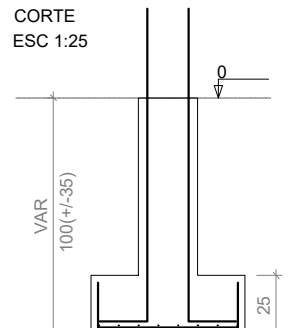

S1=S2=S3=S4=S5=S6=S7=S8=S9=S12=S13=S15
=S16=S17=S21=S22=S23=S24=S25=S28=S31
=S32=S33=S34=S35=S36=S37=S38=S39=S40
=S42=S43=S44=S45=S47=S48=S49=S50=S52
=S53=S54=S55=S56=S57=S58=S59=S60

Solo com capacidade de suporte > 1.50 kgf/cm²
Solo compactado sobre a sapata
peso específico > 1600.00 kg/m³

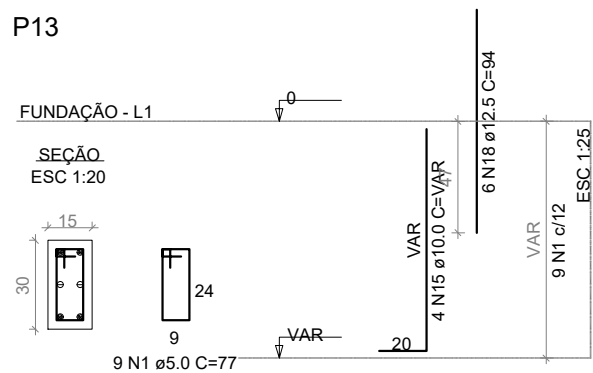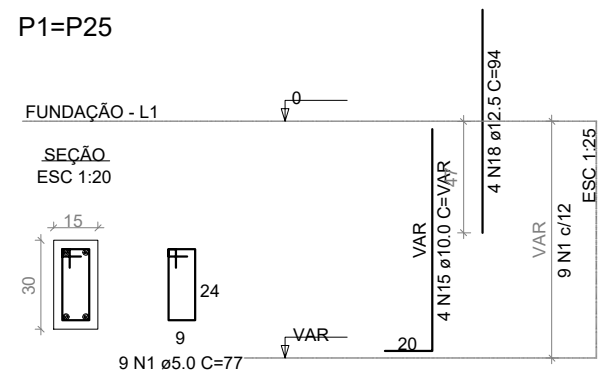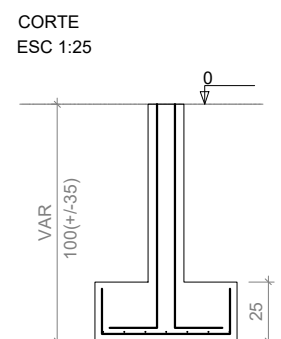

RELAÇÃO DO AÇO






















ACO	N	DIAM	QUANT	CL	UNIT	C.TOTAL	(cm)
CA60	1	5.0	504			77	38808
	2	5.0	18			67	1206
	3	5.0	9			24	216
	4	5.0	9			137	1233
	5	5.0	9			87	783
CA50	6	6.3	347			104	37647
	7	6.3	12			84	1008
	8	6.3	17			129	2193
	9	6.3	38			109	3204
	10	6.3	30			124	3720
	11	6.3	50			99	4950
	12	6.3	52			114	5928
	13	6.3	32			94	3008
	14	6.3	20			VAR	VAR
	15	10.0	222			VAR	VAR
	16	10.0	22			26	75
	17	10.0	20			94	1880
	18	12.5	20			121	2591
	19	16.0	4			121	484

RESUMO DO AÇO

ACO	DIAM	C.TOTAL	PESO + 0%
CA50	6.3	984.7	241
	10.0	381.6	235.2
	12.5	18.8	15.1
	16.0	4.8	7.6
CA60	5.0	422.5	65.1

PESO TOTAL (kg)
CA50 501.9
CA60 65.1
Volume de concreto (C-25) = 10.06 m³
Área de forma = 96.48 m²


P2=P4=P5=P6=P7=P8=P9=P12=
=P15=P16=P17=P22=P23=P24=
=P28=P31=P32=P33=P34=P37=
=P38=P39=P40=P43=P44=P45=
=P48=P49=P50=P52=P53=P54=
=P56=P57=P58=P59

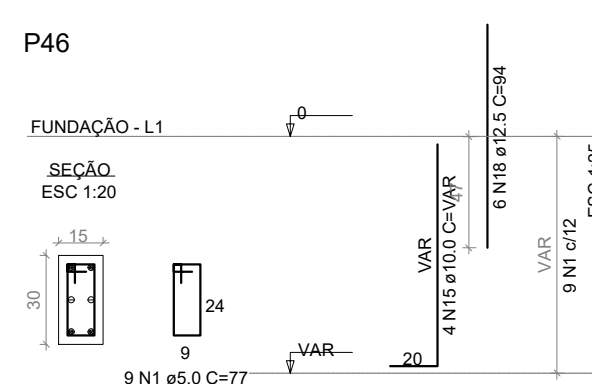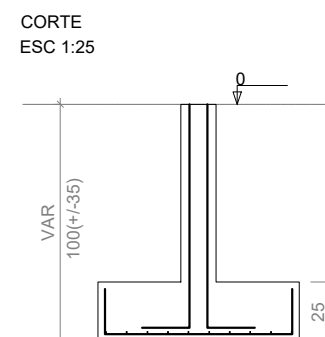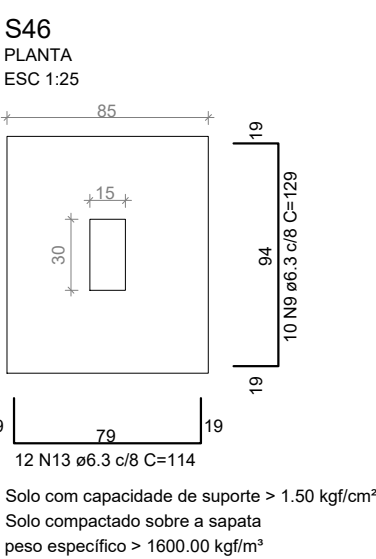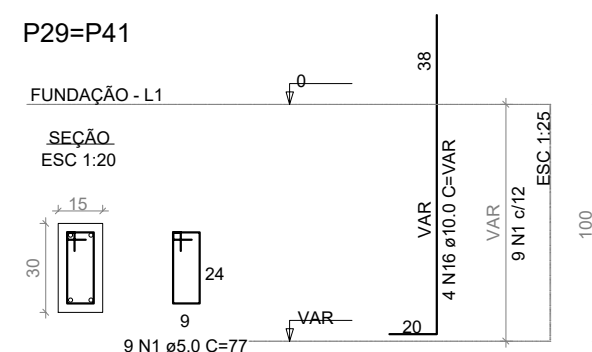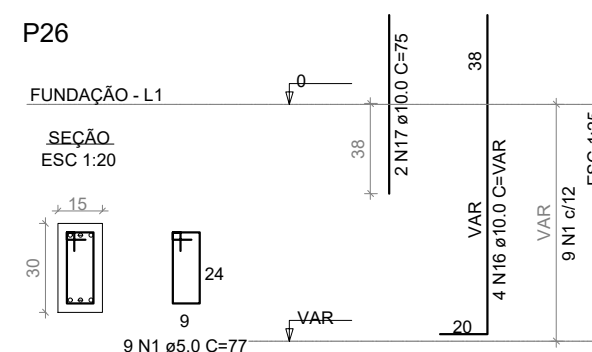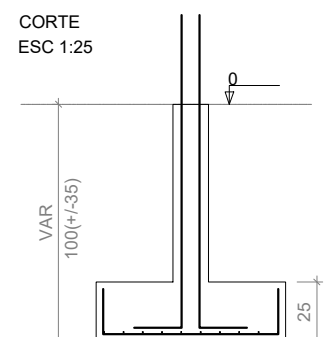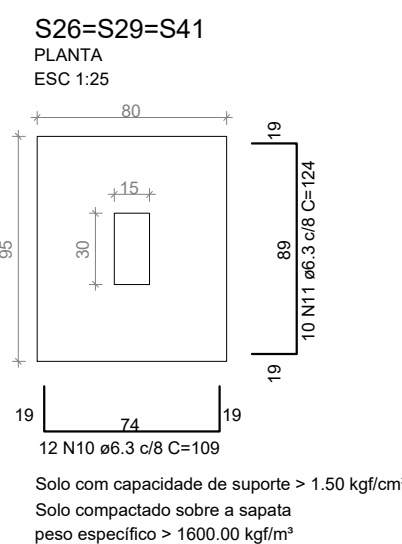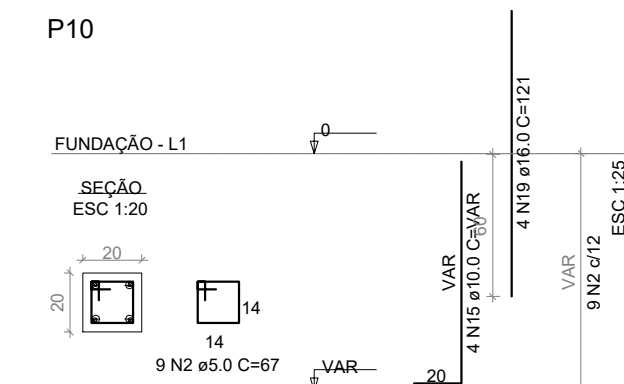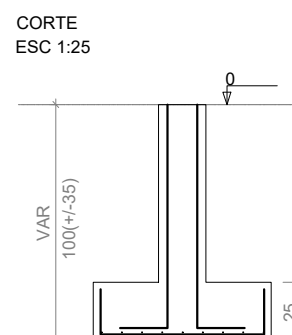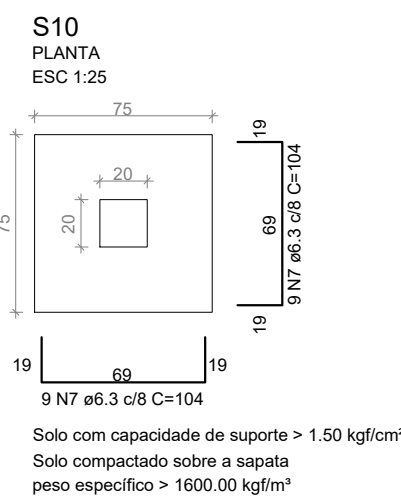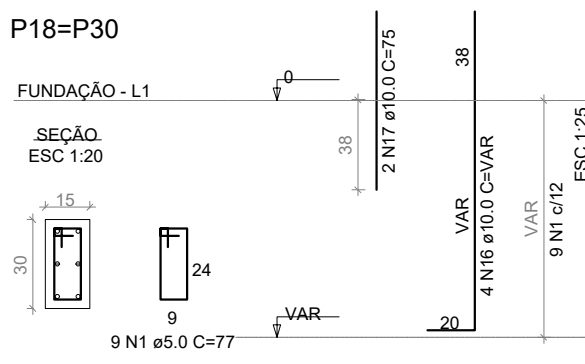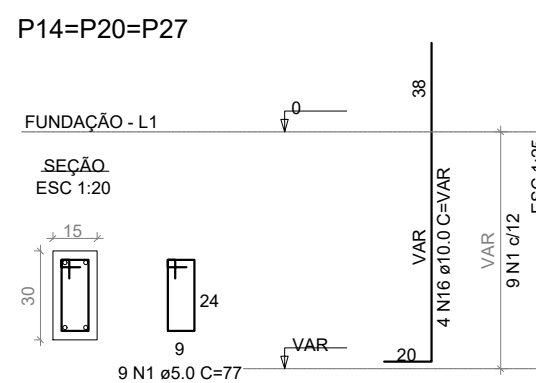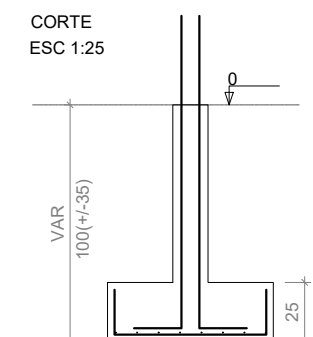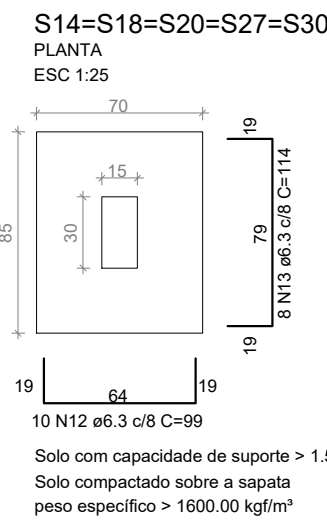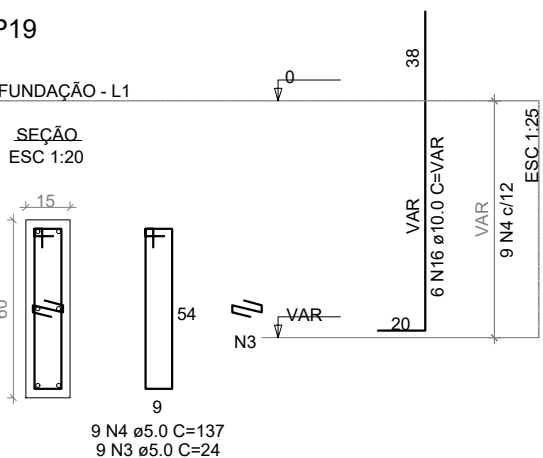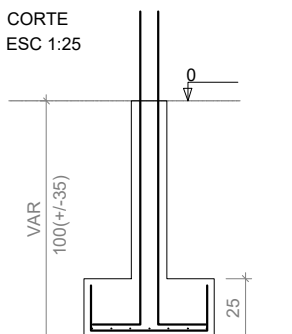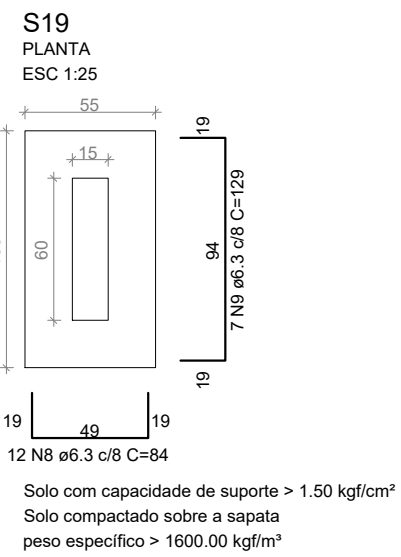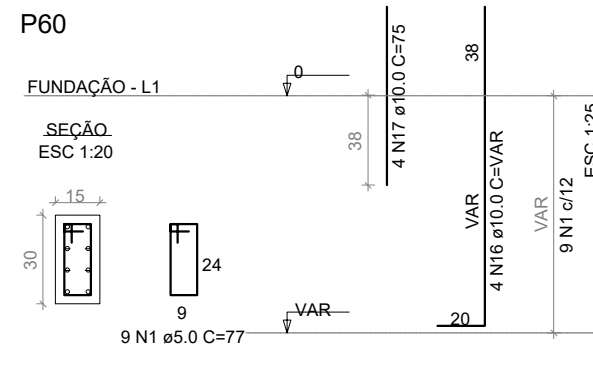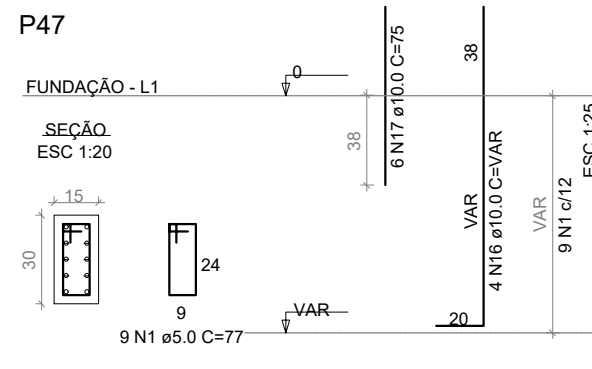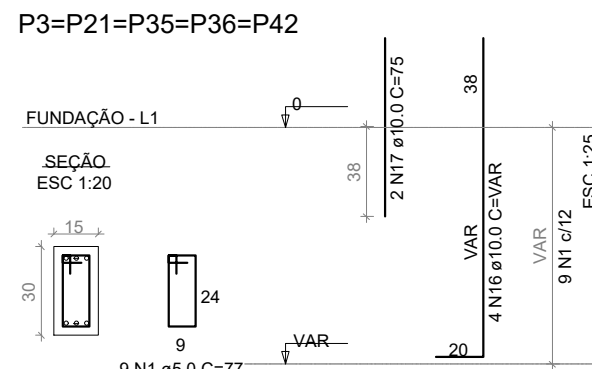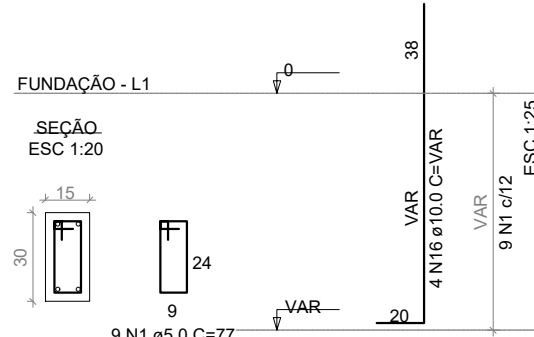

PROPRIETÁRIO: PREFEITURA MUNICIPAL DE COREMAS

PROJETO: FERNANDO MATIAS MAMEDE CREA 162056275-8

FOLHA		PROJETO: CONSTRUÇÃO DE CRECHE COM CAPACIDADE DE 50 CRIANÇAS			
03/14		CONVENIENTE: PREFEITURA MUNICIPAL DE COREMAS			
		LOCALIDADE: MUNICÍPIO DE COREMAS - PB			
	DATA	RESPONSÁVEL	RUBRICA	DADOS	
DESENHO	ABRIL/2022				
ESCALAS		DESENHOS			CONVÊNIO
INDICADO		- Fundações			
		- Lista de Materiais			
		- Legenda			
					ARQUIVO
Aprovações:					

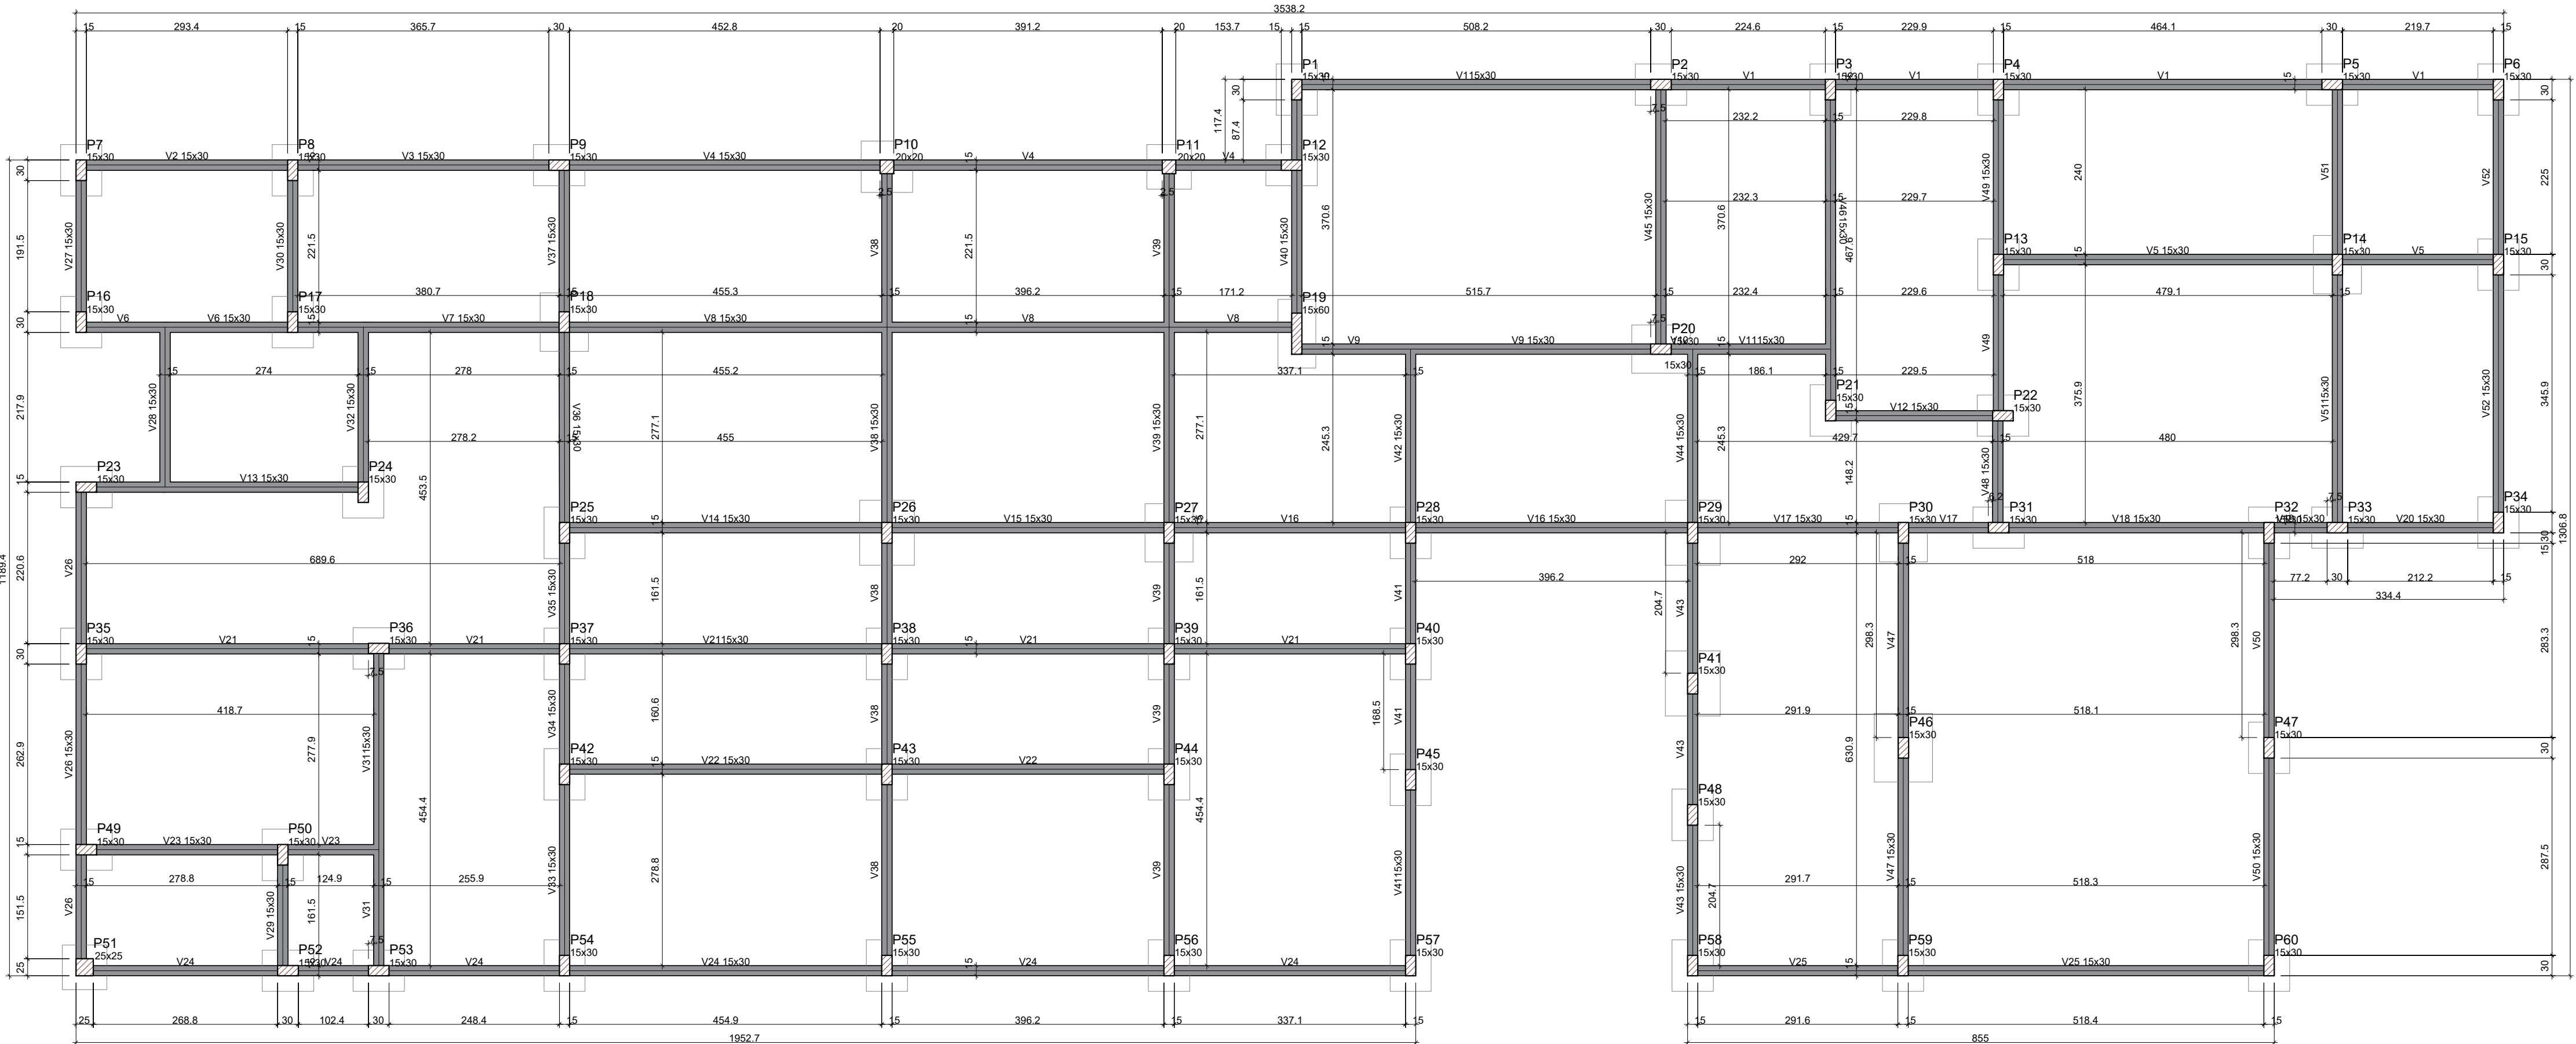

Forma do pavimento Fundação (Nível 0)
escala 1:50

Vigas			
Nome	Seção	Elevação (cm)	Nível (cm)
V1	15x30	0	0
V2	15x30	0	0
V3	15x30	0	0
V4	15x30	0	0
V5	15x30	0	0
V6	15x30	0	0
V7	15x30	0	0
V8	15x30	0	0
V9	15x30	0	0
V10	15x30	0	0
V11	15x30	0	0
V12	15x30	0	0
V13	15x30	0	0
V14	15x30	0	0
V15	15x30	0	0
V16	15x30	0	0
V17	15x30	0	0
V18	15x30	0	0
V19	15x30	0	0
V20	15x30	0	0
V21	15x30	0	0
V22	15x30	0	0
V23	15x30	0	0
V24	15x30	0	0
V25	15x30	0	0
V26	15x30	0	0
V27	15x30	0	0
V28	15x30	0	0
V29	15x30	0	0
V30	15x30	0	0
V31	15x30	0	0
V32	15x30	0	0
V33	15x30	0	0
V34	15x30	0	0
V35	15x30	0	0
V36	15x30	0	0
V37	15x30	0	0
V38	15x30	0	0
V39	15x30	0	0
V40	15x30	0	0
V41	15x30	0	0
V42	15x30	0	0
V43	15x30	0	0
V44	15x30	0	0
V45	15x30	0	0
V46	15x30	0	0
V47	15x30	0	0
V48	15x30	0	0
V49	15x30	0	0
V50	15x30	0	0
V51	15x30	0	0
V52	15x30	0	0

Características das materiais			
fck	Ecs		
(kgf/cm²)	(kgf/cm²)		
250	241500		

Legenda dos pilares	
	Pilar que passa


Legenda das vigas e paredes	
	Viga

Pilares			
Nome	Seção	Elevação (cm)	Nível (cm)
P1	15x30	0	0
P2	15x30	0	0
P3	15x30	0	0
P4	15x30	0	0
P5	15x30	0	0
P6	15x30	0	0
P7	15x30	0	0
P8	15x30	0	0
P9	15x30	0	0
P10	20x20	0	0
P11	20x20	0	0
P12	15x30	0	0
P13	15x30	0	0
P14	15x30	0	0
P15	15x30	0	0
P16	15x30	0	0
P17	15x30	0	0
P18	15x30	0	0
P19	15x30	0	0
P20	15x30	0	0
P21	15x30	0	0
P22	15x30	0	0
P23	15x30	0	0
P24	15x30	0	0
P25	15x30	0	0
P26	15x30	0	0
P27	15x30	0	0
P28	15x30	0	0
P29	15x30	0	0
P30	15x30	0	0
P31	15x30	0	0
P32	15x30	0	0
P33	15x30	0	0
P34	15x30	0	0
P35	15x30	0	0
P36	15x30	0	0
P37	15x30	0	0
P38	15x30	0	0
P39	15x30	0	0
P40	15x30	0	0
P41	15x30	0	0
P42	15x30	0	0
P43	15x30	0	0
P44	15x30	0	0
P45	15x30	0	0
P46	15x30	0	0
P47	15x30	0	0
P48	15x30	0	0
P49	15x30	0	0
P50	15x30	0	0
P51	15x30	0	0
P52	15x30	0	0
P53	15x30	0	0
P54	15x30	0	0
P55	15x30	0	0
P56	15x30	0	0
P57	15x30	0	0
P58	15x30	0	0
P59	15x30	0	0
P60	15x30	0	0

PROPRIETÁRIO: PREFEITURA MUNICIPAL DE COREMAS

PROJETO: FERNANDO MATIAS MAMEDE CREA 162056275-8


FOLHA	PROJETO: CONSTRUÇÃO DE CRECHE COM CAPACIDADE DE 50 CRIANÇAS		
02/14	CONVENIENTE: PREFEITURA MUNICIPAL DE COREMAS		
	LOCALIDADE: MUNICÍPIO DE COREMAS - PB		
DATA	RESPONSÁVEL	RUBRICA	DADOS
DESENHO	ABRIL/2022		
ESCALAS	DESENHOS		CONVÊNIO
INDICADO	- Forma baldrame		
			ARQUIVO
Aprovações:			


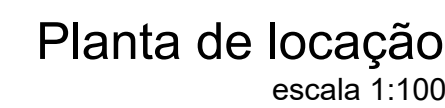


Os esforços indicados nesta tabela são os valores máximos obtidos pela envoltória de todas as combinações definidas para as fundações. Para análises complementares, deve-se consultar o relatório de esforços na fundação, que apresenta os valores calculados para cada combinação.

Coordenadas (m)	Localización en el XZ	Nombre
237,79 P1	P1, P35	
237,92 P51		
238,12 P23, P49		
531,62 P50		
539,12 P52		
548,17 P8, P17		
664,87 P24		
667,47 P36, P53		
934,41 P9		
941,91 P10		
942,25 P25, P37, P42, P54		
1412,20 P10, P26, P38, P43, P55		
1412,20 P11, P27, P39, P44, P56		
200,58 P12		
200,58 P11, P19		
200,58 P10, P40, P45, P57		
254,22 P2, P40		
258,66 P29, P41, P48, P58		
277,35 P3		
278,77 P21		
283,23 P59		
283,23 P30, P46		
303,24 P4, P13		
303,26 P3		
302,88 P22		
3426,82 P52, P47, P60		
351,82 P6		
3526,23 P14, P53		
3551,10 P1, P2, P34, P54		

Coordenadas (km)	Localidade no eixo Y	Nome
1601.02 P2, P5		
1603.52 P1, P3, P4, P6		
1573.67 P9, P12		
1571.17 P10, P11		
1566.17 P7, P8		
1428.52 P13, P14, P15		
1344.70 P16, P17, P18		
1327.93 P19		
1306.43 P20		
1215.68 P21		
1208.38 P22		
1104.26 P23		
1098.75 P24		
1052.64 P34		
1045.14 P31, P33		
1037.64 P32, P36, P27, P28, P29, P30, P32		
860.11 P37		
861.17 P35, P37, P38, P39, P40		
817.93 P41		
724.30 P46, P47		
665.58 P42, P43, P44		
677.04 P45		
629.46 P48		
575.73 P49		
562.33 P50		
409.70 P54, P55, P56, P57, P58, P59, P60		
404.26 P51		
399.26 P52, P53		

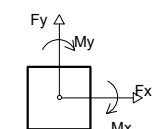

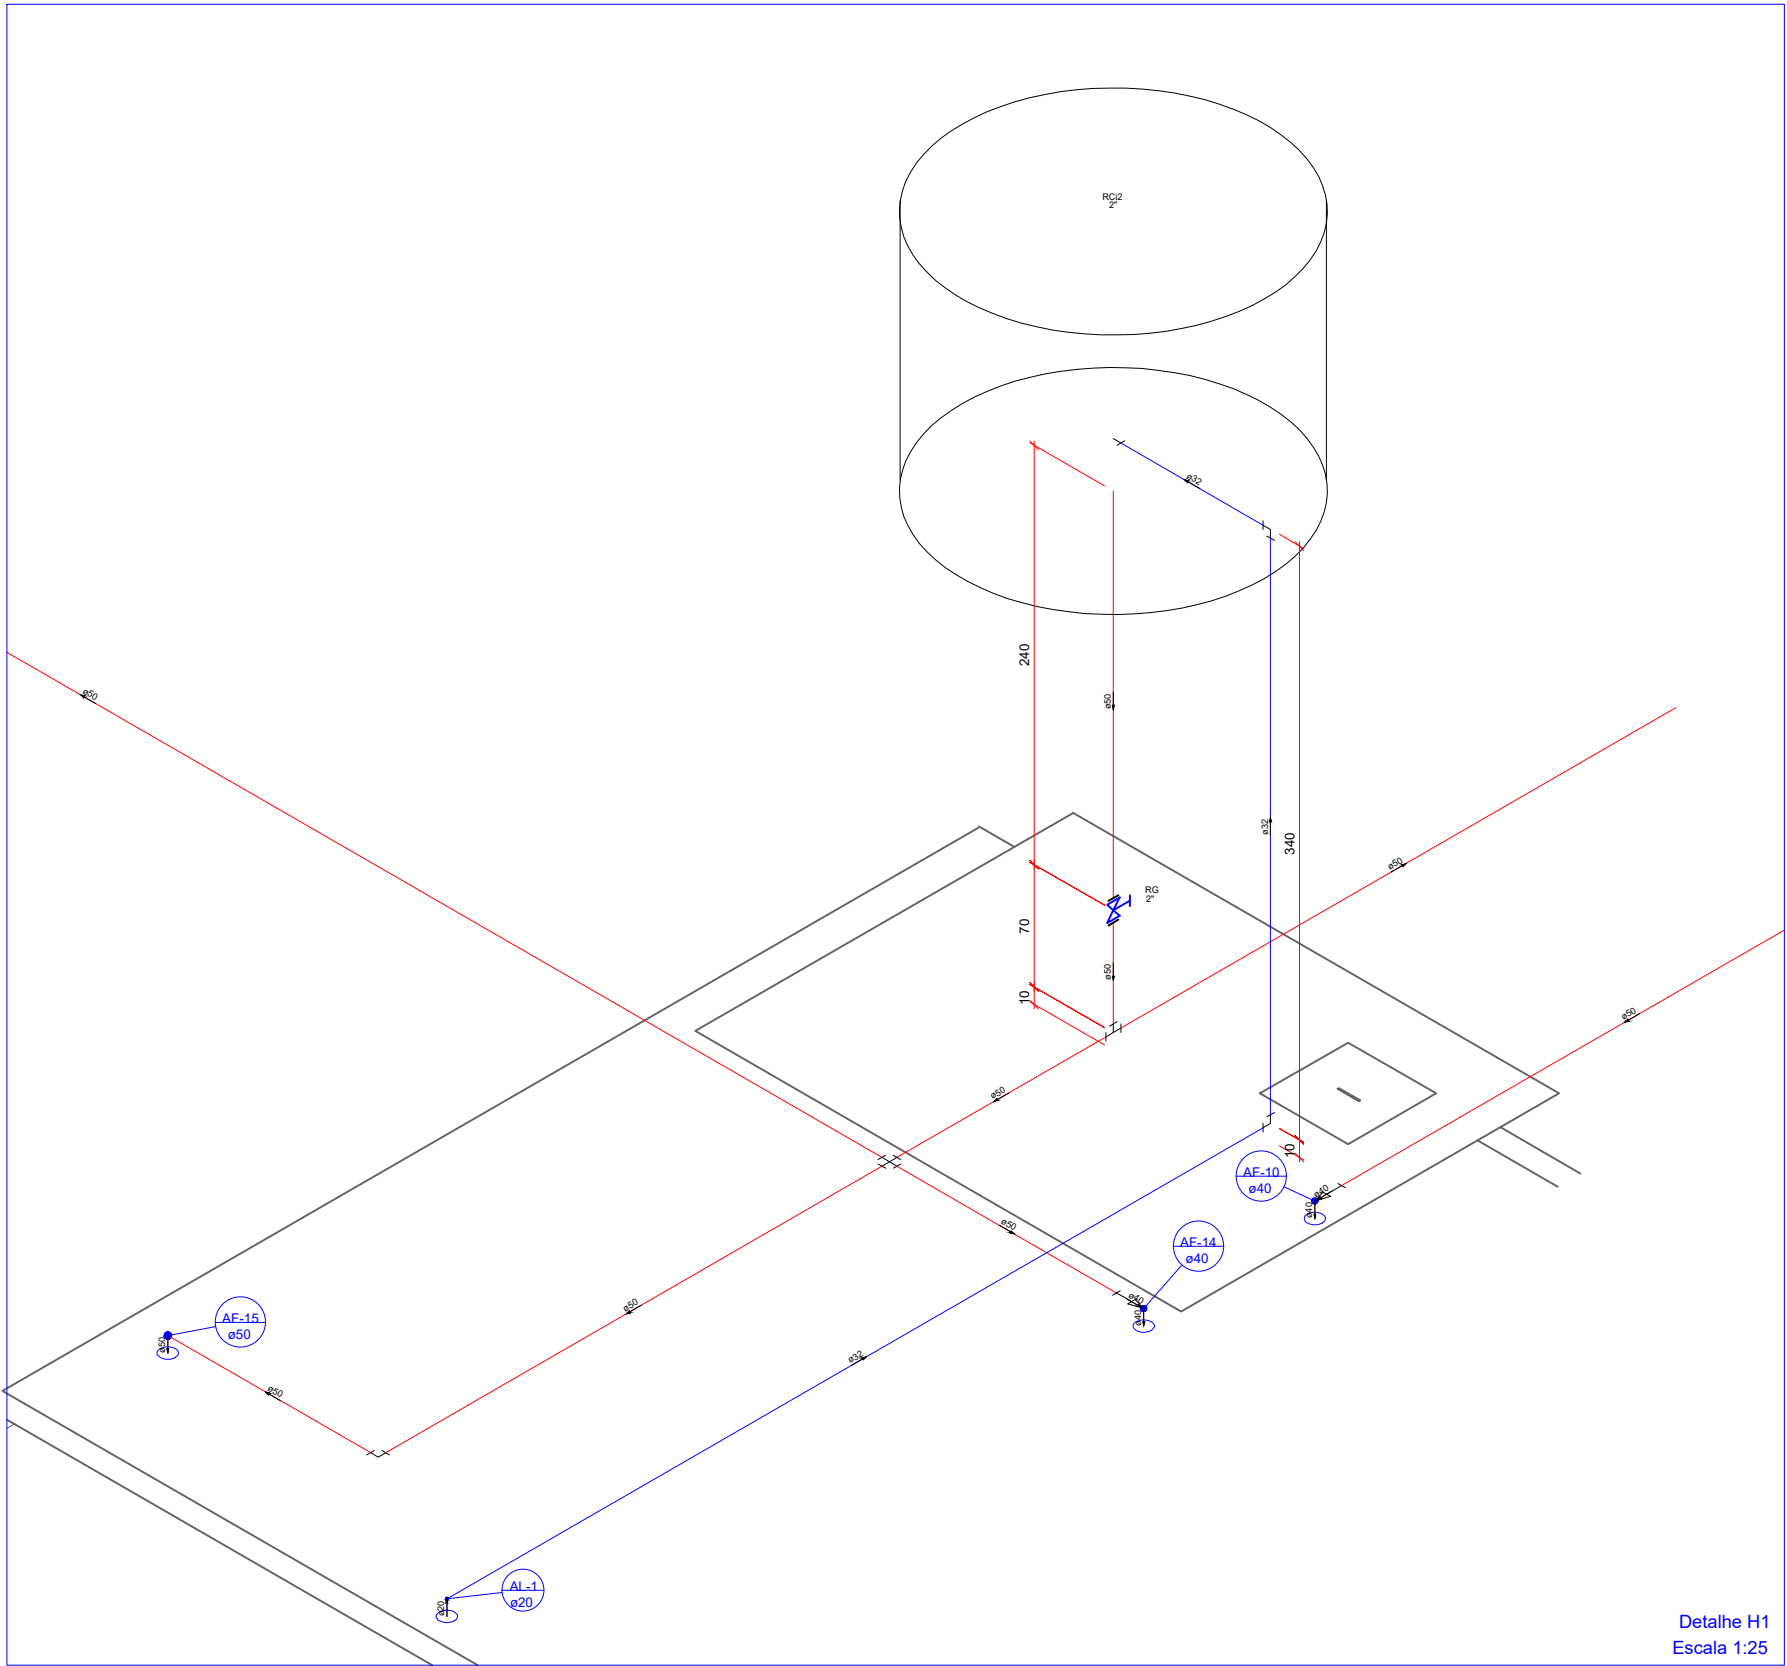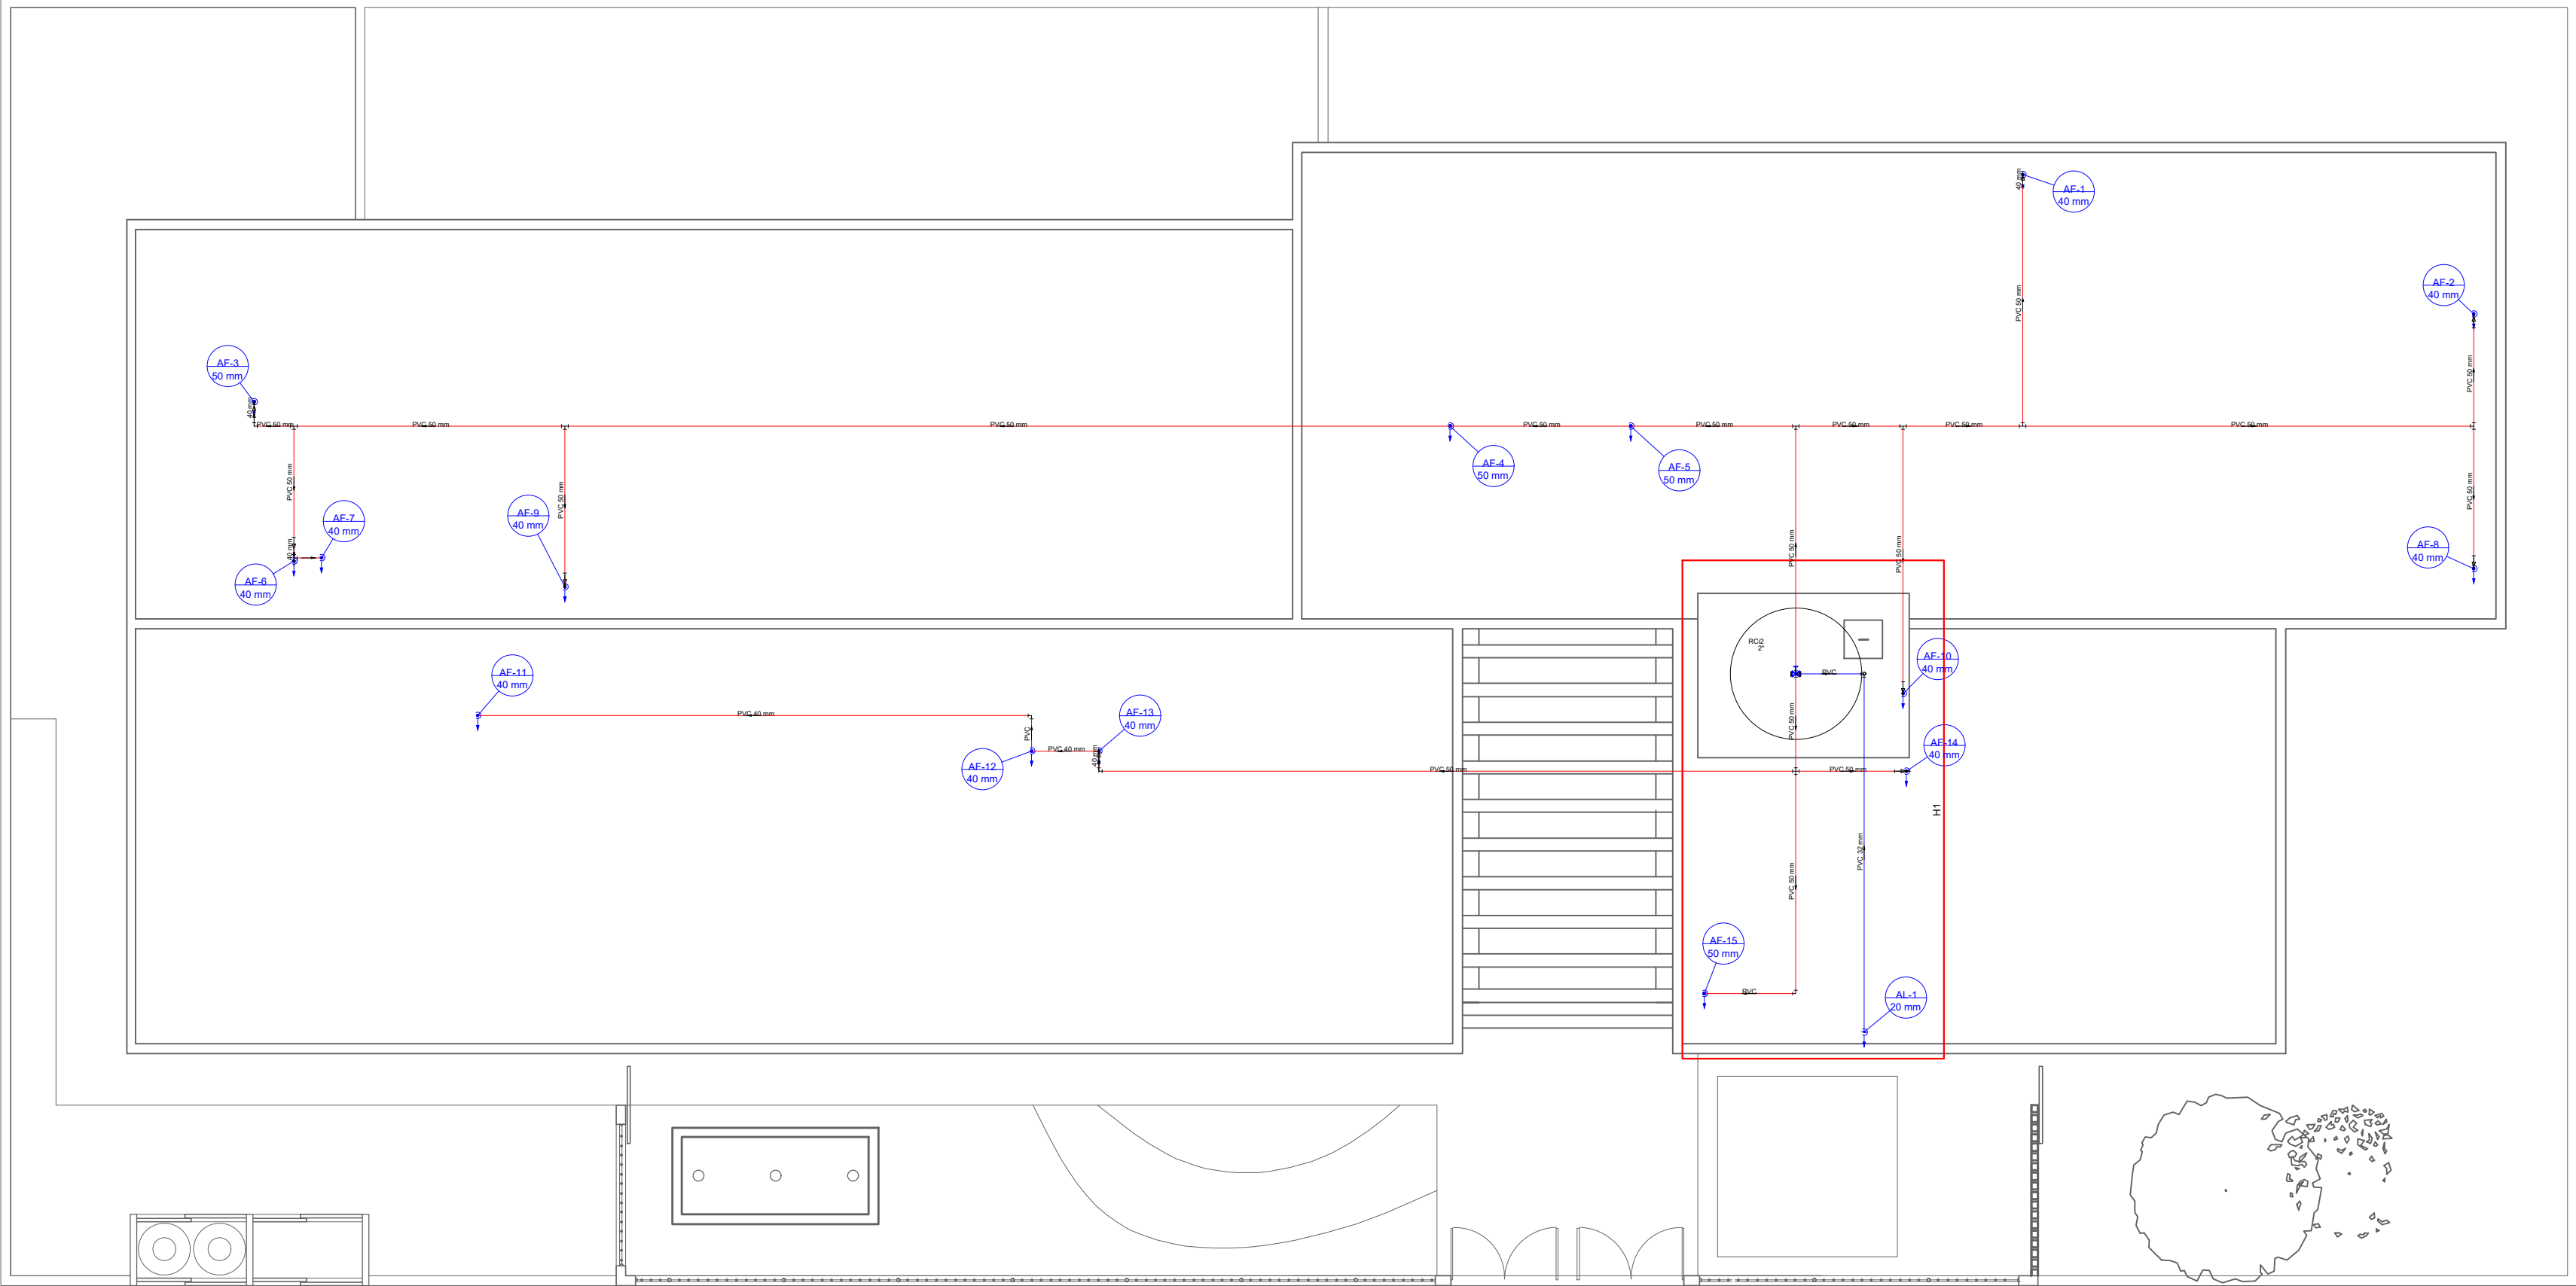

Hidráulico - Coberta
Escala 1:50

Lista de Materiais	
Materiais	Quantidade
Registro de gaveta bruto ABNT	1 pc
PVC rígido soldável	
Adapt. sold. c/ flange livre p/ ca. d' água	1 pc
60 mm - 2"	
Adapt. sold. curto cobrindo-caixa p registro	2 pc
60 mm - 2"	
Brucha de redução sold. curta	1 pc
40 mm - 32 mm	
50 mm - 40 mm	2 pc
60 mm - 50 mm	2 pc
Couante soldável	
25 mm	1 pc
Curva 90° soldável	39 pc
25 mm	
Joelho 90° soldável	1 pc
50 mm	
Tubos	
20 mm	0,06 m
32 mm	8,7 m
40 mm	11,63 m
50 mm	73,52 m
Tê 90 soldável	
25 mm	3 pc
50 mm	3 pc
60 mm	1 pc
Tê de redução 90 soldável	
50 mm - 20 mm	2 pc
50 mm - 25 mm	1 pc
Pneumático utilizado	
Fibra de vidro	1 pc
5000 L	

Legenda
Registro bruto gaveta ABNT c/PVC soldável

Dimensionamento de Reservatório Superior e Interior
A NBR 5626 estabelece que o volume total de água reservado deve atender no mínimo 24 h de consumo normal no edifício e deve considerar eventual volume adicional de água para combate a incêndio quando este estiver armazenado conjuntamente.
Considerando:
Quantidade de pessoas: 50 alunos + 15 professores + 8 funcionários administrativos + 10 funcionários de serviços gerais = 83 pessoas por turno.
Para escolas com sanitário: 100 litros por pessoa.
Consumo diário: 83 x 100 = 8300 litros por dia.
Reserva para 1 dia e meio: 8300 x 1,5 = 12450 litros.
Reservatório superior: 40% da reserva = 12450 x 0,4 = 4980 l = opção por reservatório de 5000 l.
Reservatório inferior: 60% da reserva = 12450 x 0,6 = 7470 l = opção por reservatório de 7500 l.


Dimensionamento de Bombas Hidráulicas
Opção-se por 2 bombas visando a segurança, para o caso de falha no funcionamento de uma delas.
Considerando um funcionamento de 3 h por dia, temos:
Capacidade do reservatório superior 5000 l = 5 m³
Vazão: 5 m³ / 3 h = 1,67 m³/h
As bombas escolhidas foram ambas o modelo com a seguinte especificação:
BOMBA CENTRÍFUGA, MONOFÁSICA, 0,5 CV OU 0,49 HP, HM 6 A 20 M, Q 1,2 A 8,3 M³/h, uma vez que a edificação é térrea e a altura manométrica não ultrapassa a máxima prevista.

PROPRIETÁRIO: PREFEITURA MUNICIPAL DE COREMAS - PB


FERNANDO MATIAS MAMEDE CREA 162056275-6

FOLHA	03/03	PROJETO: CONSTRUÇÃO DE CRECHES COM CAPACIDADE PARA 50 CRIANÇAS
CONCEDENTE:	PREFEITURA MUNICIPAL DE COREMAS - PB	
LOCALIDADE:	MUNICÍPIO DE COREMAS - PB	
DATA:	03/03/22	
RESPONSÁVEL:		
RUBRICA:		
DADOS:		
ESCALAS:		
INDICADA:		
DESENHOS:	Projeto Hidráulico - Coberta Planta Baixa Detalhe	PROPOSTA REVISÃO ARQUIVO


Aprovações:

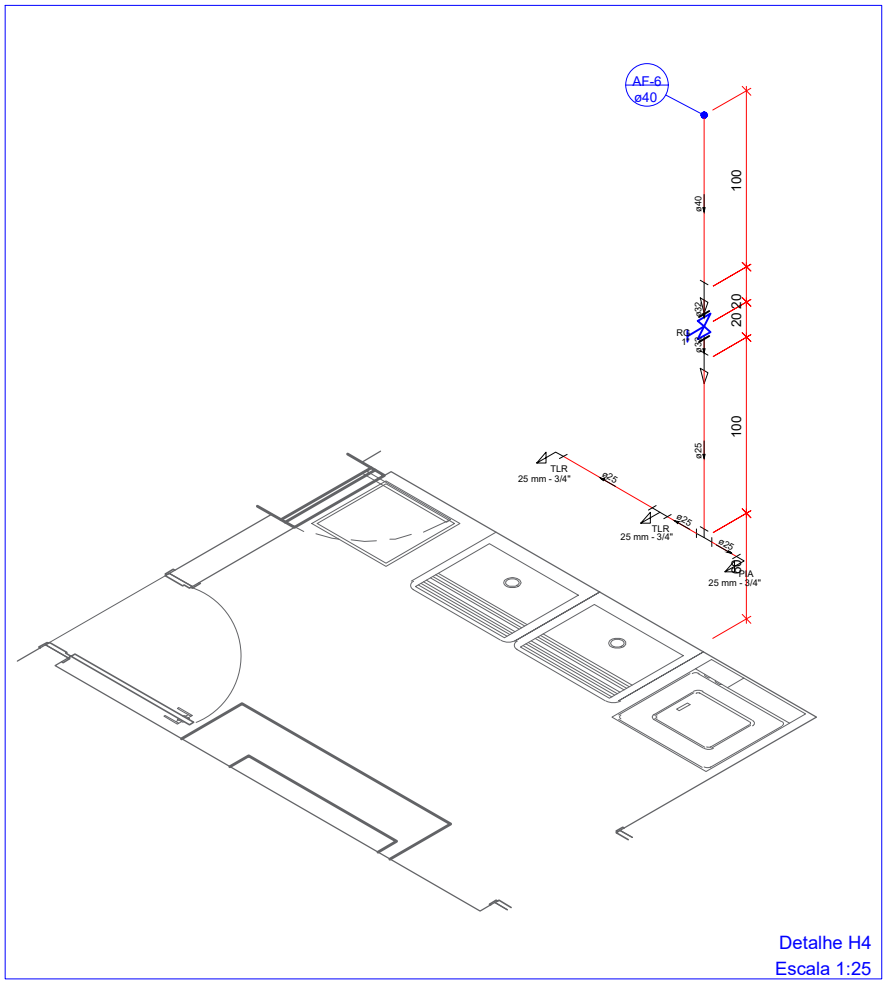


Detalhe H4
Escala 1:25

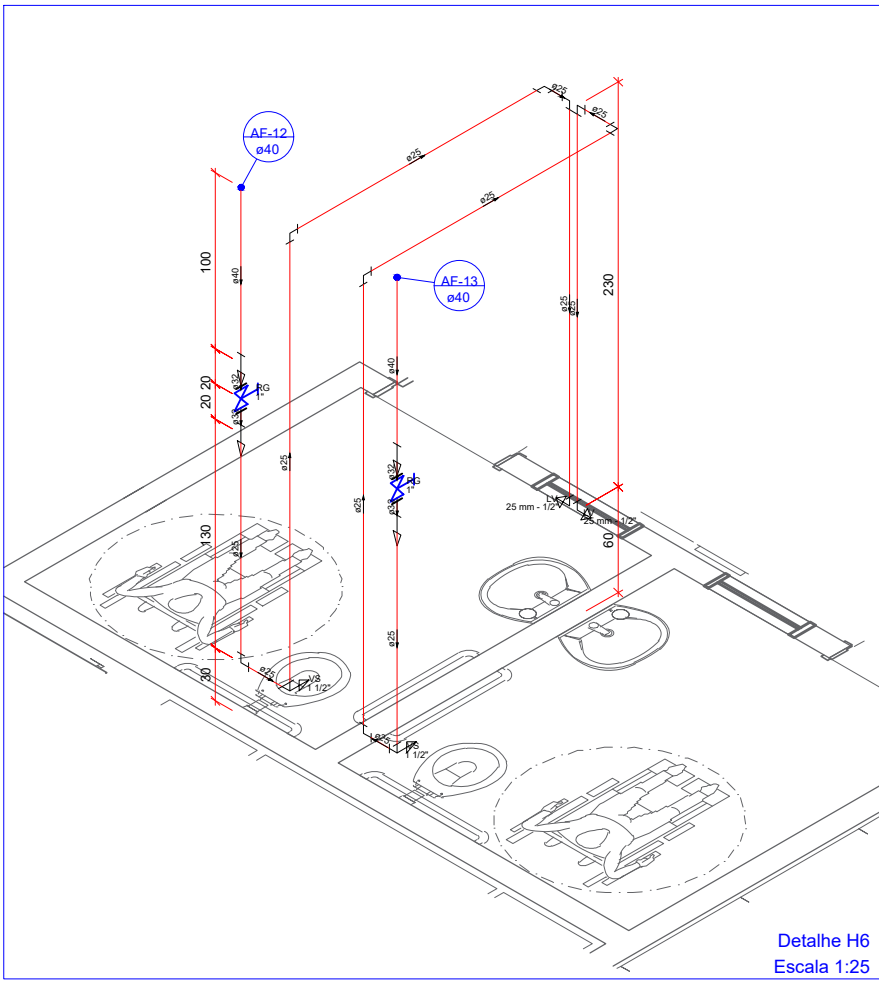


Detalhe H6
Escala 1:25

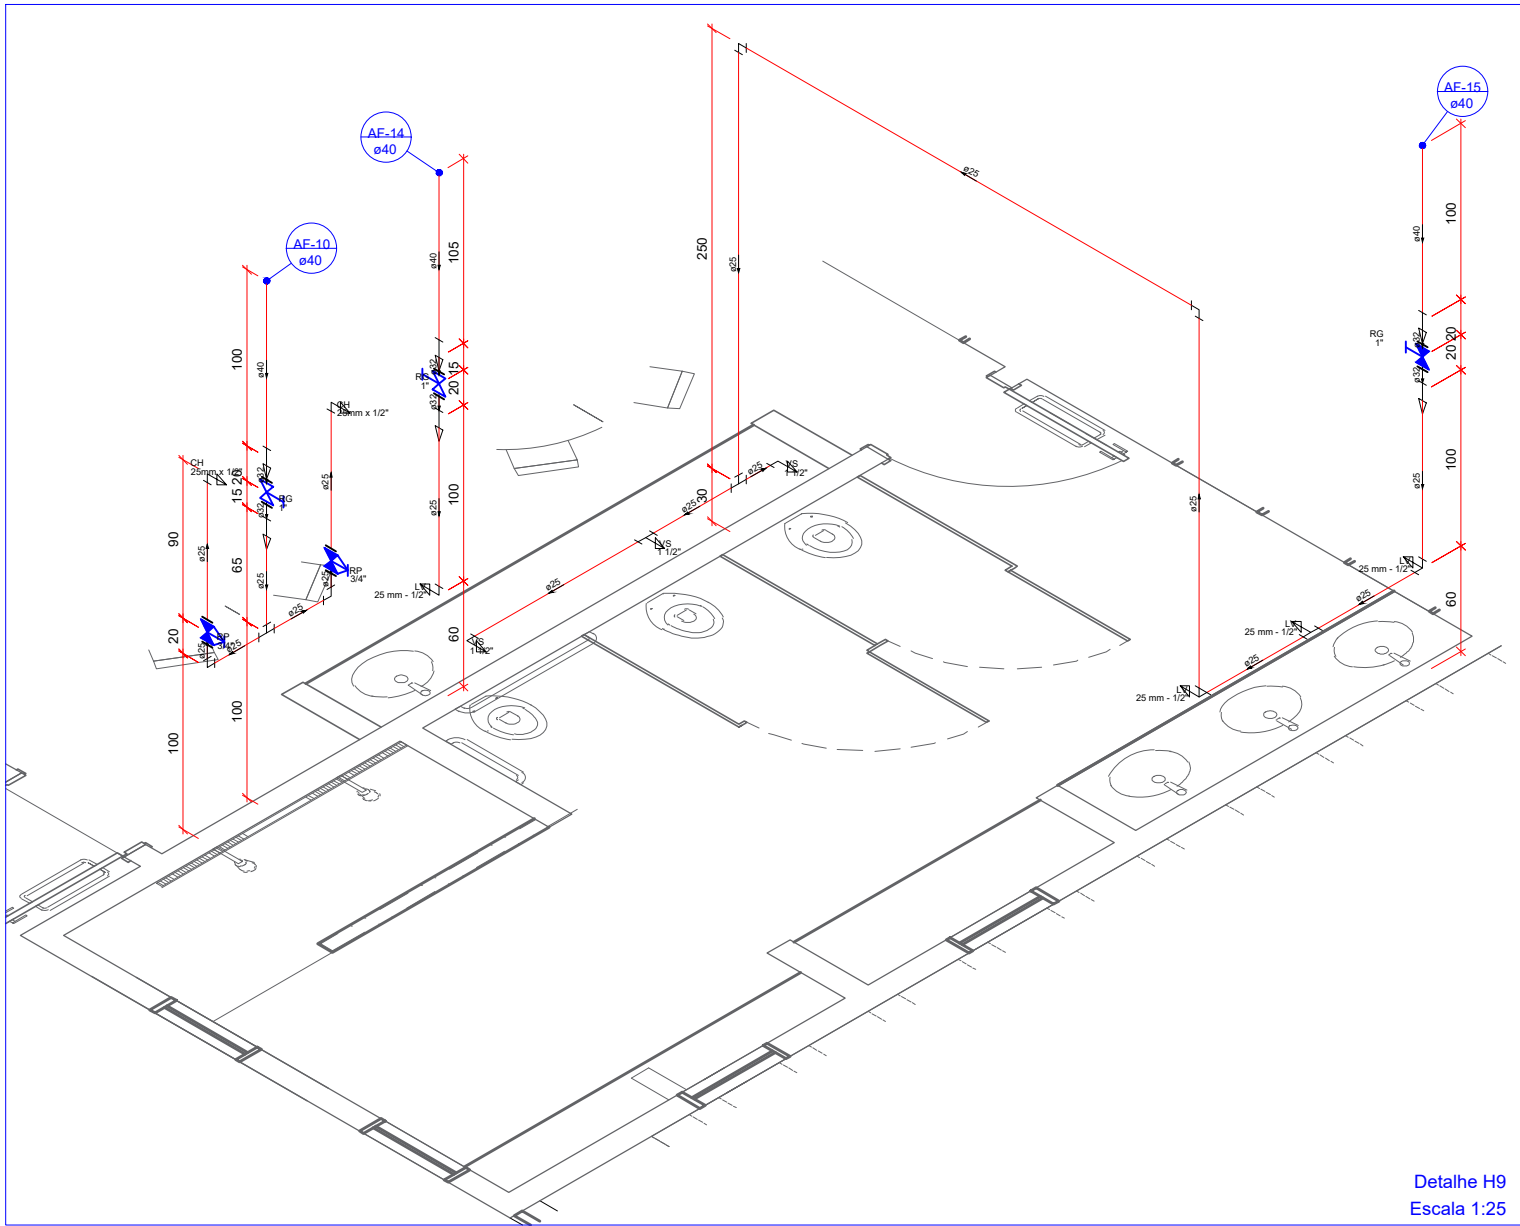


Detalhe H9
Escala 1:25

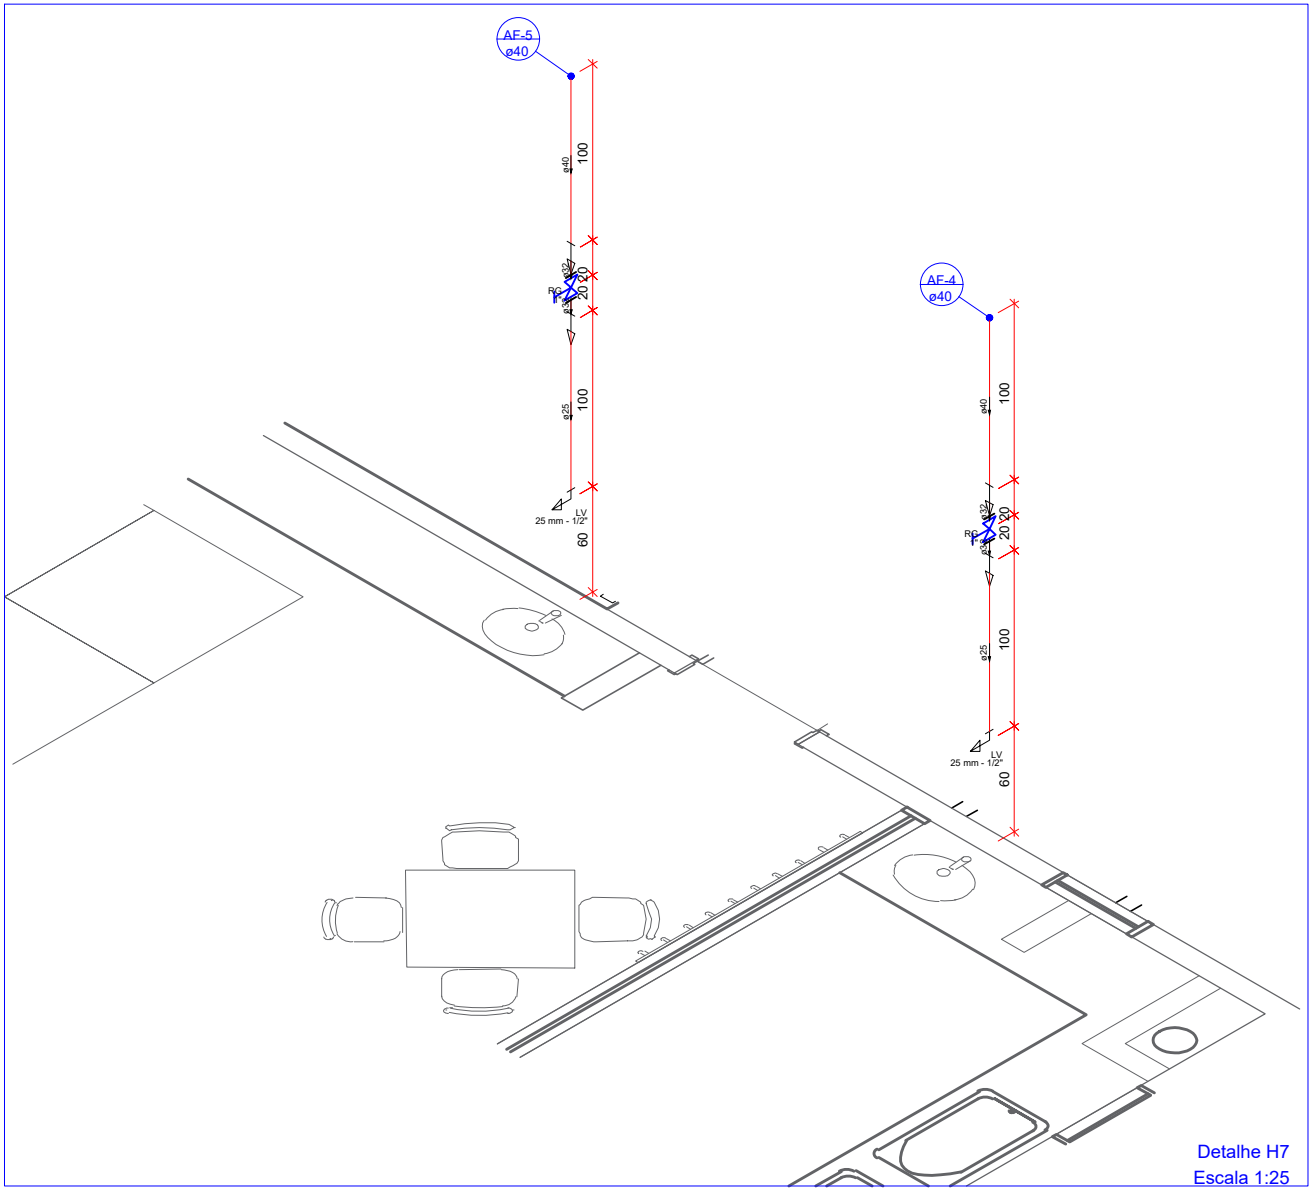


Detalhe H7
Escala 1:25

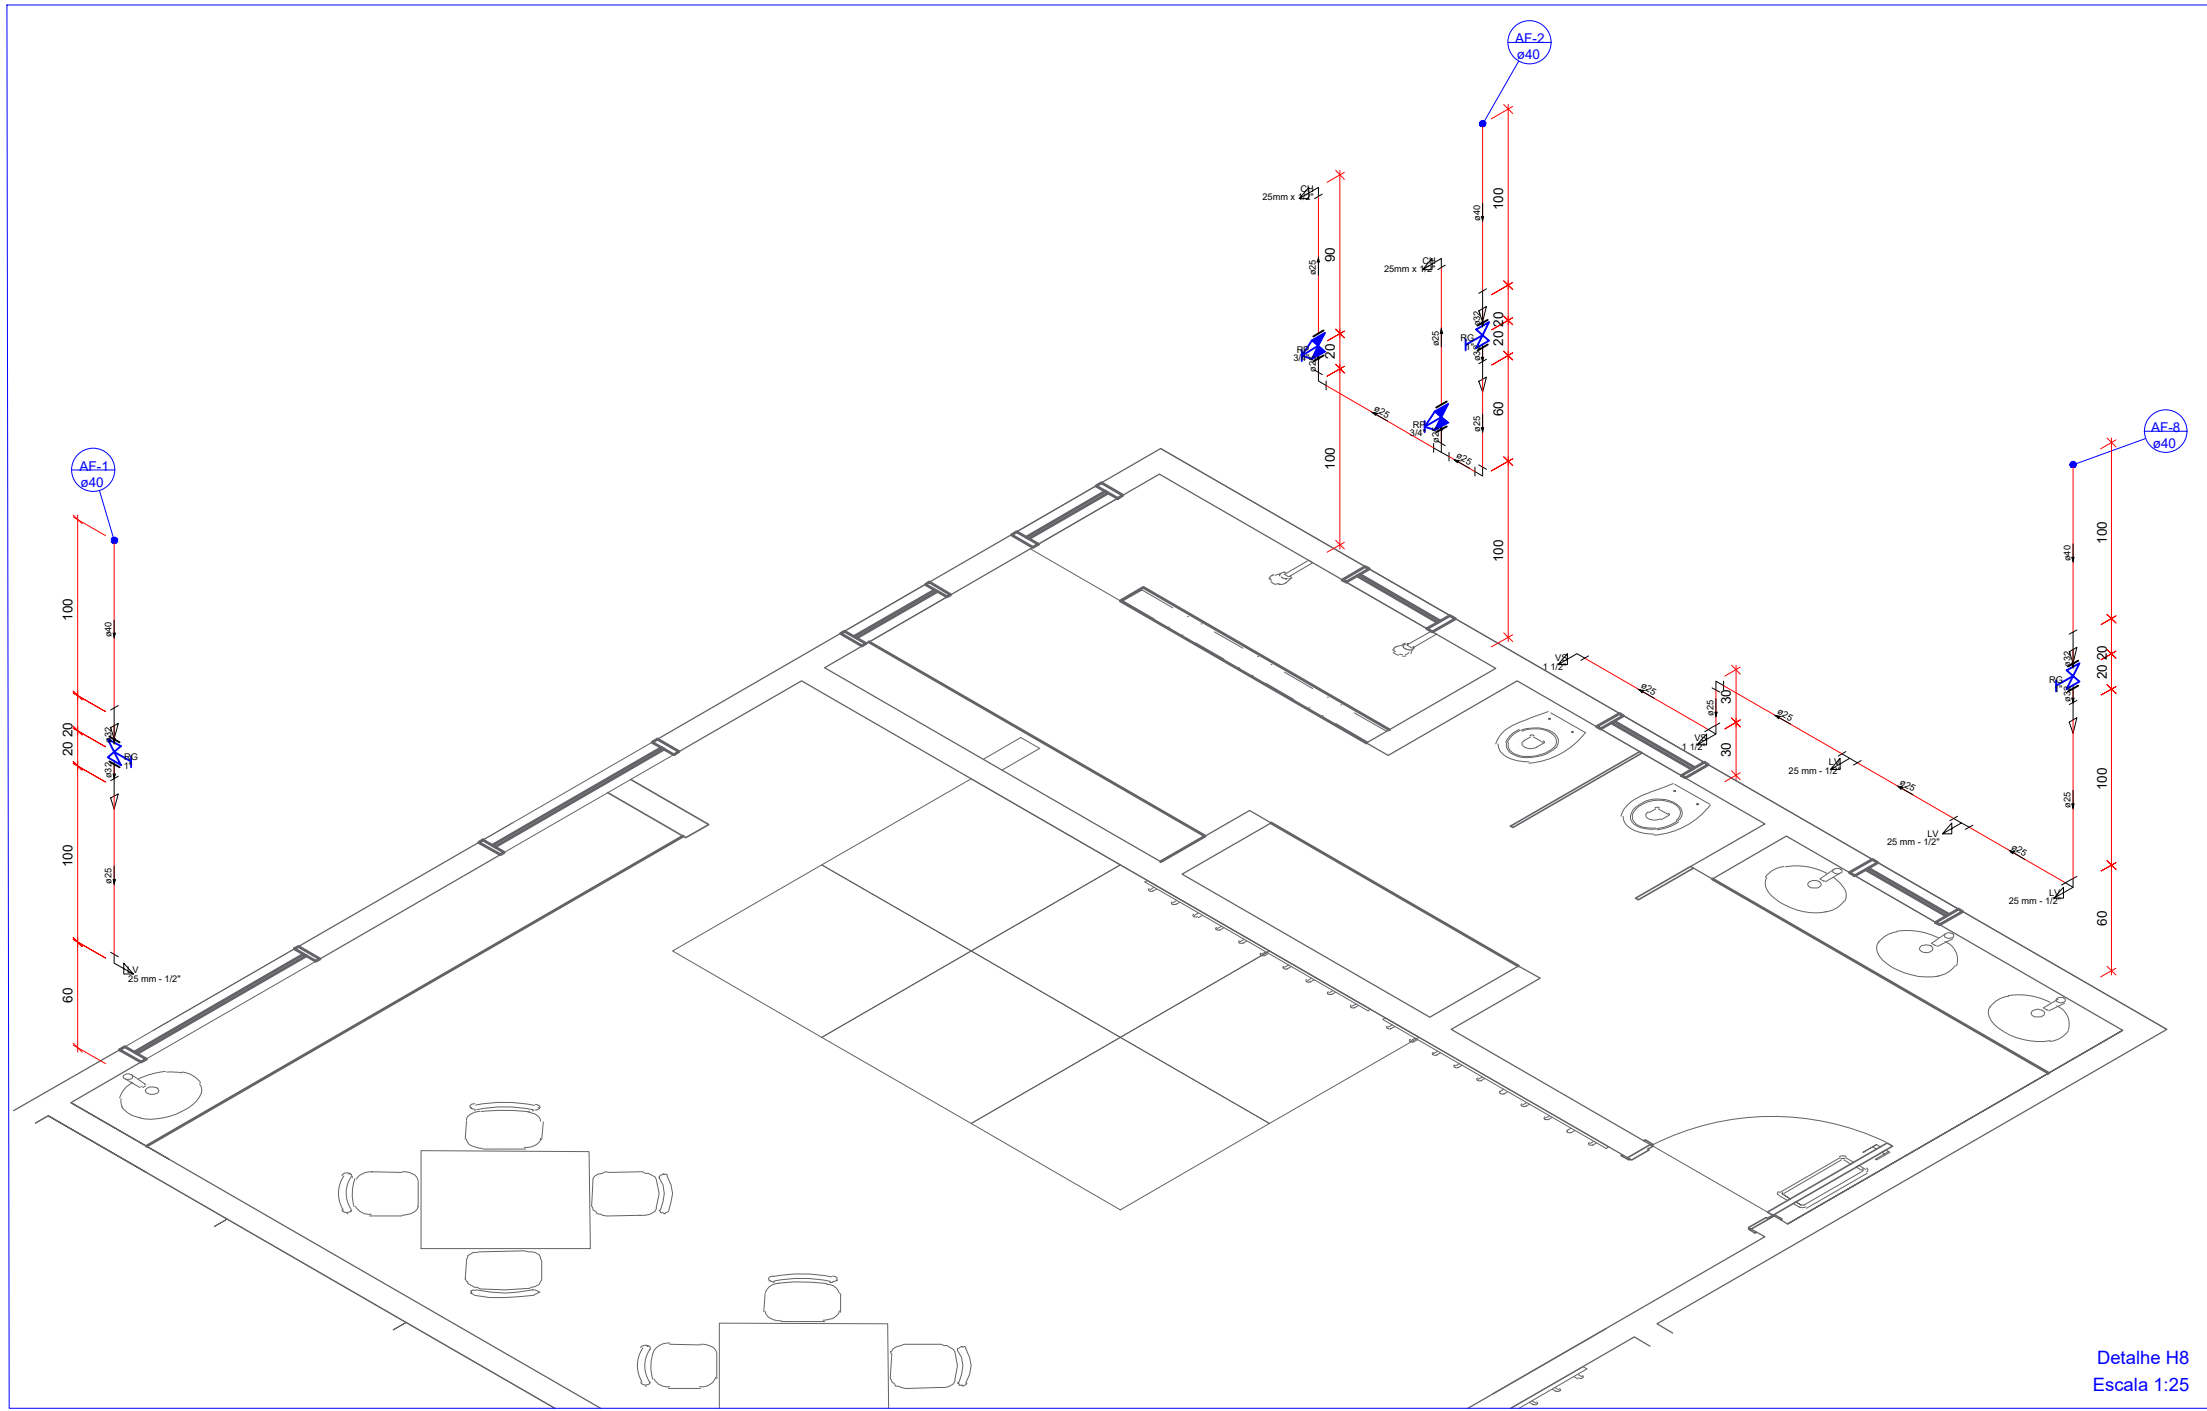

Detalhe H8
Escala 1:25

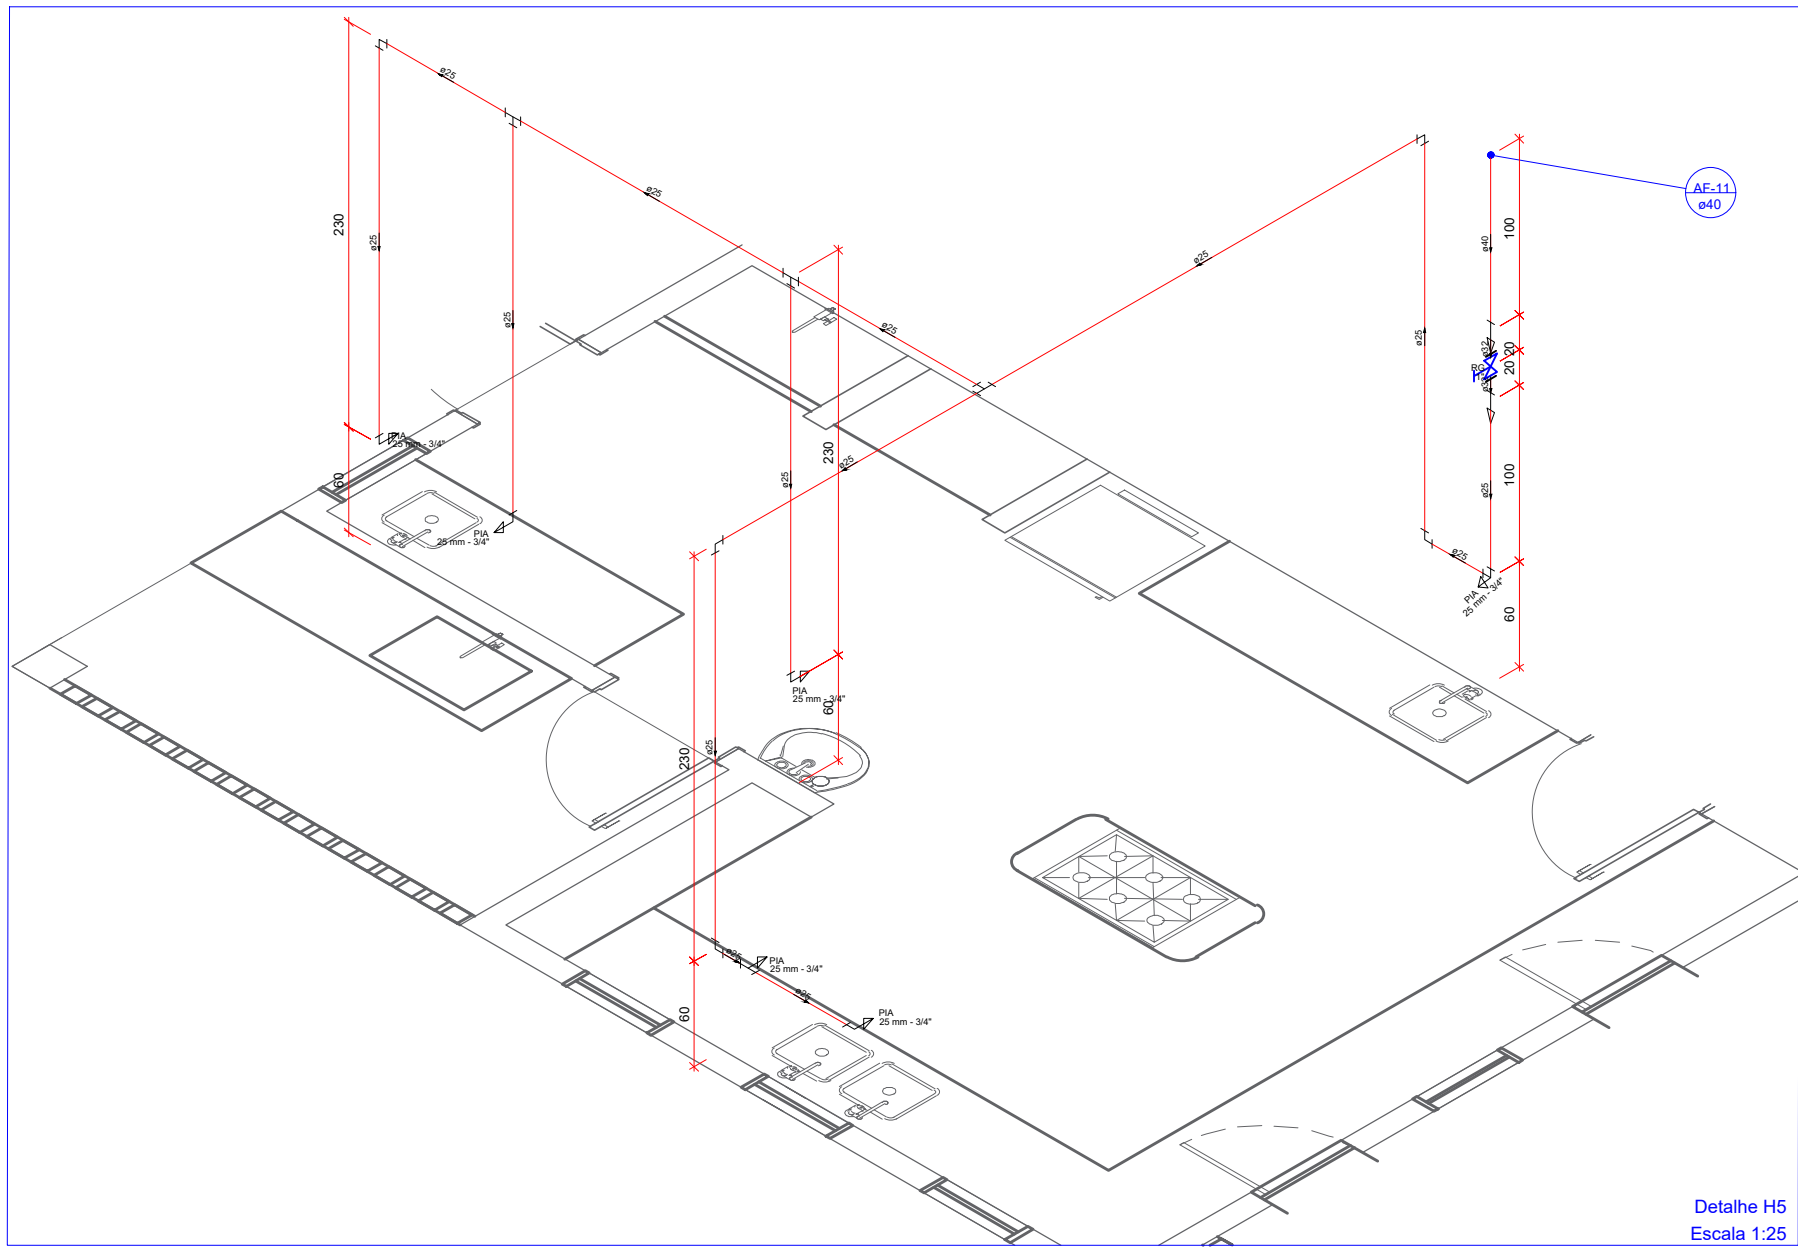

Detalhe H5
Escala 1:25

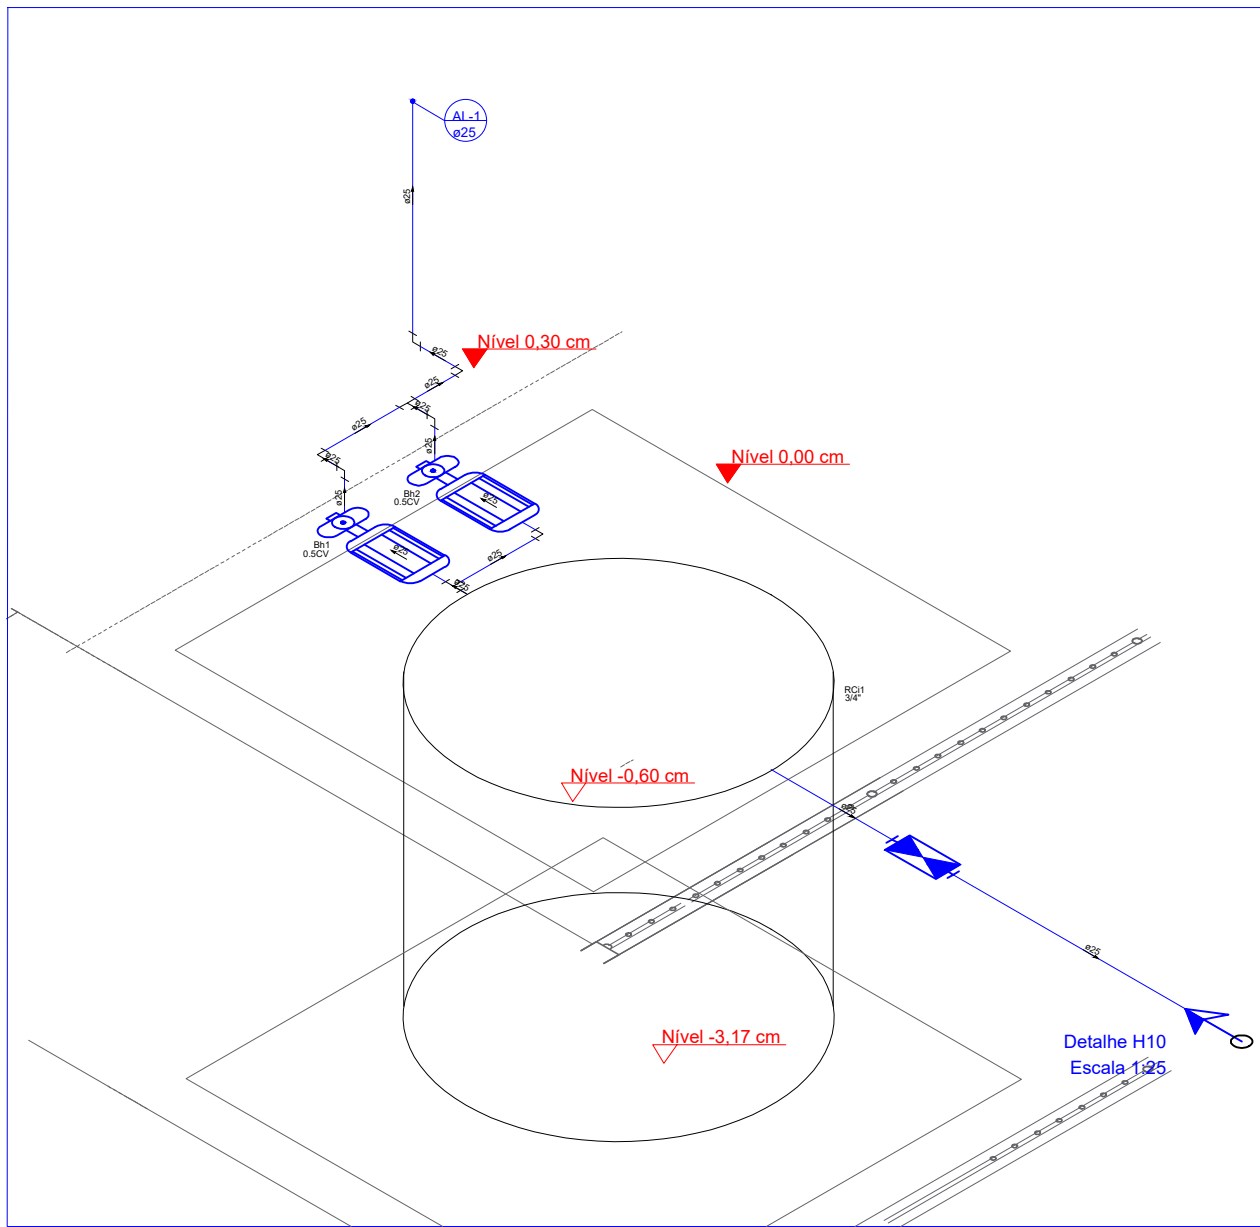

Detalhe H10
Escala 1:25

PROPRIETÁRIO: PREFEITURA MUNICIPAL DE COREMAS - PB


FERNANDO MATIAS MAMEDE CREA 162056275-8

FOLHA
02/03


PROJETO: CONSTRUÇÃO DE CRECHES COM CAPACIDADE DE 50 CRIANÇAS
CONCEDENTE: PREFEITURA MUNICIPAL DE COREMAS - PB
LOCALIDADE: MUNICÍPIO DE COREMAS - PB

DESIGNO	DATA	RESPONSÁVEL	RUBRICA	DADOS
02/03	02/2022	LINDAL CASTANHO		
VERO				
ESCALAS	DESENHOS	PROPOSTA		
INDICADA	Projeto Hidráulico - Térreo Detalhes 3 a 10	REVISÃO		
		ARQUIVO		

Aprovações:

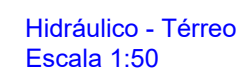

Legenda	
	Alimentador Predial
	Bomba Hidráulica
	Hidrômetros
	Registro bruto gaveta ABNT o/PVC soldável
	Registro de gaveta c/canopla cromada o/PVC soldável
	Registro de pressão c/ canopla cromada

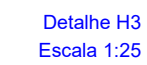

FERNANDO MATIAS MAMEDE CREA 162056275-8

01/03 | CONCEDENTE:

LOCALIDADE: MUNICÍPIO DE COREMAS - PB

	DATA	RESPONSÁVEL	RUBRICA	
07/04/2023	03/03/2023			

VISTO		
ESCALAS	DESENHOS	Projeto Hidráulico - Térreo Planta Baixa Detalhes 1 a 3
INDICADA		

Aprovações: