



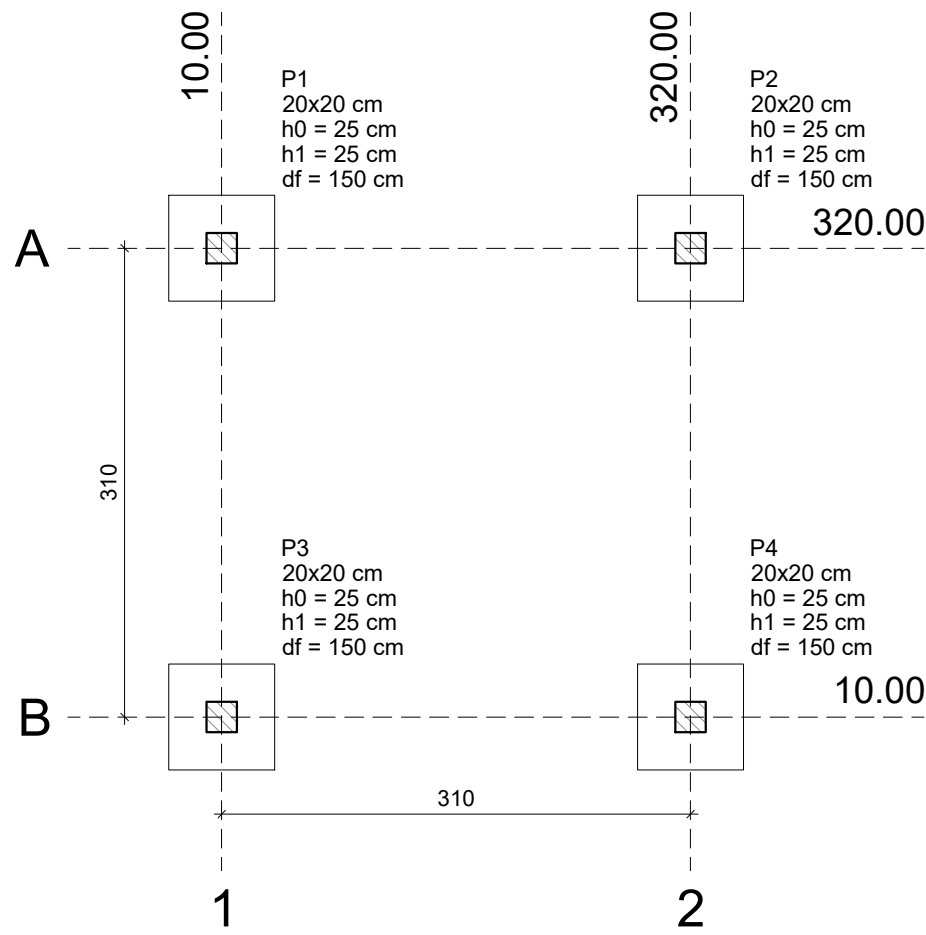

Localização estrutural – Caldeira
escala 1/50

Legenda dos Pilares	
	Pilar que morre
	Pilar que passa
	Pilar que nasce
	Pilar com mudança de seção

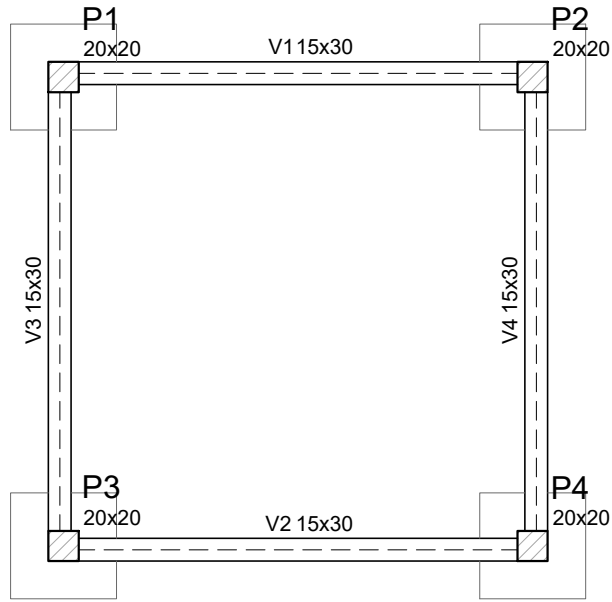


Forma Baldrame – Caldeira
escala 1/50

Vigas			
Nome	Seção (cm)	Elevação (cm)	Nível (cm)
V1	15x30	0	0
V2	15x30	0	0
V3	15x30	0	0
V4	15x30	0	0









Pilares			
Nome	Seção (cm)	Elevação (cm)	Nível (cm)
P1	20 x 20	0	0
P2	20 x 20	0	0
P3	20 x 20	0	0
P4	20 x 20	0	0

Características dos materiais	
fck (kgf/cm ²)	Ecs (kgf/cm ²)
250	238000


Pilar										Fundação				
Nome	Seção (cm)	X (cm)	Y (cm)	Carga Máx. (tf)	Carga Min. (tf)	Mx (kgf.m)	My (kgf.m)	Fx (tf)	Fy (tf)	Lado B (cm)	Lado H (cm)	h0 / ha (cm)	h1 / hb (cm)	df (cm)
P1	20x20	10.00	320.00	5.9	4.9	200	200	0.3	0.3	70	70	25	25	150
P2	20x20	320.00	320.00	5.9	4.9	200	200	0.3	0.3	70	70	25	25	150
P3	20x20	10.00	10.00	5.8	4.8	200	200	0.3	0.3	70	70	25	25	150
P4	20x20	320.00	10.00	5.8	4.8	200	200	0.3	0.3	70	70	25	25	150

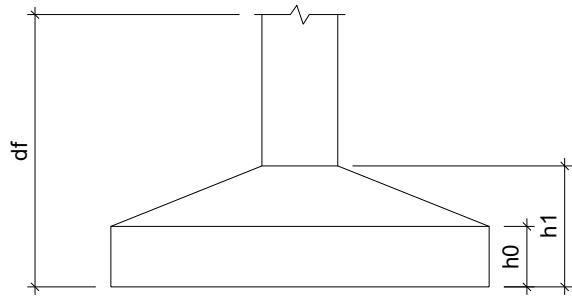


Detalhe estrutural – Caldeira
escala 1/50

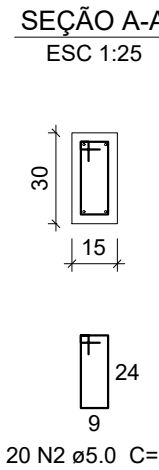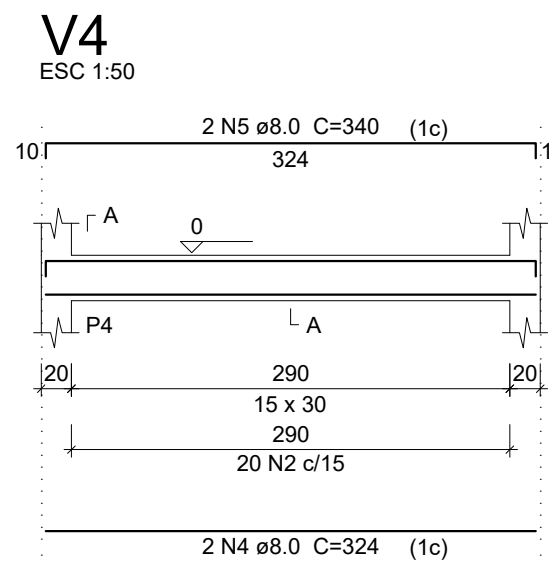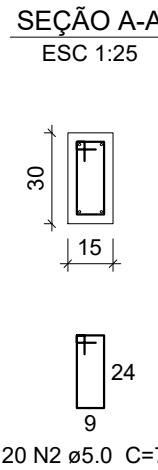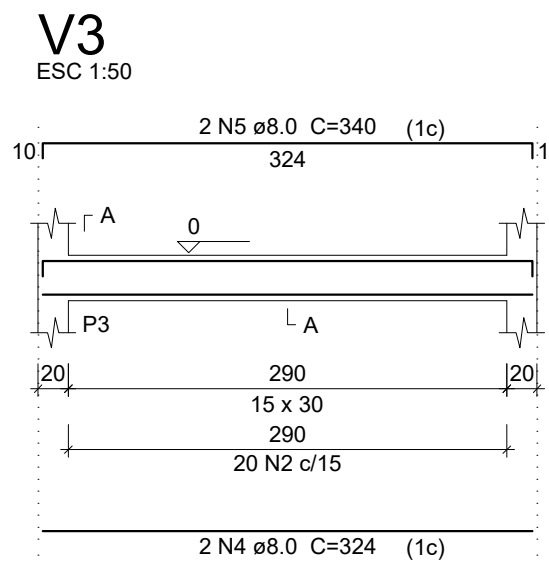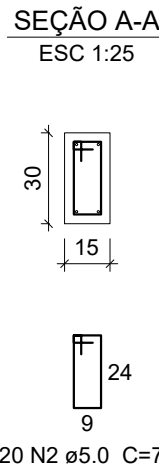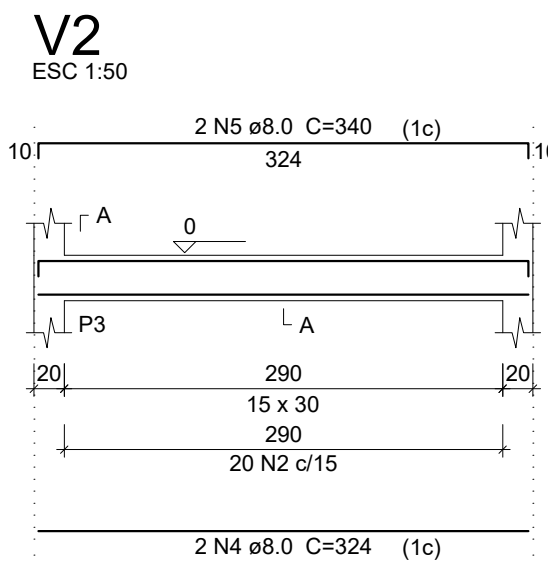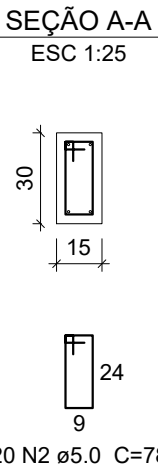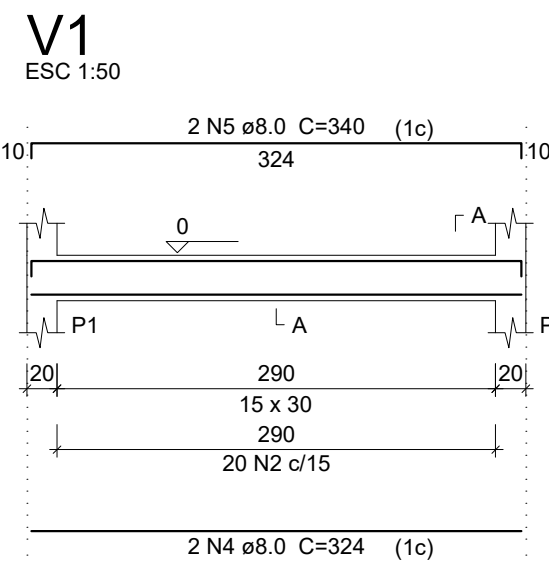



Detalhe Fundação – Vigas
escala 1/50

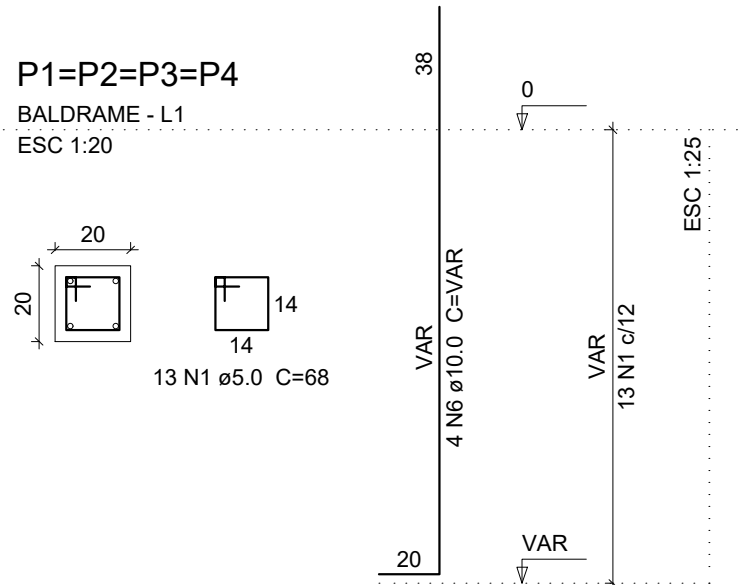

Detalhe Pilares – Caldeira
escala 1/50

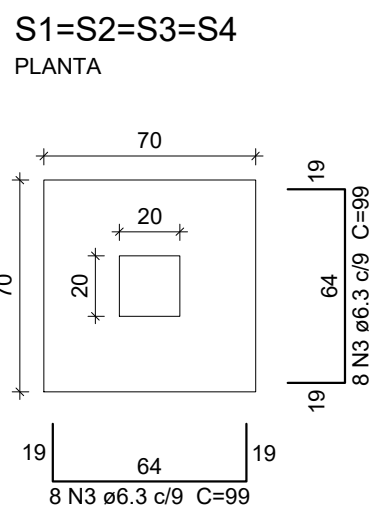

Detalhe Fundação – Caldeira
escala 1/20

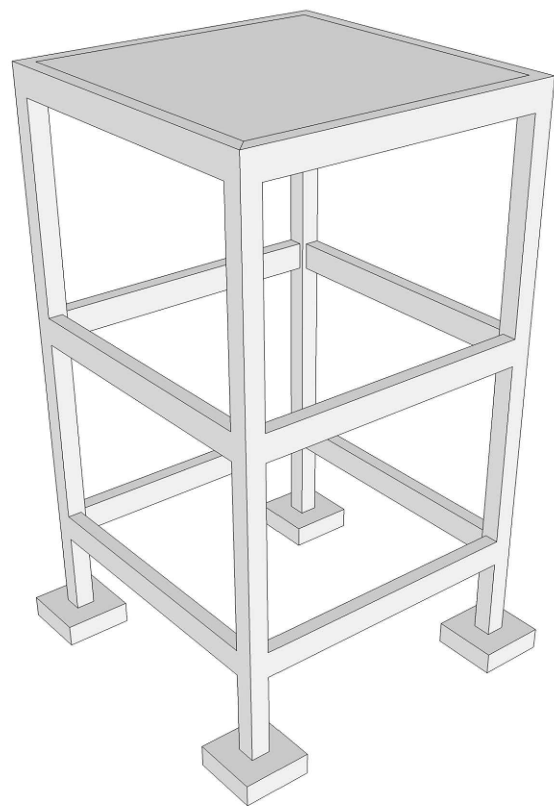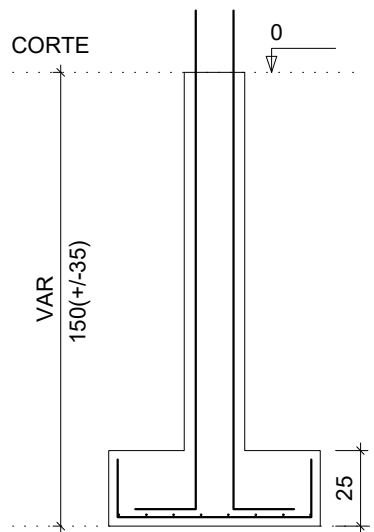

Maquete Estrutural 3D – Caldeira
escala 1/50

Relação do aço

AÇO	N	DIAM	Q	UNIT (cm)	C.TOTAL (cm)
CA60	1	5.0	52	68	3536
	2	5.0	80	78	6240
	3	6.3	64	99	6336
	4	8.0	8	324	2592
	5	8.0	8	340	2720
	6	10.0	16	VAR	VAR

Resumo do aço

AÇO	DIAM	C.TOTAL (m)	PESO + 10 % (kg)
CA50	6.3	63.4	17.1
	8.0	53.2	23.1
	10.0	33	22.4
CA60	5.0	97.8	16.6
PESO TOTAL			
CA50	62.5		
CA60	16.6		

RESPONSÁVEL TÉCNICO:

PROPRIETÁRIO:

PRANCHA		PREFEITURA MUNICIPAL DE COREMAS – PB			
1/3		PROJETO DE CONSTRUÇÃO DE MATADOURO – 9389922022			
		PROJETO ESTRUTURAL - CALDEIRA - BALDRAME			
DESENHO	DATA	RESPONSÁVEL		RUBRICA	
PROJETO				ÁREA DO TERRENO	ÁREA ÚTIL
CÓPIA				10.000,00 M²	971,43 M²
ESCALA:		DESENHO:		ÁREA CONSTRUIDA	
1:20 1:50 1:20 s/esc		LOCAÇÃO ESTRUTURAL FORMA BALDRAME DETALHES VIGAS, FUNDAÇÃO E PILARES MAQUETE ESTRUTURAL 3D - CALDEIRA		871,58 M²	