



Fachada Lateral Direita – Curral Bovino

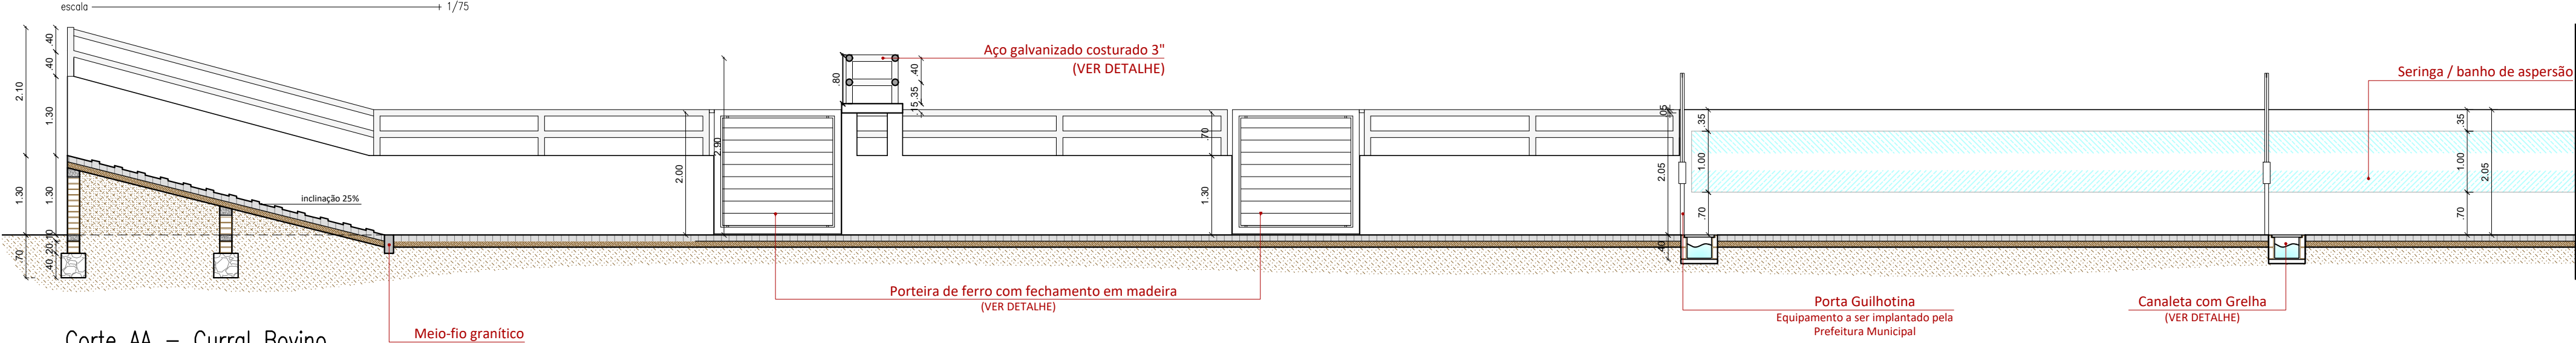

Corte AA – Curral Bovino

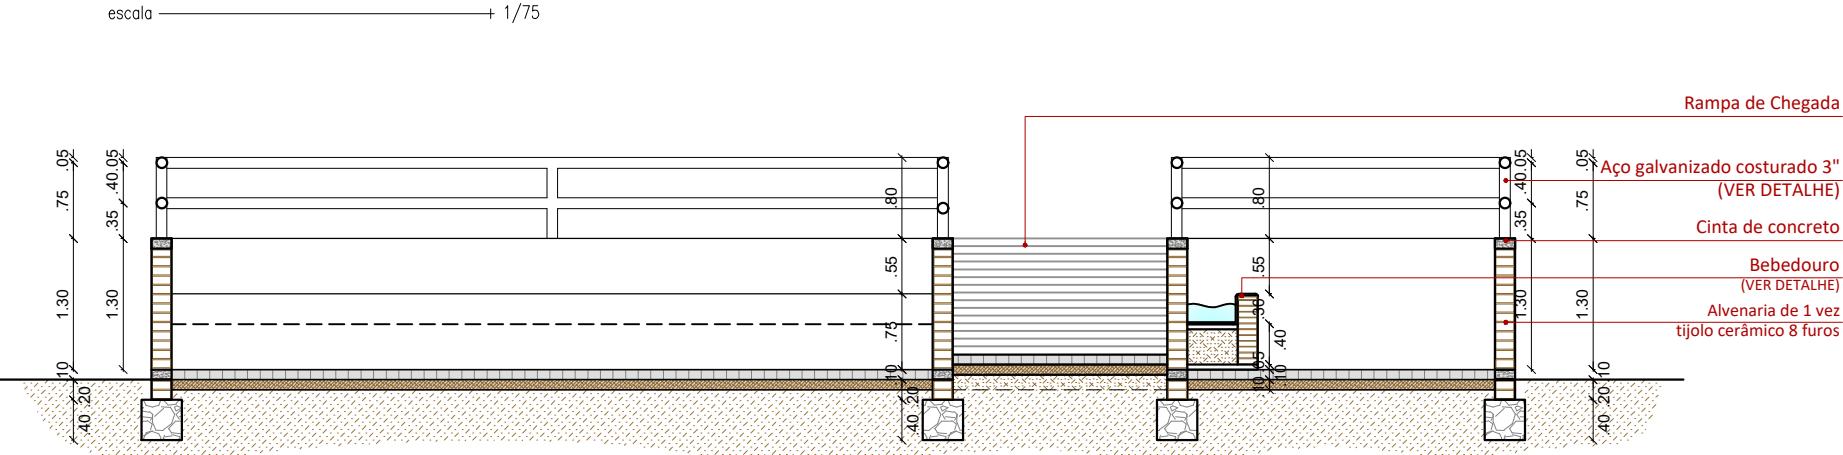

Corte BB – Curral Bovino



Corte CC – Curral Bovino



Detalhe perspectivado – Seringa/Banho

|                      |                                                 |                         |                 |
|----------------------|-------------------------------------------------|-------------------------|-----------------|
| RESPONSÁVEL TÉCNICO: |                                                 |                         |                 |
| PROPRIETÁRIO:        |                                                 |                         |                 |
| PRANCHA<br><br>3/4   | PREFEITURA MUNICIPAL DE COREMAS – PB            |                         |                 |
|                      | PROJETO DE CONSTRUÇÃO DE MATADOURO – 9389922022 |                         |                 |
|                      | PROJETO ARQUITETÔNICO – CURRAL BOVINO           |                         |                 |
|                      | DATA                                            | RESPONSÁVEL             | RUBRICA         |
| DESENHO              |                                                 |                         |                 |
| PROJETO              |                                                 |                         | ÁREA DE TERRENO |
| CÓPIA                |                                                 |                         | 10.000,00 M²    |
| ESCALA:              |                                                 | DESENHO:                | ÁREA CONSTRUÍDA |
| 1/75                 |                                                 | CORTE AA, BB E CC       | 871,58 M²       |
| 1/75                 |                                                 | FACHADA LATERAL DIREITA |                 |