




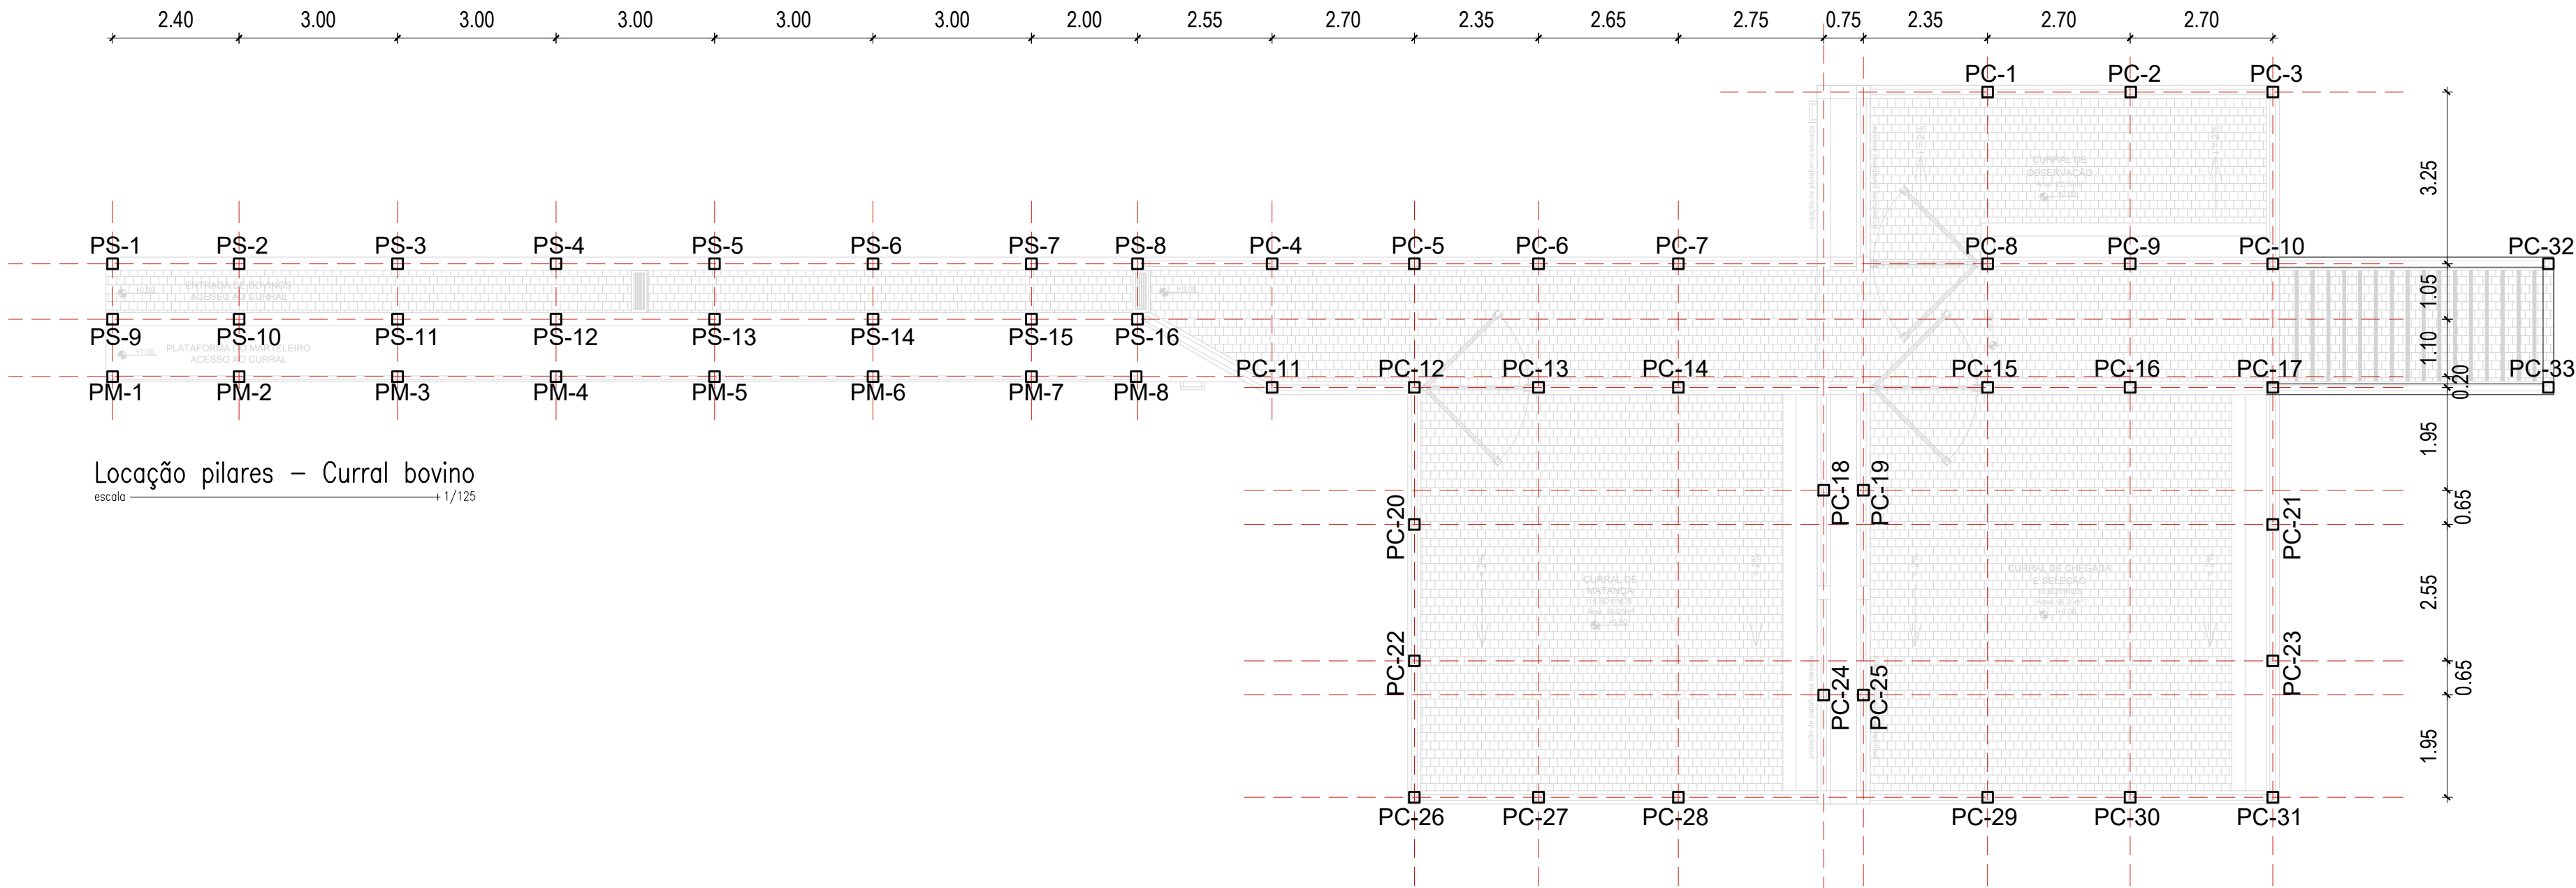


Locação pilares – Curral bovino
escala 1/125

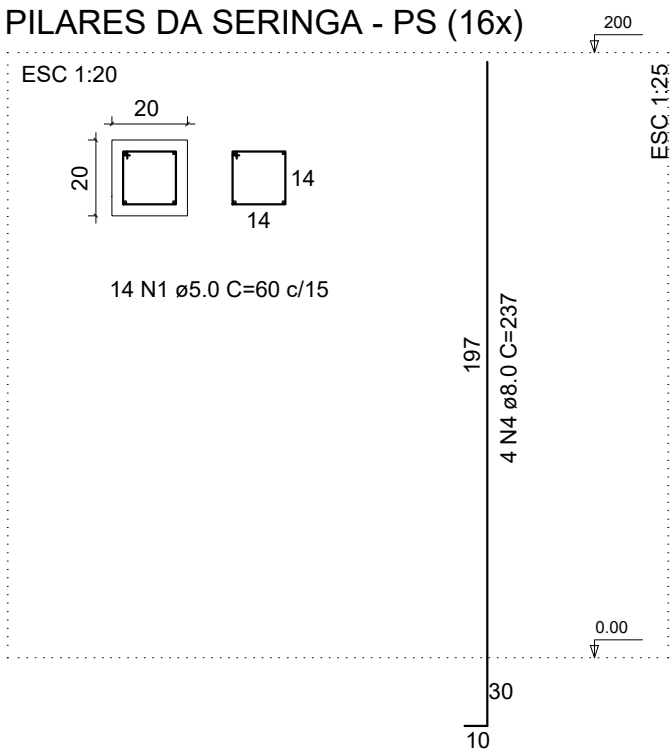

Relação do aço					PILARES
AÇO	N	DIAM	Q	UNIT (cm)	C.TOTAL (cm)
CA60	1	5.0	559	60	33540
CA50	2	8.0	124	167	20708
	3	8.0	32	137	4384
	4	8.0	64	237	15168
Resumo do aço					
AÇO	DIAM	C.TOTAL (m)	PESO + 10 % (kg)		
CA50	8.0	402.6	108.5		
CA60	5.0	335.4	56.8		
PESO TOTAL					
CA50	108.5				
CA60	56.8				

Detalhe pilares – Curral bovino
escala 1/20

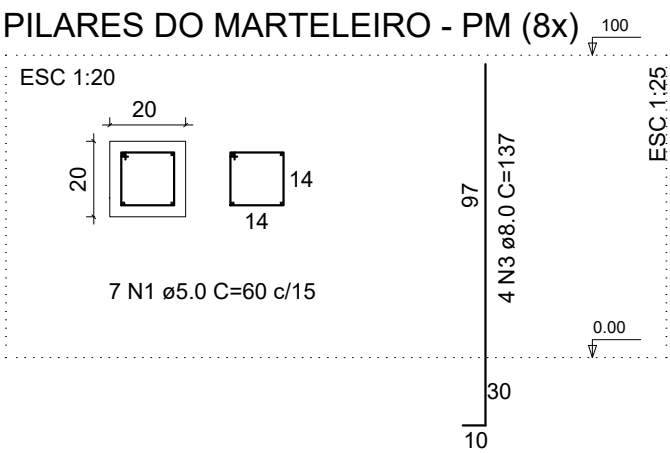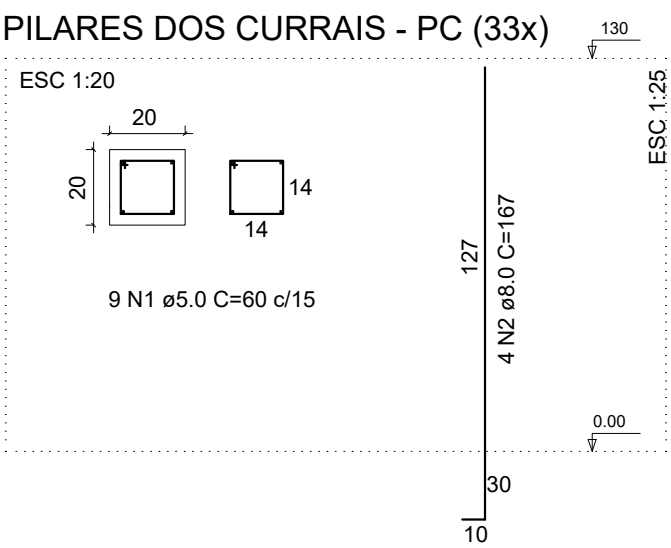

RESPONSÁVEL TÉCNICO:				
PROPRIETÁRIO:				
PRANCHA 5/6		PREFEITURA MUNICIPAL DE COREMAS – PB		
		PROJETO DE CONSTRUÇÃO DE MATADOURO – 9389922022		
		PROJETO ESTRUTURAL - CINTAS E PILARES CURRAL BOVINO		
	DATA	RESPONSÁVEL	RUBRICA	
DESENHO				
PROJETO			ÁREA DO TERRENO	ÁREA ÚTIL
CÓPIA			10,000,00 M²	971,43 M²
ESCALA:		DESENHO:	ÁREA CONSTRUÍDA	
1:125 1:20		LOCAÇÃO PILARES DETALHE PILARES	871,58 M²	
9389922022_Curral.Bovino_Est.Cintas.Pilares				