



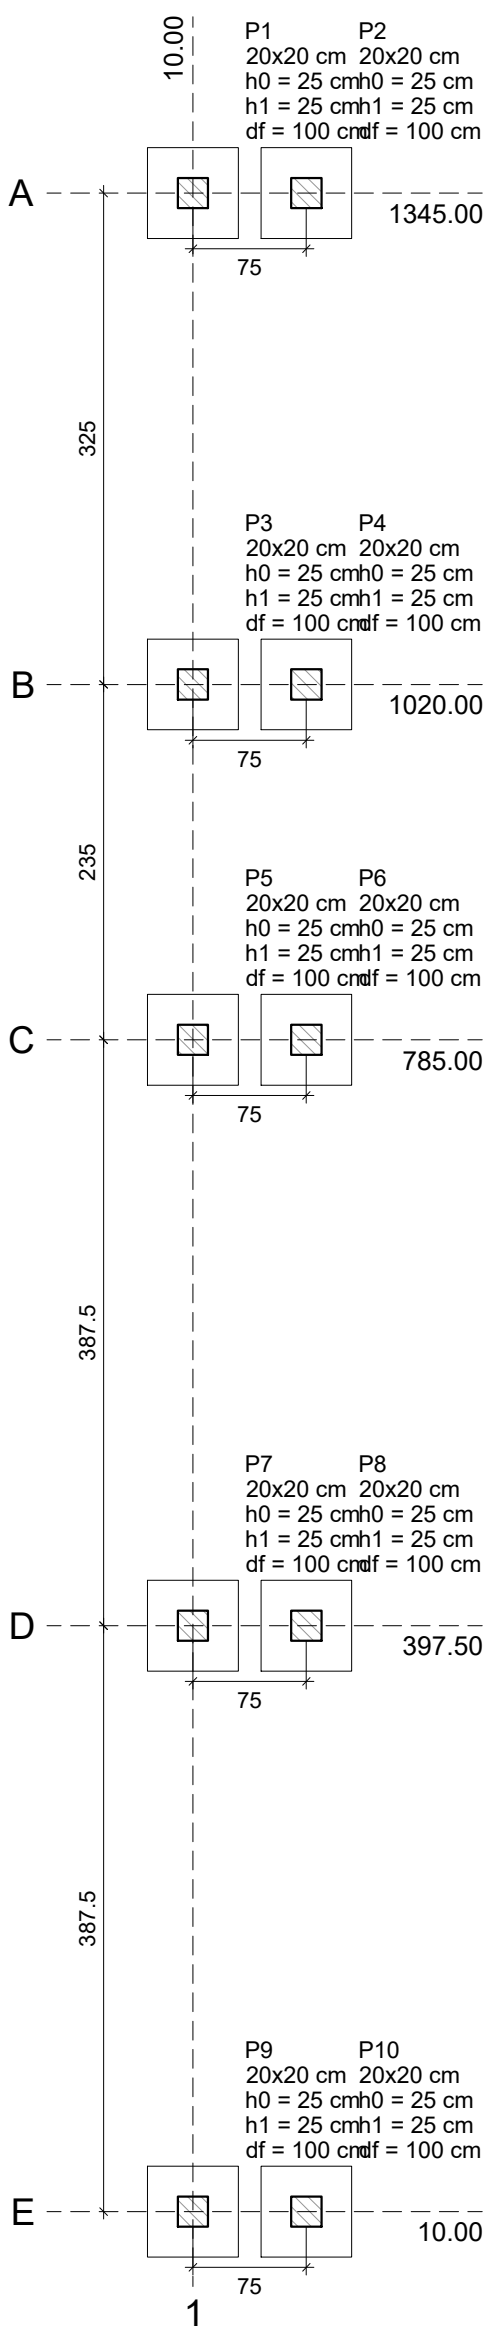


Locação Fundação – Curral bovino
escala 1/50

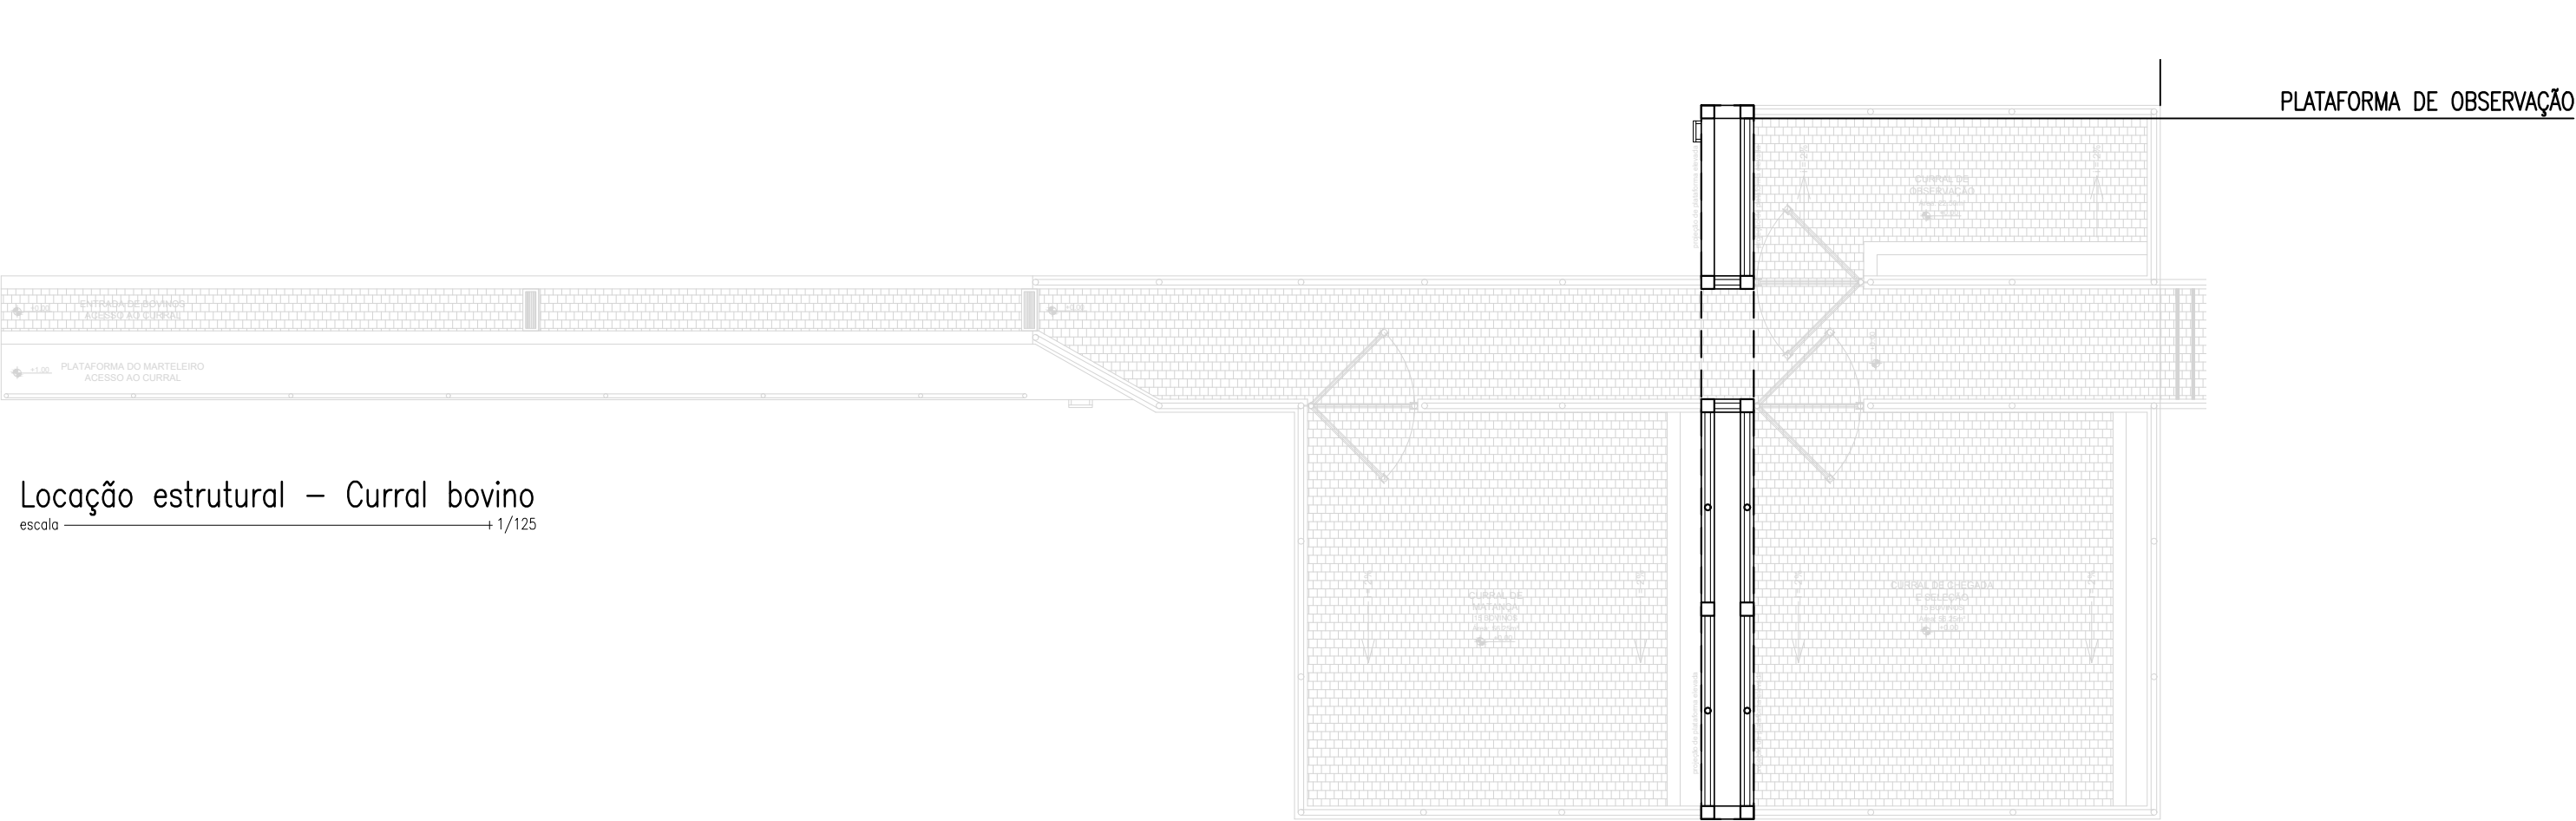

Locação estrutural – Curral bovino
escala 1/125


Pilar											Fundação				
Nome	Seção (cm)	X (cm)	Y (cm)	Carga Máx. (tf)	Carga Min. (tf)	Mx (kgf.m)	My (kgf.m)	Fx (tf)	Fy (tf)		Lado B (cm)	Lado H (cm)	h0 / ha (cm)	h1 / hb (cm)	df (cm)
P1	20x20	10.00	1345.00	0.9	0.6	100	100	0.1	0.1		60	60	25	25	100
P2	20x20	85.00	1345.00	0.9	0.6	100	100	0.1	0.1		60	60	25	25	100
P3	20x20	10.00	1020.00	1.4	1.0	100	100	0.1	0.1		60	60	25	25	100
P4	20x20	85.00	1020.00	1.4	1.0	100	100	0.1	0.1		60	60	25	25	100
P5	20x20	10.00	785.00	1.4	1.0	100	100	0.1	0.1		60	60	25	25	100
P6	20x20	85.00	785.00	1.4	1.0	100	100	0.1	0.1		60	60	25	25	100
P7	20x20	10.00	397.50	1.8	1.3	100	100	0.1	0.1		60	60	25	25	100
P8	20x20	85.00	397.50	1.8	1.3	100	100	0.1	0.1		60	60	25	25	100
P9	20x20	10.00	10.00	0.9	0.7	100	100	0.1	0.1		60	60	25	25	100
P10	20x20	85.00	10.00	0.9	0.7	100	100	0.1	0.1		60	60	25	25	100

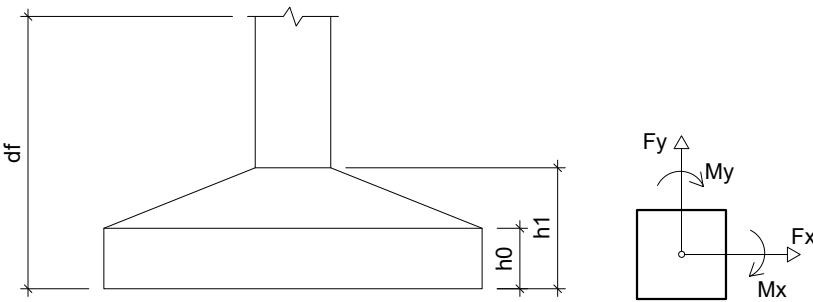

Detalhe estrutural – Curral bovino
escala 1/50

Locação no eixo X	
Coordenadas (cm)	Nome
10.00	P1, P3, P5, P7, P9
85.00	P2, P4, P6, P8, P10

Locação no eixo Y	
Coordenadas (cm)	Nome
1345.00	P1, P2
1020.00	P3, P4
785.00	P5, P6
397.50	P7, P8
10.00	P9, P10

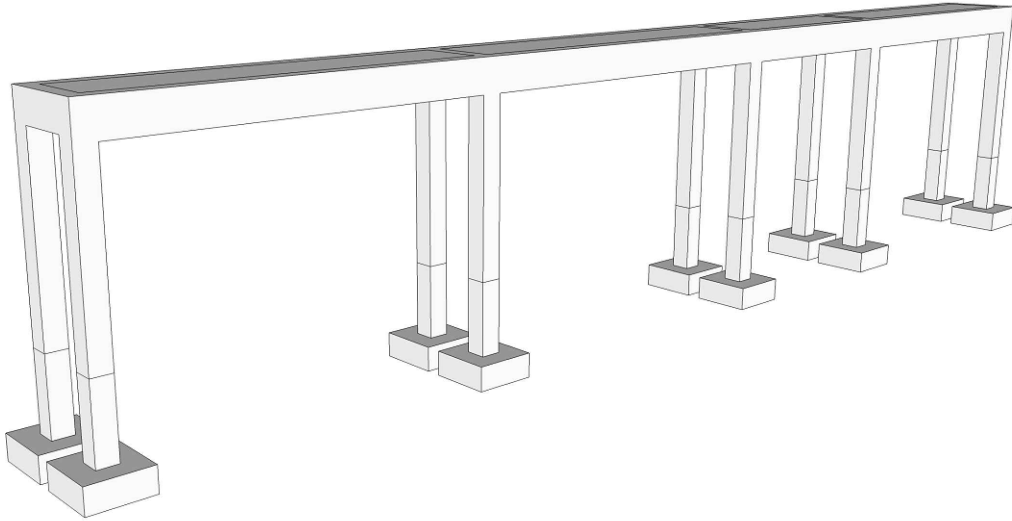

Maquete Estrutural 3D – Plataforma de observação do Curral Bovino
escala 1/50

RESPONSÁVEL TÉCNICO:

PROPRIETÁRIO:

PRANCHA		PREFEITURA MUNICIPAL DE COREMAS – PB			
1/6		PROJETO DE CONSTRUÇÃO DE MATADOURO – 9389922022			
		PROJETO ESTRUTURAL - PLATAFORMA DO CURRAL BOVINO - FUNDAÇÃO			
	DATA	RESPONSÁVEL		RUBRICA	
DESENHO					
PROJETO				ÁREA DO TERRENO	ÁREA ÚTIL
CÓPIA				10.000,00 M²	971,43 M²
ESCALA:		DESENHO:		ÁREA CONSTRUIDA	871,58 M²
1:50 1:50 1:20 5:ESC		LOCAÇÃO FUNDAÇÃO FORMA BALDRAMÉ DETALHE ESTRUTURAL MAQUETE ESTRUTURAL 3D - PLATAFORMA			