



Forma da Plataforma – Curral bovino
escala 1/50

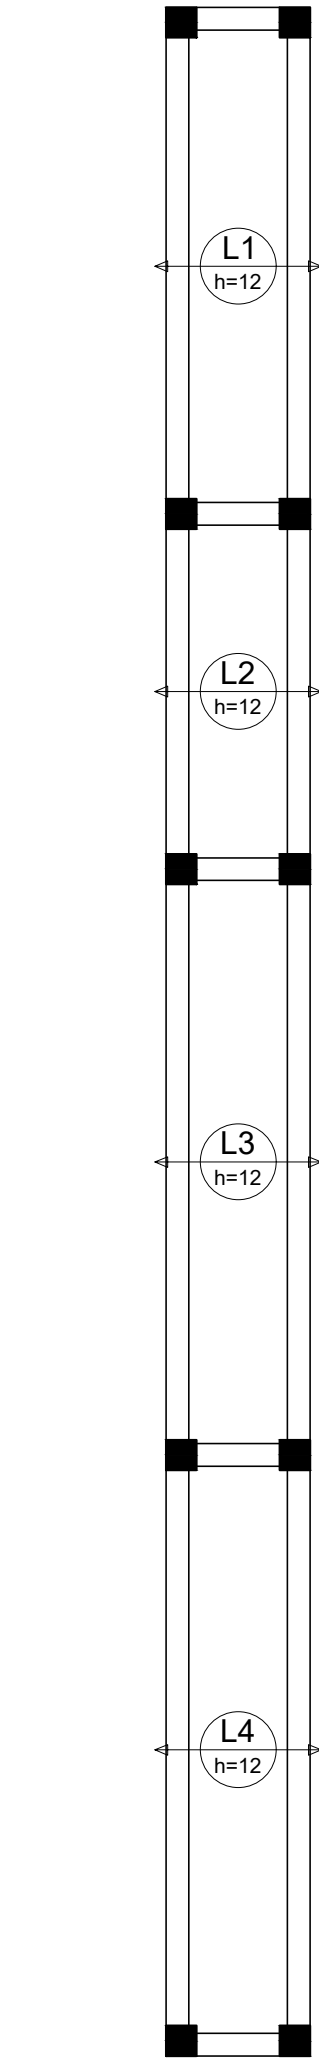

Armação positiva (eixo X)
da Plataforma – Curral bovino
escala 1/50

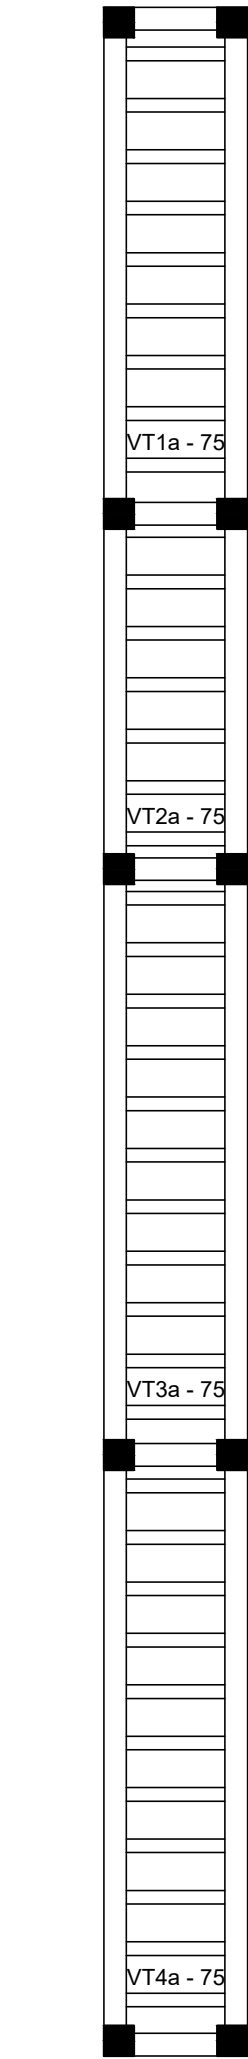

Planta da vigotas pré-moldadas
– Curral bovino
escala 1/50

Legenda dos Pilares	
	Pilar que morre
	Pilar que passa
	Pilar que nasce
	Pilar com mudança de seção


Lajes						Sobrecarga (kgf/m²)		
Nome	Tipo	Altura (cm)	Elevação (cm)	Nível (cm)	Peso próprio (kgf/m²)	Adicional	Acidental	Localizada
L1	Treliçada 1D	12	0	215	259	0	200	-
L2	Treliçada 1D	12	0	215	259	0	200	-
L3	Treliçada 1D	12	0	215	259	0	200	-
L4	Treliçada 1D	12	0	215	259	0	200	-

Blocos de enchimento						
Detalhe	Tipo	Nome	Dimensões(cm)			Quantidade
			hb	bx	by	
1	Lajota cerâmica	B8/25/20	8	25	20	111

Vigas			
Nome	Seção (cm)	Elevação (cm)	Nível (cm)
V1	15x30	0	215
V2	15x30	0	215
V3	15x30	0	215
V4	15x30	0	215
V5	15x30	0	215
V6	15x35	0	215
V7	15x35	0	215

Pilares			
Nome	Seção (cm)	Elevação (cm)	Nível (cm)
P1	20 x 20	0	215
P2	20 x 20	0	215
P3	20 x 20	0	215
P4	20 x 20	0	215
P5	20 x 20	0	215
P6	20 x 20	0	215
P7	20 x 20	0	215
P8	20 x 20	0	215
P9	20 x 20	0	215
P10	20 x 20	0	215

Características dos materiais	
fck (kgf/cm²)	Ecs (kgf/cm²)
250	238000

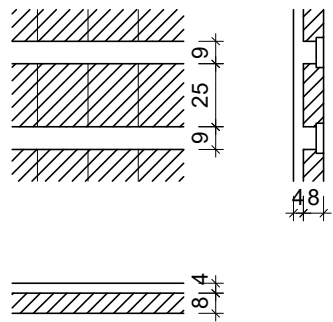

Detalhe laje – Curral bovino
escala 1/50

Documento assinado digitalmente
gov.br MICHAEL JACKSON MAMEDE SOUZA
Data: 11/03/2024 15:41:12-0300
Verifique em <https://validar.RF.gov.br>

RESPONSÁVEL TÉCNICO:

PROPRIETÁRIO:

PRANCHA		PREFEITURA MUNICIPAL DE COREMAS – PB			
3/6		PROJETO DE CONSTRUÇÃO DE MATADOURO – 9389922022			
		PROJETO ESTRUTURAL - PLATAFORMA DO CURRAL BOVINO - PASSARELA			
	DATA	RESPONSÁVEL		RUBRICA	
DESENHO					
PROJETO				ÁREA DO TERRENO	ÁREA ÚTIL
CÓPIA				10.000,00 M²	971,43 M²
ESCALA:		DESENHO:		ÁREA CONSTRUIDA	
1 : 50 1 : 50 1 : 50 1 : 30		FORMA PLATAFORMA ARMAÇÃO POSITIVA (EIXO X) VIGOTAS PRÉ-MOLDADAS DETALHE LAJE PRÉ-MOLDADA		871,58 M²	