


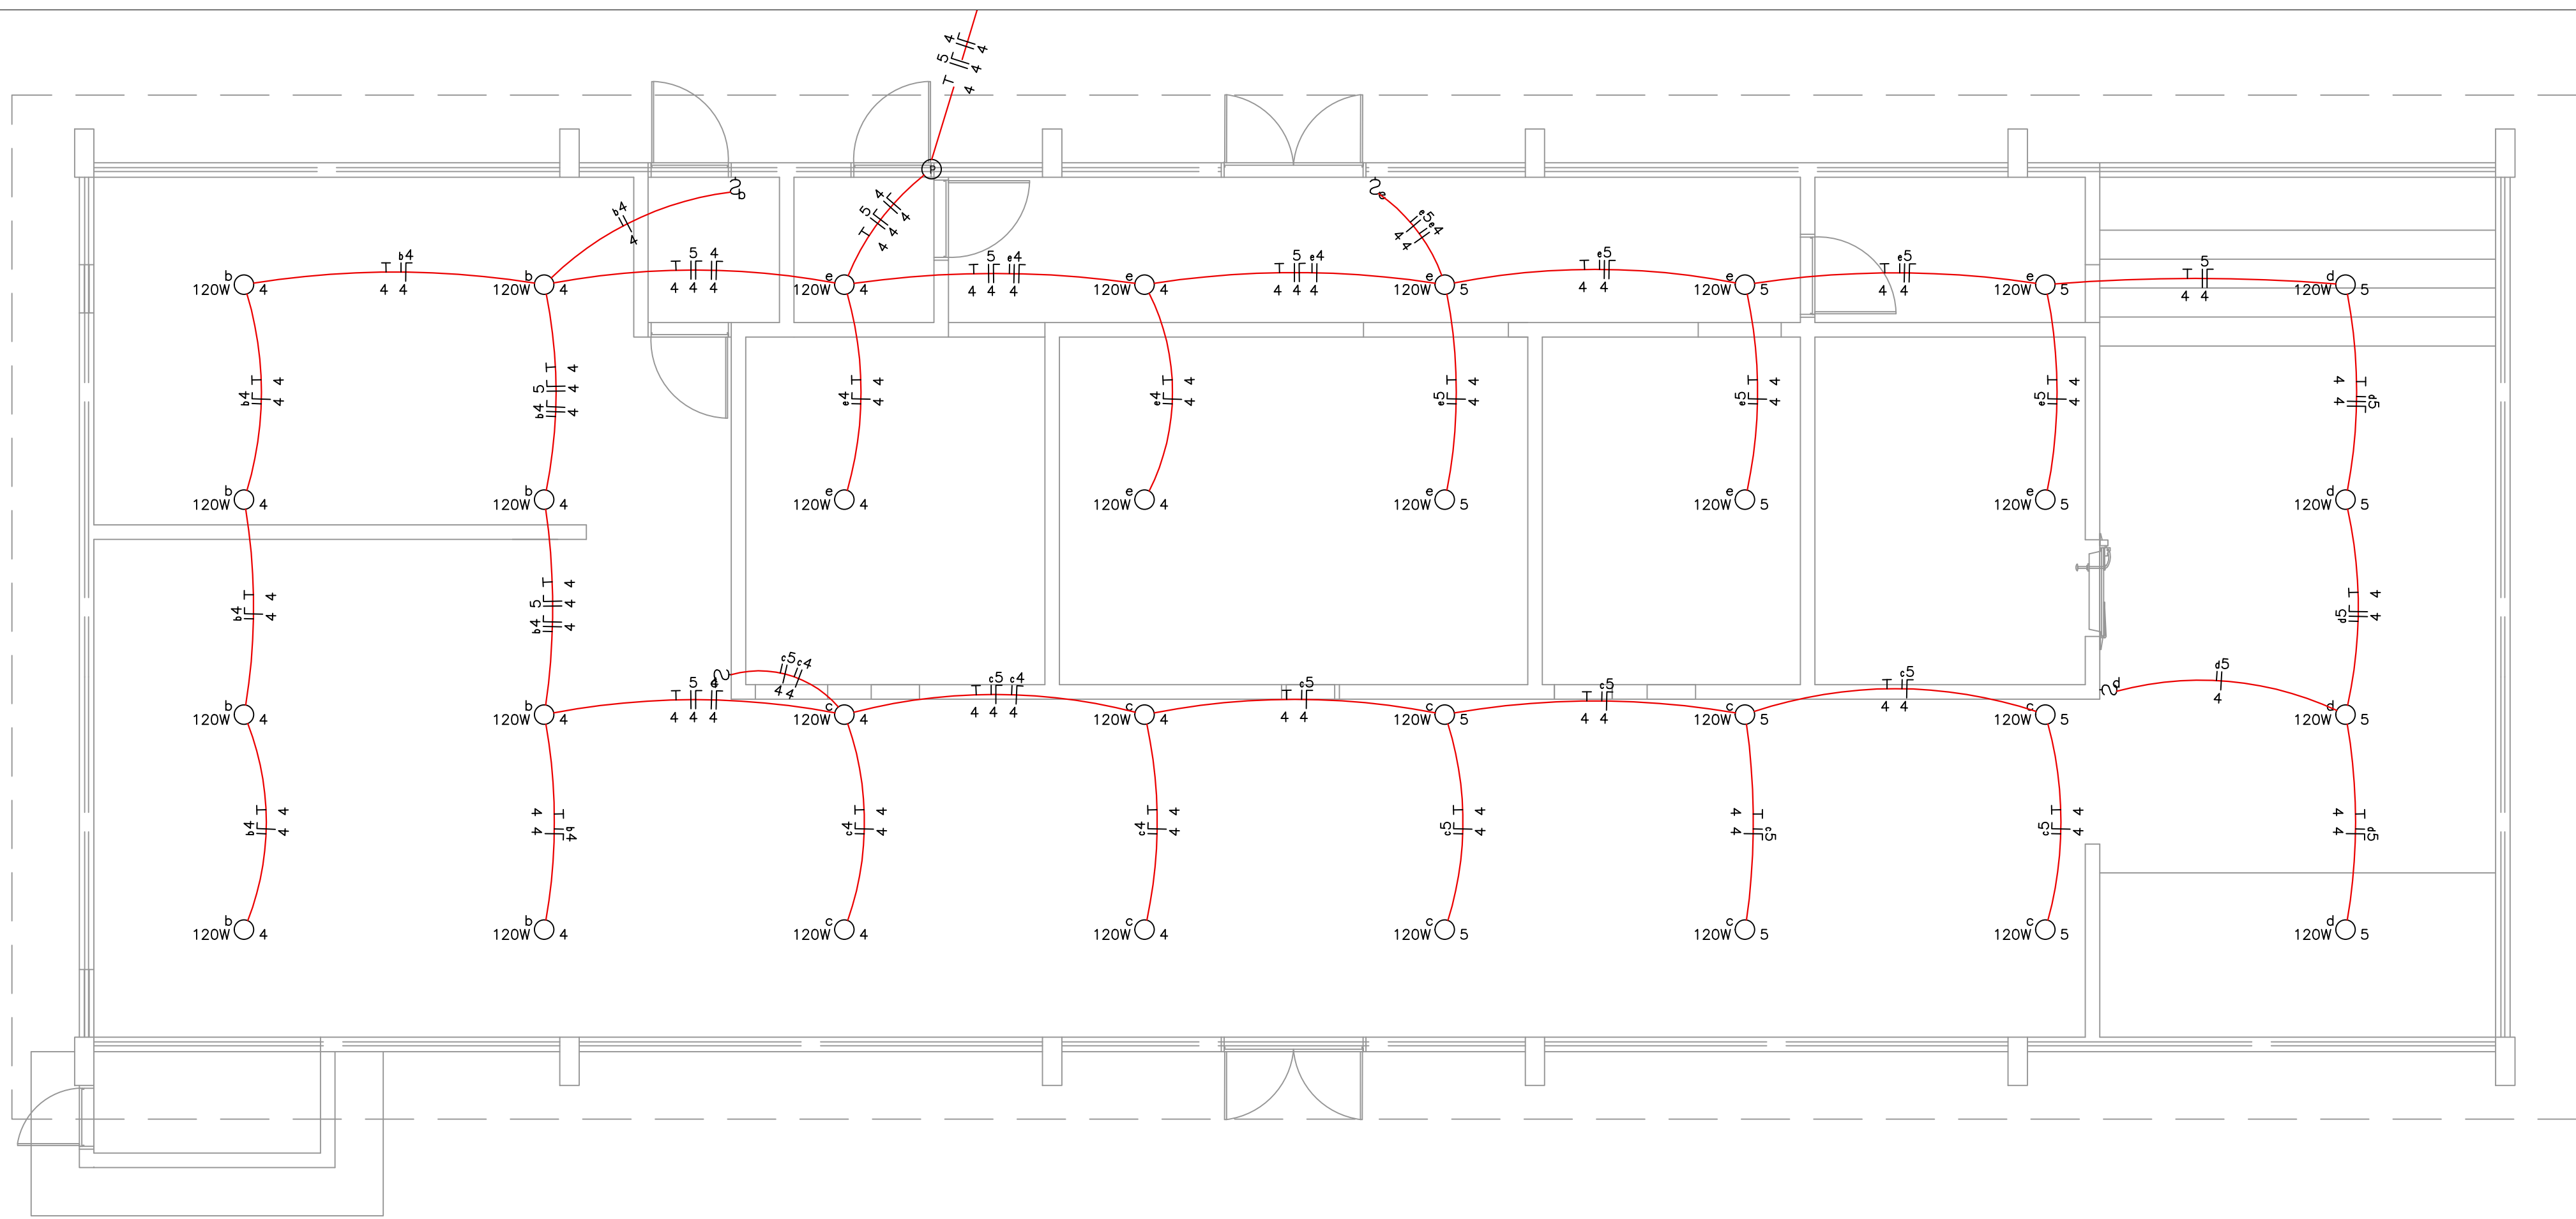


Planta Baixa Elétrica - Galpão

escala 1/50

NBR-5444				
Num.	Quant.	Und.	Dimensão	Descrição
1	1	pc		Caixa de passagem na parede 2x4
2	32	pc		Caixa Octogonal 3" x 3" pvc
3	17	pc	1"	Curvo raspadel macho - Rígido
4	32	m	1"	Eletroduto Rígido - Parede
5	13,97	m	1"	Eletroduto Rígido - Piso
6	88,51	m	1"	Eletroduto Rígido - Teto
7	32	pc		Luminária de LED para Galpões 120W
8	34	pc		Luzo raspadel - Rígido
9	1	pc		Quadro Parcial de luz e força(24 mds)br


Interruptor com letra S				
Num.	Quant.	Und.	Dimensão	Descrição
1	4	pc		Caixa 2x4
2	4	pc		Interruptor simples

Fiação e Disposições de Fiação				
Num.	Quant.	Und.	Dimensão	Descrição
1	2	pc	1P10A	Disjuntor a seco - DN
2	14	pc	1P25A	Disjuntor a seco - DN
3	1	pc	3P125A	Disjuntor a seco - DN
4	140,87	m	4 mm2	Fio cabo 750 V - PVC - Fase
5	144,44	m	4 mm2	Fio cabo 750 V - PVC - Neutro
6	118,76	m	4 mm2	Fio cabo 750 V - PVC - Retorno
7	88,61	m	4 mm2	Fio cabo 750 V - PVC - Terra

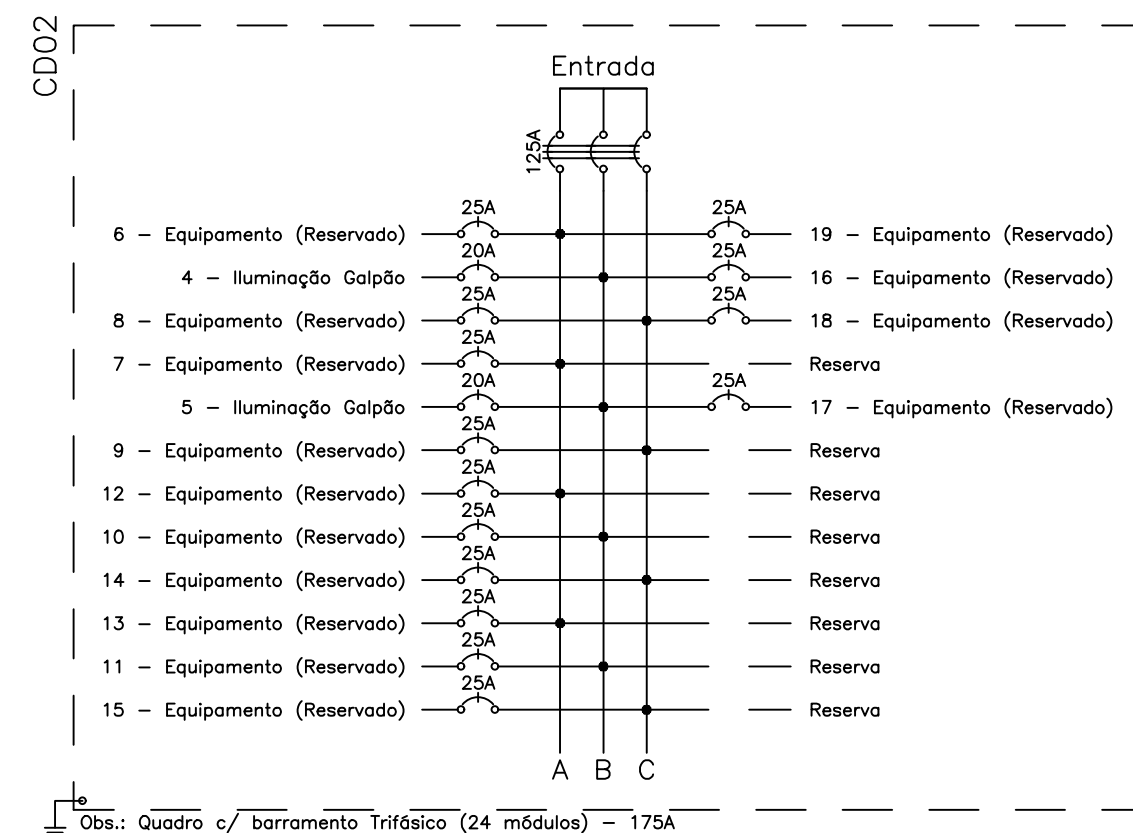

Obs.: Quadro c/ barramento trifásico (24 módulos) - 175A

Quadro de Cargas												
CDD2												
Ord.	Descrição	Inteligência	Id. Sim	Pot. W	Pot. VA	Def. (Reservado)	Fat. Def.	Con. T	Fase	Pot. A	Def. A	Obs.
4	Iluminação Galpão	16		1600,0	1600,0	0,00	8,75	1	25A	2,5	B	Obs.
5	Iluminação Galpão	16		1600,0	1600,0	0,00	8,75	1	25A	2,5	B	Obs.
6	Equipamento (Reservado)	1		3300,0	4125,0	0,00	16,75	1	25A	4,0	A	Obs.
7	Equipamento (Reservado)	1		3300,0	4125,0	0,00	16,75	1	25A	4,0	A	Obs.
8	Equipamento (Reservado)	1		3300,0	4125,0	0,00	16,75	1	25A	4,0	C	Obs.
9	Equipamento (Reservado)	1		3300,0	4125,0	0,00	16,75	1	25A	4,0	C	Obs.
10	Equipamento (Reservado)	1		3300,0	4125,0	0,00	16,75	1	25A	4,0	B	Obs.
11	Equipamento (Reservado)	1		3300,0	4125,0	0,00	16,75	1	25A	4,0	B	Obs.
12	Equipamento (Reservado)	1		3300,0	4125,0	0,00	16,75	1	25A	4,0	A	Obs.
13	Equipamento (Reservado)	1		3300,0	4125,0	0,00	16,75	1	25A	4,0	A	Obs.
14	Equipamento (Reservado)	1		3300,0	4125,0	0,00	16,75	1	25A	4,0	C	Obs.
15	Equipamento (Reservado)	1		3300,0	4125,0	0,00	16,75	1	25A	4,0	C	Obs.
16	Equipamento (Reservado)	1		3300,0	4125,0	0,00	16,75	1	25A	4,0	B	Obs.
17	Equipamento (Reservado)	1		3300,0	4125,0	0,00	16,75	1	25A	4,0	B	Obs.
18	Equipamento (Reservado)	1		3300,0	4125,0	0,00	16,75	1	25A	4,0	C	Obs.
19	Equipamento (Reservado)	1		3300,0	4125,0	0,00	16,75	1	25A	4,0	A	Obs.
Total		32		14	3060,0	1780,0						
Atenuação: 0-4,8m 01-2%						3027,4	1875,0	0,00	8,81	3,88	3	125A 50 ABC -
				Potência Demandada: 100K (50040,0 W) (61590,0 VA)								
				Corrente nos Fases: Iph=15,8 A Iph=15,8 A Iph=15,8 A								

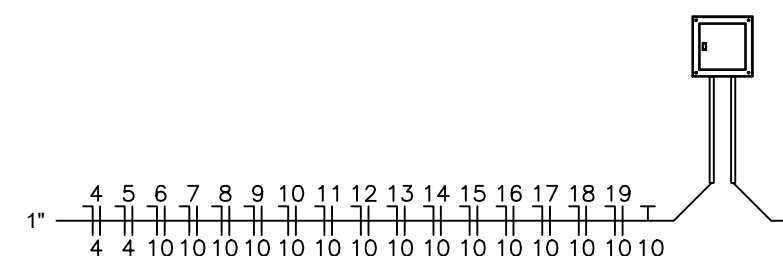

Vista do Quadro

escala 1/50

LEGENDA:

	- Arandela		- Relé Fotoelétrico
	- Interruptor duplo		- Disjuntor a seco - DIN 10A 1P
	- Interruptor simples		- Disjuntor a seco - DIN 10A 3P
	- Luminária LED 120w		- Disjuntor a seco - DIN 125A 3P
	- Luminária LED 25W		- Disjuntor a seco - DIN 25A 1P
	- Poste		- Eletroduto no Teto/ Aéreo
	- Tomada 130cm		- Eletroduto no Piso
	- Tomada baixa 30cm		- Neutro, Fase, Retorno, Terra
	- Tomada no piso		- Fio de cobre nu aéreo 6mm
	- Quadro Geral de luz e força	OBSERVAÇÕES	
	- Quadro Parcial de luz e força	10m: O eletroduto que não estiver indicado e dimensionamento, considerar como Ø17.	
	- Caixa de passagem na parede	10m: A fiação que não estiver indicada o dimensionamento, considerar como Ø10mm.	
	- Caixa de passagem no piso	10m: Cada poste terá uma caixa de Passagem e Reletoelétrico.	

Documentação assinada digitalmente
MICHAEL ANDRESON MANEIRA SOUSA
Data: 11/03/2024 09:23:39
Verifique em: https://validar.br.gov.br

RESPONSÁVEL TÉCNICO:				
PROPRIETÁRIO:				
FRANCHA		PREFEITURA MUNICIPAL DE COREMAS – PB		
2/3		PROJETO DE CONSTRUÇÃO DE MATADOURO – 9389922022		
		PROJETO ELÉTRICO		
DATA	RESPONSÁVEL		RUBRICA	
DESENHO				
PROJETO				
CÓPIA				
ESCALA:	DESENHO:		ÁREA DO TERRENO 10.000,00 m²	
1:175	PLANTA BAIXA ELÉTRICO - GALPÃO		ÁREA ÚTIL 971,43 m²	
1:150	VISTA DO QUADRO		ÁREA CONSTRUIDA 871,08 m²	
5/52C	DIAGRAMA UNIFILAR, QD DE CARGAS E LISTA DE MATERIAIS			
9980020202_ELEET				

00000002_2107