




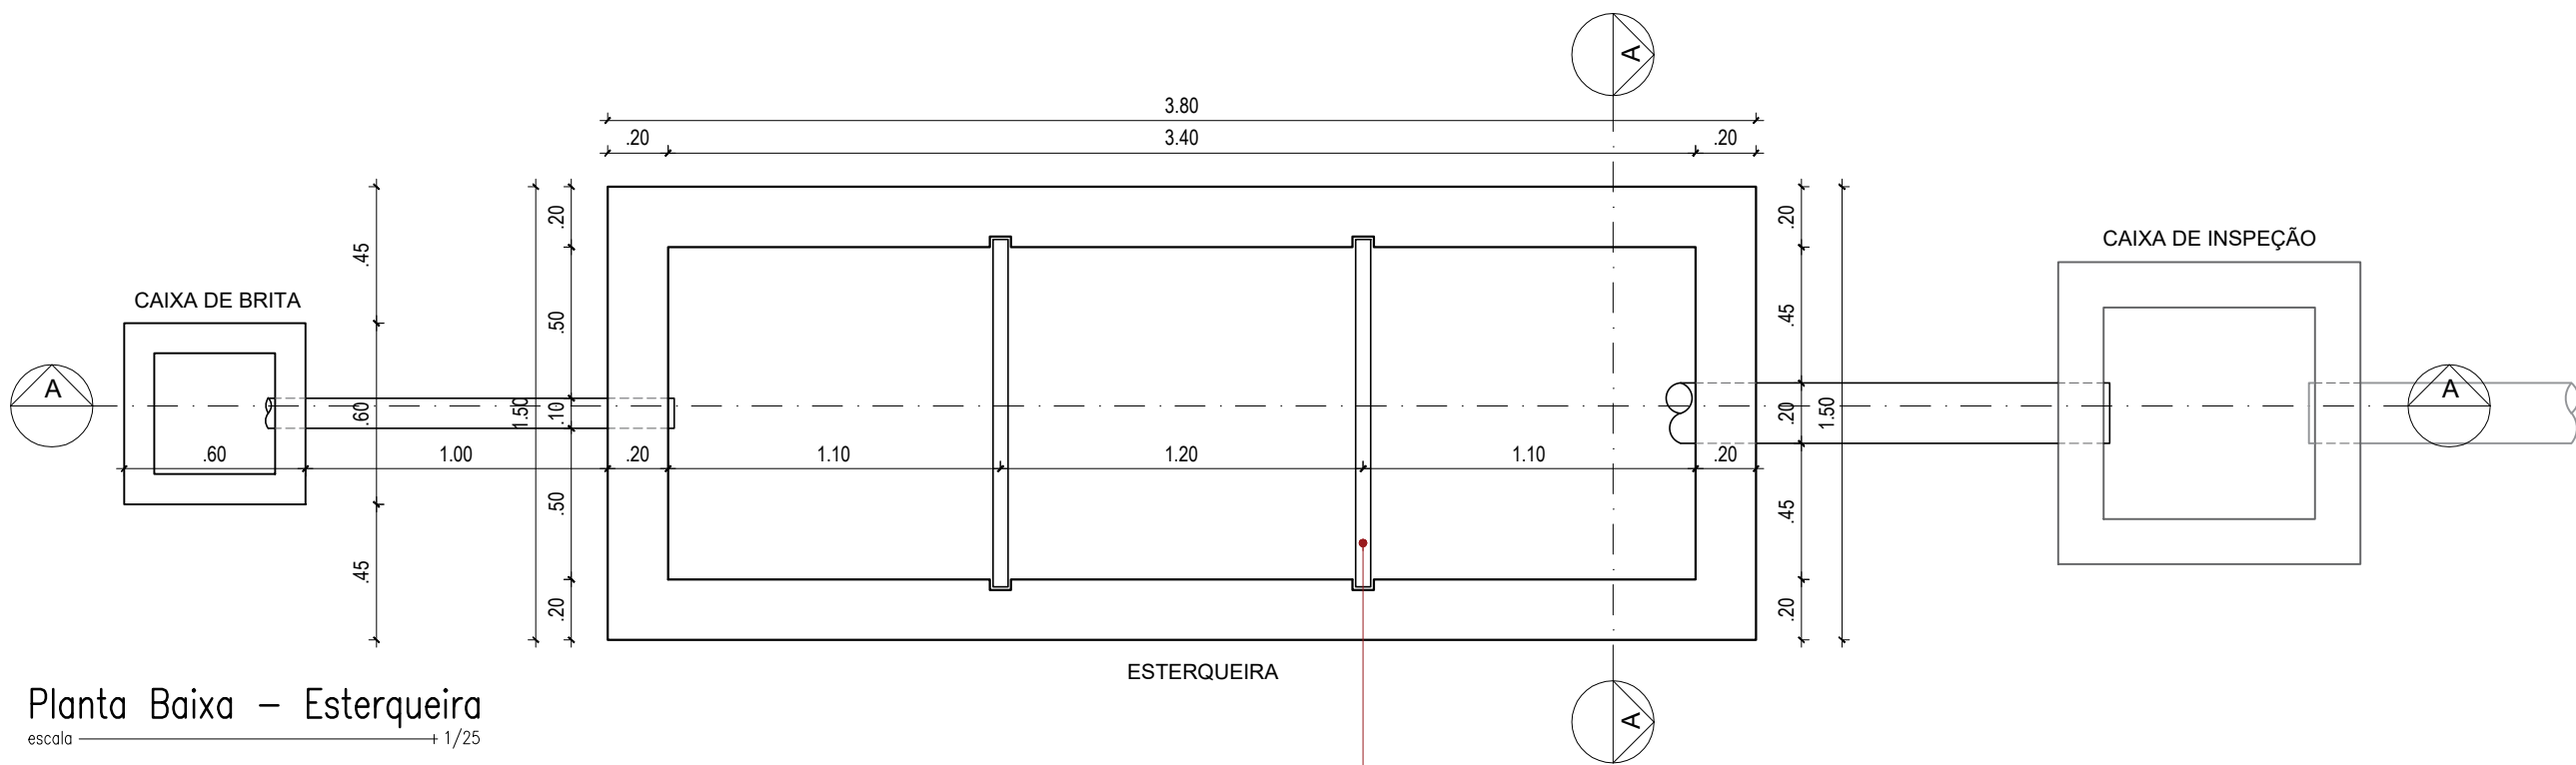


Planta Baixa – Esterqueira
escala 1/25

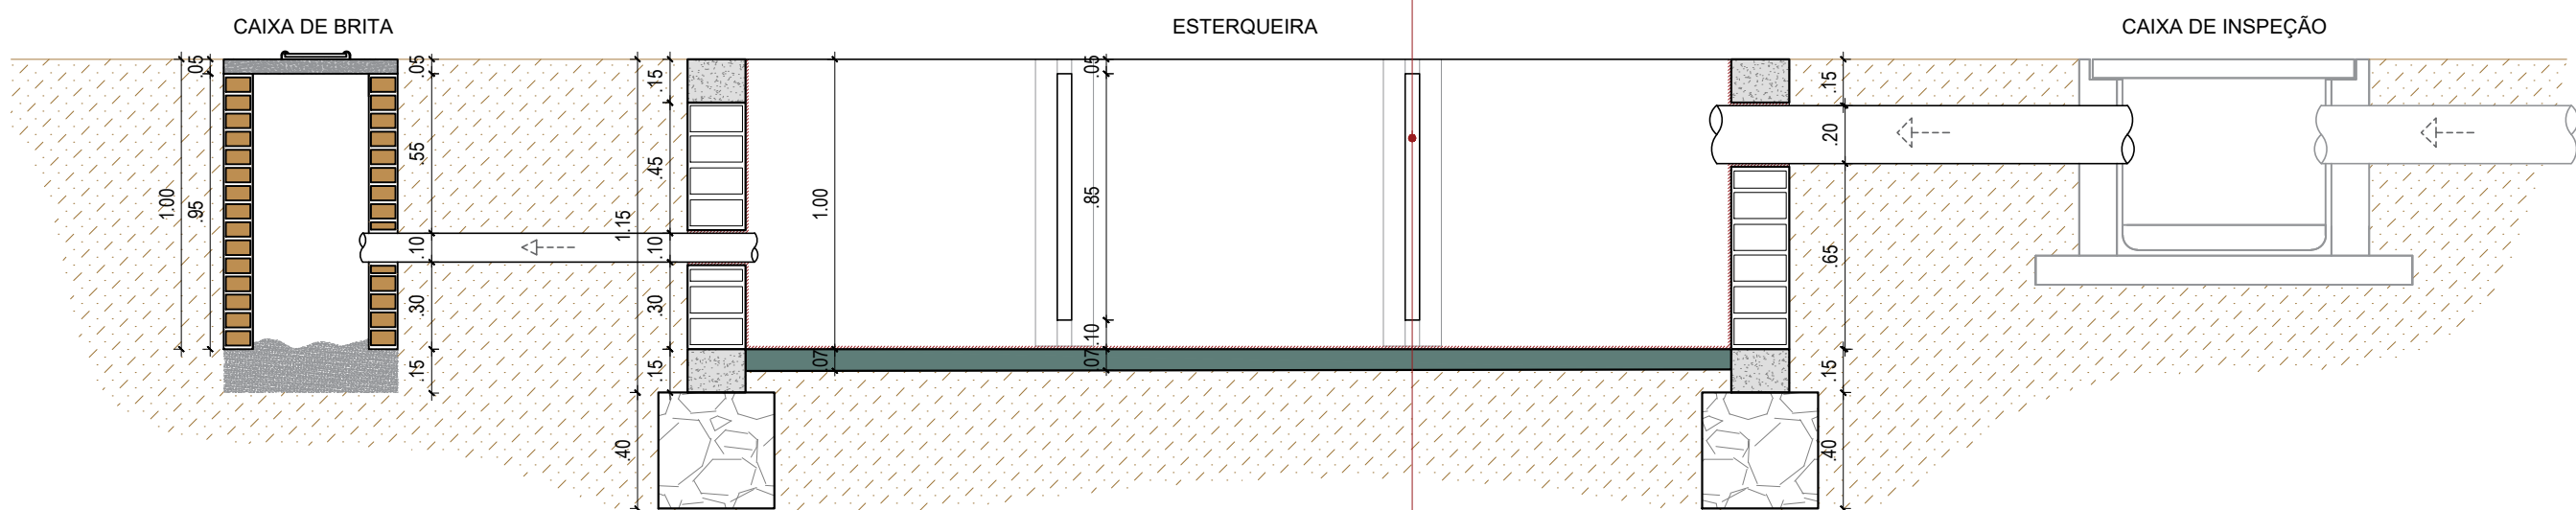


Corte Longitudinal – AA
escala 1/25

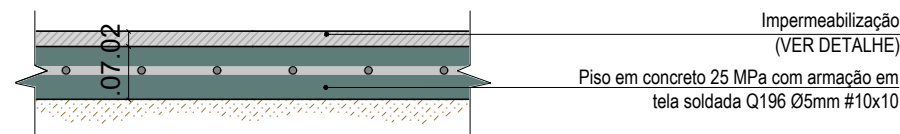

Detalhe – Piso de conc. com tela
escala 1/10

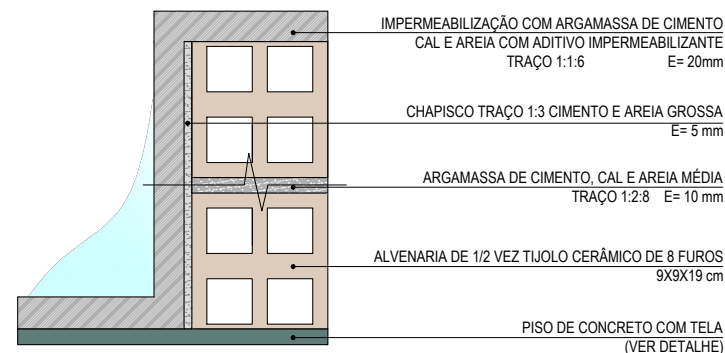

Detalhe – Impermeabilização
escala 1/5

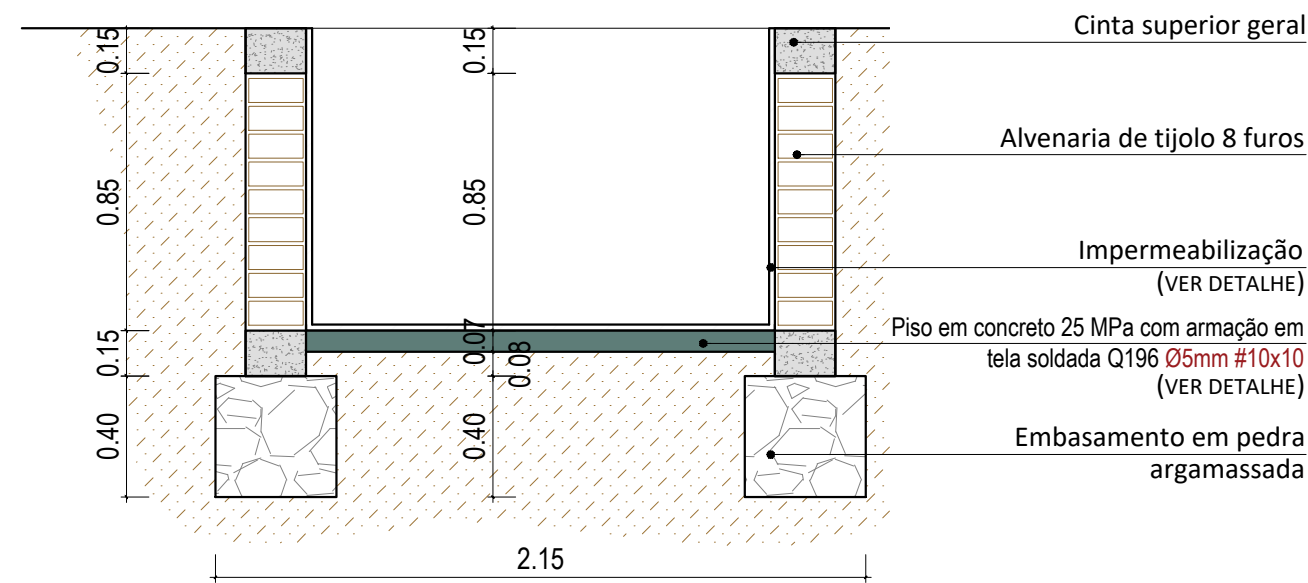

Corte BB – Transversal
escala 1/25

NOTA TÉCNICAS - PROJETO ARQUITETÔNICO ESTERQUEIRA

- NT 01: A esterqueira foi dimensionada para acumular todo o resíduo do curral durante uma jornada de trabalho. Devendo ser limpo manualmente no final da jornada de trabalho do dia, onde o resíduo deve ser lançado no solo como adubo. O resíduo da esterqueira não vai ser tratado na ETE.

RESPONSÁVEL TÉCNICO:

PROPRIETÁRIO:

PRANCHA 1/2		PREFEITURA MUNICIPAL DE COREMAS – PB			
		PROJETO DE CONSTRUÇÃO DE MATADOURO – 9389922022			
		PROJETO ARQUITETÔNICO – ESTERQUEIRA			
	DATA	RESPONSÁVEL		RUBRICA	
DESENHO					
PROJETO				ÁREA DE TERRENO	ÁREA CONSTRUÍDA
CÓPIA				10.000,00 M²	871,58 M²
ESCALA:		DESENHO:			
1/25		PLANTA BAIXA			
1/25		CORTE AA			
1/25		DET. CINTA / PILARES / FUNDAÇÃO			
1/10		DET. PISO DE CONCRETO			
1/5		DET. IMPERMEABILIZAÇÃO			

9389922022_Esterqueira

9389922022_Esterqueira