



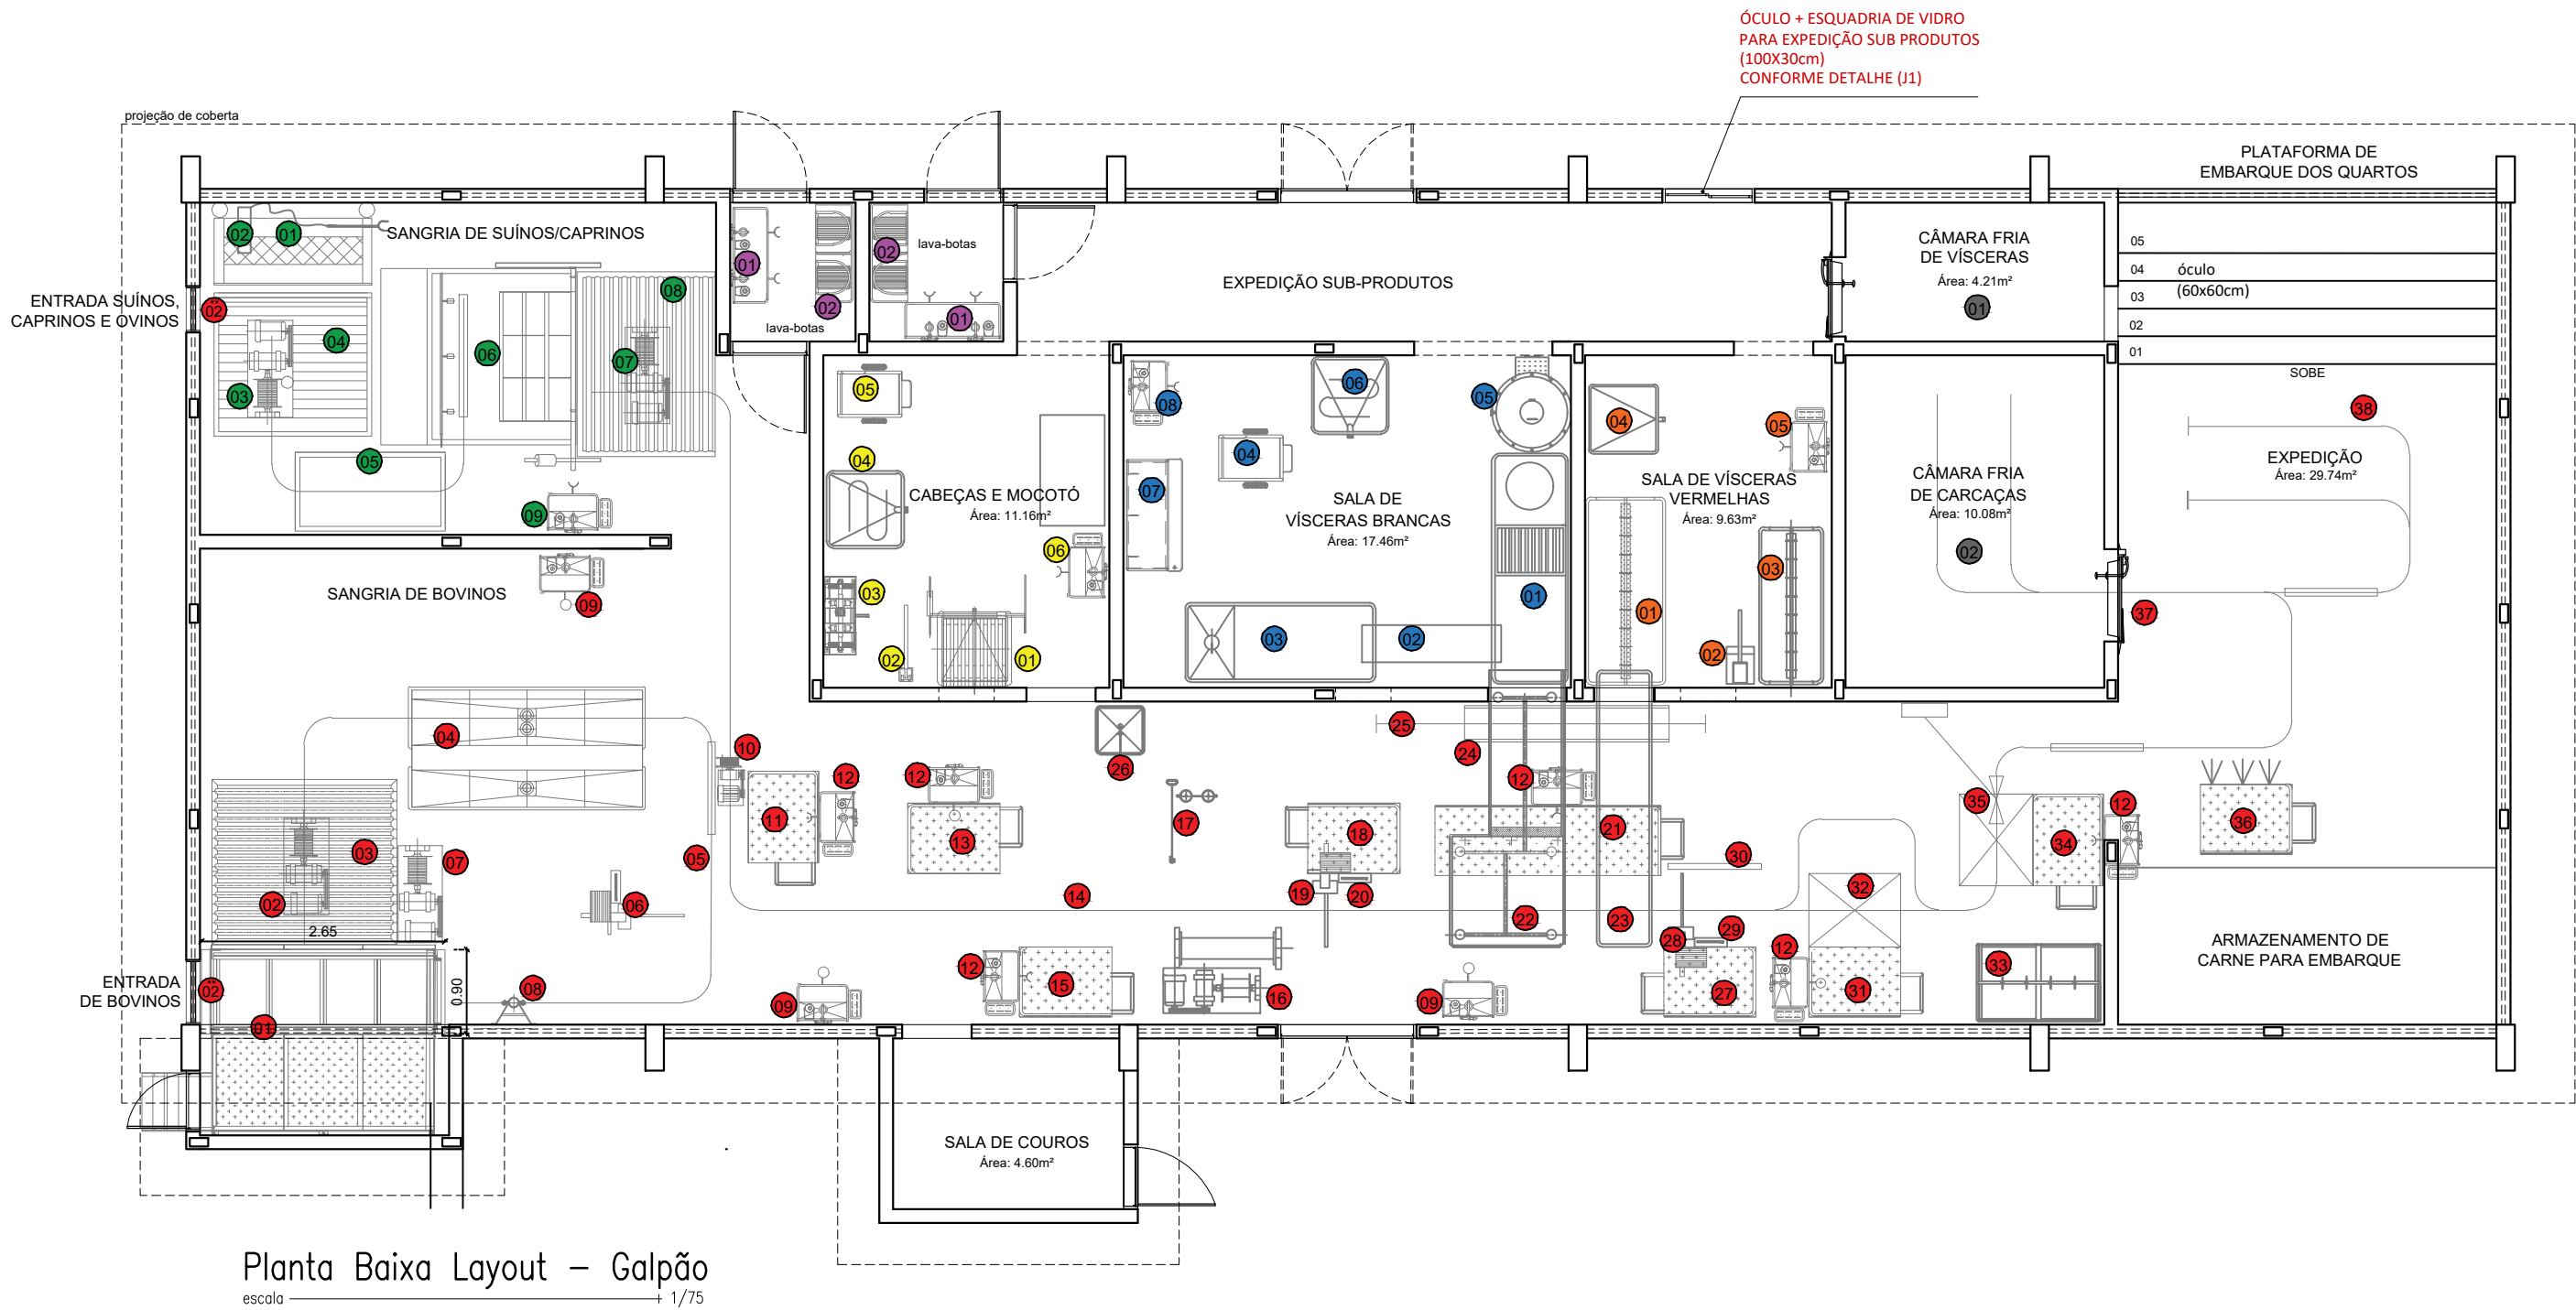

SALA DE ABATE BOVINO	SALA DE ABATE SUÍNO
01 - BOX DE ATORDOAMENTO 02 - GUINCHO PARA SANGRIA BOVINA 03 - GRADE DE DESLIZAMENTO 04 - CANALETA DE SANGRIA BOVINA 05 - TRILHAMENTO AÉREO PARA SANGRIA COM DESCIDA 06 - SERRA DE CHIFRES COM ESTERILIZADOR 07 - GUINCHO PARA ACIDENTADOS 08 - ELEVADOR HIDRÁULICO DE CARRETIHAS 09 - LAVATÓRIO TIPO PAREDE COM ESTERILIZADOR 10 - GUINCHO PARA TRANSPASSE 11 - PLATAFORMA PARA TRANSPASSE 12 - LAVATÓRIO TIPO PLATAFORMA COM ESTERILIZADOR 13 - PLATAFORMA PARA ABERTURA DE CARÇA 14 - TRILHAMENTO AÉREO PARA ESFOLA E EVISCERAÇÃO 15 - PLATAFORMA PARA ESFOLA DAS COSTAS 16 - GUINCHO COM ROLETE PARA RETIRADA DE COURO 17 - DESLOCADOR DE ESOPAGO COM ESTERILIZADOR 18 - PLATAFORMA PARA SERRA DE PEITO 19 - SERRA DE PEITO 20 - ESTERILIZADOR PARA SERRA DE PEITO 21 - PLATAFORMA PARA EVISCERAÇÃO 22 - MESA PARA EVISCERAÇÃO ABDOMINAL 23 - MESA PARA EVISCERAÇÃO TORÁCICA 24 - CALHA PARA RESPINGOS DE CABEÇAS 25 - TRILHO PARA DEPOSITO DE CABEÇAS 26 - BOX PARA LAVAR CABEÇAS 27 - PLATAFORMA MÓVEL PARA SERRA DE CARÇAÇAS 28 - SERRA DE CARÇAÇAS 29 - ESTERILIZADOR PARA SERRA DE CARÇAÇAS 30 - ANTEPARO PARA SERRA DE CARÇAÇAS 31 - PLATAFORMA PARA INSPEÇÃO 32 - BANDEJA COLETORA DE RESÍDUOS 33 - MESA COM BANDEJAS PARA INSPEÇÃO FINAL 34 - PLATAFORMA PARA CORTE DOS QUARTOS 35 - BALANÇA AÉREA 36 - PLATAFORMA PARA LAVAGEM DE CARÇAÇAS 37 - TRILHAMENTO AÉREO PARA CÂMARA DE RESFRIAMENTO 38 - TRILHAMENTO AÉREO PARA TENDAL DE EMBARQUE	01 - BOX DE INSENSIBILIZAÇÃO SUÍNA 02 - INSENSIBILIZADOR SUÍNO 03 - GUINCHO PARA SANGRIA BOVINA 04 - GRADE DE DESLIZAMENTO 05 - TRILHAMENTO AÉREO PARA SANGRIA COM DESCIDA 06 - TANQUE PARA ESCALDAR SUÍNOS 07 - GUINCHO PARA ELEVAR SUÍNOS 08 - MESA PARA RETOQUES 09 - LAVATÓRIO TIPO PEDESTAL COM ESTERILIZADOR
BUCHARIA E TRIPARIA	
01 - MESA PARA RECEBER E ABRIR BUCHOS 02 - CALHA PARA TRIPAS 03 - MESA PARA ESVAZIAR TRIPAS 04 - CARRINHO PARA TRANSPORTE DE RESÍDUOS 05 - MÁQUINA PARA LAVAR BUCHOS 06 - TANQUE PARA ESCALDAR BUCHOS 07 - ESTIANTE PARA TOALETE DE BUCHOS 08 - LAVATÓRIO TIPO PAREDE COM ESTERILIZADOR	
SEÇÃO DE MIÚDOS E CABEÇAS	
01 - MESA PARA RECEPÇÃO DE MIÚDOS 02 - DESARTICULADOR DE MAXILAR 03 - MESA PARA RECEPÇÃO DE CABEÇAS 04 - TANQUE PARA RECEPÇÃO DE BUCHOS LIMPOS 05 - LAVATÓRIO TIPO PAREDE COM ESTERILIZADOR	
SEÇÃO DE MOCOTÔS	
01 - TANQUE PARA ESCALDAR MOCOTÔS 02 - ARRANCADOR DE CASCO 03 - MÁQUINA PARA DEPILAR MOCOTÔS 04 - TANQUE PARA CLARIFICAR MOCOTÔS 05 - CARRINHO PARA TRANSPORTE DE MOCOTÔS 06 - LAVATÓRIO TIPO PAREDE COM ESTERILIZADOR	
CÂMARAS FRIAS	
01 - CÂMARA FRIA DE VÍSCERAS 02 - CÂMARA FRIA DE CARÇAÇAS	ENTRADA SANITÁRIA
OUTROS EQUIPAMENTOS	
*01 - CALDEIRA 300KG **02 - PORTAS GUILHOTINA INCLUSIVE CURRAIS	

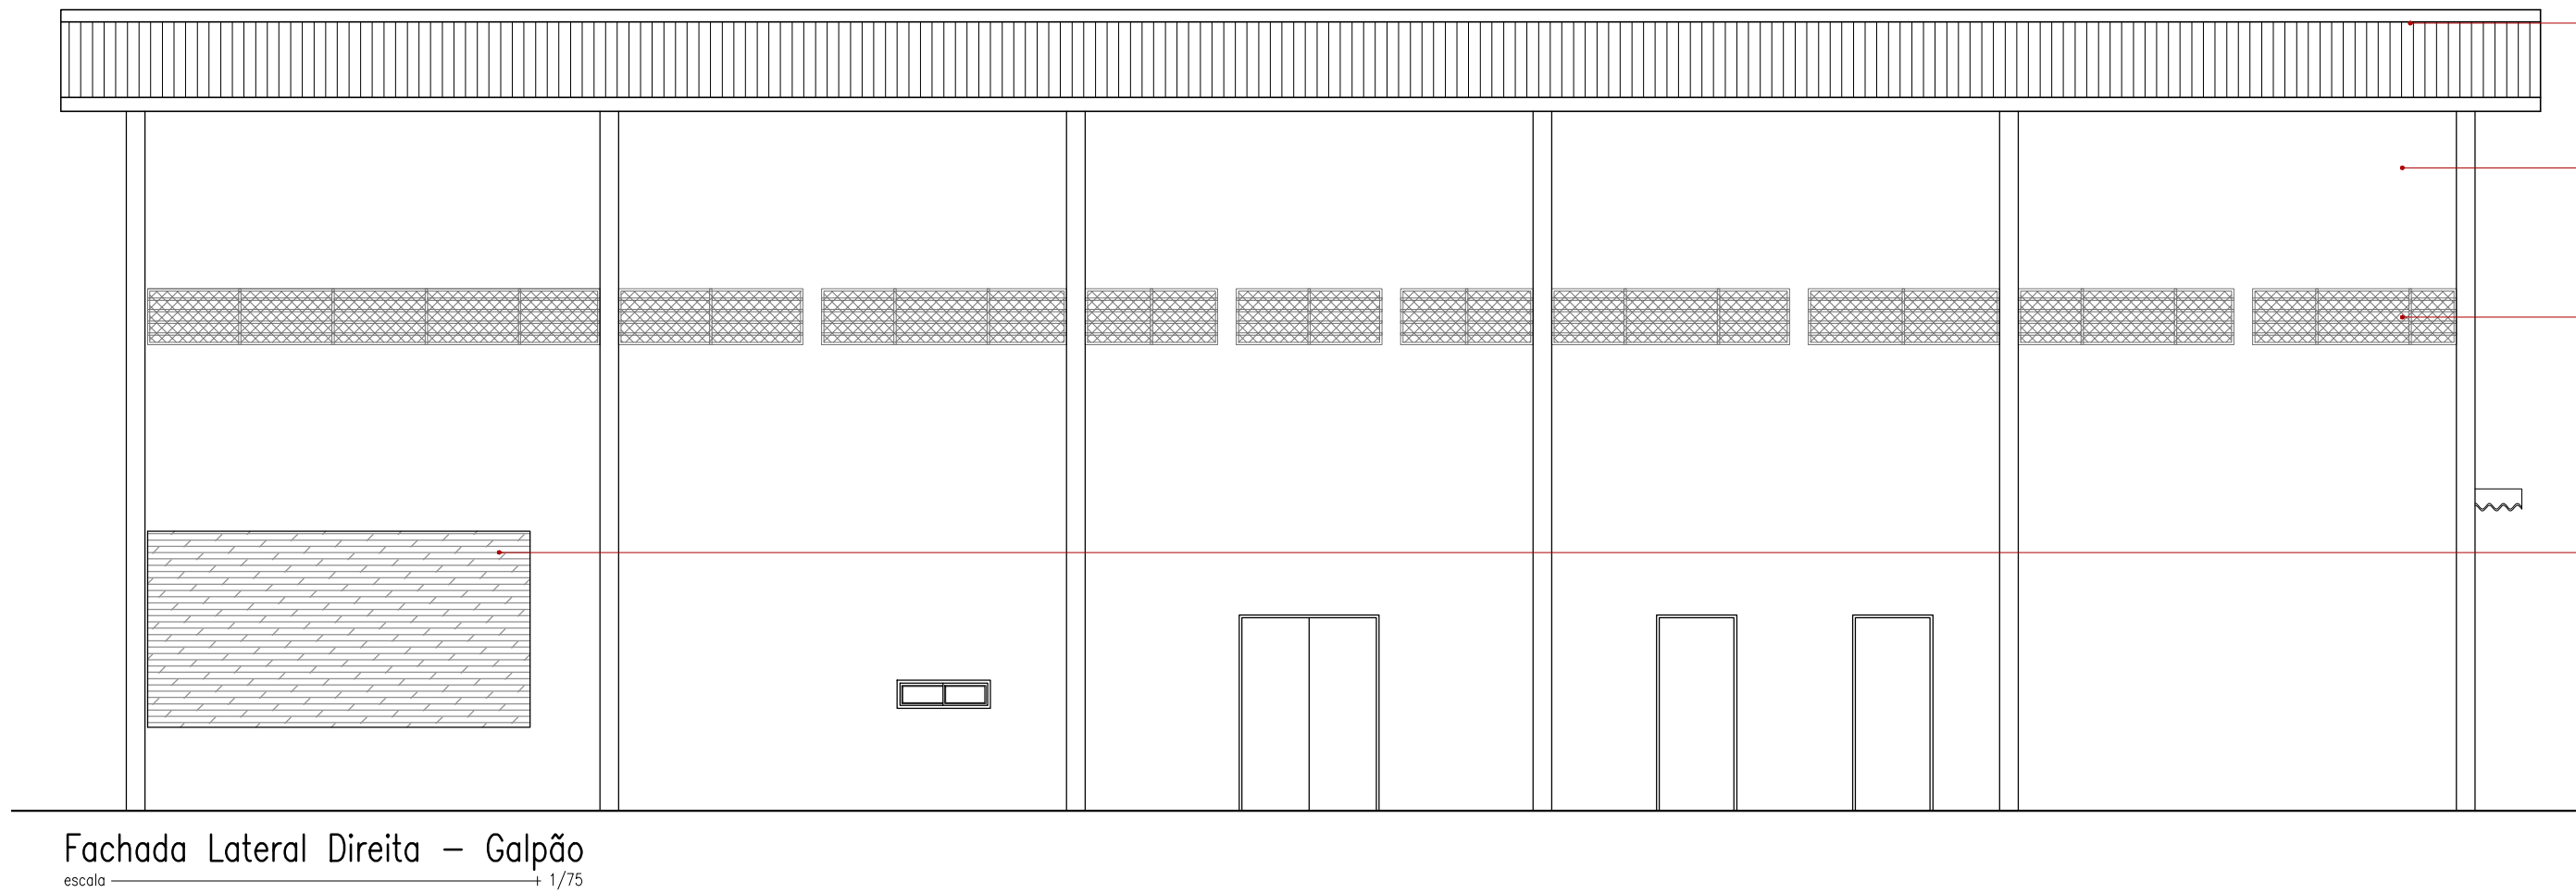

RESPONSÁVEL TÉCNICO:

PROPRIETÁRIO:

PRANCHA	PREFEITURA MUNICIPAL DE COREMAS – PB		
	PROJETO DE CONSTRUÇÃO DE MATADOURO – 9389922022		
	PROJETO ARQUITETÔNICO – GALPÃO		
	DATA	RESPONSÁVEL	RUBRICA
DESENHO			
PROJETO			
CÓPIA			
ESCALA:	DESENHO:		
1/75	PLANTA BAIXA – LAYOUT		
1/75	FACHADA LATERAL DIREITA		
		ÁREA DE TERRENO	ÁREA CONSTRUÍDA
		10.000,00 M²	871,58 M²