





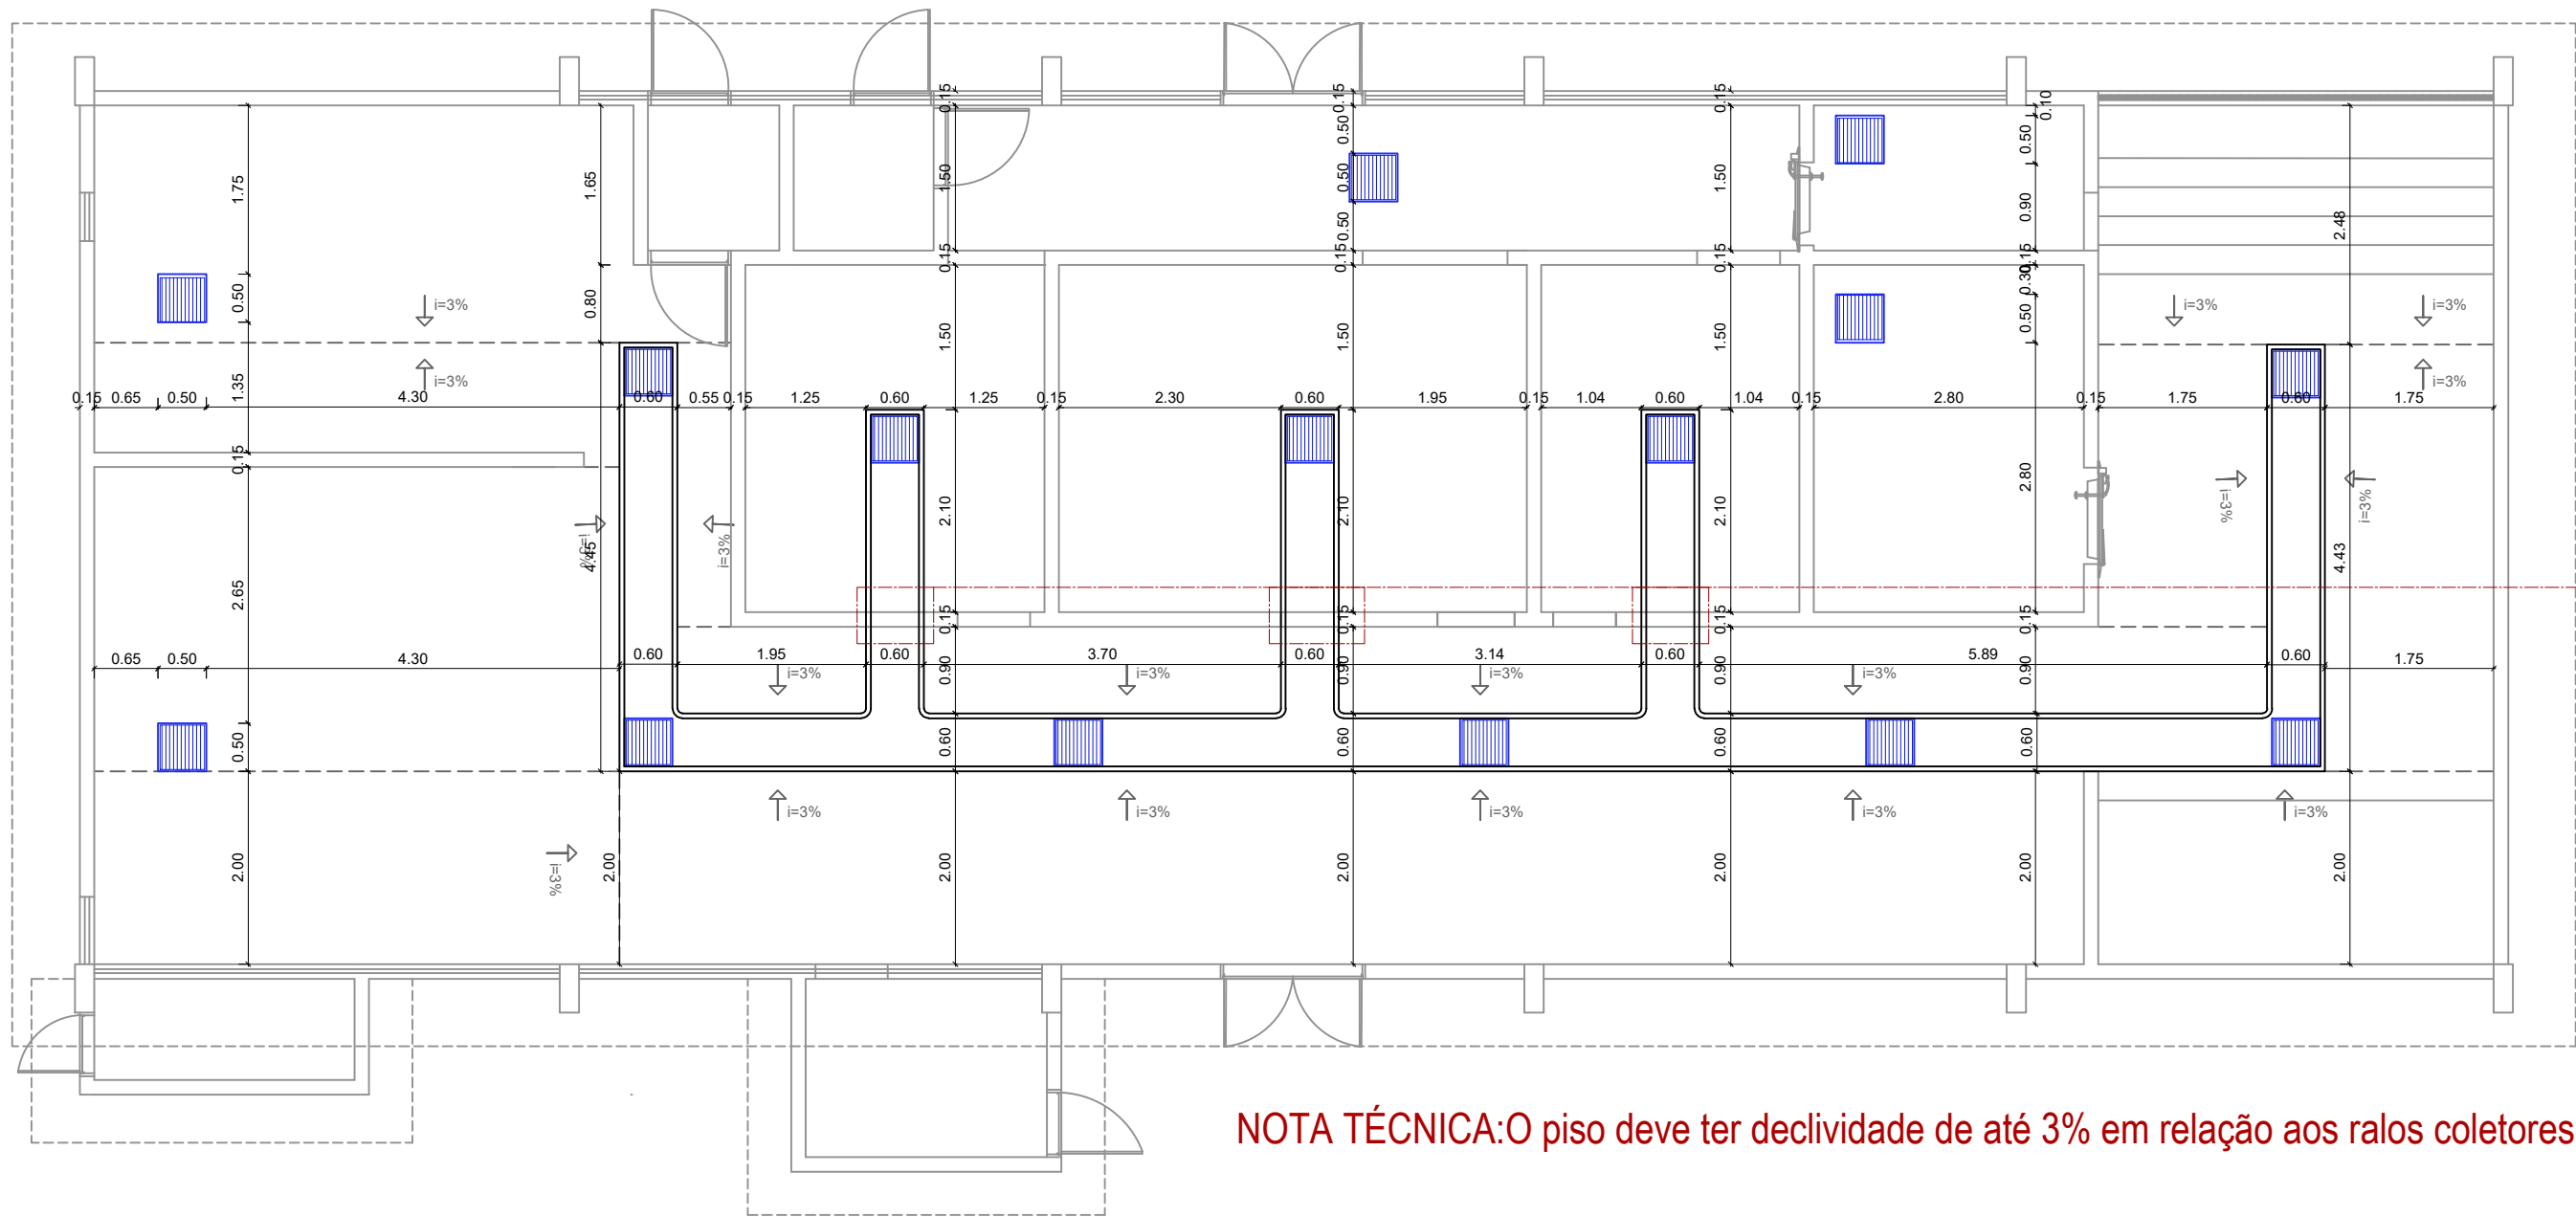


Planta Baixa Canaletas – Galpão
escala 1/75


NOTA TÉCNICA:O piso deve ter declividade de até 3% em relação aos ralos coletores

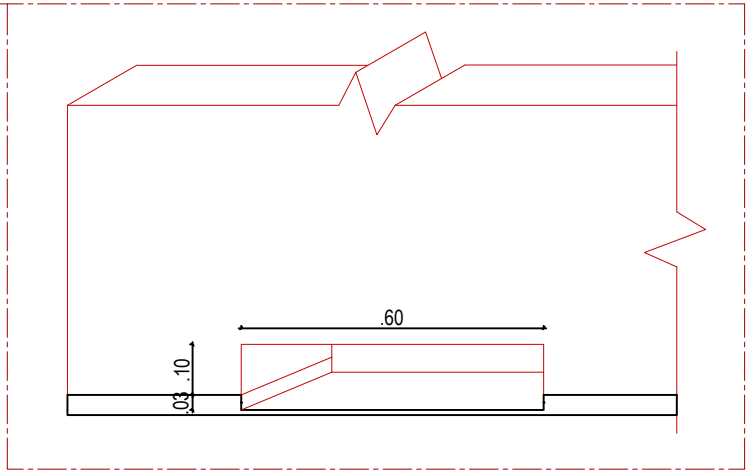


Detalhe – passagem sob paredes
escala 1/15

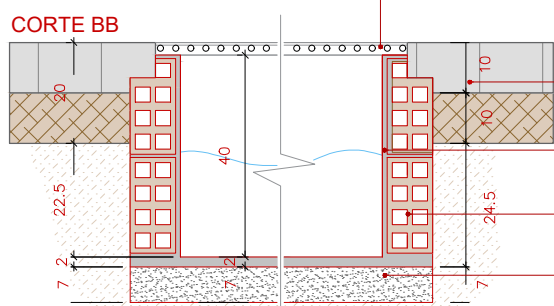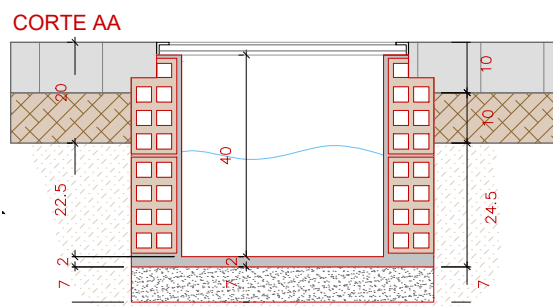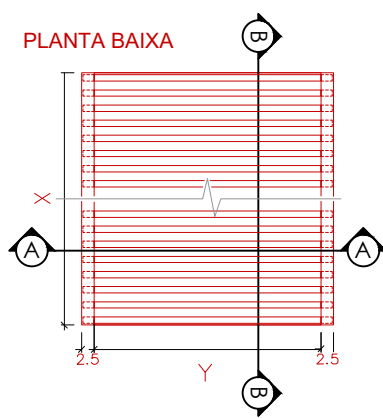

- Grade de ferro em barra de aço CA-25 Ø25mm
- Piso em paralelepípedo (VER DETALHE)
- Impermeabilização (VER DETALHE)
- Alvenaria de 1 vez tijolo de 8 furos
- Lastro de concreto magro traço 1:4.5:4.5
- Solo Natural
- IMPERMEABILIZAÇÃO COM ARGAMASSA DE CIMENTO CAL E AREIA COM ADITIVO IMPERMEABILIZANTE TRAÇO 1:1:6 E= 20mm
- CHAPISCO TRAÇO 1:3 CIMENTO E AREIA GROSSA E= 5 mm
- ARGAMASSA DE CIMENTO, CAL E AREIA MÉDIA TRAÇO 1:2:8 E= 10 mm
- ALVENARIA DE 1/2 VEZ TIJOLO CERÂMICO DE 8 FUROS 9X9X19 cm
- LASTRO DE CONCRETO MAGRO TRAÇO 1:4.5:4.5

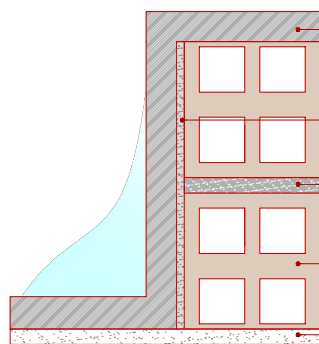

Detalhe – Grelha
escala 1/5

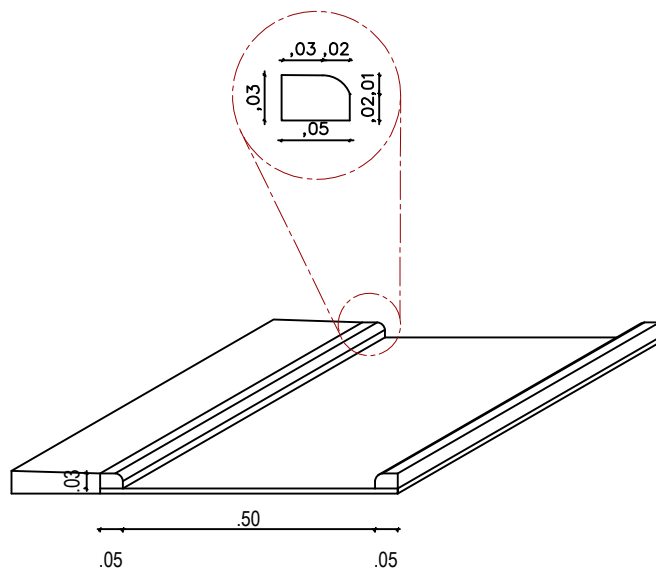

Detalhe – Canaleta
escala 1/10

Documento assinado digitalmente
MICHAEL JACKSON MAMEDE SOUZA
Data: 11/03/2024 15:21:02-0300
Verifique em <https://validar.iti.gov.br>

Detalhe – Grelha de drenagem
escala 1/15

CANALETA COM GRELHA	
VARIÁVEL X (m)	VARIÁVEL Y (m)
0,50 m	0,45 m

RESPONSÁVEL TÉCNICO:

PROPRIETÁRIO:

PRANCHA		PREFEITURA MUNICIPAL DE COREMAS – PB	
4/5		PROJETO DE CONSTRUÇÃO DE MATADOURO – 9389922022	
		PROJETO ARQUITETÔNICO – GALPÃO	
	DATA	RESPONSÁVEL	RUBRICA
DESENHO			
PROJETO			
CÓPIA			
ESCALA:	DESENHO:		
1/75	PLANTA BAIXA CANALETA – GALPÃO		
1/15	DETALHE – GRELHA DE DRENAGEM		
1/5	DETALHE – CANALETA		
1/5	DETALHE – PASSAGEM SOB PAREDES		