


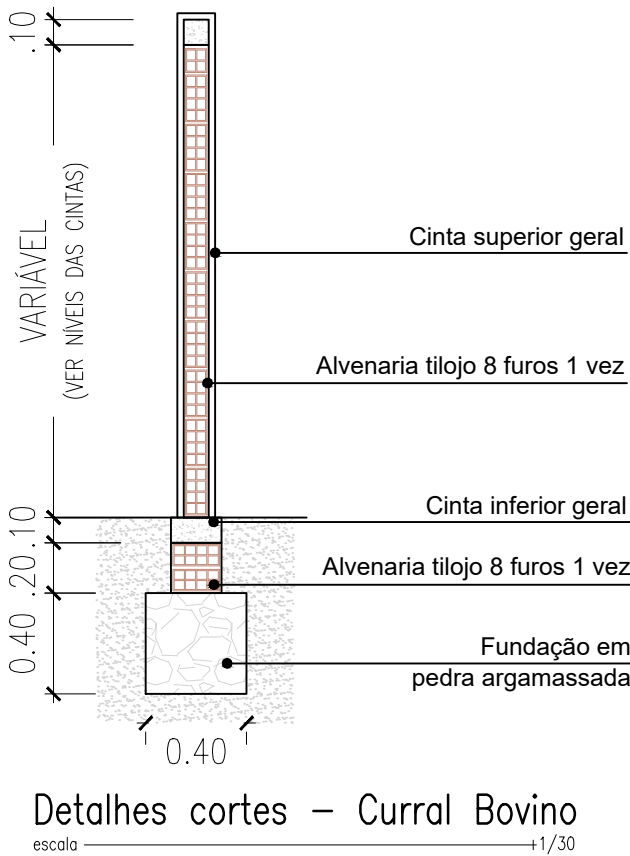
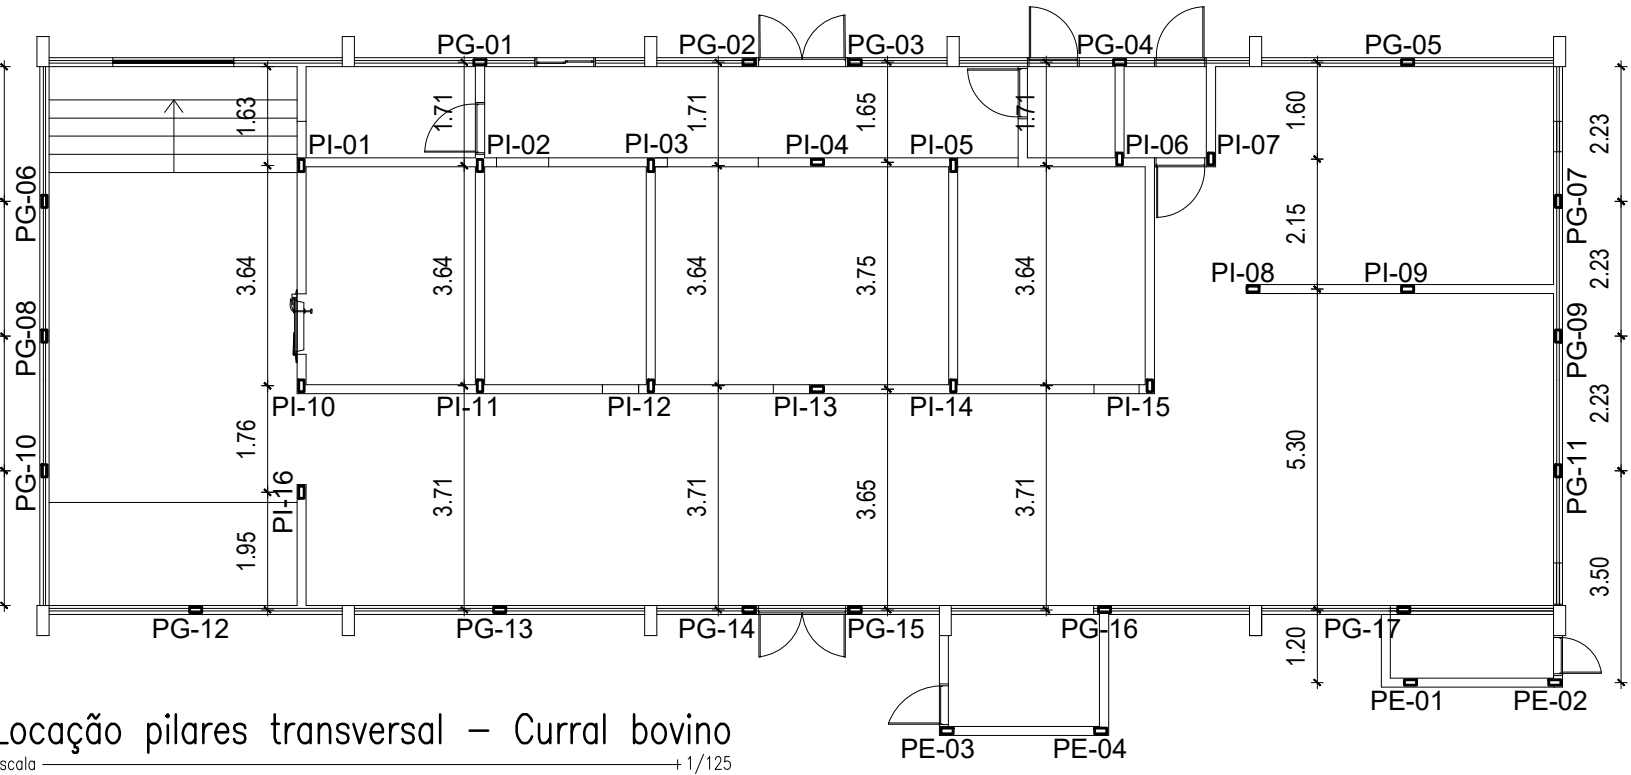


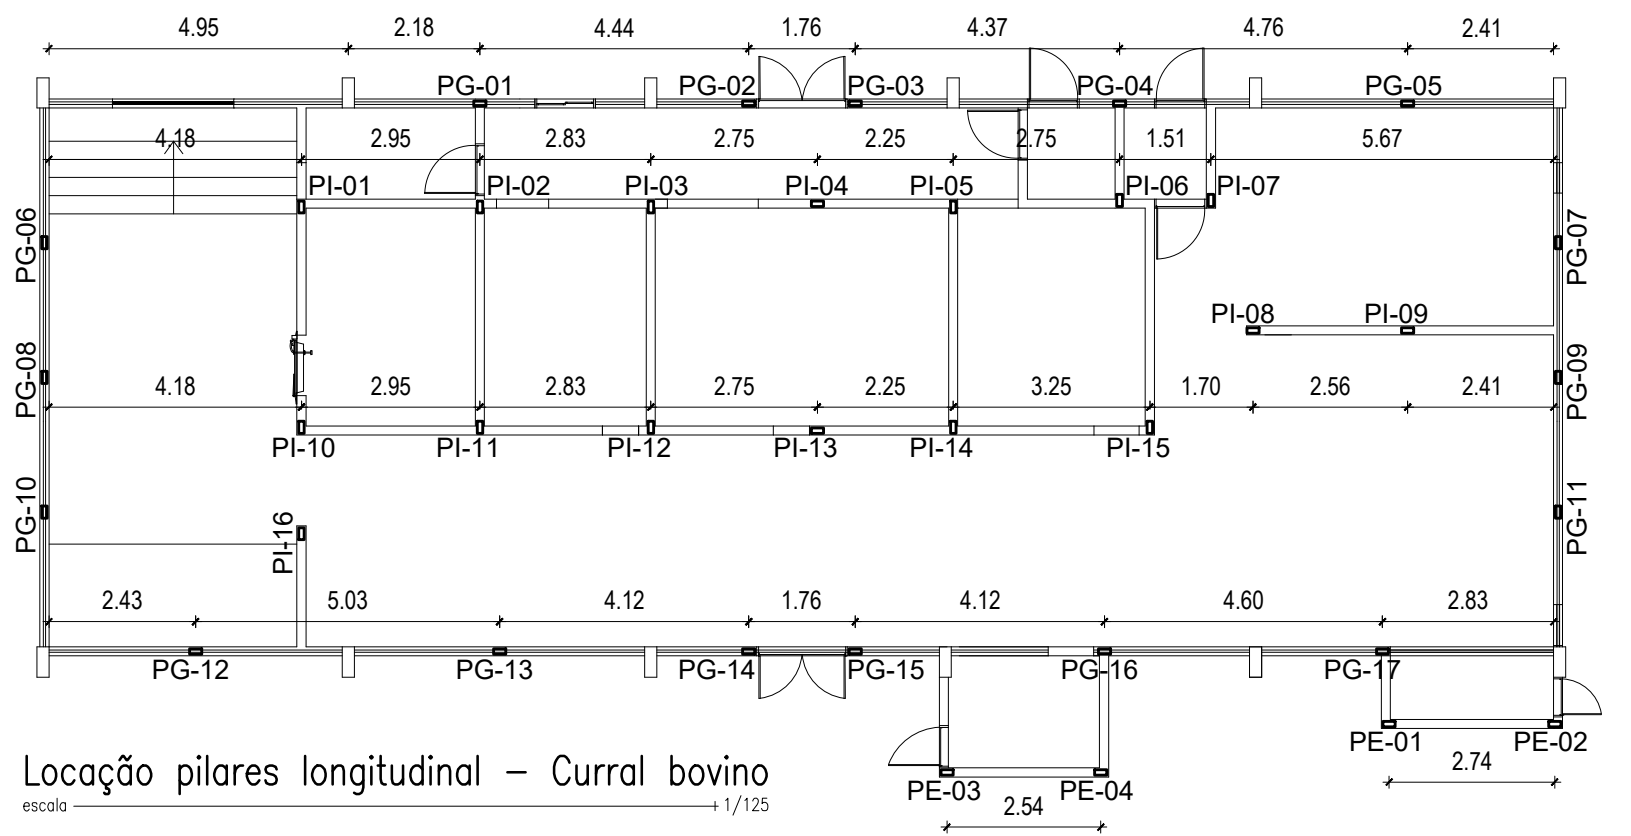


PILARES DO GALPÃO - PG (17x)

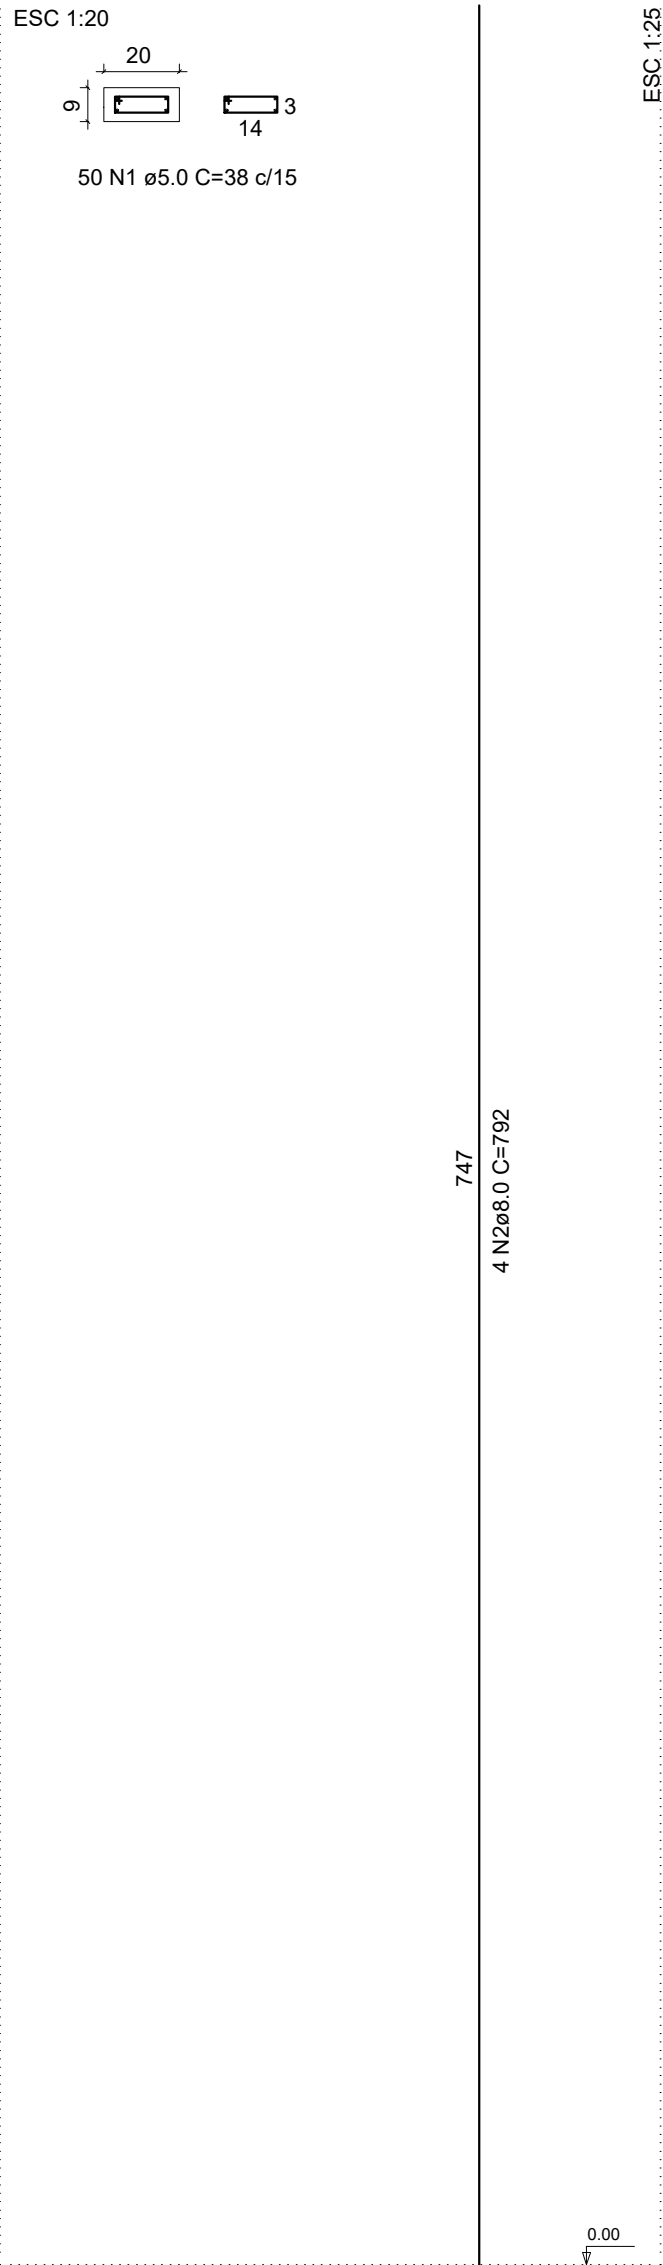

PILARES INTERNOS - PI (16x)

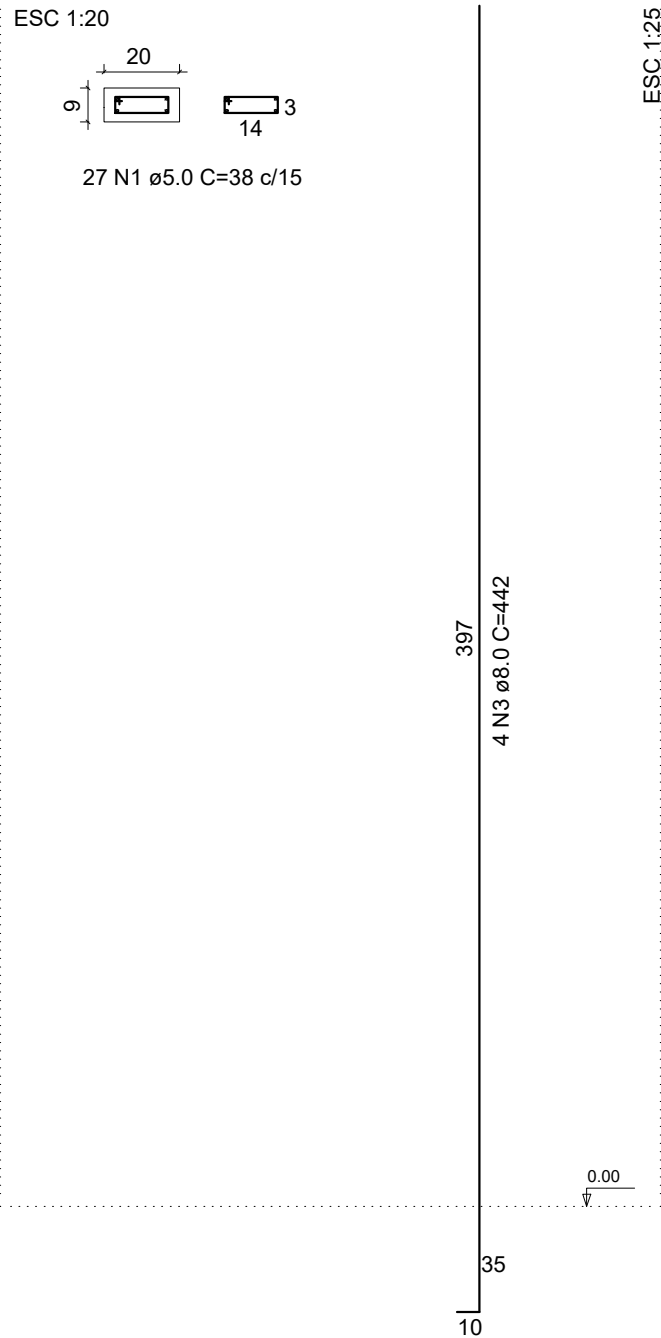

PILARES EXTERNOS - PE (4x)

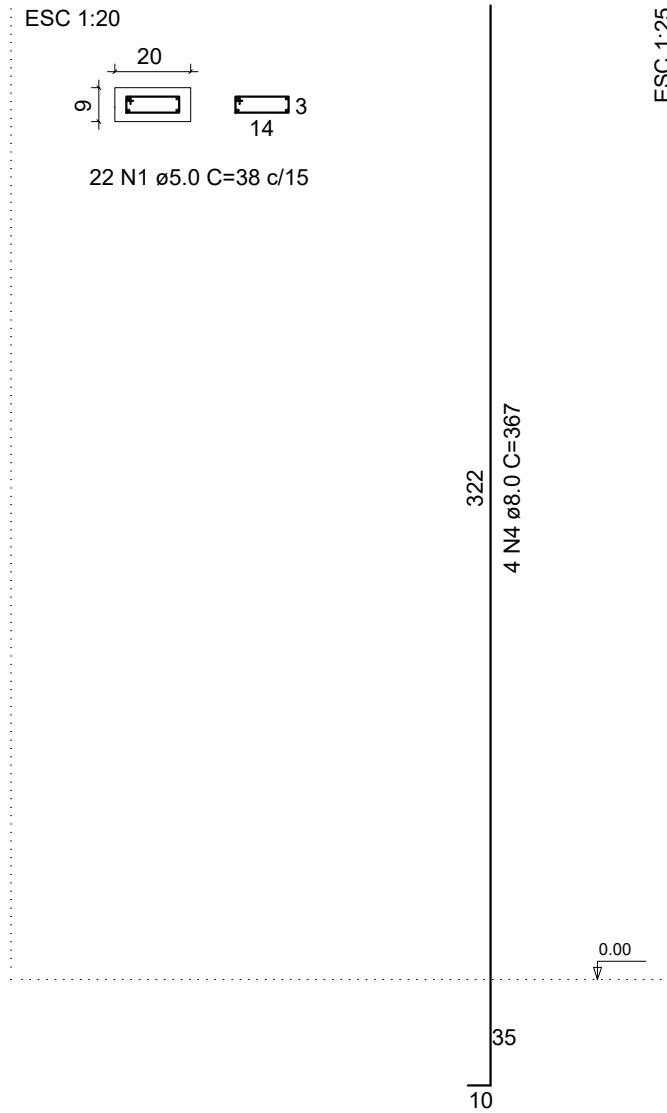

Relação do aço

AÇO	N	DIAM	Q	UNIT (cm)	C.TOTAL (cm)
CA60	1	5.0	1326	38	50388
CA50	2	8.0	68	792	53856
CA50	3	8.0	64	442	28288
CA50	4	8.0	8	367	2936

Resumo do aço

AÇO	DIAM	C.TOTAL (m)	PESO + 10 % (kg)
CA50	8.0	850.8	369.6
CA60	5.0	503.8	85.3
PESO TOTAL			
CA50	369.6		
CA60	85.3		

RESPONSÁVEL TÉCNICO:

PROPRIETÁRIO:

PRANCHA 1/2		PREFEITURA MUNICIPAL DE COREMAS – PB			
		PROJETO DE CONSTRUÇÃO DE MATADOURO – 9389922022			
		PROJETO ESTRUTURAL - CINTAS E PILARES GALPÃO			
	DATA	RESPONSÁVEL		RUBRICA	
DESENHO					
PROJETO				ÁREA DO TERRENO	ÁREA ÚTIL
CÓPIA				10.000,00 M²	971,43 M²
ESCALA:		DESENHO:		ÁREA CONSTRUIDA	
1:1 25		LOCAÇÃO PILARES LONGITUDINAL		871,58 M²	
1:1 25		LOCAÇÃO PILARES TRANSVERSAL			
1:30		DETALHE CORTES			