

TERRAS BARTOLOMEU GUARRIDO

P2


80

P1


TERRAS BARTOLOMEU GUARRIDO
125

P4

PB-366

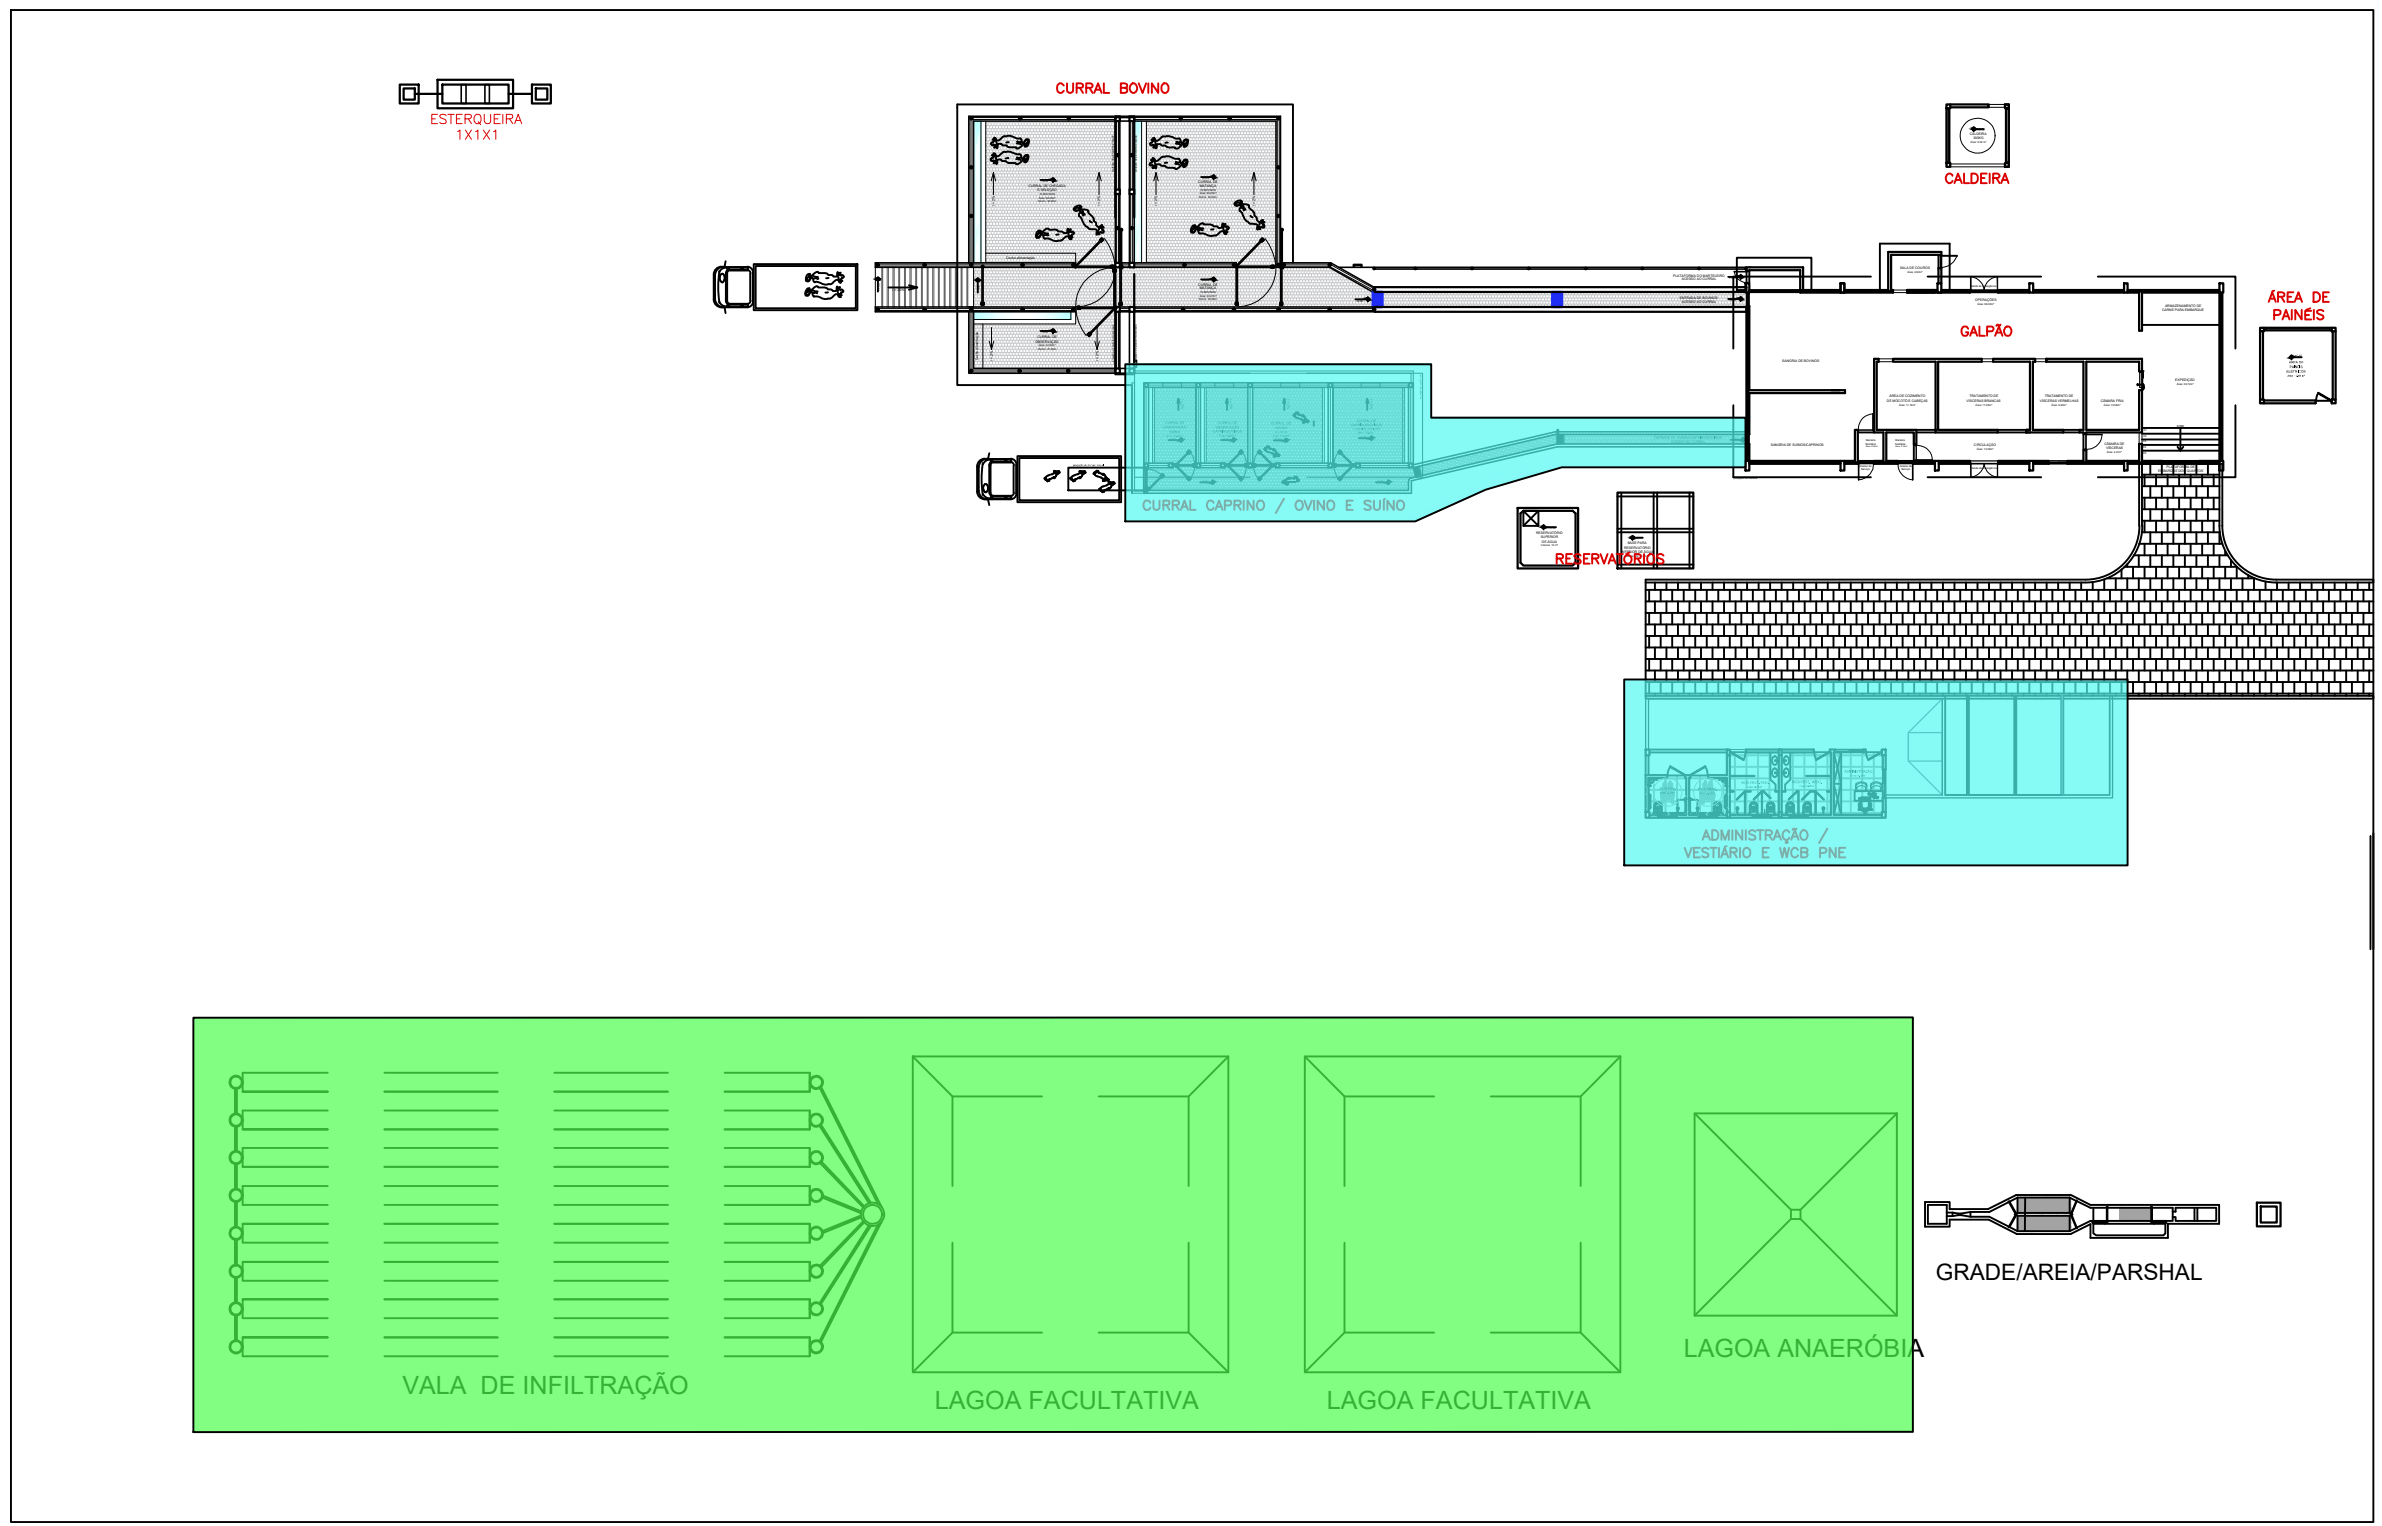

PLANTA BAIXA GERAL
Escala 1:400

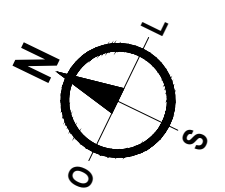

NOTA TÉCNICAS – PROJETO MATADOURO

NT 01: A terraplenagem de toda a área necessária para a execução do Projeto de Construção do Matadouro Público deste município serão executados através de recursos próprios municipais.

COORDENADAS DOS VÉRTICES DO TERRENO	
VÉRTICE	PONTO
P1	E 622067.00 S 9224900.00
P2	E 622139.00 S 9224935.00
P3	E 622121.00 S 9224788.00
P4	E 622193.00 S 9224823.00

TERRENO PARA IMPLANTAÇÃO DO MATADOURO		
LEGENDA	COMP. X LARG.(m)	ÁREA(m²)
	125,00 X 80,00	10.000,00

LEGENDA	
PAV. PARALELEPÍPEDO	260,58 m²
MEIO-FIO GRANÍTICO	92,98 m
A SER EXECUTADO COM RECURSOS DESTE CONVÊNIO	
A SER EXECUTADO COM RECURSOS PRÓPRIOS	
A SER EXECUTADO EM FUTURAS ETAPAS	

RESPONSÁVEL TÉCNICO:

PROPRIETÁRIO:

PRANCHA 1/2	PREFEITURA MUNICIPAL DE COREMAS – PB				
	PROJETO DE CONSTRUÇÃO DE MATADOURO – 9389922022				
	PROJETO ARQUITETÔNICO – GERAL				
	DATA	RESPONSÁVEL	RUBRICA		
DESENHO					
PROJETO					
CÓPIA			ÁREA DO TERRENO 10.000,00 M²	ÁREA ÚTIL 971,43 M²	ÁREA CONSTRUIDA 871,58 M²
ESCALA:	DESENHO:				
	1/400		PLANTA BAIXA GERAL		