

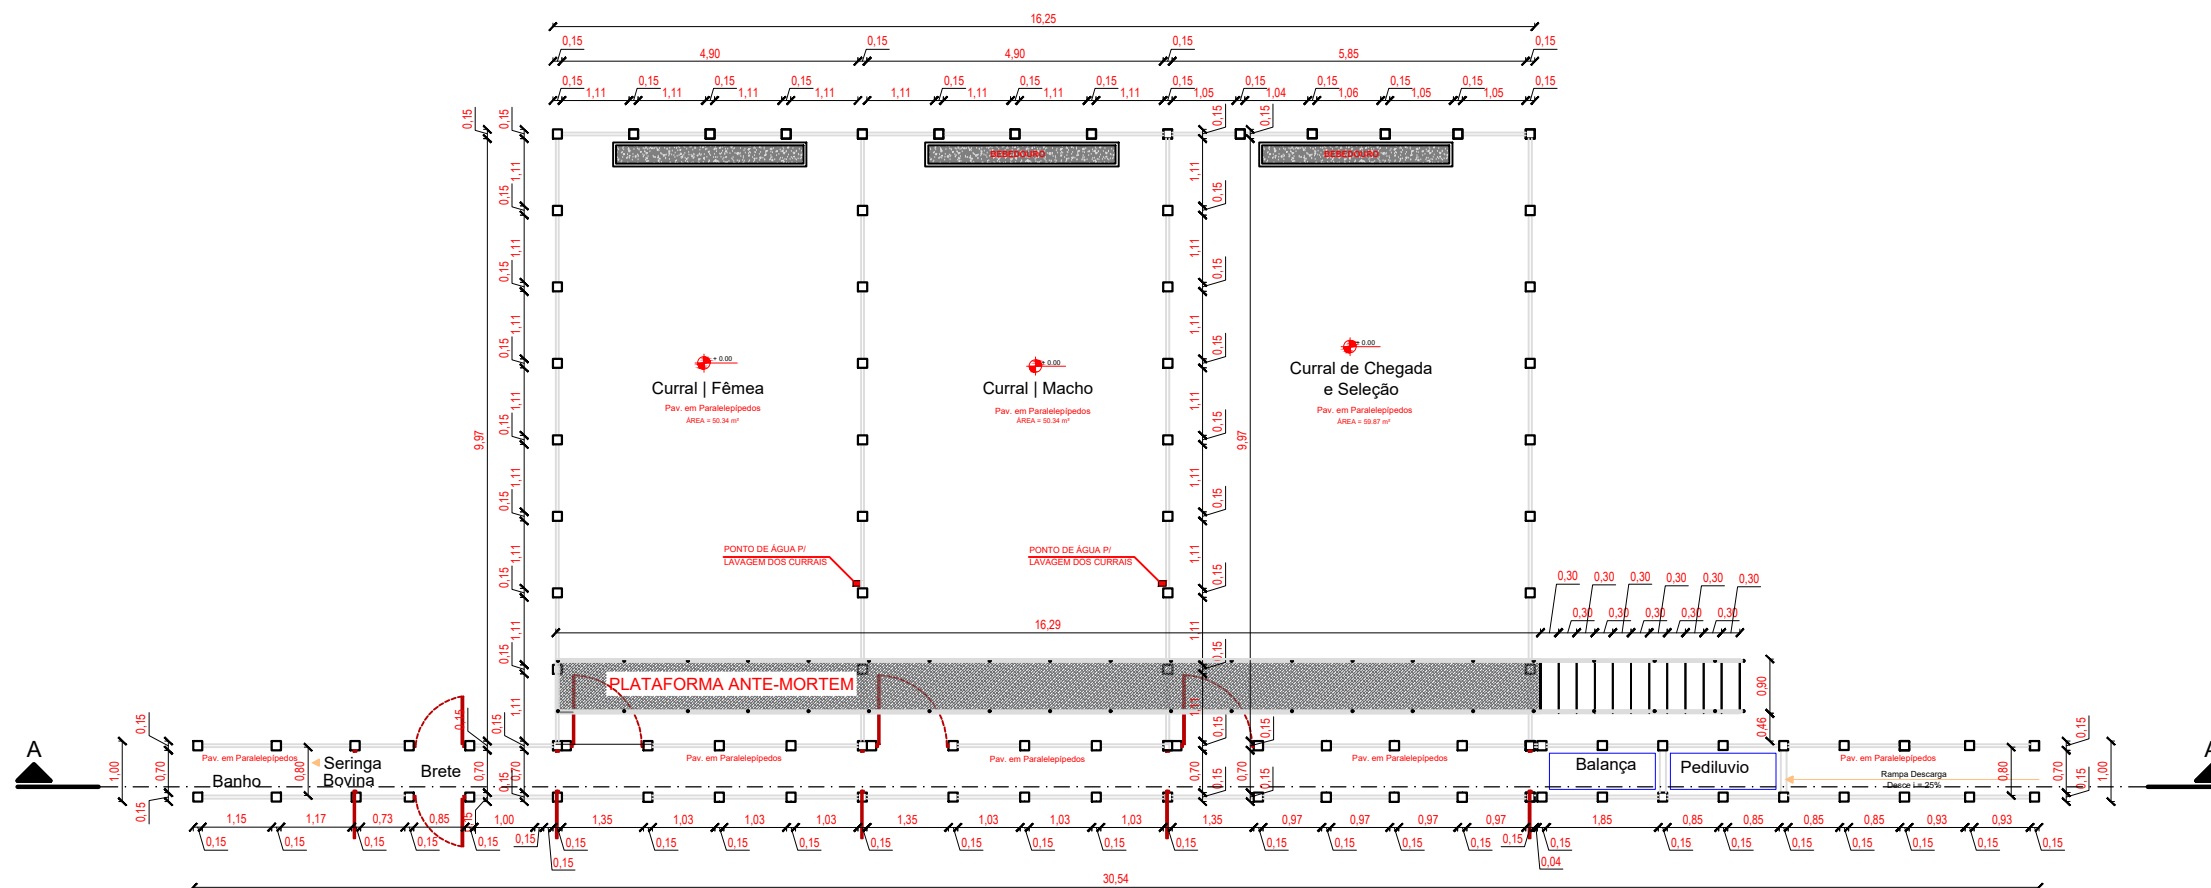


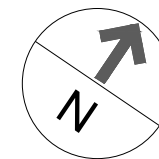

PLANTA BAIXA _ CURRAL
ESCALA _____ 1/125

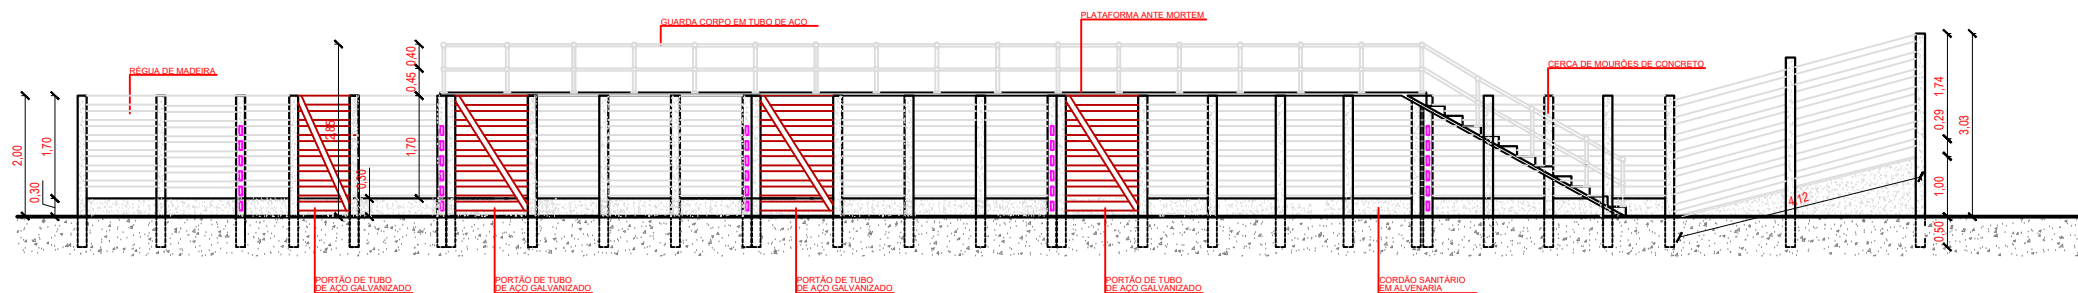

CORTE AA _ CURRAL
ESCALA _____ 1/125