



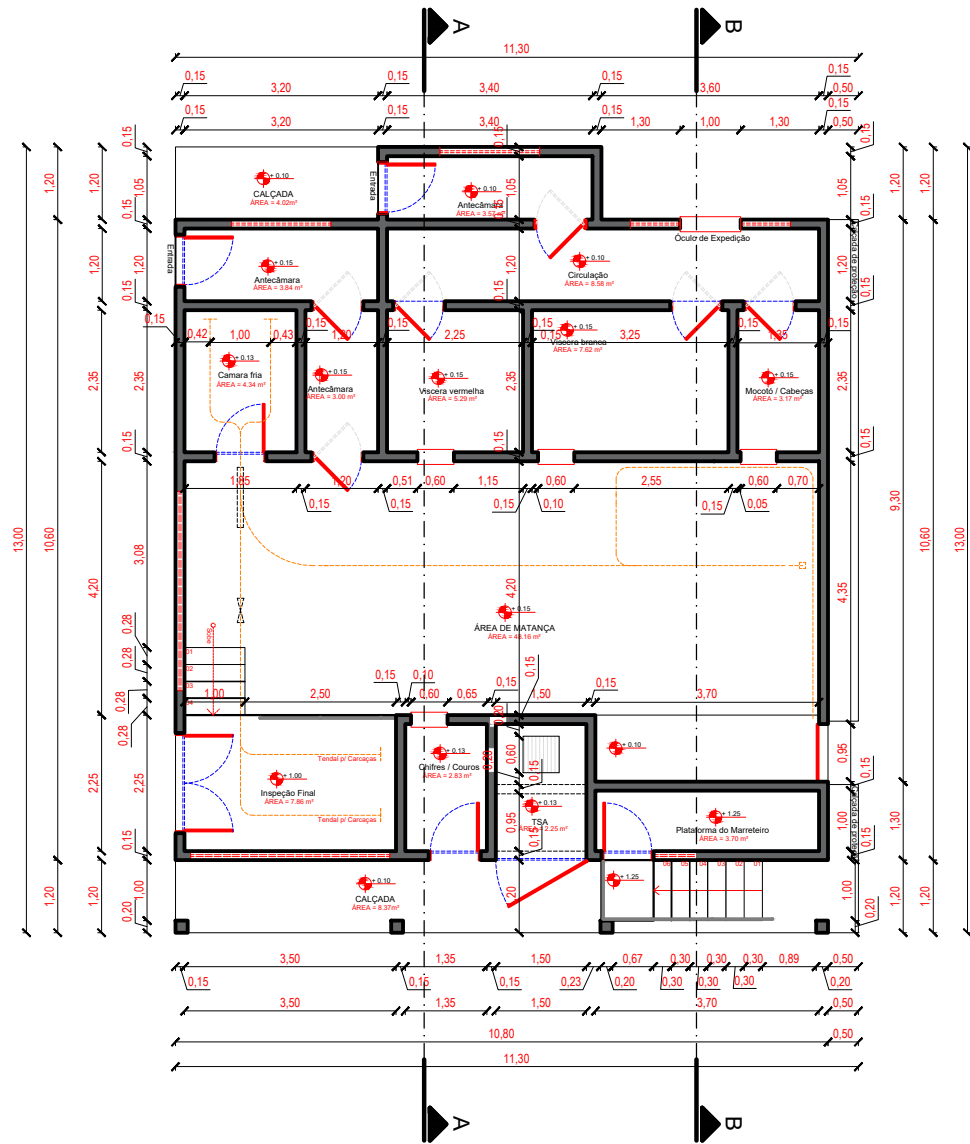

PLANTA BAIXA _ LAYOUT _ ÁREA DE MATANÇA
ESCALA 1/125

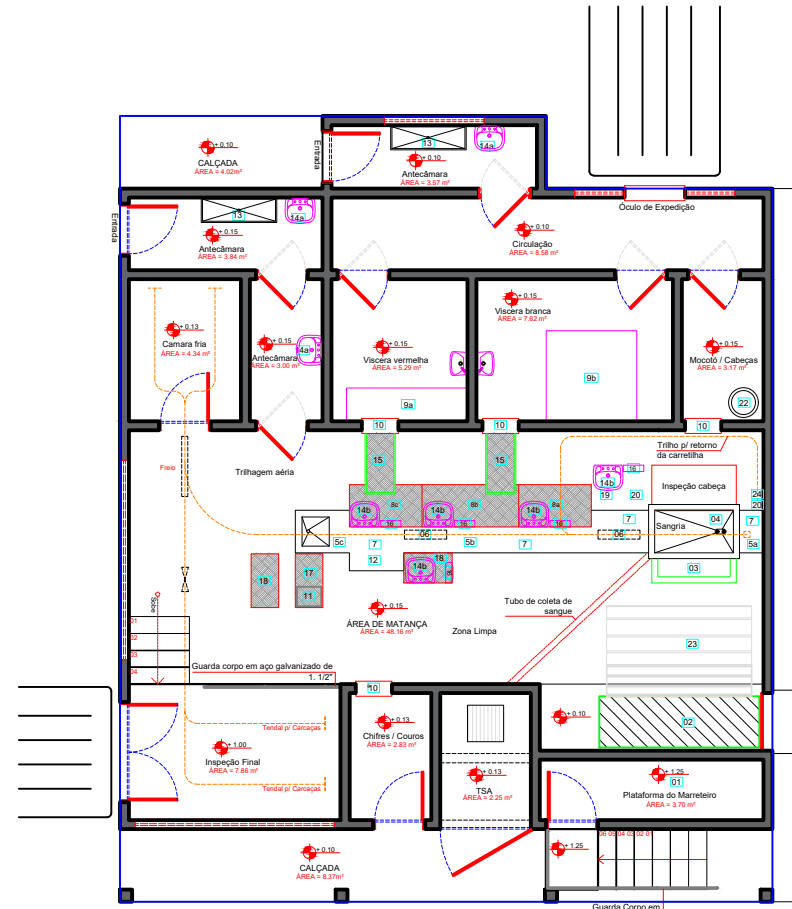

PLANTA BAIXA _ LAYOUT _ ÁREA DE MATANÇA
ESCALA 1/125

QUADRO DE ESQUADRIA - (MATANÇA)						
TIPO	DESCRIÇÃO	LARGURA	ALTURA	FOLHAS	PEITORIL	QUANT.:
PTF1	PORTÃO DE FERRO	1.50	2.10	1	-	1
PA1	PORTA DE ALUMÍNIO	1.80	3.15	2	-	1
PA2	PORTA DE ALUMÍNIO	0.80	2.50	1	-	1
PA3	PORTA DE ALUMÍNIO	0.80	2.10	1	-	4
PA4	PORTA DE ALUMÍNIO - VAI E VEM	0.80	2.10	1	-	6
PA5	PORTA DE AÇO GALV - ENROLAR	0.95	1.80	1	-	1
JA1	JANELA DE ALUMÍNIO - BASCULANTE	1.65	0.60	-	2.30/6.0	8
JA2	JANELA DE ALUMÍNIO - BASCULANTE	2.65	0.60	-	2.30	1
JA3	JANELA DE ALUMÍNIO - BASCULANTE	2.74	0.60	-	2.30	1
JA4	JANELA DE ALUMÍNIO - BASCULANTE	3.30	0.60	-	2.30	2

LEGENDA DE EQUIPAMENTOS

- 1 - PLATAFORMA DO MARRETEIRO
- 2 - BOX DE ATORDOAMENTO
- 3 - VÔMITO BOVINO
- 4 - COLETOR DE SANGUE
- 5 - TRILHO SUSPENSO
 - a - TRILHO h=5,25
 - b - TRILHO h=4,50
 - c - TRILHO h=3,50
- 6 - DESCIDA DO TRILHO
- 7 - CANALETA DO PISO i=2%
- 8 - PLATAFORMAS
 - a - CORREAR PARTE ALTA h=1,60
 - b - EVISCERAÇÃO h=1,20
 - c - SERRA CARÇA h=0,80
- 9 - MESA DE INOX S/ CUBA
 - a - VÍCERAS BRANCA (1.50x1.50)m
 - b - VÍCERAS VERMELHA (2.00x0.50)m
- 10 - ÓCULO COM CORTINA ISOLANTE
- 11 - SERRA CARÇA
- 12 - CALHETA HIGIENIZAÇÃO CARÇA
- 13 - LAVAR BOTAS
- 14 - PIA P/ ANTEBRAÇO
 - a - LAVA MÃOS SIMPLES
 - b - LAVA MÃO PROFUNDA
- 15 - CALHA DE AÇO GALVANIZADO P/ VÍCERAS
- 16 - ESTERELIZADOR DE FACAS
- 17 - PLATAFORMA MÓVEL
- 18 - PLATAFORMA SIMPLES
- 19 - GUINCHO DE TRANSPASSE
- 20 - SERRA ELÉTRICA
- 21 - DETALHE DO TRILHO PARA RETORNO DA CARRETLHA
- 22 - LAVADOR DE CABEÇAS
- 23 - GRADE EM AÇO GALVANIZADO P/ DESLIZAMENTO DE BOI ABATIDO
- 24 - DESCEDOR DE CARRETLHA