




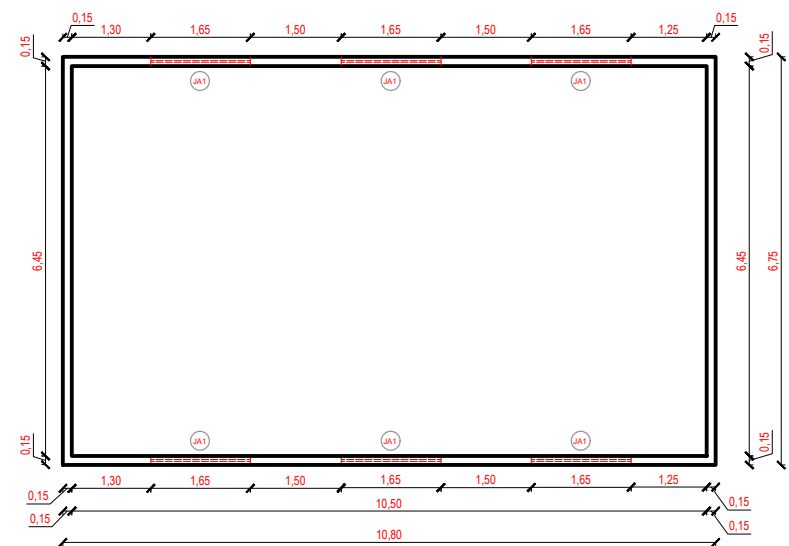


PLANTA BAIXA _ DETALHE ESQUADRIAS ELEVADAS
ESCALA 1/125

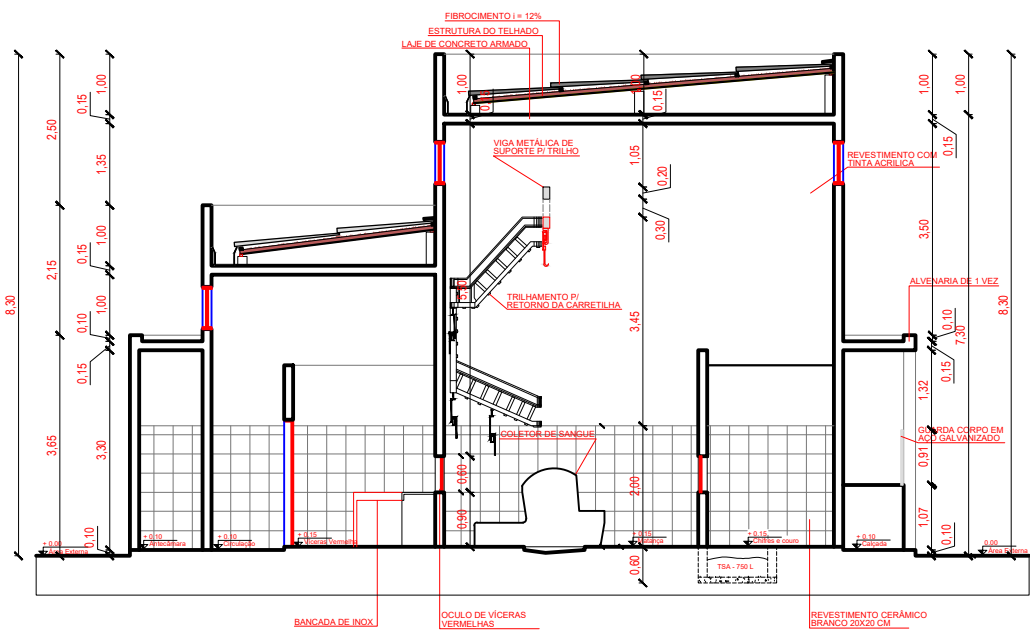

CORTE _ AA
ESCALA 1/125

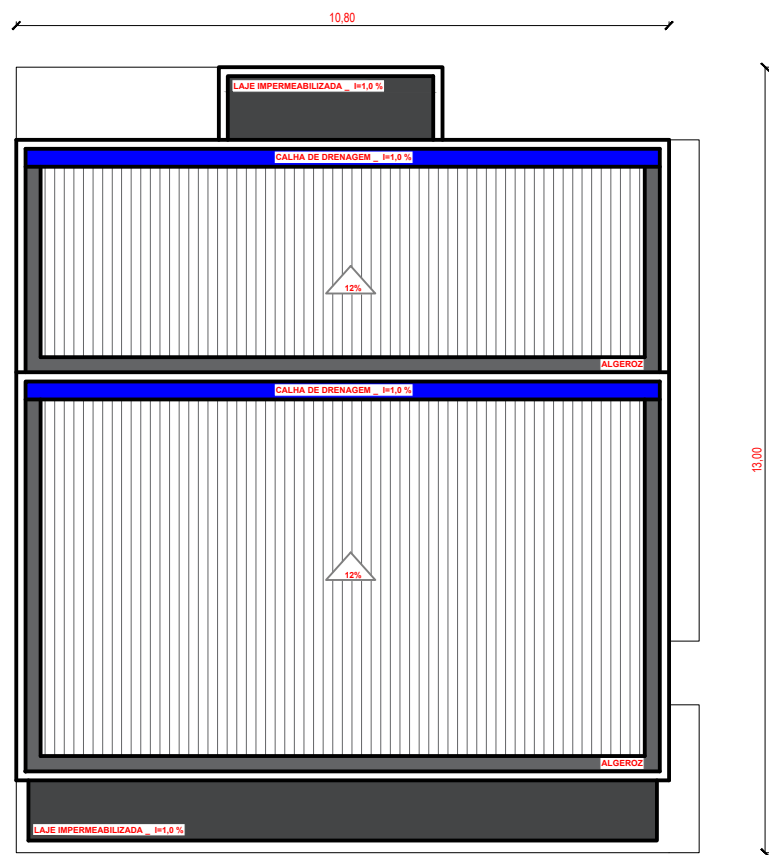

PLANTA DE COBERTA
ESCALA 1/125

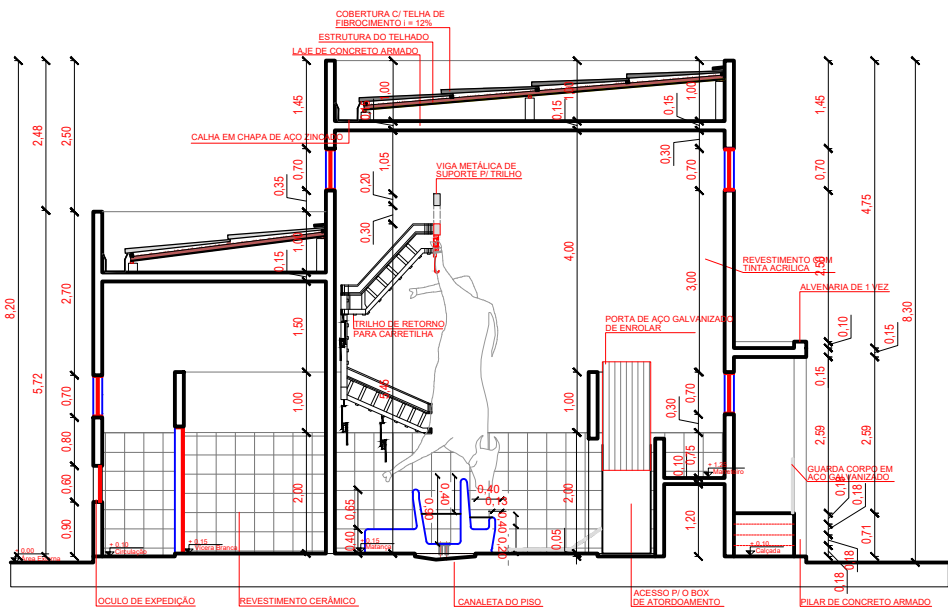

CORTE _ BB
ESCALA 1/125