




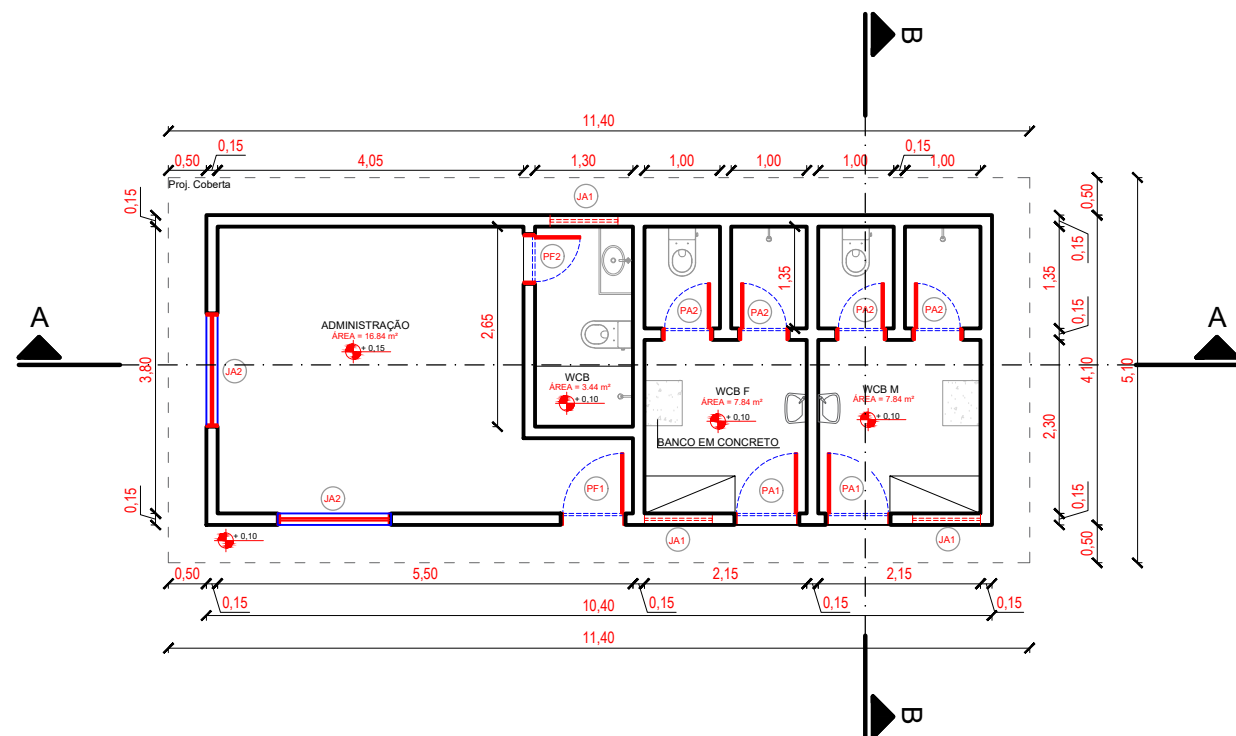


PLANTA BAIXA _ ADMINISTRAÇÃO
ESCALA 1/100

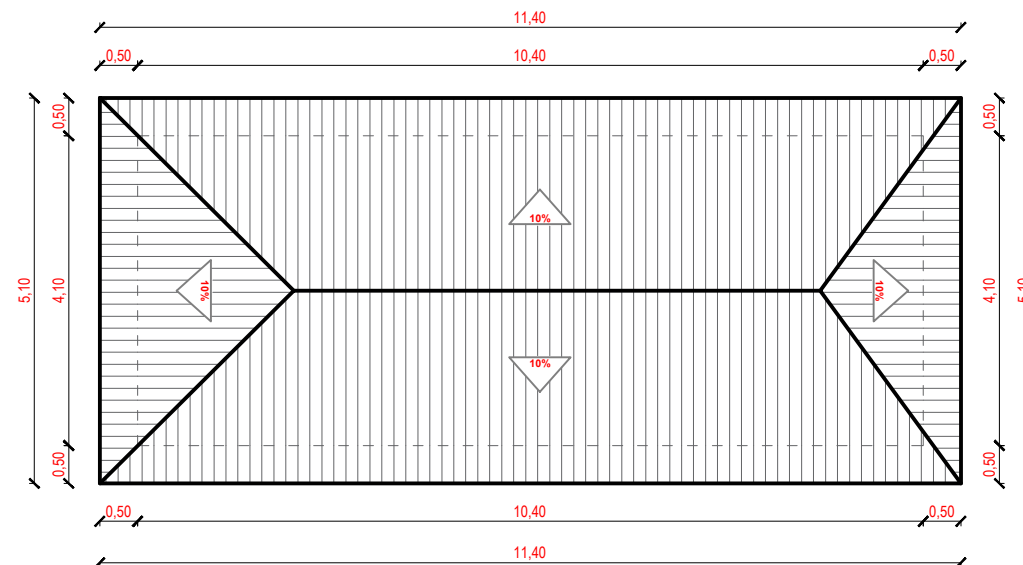


PLANTA DE COBERTA
ESCALA 1/100

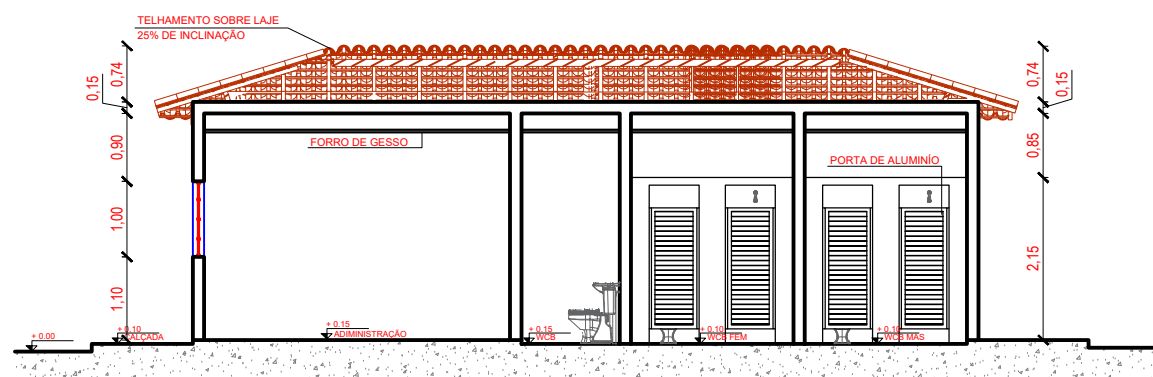

CORTE _ AA
ESCALA 1/100

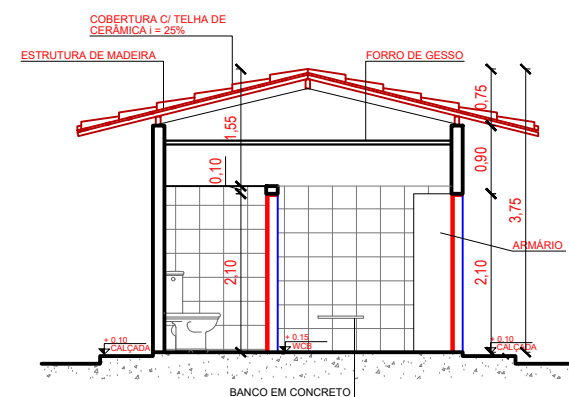

CORTE _ BB
ESCALA 1/100

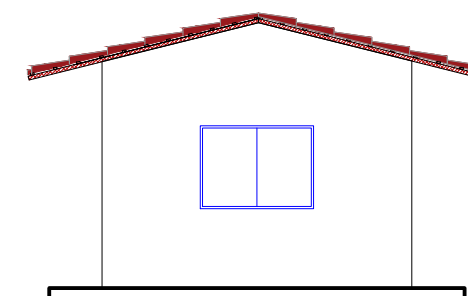

FACHADA LATERAL
ESCALA 1/100

QUADRO DE ESQUADRIA - (ADMINISTRAÇÃO)

TIPO	DESCRIÇÃO	LARGURA	ALTURA	FOLHAS	PEITORIL	QUANT.:
PF1	PORTA DE FERRO	0.80	2.10	1	-	1
PF2	PORTA DE FERRO	0.60	2.10	1	-	1
PA1	PORTA DE ALUMÍNIO	0.80	2.10	1	-	2
PA2	PORTA DE ALUMÍNIO	0.60	1.80	1	-	4
JA1	JANELA EM ALUMÍNIO	0.90	0.30	-	1.80	3
JA2	JANELA EM ALUMÍNIO	1.50	1.10	-	1.10	2