



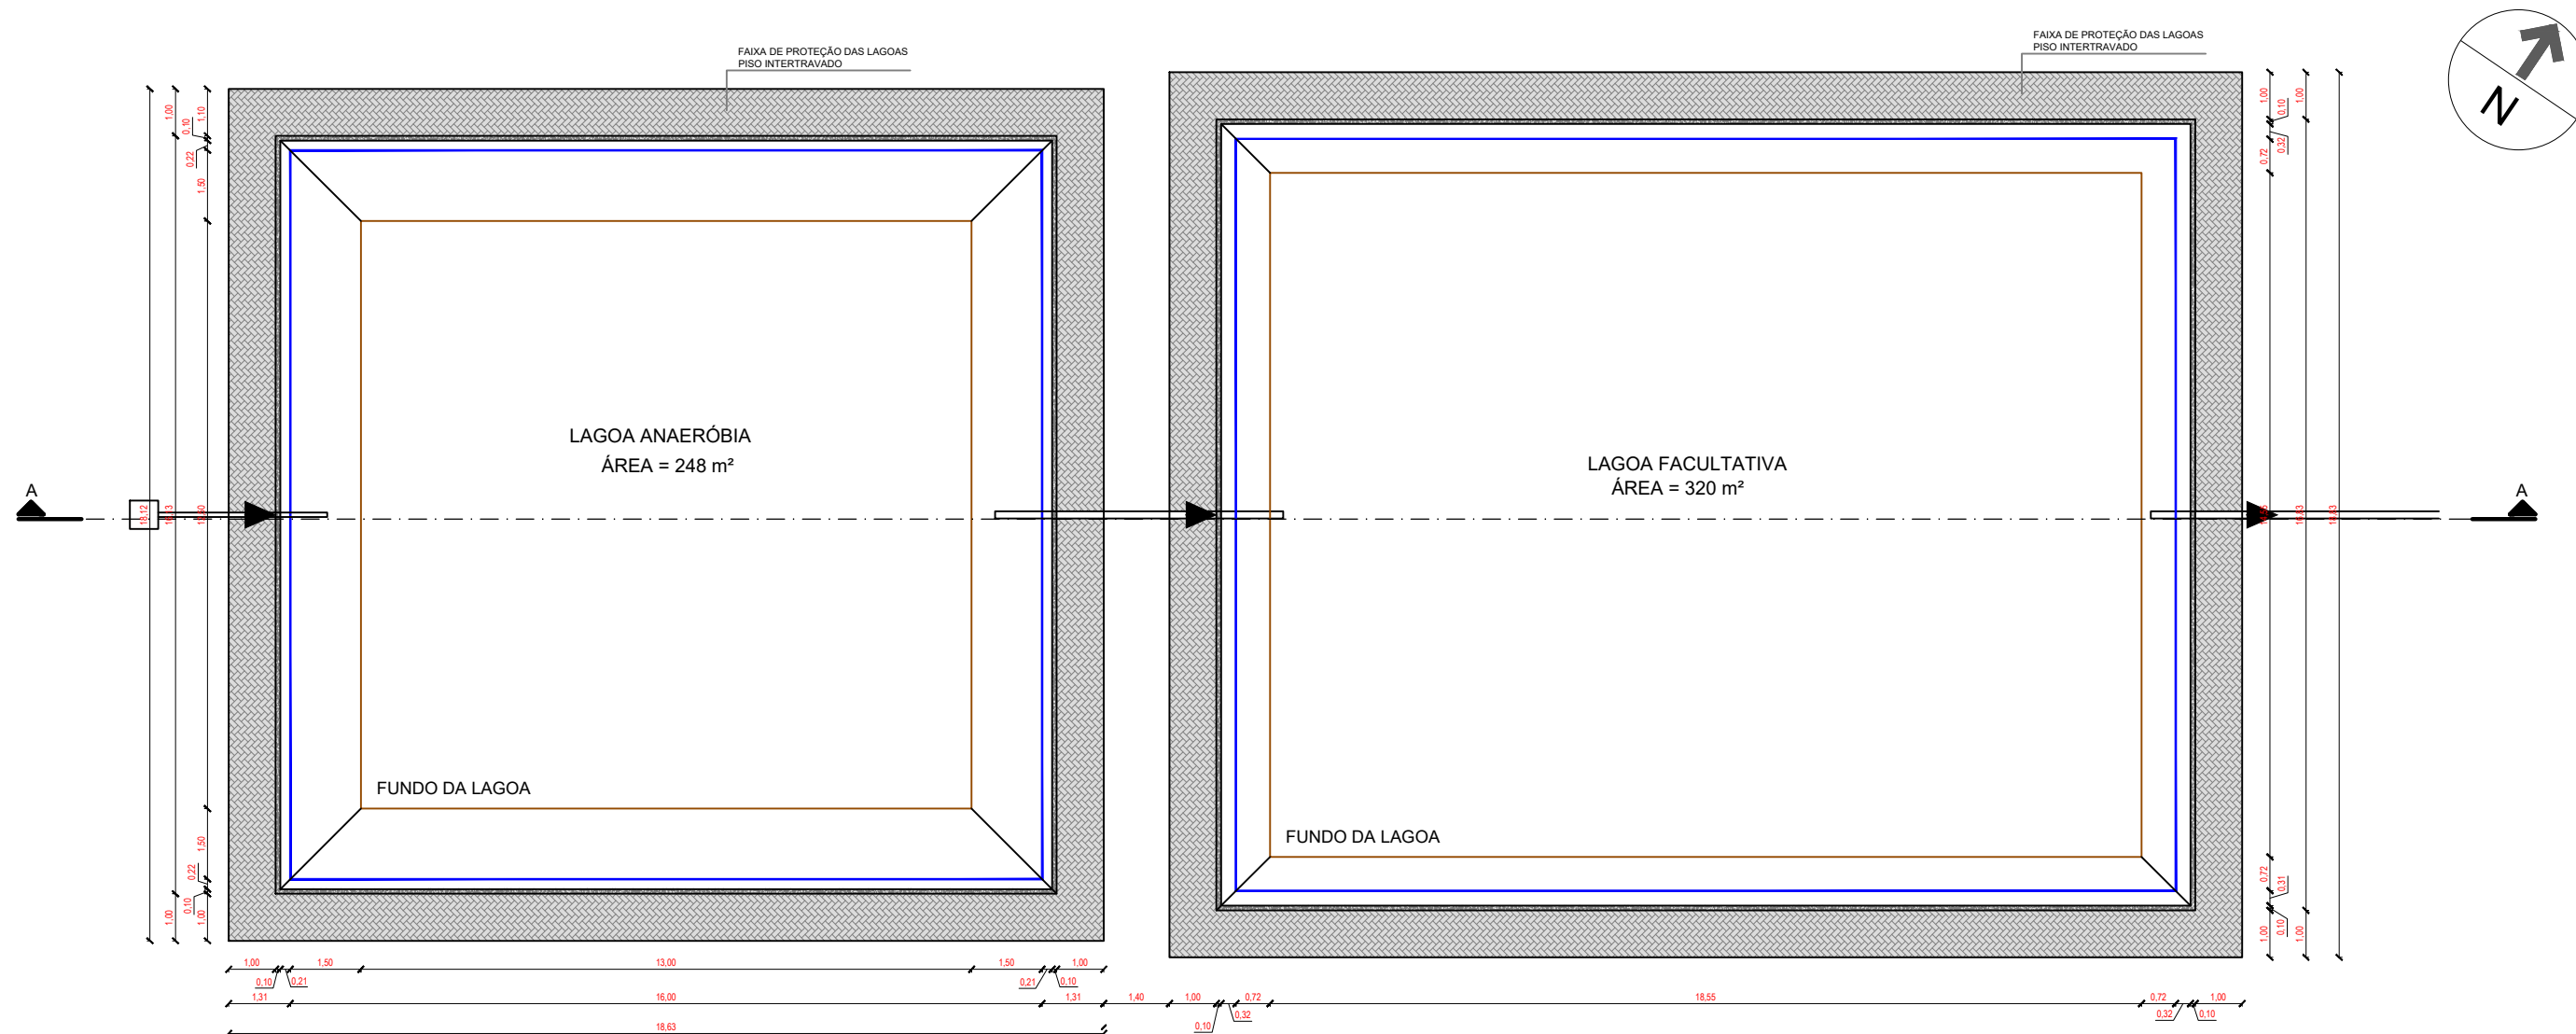

PLANTA BAIXA _ LAGOAS
ESCALA _____ 1/150

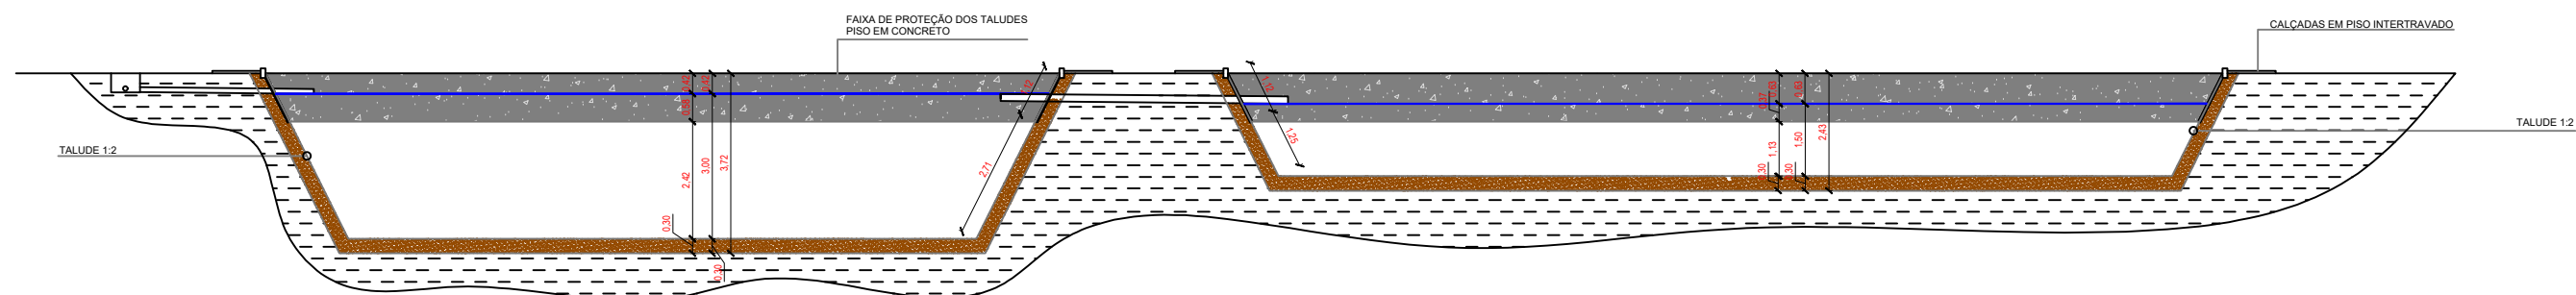

CORTE AA _ LAGOAS
ESCALA _____ 1/150