


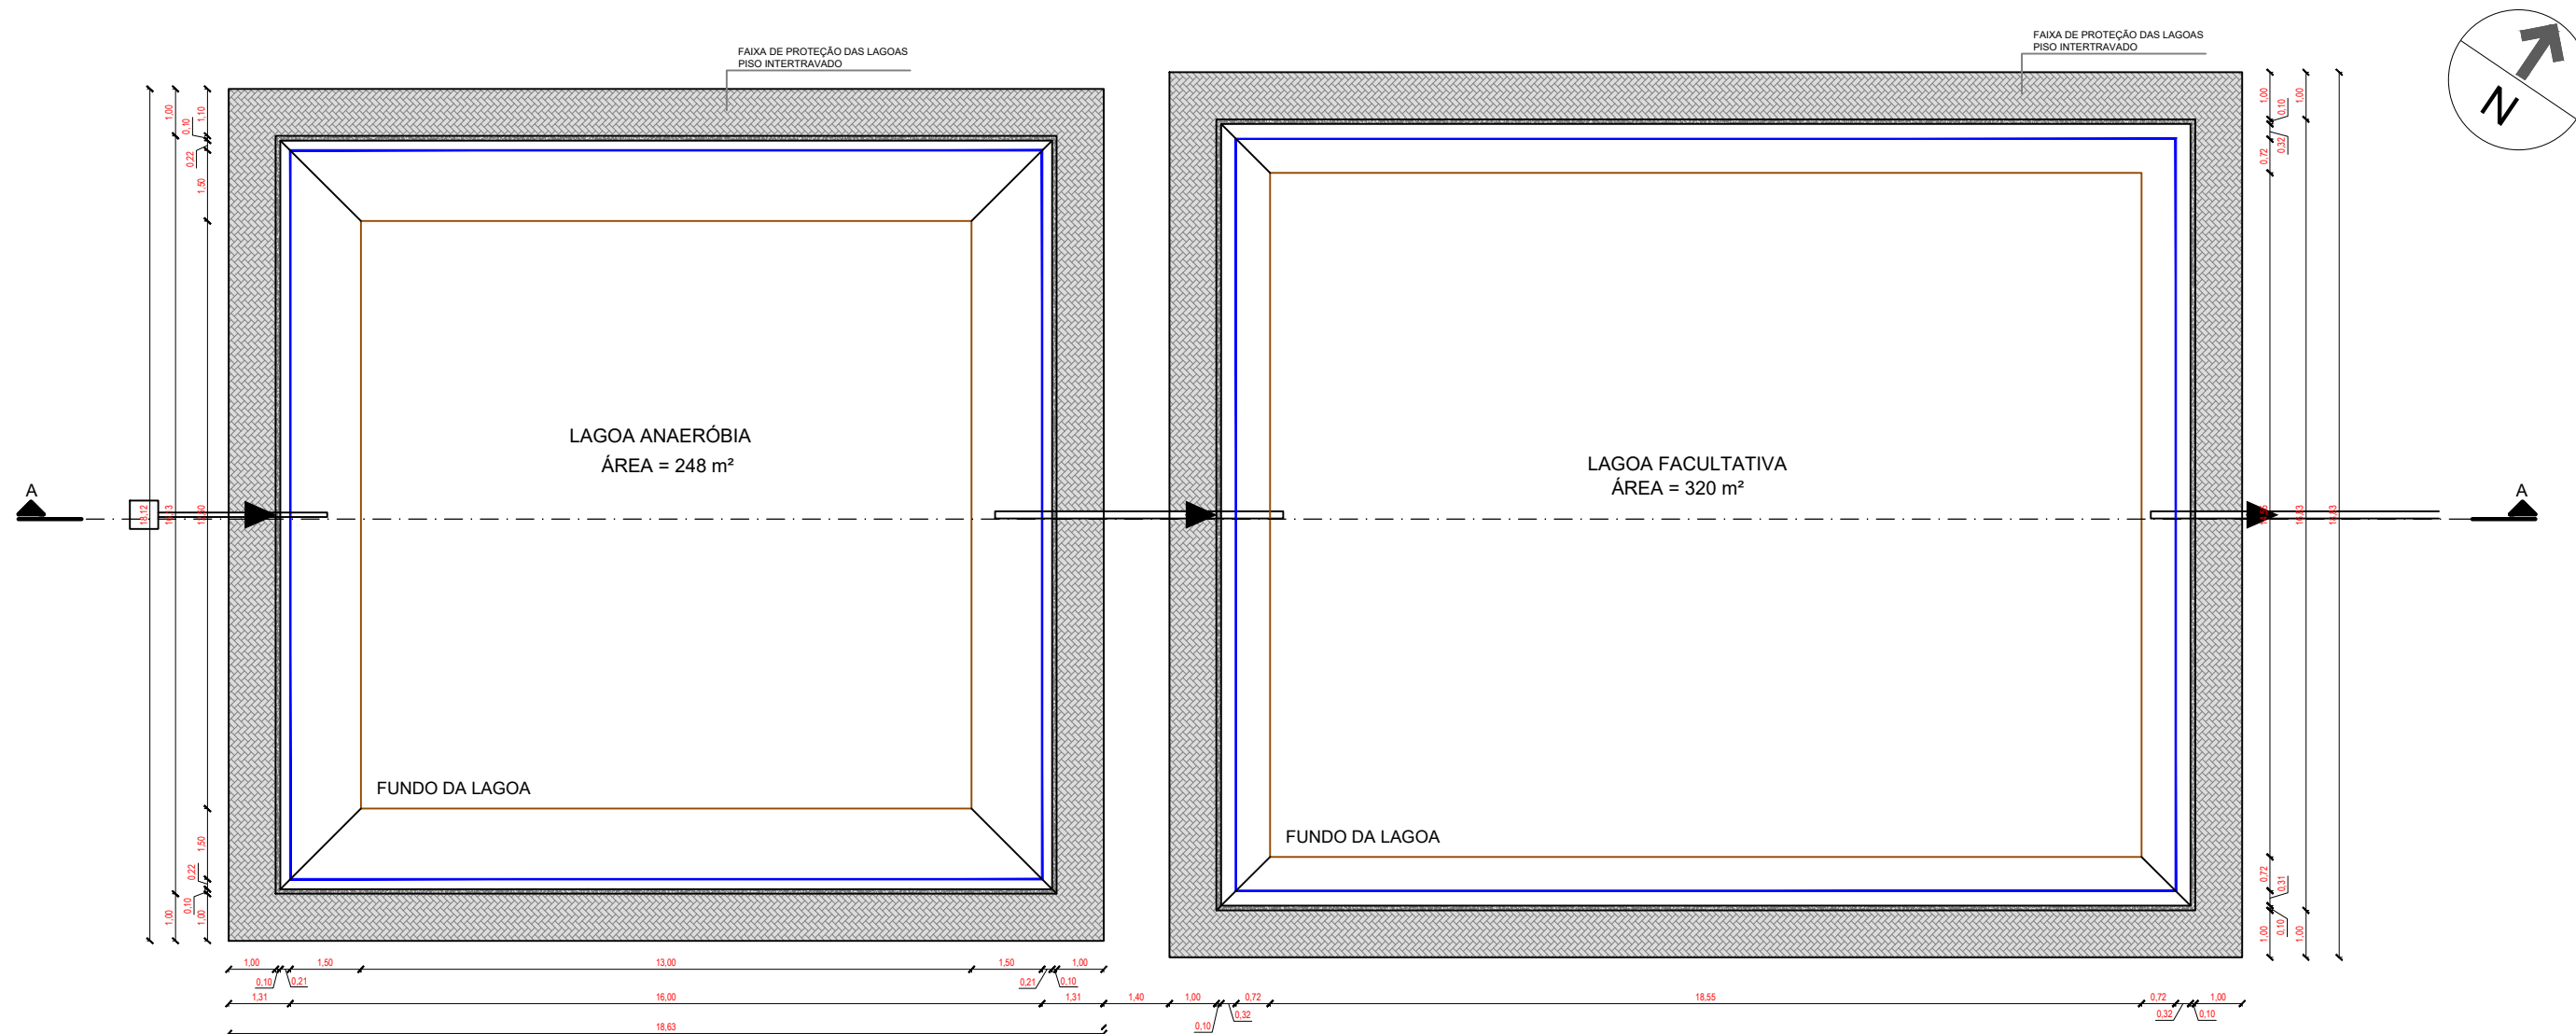


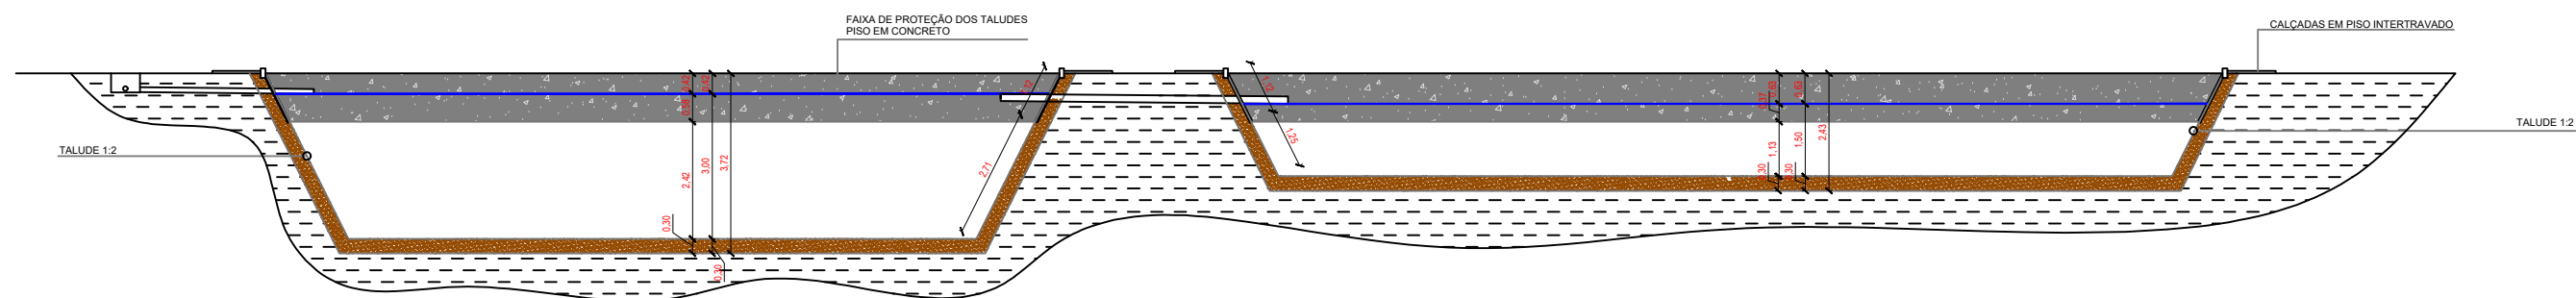


PLANTA BAIXA _ LAGOAS
ESCALA _____ 1/150

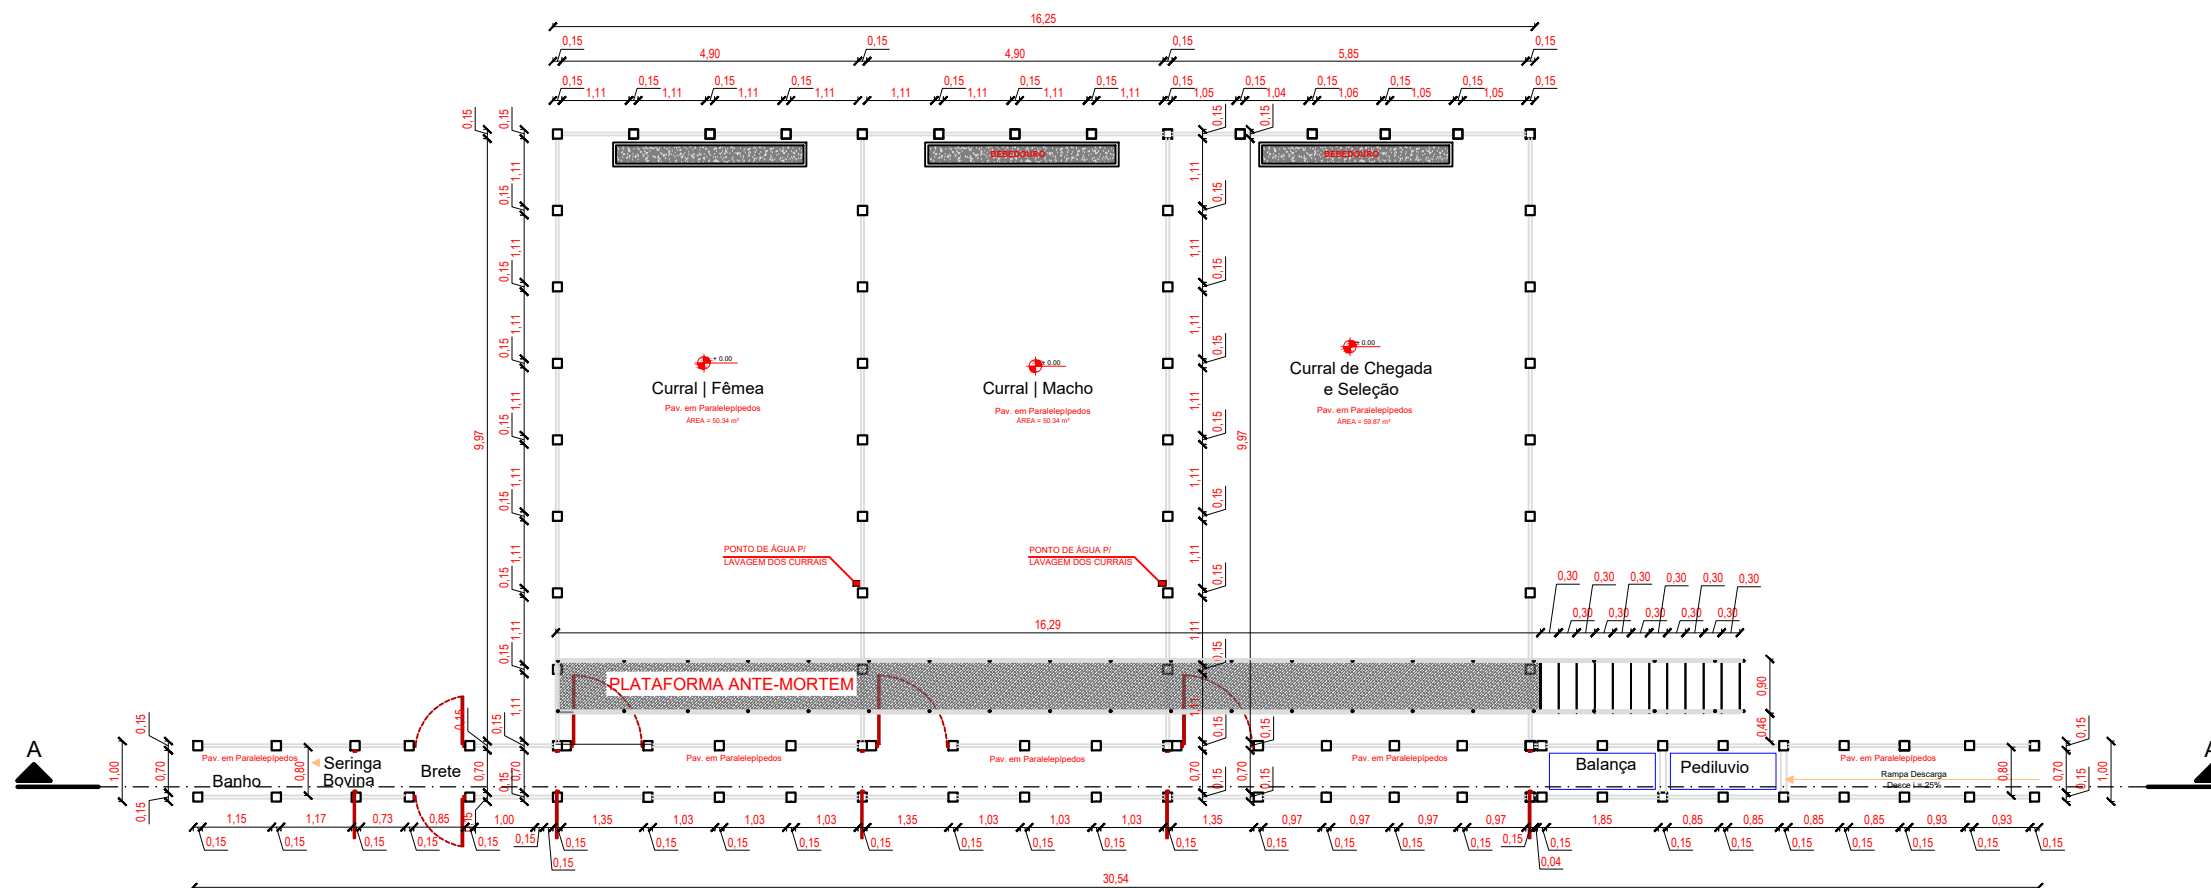


CORTE AA _ LAGOAS
ESCALA _____ 1/150

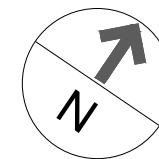


PLANTA BAIXA _ CURRAL
ESCALA 1/125

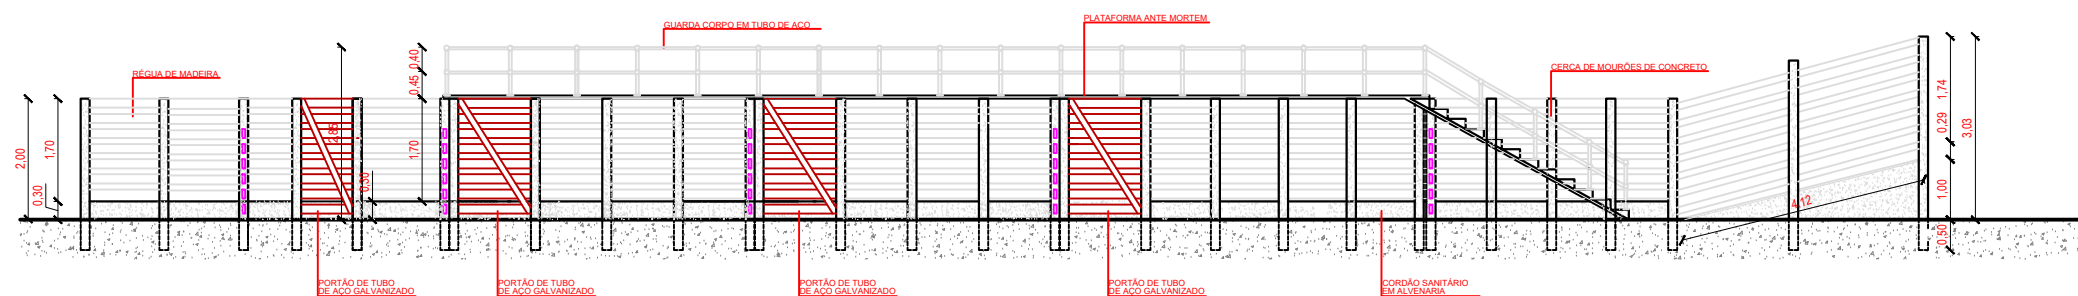

CORTE AA _ CURRAL
ESCALA 1/125

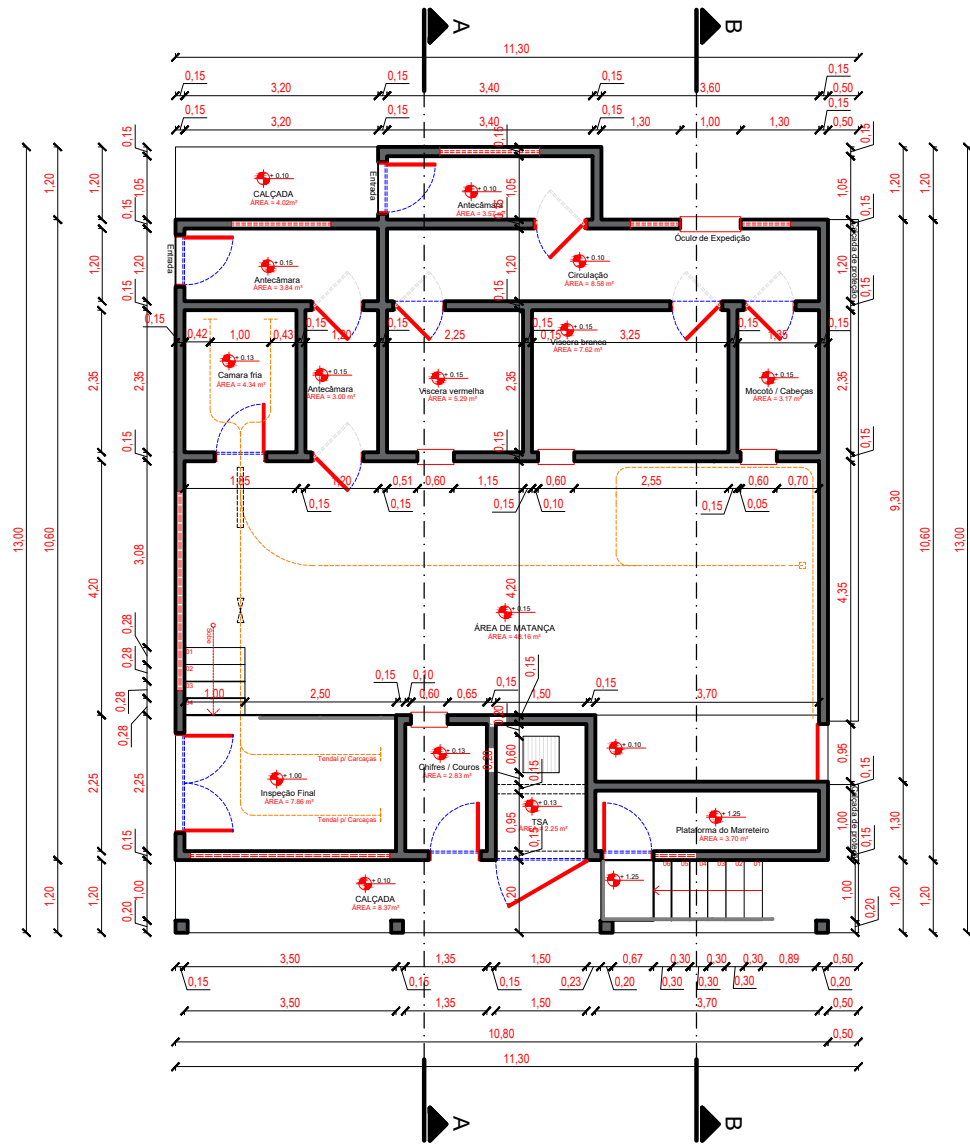

PLANTA BAIXA _ LAYOUT _ ÁREA DE MATANÇA
ESCALA 1/125

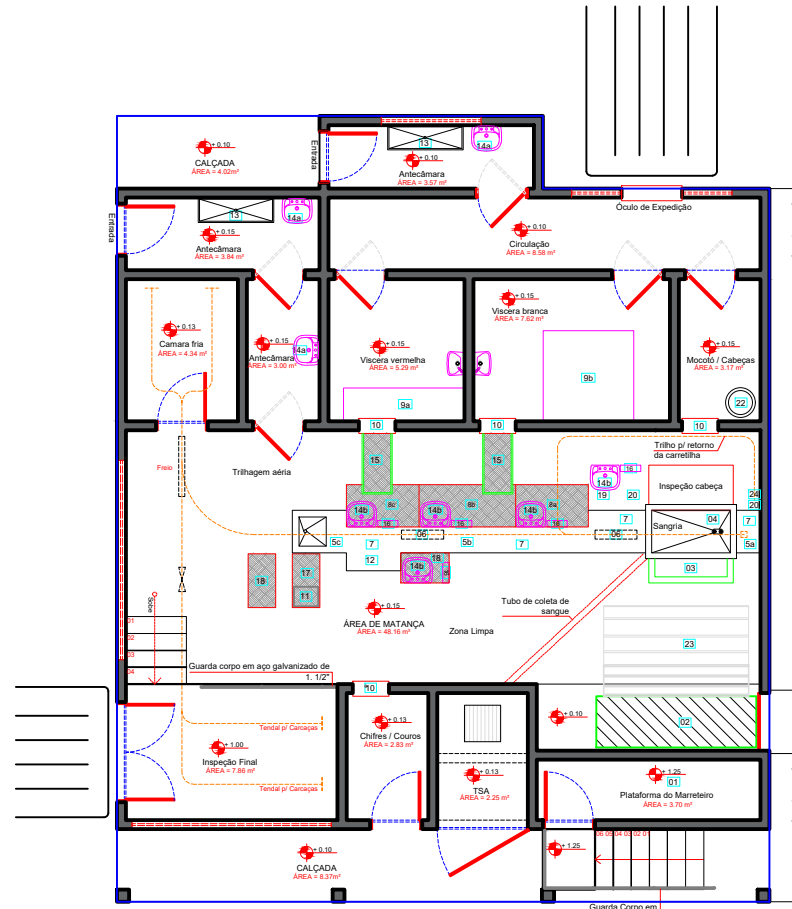

PLANTA BAIXA _ LAYOUT _ ÁREA DE MATANÇA
ESCALA 1/125

QUADRO DE ESQUADRIA - (MATANÇA)						
TIPO	DESCRIÇÃO	LARGURA	ALTURA	FOLHAS	PEITORIL	QUANT.:
PTF1	PORTÃO DE FERRO	1.50	2.10	1	-	1
PA1	PORTA DE ALUMÍNIO	1.80	3.15	2	-	1
PA2	PORTA DE ALUMÍNIO	0.80	2.50	1	-	1
PA3	PORTA DE ALUMÍNIO	0.80	2.10	1	-	4
PA4	PORTA DE ALUMÍNIO - VAI E VEM	0.80	2.10	1	-	6
PA5	PORTA DE AÇO GALV - ENROLAR	0.95	1.80	1	-	1
JA1	JANELA DE ALUMÍNIO - BASCULANTE	1.65	0.60	-	2.30/6.0	8
JA2	JANELA DE ALUMÍNIO - BASCULANTE	2.65	0.60	-	2.30	1
JA3	JANELA DE ALUMÍNIO - BASCULANTE	2.74	0.60	-	2.30	1
JA4	JANELA DE ALUMÍNIO - BASCULANTE	3.30	0.60	-	2.30	2

LEGENDA DE EQUIPAMENTOS

- 1 - PLATAFORMA DO MARRETEIRO

2 - BOX DE ATORDOAMENTO

3 - VÔMITO BOVINO

4 - COLETOR DE SANGUE

5 - TRILHO SUSPENSO

5a - TRILHO h=5,25

5b - TRILHO h=4,50

5c - TRILHO h=3,50

6 - DESCIDA DO TRILHO

7 - CANALETA DO PISO i=2%

8 - PLATAFORMAS

8a - CORREAR PARTE ALTA h=1,60

8b - EVISCERAÇÃO h=1,20

8c - SERRA CARÇAÇA h=0,80

9 - MESA DE INOX S/ CUBA

9a - VÍCERAS BRANCA (1.50x1.50)m

9b - VÍCERAS VERMELHA (2.00x0.50)m

10 - ÓCULO COM CORTINA ISOLANTE
- 11 - SERRA CARÇAÇA

12 - CALHETA HIGIENIZAÇÃO CARÇAÇA

13 - LAVAR BOTAS

14 - PIA P/ ANTEBRAÇO

14a - LAVA MÃOS SIMPLES

14b - LAVA MÃO PROFUNDA

15 - CALHA DE AÇO GALVANIZADO P/ VÍCERAS

16 - ESTERELIZADOR DE FACAS

17 - PLATAFORMA MÓVEL

18 - PLATAFORMA SIMPLES

19 - GUINCHO DE TRANSPASSE


20 - SERRA ELÉTRICA

21 - DETALHE DO TRILHO PARA RETORNO DA CARRETLHA


22 - LAVADOR DE CABEÇAS

23 - GRADE EM AÇO GALVANIZADO P/ DESLIZAMENTO DE BOI ABATIDO


24 - DESCEDOR DE CARRETLHA

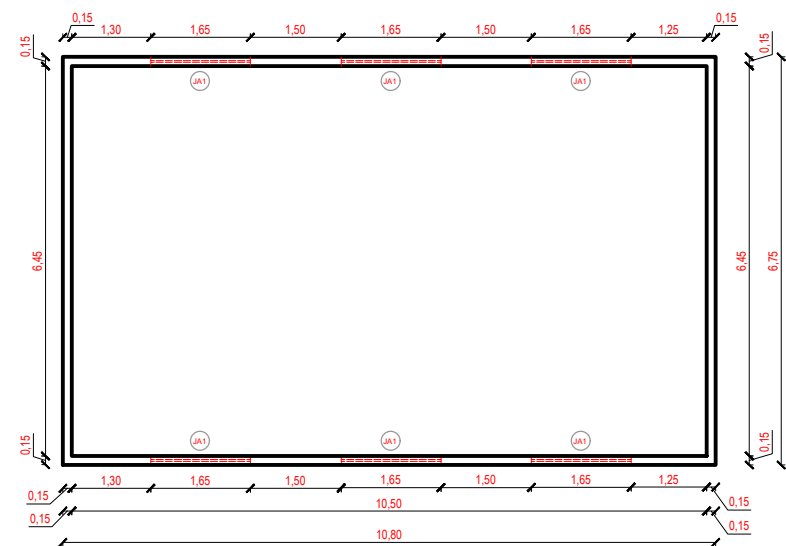


PLANTA BAIXA _ DETALHE ESQUADRIAS ELEVADAS
ESCALA 1/125

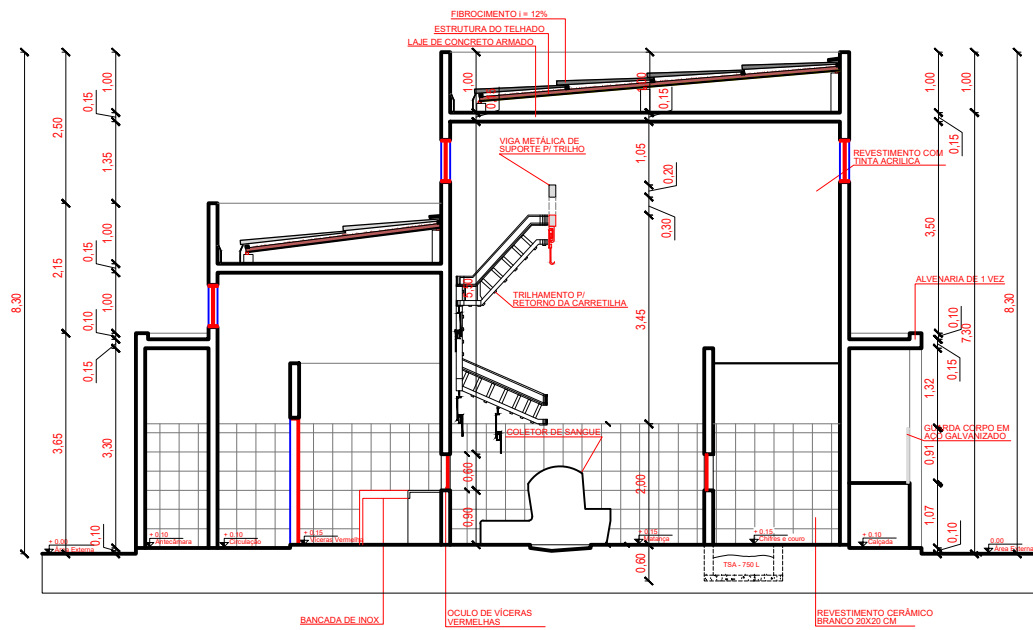


CORTE _ AA
ESCALA 1/125

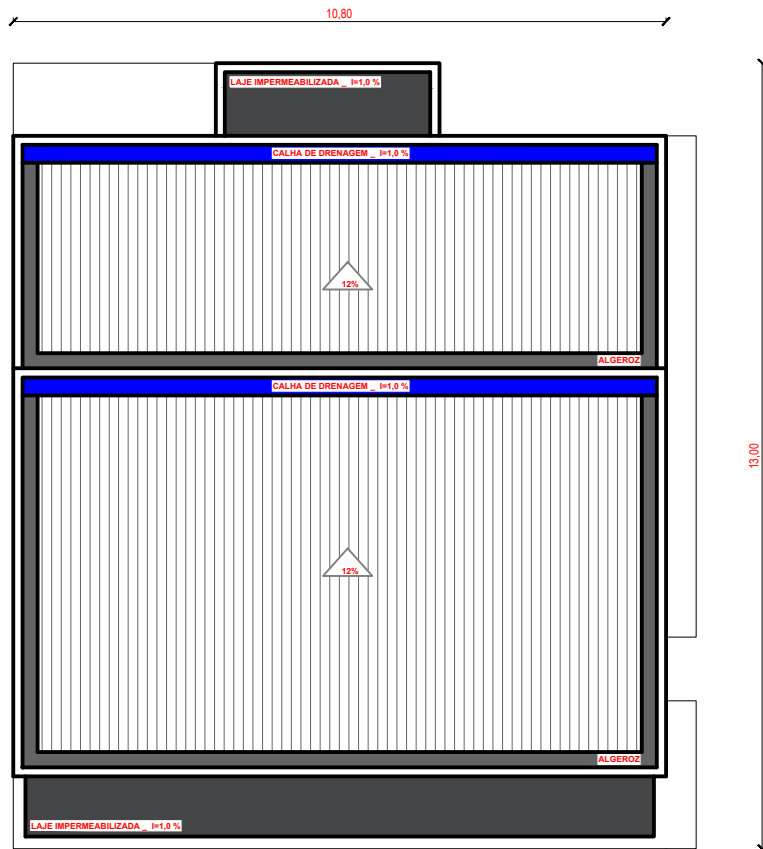


PLANTA DE COBERTA
ESCALA 1/125

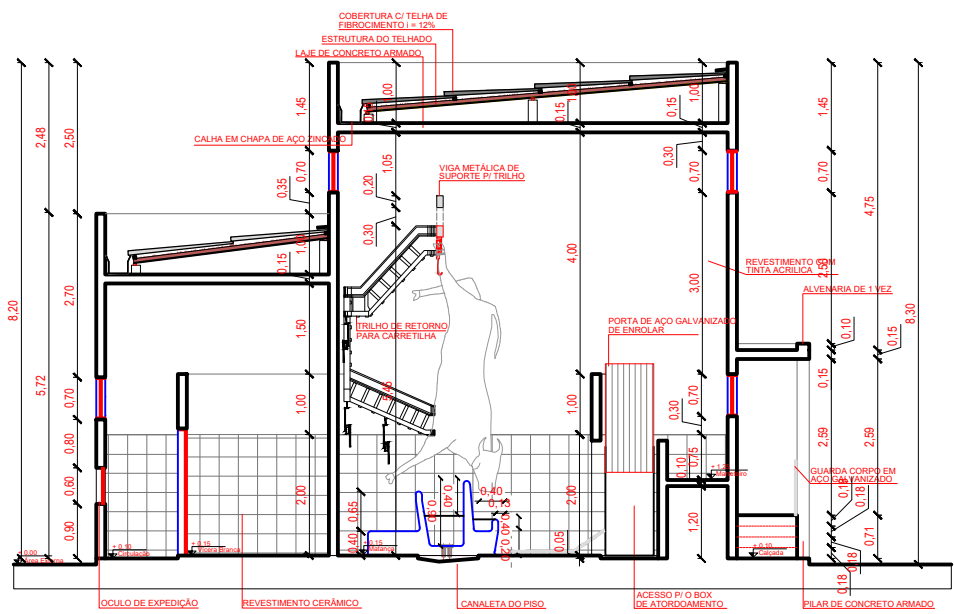



CORTE _ BB
ESCALA 1/125

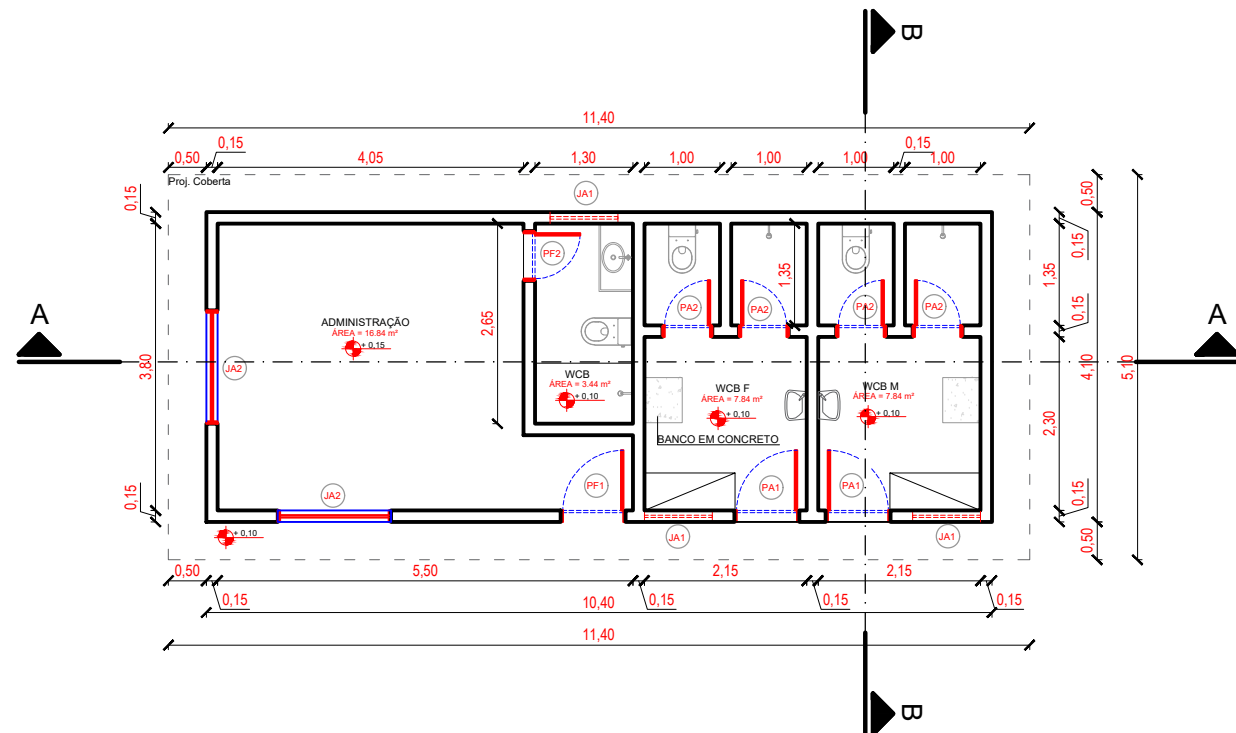


PLANTA BAIXA _ ADMINISTRAÇÃO
ESCALA 1/100

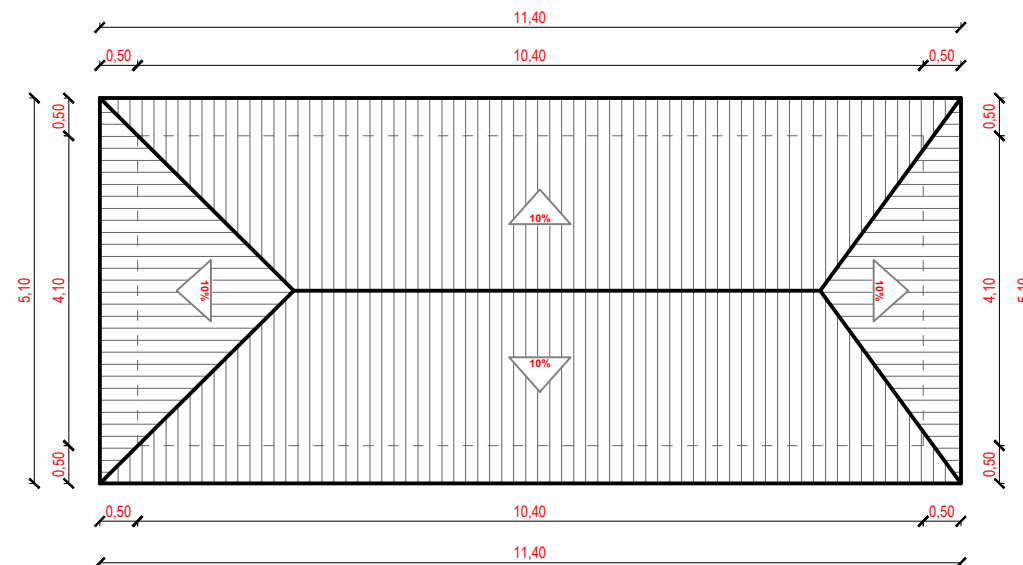


PLANTA DE COBERTA
ESCALA 1/100

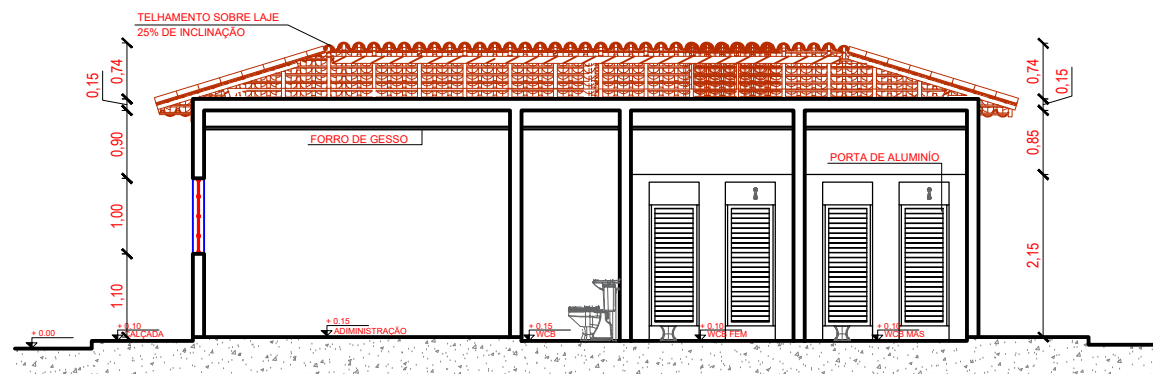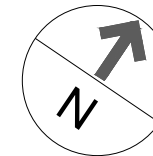

CORTE _ AA
ESCALA 1/100

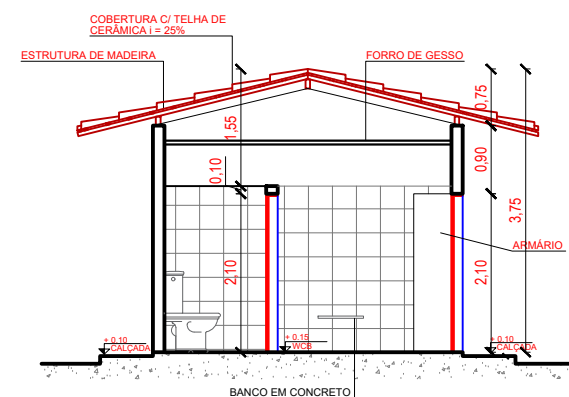

CORTE _ BB
ESCALA 1/100

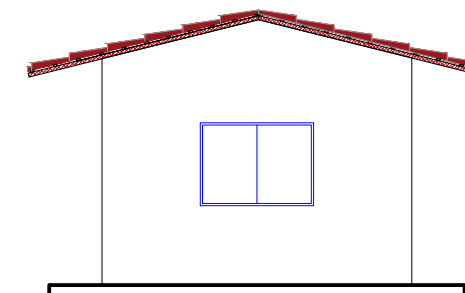

FACHADA LATERAL
ESCALA 1/100

QUADRO DE ESQUADRIA - (ADMINISTRAÇÃO)

TIPO	DESCRIÇÃO	LARGURA	ALTURA	FOLHAS	PEITORIL	QUANT.:
PF1	PORTA DE FERRO	0.80	2.10	1	-	1
PF2	PORTA DE FERRO	0.60	2.10	1	-	1
PA1	PORTA DE ALUMÍNIO	0.80	2.10	1	-	2
PA2	PORTA DE ALUMÍNIO	0.60	1.80	1	-	4
JA1	JANELA EM ALUMÍNIO	0.90	0.30	-	1.80	3
JA2	JANELA EM ALUMÍNIO	1.50	1.10	-	1.10	2