



Pilares P1=P2=P3=P4  
Cobrimento Nominal: 2,5cm


| Resumo Aço Pilares | Comp. total (m) | Peso+10% (kg) | Total |
|--------------------|-----------------|---------------|-------|
| CA-50-A Ø10        | 483,9           | 329           | 329   |
| CA-60-B Ø5         | 338,6           | 58            | 58    |
| Total              |                 |               | 387   |

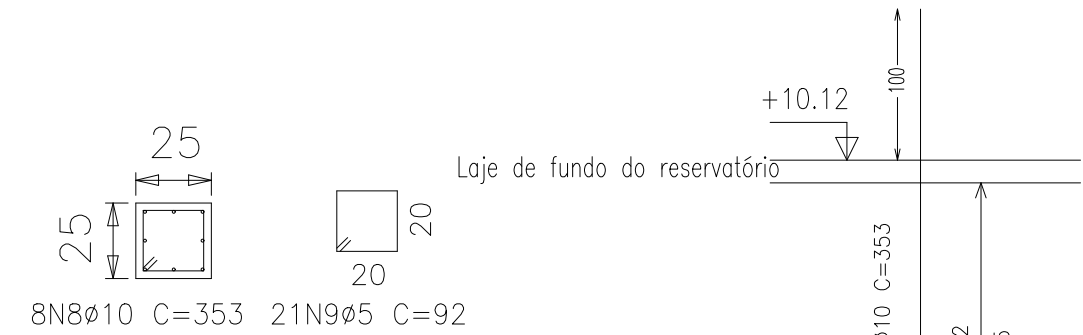


| Aço     | Pos. | Diam. | Q. | Comp. (cm) | Total (cm) | x 4 (cm) |
|---------|------|-------|----|------------|------------|----------|
| CA-50-A | 8    | Ø10   | 8  | 353        | 2824       | 11296    |
| CA-60-B | 9    | Ø5    | 21 | 92         | 1932       | 7728     |

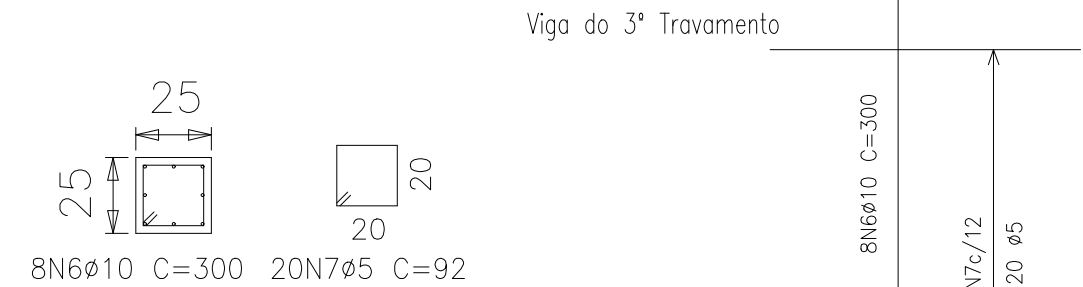

| Aço     | Pos. | Diam. | Q. | Comp. (cm) | Total (cm) | x 4 (cm) |
|---------|------|-------|----|------------|------------|----------|
| CA-50-A | 6    | Ø10   | 8  | 300        | 2400       | 9600     |
| CA-60-B | 7    | Ø5    | 20 | 92         | 1840       | 7360     |

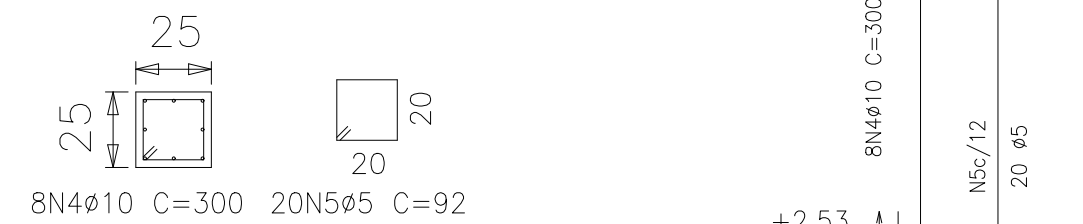


| Aço     | Pos. | Diam. | Q. | Comp. (cm) | Total (cm) | x 4 (cm) |
|---------|------|-------|----|------------|------------|----------|
| CA-50-A | 4    | Ø10   | 8  | 300        | 2400       | 9600     |
| CA-60-B | 5    | Ø5    | 20 | 92         | 1840       | 7360     |

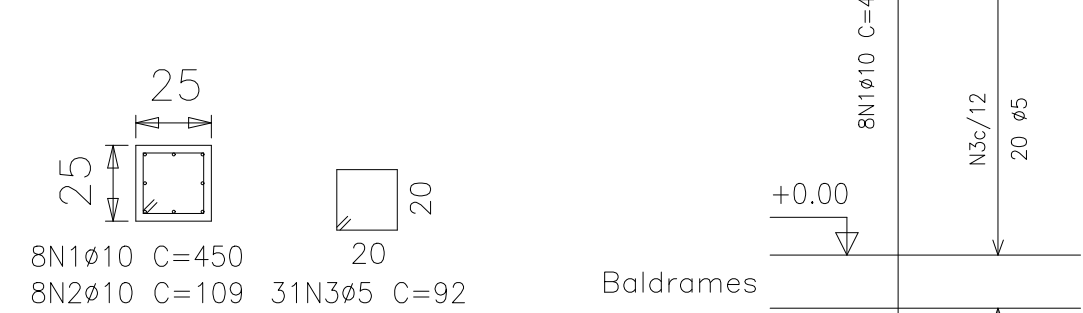


| Aço     | Pos. | Diam. | Q. | Comp. (cm) | Total (cm) | x 4 (cm) |
|---------|------|-------|----|------------|------------|----------|
| CA-50-A | 1    | Ø10   | 8  | 450        | 3600       | 14400    |
| CA-60-B | 2    | Ø10   | 8  | 109        | 872        | 3488     |
| CA-60-B | 3    | Ø5    | 31 | 92         | 2852       | 11408    |




Detalhamento dos Pilares  
escala → 1/50

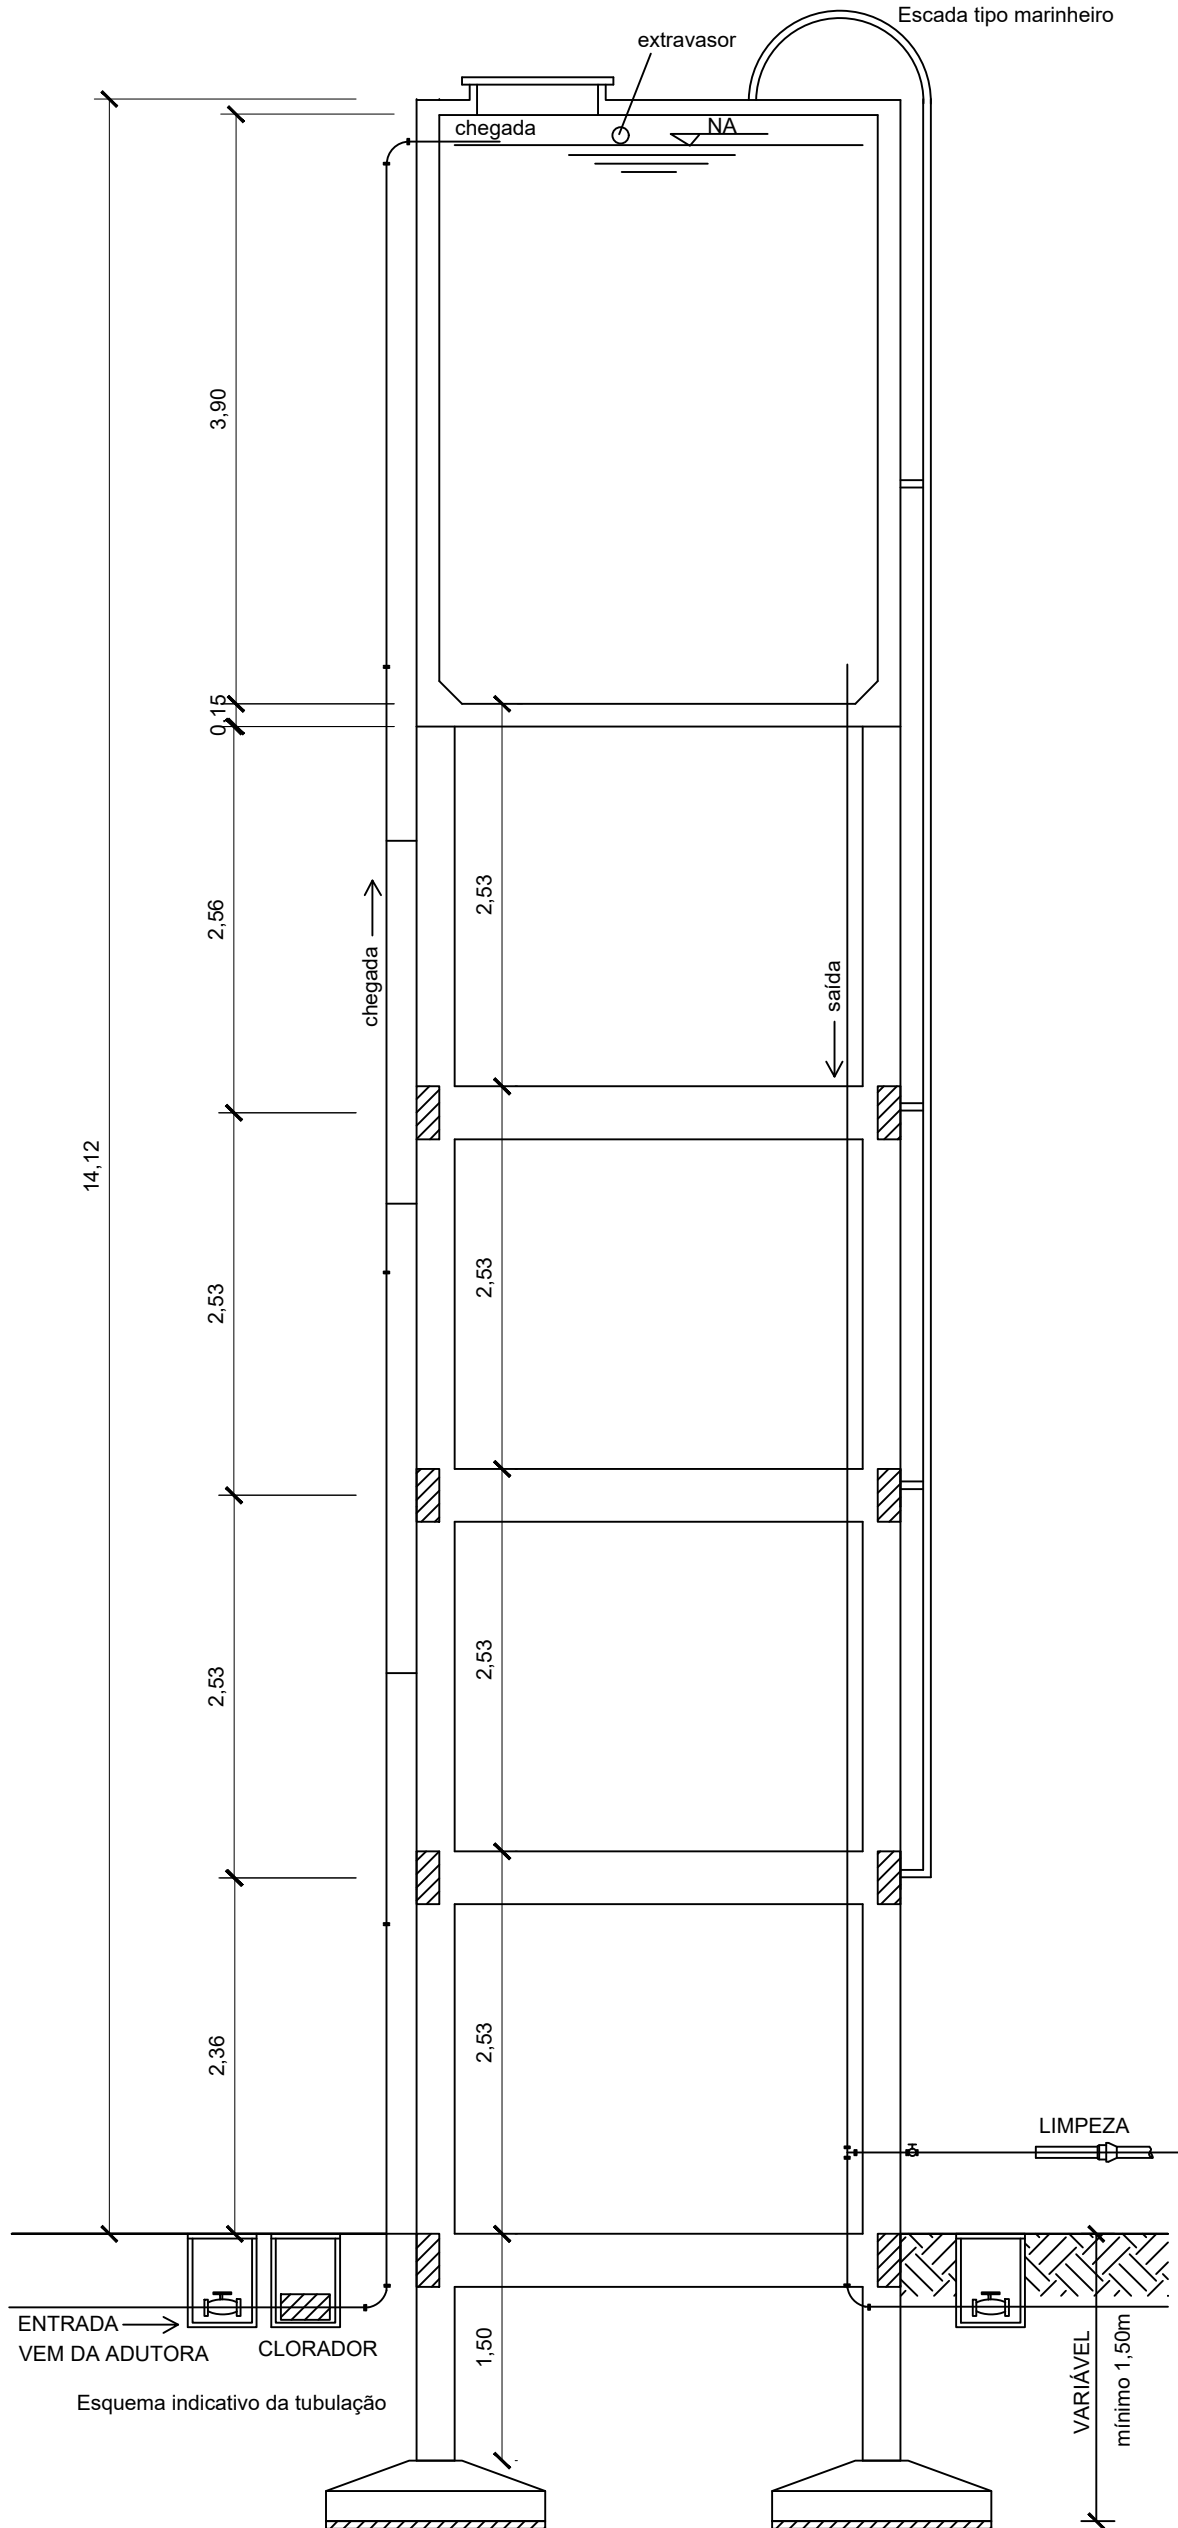


Seção da estrutura  
escala → 1/50

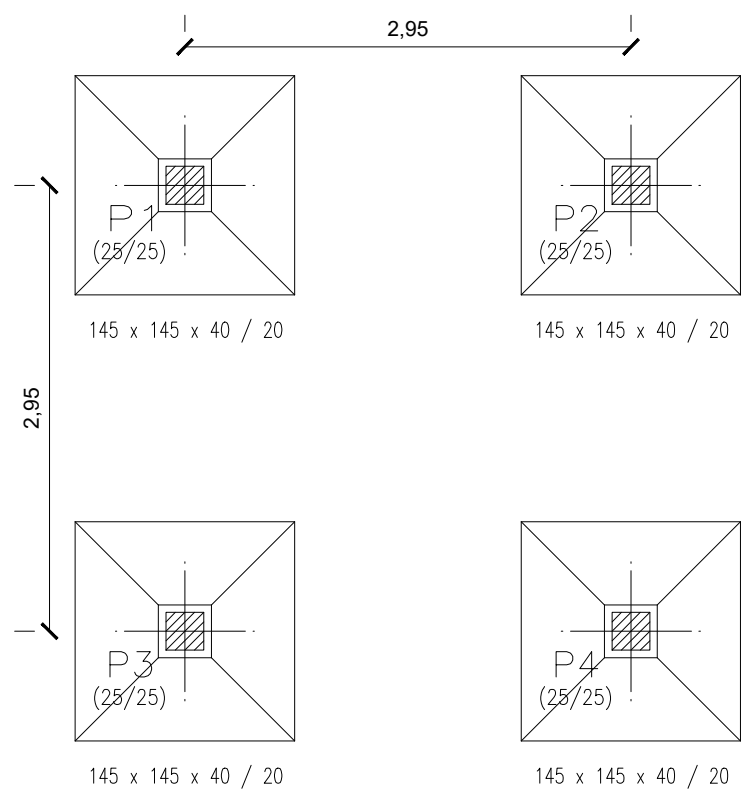

Planta de Forma das fundações  
escala → 1/50

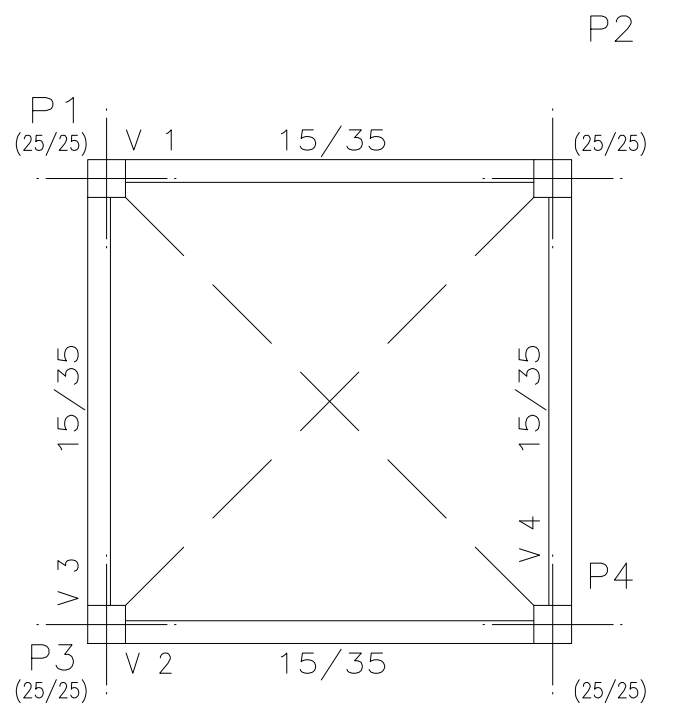

Planta de Forma vigas de travamento  
escala → 1/50

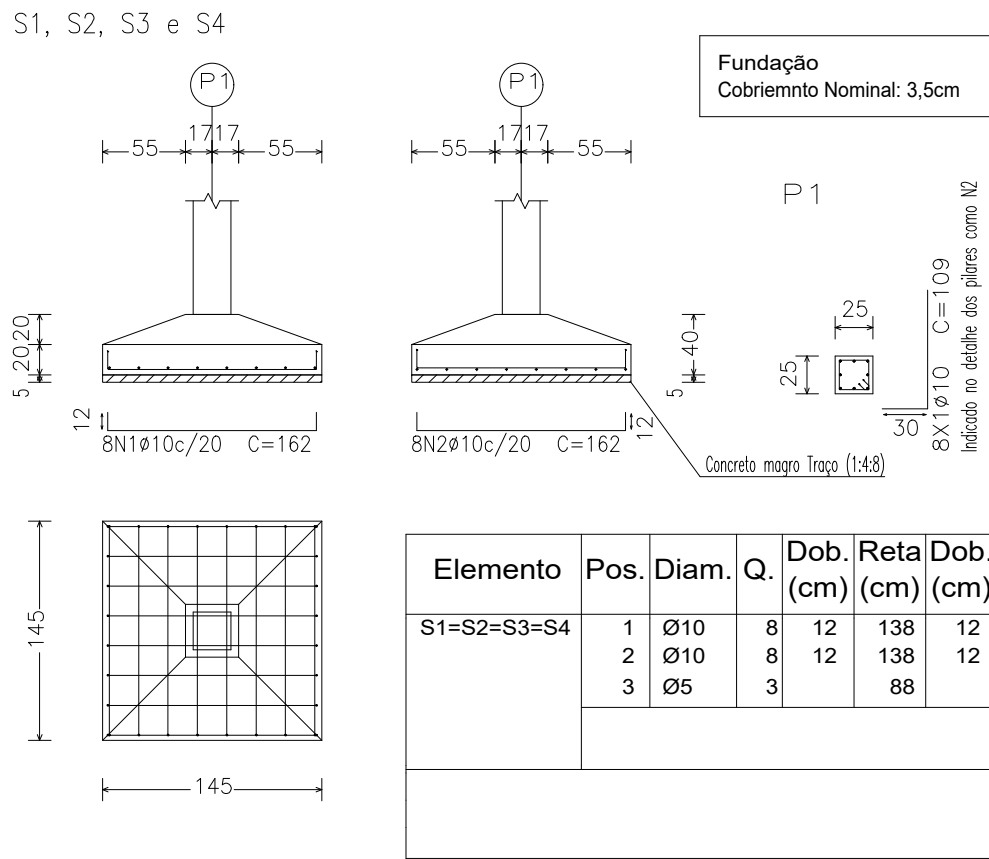

Detalhamento de Sapatas  
escala → 1/50

|                      |      |   |  |                 |           |
|----------------------|------|---|--|-----------------|-----------|
| RESPONSÁVEL TÉCNICO: |      |   |  |                 |           |
| PROPRIETÁRIO:        |      |   |  |                 |           |
| PRANCHA<br><br>2/2   |      | PREFEITURA MUNICIPAL DE COREMAS – PB   |  |                 |           |
|                      |      | PROJETO DE CONSTRUÇÃO DE MATADOURO – 9389922022   |  |                 |           |
|                      |      | PROJETO ESTRUTURAL - RESERVATÓRIO DE ASTECIMENTO DE ÁGUA   |  |                 |           |
|                      | DATA | RESPONSÁVEL   |  | RUBRICA         |           |
| DESENHO              |      |   |  |                 |           |
| PROJETO              |      |   |  | ÁREA DO TERRENO | ÁREA ÚTIL |
| CÓPIA                |      |   |  | 10.000,00 M²    | 971,43 M² |
| ESCALA:              |      | DESENHO:<br>DETALHAMENTO DOS PILARES<br>SEÇÃO DA ESTRUTURA<br>PLANTA DE FORMA DAS FUNDACÕES<br>PLANTA DE FORMA VIGAS DE TRAVAMENTO<br>DETALHAMENTO DE SAPATAS |  | ÁREA CONSTRUIDA | 871,58 M² |
| 1:50                 |      |   |  |                 |           |
| 1:50                 |      |   |  |                 |           |
| 1:50                 |      |   |  |                 |           |
| 1:50                 |      |   |  |                 |           |

9389922022\_Reservatorio.superior\_Estrutural