




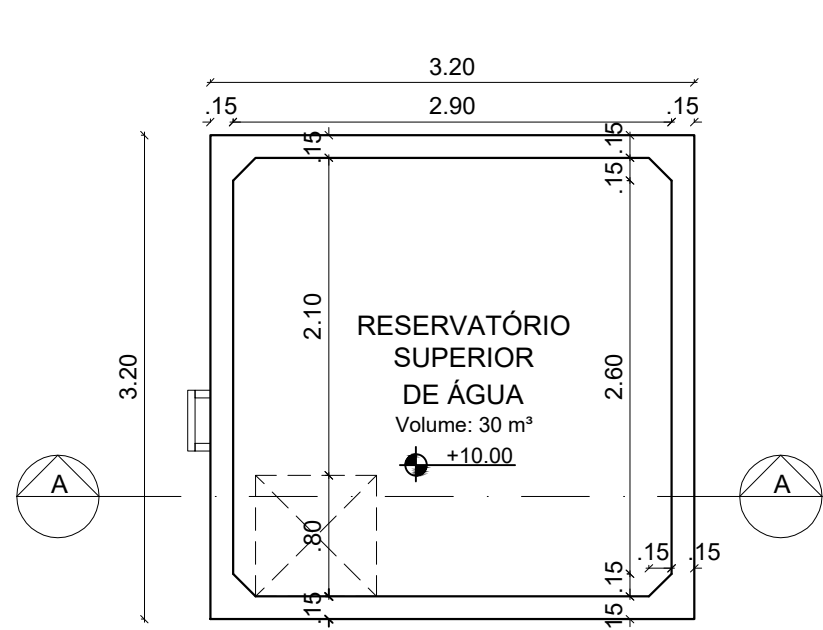


Planta Baixa – Reservatório Superior
escala 1/50

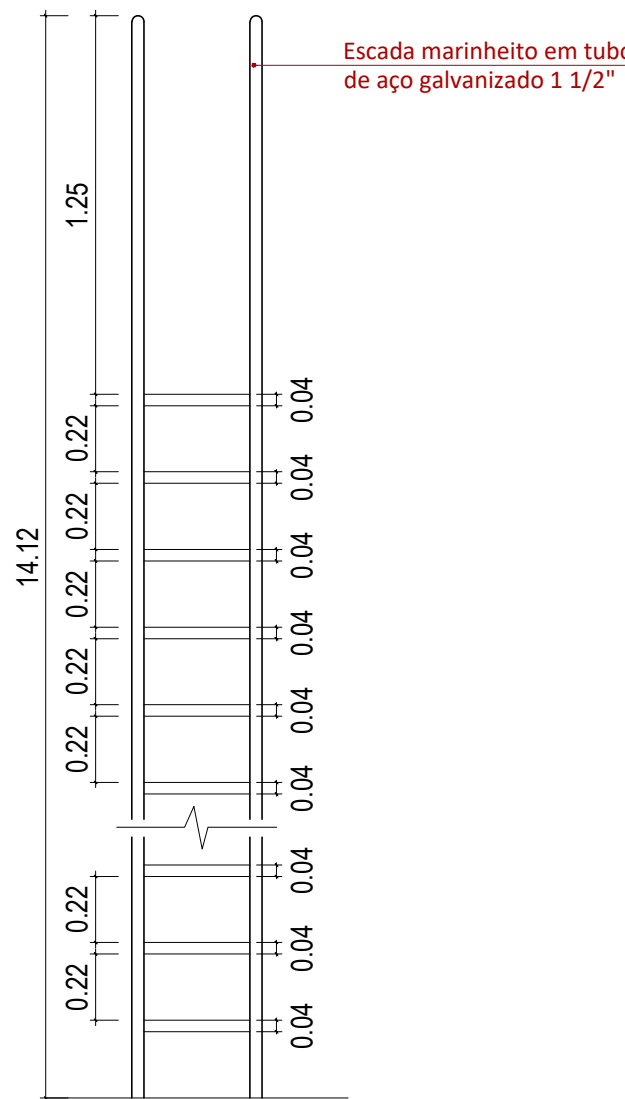


Detalhes – Escada Marinheiro
escala 1/25

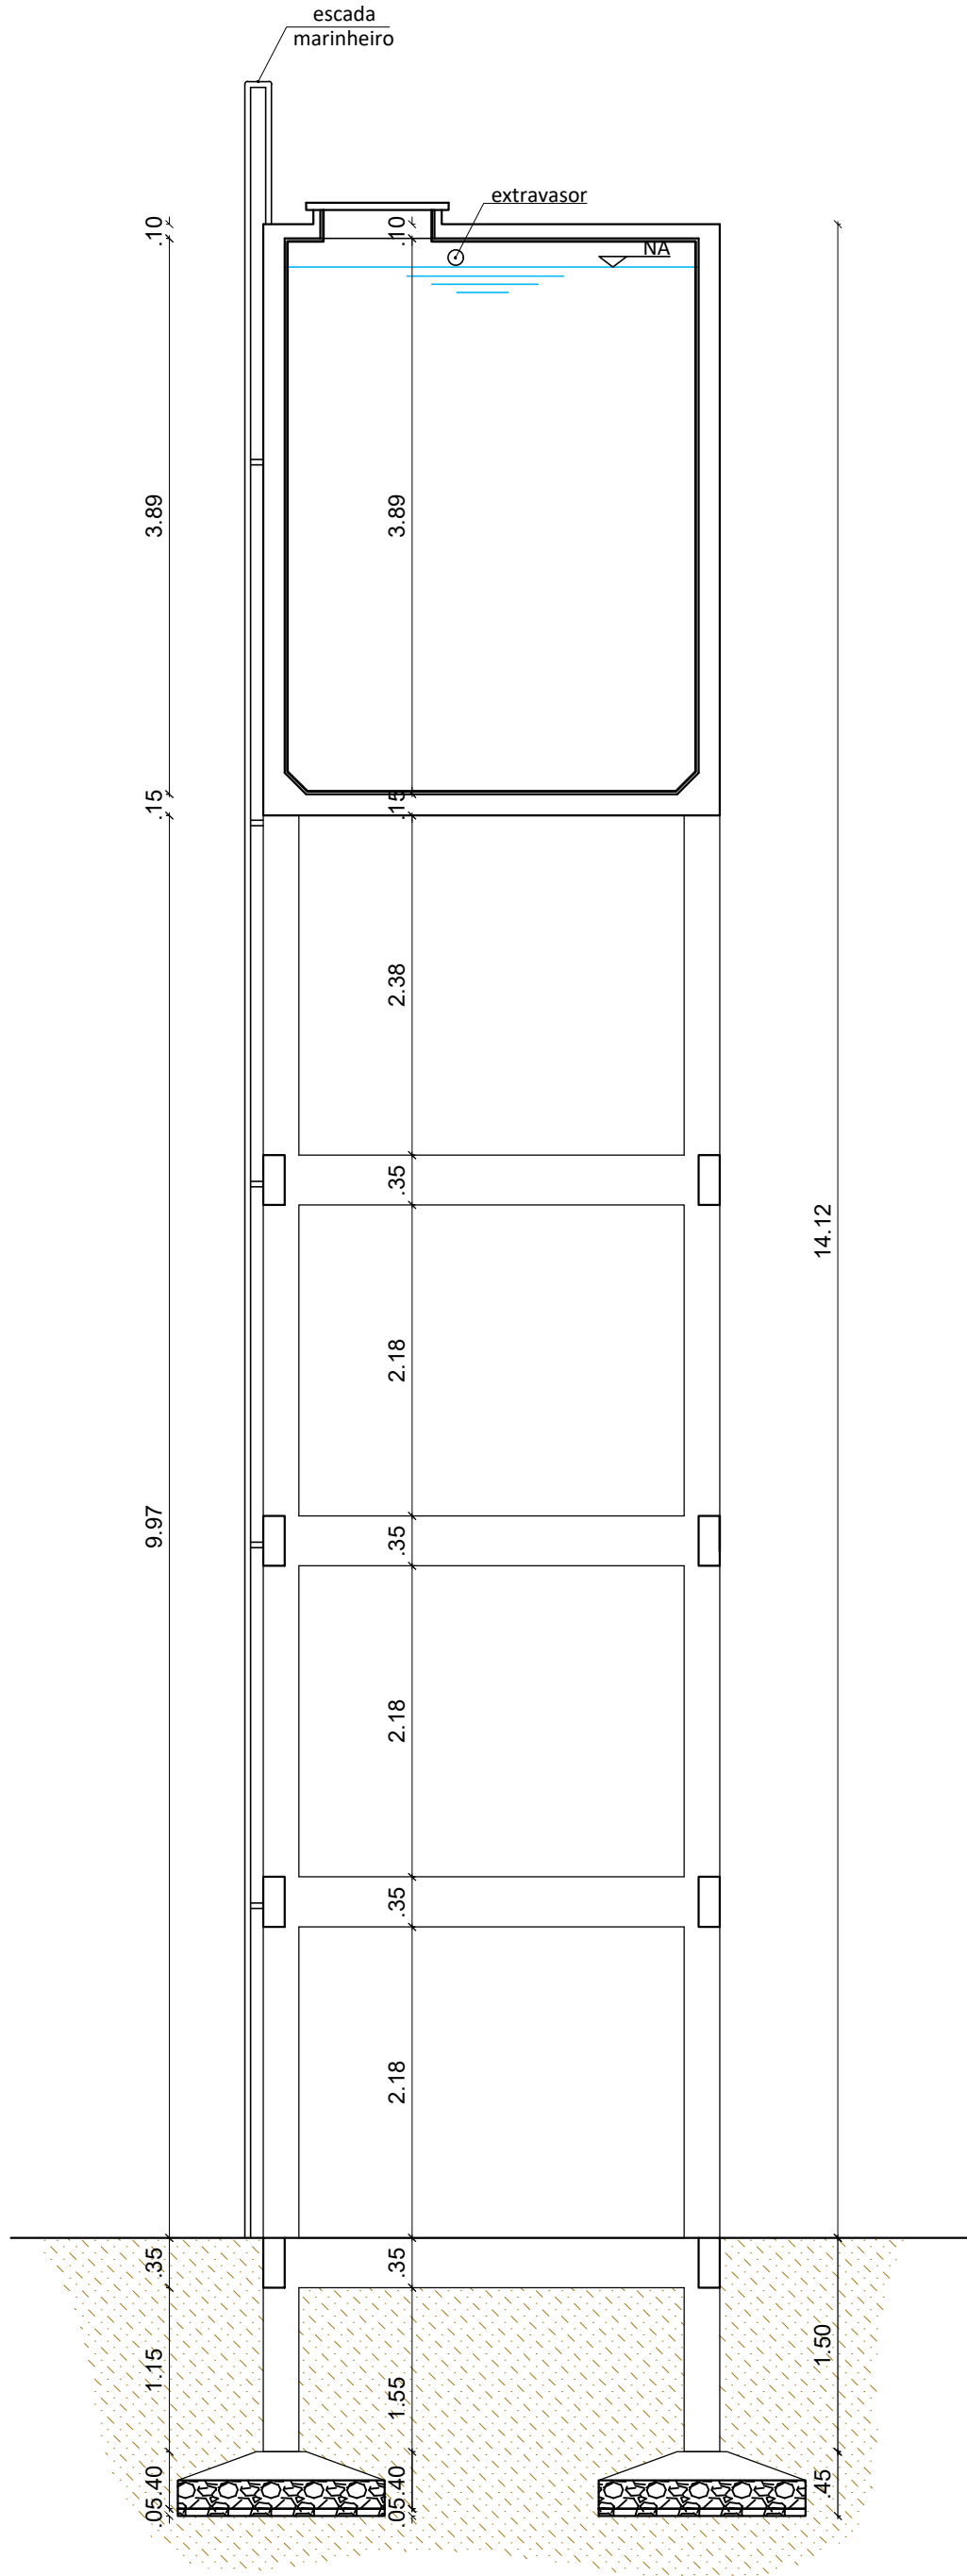

Corte AA – Reservatório Superior
escala 1/50

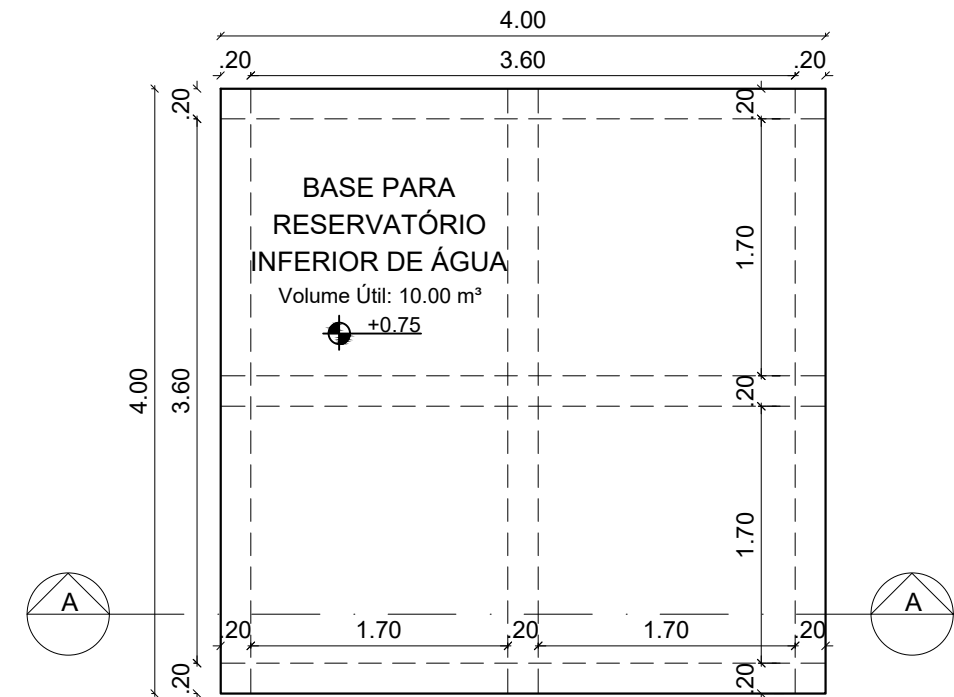

Planta Baixa – Base Reservatório Inferior
escala 1/50

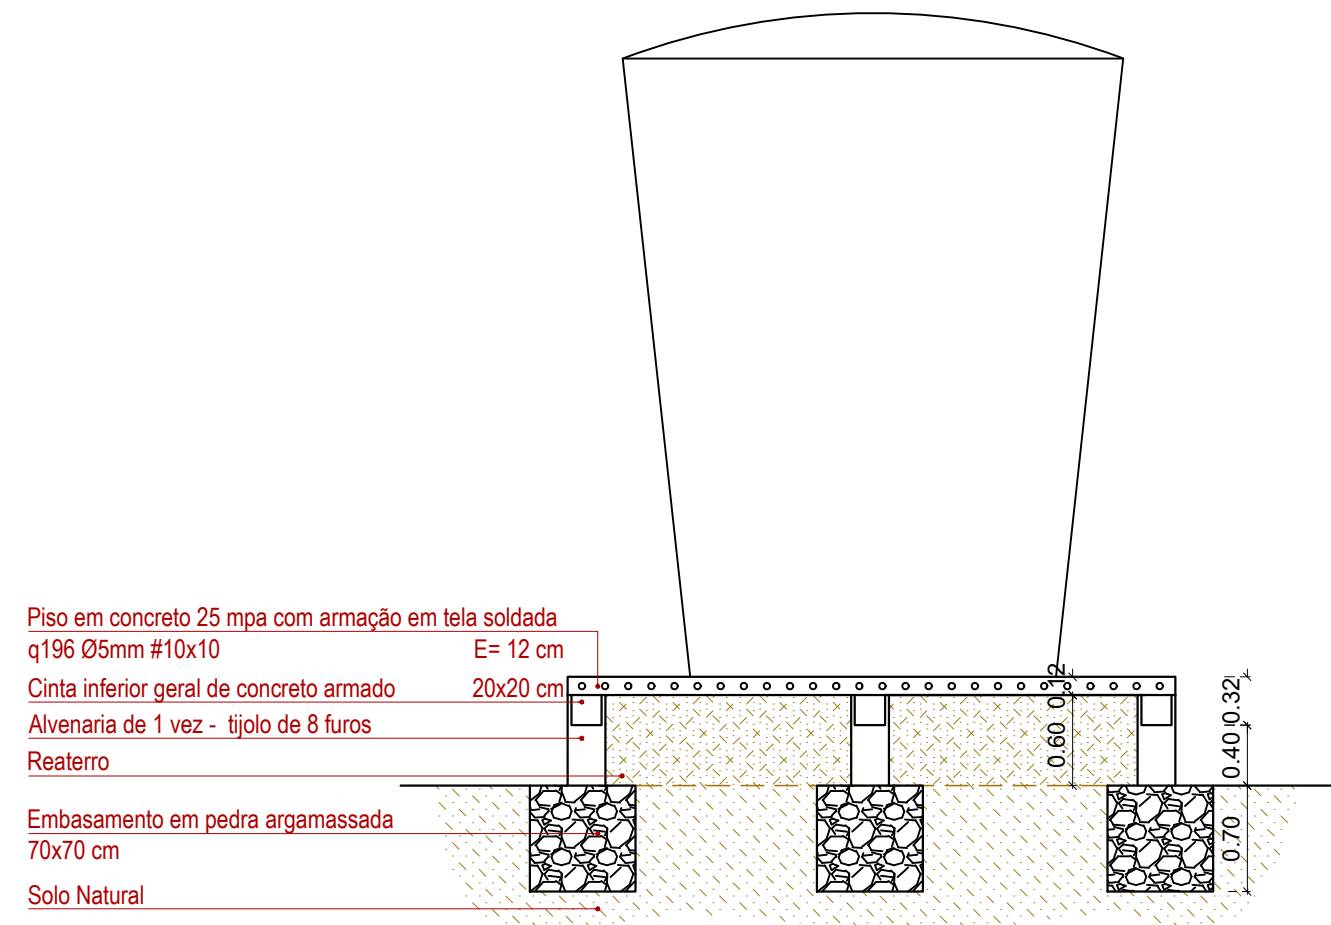

Corte AA – Base Reservatório Inferior
escala 1/50

Documento assinado digitalmente
MICHAEL JACKSON MAMEDE SOUZA
Data: 11/03/2024 15:32:23-0300
Verifique em <https://validar.it.gov.br>

RESPONSÁVEL TÉCNICO:

PROPRIETÁRIO:

PRANCHA		PREFEITURA MUNICIPAL DE COREMAS – PB		
1/2		PROJETO DE CONSTRUÇÃO DE MATADOURO – 9389922022		
		PROJETO ARQUITETÔNICO – RESERVATÓRIO DE ÁGUA		
	DATA	RESPONSÁVEL	RUBRICA	
DESENHO				
PROJETO			ÁREA DE TERRENO	ÁREA CONSTRUÍDA
CÓPIA			10.000,00 M²	871,58 M²
ESCALA:		DESENHO:		
1/50		PLANTA BAIXA – RESERVATÓRIO SUP.		
1/50		CORTE AA – RESERVATÓRIO SUP.		
1/50		PLANTA BAIXA – BASE RESERVATÓRIO INF.		
1/50		CORTE AA – BASE RESERVATÓRIO INF.		