


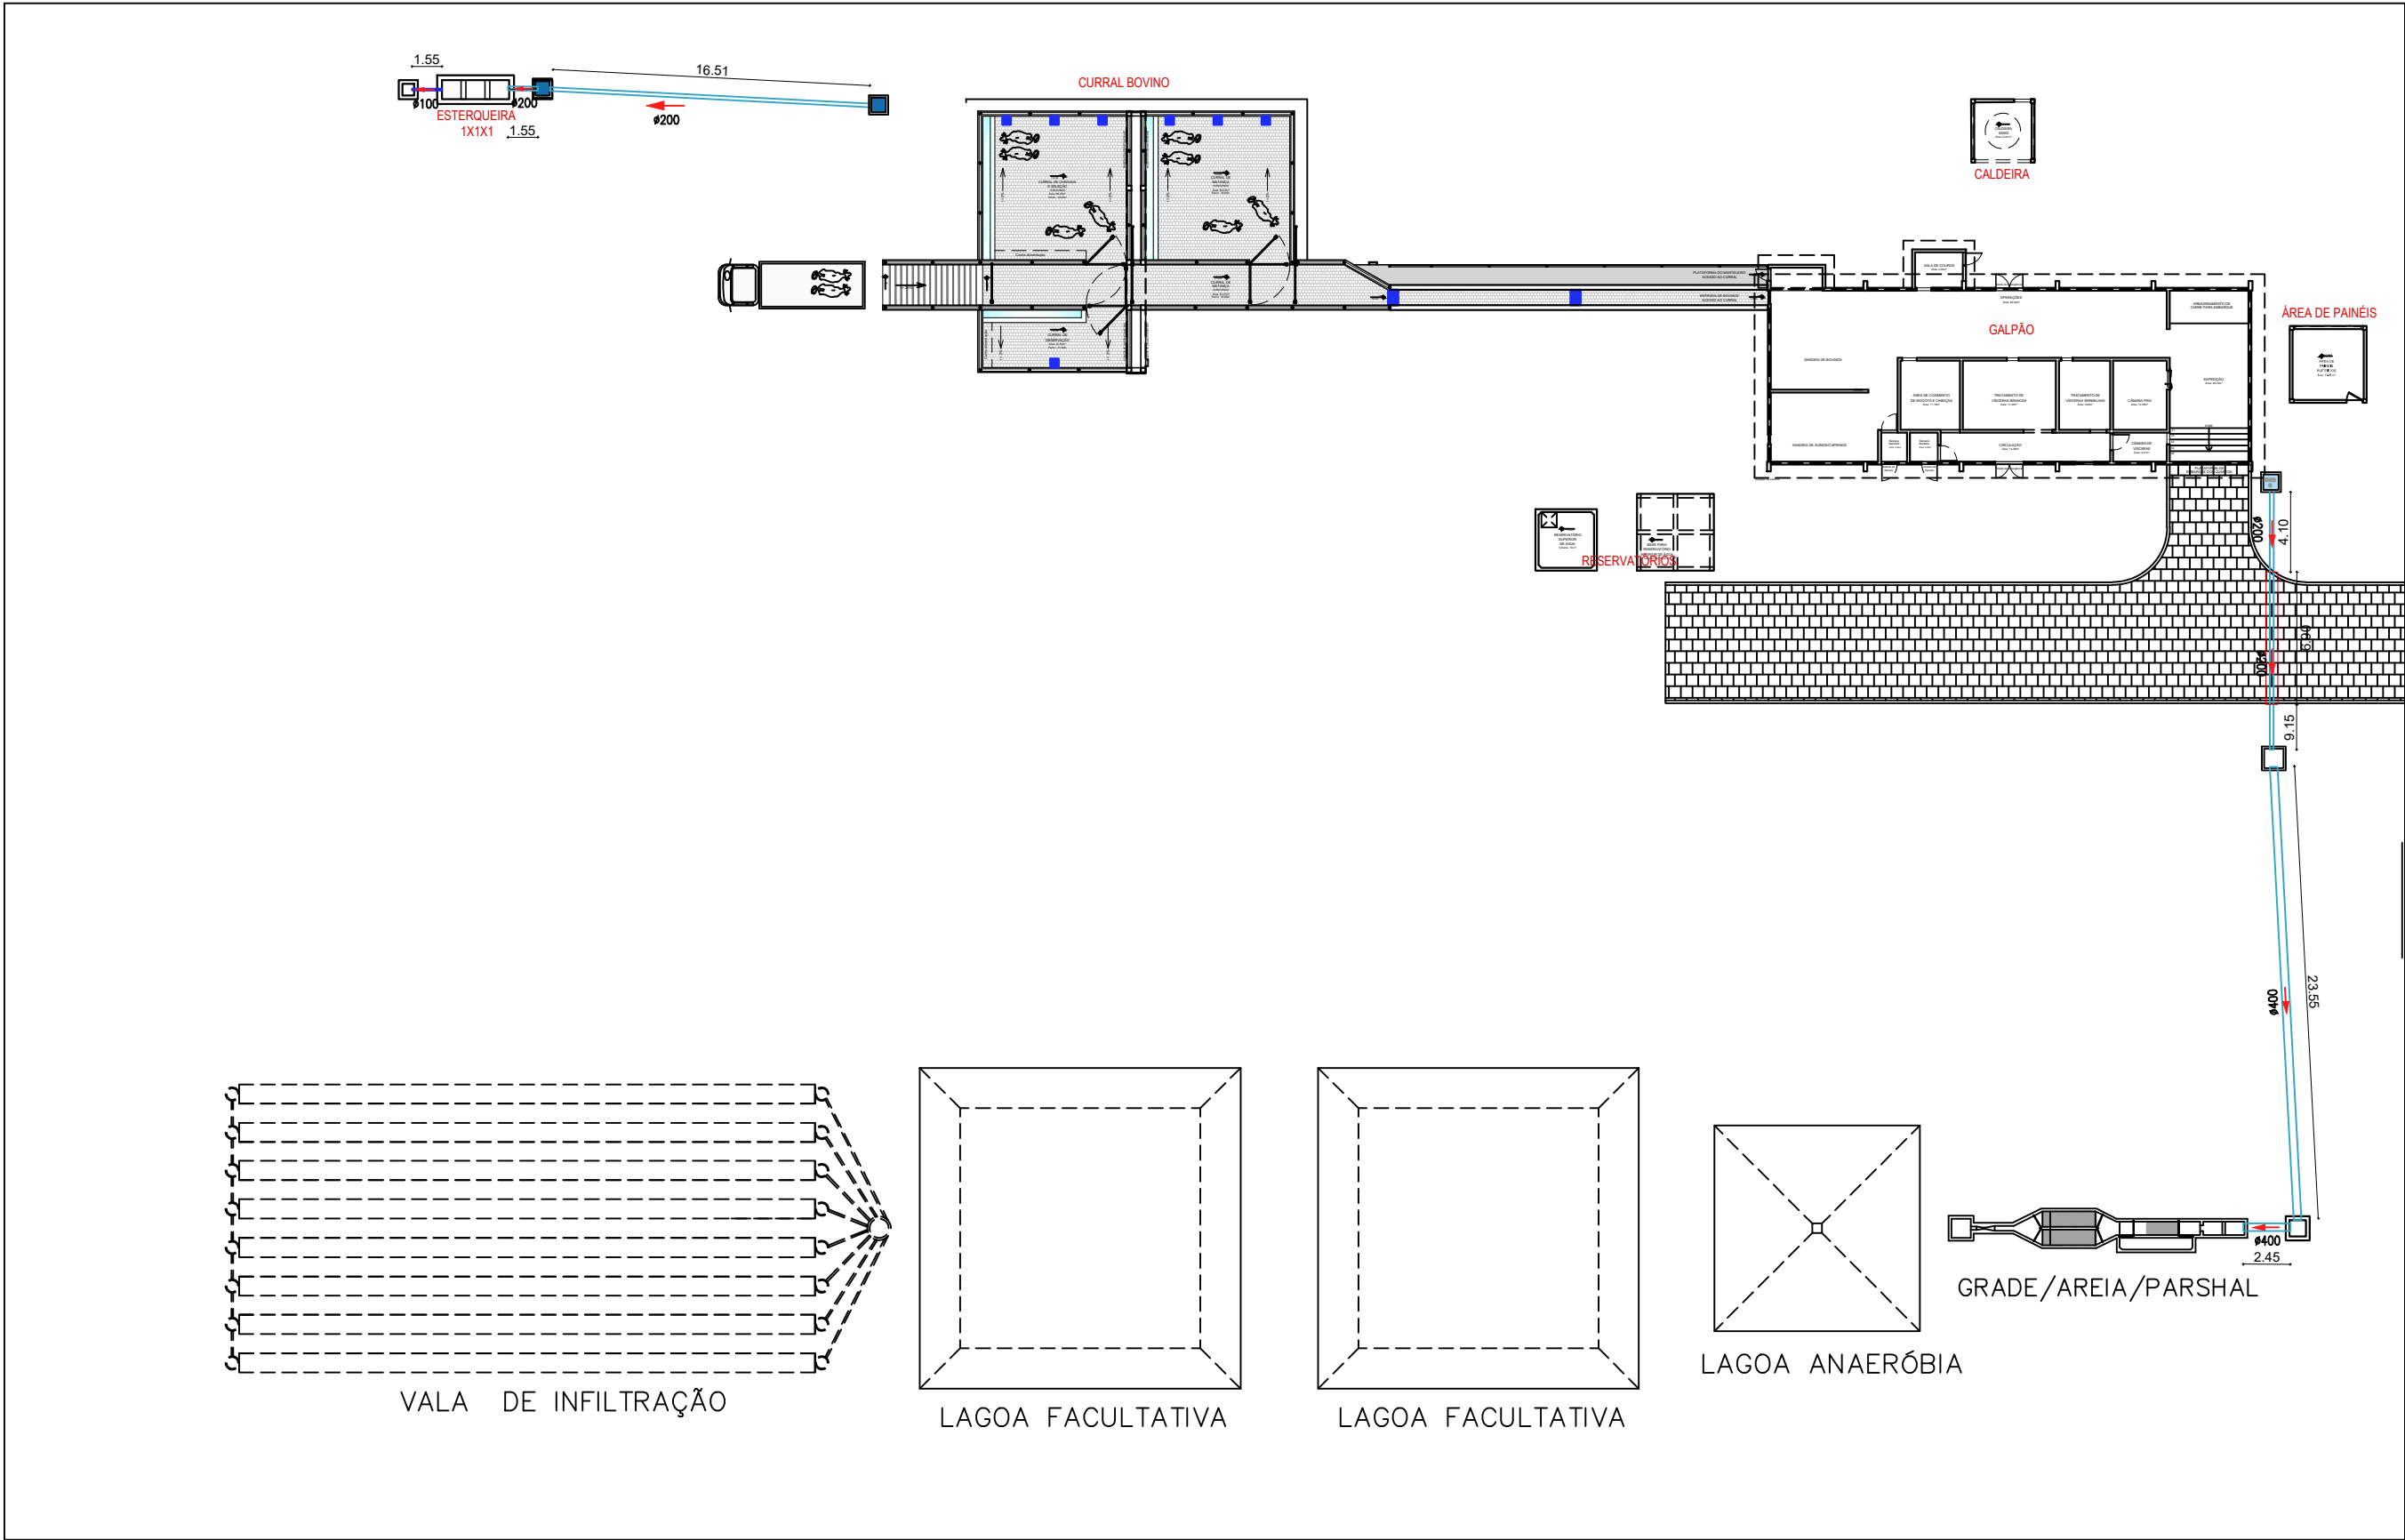

LEGENDA	
TUBULAÇÃO	
	- Tubo PVC corrugado em parede dupla 400mm
	- Tubo PVC corrugado em parede dupla 200mm
	- Tubo PVC Soldável branco 100mm
	- Tubo PVC corrugado com proteção mecânica
CAIXAS - SANITÁRIO	
	- Caixa de Gordura em alvenaria de tijolo de 8 furos 80 x 80 cm
	- Caixa de Inspeção em alvenaria de tijolo de 8 furos 100 x 100 cm
	- Caixa de Inspeção em alvenaria de tijolo de 8 furos 80 x 80 cm
	- Caixa de Inspeção em alvenaria de tijolo de 8 furos 60 x 60 cm
	A SER EXECUTADO POR ESTE CONVÊNIO
	A SER EXECUTADO COM RECURSOS PRÓPRIOS PELA PREF. MUNICIPAL
	A SER EXECUTADA EM FUTURAS ETAPAS

Planta Baixa Sanitário – Área Externa
escala 1/350

TUBULAÇÃO SANITÁRIO EXTERNO				
Quant.	Und.	Dimensão	Descrição	
26.00	m	400mm	Tubo PVC corrugado parede dupla marrom	
36.75	m	200mm	Tubo PVC corrugado parede dupla marrom	
1.55	m	100mm	Tubo PVC parede maciça marrom	
6.90	m	200mm	Tubo PVC corrugado c/ prot. mecânica	
2.00	unid.	100x100cm	Caixa de inspeção em alvenaria de tijolos	
1.00	unid.	80x80cm	Caixa de inspeção em alvenaria de tijolos	
1.00	unid.	60x60cm	Caixa de inspeção em alvenaria de tijolos	

NOTAS TÉCNICAS - PROJETO SANITÁRIO MATADOURO PÚBLICO	
- NT 01: Tubulações PVC com diâmetro nominal igual a ou inferior a 75mm considerar declividade mínima de 2%.	
- NT 02: Tubulações PVC com diâmetro nominal igual a ou superior a 100mm considerar declividade mínima de 1%.	
- NT 03: A declividade máxima a ser considera para tubulações horizontais é de 5%.	
- NT 04: A concepção dos ramais de ventilação se deu conforme o que preconiza a "NBR 8160 - Sistemas prediais de esgoto sanitário - Projeto e execução", onde no seu item 4.3.11 estabelece que prédios de apenas um pavimento pode ser considerado tubo ventilador direto na caixa de inspeção.	

RESPONSÁVEL TÉCNICO:			
PROPRIETÁRIO:			
PRANCHA		PREFEITURA MUNICIPAL DE COREMAS – PB	
1/5		PROJETO DE CONSTRUÇÃO DE MATADOURO – 9389922022	
		PROJETO SANITÁRIO	
	DATA	RESPONSÁVEL	RUBRICA
DESENHO			
PROJETO			
CÓPIA			
ESCALA:			
1:350		DESENHO:	
		PLANTA BAIXA SANITÁRIO - ÁREA EXTERNA	
		ÁREA DE TERRENO	ÁREA CONSTRUÍDA
		10.000,00 M²	871,58 M²