




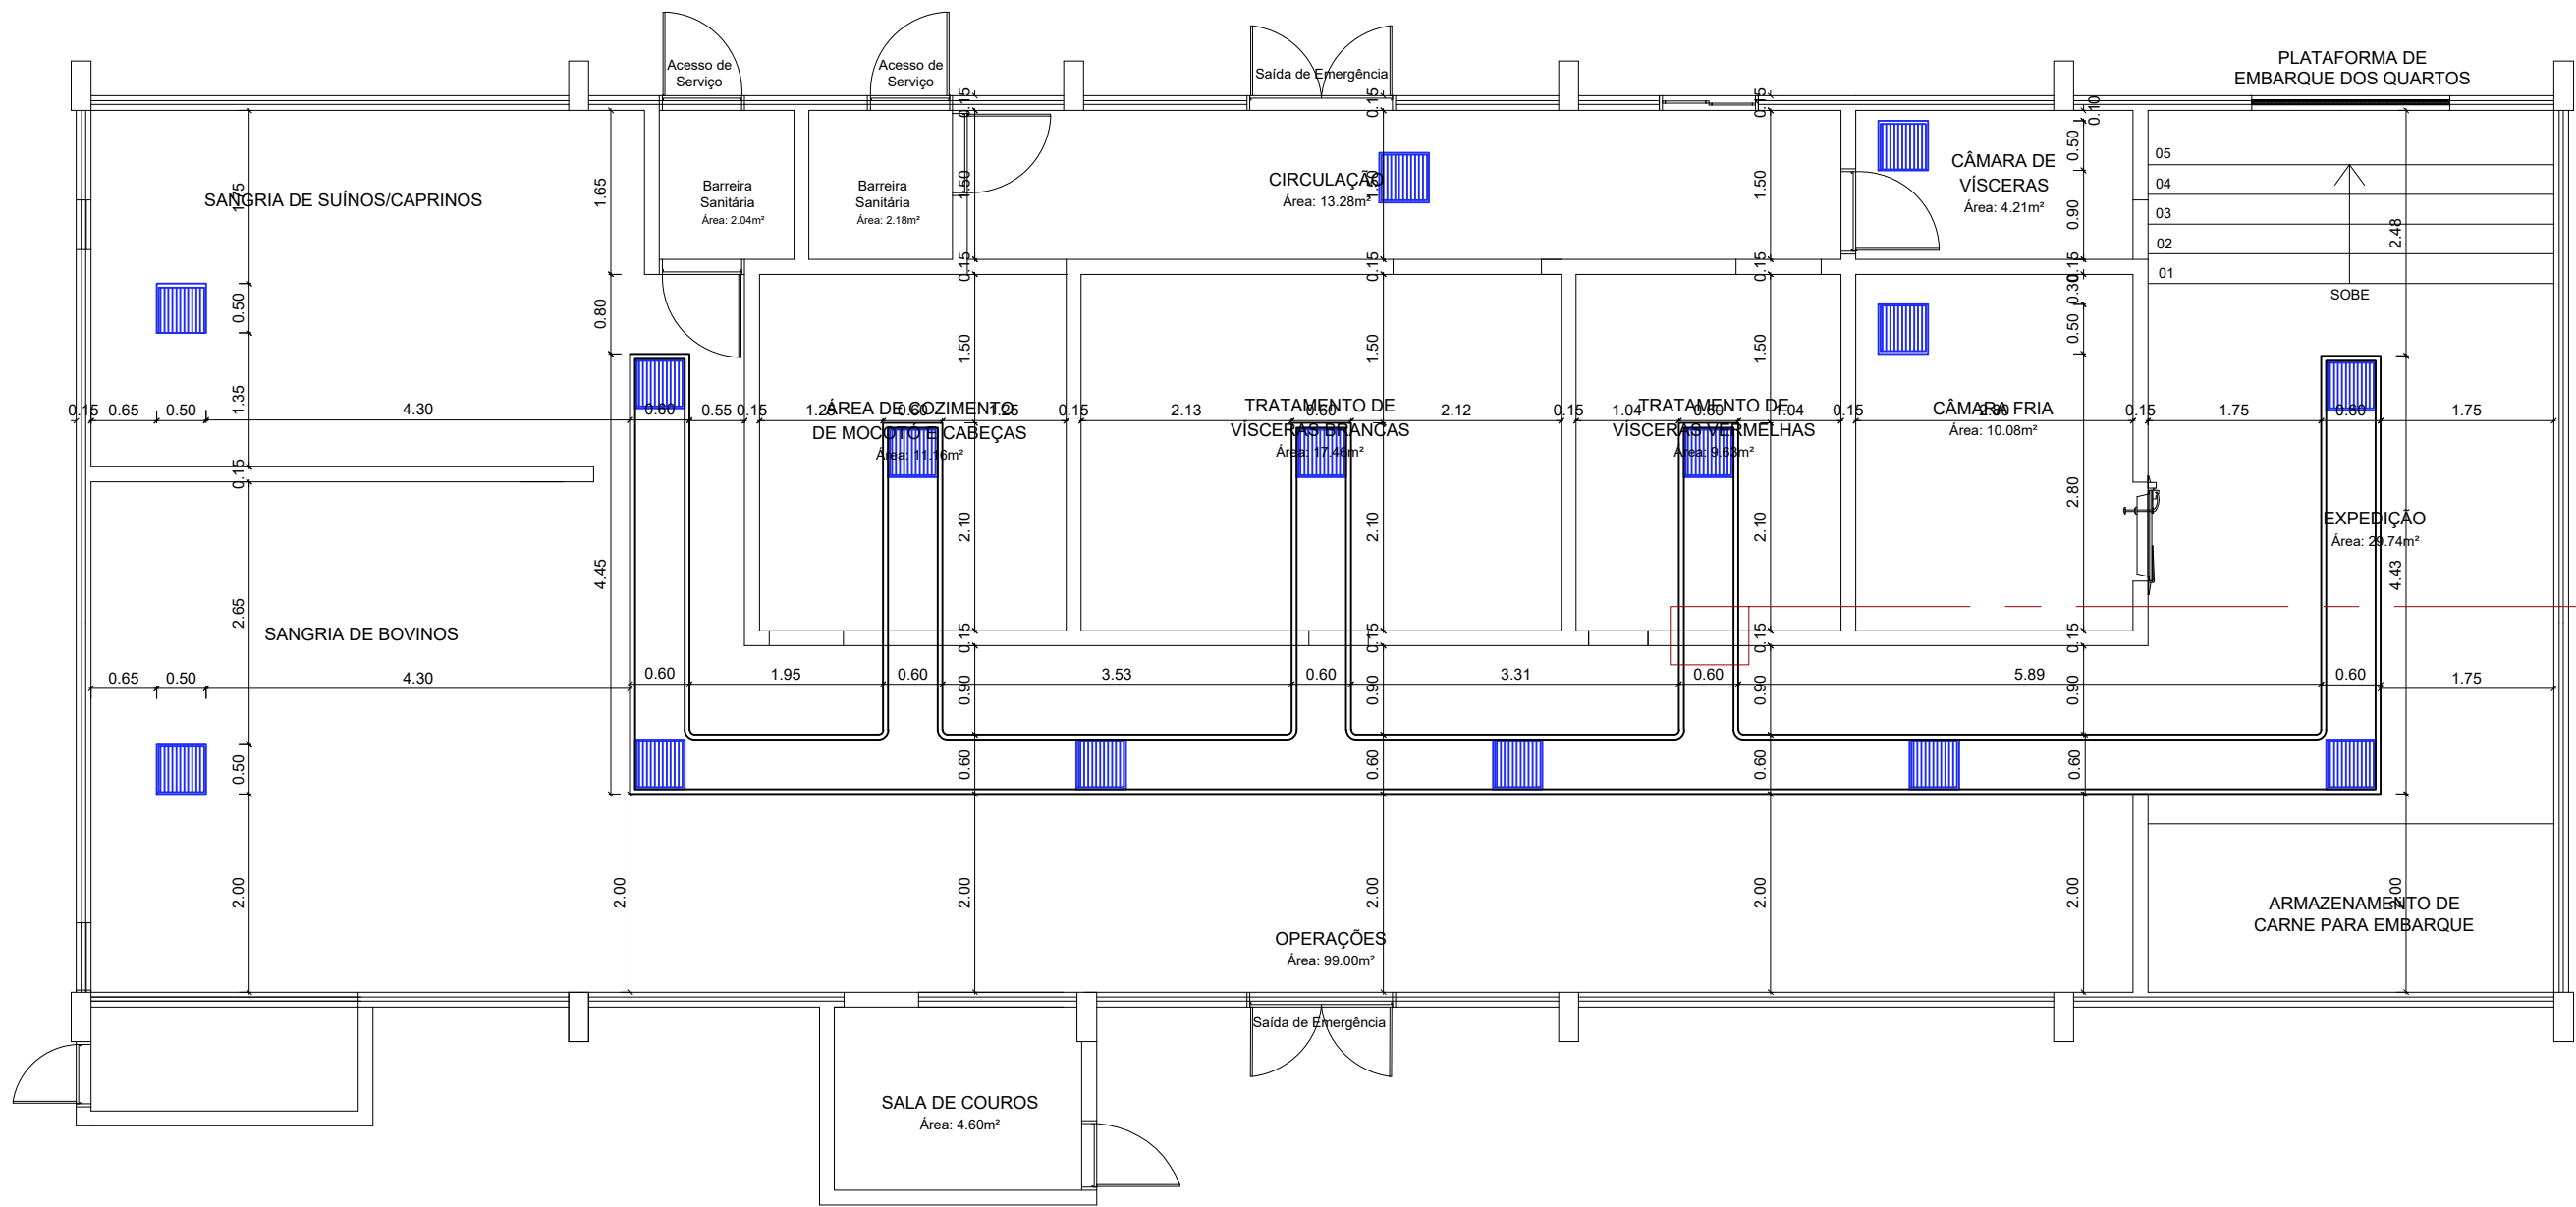


Planta Baixa Canaletas – Galpão
escala 1/75

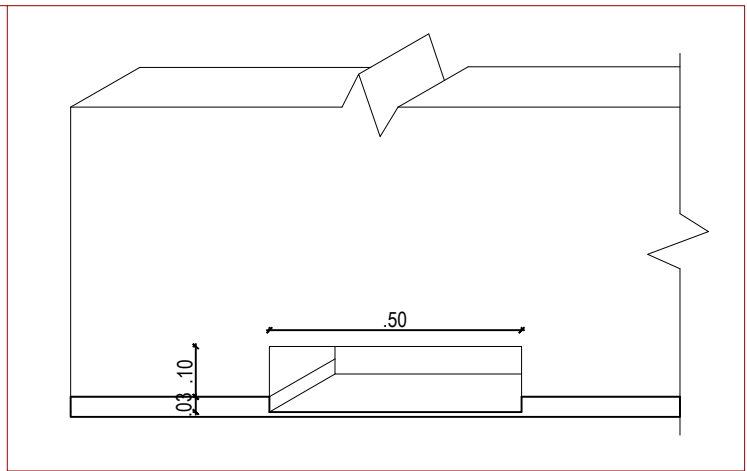


Detalhe – passagem sob paredes
escala 1/15

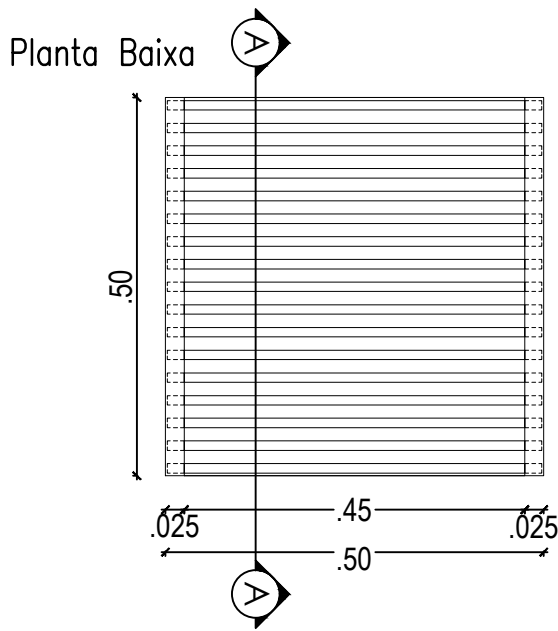


Corte AA

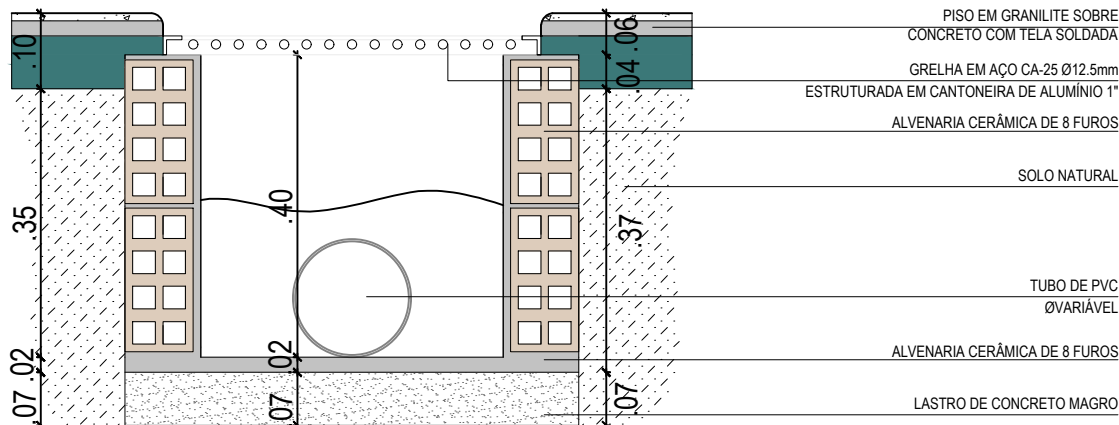

Detalhe – Grelha de drenagem
escala 1/10

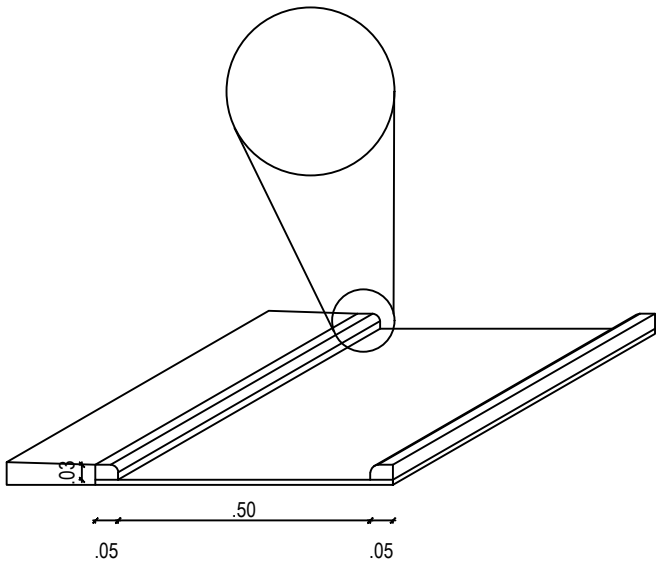

Detalhe – Canaleta
escala 1/10

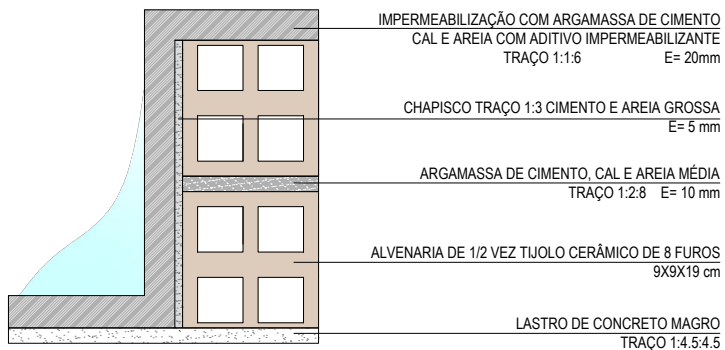

Detalhe – Grelha
escala 1/5

RESPONSÁVEL TÉCNICO:				
PROPRIETÁRIO:				
PRANCHA		PREFEITURA MUNICIPAL DE COREMAS – PB		
3/5		PROJETO DE CONSTRUÇÃO DE MATADOURO – 9389922022		
		PROJETO SANITÁRIO		
	DATA	RESPONSÁVEL	RUBRICA	
DESENHO				
PROJETO			ÁREA DE TERRENO	ÁREA CONSTRUÍDA
CÓPIA			10.000,00 M²	871,58 M²
ESCALA:	DESENHO:			
1:75	PLANTA BAIXA CANALETA - GALPÃO			
1:10	DETALHE - GRELHA DE DRENAGEM			
1:5	DETALHE - CANALETA			
1:5	DETALHE - PASSAGEM SOB PAREDES			