



ELEVAÇÃO SUPERIOR | BANCO 02
ESCALA 1/75

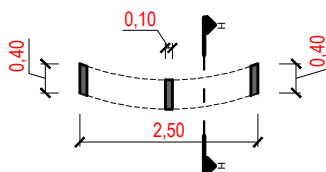


ELEVAÇÃO LATERAL | BANCO 02
ESCALA 1/75




PLANTA BAIXA | BANCO 02
ESCALA 1/75

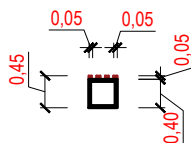


CORTE HH | BANCO 02
ESCALA 1/75

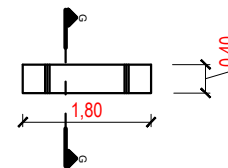


ELEVAÇÃO SUPERIOR | BANCO 01
ESCALA 1/75

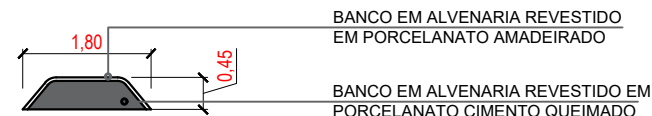


ELEVAÇÃO LATERAL | BANCO 01
ESCALA 1/75

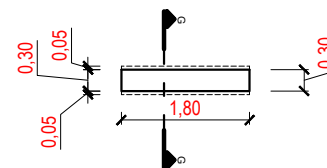

PLANTA BAIXA | BANCO 01
ESCALA 1/75

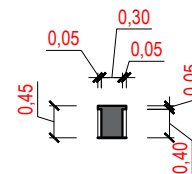


CORTE GG | BANCO 01
ESCALA 1/75

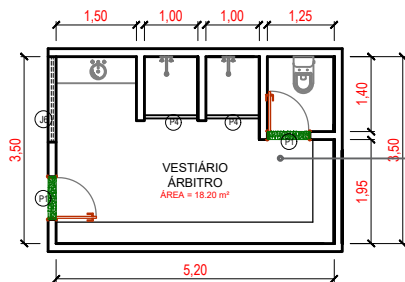

PLANTA BAIXA | VESTIÁRIO
ESCALA 1/100


PISO REVESTIDO EM
CERÂMICA ACETINADO TIPO
CIMENTO QUEIMADO

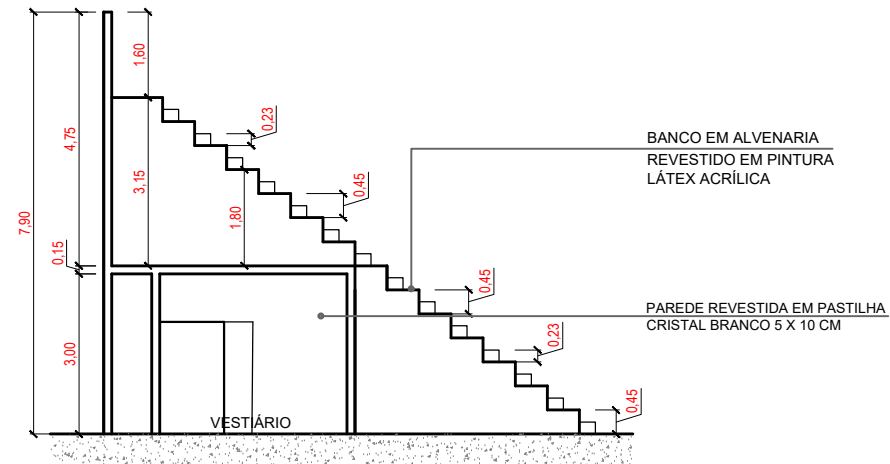





CORTE | CC
ESCALA 1/100


QUADRO DE ESQUADRIA

TIPO	DESCRIÇÃO	LARGURA	ALTURA	FOLHAS	PEITORIL	QUANT.:
P1	PORTA DE ALUMÍNIO	0.80	2.10	1	-	19
P2	PORTA DE MADEIRA	0.80	2.10	1	-	2
P3	PORTA DE MADEIRA	0.80	2.10	1	-	2
P4	PORTA DE ALUMÍNIO	0.80	2.10	1	-	10
P5	PORTÃO DE AÇO	4.00	2.10	1	-	1
P6	PORTÃO DE AÇO	1.20	2.10	1	-	2
P7	PORTÃO DE AÇO	3.50	2.10	1	-	1
J1	JANELA DE VIDRO - BASCULANTE	0.80	0.40	2	1.70	6
J2	JANELA DE MADEIRA - BASCULANTE	4.15	1.00	3	1.10	2
J3	JANELA DE MADEIRA - BASCULANTE	0.80	1.00	1	1.10	2
J4	JANELA DE MADEIRA - BASCULANTE	1.60	1.00	2	1.10	2
J5	JANELA DE CONCRETO - COBOGÓ	3.00	0.40	1	1.70	4
J6	JANELA DE CONCRETO - COBOGÓ	2.00	0.40	1	1.70	3
J7	JANELA DE CONCRETO - COBOGÓ	1.25	0.40	1	1.70	2
J8	JANELA DE VIDRO - CORRER	0.90	1.00	2	1.10	2
J9	JANELA DE VIDRO - CORRER	3.35	1.00	4	1.10	1

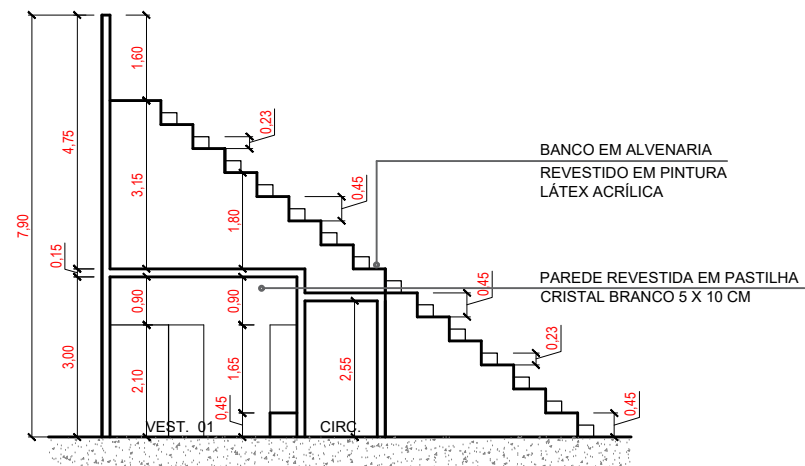


CORTE | AA
ESCALA 1/100

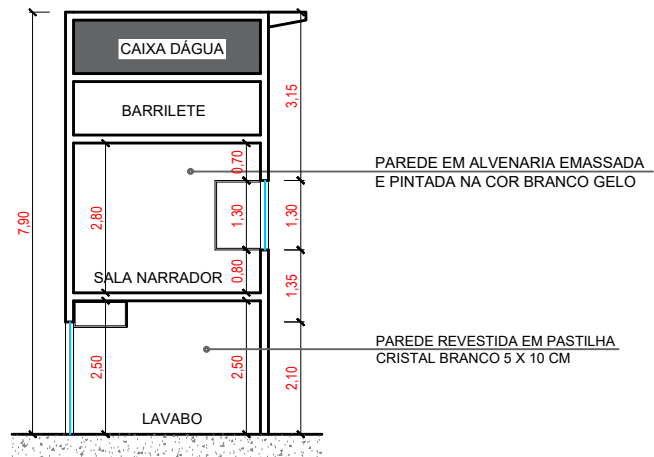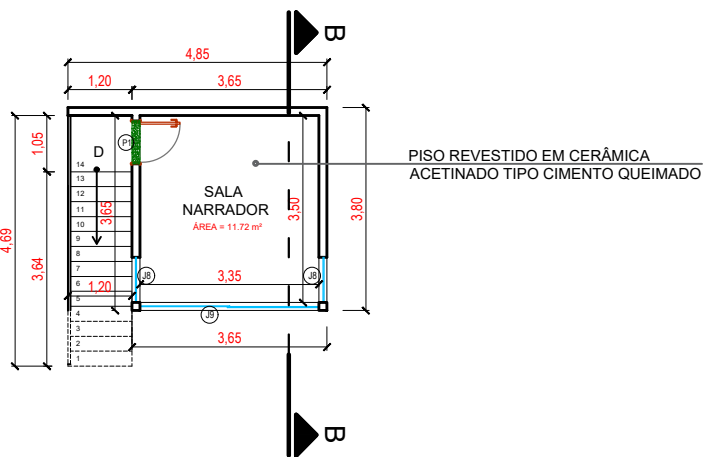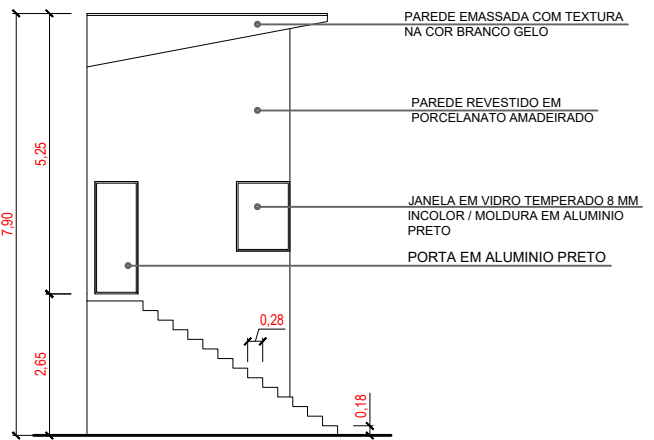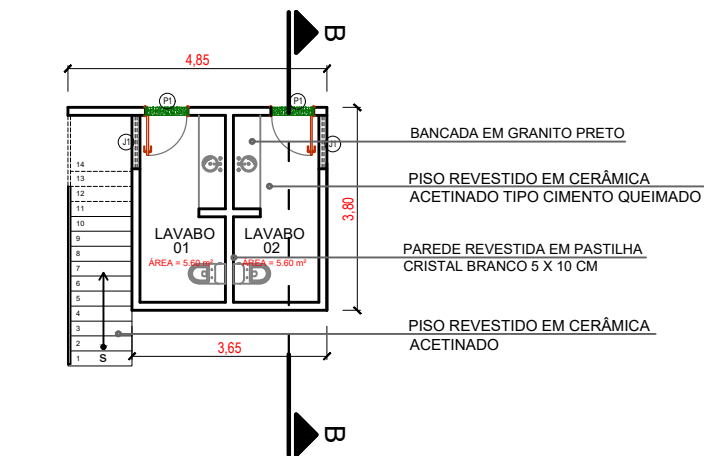


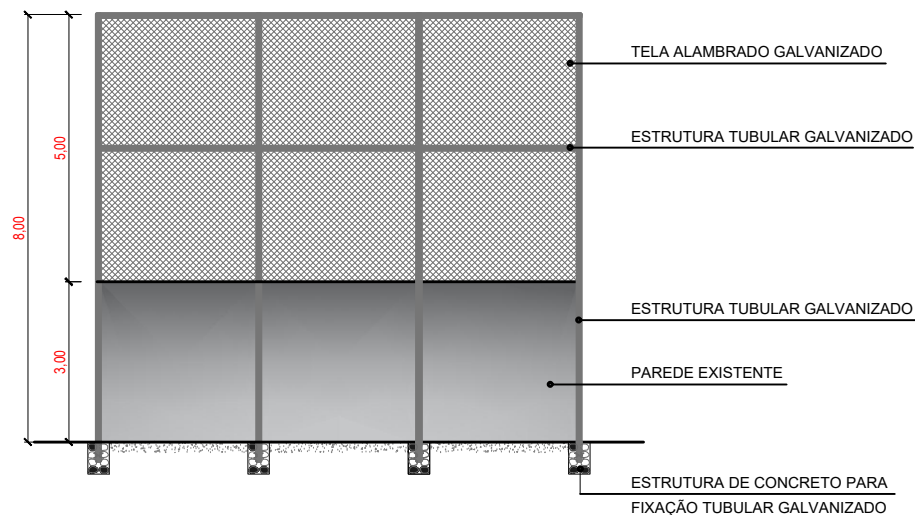


ELEVAÇÃO FRONTAL
ESCALA 1/100

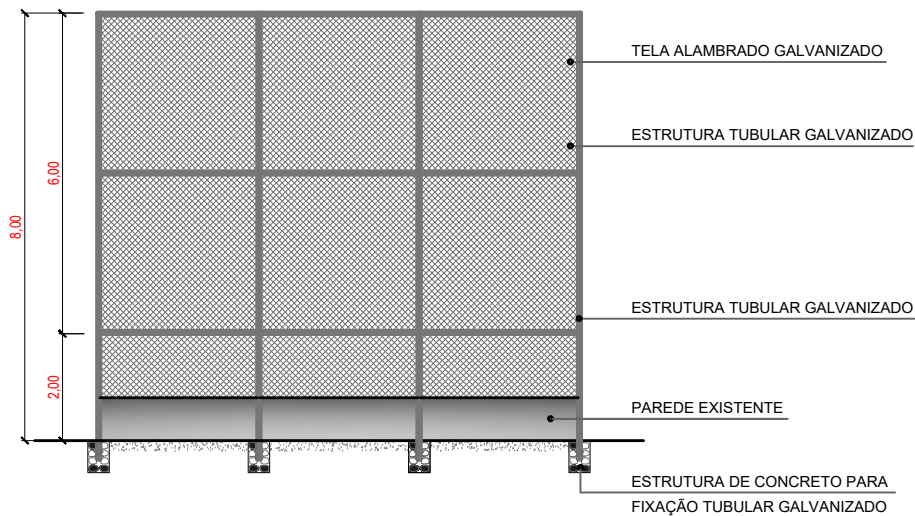


ELEVAÇÃO FRONTAL
ESCALA 1/100

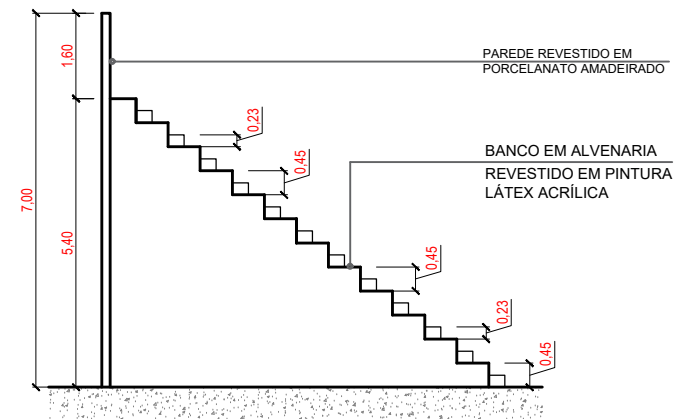


CORTE CC
ESCALA 1/100

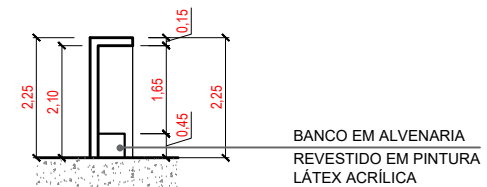


CORTE DD
ESCALA 1/100

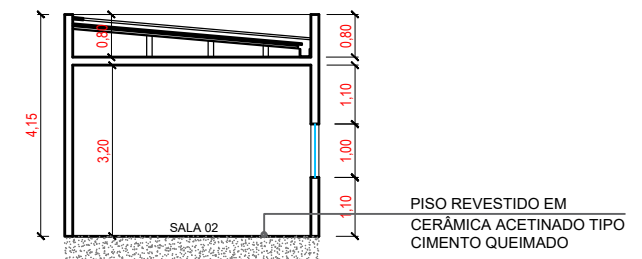


CORTE GG
ESCALA 1/100

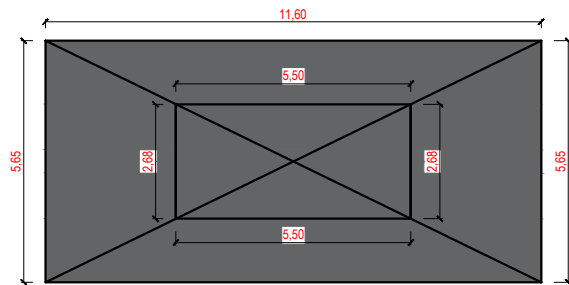


PLANTA DE COBERTA | QUIOSQUE
ESCALA 1/125

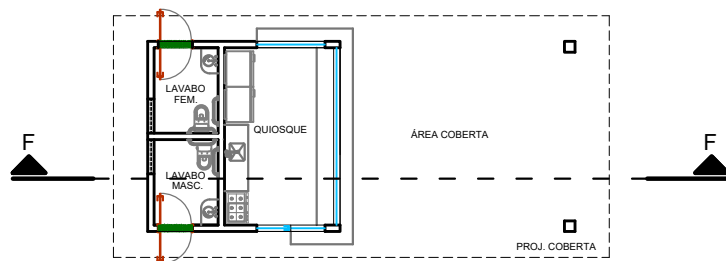


PLANTA BAIXA | LAYOUT | QUIOSQUE
ESCALA 1/125

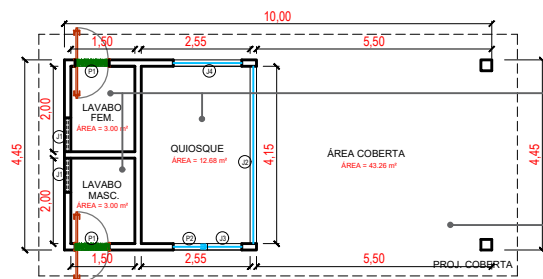


PLANTA BAIXA | QUIOSQUE
ESCALA 1/125

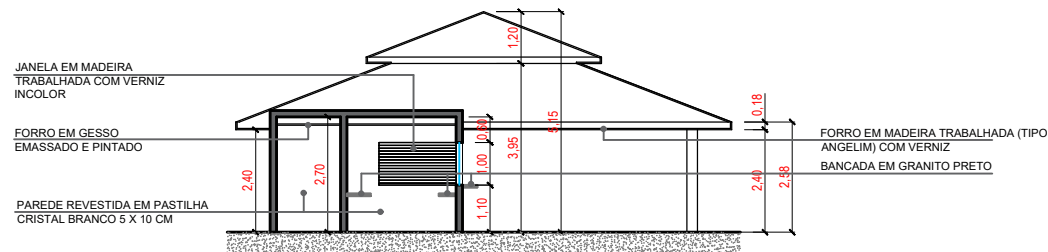


CORTE FF
ESCALA 1/125

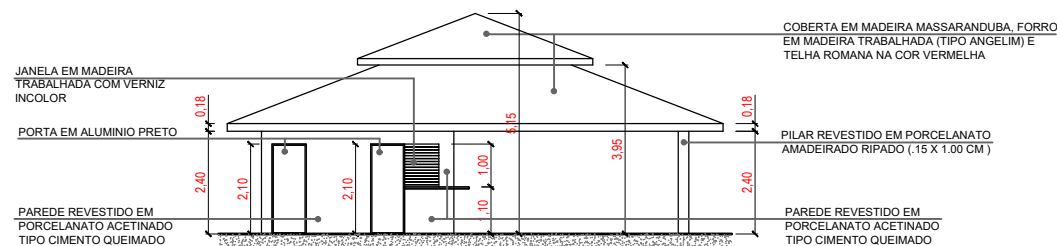


ELEVAÇÃO LATERAL
ESCALA 1/125

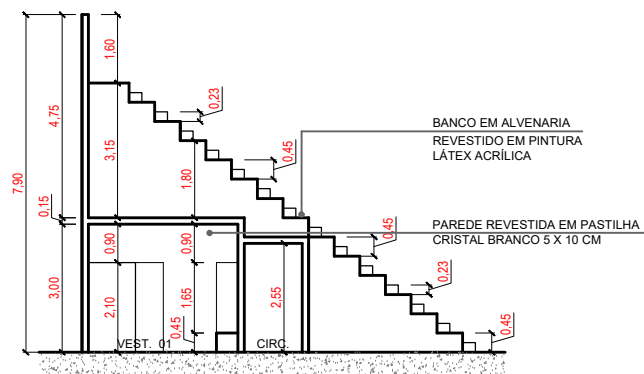


CORTE AA
ESCALA 1/125

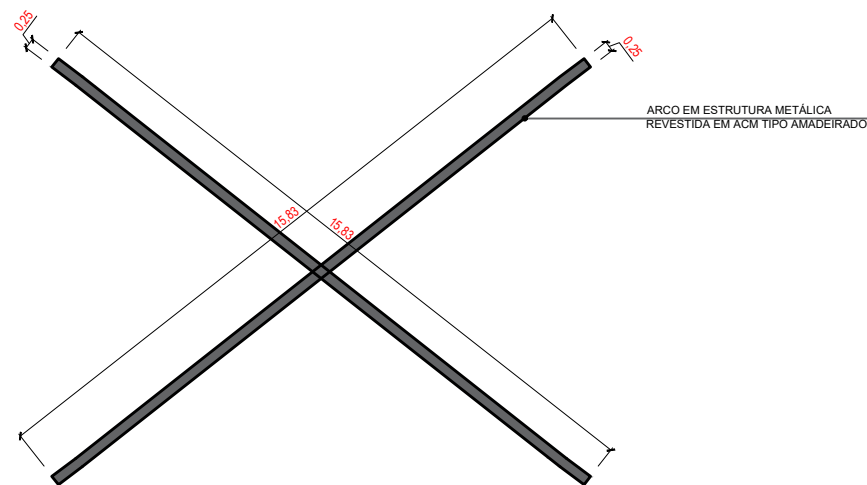

ELEVAÇÃO SUPERIOR
ESCALA 1/125

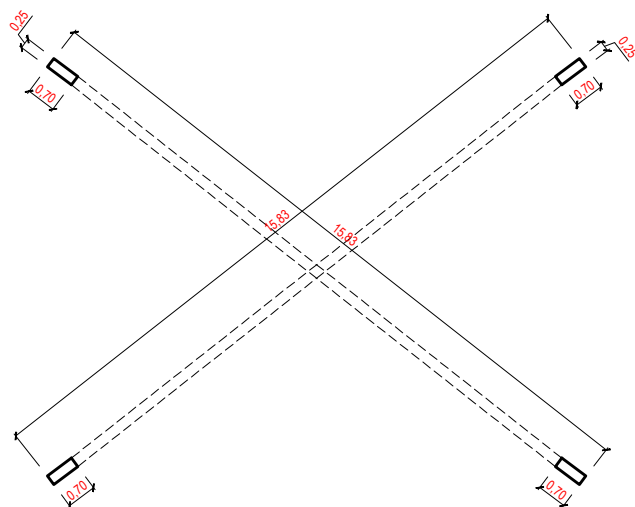

PLANTA BAIXA | ARCO
ESCALA 1/125

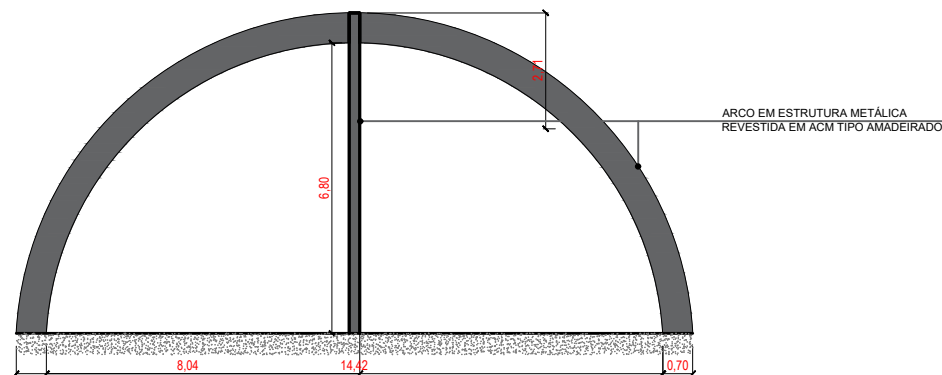

ELEVAÇÃO FRONTAL
ESCALA 1/125

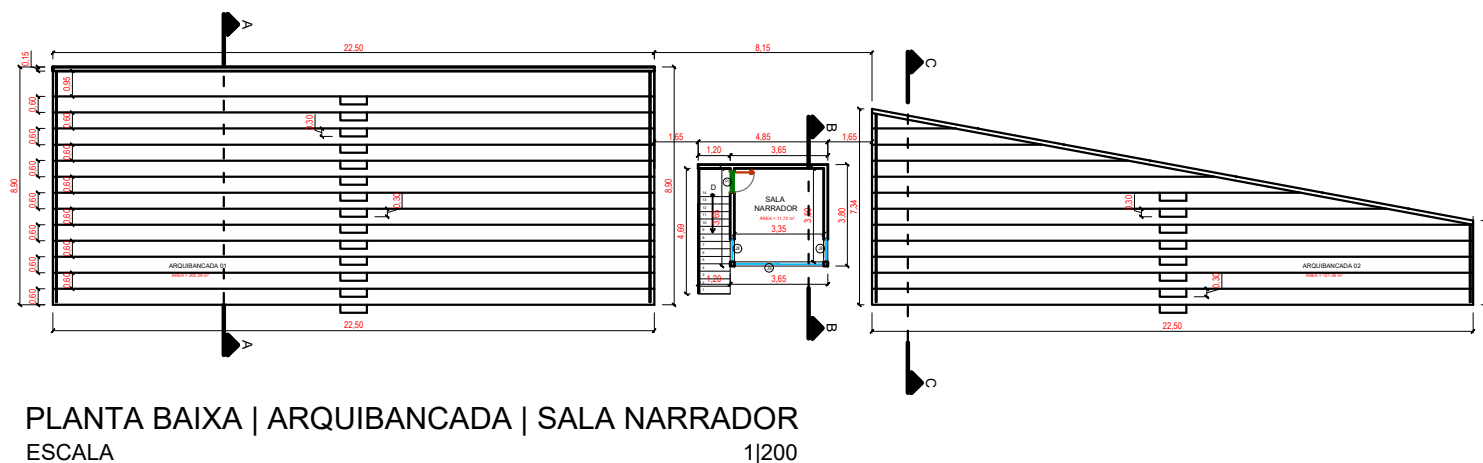
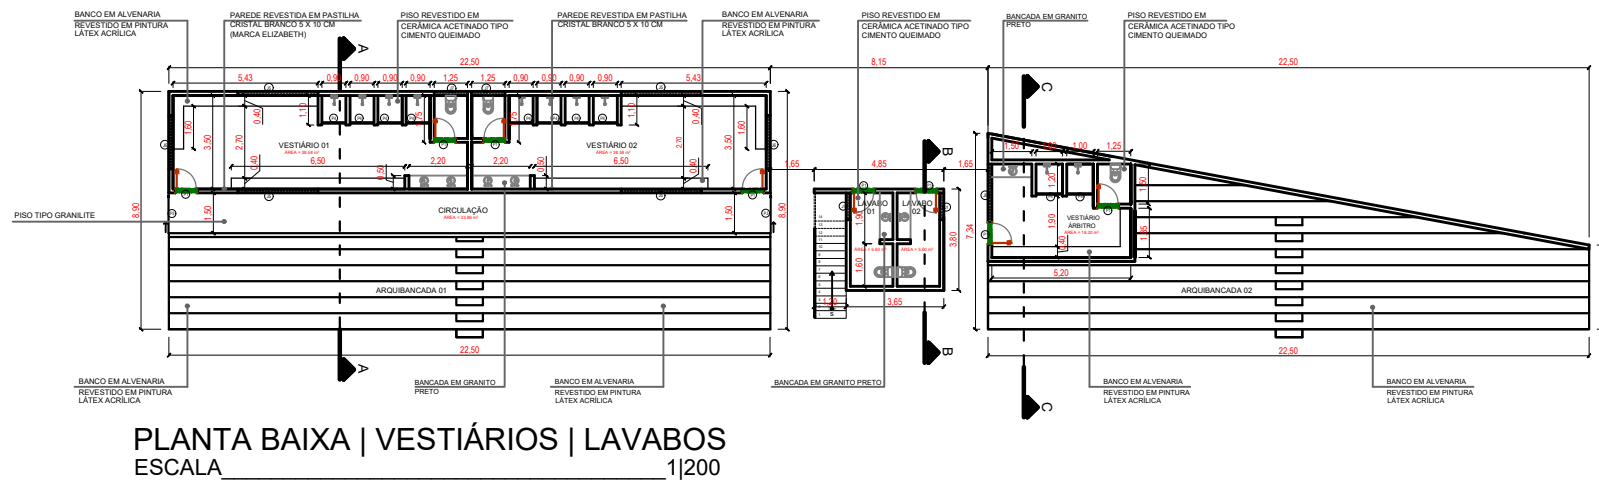




IMAGEM | 3D
ESCALA__1|200



IMAGEM | 3D
ESCALA__1|200



IMAGEM | 3D
ESCALA ___ 1/200



IMAGEM | 3D
 ESCALA__1|200



IMAGEM | 3D
ESCALA__1|200



IMAGEM | 3D
ESCALA__1|200





IMAGEM | 3D
ESCALA__1|200




IMAGEM | 3D
ESCALA__1|200




IMAGEM | 3D
ESCALA__1|200

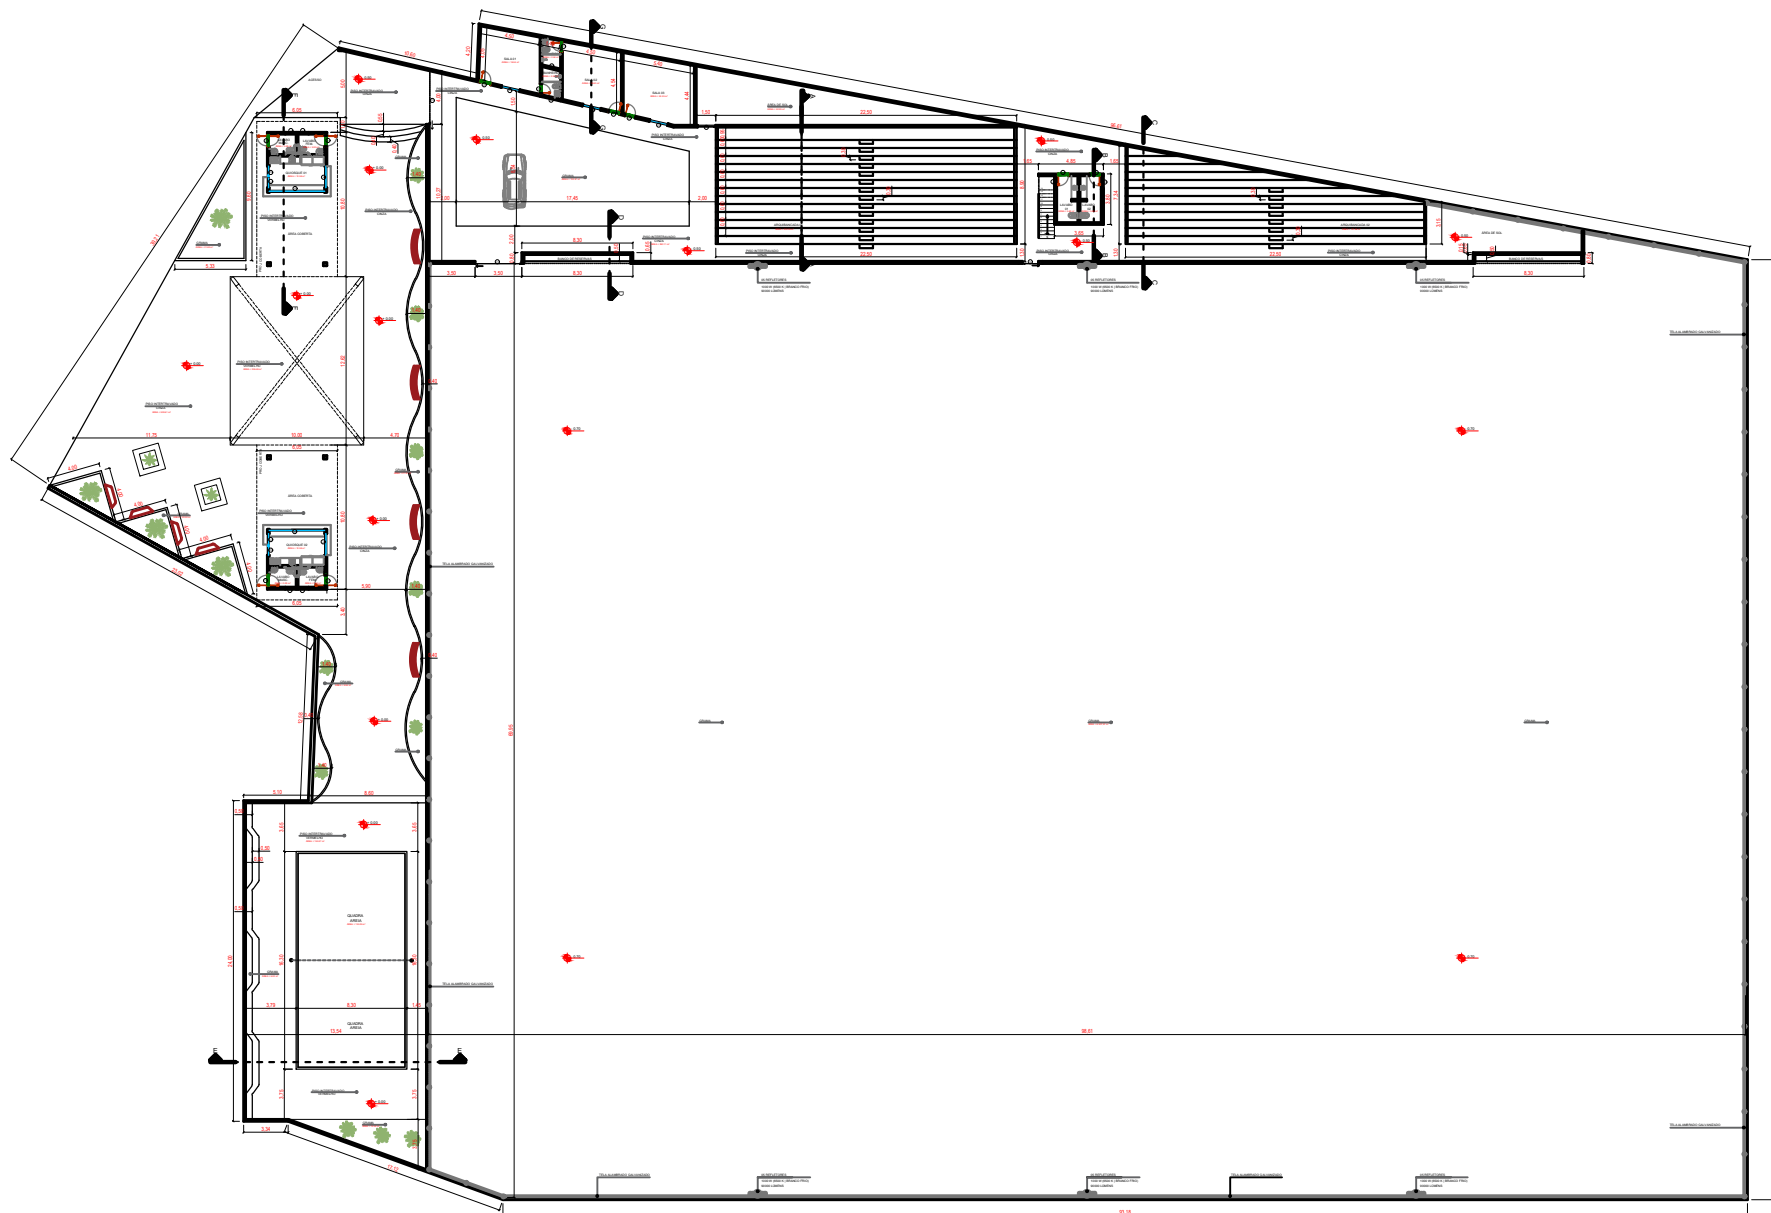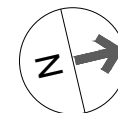


PLANTA BAIXA | LAYOUT
ESCALA 1/400

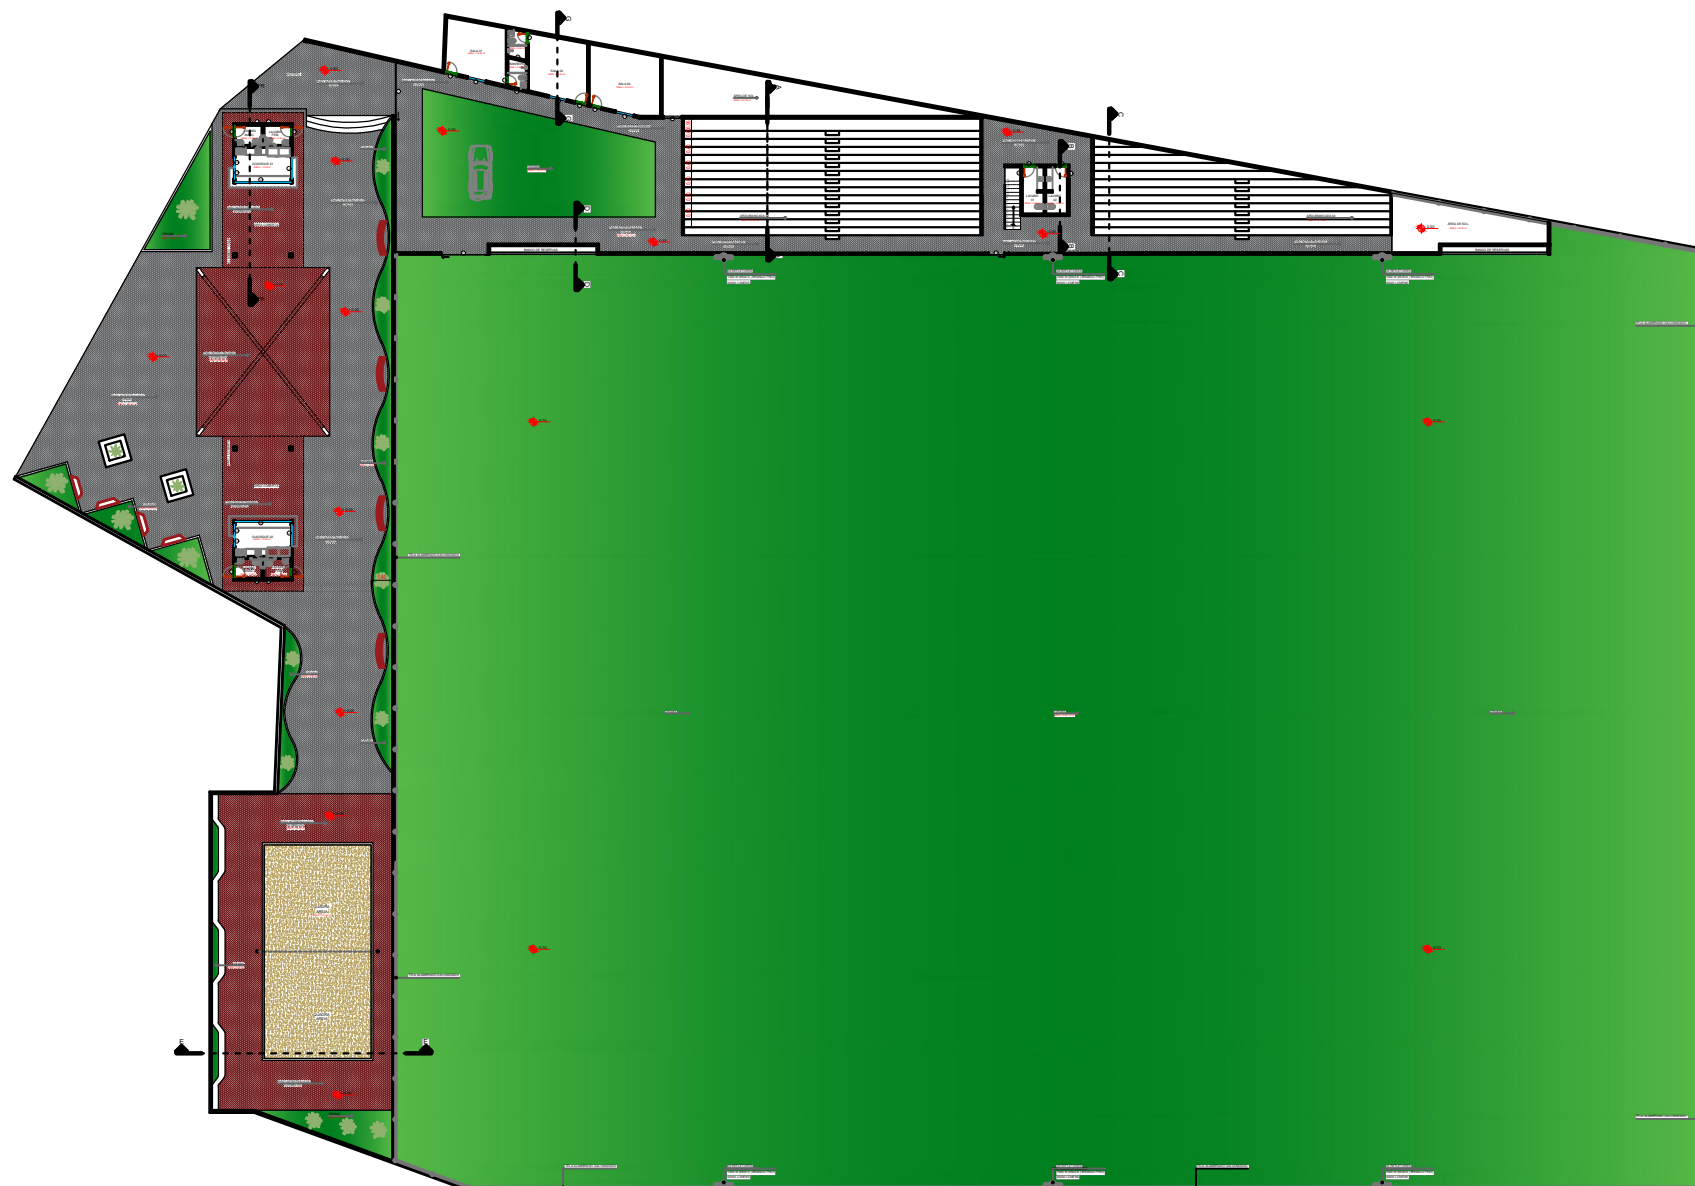


PLANTA BAIXA | IMPLANTAÇÃO
ESCALA _____ 1/400

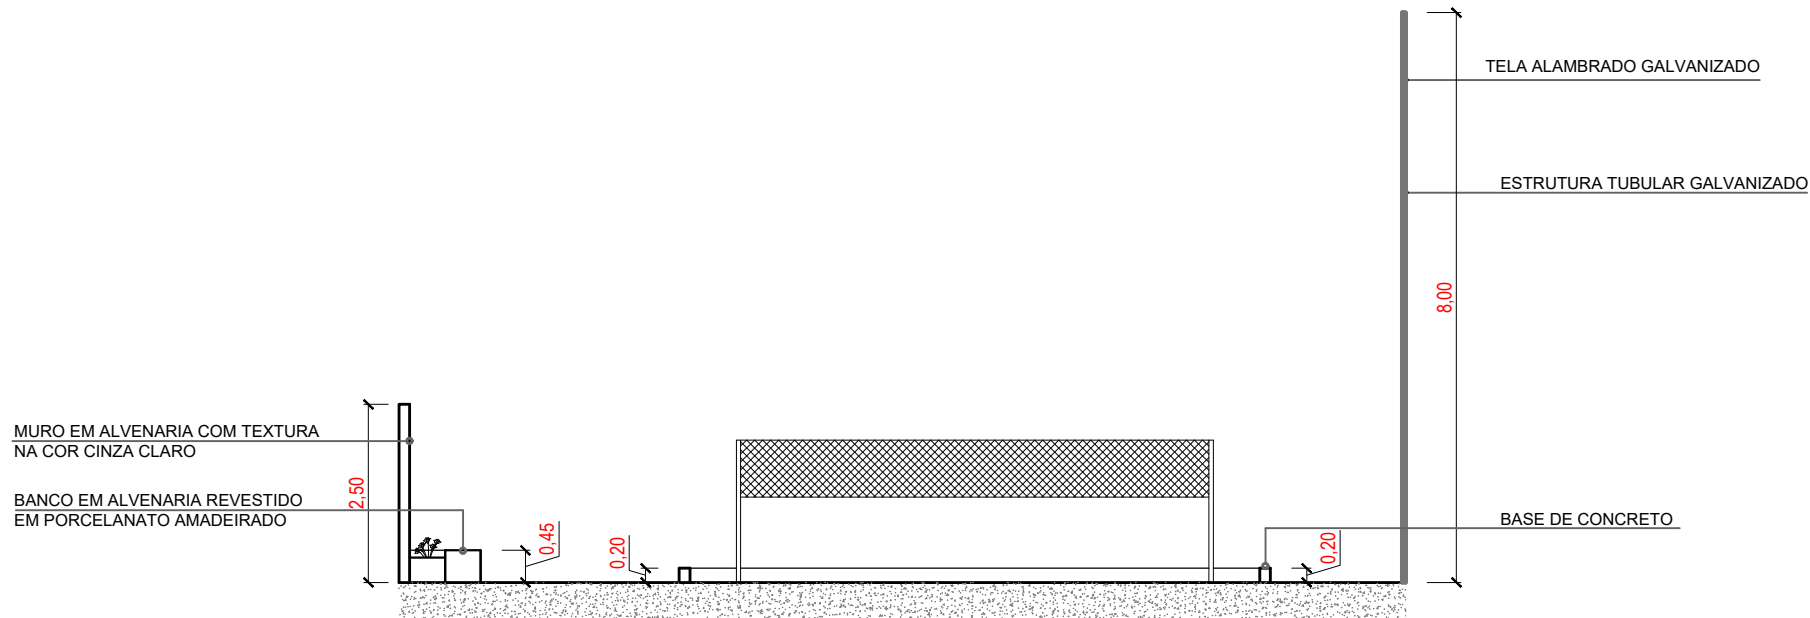


CORTE EE
ESCALA_1/75

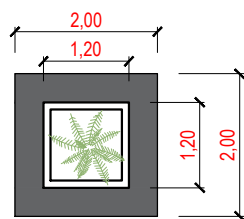

ELEVAÇÃO SUPERIOR | BANCO 03
ESCALA_1/75

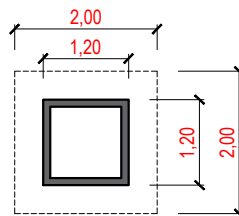

PLANTA BAIXA | BANCO 03
ESCALA_1/75

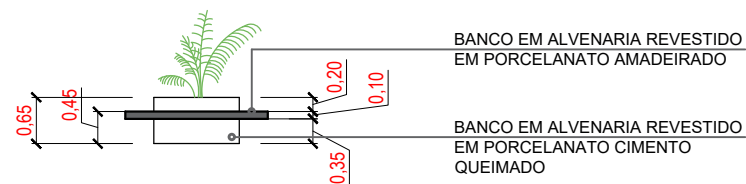

ELEVAÇÃO LATERAL | BANCO 03
ESCALA_1/75