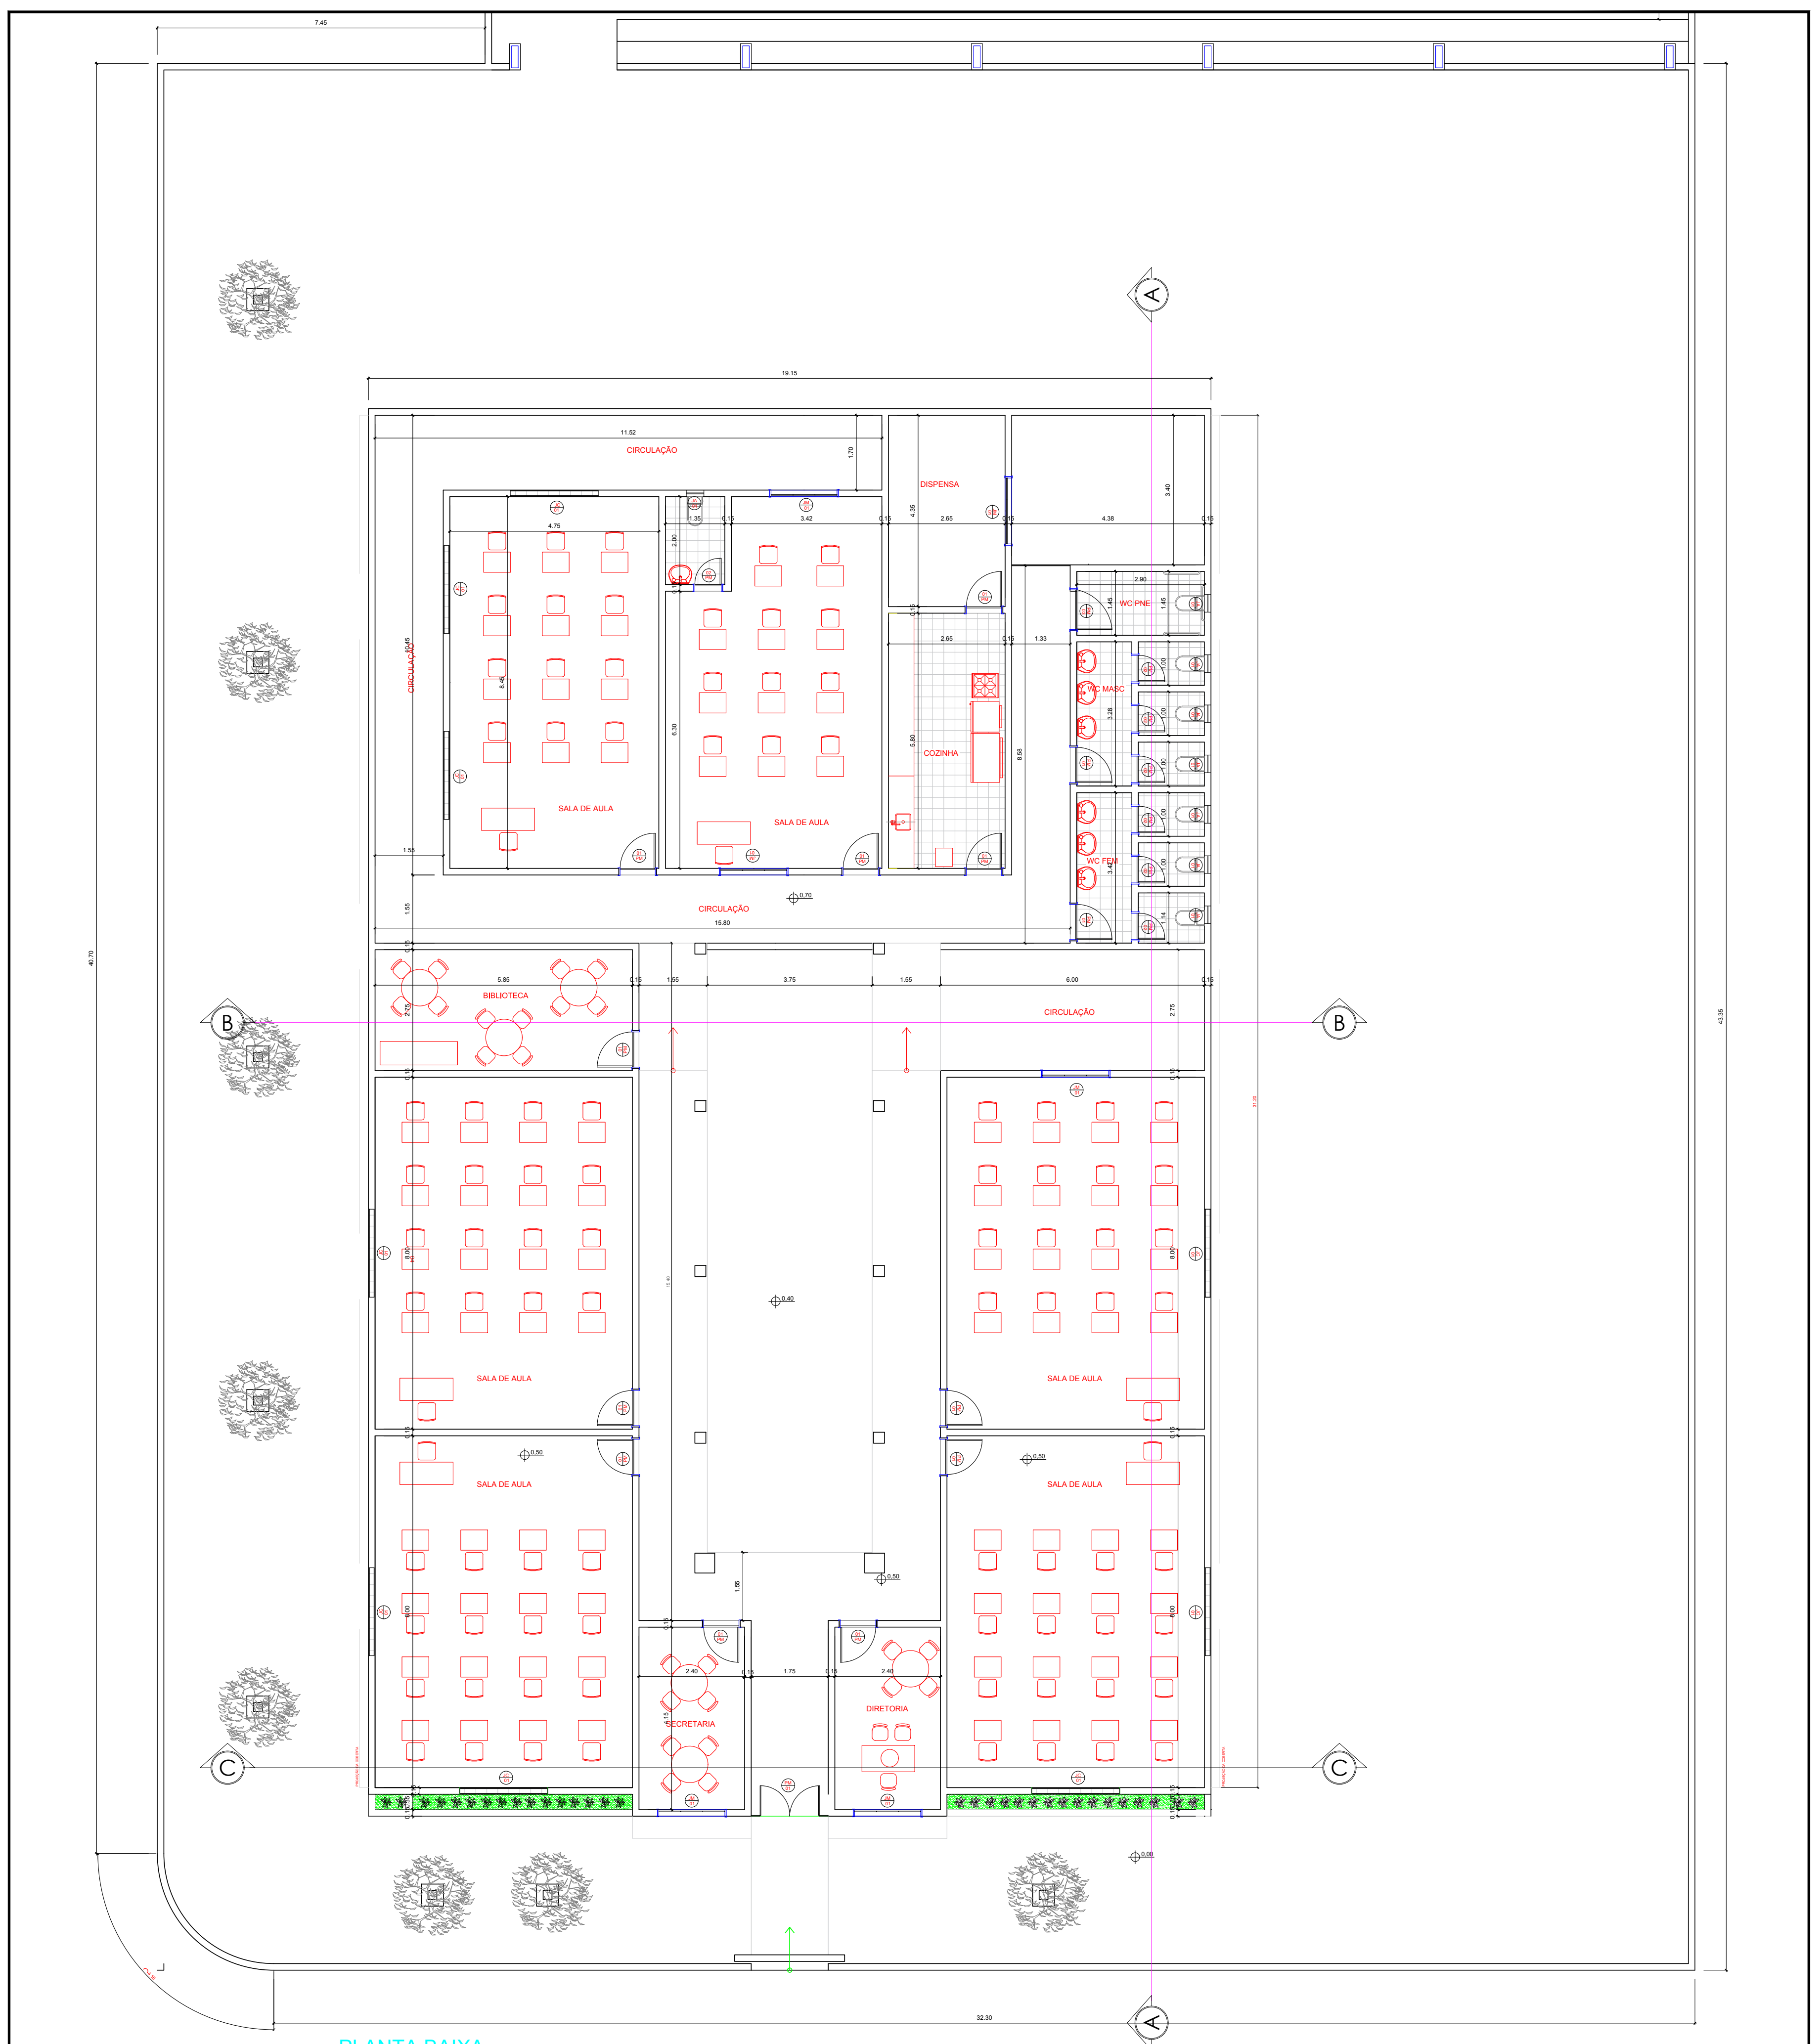
7.45
19.15
11.52
CIRCULAÇÃO
DISPENSA
COZINHA
WC PNE
WC MASC
WC FEM
SALA DE AULA
SALA DE AULA
CIRCULAÇÃO
15.80
BIBLIOTECA
CIRCULAÇÃO
SALA DE AULA
SALA DE AULA
SALA DE AULA
SALA DE AULA
SECRETARIA
DIRETORIA
A
B
C
40.70
43.35
32.30

PLANTA BAIXA

ESCALA 1:50

EPE

PROJETO: REFORMA DA ESCOLA FLÓRIDO NITÃO DINIZ
LOCAL: ZUNA URBANA, MUNCÍPIO DE COREMAS - PB
PROPRIETÁRIO: PREFEITURA MUNICIPAL DE COREMAS - PB
RESPONSÁVEL TÉCNICO: Kleber Sá de Oliveira
CREA: 160268278-0
ANOTAÇÕES:
DATA: DEZ - 2019
FOLHA 01/03
ESCALA: 1:50
DESENHOS: Planta Baixa
ARQUIVO: ESCOLA_DNOCS_COREMAS.DWG
DESENHO: Diego Romualdo de Medeiros

QUADRO RESUMO DE ESQUADRIAS

ESQUADRIA	DIMENSÃO (LxH)cm	QUANT.	LOCAL	TIPO
PM 01	86,0 x 210,0	13	WC F/M, SALAS	PORTA DE MADEIRA
PM 02	60,0 x 210,0	7	WCS	PORTA DE MADEIRA
PM 03	90,0 x 210,0	1	WC PNE	PORTA DE MADEIRA
JA 01	40,0 x 40,0	8	WC FEM,/MASC.	JANELA DE ALUMÍNIO
JM 01	110,0 x 40,0	6	SALAS/COZ./DISP,	JANELA DE MADEIRA
JC 01	150,0 x 100	1	SALAS	COBOGÓ

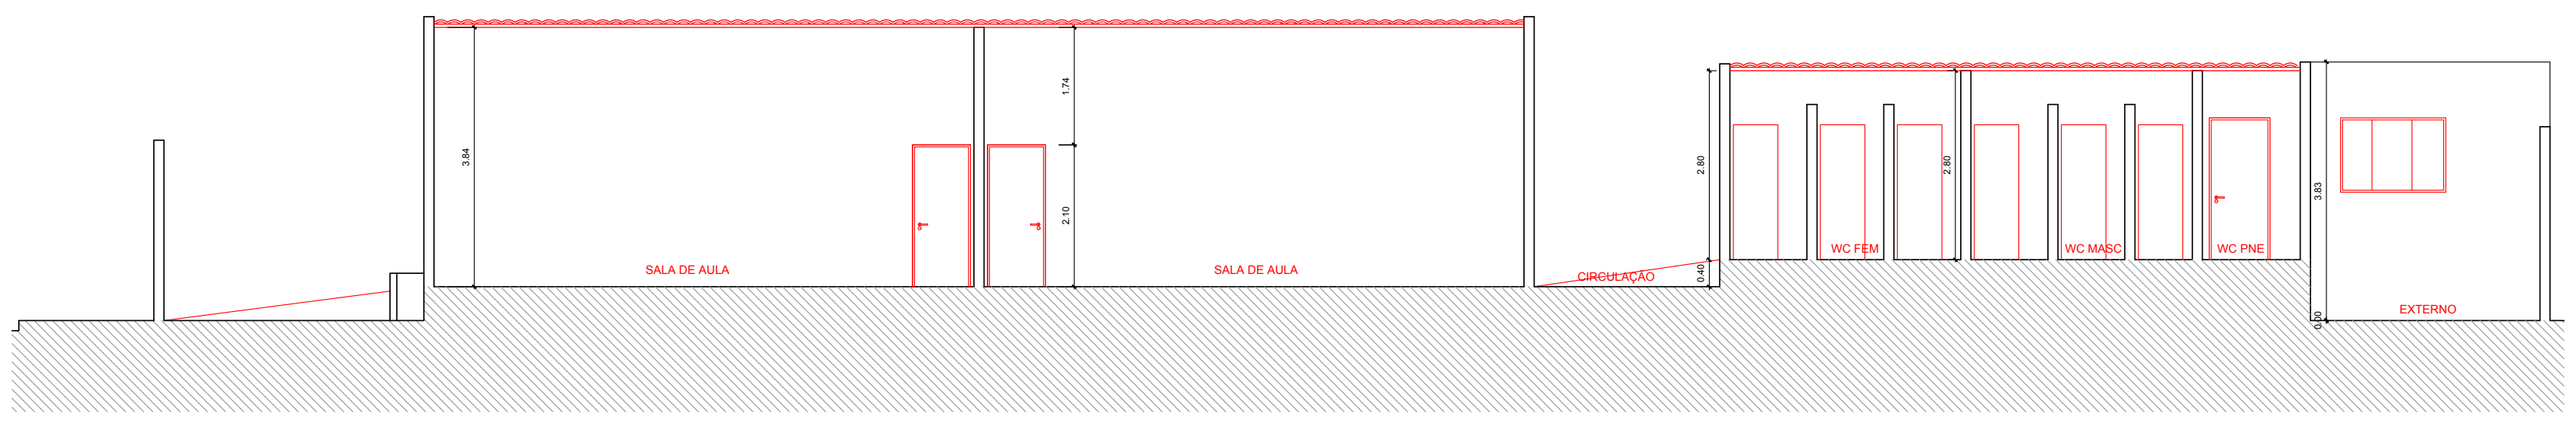
3.84
1.74
2.10
SALA DE AULA
SALA DE AULA
CIRCULAÇÃO
0.40
2.80
2.80
WC FEM
WC MASC
WC PNE
3.83
EXTERNO

CORTE AA

ESCALA 1/45

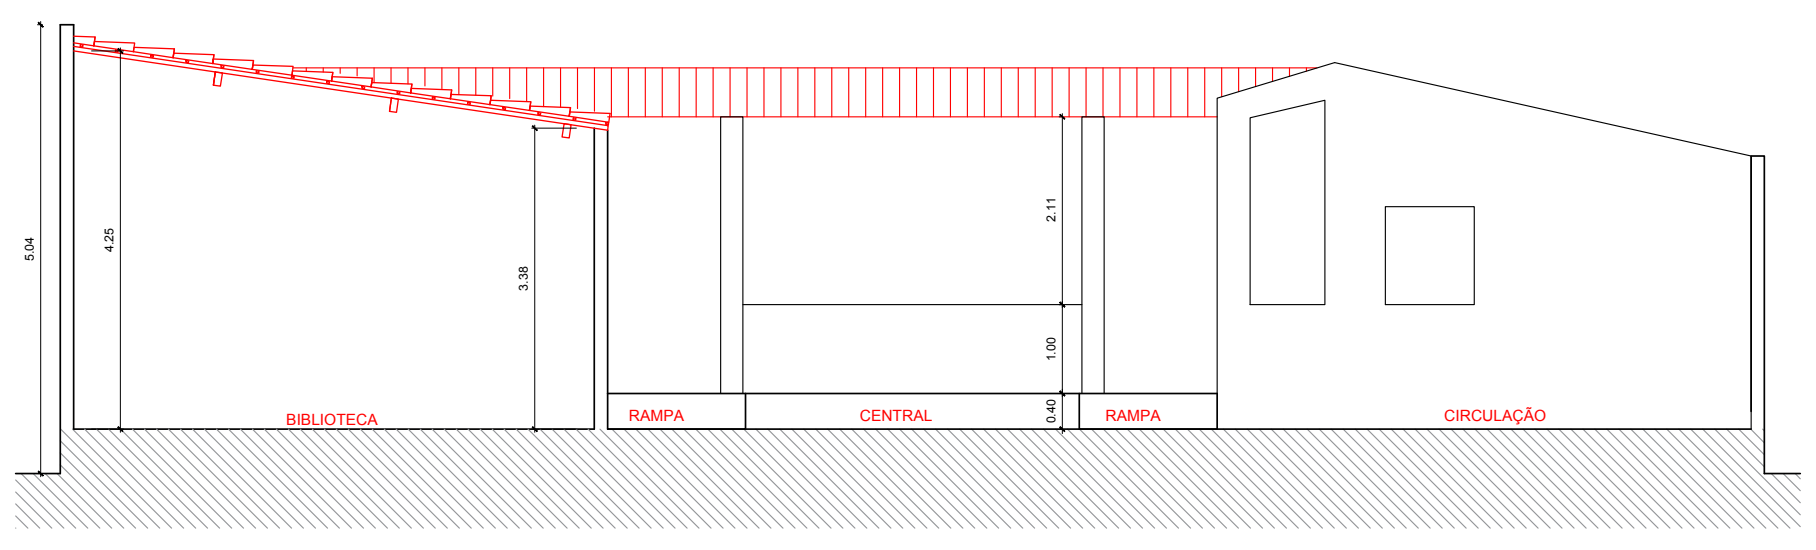
5.04
4.25
3.38
2.11
1.00
0.40
BIBLIOTECA
RAMPA
CENTRAL
RAMPA
CIRCULAÇÃO

CORTE BB

ESCALA 1/45

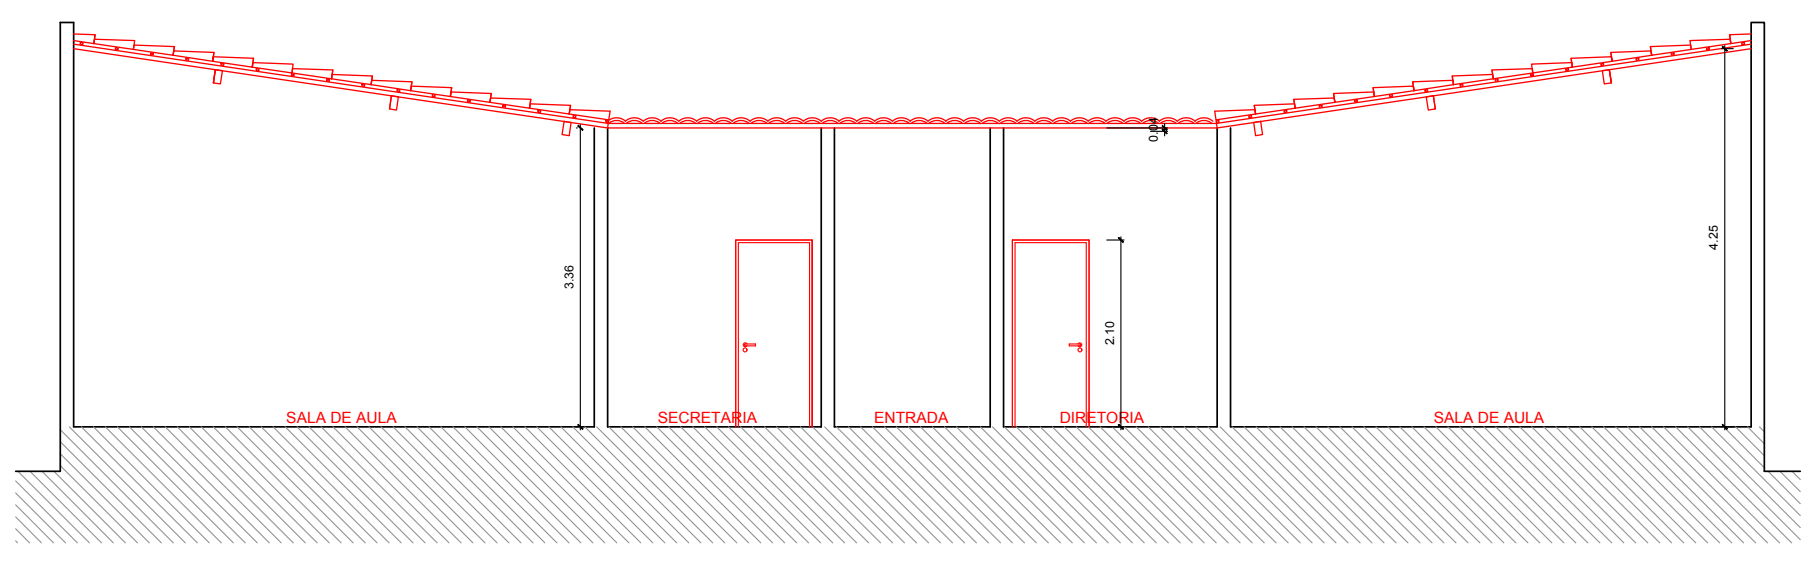
3.36
2.10
4.25
SALA DE AULA
SECRETARIA
ENTRADA
DIRETORIA
SALA DE AULA

CORTE CC

ESCALA 1/45

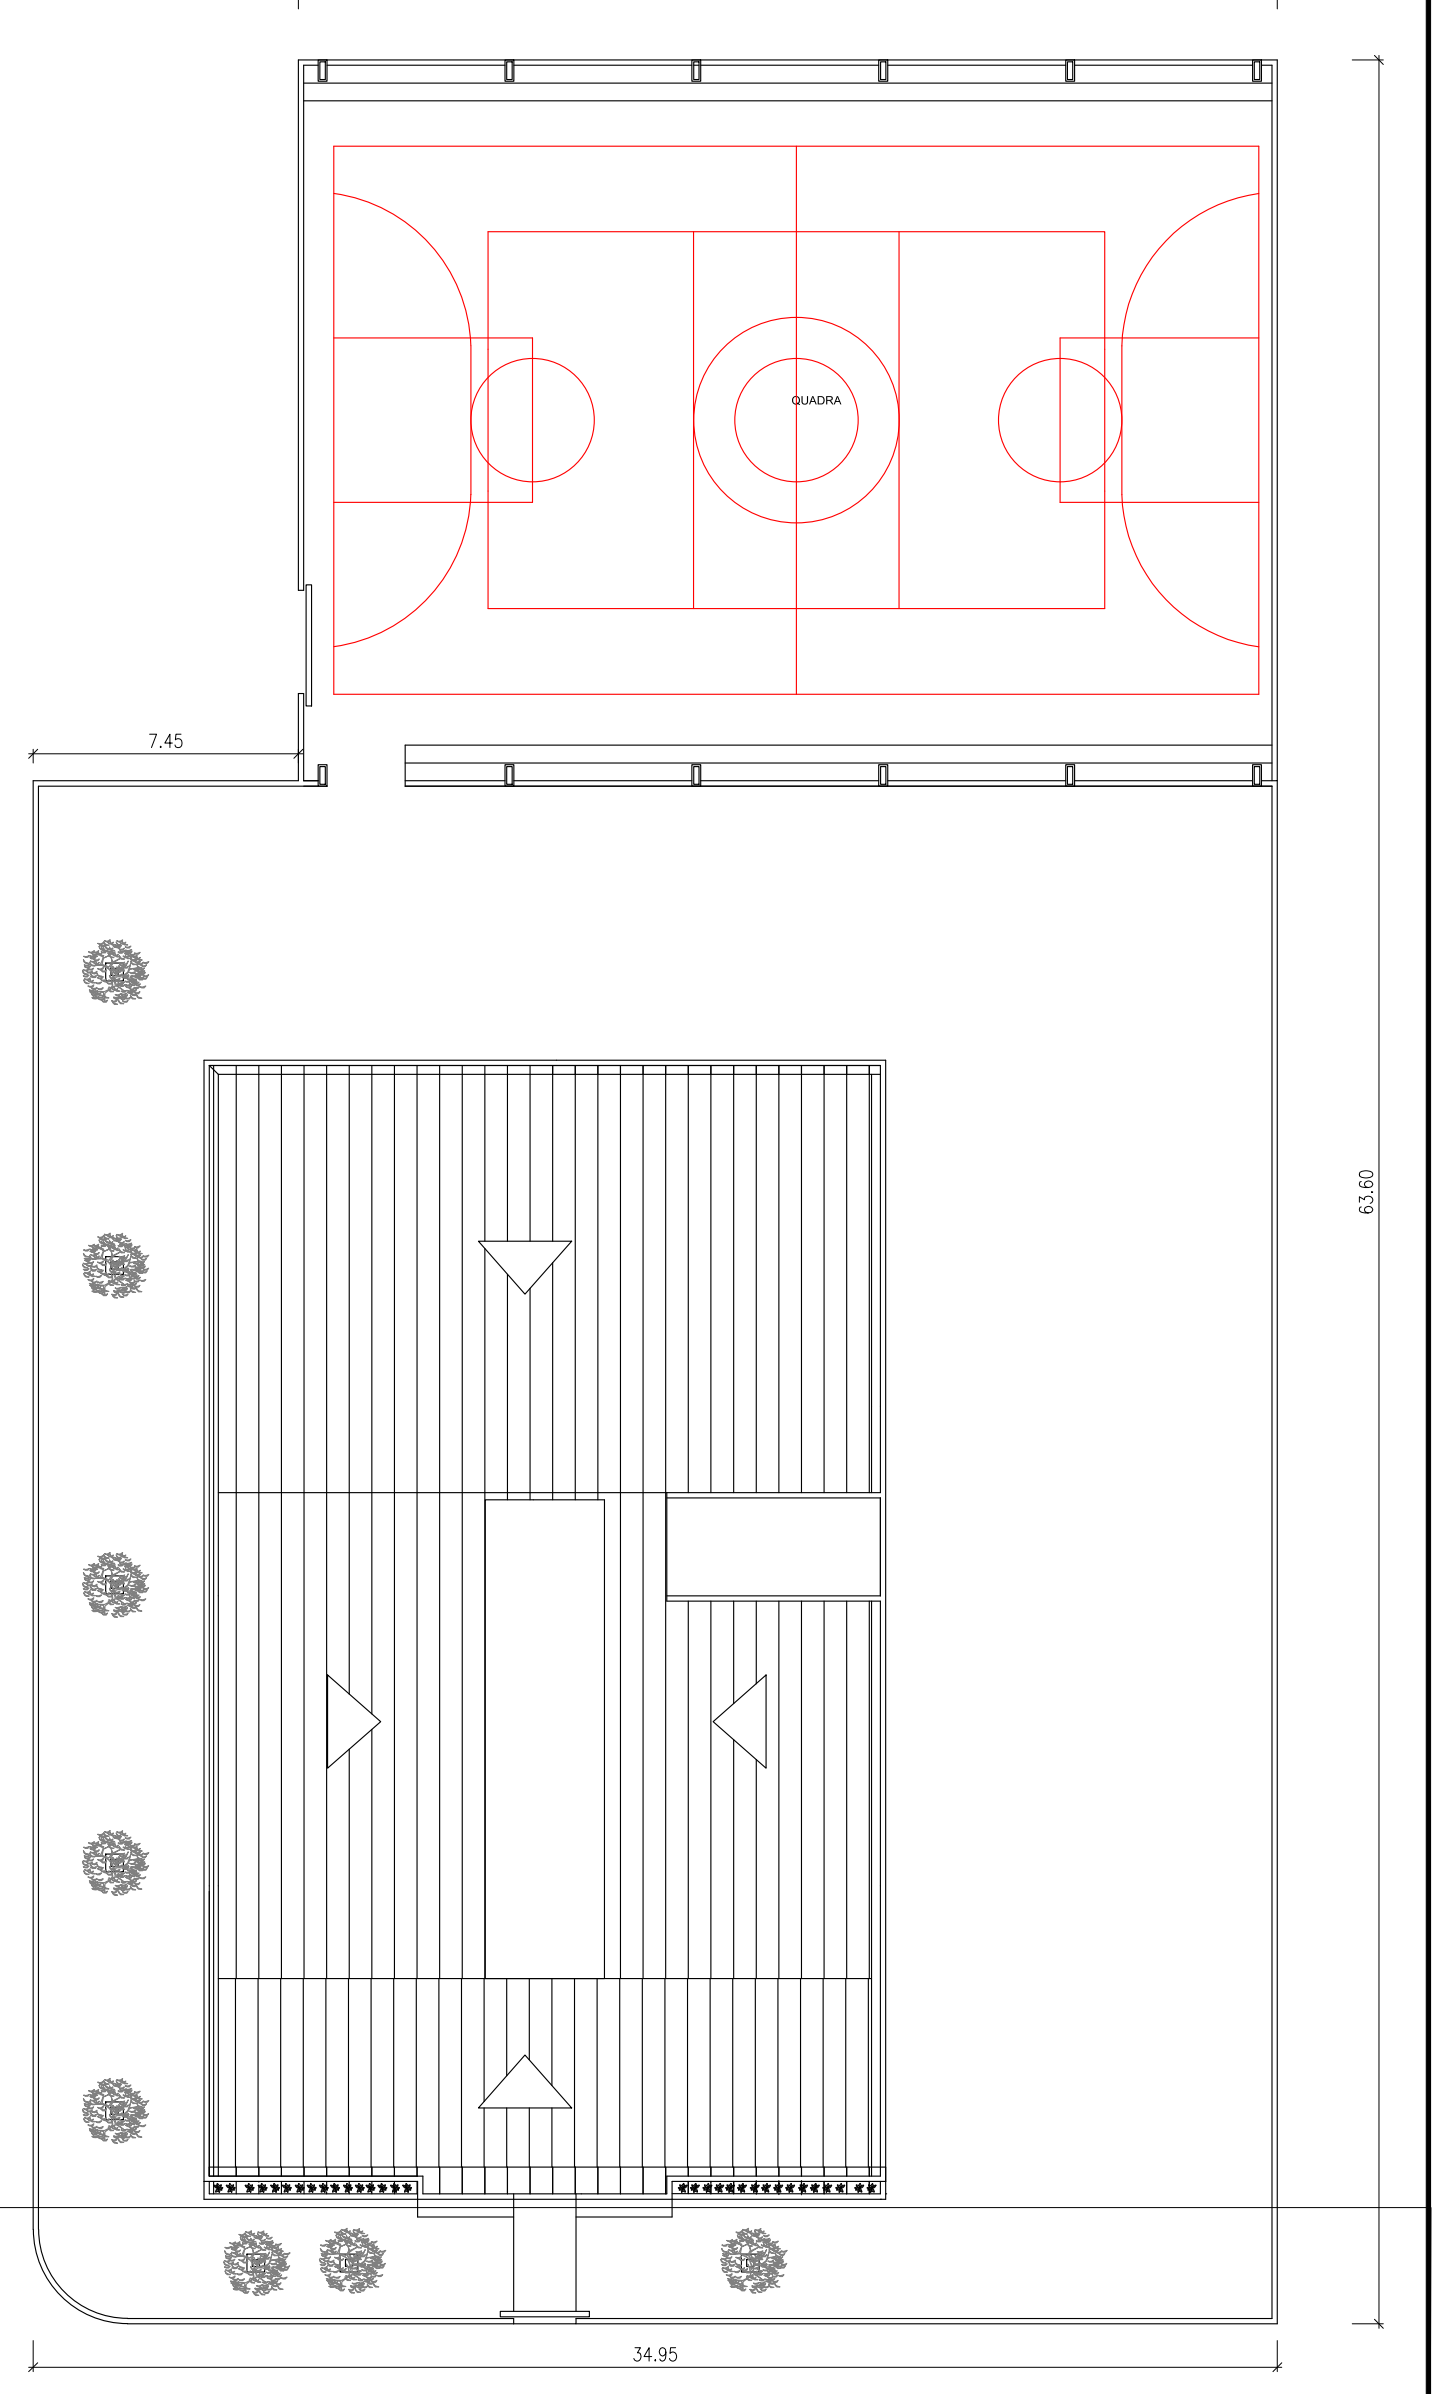
QUADRA
7.45
63.60
34.95

PLANTA DE COBERTA E LOCAÇÃO

ESCALA 1:125

EPE

PROJETO: REFORMA DA ESCOLA FLÓRIDO NITÃO DINIZ
LOCAL: ZUNA URBANA, MUNCÍPIO DE COREMAS - PB
PROPRIETÁRIO: PREFEITURA MUNICIPAL DE COREMAS - PB
RESPONSÁVEL TÉCNICO: Kleber Sá de Oliveira
CREA: 160268278-0
ANOTAÇÕES:
DATA: DEZ - 2019
FOLHA 02/03
ESCALA: 1:50
1:125
DESENHOS: Cortes
Locação e Coberta
ARQUIVO: ESCOLA_DNOCS_COREMAS.DWG
DESENHO: Diego Romualdo de Medeiros