



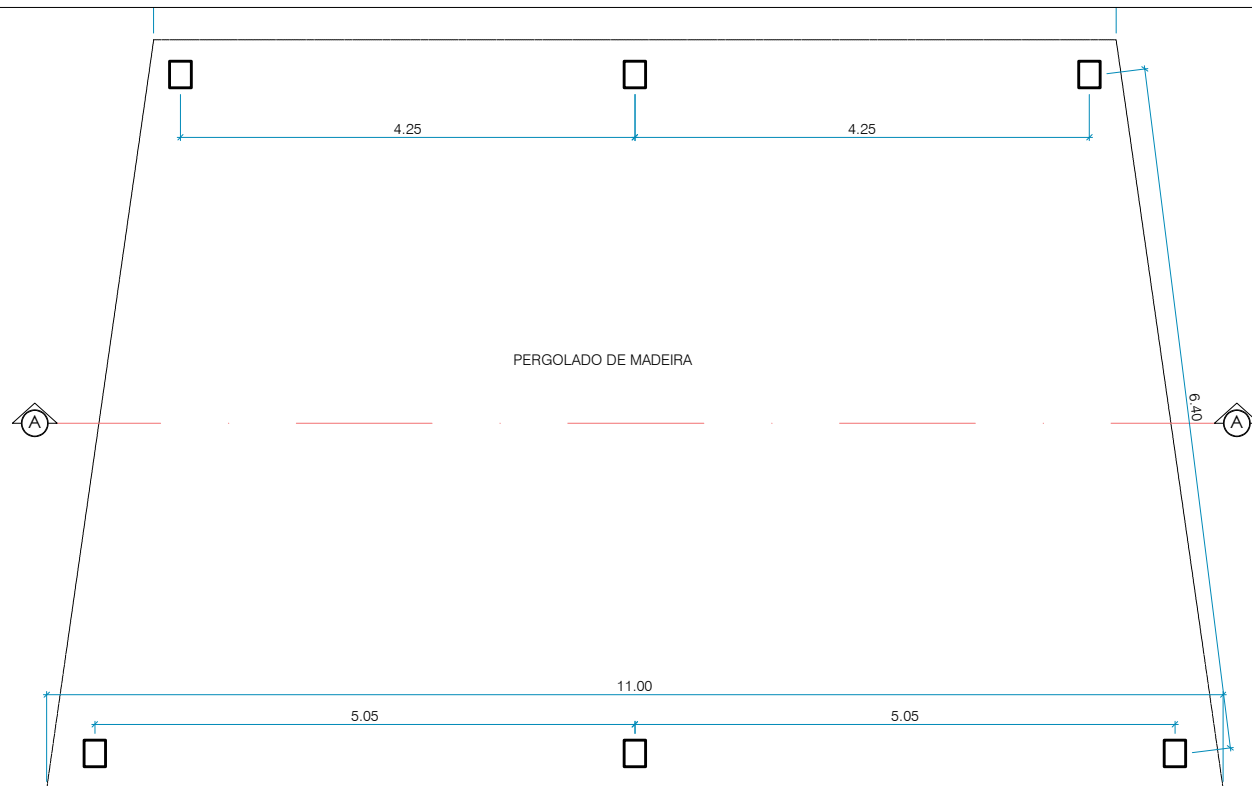

DETALHE 04
COBERTA PLAYGROUND ESCALA: 1/50

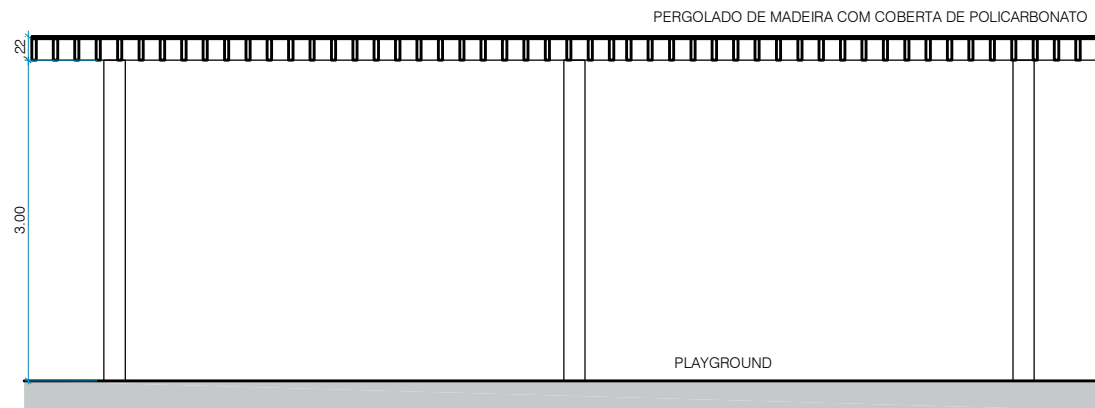

CORTE AA
COBERTA PLAYGROUND ESCALA: 1/50

		Projeto:	Arquiteta:		
		Projeto de Urbanismo - Praça Nova Coremas	Kirya Cristinne		
		Proprietário:	CAU n° A165582-S		
Prefeitura Municipal de Coremas PB		Escala:	indicada	Prancha:	ÚNICA
		Data:	MAR/2025		

* Conferir medidas no local