


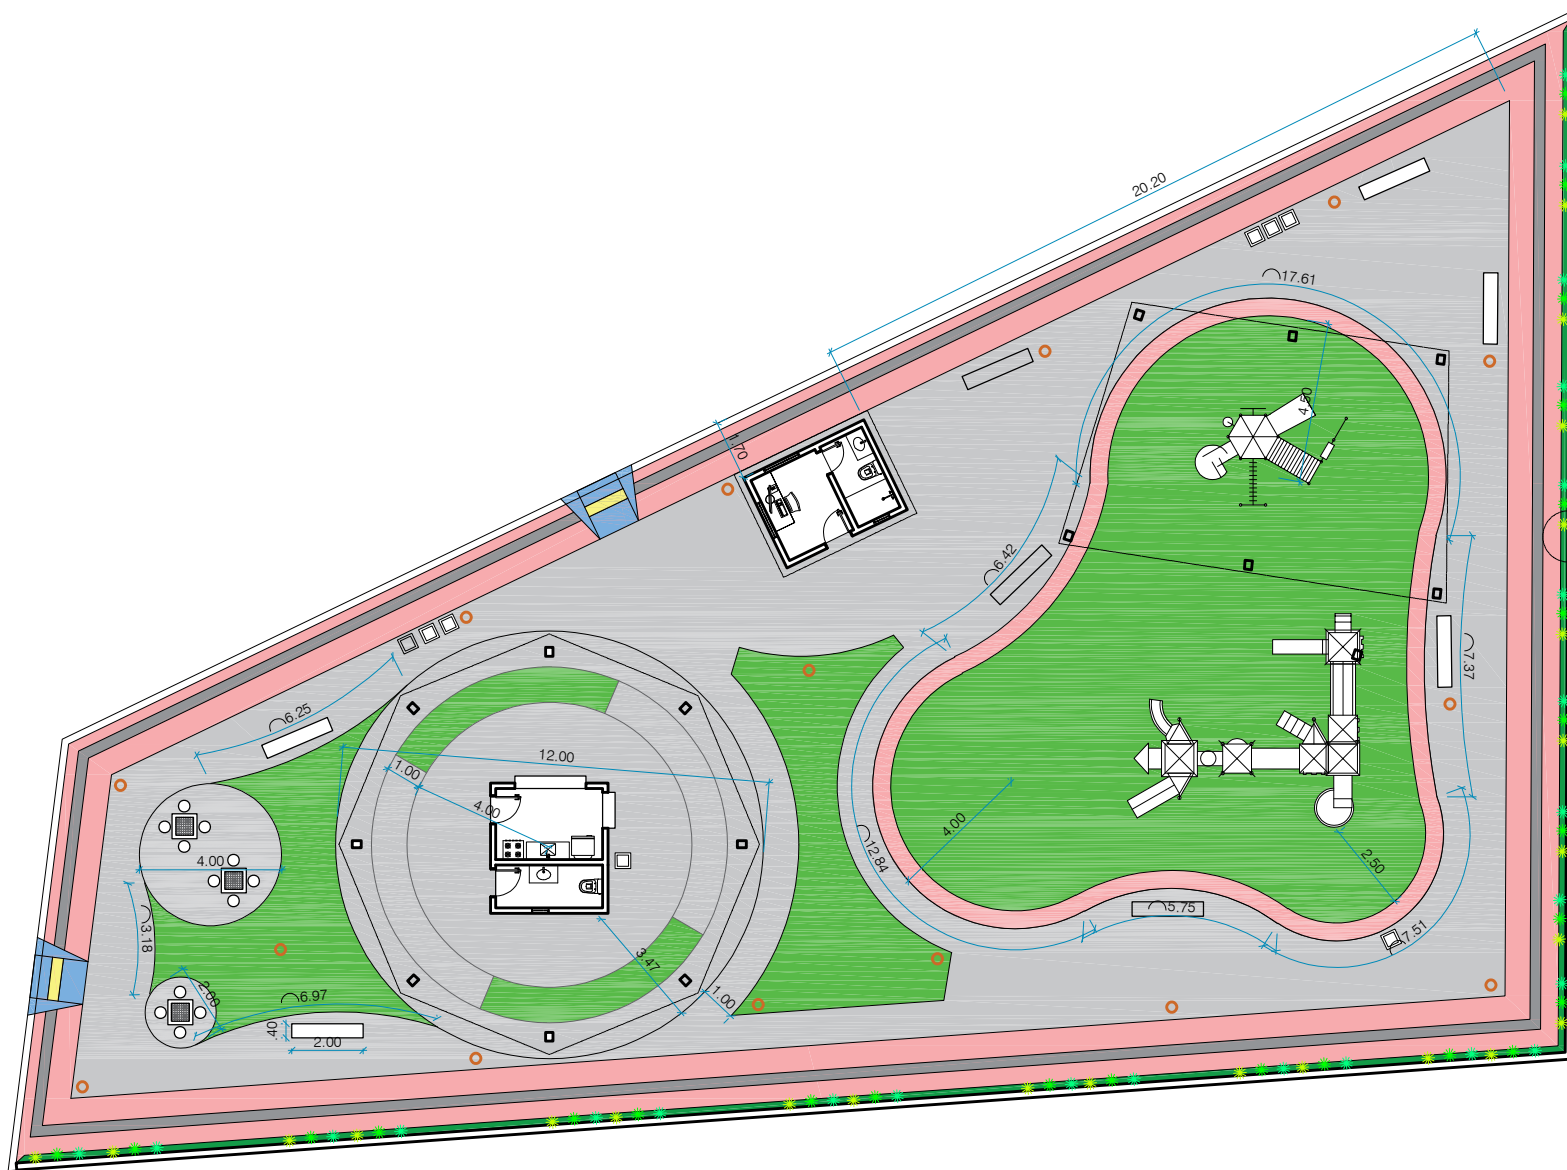

- LEGENDA
- Piso Intertravado Retangular 10x20cm Vermelho | Área: 192m²
 - Piso Intertravado Retangular 10x20cm Cinza | Área: 400m²
 - Piso revestido com Grama Esmeralda | Área: 250m²
 - Piso tatil direcional | Área: 38m²
 - Piso tatil de alerta | Área: 1m²
 - Poste pré moldado de entre 4 a 5m | 16uni
 - Banco de concreto com tampo de Mármore Travertino | 08uni
Cada banco possui Área banco: 1,8m² e Área marmore: 0,8m²
 - Piso de concreto com pintura para piso cor Azul | Área: 5,20m²

PLANTA BAIXA
PRAÇA NOVA COREMAS

ESCALA: 1/150



Projeto:	Arquiteta:		
	Kirya Cristinne CAU n° A165582-S		
Proprietário:	Escala:	Prancha:	Data:
Prefeitura Municipal de Coremas PB	indicada	ÚNICA	MAR/2025

* Conferir medidas no local