


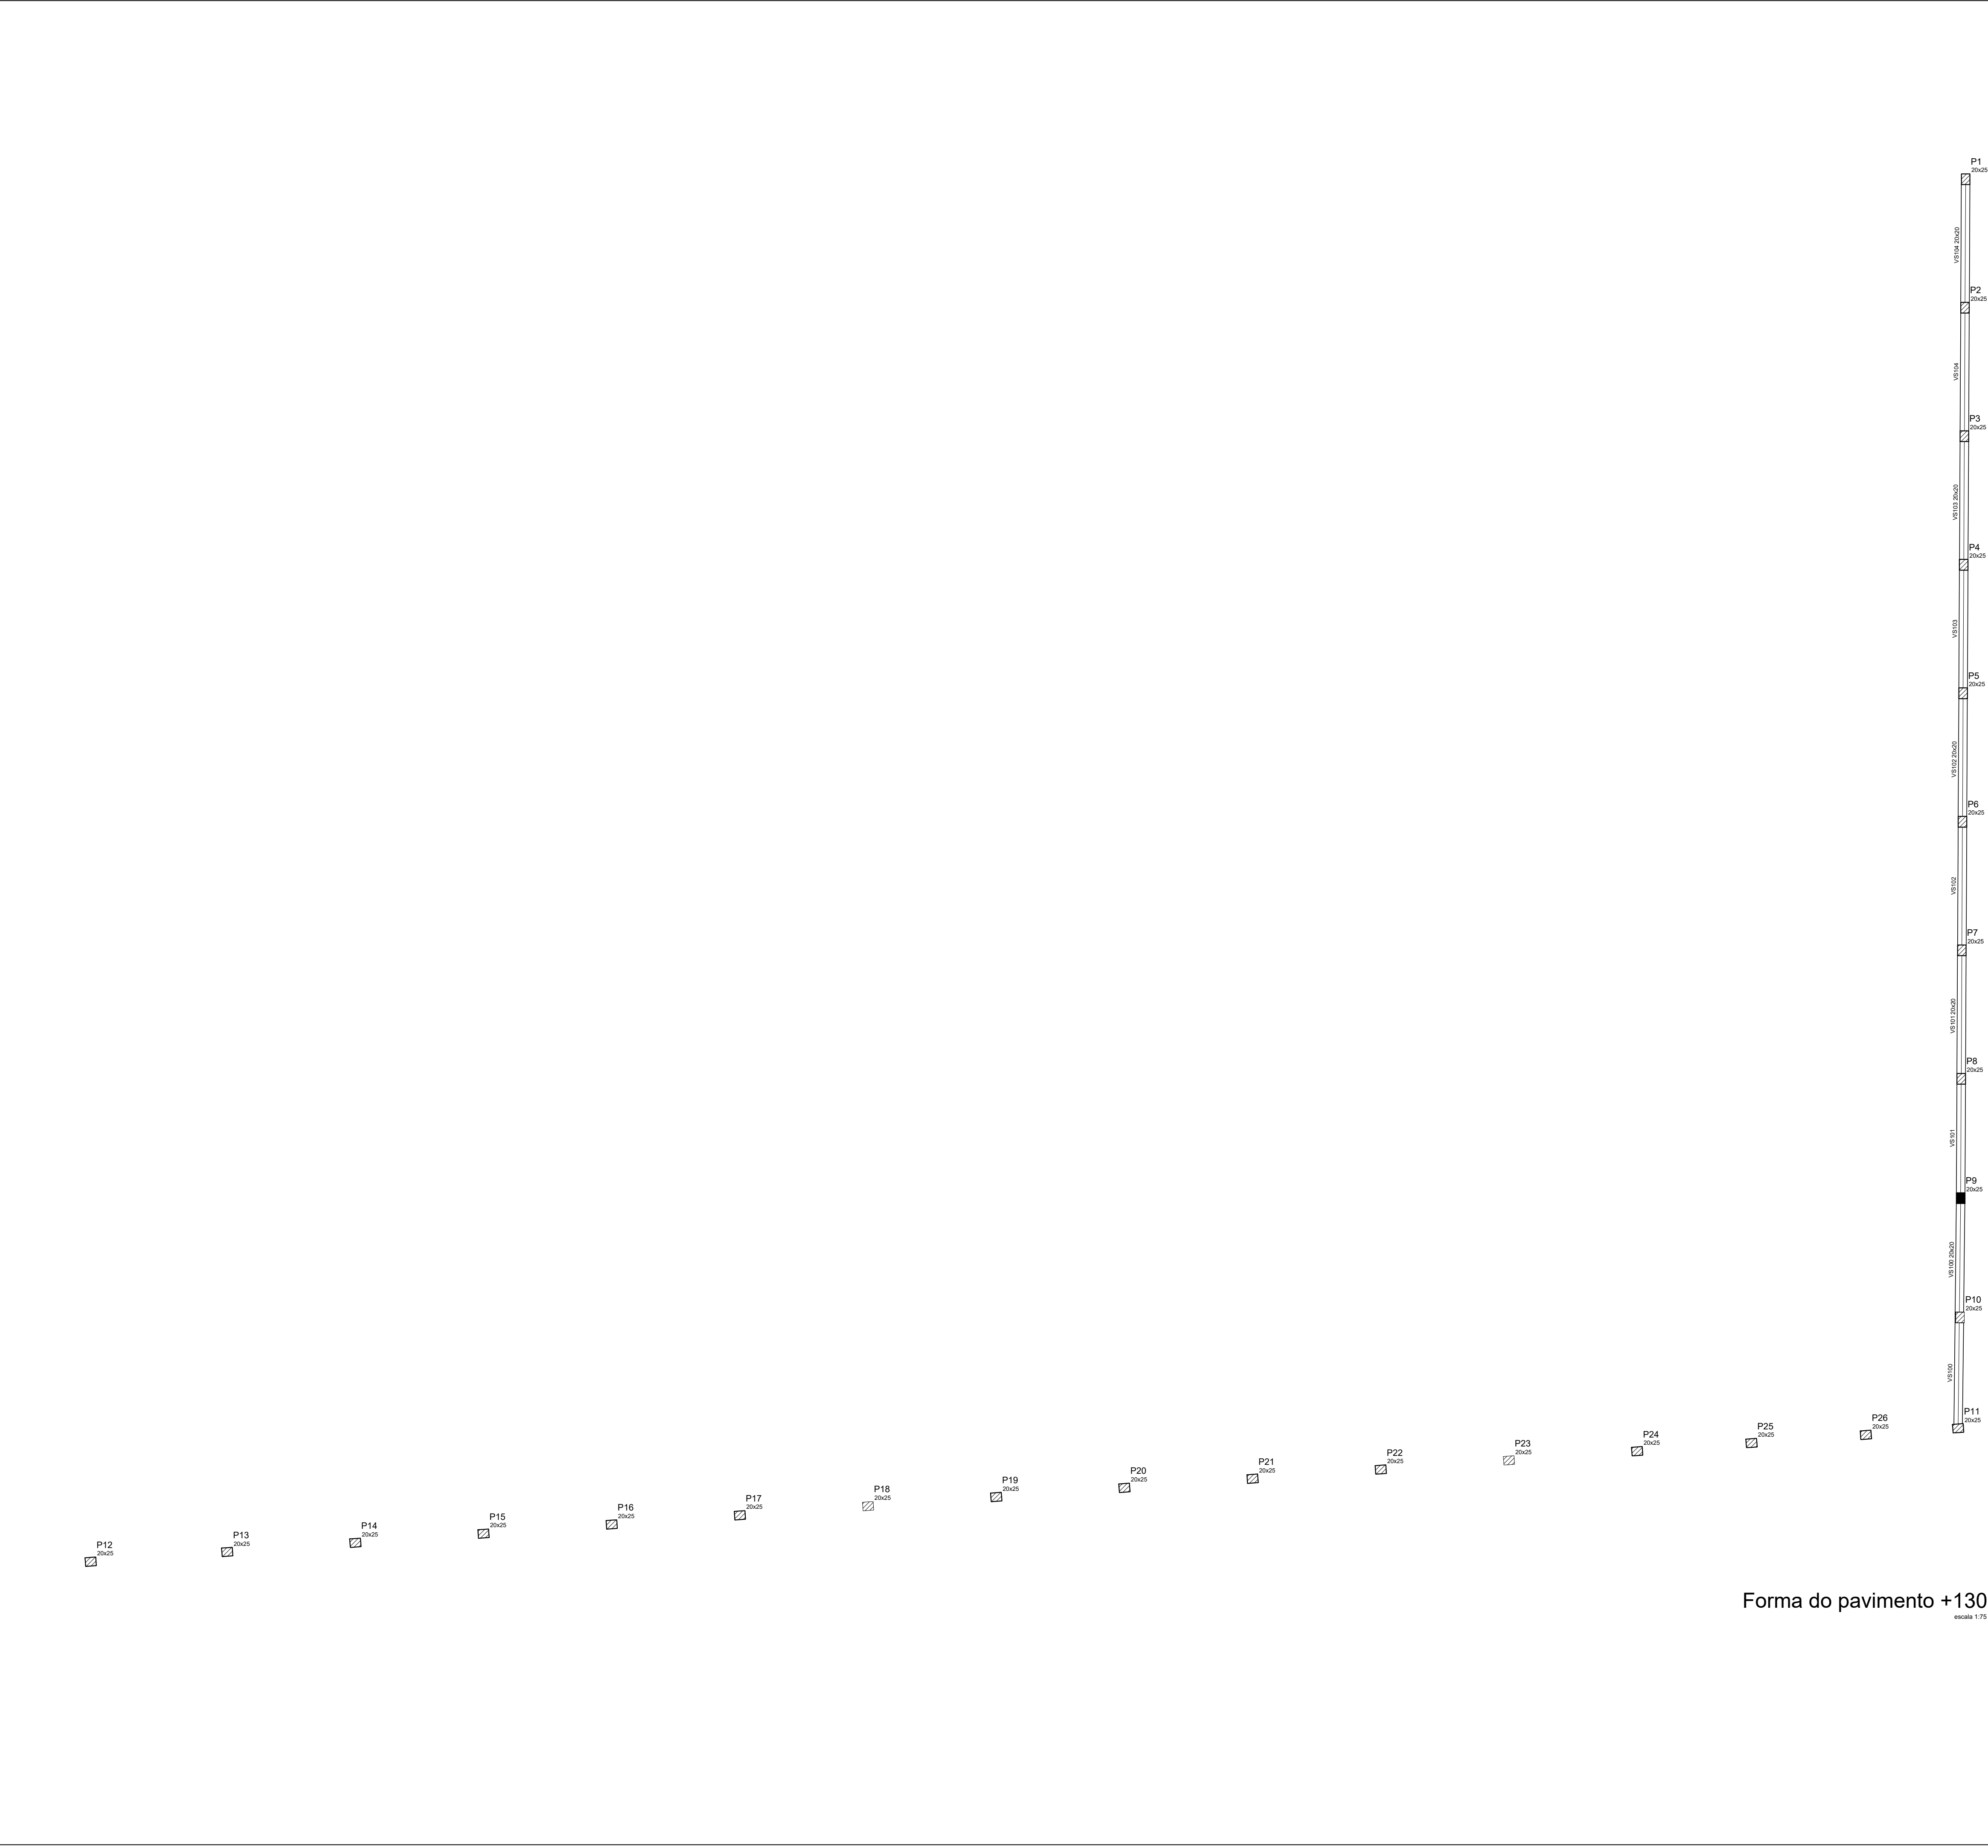

Vigas			
Nome	Seção (cm)	Elevação (cm)	Nível (cm)
VS100	20x20	0	130
VS101	20x20	0	130
VS102	20x20	0	130
VS103	20x20	0	130
VS104	20x20	0	130

Características dos materiais

fck (kgf/cm²)	Ecs (kgf/cm²)
250	238000

Pilares			
Nome	Seção (cm)	Elevação (cm)	Nível (cm)
P1	20 x 25	0	130
P2	20 x 25	0	130
P3	20 x 25	0	130
P4	20 x 25	0	130
P5	20 x 25	0	130
P6	20 x 25	0	130
P7	20 x 25	0	130
P8	20 x 25	0	130
P9	20 x 25	0	130
P10	20 x 25	0	130
P11	20 x 25	0	130
P12	20 x 25	0	130
P13	20 x 25	0	130
P14	20 x 25	0	130
P15	20 x 25	0	130
P16	20 x 25	0	130
P17	20 x 25	0	130
P18	20 x 25	0	130
P19	20 x 25	0	130
P20	20 x 25	0	130
P21	20 x 25	0	130
P22	20 x 25	0	130
P23	20 x 25	0	130
P24	20 x 25	0	130
P25	20 x 25	0	130
P26	20 x 25	0	130

Legenda dos Pilares

	Pilar que morre
	Pilar que passa
	Pilar que nasce
	Pilar com mudança de seção

PROPRIETÁRIO: PREFEITURA MUNICIPAL DE COREMAS - PB

LINCOLN CARTAXO DE LIRA JUNIOR:0689786140
Assinado de forma digital por LINCOLN CARTAXO DE LIRA JUNIOR:06897861405
Dados: 2025.07.22

PROJETO: LINCOLN CARTAXO DE LIRA JUNIOR:06897861405

CONSTRUÇÃO:

FOLHA 03/06
PROJETO: PRAÇA NOVA - COREMAS (PROJETO GUARITA)
CONCEDENTE: PREFEITURA MUNICIPAL DE COREMAS - PB
CONVENENTE: PREFEITURA MUNICIPAL DE COREMAS - PB
LOCALIDADE: COREMAS - PB

	DATA	RESPONSÁVEL	RUBRICA	DADOS
DESENHO	ABRIL/2025	LINCOLN CARTAXO		
CÓPIA				
VISTO				
INDICADA	DESENHOS - VIGAS BALDRAME.			CONVÊNIO
				REVISÃO
				ARQUIVO

Aprovações: