


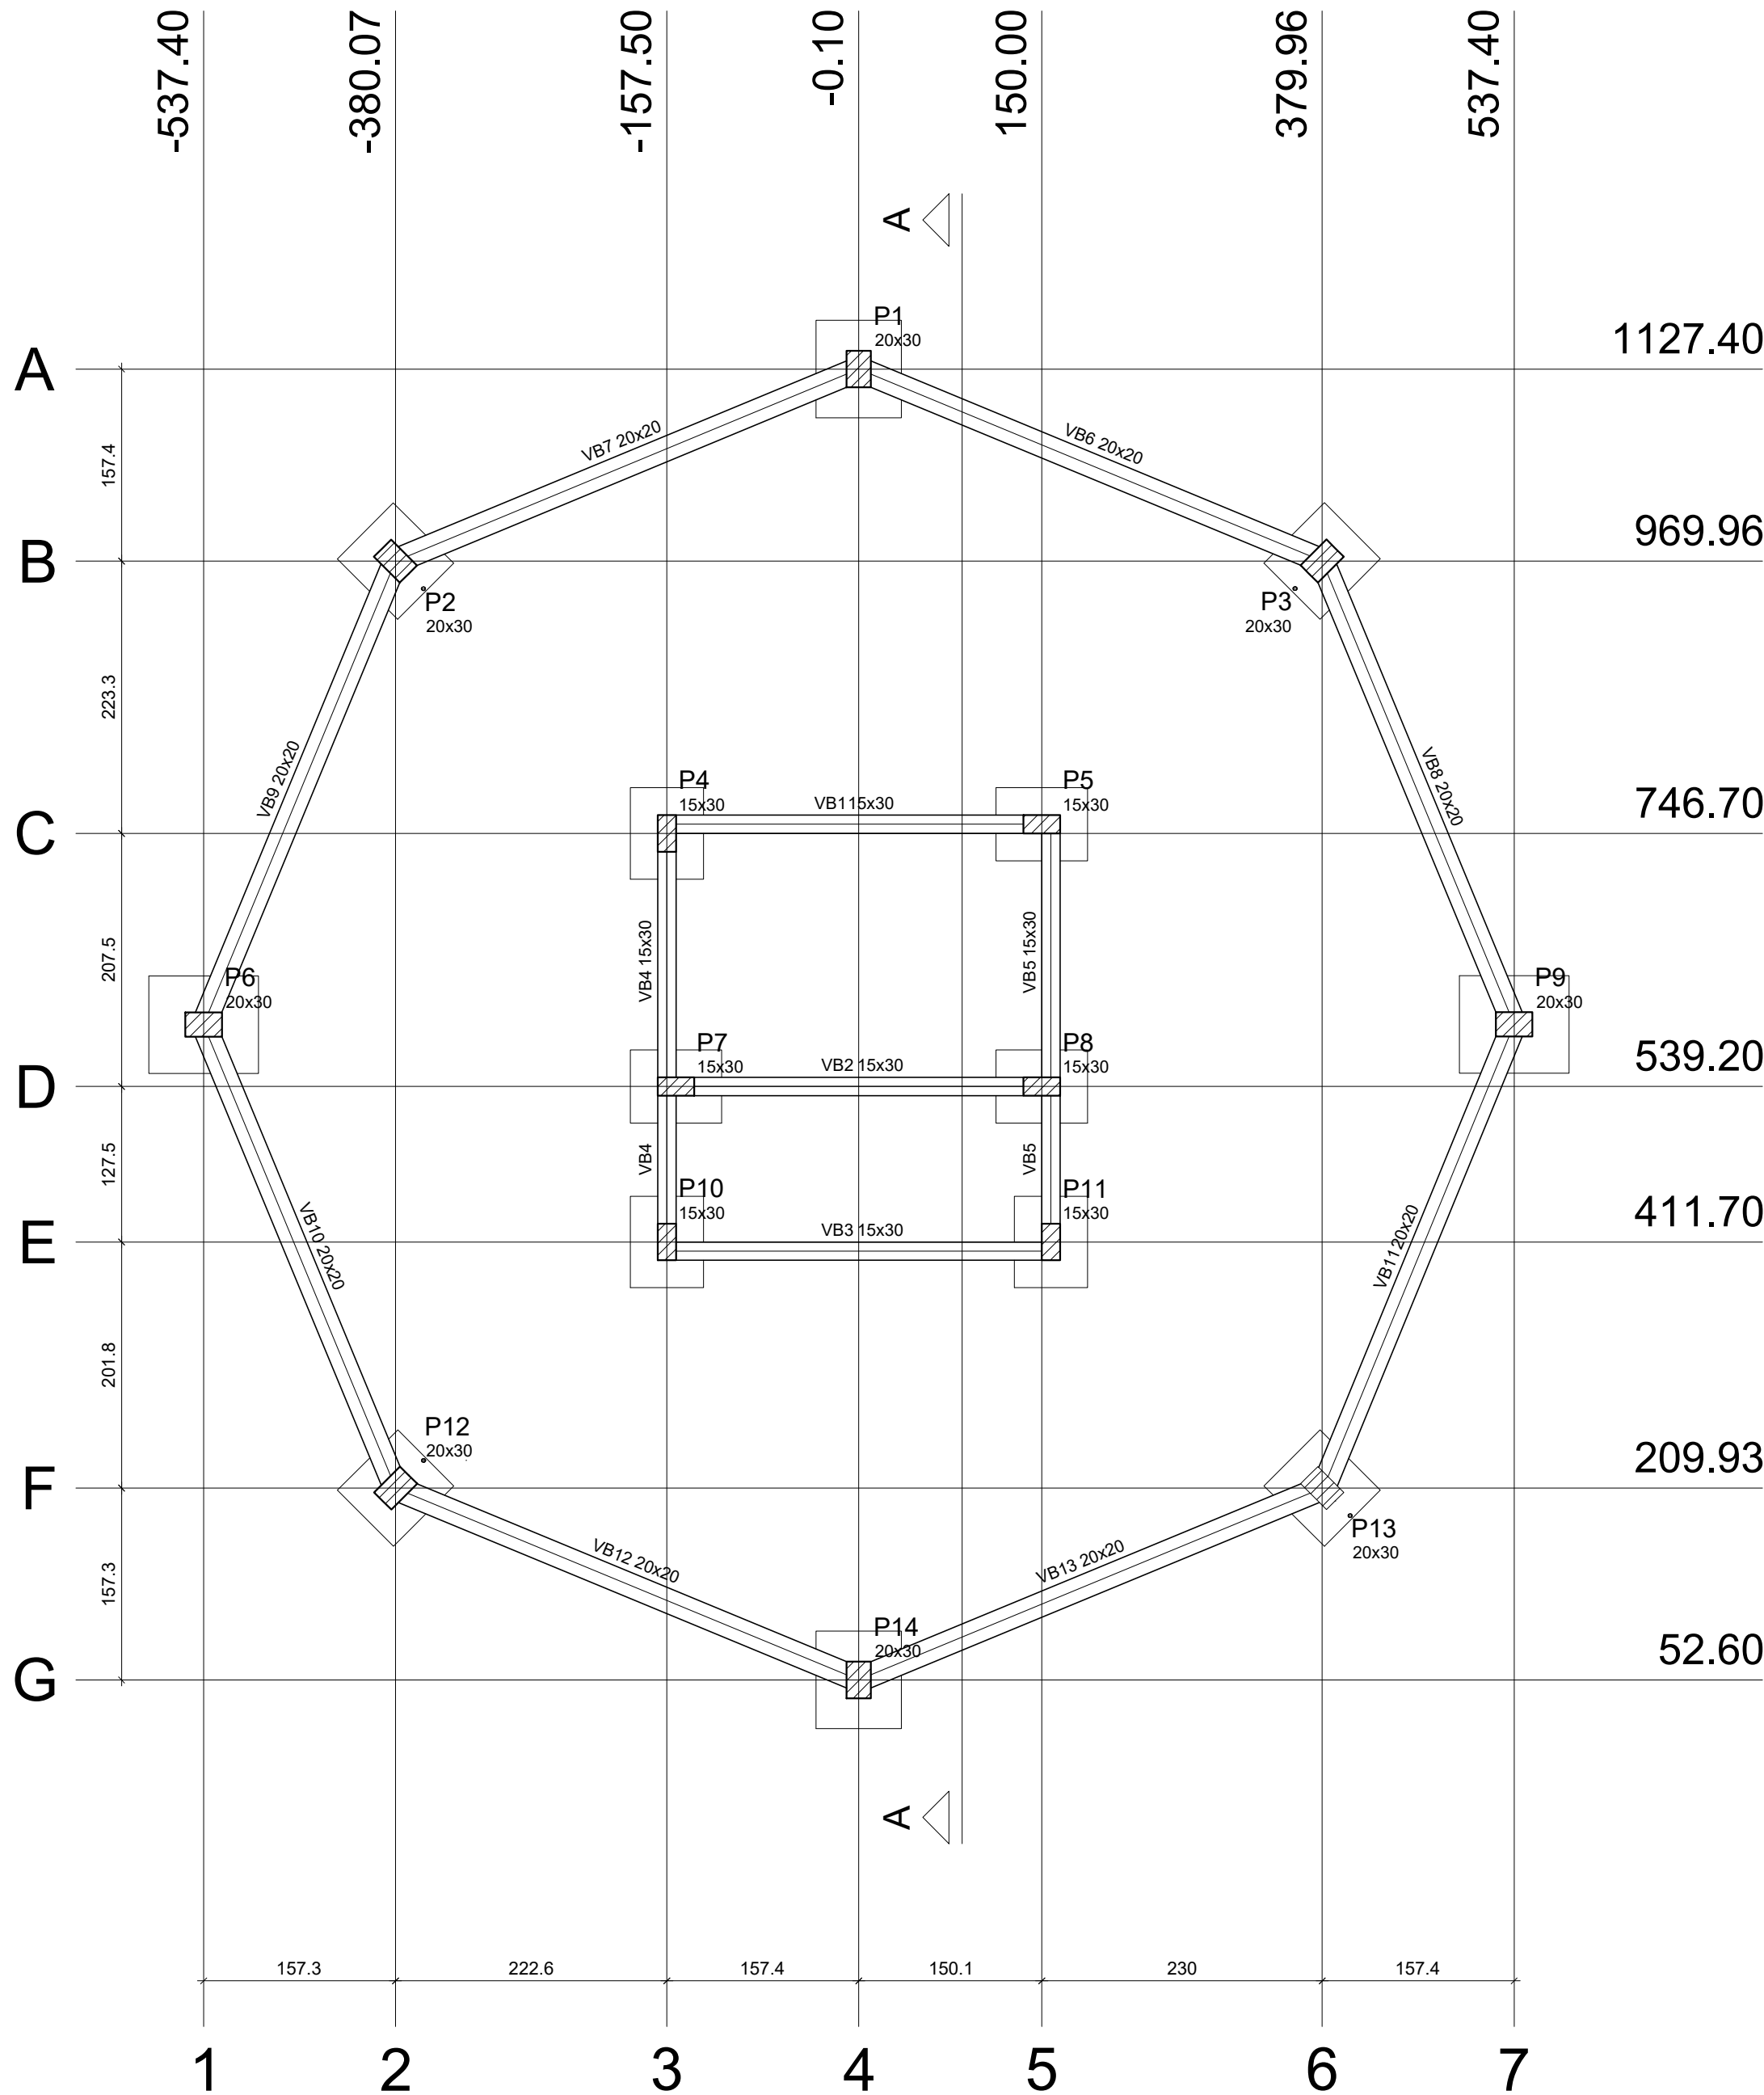

Vigas			
Nome	Seção (cm)	Elevação (cm)	Nível (cm)
VB1	15x30	0	0
VB2	15x30	0	0
VB3	15x30	0	0
VB4	15x30	0	0
VB5	15x30	0	0
VB6	20x20	0	0
VB7	20x20	0	0
VB8	20x20	0	0
VB9	20x20	0	0
VB10	20x20	0	0
VB11	20x20	0	0
VB12	20x20	0	0
VB13	20x20	0	0

Características dos materiais	
fck (kgf/cm²)	Ecs (kgf/cm²)
250	238000

Pilares			
Nome	Seção (cm)	Elevação (cm)	Nível (cm)
P1	20 x 30	0	0
P2	20 x 30	0	0
P3	20 x 30	0	0
P4	15 x 30	0	0
P5	15 x 30	0	0
P6	20 x 30	0	0
P7	15 x 30	0	0
P8	15 x 30	0	0
P9	20 x 30	0	0
P10	15 x 30	0	0
P11	15 x 30	0	0
P12	20 x 30	0	0
P13	20 x 30	0	0
P14	20 x 30	0	0

Legenda dos Pilares	
	Pilar que morre
	Pilar que passa
	Pilar que nasce
	Pilar com mudança de seção

PROPRIETÁRIO: PREFEITURA MUNICIPAL DE COREMAS - PB

PROJETO: LINCOLN CARTAXO DE LIRA JÚNIOR CREA 160.814.689-8

CONSTRUÇÃO:

FOLHA
02/07

PROJETO: PRAÇA NOVA - COREMAS (PROJETO GUARITA)
CONCEDENTE: PREFEITURA MUNICIPAL DE COREMAS - PB
CONVENIENTE: PREFEITURA MUNICIPAL DE COREMAS - PB
LOCALIDADE: COREMAS - PB

	DATA	RESPONSÁVEL	RUBRICA	DADOS
DESENHO	ABRIL/2025	LINCOLN CARTAXO		
CÓPIA				
VISTO				
ESCALAS INDICADA	DESENHOS - FORMA +0.			CONVÊNIO
				REVISÃO
				ARQUIVO

Aprovações: