

Forma do pavimento +270

escala 1:50

Vigas			
Nome	Seção (cm)	Elevação (cm)	Nível (cm)
VS1	15x30	0	270
VS2	15x30	0	270
VS3	15x30	0	270
VS4	15x30	0	270
VS5	15x30	0	270


Lajes						Sobrecarga (kgf/m²)		
Nome	Tipo	Altura (cm)	Elevação (cm)	Nível (cm)	Peso próprio (kgf/m²)	Adicional	Acidental	Localizada
LAJE1	Maciça	10	0	270	250	100	100	sim

Área de lajes			
Tipo	Altura (cm)	Bloco de Enchimento	Área (m²)
Maciça	10	-	6.00

Características dos materiais	
fck (kgf/cm²)	Ecs (kgf/cm²)
250	238000

Pilares			
Nome	Seção (cm)	Elevação (cm)	Nível (cm)
P4	15 x 30	115	385
P5	15 x 30	115	385
P7	15 x 30	150	420
P8	15 x 30	150	420
P10	15 x 30	110	380
P11	15 x 30	110	380

Legenda dos Pilares	
	Pilar que morre
	Pilar que passa
	Pilar que nasce
	Pilar com mudança de seção

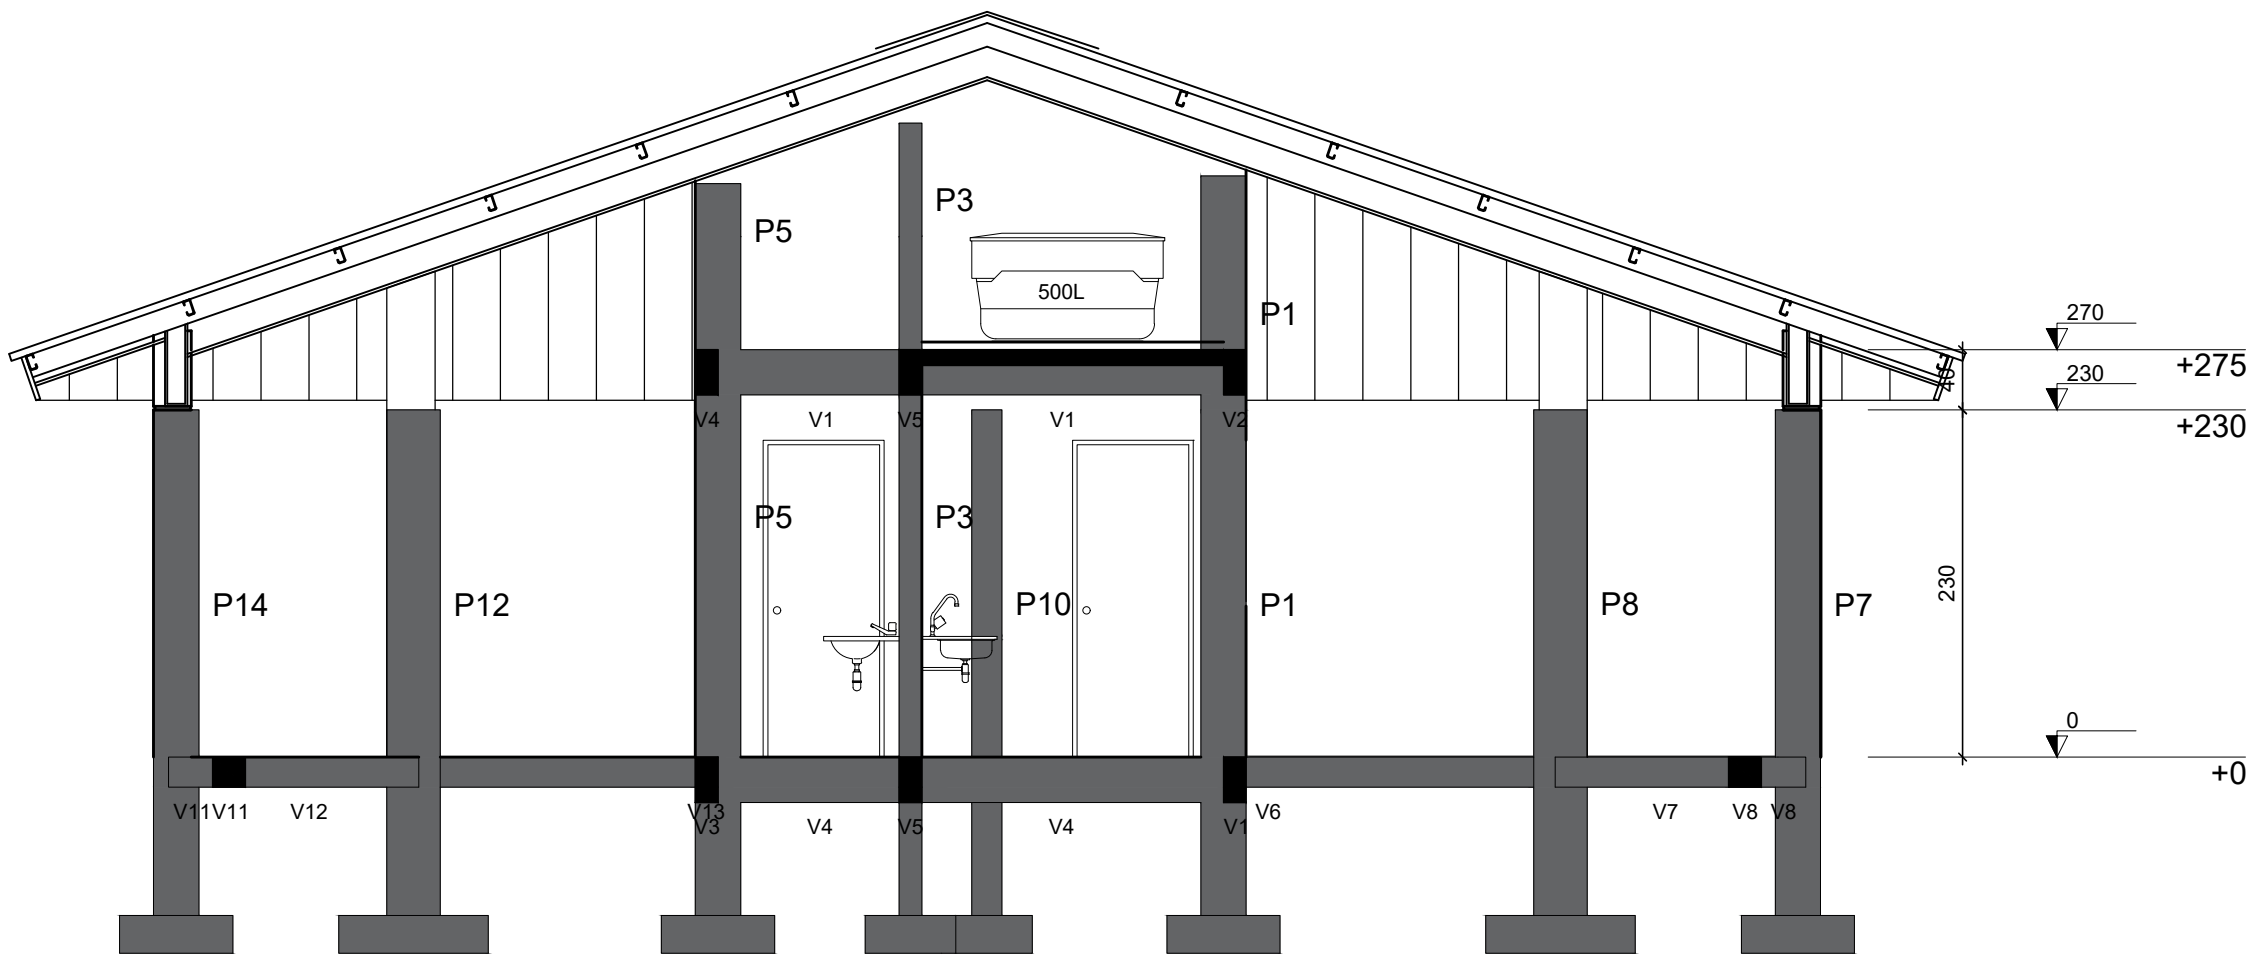

CORTE AA

escala 1:50

PROPRIETÁRIO: PREFEITURA MUNICIPAL DE COREMAS - PB

PROJETO: LINCOLN CARTAXO DE LIRA JÚNIOR CREA 160.814.689-8

CONSTRUÇÃO:

FOLHA

03/07

PROJETO: PRAÇA NOVA - COREMAS (PROJETO GUARITA)
CONCEDENTE: PREFEITURA MUNICIPAL DE COREMAS - PB
CONVENIENTE: PREFEITURA MUNICIPAL DE COREMAS - PB
LOCALIDADE: COREMAS - PB

	DATA	RESPONSÁVEL	RUBRICA	DADOS
DESENHO	ABRIL/2025	LINCOLN CARTAXO		
CÓPIA				
VISTO				
ESCALAS	DESENHOS			CONVÊNIO
INDICADA	- FORMAS +270; - CORTE AA.			REVISÃO
				ARQUIVO

Aprovações:



Av. Gov. Flávio Ribeiro Coutinho, 500, sl. 601
Jardim Oceania, 58037-005 - João Pessoa (PB)
Tel +55 (83) 3578.3426
Cel +55 (83) 99924.4447
e-mail: lclprojetos@hotmail.com